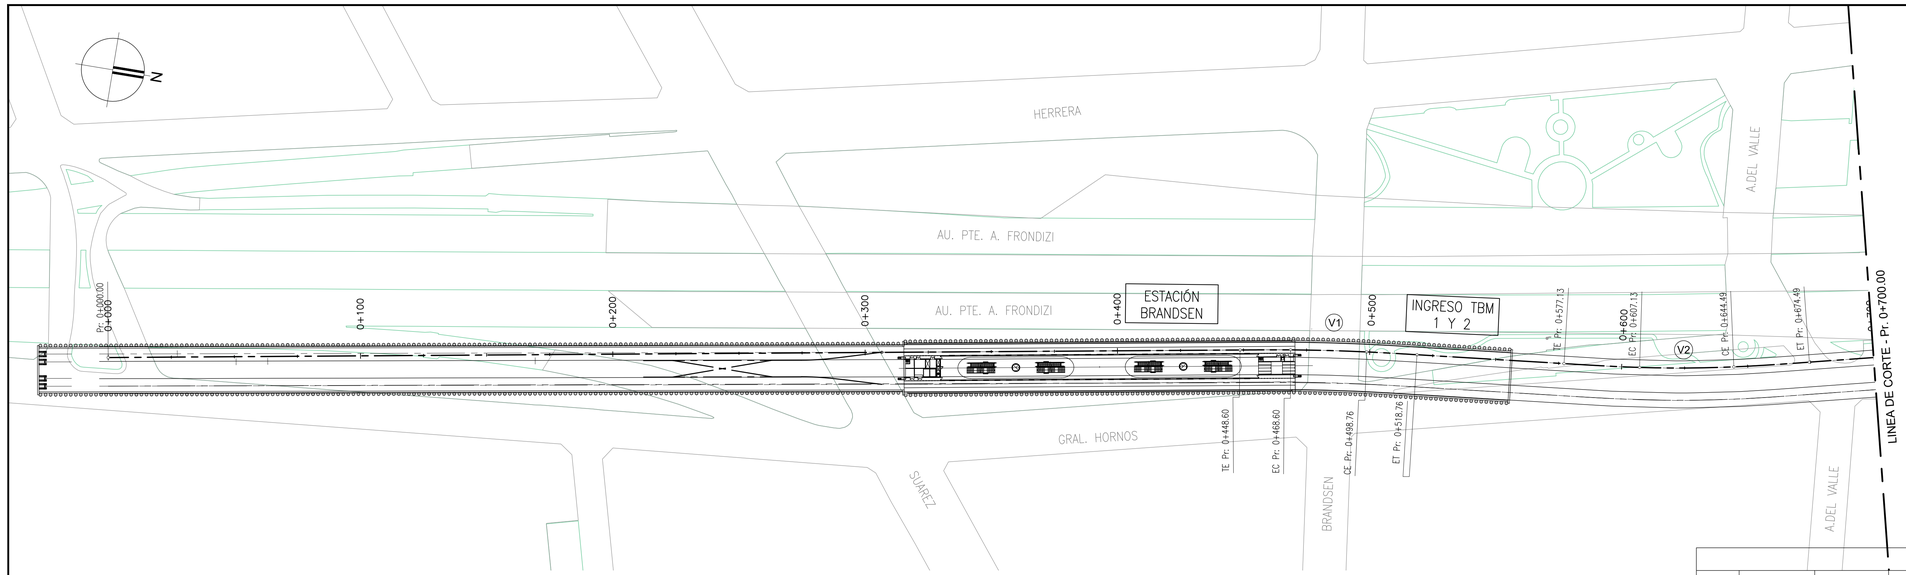

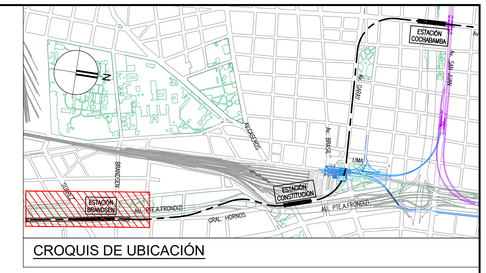

CROQUIS DE UBICACIÓN

CURVAS HORIZONTALES											
Curva N°	Prog.	X	Y	Rc (m)	Le (m)	Δ	Des (m)	Tan (m)	E (m)	VD (km/h)	PERALTE (mm)
V 1	0+483.69	7954.470	-977.491	750.00	20.00	3° 49' 56"	70.16	35.09	0.44	70	40
V 2	0+625.86	7939.681	-836.071	510.00	30.00	7° 34' 04"	97.36	48.73	1.19	70	59

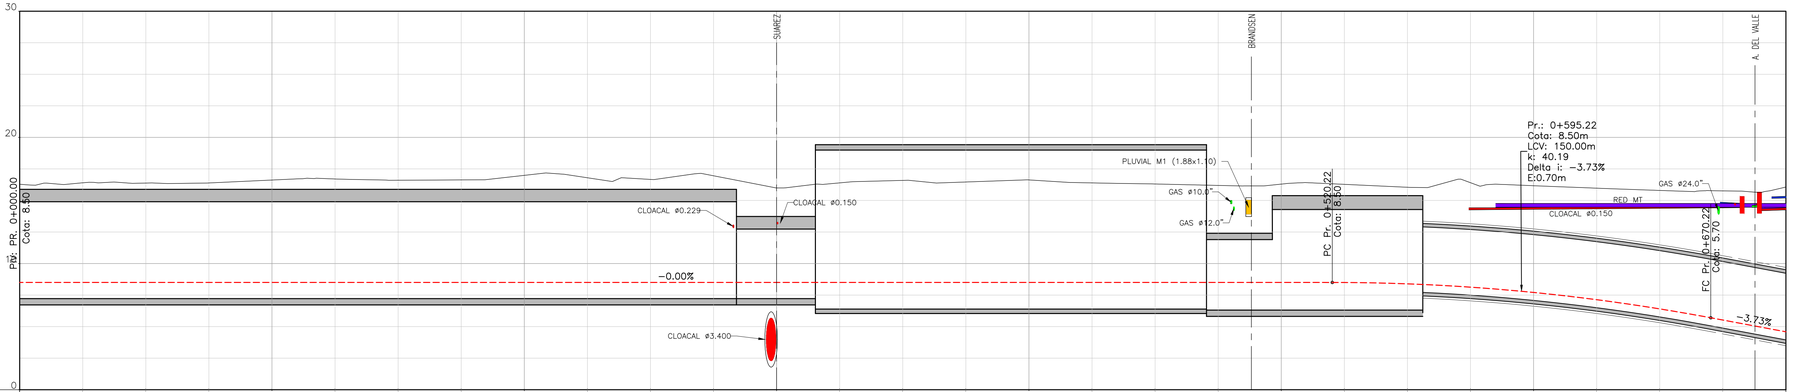

| | | | | | | | | | | |

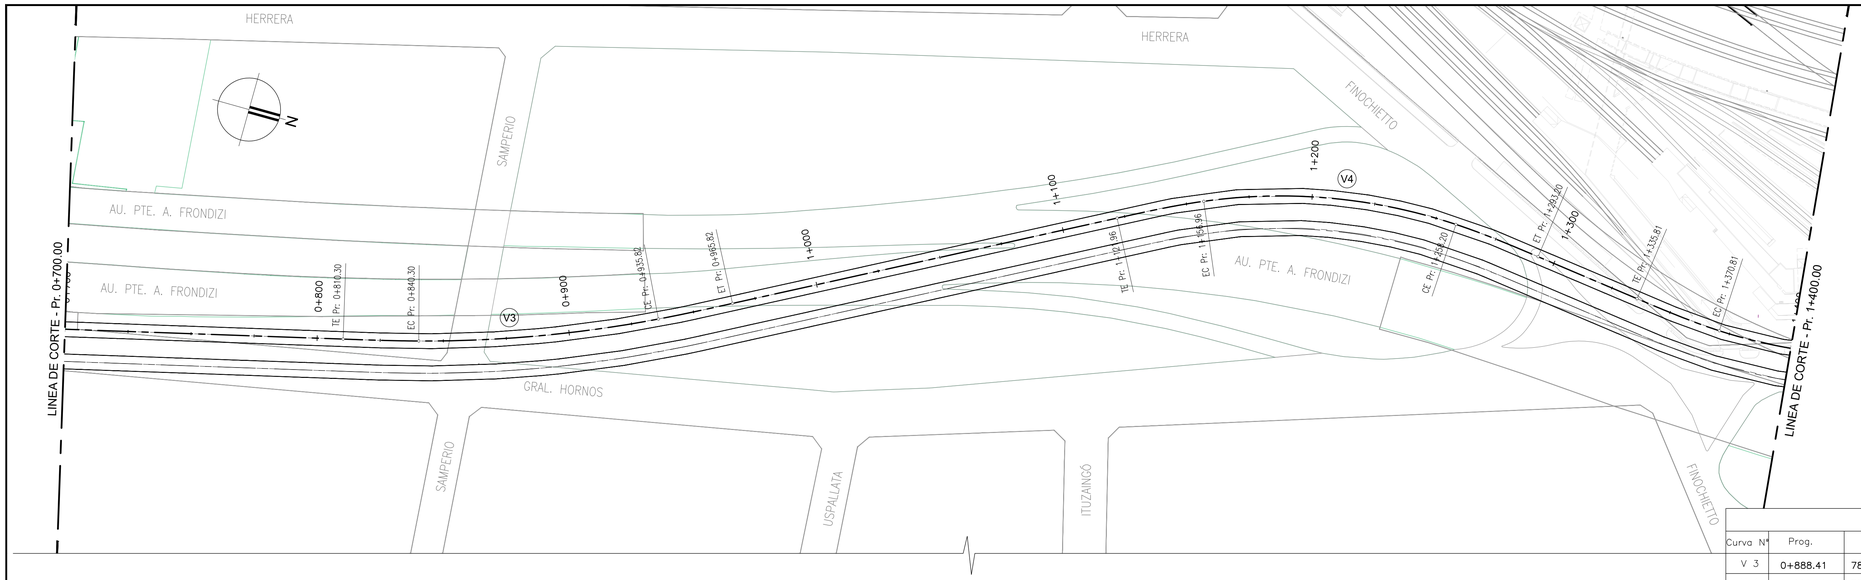

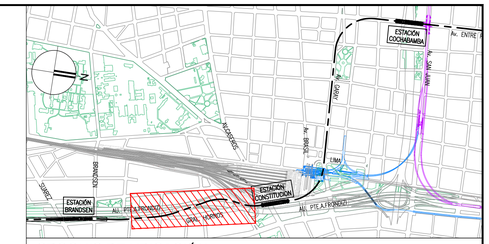

CROQUIS DE UBICACIÓN

CURVAS HORIZONTALES											
Curva Nº	Prog.	X	Y	Rc (m)	Le (m)	Δ	Des (m)	Tan (m)	E (m)	VD (km/h)	PERALTE (mm)
V 3	0+888.41	7878.196	−580.713	495.00	30.00	14° 31' 44"	155.52	78.11	4.08	70	61
V 4	1+209.91	7726.603	−296.408	220.00	35.00	35° 28' 54"	171.24	87.95	11.23	45	68

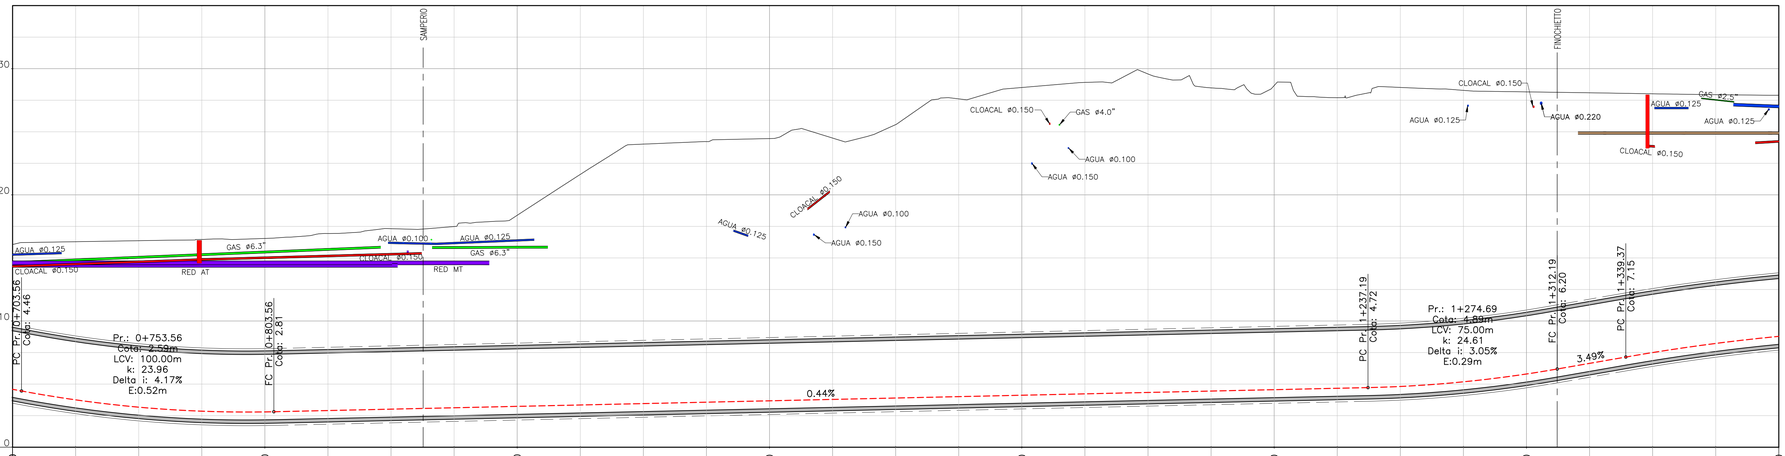

| | | | | | | | | | | |

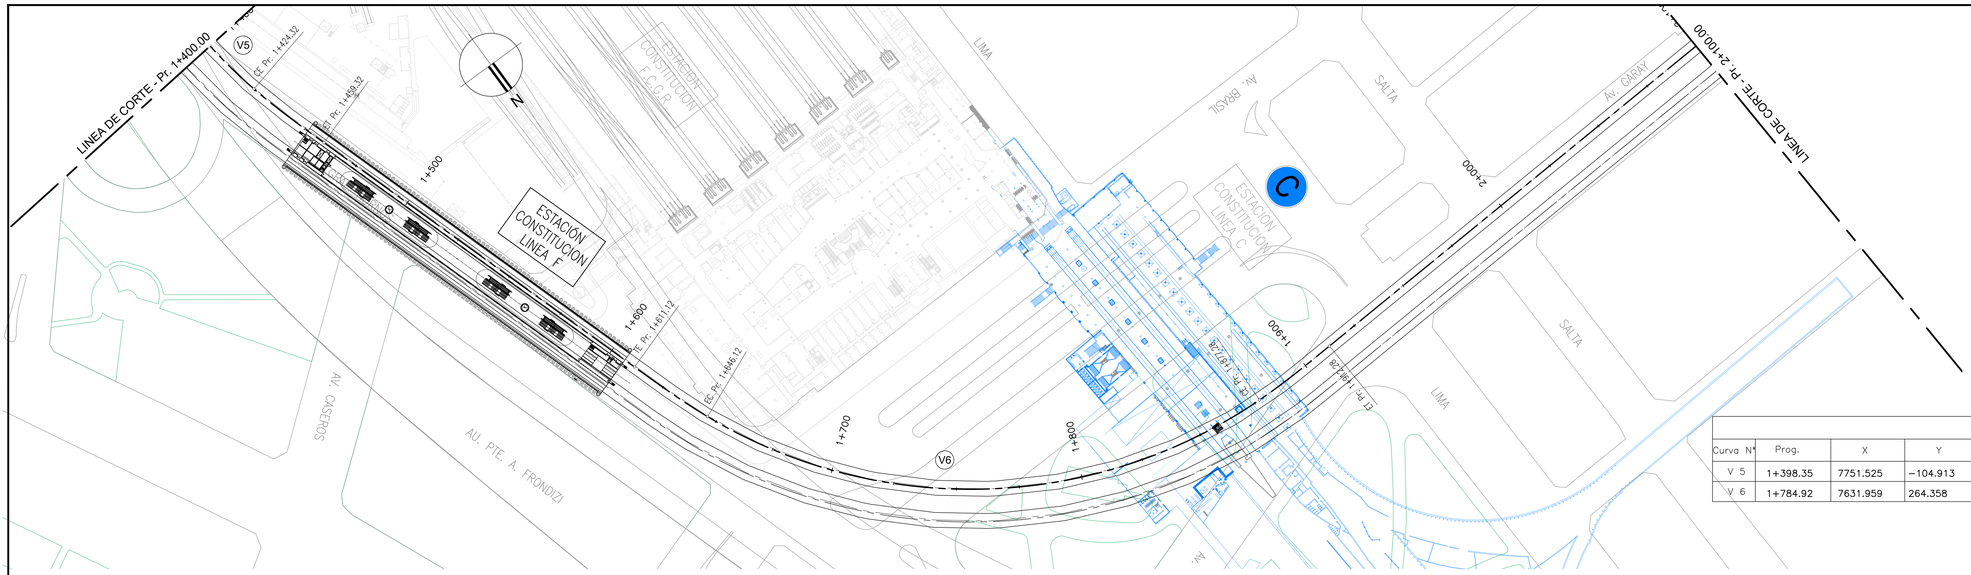

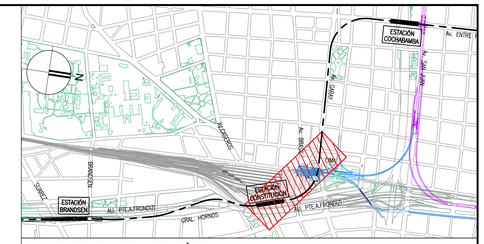

CROQUIS DE UBICACIÓN

CURVAS HORIZONTALES

Curva N°	Prog.	X	Y	Rc (m)	Le (m)	Δ	Des (m)	Tan (m)	E (m)	VD (km/h)	PERALTE (mm)
V 5	1+398.35	7751.525	−104.913	200.00	35.00	25° 21' 22"	123.51	62.54	5.26	45	70
V 6	1+784.92	7631.959	264.358	203.00	35.00	75° 07' 19"	301.16	173.80	53.40	45	70

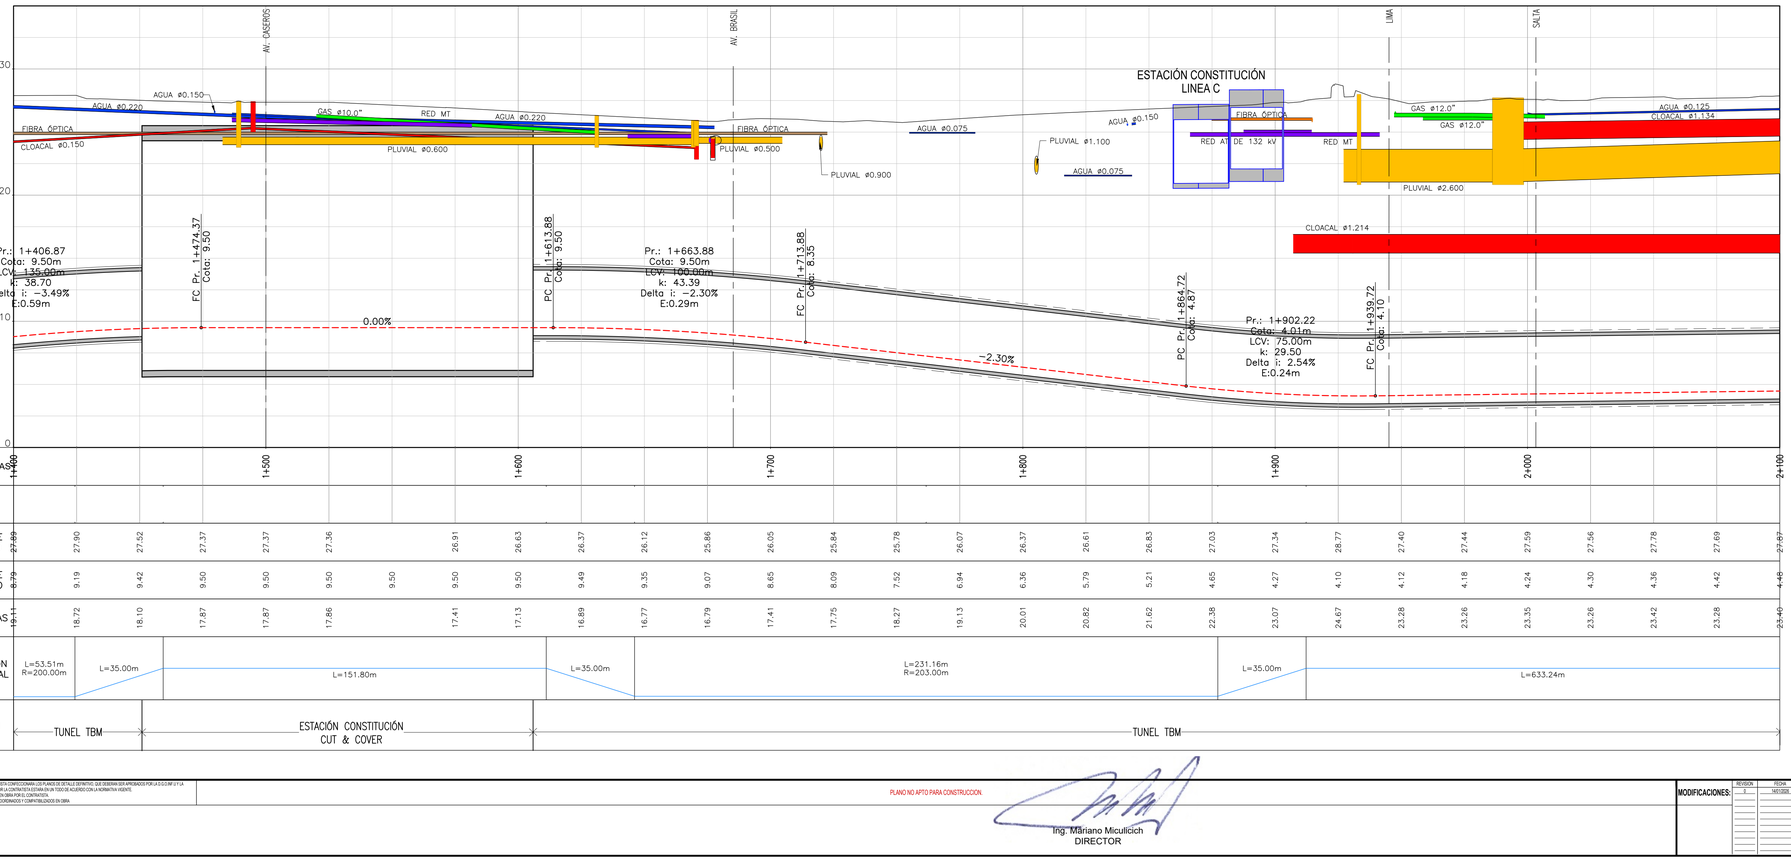

PROGRESIVAS	1+400	1+500	1+600	1+700	1+800	1+900	2+000	2+100
CAMBIO DE VIAS								
COTAS DE TERRENO	27.89 27.90 27.52 27.37 27.37 27.36 26.91 26.63 26.37 26.12 25.86 26.05 25.84 25.78 26.07 26.37 26.61 26.83 27.03 27.34 28.77 27.40 27.44 27.59 27.56 27.78 27.69 27.67							
COTAS DE PROYECTO	8.79 9.19 9.42 9.50 9.50 9.50 9.50 9.50 9.50 9.49 9.35 9.07 8.65 8.09 7.52 6.94 6.36 5.79 5.21 4.65 4.27 4.10 4.12 4.18 4.24 4.30 4.36 4.42 4.48							
DIFERENCIAS	19.11 18.72 18.10 17.87 17.87 17.86 17.41 17.13 16.89 16.77 16.79 17.41 17.75 18.27 19.13 20.01 20.82 21.62 22.38 23.07 24.67 23.28 23.26 23.35 23.26 23.42 23.28 23.40							
ALINEACIÓN HORIZONTAL	L=53.51m R=200.00m	L=35.00m	L=151.80m	L=35.00m	L=231.16m R=203.00m	L=35.00m	L=633.24m	
SECCIÓN	TUNEL TBM	ESTACIÓN CONSTITUCIÓN CUT & COVER		TUNEL TBM				

REFERENCIAS INTERFERENCIAS:

- RED BT - MT -AT
- RED PLUVIAL
- RED CLOACAL
- RED DE AGUA CORRIENTE
- RED DE GAS
- RED DE FIBRA OPTICA
- RED TELEFÓNICA

NOTAS:

1- SISTEMA DE COORDENADAS DE LA CIUDAD DE BUENOS AIRES.

2- TODAS LAS MEDIDAS ESTÁN EXPRESADAS EN METROS, SALVO INDICACIÓN CONTRARIA

0 5 10m — ESCALA 1:200

0 50m — ESCALA 1:1.000

NOTAS: EL PRESENTE PLANO ES INDICATIVO. LA CONTRATISTA CONFECCIONARA LOS PLANOS DE DETALLE CONSTRUCTIVO, QUE DEBERAN SER APROBADOS POR LA D.G.ISP. Y / O LA INSPECCION DE OBRA. EL PLANO PRESENTADO POR LA CONTRATISTA ESTARA EN TODO DE ACUERDO CON LA NORMATIVA VIGENTE.
TODAS LAS MEDIDAS Y NIVELES SE VERIFICARAN EN OBRA POR EL CONTRATISTA.
TODOS LOS DETALLES CONSTRUCTIVOS SERAN COORDINADOS Y COMPATIBILIZADOS EN OBRA.

PLANO NO APTO PARA CONSTRUCCION.

Ing. Mariano Miculicich
DIRECTOR

MODIFICACIONES:

REVISIÓN	FECHA	DESCRIPCIÓN
0	14/1/2026	EMISIÓN INICIAL

MINISTERIO DE INFRAESTRUCTURA
SUBSECRETARIA DE PROYECTOS Y OBRAS
DIRECCION GENERAL DE PROYECTOS

DGPRO

Obra: LÍNEA F
Plano: TRAZADO DE VÍAS - PLANIALTIMETRÍA VÍA ASCENDENTE - PR. 1+400 A 2+100
Fecha: 14/01/2026 | Eq. de Proyecto: UPU-ATEC-IATASA | Dibujó: N.S. | Revisó: G.D.R. | Escala: Indicada

IF-2026-20223041-GCABA-APRA | Plano N° 003 | LF-VI-T01-VIA-PL-003

15/1/2026 09:41 a. m.
LF-VI-T01-VIA-PL-003 - PLANIALTIMETRIA T1 - VIA ASC.dwg

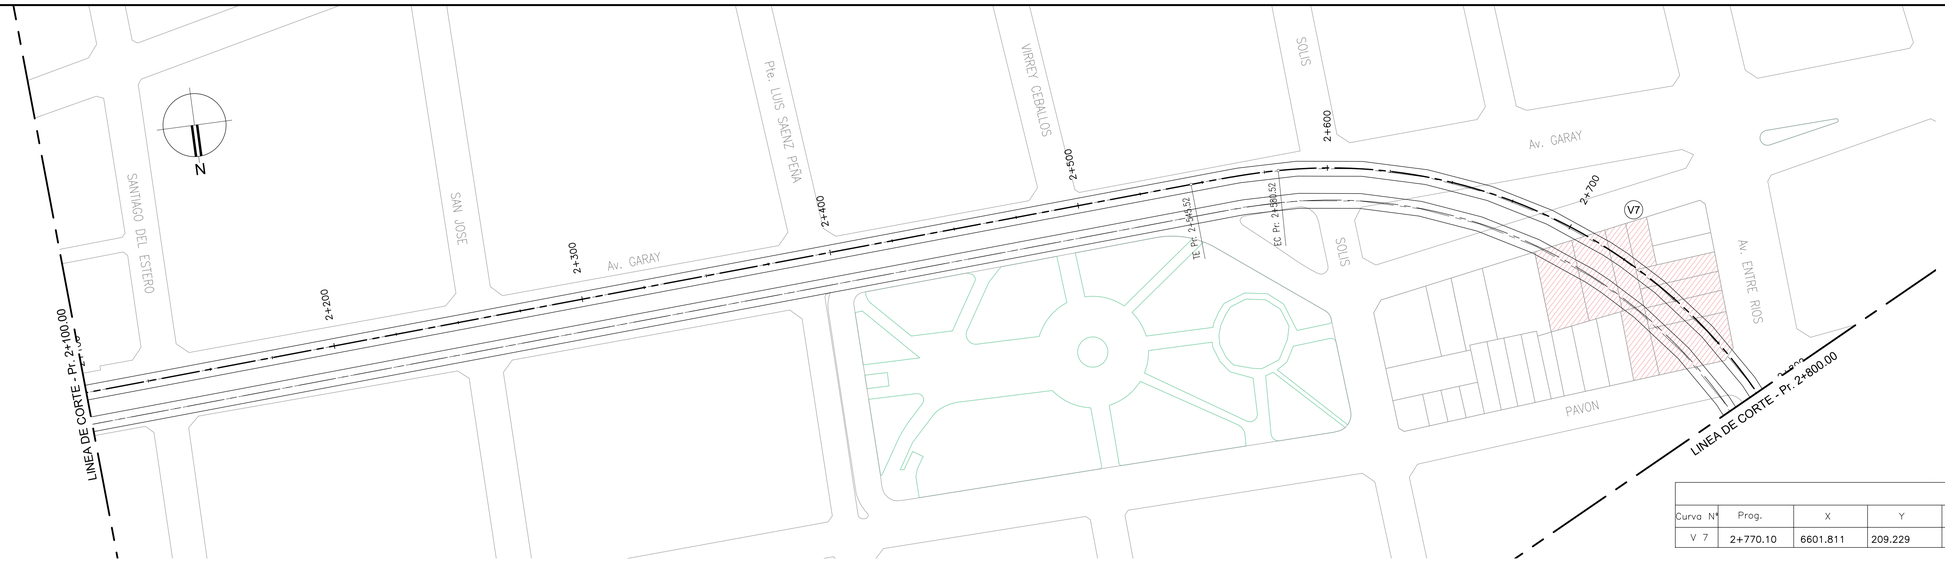

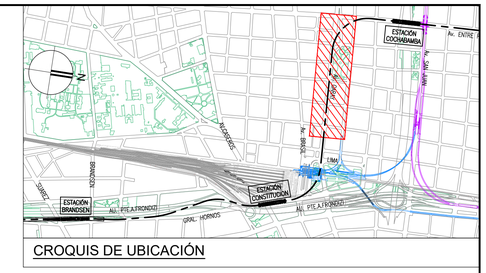

CROQUIS DE UBICACIÓN

CURVAS HORIZONTALES											
Curva N°	Prog.	X	Y	Rc (m)	Le (m)	Δ	Des (m)	Tan (m)	E (m)	VD (km/h)	PERALTE (mm)
V 7	2+770.10	6601.811	209.229	205.00	35.00	90° 30' 40"	358.84	224.58	86.57	45	70

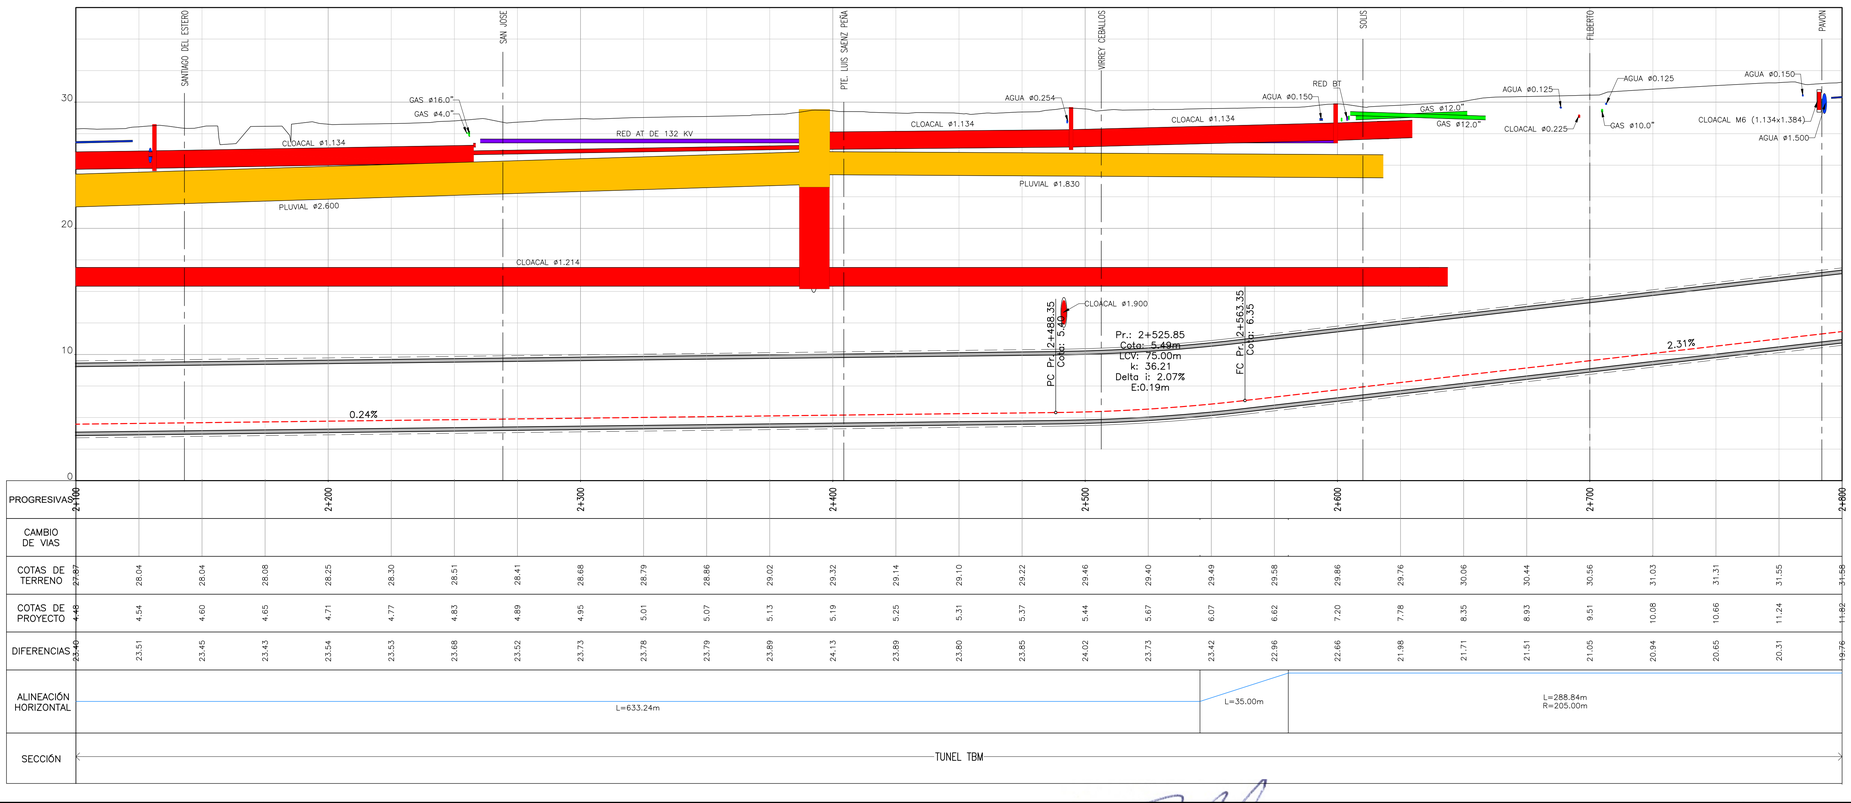

| | | | | | | | | | | |

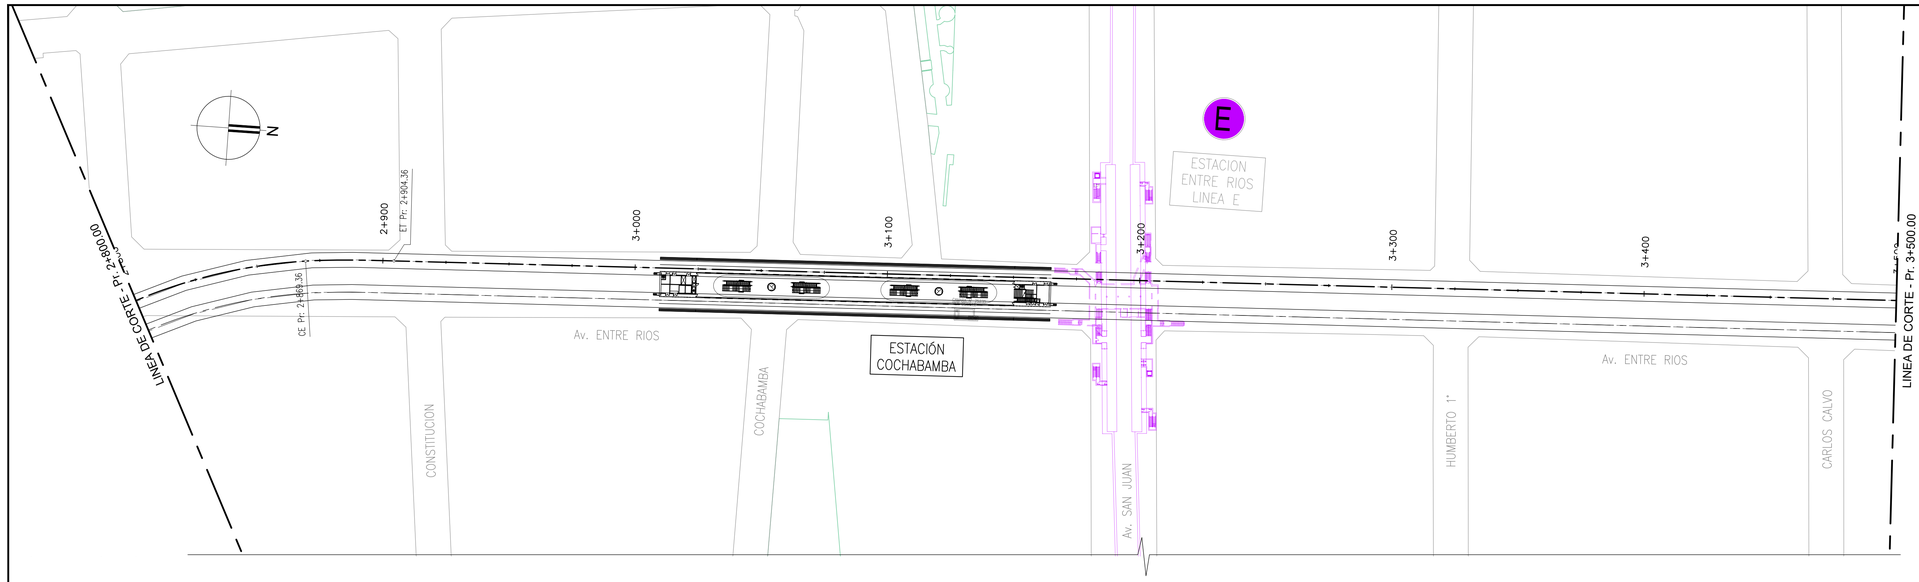

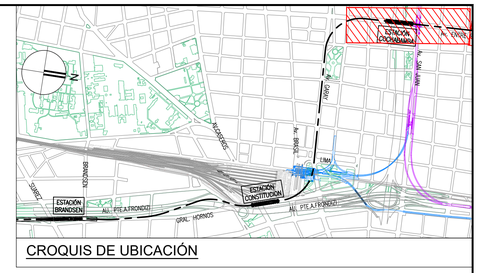

CROQUIS DE UBICACIÓN

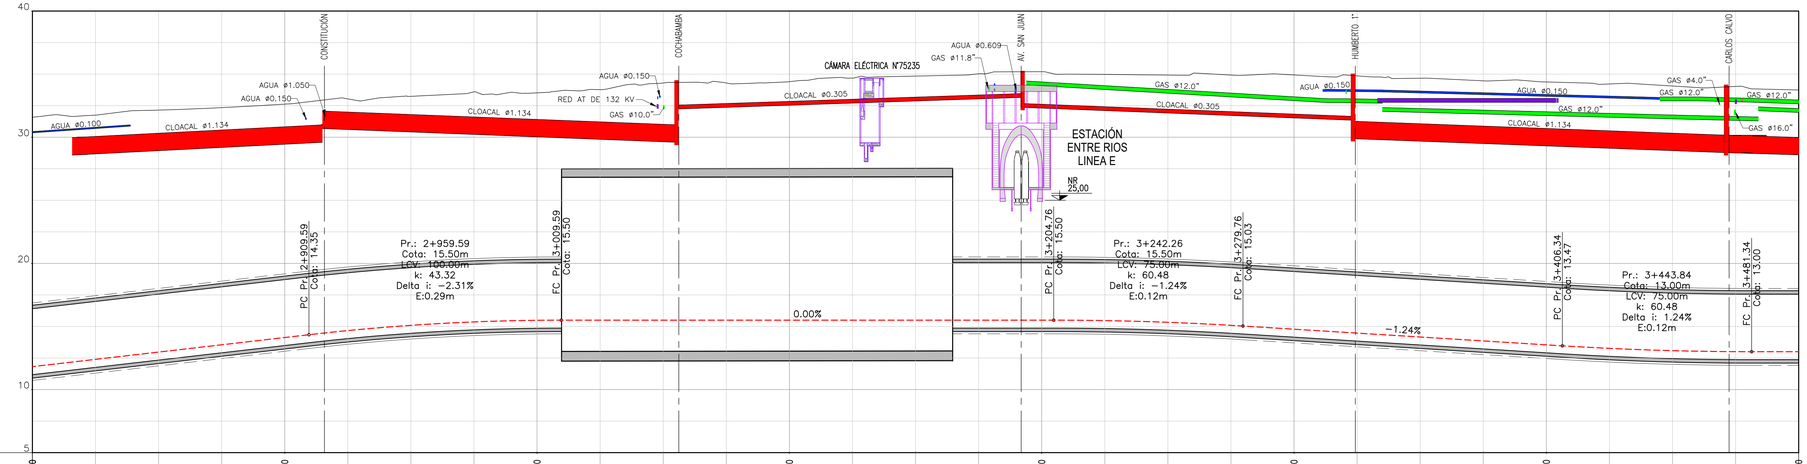

| | | |

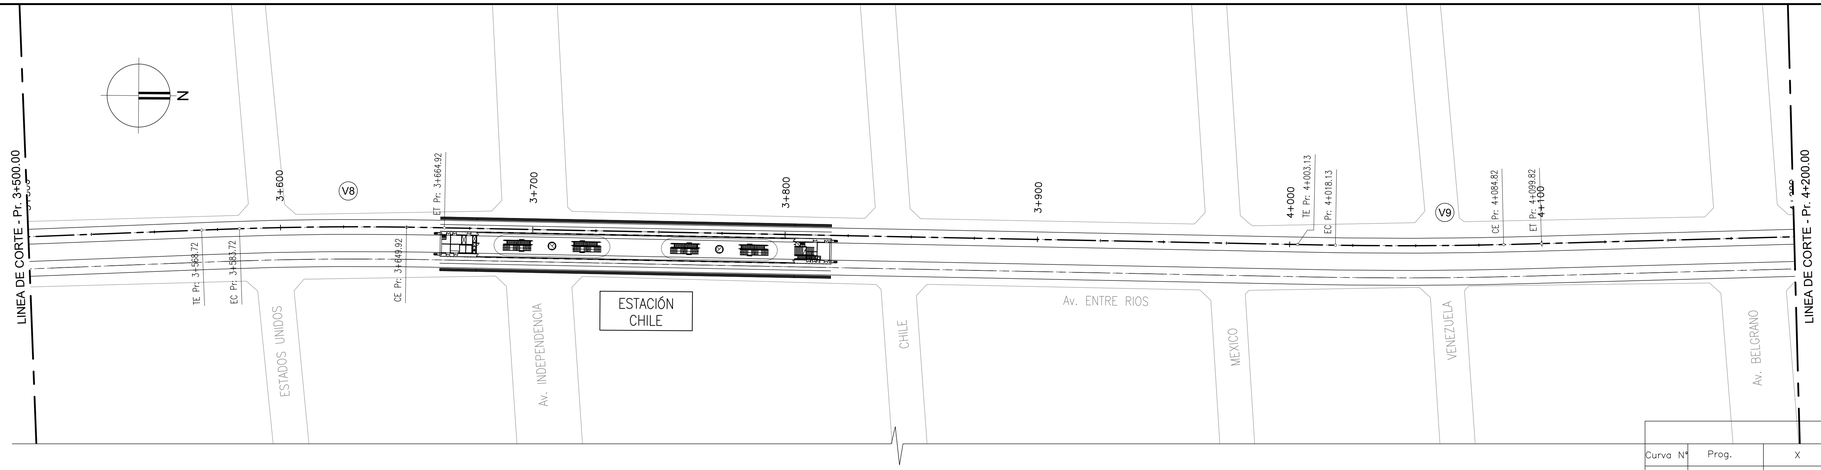

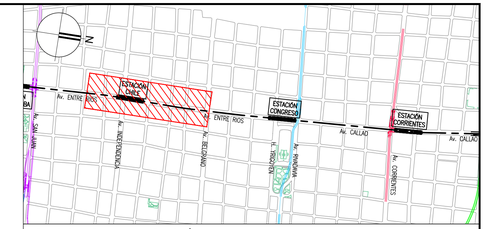

CROQUIS DE UBICACIÓN

CURVAS HORIZONTALES

Curva Nº	Prog.	X	Y	Rc (m)	Le (m)	Δ	Des (m)	Tan (m)	E (m)	VD (km/h)	PERALTE (mm)
V 8	3+616.83	6560.085	1145.357	1400.00	15.00	3° 19' 24"	96.21	48.12	0.60	90	32
V 9	4+051.48	6565.937	1579.993	1750.00	15.00	2° 40' 28"	96.68	48.35	0.48	90	26

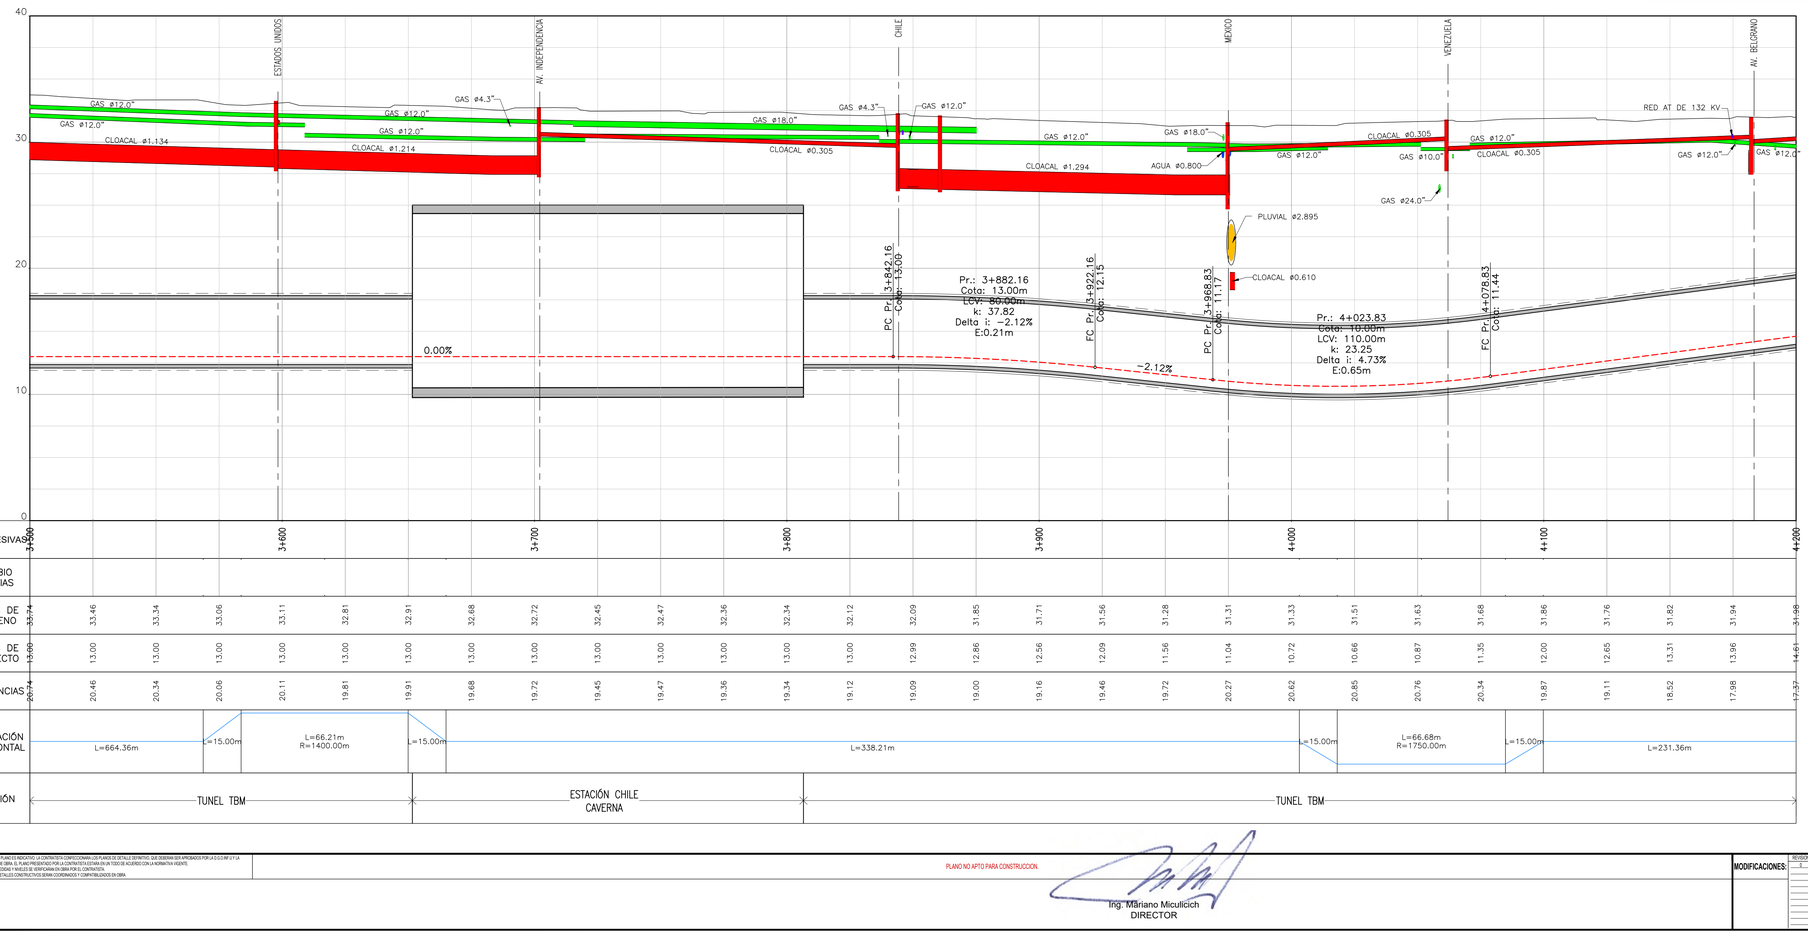

| | | |

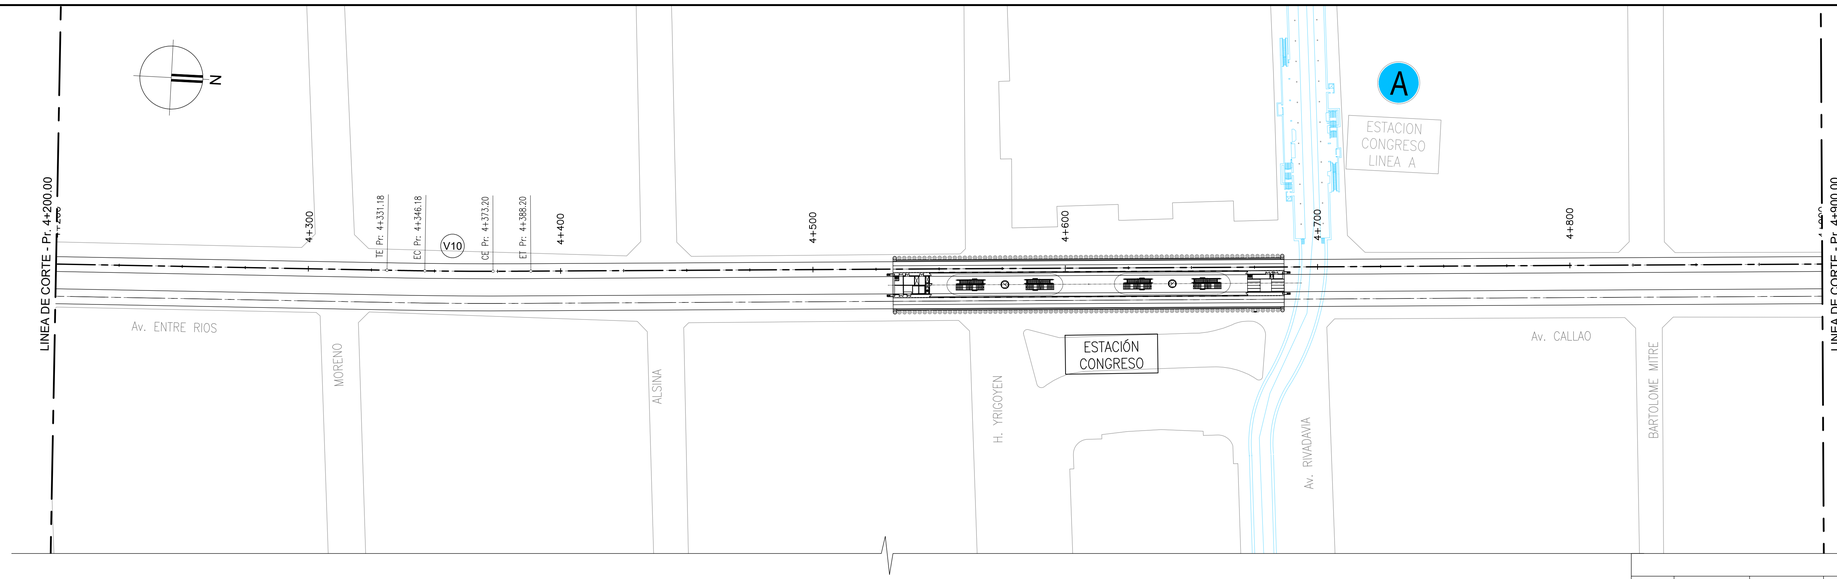

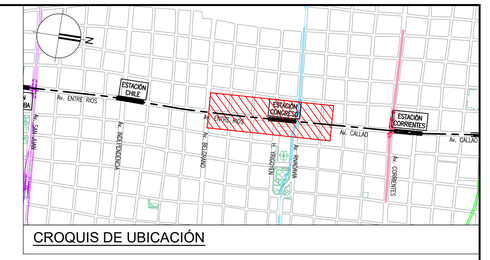

CROQUIS DE UBICACIÓN

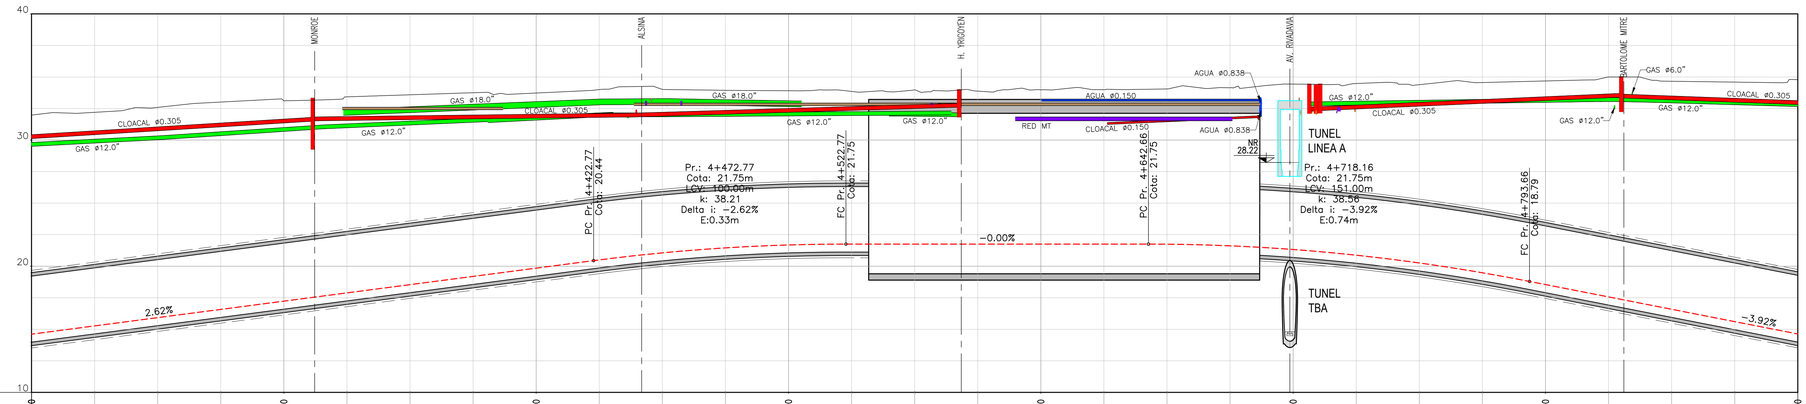

PROGRESIVAS	4+200	4+300	4+400	4+500	4+600	4+700	4+800	4+900
CAMBIO DE VIAS								
COTAS DE TERRENO	31.88 32.20 32.59 33.01 33.11 33.42 33.59 33.75 33.73 34.00 34.01 33.94 33.90 33.86 33.98 33.88 33.98 33.99 34.05 34.14 34.43 34.48 34.39 34.56 34.68 35.00 34.66 34.59 34.73							
COTAS DE PROYECTO	14.61 15.27 15.92 16.68 17.23 17.88 18.54 19.19 19.85 20.50 21.06 21.45 21.68 21.75 21.75 21.75 21.75 21.75 21.74 21.62 21.32 20.87 20.26 19.48 18.55 17.57 16.59 15.61 14.63							
DIFERENCIAS	17.27 16.93 16.67 16.43 15.88 15.54 15.05 14.56 13.88 13.50 12.95 12.49 12.22 12.10 12.23 12.13 12.23 12.24 12.31 12.53 13.11 13.61 14.13 15.08 16.13 17.43 18.07 18.98 20.16							
ALINEACIÓN HORIZONTAL	L=231.36m	=15.00m	L=27.02m R=1745.00m	L=15.00m	L=971.86m			
SECCIÓN	TUNEL TBM				ESTACIÓN CONGRESO CUT & COVER		TUNEL TBM	

REFERENCIAS INTERFERENCIAS:

- RED BT - MT -AT
- RED PLUVIAL
- RED CLOACAL
- RED DE AGUA CORRIENTE
- RED DE GAS
- RED DE FIBRA OPTICA
- RED TELEFÓNICA

NOTAS:

1- SISTEMA DE COORDENADAS DE LA CIUDAD DE BUENOS AIRES.

2- TODAS LAS MEDIDAS ESTÁN EXPRESADAS EN METROS, SALVO INDICACIÓN CONTRARIA

CURVAS HORIZONTALES											
Curva N°	Prog.	X	Y	Rc (m)	Le (m)	Δ	Des (m)	Tan (m)	E (m)	VD (km/h)	PERALTE (mm)
V 10	4+359.69	6555.701	1888.048	1745.00	15.00	1° 22' 47"	57.02	28.51	0.13	90	26

0 5 10m — ESCALA 1:200

0 50m — ESCALA 1:1.000

NOTAS: EL PRESENTE PLANO ES INDICATIVO. LA CONTRATISTA CONFECCIONARA LOS PLANOS DE DETALLE DEFINITIVO, QUE DEBERAN SER APROBADOS POR LA D.G.INF.U.Y LA INSPECCION DE OBRA. EL PLANO PRESENTADO POR LA CONTRATISTA ESTARA EN CONTACTO DE ACUERDO CON LA NORMATIVA VIGENTE.
TODAS LAS MEDIDAS Y NIVELES SE VERIFICARAN EN OBRA POR EL CONTRATISTA.
TODOS LOS DETALLES CONSTRUCTIVOS SERAN COORDINADOS Y COMPATIBILIZADOS EN OBRA.

PLANO NO APTO PARA CONSTRUCCION.

Ing. Mariano Miculicich
DIRECTOR

MODIFICACIONES:

REVISION	FECHA	DESCRIPCION
1	14/01/2026	EMISION INICIAL

MINISTERIO DE INFRAESTRUCTURA
SUBSECRETARIA DE PROYECTOS Y OBRAS
DIRECCION GENERAL DE PROYECTOS

DGPRO

Obra: LINEA F			IF-2026-20223041-GCABA-APRA Plano N°
Plano: TRAZADO DE VÍAS - PLANIALTIMETRÍA VÍA ASCENDENTE - PR. 4+200 A 4+900			LF-VI-T01-VIA-PL-007
Fecha: 14/01/2026	Eq. de Proyecto: UPU-ATEC-IATASA	Dibujó: N.S.	Revisó: G.D.R. Escala: Indicada 007

15/1/2026 09:41 p. m.
U:\-IN-T01-VIA-PL-0001-009 - PLANIALTIMETRIA T1 - VIA ASC.dwg

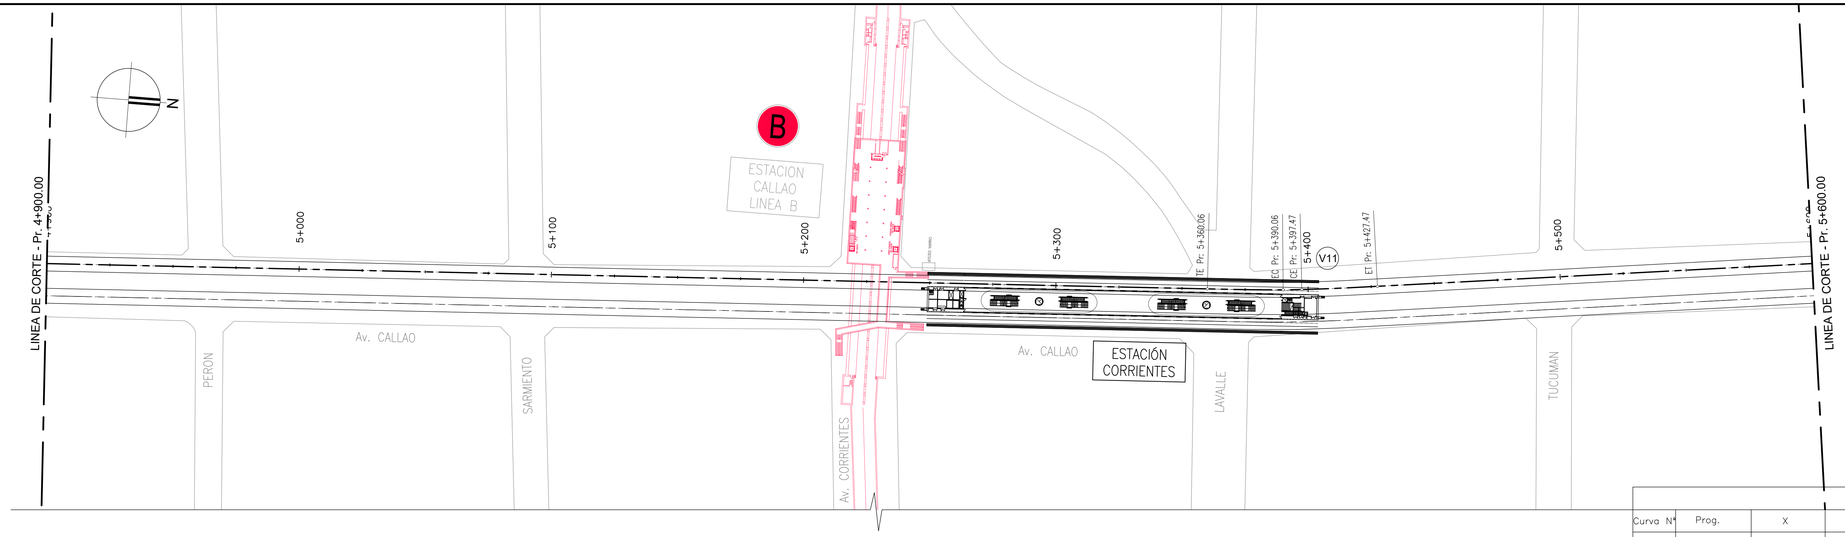

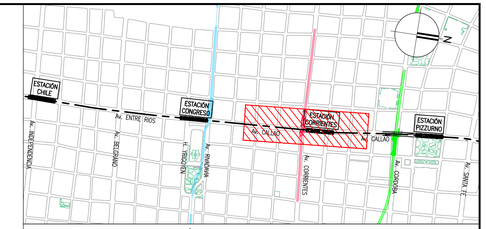

CROQUIS DE UBICACIÓN

CURVAS HORIZONTALES

Curva N°	Prog.	X	Y	Rc (m)	Le (m)	Δ	Des (m)	Tan (m)	E (m)	VD (km/h)	PERALTE (mm)
V 11	5+393.78	6496.486	2920.439	505.00	30.00	4° 14' 39"	67.41	33.72	0.42	75	59

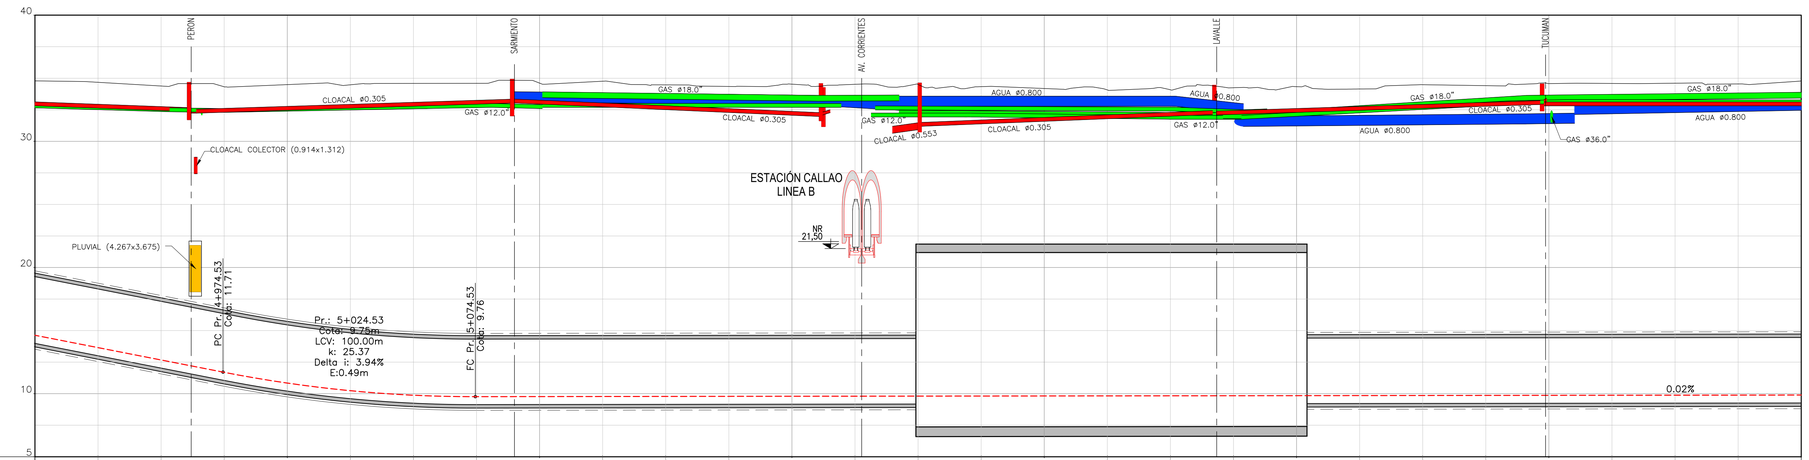

| | | |

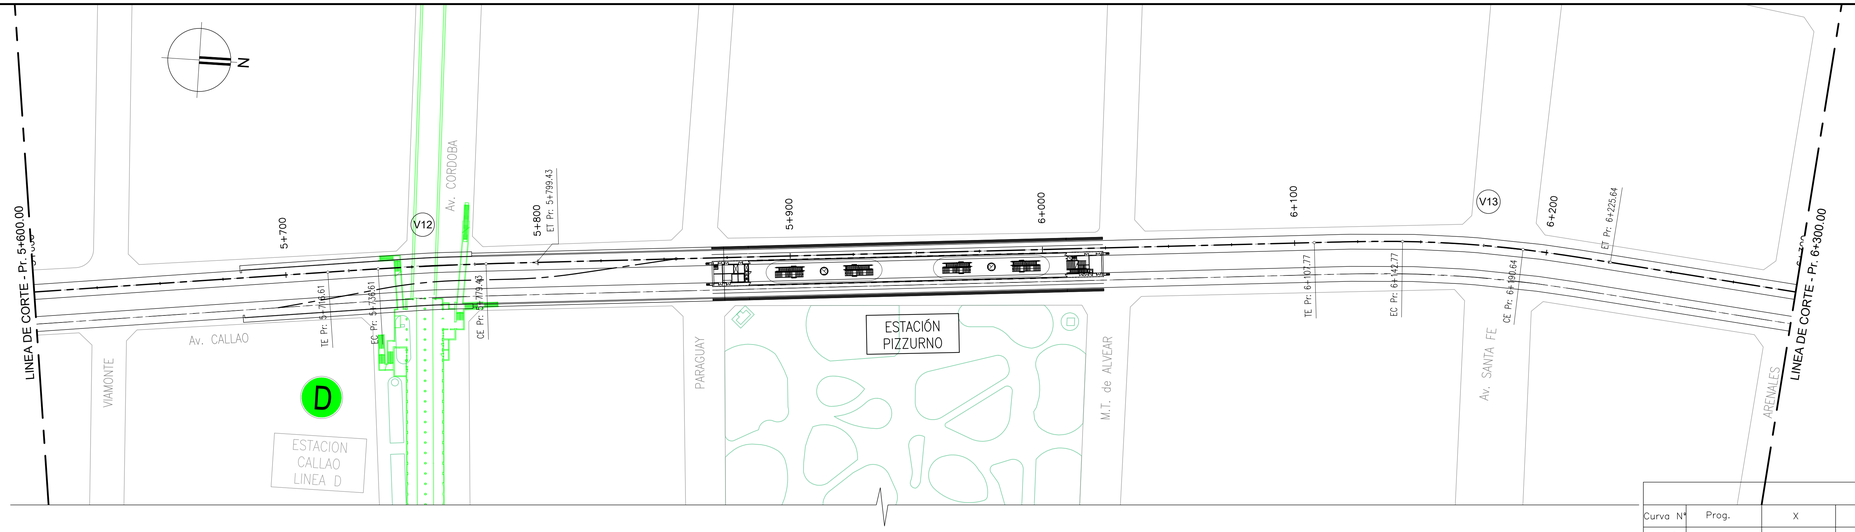

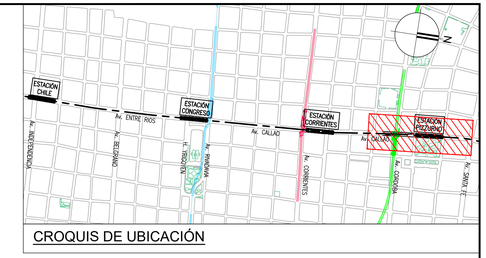

CROQUIS DE UBICACIÓN

CURVAS HORIZONTALES											
Curva N°	Prog.	X	Y	Rc (m)	Le (m)	Δ	Des (m)	Tan (m)	E (m)	VD (km/h)	PERALTE (mm)
V 12	5+758.02	6448.769	3281.566	1495.00	20.00	2° 24' 27"	82.82	41.41	0.34	70	20
V 13	6+166.83	6412.289	3688.750	450.00	35.00	10° 33' 04"	117.87	59.06	2.03	70	67

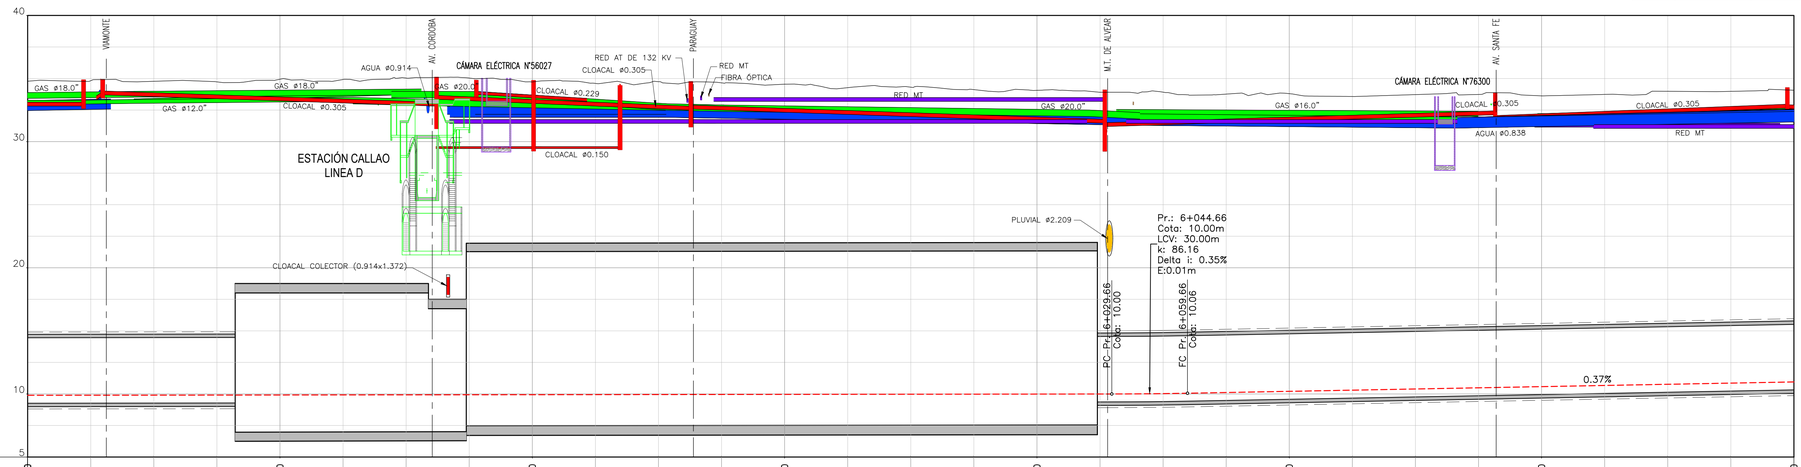

PROGRESIVAS	5+600	5+700	5+800	5+900	6+000	6+100	6+200	6+300
CAMBIO DE VIAS				5+854.7				
COTAS DE TERRENO	34.78 34.83	34.78 34.73	34.94 34.92	35.04 35.04	34.73 34.61	34.75 34.66	34.55 34.28	34.31 34.12
COTAS DE PROYECTO	9.89 9.90	9.90 9.91	9.92 9.92	9.93 9.93	9.94 9.95	9.95 9.96	9.96 9.97	9.98 9.98
DIFERENCIAS	24.89 24.93	24.87 24.82	25.03 25.00	25.11 25.10	24.79 24.67	24.79 24.70	24.59 24.30	24.34 24.14
ALINEACIÓN HORIZONTAL	L=289.14m	L=20.00m	L=42.82m R=1495.00m	L=20.00m	L=308.34m			
SECCIÓN	TUNEL TBM	SECCIÓN ESPECIAL 1	SECCIÓN ESPECIAL 2	EXTENSIÓN CAVERNA ESTACIÓN	ESTACIÓN PIZZURNO CAVERNA			

PROGRESIVAS	6+100	6+200	6+300
CAMBIO DE VIAS			
COTAS DE TERRENO	33.92 33.77	33.80 33.58	33.73 33.74	33.63 33.74	33.99 33.98	34.07
COTAS DE PROYECTO	10.03 10.11	10.21 10.30	10.39 10.49	10.58 10.67	10.77 10.86	10.95
DIFERENCIAS	23.89 23.65	23.59 23.28	23.33 23.25	23.05 23.07	23.22 23.12	23.12
ALINEACIÓN HORIZONTAL	L=35.00m	L=47.87m R=450.00m	L=35.00m	L=146.45m		
SECCIÓN	TUNEL TBM					

REFERENCIAS INTERFERENCIAS:

- RED BT - MT -AT
- RED PLUVIAL
- RED CLOACAL
- RED DE AGUA CORRIENTE
- RED DE GAS
- RED DE FIBRA OPTICA
- RED TELEFÓNICA

NOTAS:

1- SISTEMA DE COORDENADAS DE LA CIUDAD DE BUENOS AIRES.

2- TODAS LAS MEDIDAS ESTÁN EXPRESADAS EN METROS, SALVO INDICACIÓN CONTRARIA

0 5 10m
ESCALA 1:200

0 50m
ESCALA 1:1.000

NOTAS: EL PRESENTE PLANO ES INDICATIVO. LA CONTRATISTA CONFECCIONARA LOS PLANOS DE DETALLE CONSTRUCTIVO, QUE DEBERAN SER APROBADOS POR LA D.G.OBR° LY LA INSPECCION DE OBRA. EL PLANO PRESENTADO POR LA CONTRATISTA ESTARA EN UN TODO DE ACUERDO CON LA NORMATIVA VIGENTE.
TODAS LAS MEDIDAS Y NIVELES SE VERIFICARAN EN OBRA POR EL CONTRATISTA.
TODOS LOS DETALLES CONSTRUCTIVOS SERAN COORDINADOS Y COMPATIBILIZADOS EN OBRA.

PLANO NO APTO PARA CONSTRUCCION.

Ing. Mariano Miculicich
DIRECTOR

MODIFICACIONES:

REVISION	FECHA	DESCRIPCION
0	14/1/2026	EMISION INICIAL

MINISTERIO DE INFRAESTRUCTURA
SUBSECRETARIA DE PROYECTOS Y OBRAS
DIRECCION GENERAL DE PROYECTOS

DGPRO

Obra: LINEA F
Plano: TRAZADO DE VÍAS - PLANIALTIMETRÍA VÍA ASCENDENTE - PR. 5+600 A 6+300
Fecha: 14/01/2026 | Eq. de Proyecto: UPU-ATEC-IATASA | Dibujó: N.S. | Revisó: G.D.R. | Escala: Indicada

IF-2026-20223041-GCABA-APRA | Plano N° 009 | LF-VI-T01-VIA-PL-009

15/1/2026 09:41 a. m.
LF-VI-T01-VIA-PL-001-009 - PLANIALTIMETRIA T1 - VIA ASC.dwg

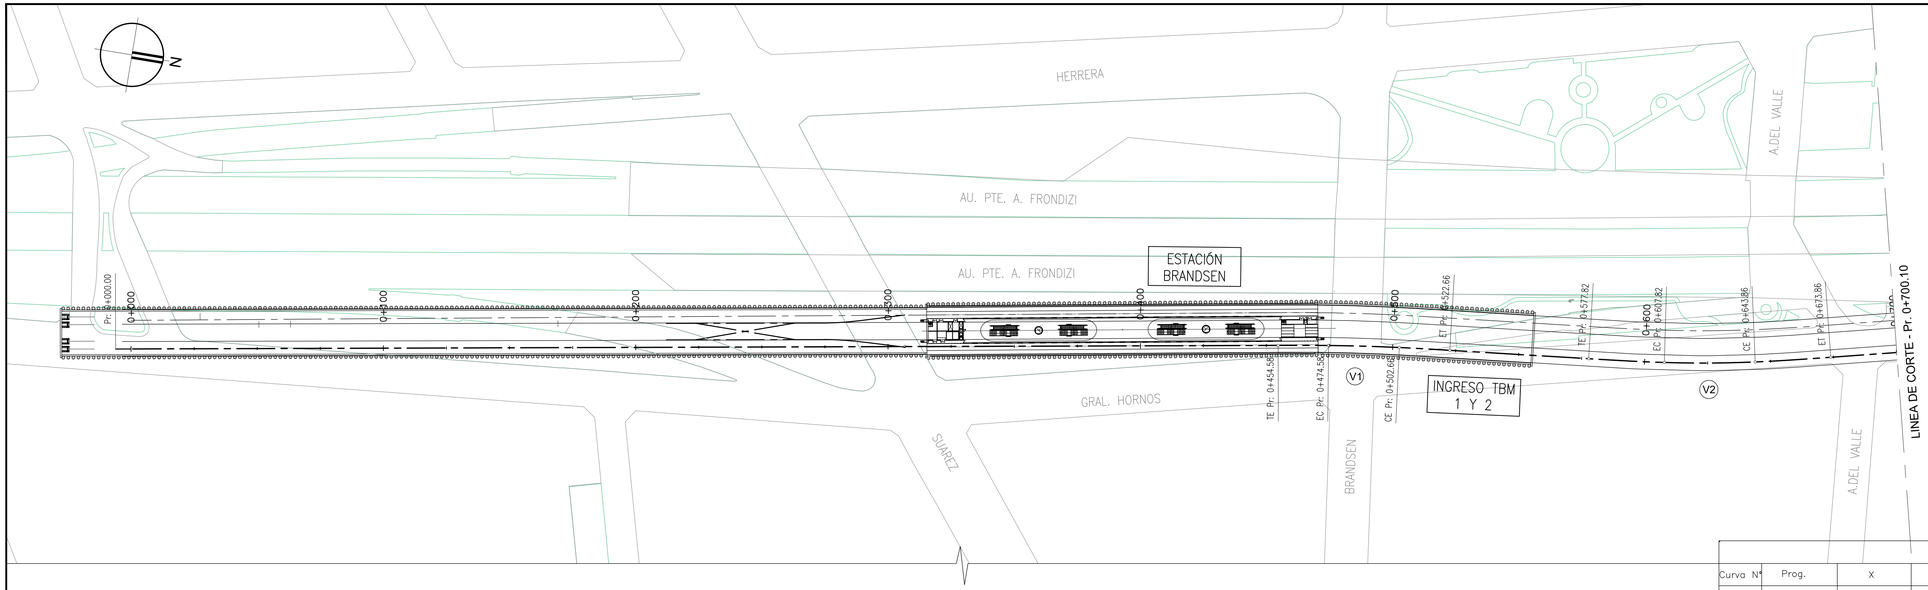

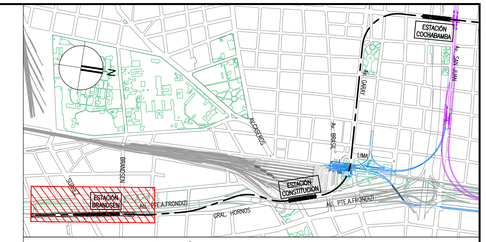

CROQUIS DE UBICACIÓN

CURVAS HORIZONTALES

Curva Nº	Prog.	X	Y	Rc (m)	Le (m)	Δ	Des (m)	Tan (m)	E (m)	VD (km/h)	PERALTE (mm)
V 1	0+488.63	7966.552	−970.439	760.00	20.00	3° 37' 28"	68.08	34.05	0.40	70	39
V 2	0+625.89	7952.274	−833.906	500.00	30.00	7° 34' 04"	96.04	48.07	1.17	70	60

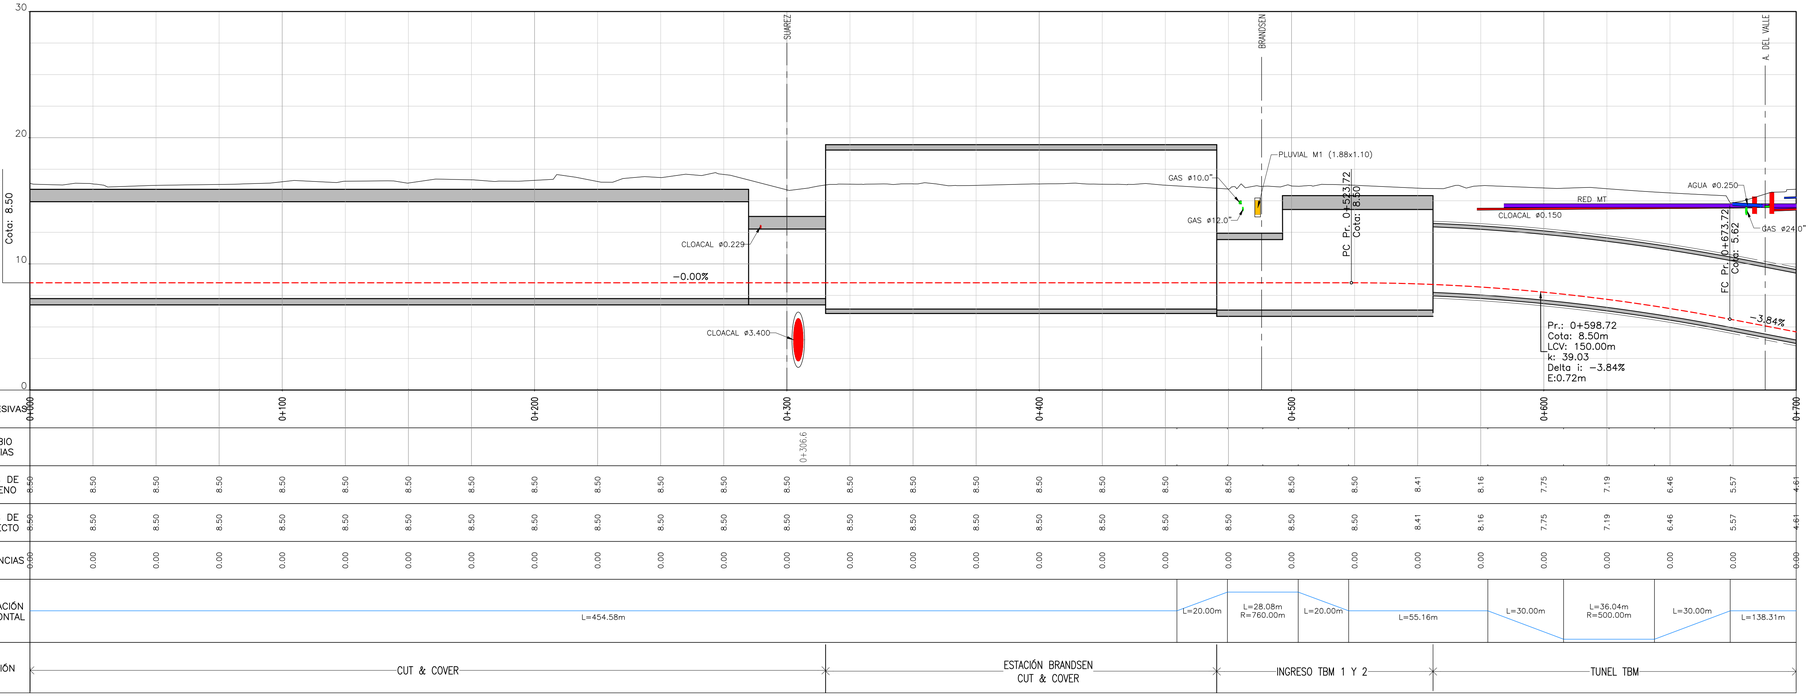

REFERENCIAS INTERFERENCIAS:

- RED BT - MT -AT
- RED PLUVIAL
- RED CLOACAL
- RED DE AGUA CORRIENTE
- RED DE GAS
- RED DE FIBRA OPTICA
- RED TELEFÓNICA

NOTAS:

1- SISTEMA DE COORDENADAS DE LA CIUDAD DE BUENOS AIRES.

2- TODAS LAS MEDIDAS ESTÁN EXPRESADAS EN METROS, SALVO INDICACIÓN CONTRARIA

0 5 10m
ESCALA 1:200

0 50m
ESCALA 1:1.000

NOTAS: EL PRESENTE PLANO ES INDICATIVO. LA CONTRATISTA CONFECCIONARA LOS PLANOS DE DETALLE DEFINITIVO, QUE DEBERAN SER APROBADOS POR LA D.G.OBR Nº 1 A LA INSPECCION DE OBRA. EL PLANO PRESENTADO POR LA CONTRATISTA ESTARA EN UN TODO DE ACUERDO CON LA NORMATIVA VIGENTE.
TODAS LAS MEDIDAS Y NIVELES SE VERIFICARAN EN OBRA POR EL CONTRATISTA.
TODOS LOS DETALLES CONSTRUCTIVOS DEBRAN COORDINADOS Y CONPATIBILIZADOS EN OBRA.

PLANO NO APTO PARA CONSTRUCCION

Ing. Mariano Miculicich
DIRECTOR

MODIFICACIONES:

REVISION	FECHA	DESCRIPCION
0	14/01/2026	EMISIÓN INICIAL

MINISTERIO DE INFRAESTRUCTURA
SUBSECRETARIA DE PROYECTOS Y OBRAS
DIRECCION GENERAL DE PROYECTOS

DGPRO

Obra: LINEA F — IF-2026-20223041-GCABA-APRA — Plano Nº 010

Plano: TRAZADO DE VÍAS - PLANIALTIMETRÍA VÍA DESCENDENTE - PR. 0+000 A 0+700 — LF-VI-T01-VIA-PL-010

Fecha: 14/01/2026 | Eq. de Proyecto: UPU-ATEC-IATASA | Dibujó: N.S. | Revisó: G.D.R. | Escala: Indicada

14/1/2026 16:49 p. m.
LF-VI-T01-VIA-PL-010-018 - PLANIALTIMETRIA T1 - VIA DESC.dwg

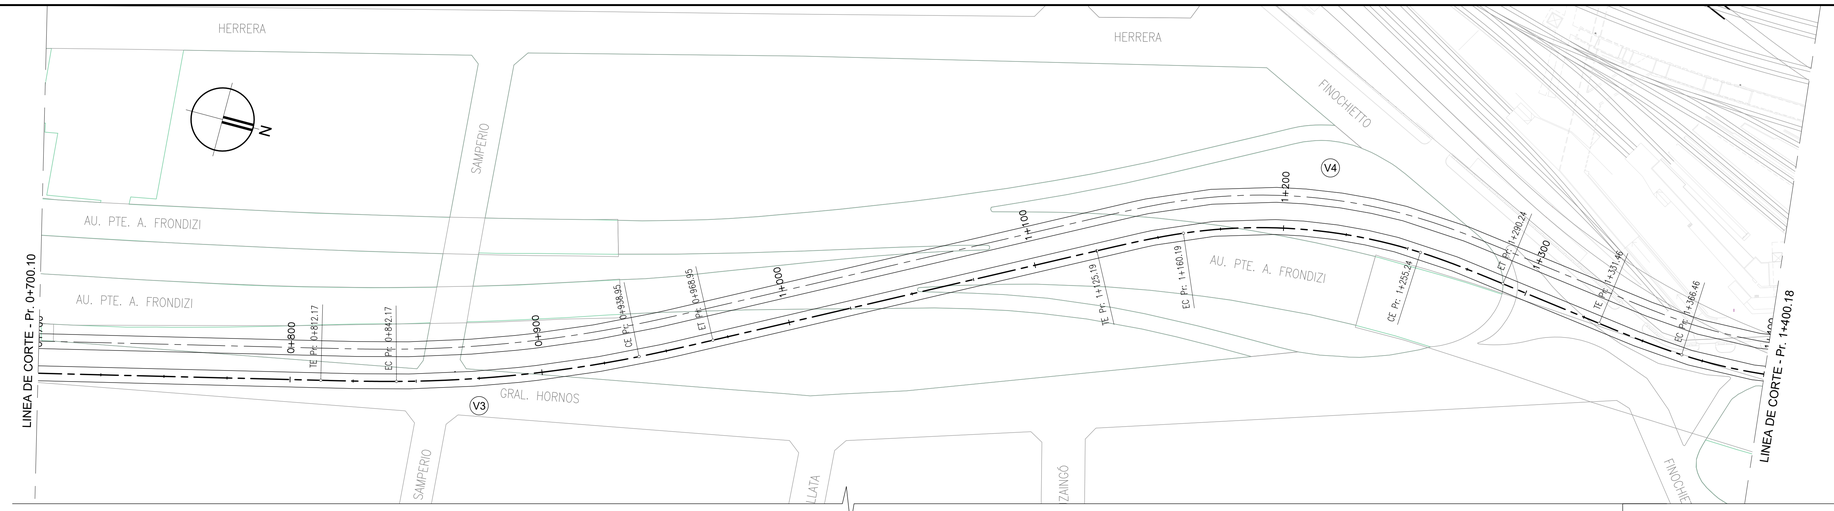

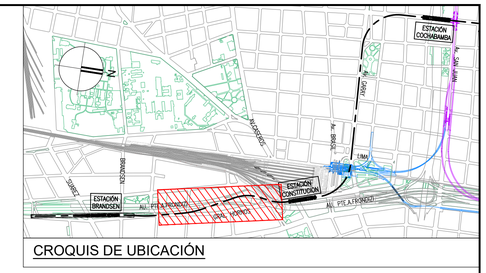

CROQUIS DE UBICACIÓN

CURVAS HORIZONTALES											
Curva Nº	Prog.	X	Y	Rc (m)	Le (m)	Δ	Des (m)	Tan (m)	E (m)	VD (km/h)	PERALTE (mm)
V 3	0+890.91	7890.211	−576.148	500.00	30.00	14° 31' 44"	156.79	78.74	4.12	70	60
V 4	1+209.95	7739.773	−294.009	210.00	35.00	35° 28' 54"	165.05	84.76	10.74	45	70

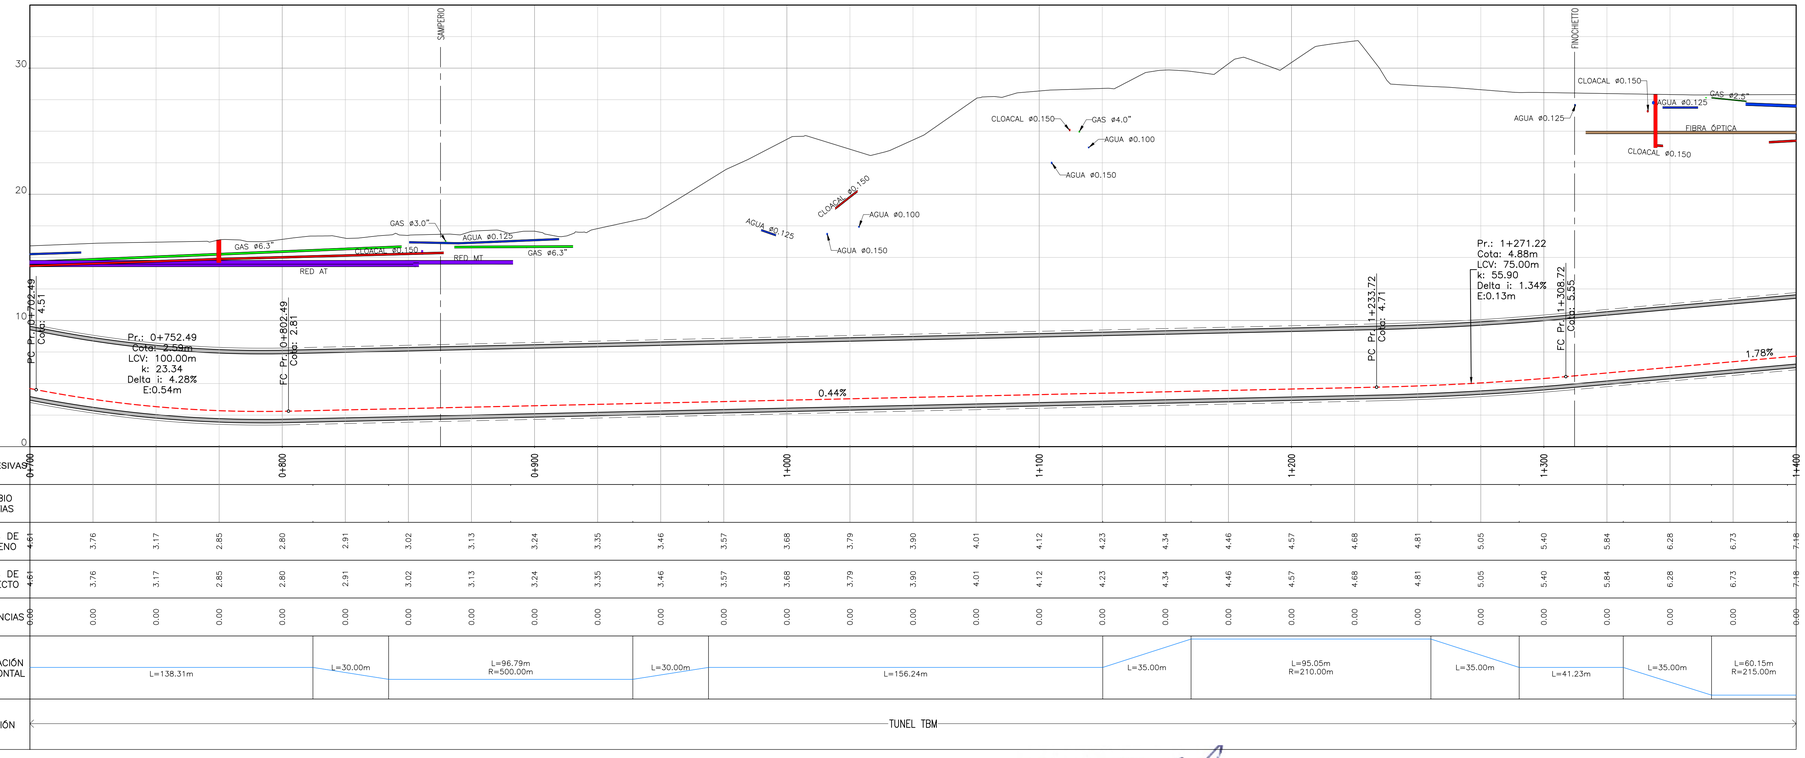

	0+700	0+800	0+900	1+000	1+100	1+200	1+300	1+400
PROGRESIVAS								
CAMBIO DE VIAS								
COTAS DE TERRENO	4.61 3.76 3.17 2.85 2.80 2.91 3.02 3.13 3.24 3.35 3.46 3.57 3.68 3.79 3.90 4.01 4.12 4.23 4.34 4.46 4.57 4.68 4.81 5.05 5.40 5.84 6.28 6.73 7.18							
COTAS DE PROYECTO	4.61 3.76 3.17 2.85 2.80 2.91 3.02 3.13 3.24 3.35 3.46 3.57 3.68 3.79 3.90 4.01 4.12 4.23 4.34 4.46 4.57 4.68 4.81 5.05 5.40 5.84 6.28 6.73 7.18							
DIFERENCIAS	0.00 0.00 0.00 0.00 0.00 0.00 0.00 0.00 0.00 0.00 0.00 0.00 0.00 0.00 0.00 0.00 0.00 0.00 0.00 0.00 0.00 0.00 0.00 0.00 0.00 0.00 0.00 0.00 0.00							
ALINEACIÓN HORIZONTAL	L=138.31m	L=30.00m	L=96.79m R=500.00m	L=30.00m	L=156.24m	L=35.00m	L=95.05m R=210.00m	L=35.00m	L=41.23m	L=35.00m	L=60.15m R=215.00m
SECCIÓN	TUNEL TBM							

REFERENCIAS INTERFERENCIAS:

- RED BT - MT -AT
- RED DE GAS
- RED PLUVIAL
- RED DE FIBRA OPTICA
- RED CLOACAL
- RED TELEFÓNICA
- RED DE AGUA CORRIENTE

NOTAS:

1- SISTEMA DE COORDENADAS DE LA CIUDAD DE BUENOS AIRES.

2- TODAS LAS MEDIDAS ESTÁN EXPRESADAS EN METROS, SALVO INDICACIÓN CONTRARIA

0 5 10m — ESCALA 1:200

0 50m — ESCALA 1:1.000

NOTAS: EL PRESENTE PLANO ES INDICATIVO. LA CONTRATISTA CONFECCIONARA LOS PLANOS DE DETALLE DEFINITIVO, QUE DEBERAN SER APROBADOS POR LA D.G.INF.U.Y LA INSPECCION DE OBRA. EL PLANO PRESENTADO POR LA CONTRATISTA ESTARA EN SU TODO DE ACUERDO CON LA NORMATIVA VIGENTE.
TODAS LAS MEDIDAS Y NIVELES SE VERIFICARAN EN OBRA POR EL CONTRATISTA.
TODOS LOS DETALLES CONSTRUCTIVOS SERAN COORDINADOS Y COMPATIBILIZADOS EN OBRA.

PLANO NO APTO PARA CONSTRUCCION

Ing. Mariano Miculicich
DIRECTOR

MODIFICACIONES:

REVISION	FECHA	DESCRIPCION
1	14/01/2026	EMISION INICIAL

MINISTERIO DE INFRAESTRUCTURA
SUBSECRETARIA DE PROYECTOS Y OBRAS
DIRECCION GENERAL DE PROYECTOS

DGPRO

Obra: LINEA F
IF-2026-20223041-GCABA-APRA
Plano Nº 011
Plano: TRAZADO DE VÍAS - PLANIALTIMETRÍA VÍA DESCENDENTE - PR. 0+700 A 1+400
LF-VI-T01-VIA-PL-011
Fecha: 14/01/2026 | Eq. de Proyecto: UPU-ATEC-IATASA | Dibujó: N.S. | Revisó: G.D.R. | Escala: Indicada

14/1/2026 16:49 p. m.
LF-VI-T01-VIA-PL-010-018 - PLANIALTIMETRIA 11 - VIA DESC.dwg

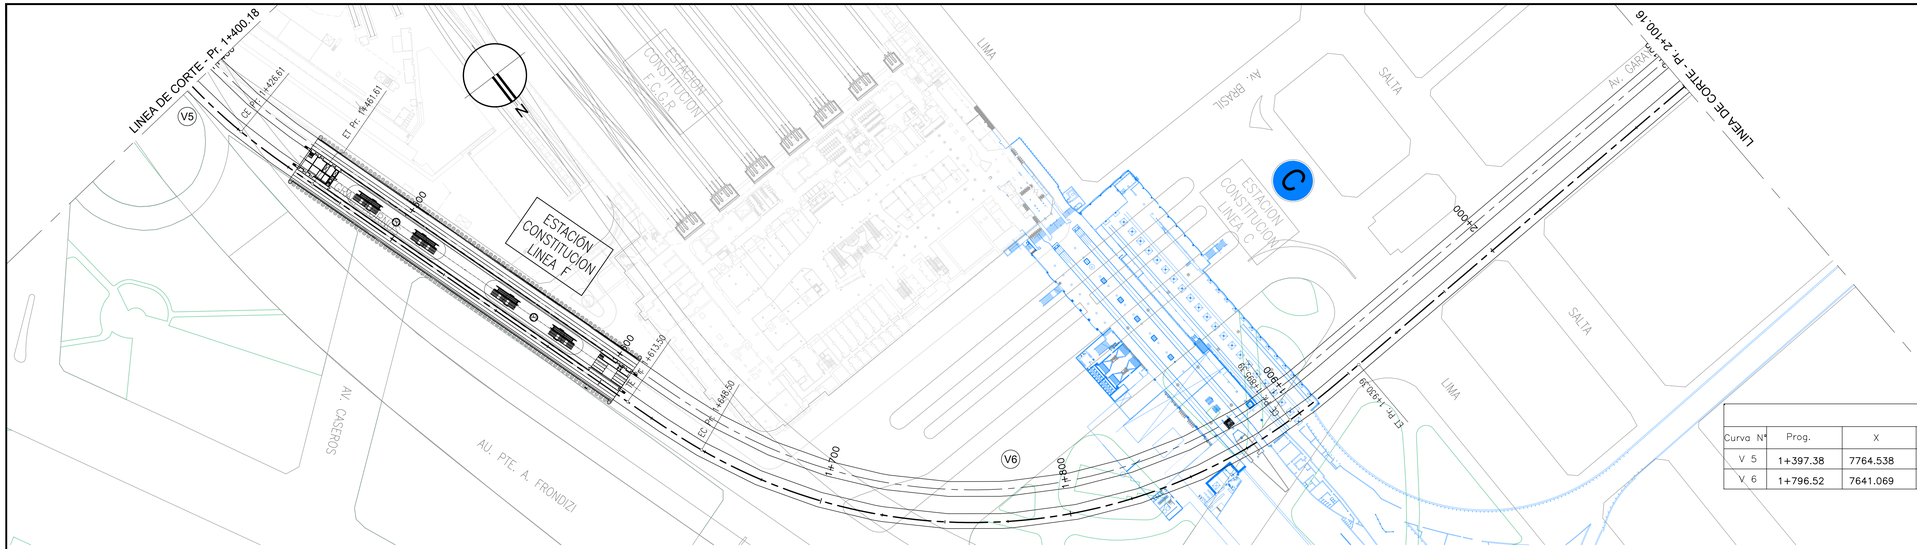

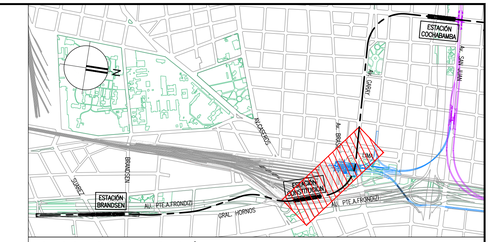

CROQUIS DE UBICACIÓN

CURVAS HORIZONTALES

Curva N°	Prog.	X	Y	Rc (m)	Le (m)	Δ	Des (m)	Tan (m)	E (m)	VD (km/h)	PERALTE (mm)
V 5	1+397.38	7764.538	−103.714	215.00	35.00	25° 21' 22"	130.15	65.92	5.62	45	70
V 6	1+796.52	7641.069	277.614	215.00	35.00	75° 07' 19"	316.89	183.02	56.52	45	70

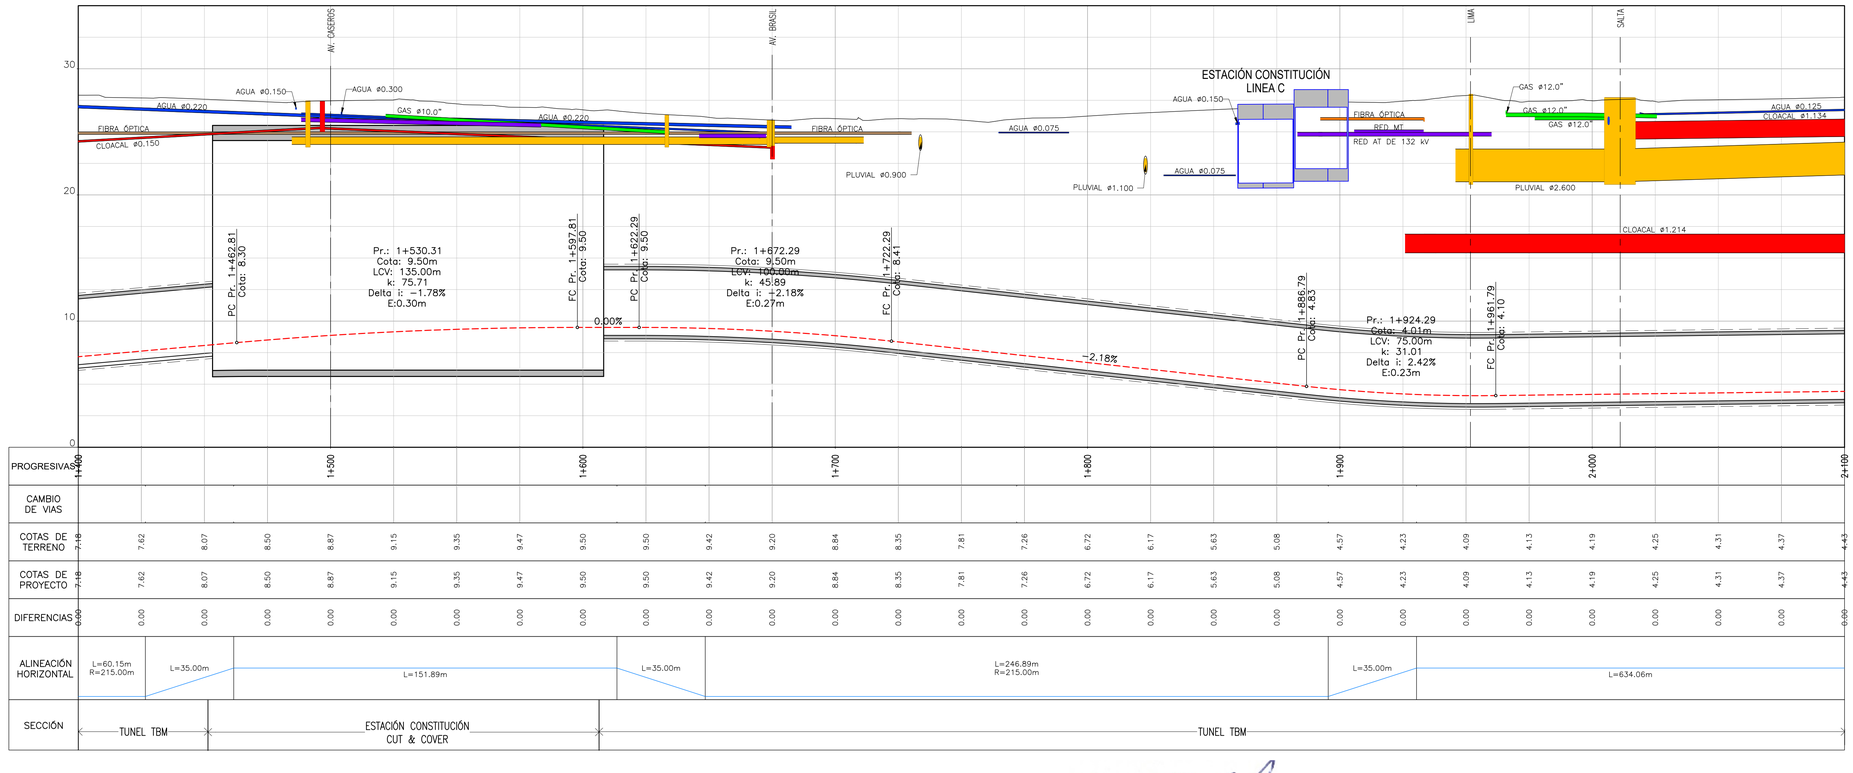

PROGRESIVAS	1+400	1+500	1+600	1+700	1+800	1+900	2+000	2+100
CAMBIO DE VIAS								
COTAS DE TERRENO	7.18 7.62 8.07 8.50 8.87 9.15 9.35 9.47 9.50 9.50 9.42 9.20 8.84 8.35 7.81 7.26 6.72 6.17 5.63 5.08 4.57 4.23 4.09 4.13 4.19 4.25 4.31 4.37 4.43							
COTAS DE PROYECTO	7.18 7.62 8.07 8.50 8.87 9.15 9.35 9.47 9.50 9.50 9.42 9.20 8.84 8.35 7.81 7.26 6.72 6.17 5.63 5.08 4.57 4.23 4.09 4.13 4.19 4.25 4.31 4.37 4.43							
DIFERENCIAS	0.00 0.00 0.00 0.00 0.00 0.00 0.00 0.00 0.00 0.00 0.00 0.00 0.00 0.00 0.00 0.00 0.00 0.00 0.00 0.00 0.00 0.00 0.00 0.00 0.00 0.00 0.00 0.00 0.00							
ALINEACIÓN HORIZONTAL	L=60.15m R=215.00m	L=35.00m	L=151.89m	L=35.00m	L=246.89m R=215.00m	L=35.00m	L=634.06m	
SECCIÓN	TUNEL TBM	ESTACIÓN CONSTITUCIÓN CUT & COVER			TUNEL TBM			

REFERENCIAS INTERFERENCIAS:

- RED BT - MT -AT
- RED PLUVIAL
- RED CLOACAL
- RED DE AGUA CORRIENTE
- RED DE GAS
- RED DE FIBRA OPTICA
- RED TELEFÓNICA

NOTAS:

1- SISTEMA DE COORDENADAS DE LA CIUDAD DE BUENOS AIRES.

2- TODAS LAS MEDIDAS ESTÁN EXPRESADAS EN METROS, SALVO INDICACIÓN CONTRARIA

0 5 10m
ESCALA 1:200

0 50m
ESCALA 1:1.000

NOTAS: EL PRESENTE PLANO ES INDICATIVO. LA CONTRATISTA CONFECCIONARA LOS PLANOS DE DETALLE DEFINITIVO, QUE DEBERAN SER APROBADOS POR LA D.G.D.M.P. Y LA INSPECCION DE OBRA. EL PLANO PRESENTADO POR LA CONTRATISTA ESTARA EN UN TODO DE ACUERDO CON LA NORMATIVA VIGENTE. TODAS LAS MEDIDAS Y NIVELES SE VERIFICARAN EN OBRA POR EL CONTRATISTA. TODOS LOS DETALLES CONSTRUCTIVOS SERAN COORDINADOS Y COMPATIBILIZADOS EN OBRA.

PLANO NO APTO PARA CONSTRUCCION

Ing. Mariano Miculicich
DIRECTOR

MODIFICACIONES:

REVISION	FECHA	DESCRIPCION
0	14/01/2026	EMISIÓN INICIAL

MINISTERIO DE INFRAESTRUCTURA
SUBSECRETARIA DE PROYECTOS Y OBRAS
DIRECCION GENERAL DE PROYECTOS

DGPRO

Obra: LINEA F
IF-2026-20223041-GCABA-APRA
Plano N°: 012
Plano: TRAZADO DE VÍAS - PLANIALTIMETRÍA VÍA DESCENDENTE - PR. 1+400 A 2+100
LF-VI-T01-VIA-PL-012
Fecha: 14/01/2026 | Eq. de Proyecto: UPU-ATEC-IATASA | Dibujó: N.S. | Revisó: G.D.R. | Escala: Indicada

14/1/2026 16:49 p. m.
LF-VI-T01-VIA-PL-010-018 - PLANIALTIMETRIA T1 - VIA DESC.dwg

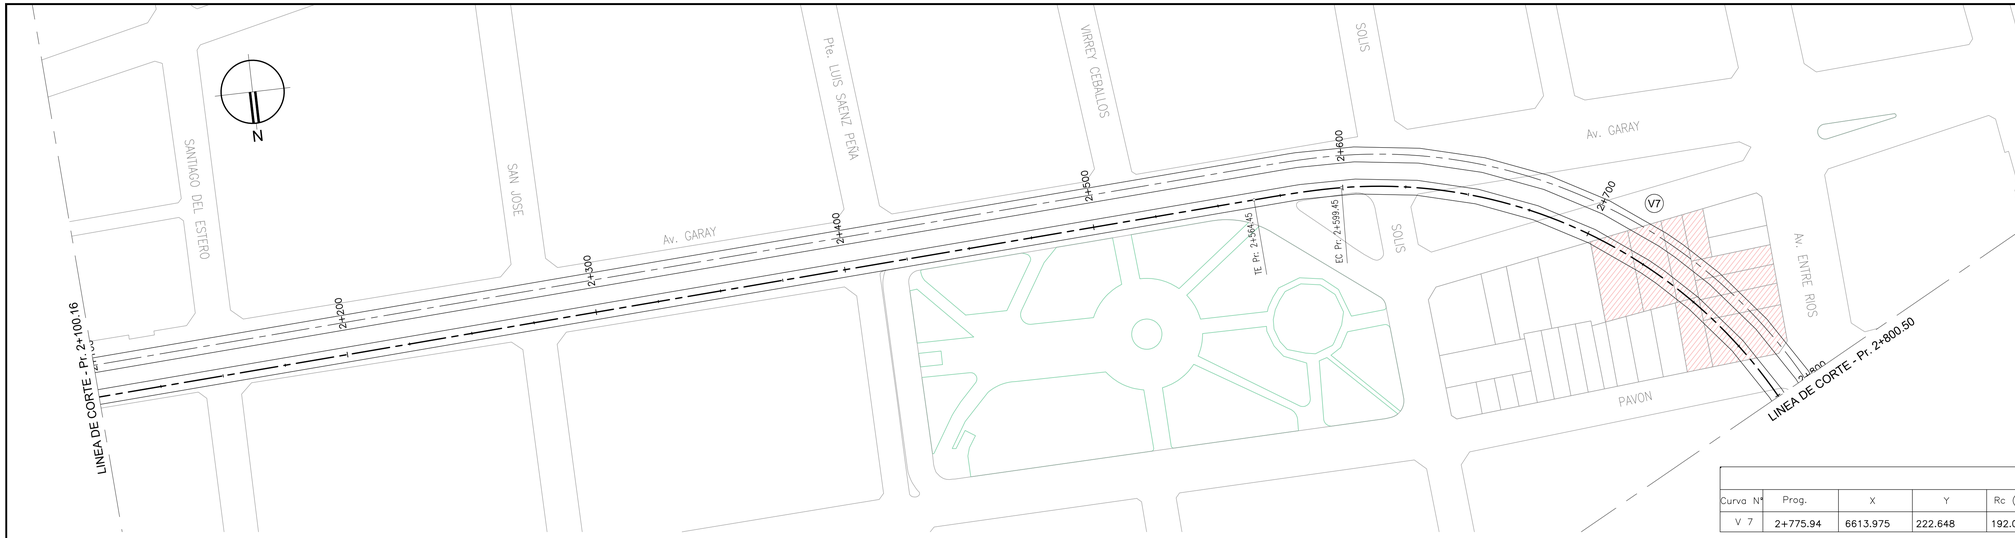

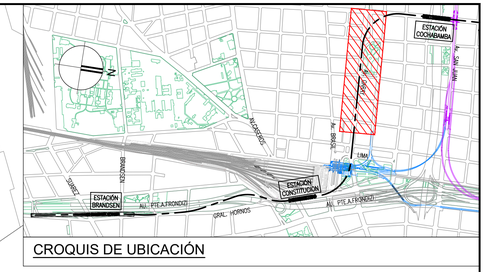

CROQUIS DE UBICACIÓN

CURVAS HORIZONTALES											
Curva Nº	Prog.	X	Y	Rc (m)	Le (m)	Δ	Des (m)	Tan (m)	E (m)	VD (km/h)	PERALTE (mm)
V 7	2+775.94	6613.975	222.648	192.00	35.00	90° 30' 40"	338.31	211.48	81.13	45	70

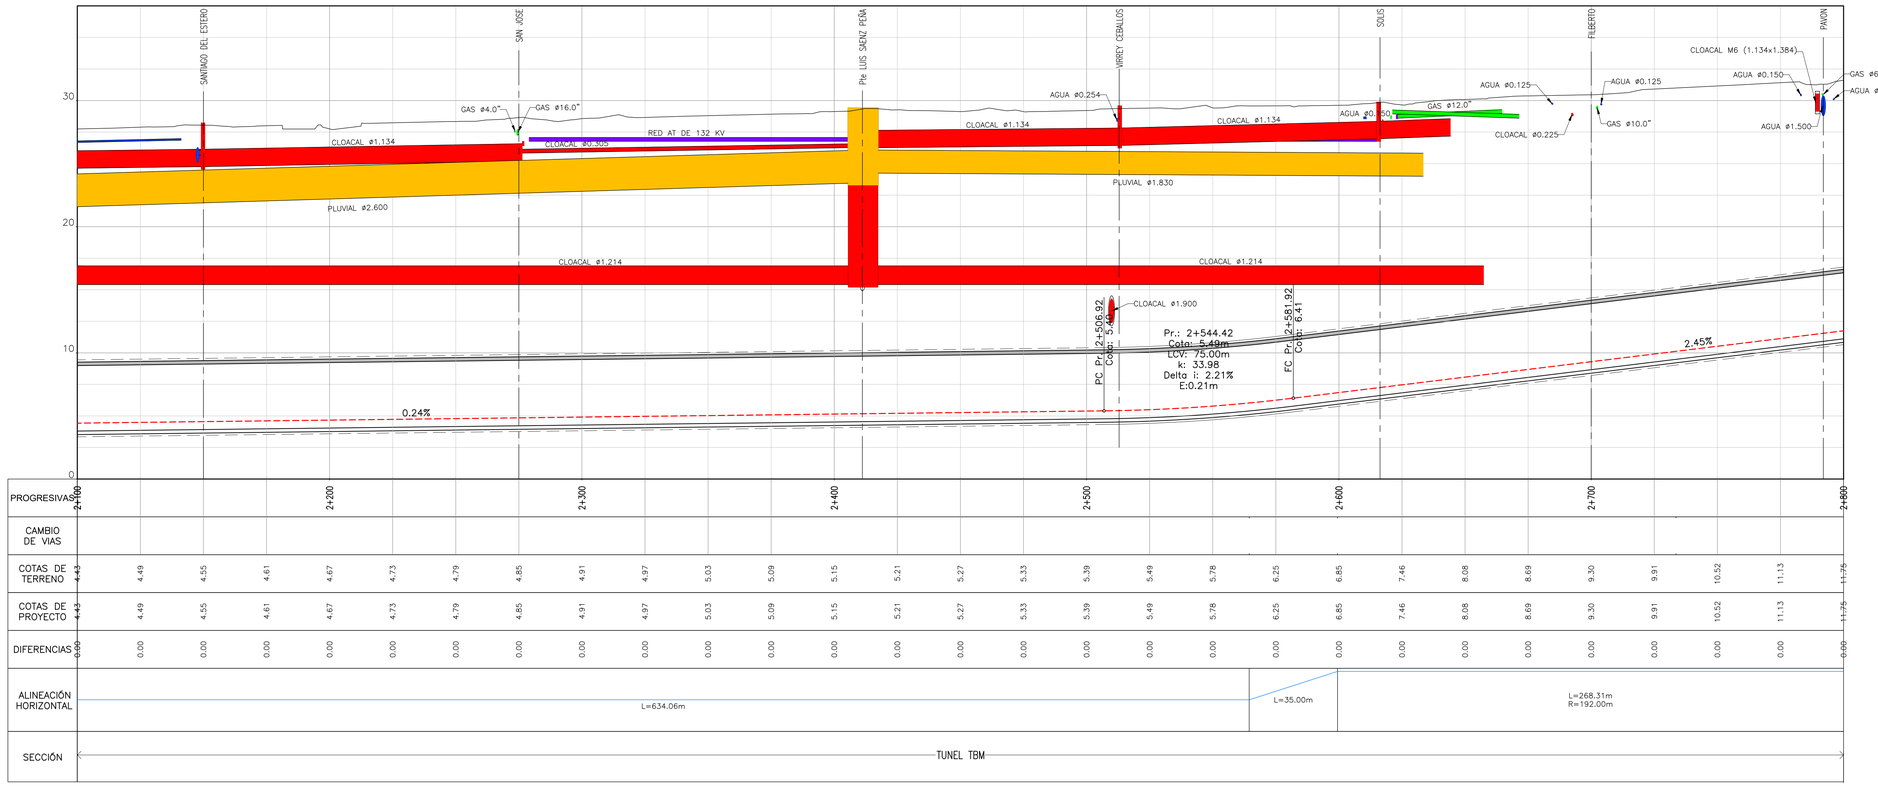

PROGRESIVAS	2+100	2+200	2+300	2+400	2+500	2+600	2+700	2+800
CAMBIO DE VIAS								
COTAS DE TERRENO	4.43	4.49 4.55 4.61 4.67 4.73 4.79 4.85 4.91 4.97 5.03 5.09 5.15 5.21 5.27 5.33 5.39 5.49 5.78 6.25 6.85 7.46 8.08 8.69 9.30 9.91 10.52 11.13						11.75
COTAS DE PROYECTO	4.43	4.49 4.55 4.61 4.67 4.73 4.79 4.85 4.91 4.97 5.03 5.09 5.15 5.21 5.27 5.33 5.39 5.49 5.78 6.25 6.85 7.46 8.08 8.69 9.30 9.91 10.52 11.13						11.75
DIFERENCIAS	0.00	0.00 0.00 0.00 0.00 0.00 0.00 0.00 0.00 0.00 0.00 0.00 0.00 0.00 0.00 0.00 0.00 0.00 0.00 0.00 0.00 0.00 0.00 0.00 0.00 0.00 0.00 0.00 0.00						0.00
ALINEACIÓN HORIZONTAL		L=634.06m				L=35.00m	L=268.31m R=192.00m	
SECCIÓN		TUNEL TBM						

REFERENCIAS INTERFERENCIAS:

- RED BT - MT -AT
- RED PLUVIAL
- RED CLOACAL
- RED DE AGUA CORRIENTE
- RED DE GAS
- RED DE FIBRA OPTICA
- RED TELEFÓNICA

NOTAS:

1- SISTEMA DE COORDENADAS DE LA CIUDAD DE BUENOS AIRES.

2- TODAS LAS MEDIDAS ESTÁN EXPRESADAS EN METROS, SALVO INDICACIÓN CONTRARIA

0 5 10m
ESCALA 1:200

0 50m
ESCALA 1:1.000

NOTAS: EL PRESENTE PLANO ES INDICATIVO. LA CONTRATISTA CONFECCIONARA LOS PLANOS DE DETALLE DEFINITIVO, QUE DEBERAN SER APROBADOS POR LA D.G.ING.Y.V.U.A. INSPECCION DE OBRA. EL PLANO PRESENTADO POR LA CONTRATISTA ESTARA EN TODO DE ACUERDO CON LA NORMATIVA VIGENTE. TODAS LAS MEDIDAS Y NIVELES SE VERIFICARAN EN OBRA POR EL CONTRATISTA. TODOS LOS DETALLES CONSTRUCTIVOS SERAN COORDINADOS Y COMPATIBILIZADOS EN OBRA

PLANO NO APTO PARA CONSTRUCCION

Ing. Mariano Miculicich
DIRECTOR

MODIFICACIONES:	REVISION	FECHA	DESCRIPCION
	0	14/1/2026	EMISIÓN INICIAL
	1		

MINISTERIO DE INFRAESTRUCTURA
SUBSECRETARIA DE PROYECTOS Y OBRAS
DIRECCION GENERAL DE PROYECTOS

DGPRO

Obra: LÍNEA F
IF-2026-20223041-GCABA-APRA
Plano Nº 013
Plano: TRAZADO DE VÍAS - PLANIALTIMETRÍA VÍA DESCENDENTE - PR. 2+100 A 2+800
LF-VI-T01-VIA-PL-013
Fecha: 14/01/2026 | Eq. de Proyecto: UPU-ATEC-IATASA | Dibujó: N.S. | Revisó: G.D.R. | Escala: Indicada

14/1/2026 16:49 p. m.
LF-VI-T01-VIA-PL-013-018 - PLANIALTIMETRIA T1 - VIA DESC.dwg

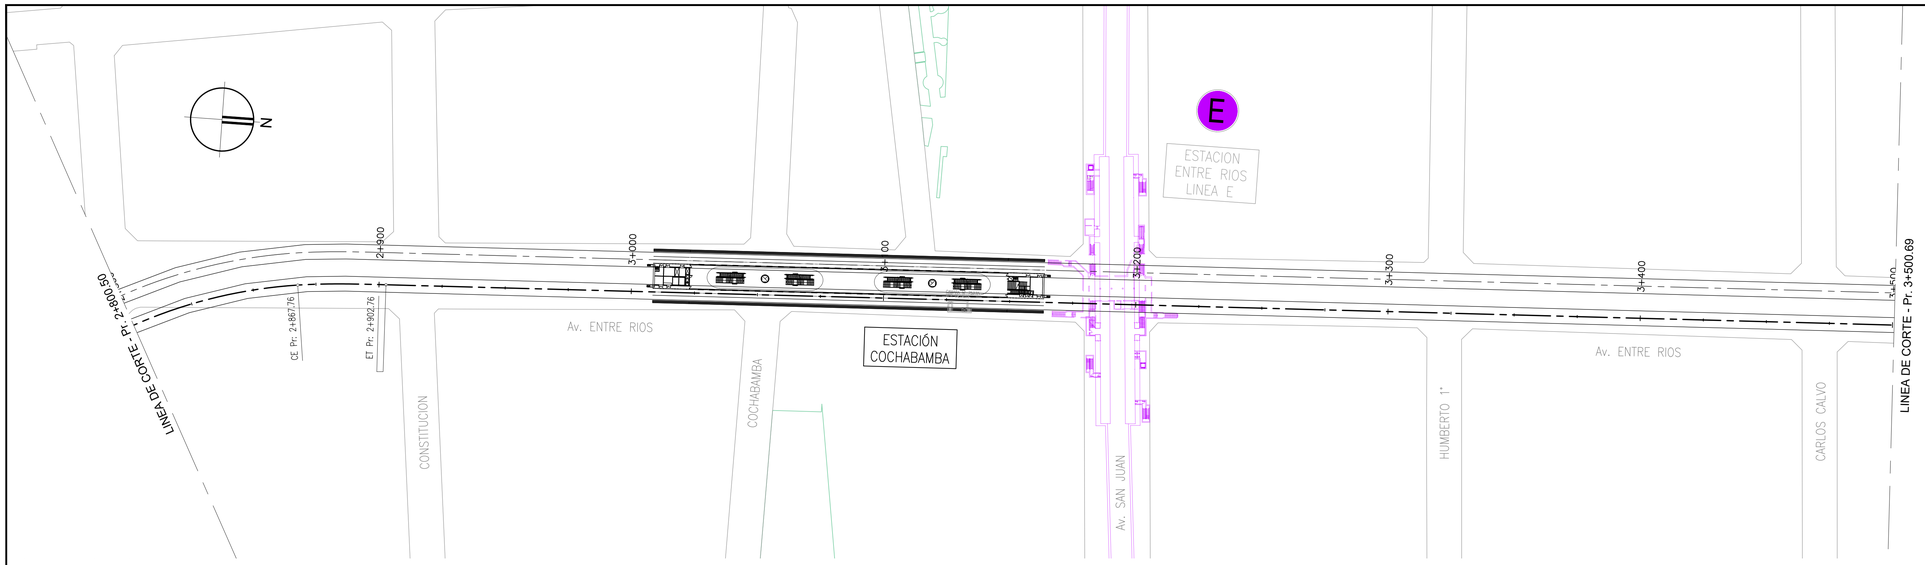

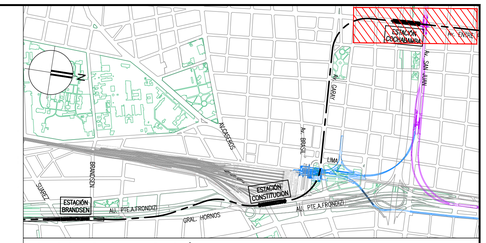

CROQUIS DE UBICACIÓN

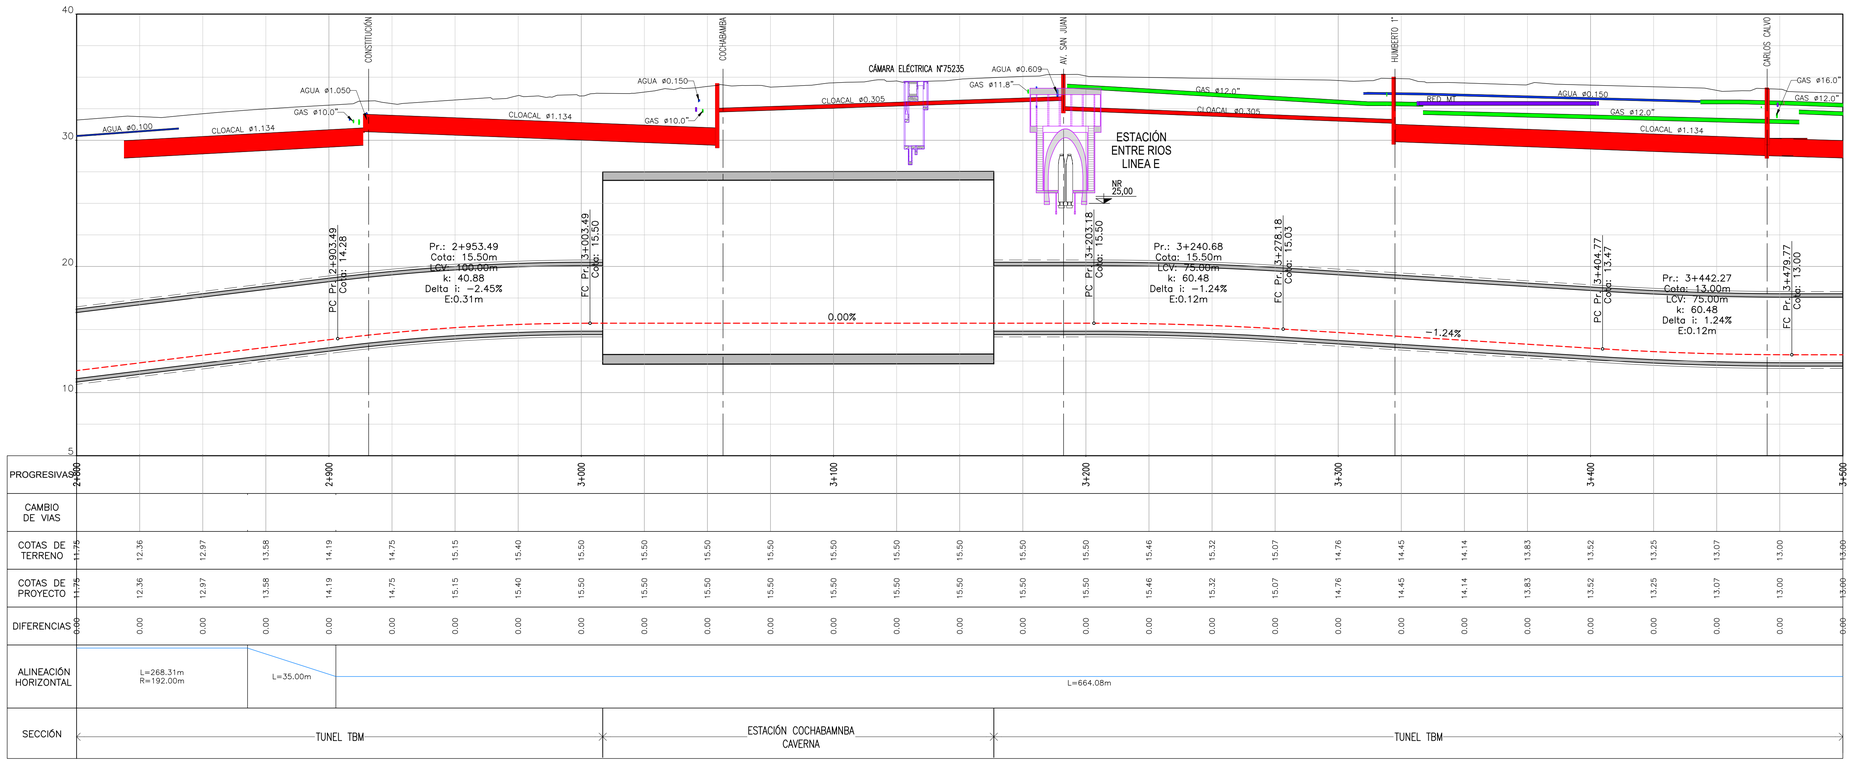

REFERENCIAS INTERFERENCIAS:

- RED BT - MT -AT
- RED PLUVIAL
- RED CLOACAL
- RED DE AGUA CORRIENTE
- RED DE GAS
- RED DE FIBRA OPTICA
- RED TELEFÓNICA

NOTAS:

1- SISTEMA DE COORDENADAS DE LA CIUDAD DE BUENOS AIRES.

2- TODAS LAS MEDIDAS ESTÁN EXPRESADAS EN METROS, SALVO INDICACIÓN CONTRARIA

ESCALA 1:200

ESCALA 1:1.000

NOTAS: EL PRESENTE PLANO ES INDICATIVO. LA CONTRATISTA CONFECCIONARA LOS PLANOS DE DETALLE DEFINITIVO, QUE DEBERAN SER APROBADOS POR LA D.G.SMT.Y LA INSPECCION DE OBRA. EL PLANO PRESENTADO POR LA CONTRATISTA ESTARA EN UN TODO DE ACUERDO CON LA NORMATIVA VIGENTE.
TODAS LAS MEDIDAS Y NIVELES SE VERIFICARAN EN OBRA POR EL CONTRATISTA.
TODOS LOS DETALLES CONSTRUCTIVOS DEBRAN COORDINADOS Y CONSENSUADOS EN OBRA

PLANO NO APTO PARA CONSTRUCCION

Ing. Mariano Miculicich
DIRECTOR

MODIFICACIONES:

REVISION	FECHA	DESCRIPCION
0	14/01/2026	EMISIÓN INICIAL

MINISTERIO DE INFRAESTRUCTURA
SUBSECRETARIA DE PROYECTOS Y OBRAS
DIRECCION GENERAL DE PROYECTOS

DGPRO

Obra: LINEA F			IF-2026-20223041-GCABA-APRA	Plano N°
Plano: TRAZADO DE VÍAS - PLANIALTIMETRÍA VÍA DESCENDENTE - PR. 2+800 A 3+500			LF-VI-T01-VIA-PL-014	014
Fecha: 14/01/2026	Eq. de Proyecto: UPU-ATEC-IATASA	Dibujó: N.S.	Revisó: G.D.R.	Escala: Indicada

14/1/2026 16:49 p. m.
LF-VI-T01-VIA-PL-010-018 - PLANIALTIMETRIA T1 - VIA DESC.dwg

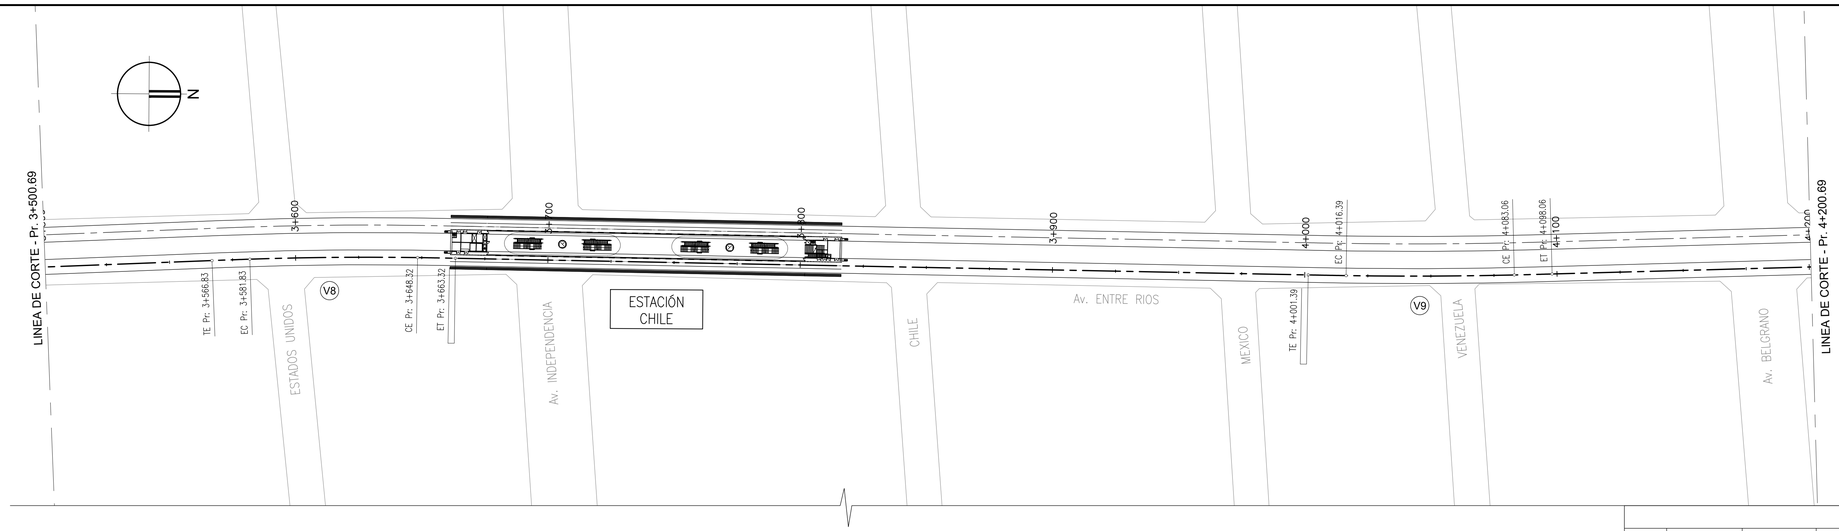

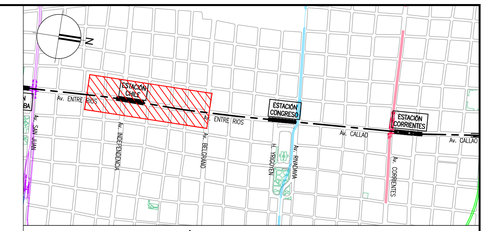

CROQUIS DE UBICACIÓN

CURVAS HORIZONTALES											
Curva Nº	Prog.	X	Y	Rc (m)	Le (m)	Δ	Des (m)	Tan (m)	E (m)	VD (km/h)	PERALTE (mm)
V 8	3+615.09	6572.839	1145.548	1405.00	15.00	3° 19' 23"	96.49	48.26	0.60	90	32
V 9	4+049.73	6578.688	1580.172	1750.00	15.00	2° 40' 26"	96.67	48.34	0.48	90	26

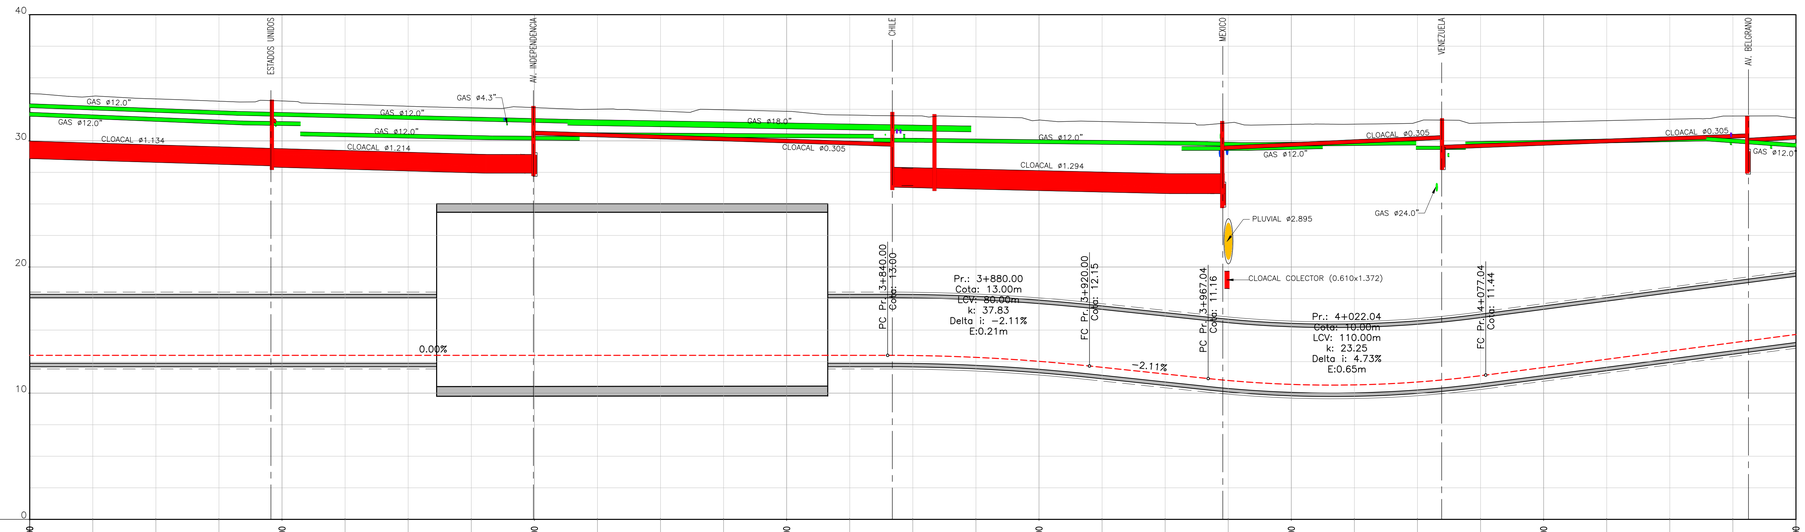

PROGRESIVAS	3+500	3+600	3+700	3+800	3+900	4+000	4+100	4+200
CAMBIO DE VIAS								
COTAS DE TERRENO	13.00	13.00 13.00 13.00 13.00 13.00 13.00 13.00 13.00 13.00 13.00 13.00 13.00 13.00 13.00 13.00 13.00	12.99 12.84 12.52 12.05 11.52 11.00 10.70 10.66 10.89 11.38 12.04 12.69 13.34 14.00	14.65
COTAS DE PROYECTO	13.00	13.00 13.00 13.00 13.00 13.00 13.00 13.00 13.00 13.00 13.00 13.00 13.00 13.00 13.00 13.00	12.99 12.84 12.52 12.05 11.52 11.00 10.70 10.66 10.89 11.38 12.04 12.69 13.34 14.00	14.65
DIFERENCIAS	0.00	0.00 0.00 0.00 0.00 0.00 0.00 0.00 0.00 0.00 0.00 0.00 0.00 0.00 0.00 0.00	0.00 0.00 0.00 0.00 0.00 0.00 0.00 0.00 0.00 0.00 0.00 0.00 0.00 0.00	0.00
ALINEACIÓN HORIZONTAL	L=664.08m	L=15.00m	L=66.49m R=1405.00m	L=15.00m	L=338.07m	L=15.00m	L=66.67m R=1750.00m	L=15.00m	L=231.71m

REFERENCIAS INTERFERENCIAS:

- RED BT - MT -AT
- RED PLUVIAL
- RED CLOACAL
- RED DE AGUA CORRIENTE
- RED DE GAS
- RED DE FIBRA OPTICA
- RED TELEFÓNICA

NOTAS:

1- SISTEMA DE COORDENADAS DE LA CIUDAD DE BUENOS AIRES.

2- TODAS LAS MEDIDAS ESTÁN EXPRESADAS EN METROS, SALVO INDICACIÓN CONTRARIA

ESCALA 1:200 (0 5 10m)

ESCALA 1:1.000 (0 50m)

NOTAS: EL PRESENTE PLANO ES INDICATIVO. LA CONTRATISTA CONFECCIONARA LOS PLANOS DE DETALLE CORRESPONDIENTES, QUE DEBERAN SER APROBADOS POR LA D.G.O.M.P. EN LA INSPECCION DE OBRA, EL PLANO PRESENTADO POR LA CONTRATISTA ESTARA EN UN TODO DE ACUERDO CON LA NORMATIVA VIGENTE.
TODAS LAS MEDIDAS Y NIVELES DE VERIFICARAN EN OBRA POR EL CONTRATISTA.
TODOS LOS DETALLES CONSTRUCTIVOS SERAN COORDINADOS Y CONFIRMADOS EN OBRA

PLANO NO APTO PARA CONSTRUCCION

Ing. Mariano Miculicich
DIRECTOR

MODIFICACIONES:

REVISION	FECHA	DESCRIPCION
0	14/01/2026	EMISIÓN INICIAL

MINISTERIO DE INFRAESTRUCTURA
SUBSECRETARIA DE PROYECTOS Y OBRAS
DIRECCION GENERAL DE PROYECTOS

DGPRO

Obra: LINEA F			IF-2026-20223041-GCABA-APRA Plano N°
Plano: TRAZADO DE VÍAS - PLANIALTIMETRÍA VÍA DESCENDENTE - PR. 3+500 A 4+200			LF-VI-T01-VIA-PL-015
Fecha: 14/01/2026	Eq. de Proyecto: UPU-ATEC-IATASA	Dibujó: N.S.	Revisó: G.D.R. Escala: Indicada 015

14/1/2026 16:49 p. m.
LF-VI-T01-VIA-PL-015-018 - PLANIALTIMETRIA T1 - VIA DESC.dwg

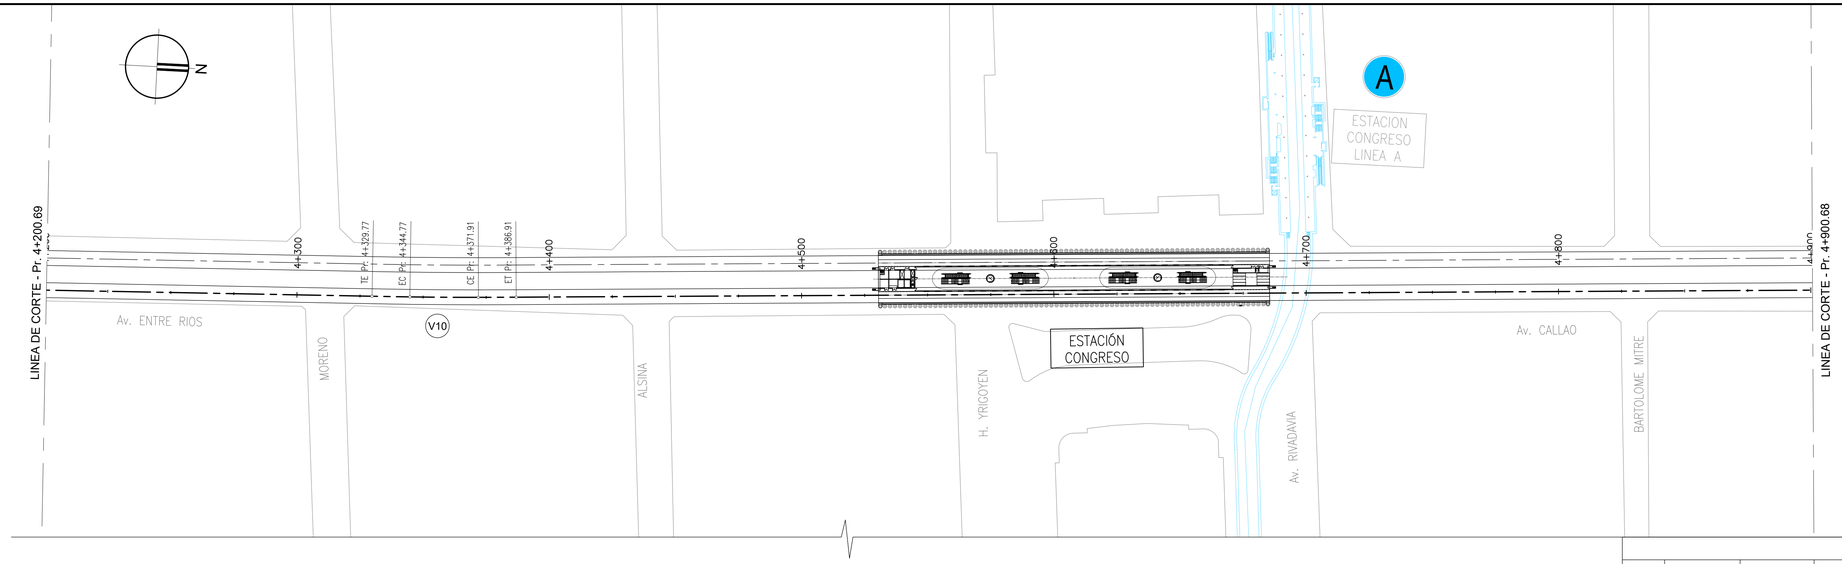

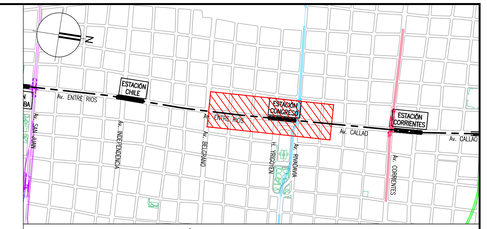

CROQUIS DE UBICACIÓN

CURVAS HORIZONTALES

Curva Nº	Prog.	X	Y	Rc (m)	Le (m)	Δ	Des (m)	Tan (m)	E (m)	VD (km/h)	PERALTE (mm)
V 10	4+358.34	6568.439	1888.625	1750.00	15.00	1° 22' 47"	57.14	28.57	0.13	90	26

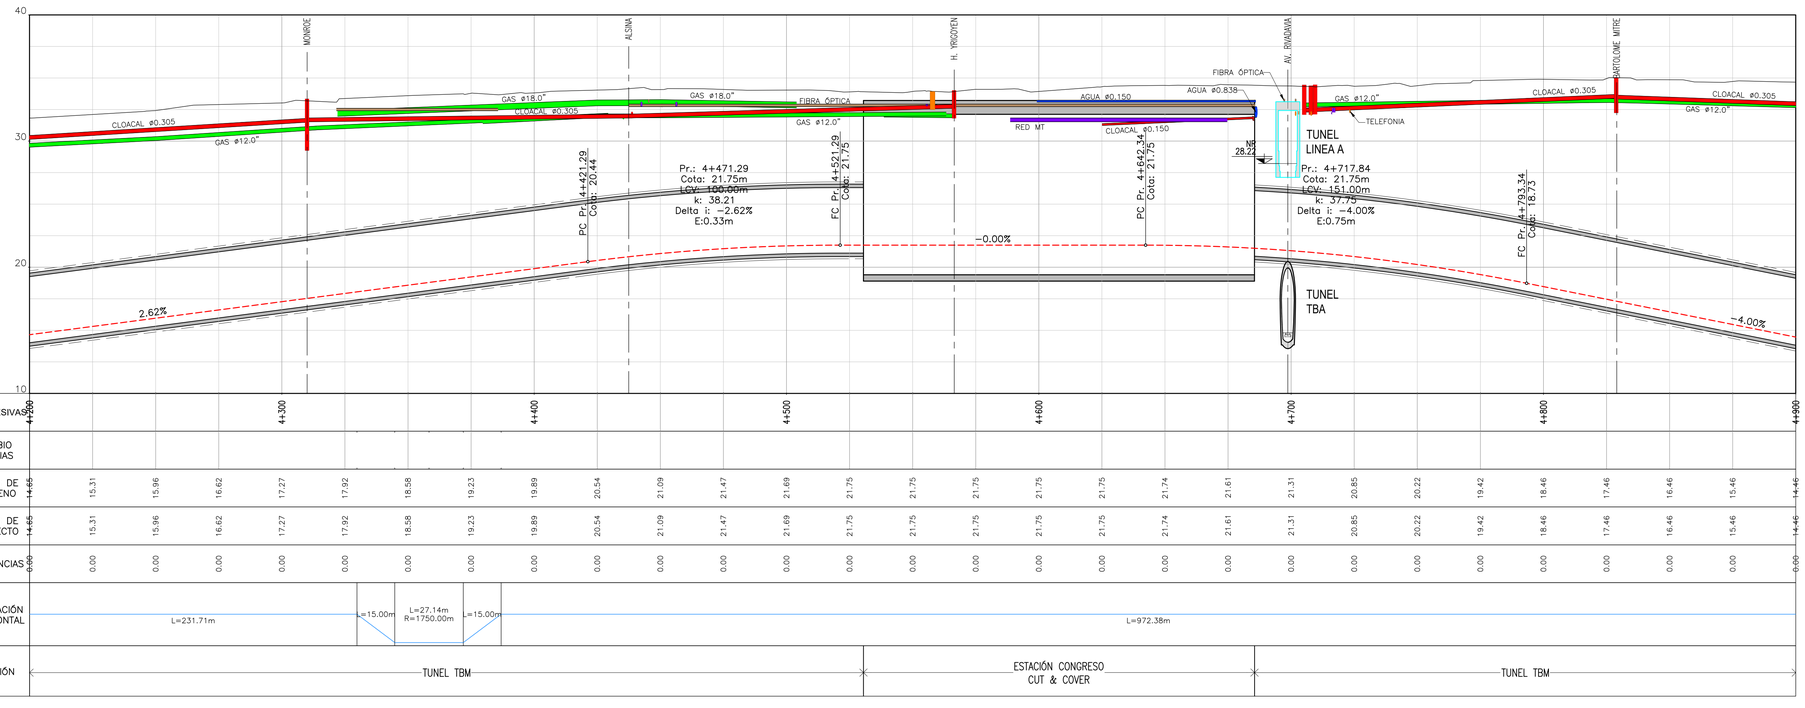

| | | |

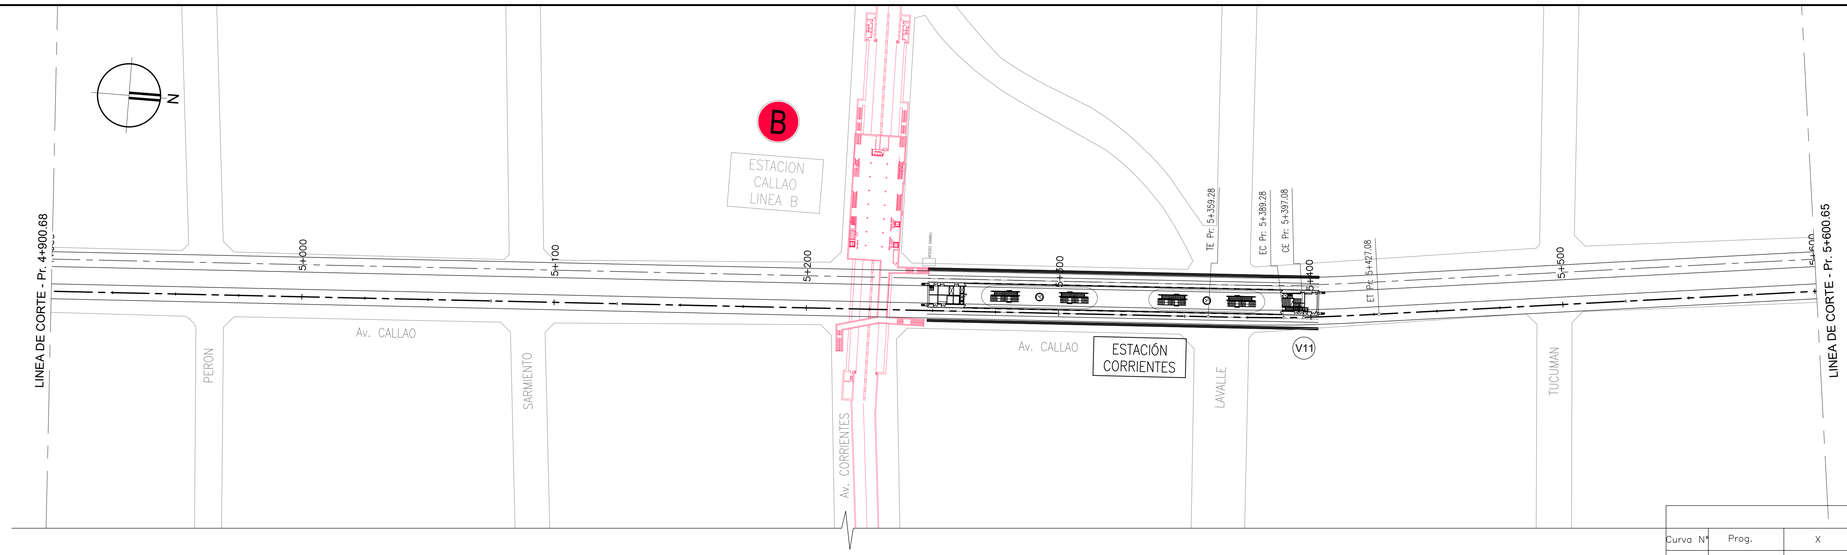

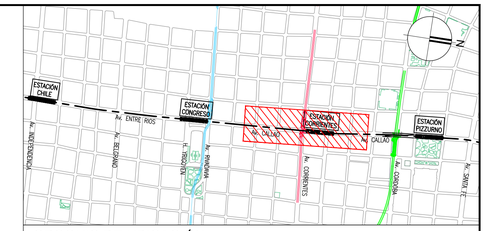

CROQUIS DE UBICACIÓN

CURVAS HORIZONTALES											
Curva Nº	Prog.	X	Y	Rc (m)	Le (m)	Δ	Des (m)	Tan (m)	E (m)	VD (km/h)	PERALTE (mm)
V 11	5+393.19	6509.180	2921.784	510.00	30.00	4° 14' 45"	67.79	33.91	0.42	75	59

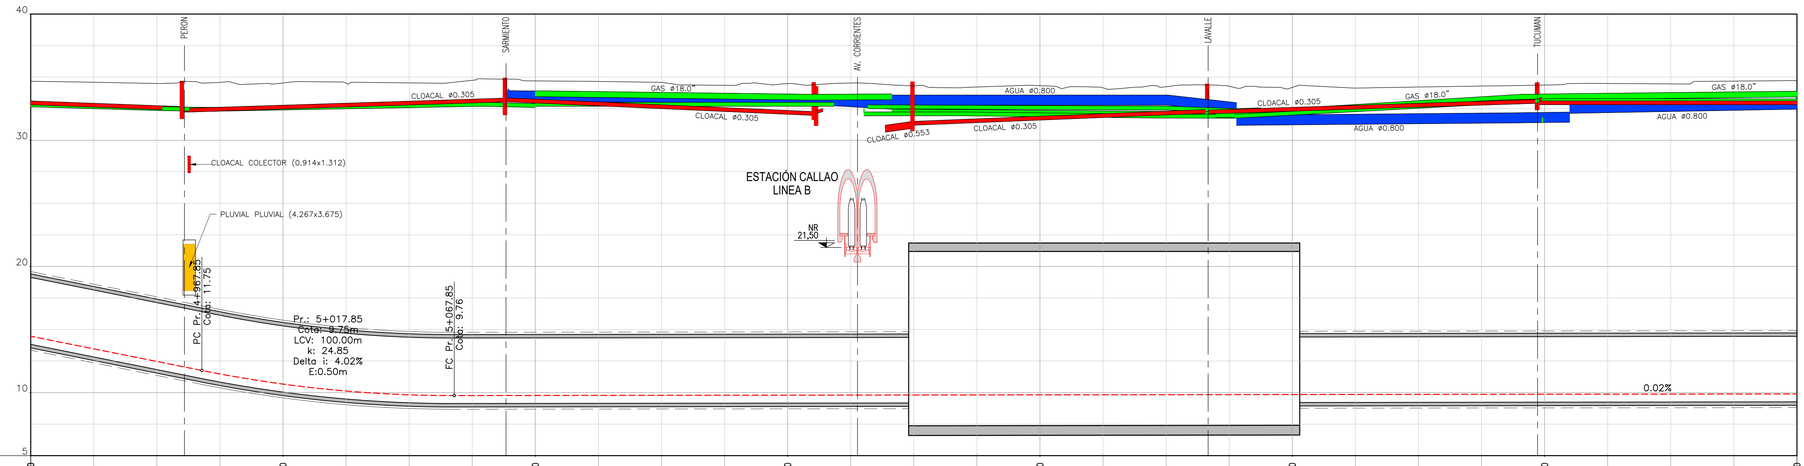

| | | | | | | | | | | |

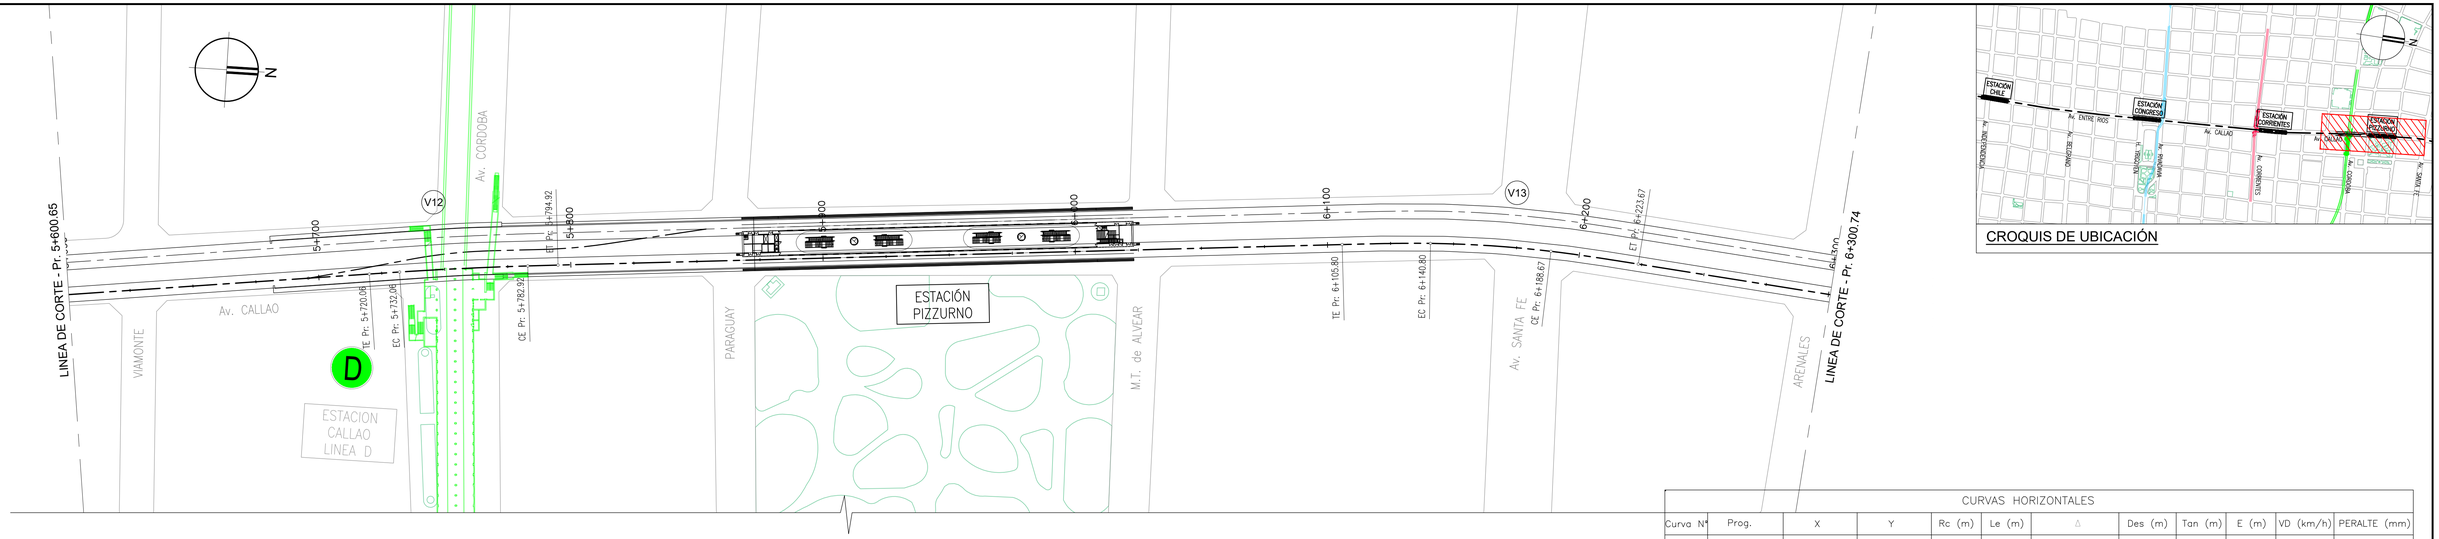

CROQUIS DE UBICACIÓN

CURVAS HORIZONTALES											
Curva N°	Prog.	X	Y	Rc (m)	Le (m)	Δ	Des (m)	Tan (m)	E (m)	VD (km/h)	PERALTE (mm)
V 12	5+757.50	6461.445	3282.971	1495.00	12.00	2° 24' 33"	74.86	37.43	0.33	70	20
V 13	6+164.86	6425.093	3688.715	450.00	35.00	10° 33' 04"	117.87	59.06	2.03	70	67

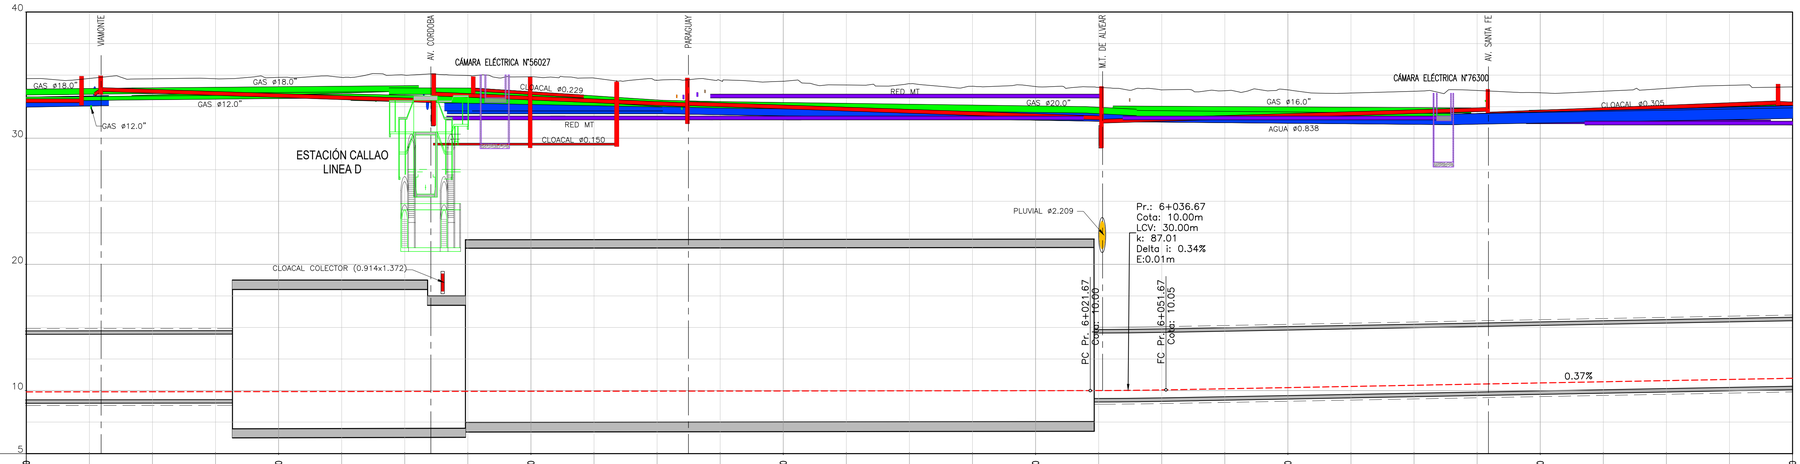

| | | | | | | | | | | |

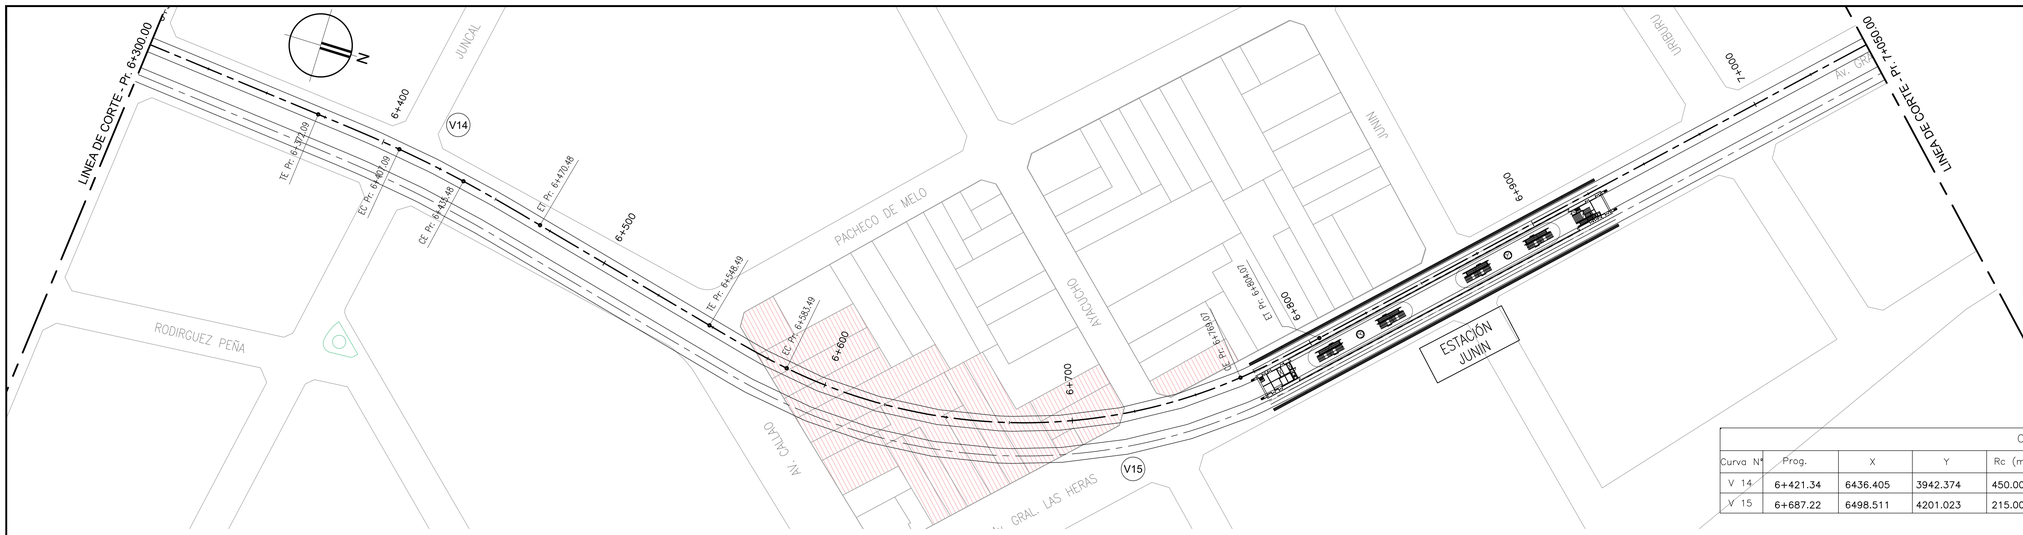

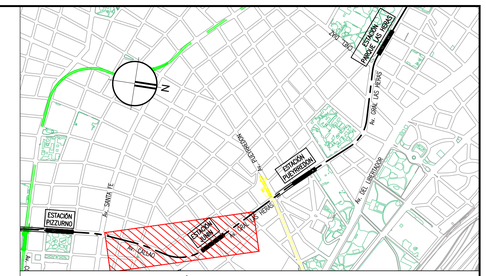

CROQUIS DE UBICACIÓN

CURVAS HORIZONTALES

Curva Nº	Prog.	X	Y	Rc (m)	Le (m)	Δ	Des (m)	Tan (m)	E (m)	VD (km/h)	PERALTE (mm)
V 14	6+421.34	6436.405	3942.374	450.00	35.00	8° 04' 14"	98.39	49.25	1.23	70	67
V 15	6+687.22	6498.511	4201.023	215.00	35.00	58° 47' 06"	255.59	138.74	32.04	45	67

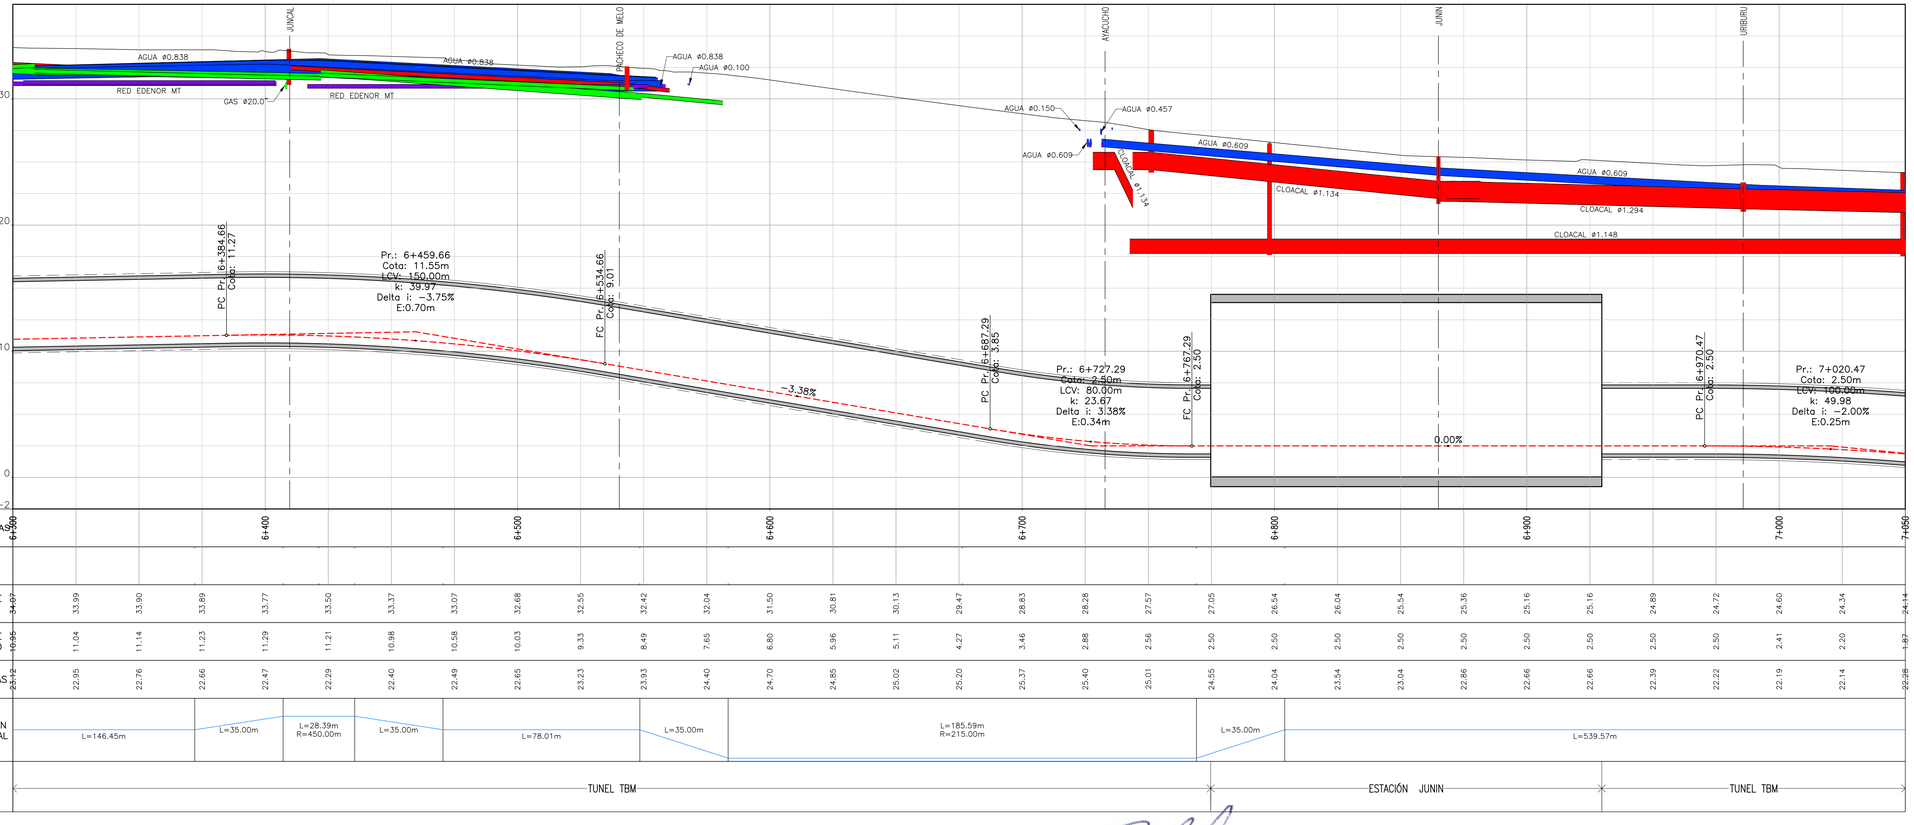

PROGRESIVAS	6+300	6+400	6+500	6+600	6+700	6+800	6+900	7+000	7+060
CAMBIO DE VIAS									
COTAS DE TERRENO	34.07	33.99	33.90	33.89	33.77	33.50	33.37	33.07	32.68	32.55	32.42	32.04	31.50	30.81	30.13	29.47	28.83	28.28	27.57	27.05	26.54	26.04	25.54	25.36	25.16	25.16	24.89	24.72	24.60	24.34	24.14
COTAS DE PROYECTO	10.95	11.04	11.14	11.23	11.29	11.21	10.98	10.58	10.03	9.33	8.49	7.65	6.80	5.96	5.11	4.27	3.46	2.88	2.56	2.50	2.50	2.50	2.50	2.50	2.50	2.50	2.50	2.50	2.41	2.20	1.87
DIFERENCIAS	23.12	22.95	22.76	22.66	22.47	22.29	22.40	22.49	22.65	23.23	23.93	24.40	24.70	24.85	25.02	25.20	25.37	25.40	25.01	24.55	24.04	23.54	23.04	22.86	22.66	22.66	22.39	22.22	22.19	22.14	22.28
ALINEACIÓN HORIZONTAL	L=146.45m	L=35.00m	L=28.39m R=450.00m	L=35.00m	L=78.01m	L=35.00m	L=185.59m R=215.00m	L=35.00m	L=539.57m																						
SECCIÓN	TUNEL TBM						ESTACIÓN JUNIN																				TUNEL TBM				

REFERENCIAS INTERFERENCIAS:

- RED BT - MT -AT
- RED PLUVIAL
- RED CLOACAL
- RED DE AGUA CORRIENTE
- RED DE GAS
- RED DE FIBRA OPTICA
- RED TELEFÓNICA

NOTAS:

1- SISTEMA DE COORDENADAS DE LA CIUDAD DE BUENOS AIRES.

2- TODAS LAS MEDIDAS ESTÁN EXPRESADAS EN METROS, SALVO INDICACIÓN CONTRARIA

ESCALA 1:200 (0 5 10m)

ESCALA 1:1.000 (0 50m)

NOTAS: EL PRESENTE PLANO ES INDICATIVO. LA CONTRATISTA CONFECCIONARA LOS PLANOS DE DETALLE DEFINITIVO, QUE DEBERAN SER APROBADOS POR LA D.G.OM Y LA INSPECCION DE OBRA. EL PLANO PRESENTADO POR LA CONTRATISTA ESTARA EN UN TODO DE ACUERDO CON LA NORMATIVA VIGENTE. TODAS LAS MEDIDAS Y NIVELES DE VEREDA SERAN IN OBRA POR EL CONTRATISTA. TODOS LOS DETALLES CONSTRUCTIVOS SERAN COORDINADOS Y COMPATIBILIZADOS EN OBRA.

PLANO NO APTO PARA CONSTRUCCION

Ing. Mariano Miculicich
DIRECTOR

MODIFICACIONES:

REVISION	FECHA	DESCRIPCION
0	14/01/2026	EMISIÓN INICIAL

MINISTERIO DE INFRAESTRUCTURA
SUBSECRETARIA DE PROYECTOS Y OBRAS
DIRECCION GENERAL DE PROYECTOS

DGPRO

Obra: LINEA F				IF-2026-20223041-GCABA-APRA	Plano Nº: 001
Plano: TRAZADO DE VÍAS - PLANIALTIMETRÍA VÍA ASCENDENTE - PR. 6+300 A 7+050				LF-VI-T02-VIA-PL-001	
Fecha: 14/01/2026	Eq. de Proyecto: UPU-ATEC-IATASA	Dibujó: N.S.	Revisó: G.D.R.	Escala: Indicada	

15/1/2026 10:44 a. m.
LF-VI-T02-VIA-PL-001-509 - PLANIALTIMETRIA T2 - VIA ASC.dwg

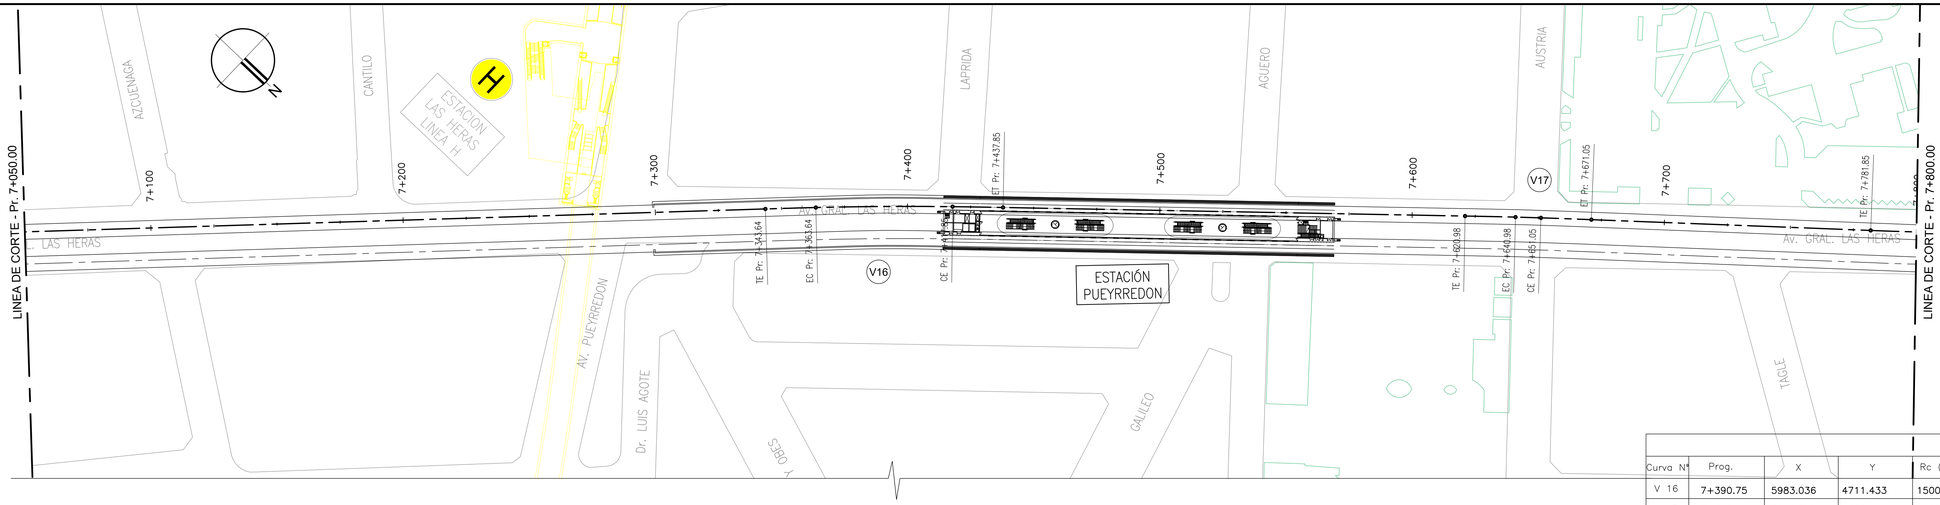

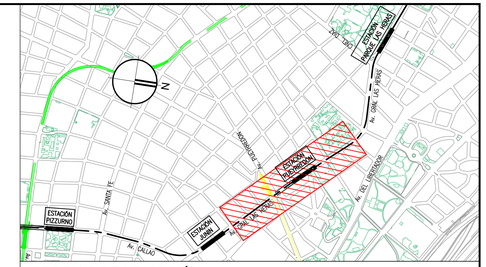

CROQUIS DE UBICACIÓN

CURVAS HORIZONTALES

Curva N°	Prog.	X	Y	Rc (m)	Le (m)	Δ	Des (m)	Tan (m)	E (m)	VD (km/h)	PERALTE (mm)
V 16	7+390.75	5983.036	4711.433	1500.00	20.00	2° 50' 05"	94.21	47.11	0.47	90	30
V 17	7+646.02	5810.742	4899.801	1500.00	20.00	1° 08' 54"	50.07	25.03	0.09	90	30

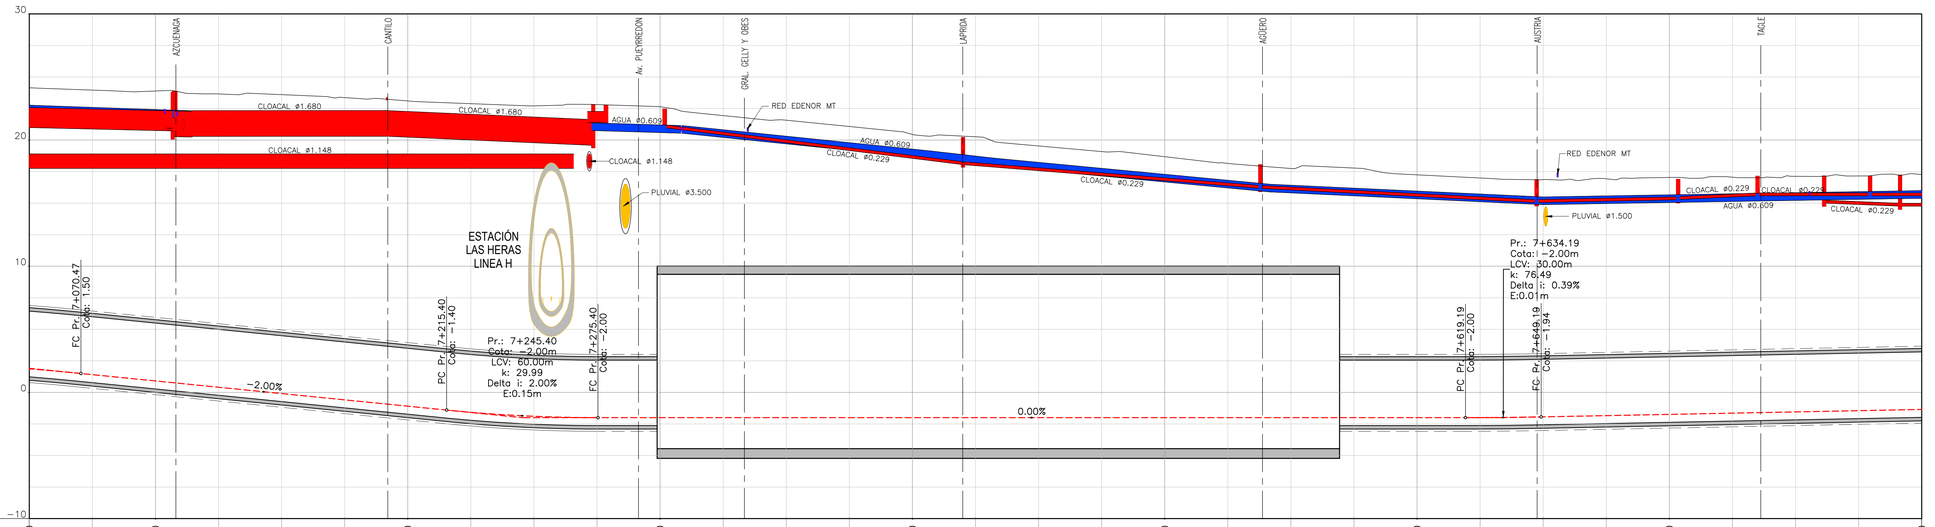

| | | |

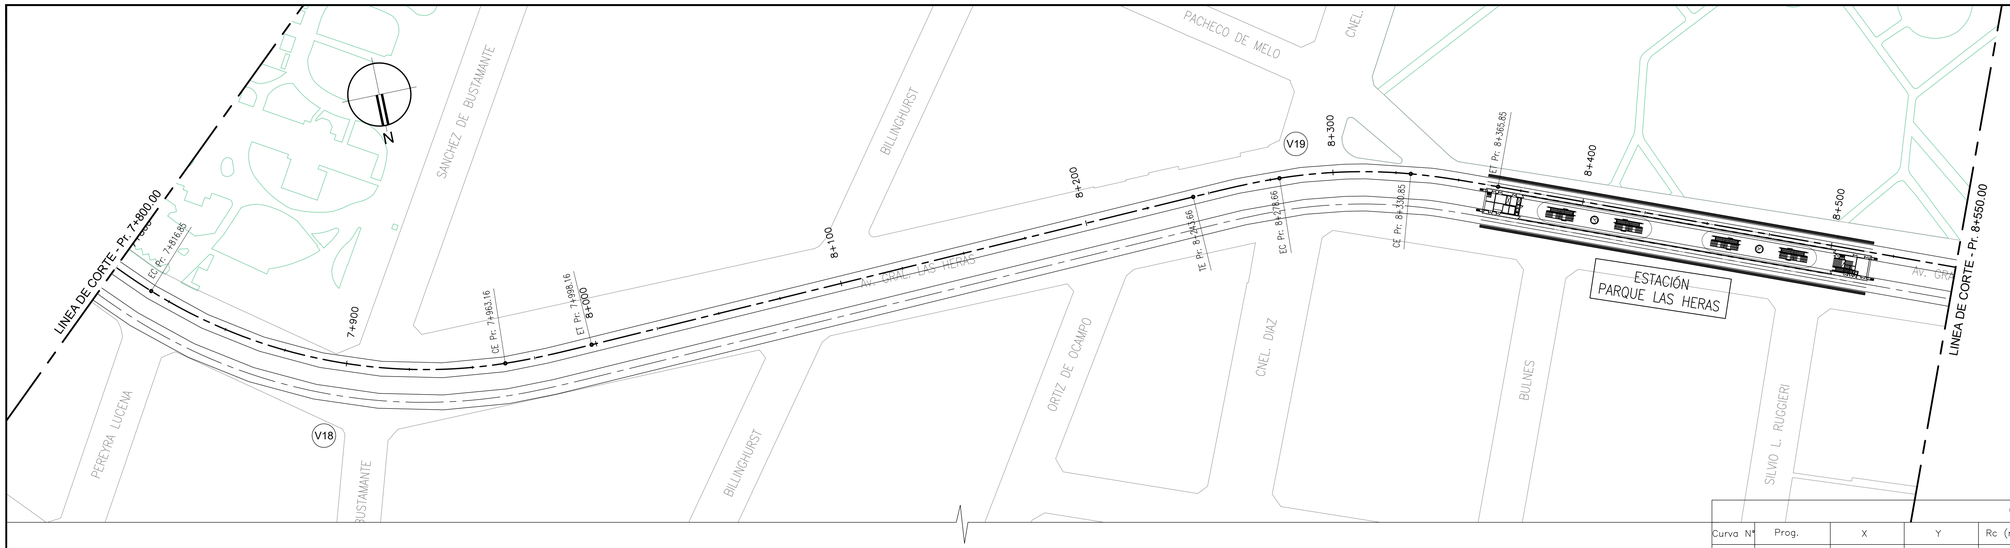

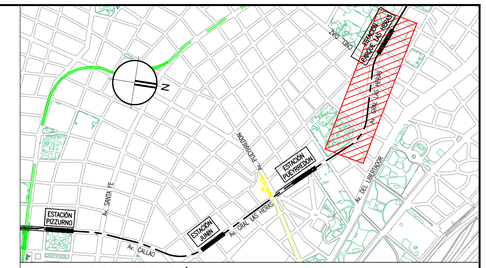

CROQUIS DE UBICACIÓN

CURVAS HORIZONTALES

Curva Nº	Prog.	X	Y	Rc (m)	Le (m)	Δ	Des (m)	Tan (m)	E (m)	VD (km/h)	PERALTE (mm)
V 18	7+896.53	5645.404	5088.003	205.00	35.00	50° 40' 19"	216.30	114.67	22.09	45	70
V 19	8+305.44	5223.691	5073.485	210.00	35.00	23° 47' 18"	122.19	61.78	4.86	45	70

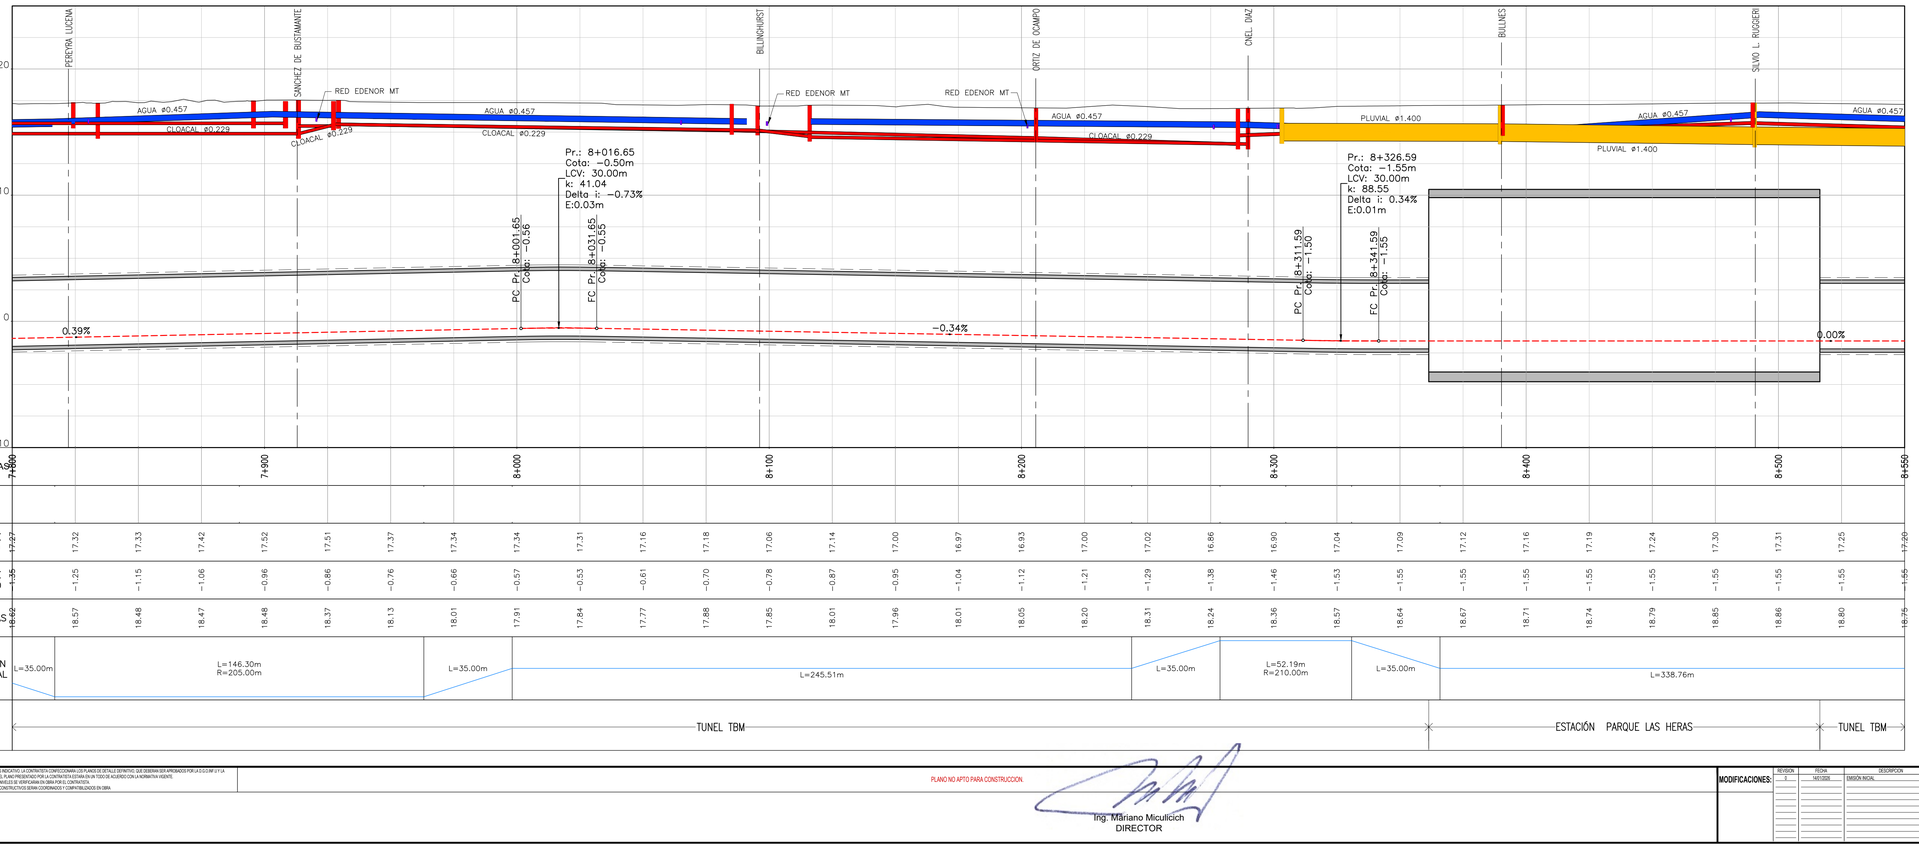

PROGRESIVAS	7+800	7+900	8+000	8+100	8+200	8+300	8+400	8+500	8+550
CAMBIO DE VIAS									
COTAS DE TERRENO	17.27	17.32	17.33	17.42	17.52	17.51	17.37	17.34	17.34
COTAS DE PROYECTO	−1.35	−1.25	−1.15	−1.06	−0.96	−0.86	−0.76	−0.66	−0.57
DIFERENCIAS	18.62	18.57	18.48	18.47	18.48	18.37	18.13	18.01	17.91
ALINEACIÓN HORIZONTAL	L=35.00m	L=146.30m R=205.00m				L=35.00m			
SECCIÓN	TUNEL TBM								

PROGRESIVAS	8+550	8+600	8+700	8+800	8+900	9+000	9+100	9+200	9+300	9+400	9+500	9+600	9+700
CAMBIO DE VIAS													
COTAS DE TERRENO	17.34	17.31	17.16	17.18	17.05	17.14	17.00	16.97	16.93	17.00	17.02	16.86	16.90
COTAS DE PROYECTO	−0.57	−0.53	−0.61	−0.70	−0.78	−0.87	−0.95	−1.04	−1.12	−1.21	−1.29	−1.38	−1.46
DIFERENCIAS	17.91	17.84	17.77	17.88	17.85	18.01	17.96	18.01	18.05	18.20	18.31	18.24	18.36
ALINEACIÓN HORIZONTAL		L=245.51m								L=35.00m	L=52.19m R=210.00m		L=35.00m
SECCIÓN	TUNEL TBM												

PROGRESIVAS	9+700	9+800	9+900	10+000	10+100	10+200	10+300	10+400	10+500	10+550
CAMBIO DE VIAS										
COTAS DE TERRENO	16.93	16.97	16.99	17.00	17.00	17.00	17.00	17.00	17.00	17.00
COTAS DE PROYECTO	−1.55	−1.55	−1.55	−1.55	−1.55	−1.55	−1.55	−1.55	−1.55	−1.55
DIFERENCIAS	18.48	18.52	18.54	18.55	18.55	18.55	18.55	18.55	18.55	18.55
ALINEACIÓN HORIZONTAL	L=338.76m									
SECCIÓN	ESTACIÓN PARQUE LAS HERAS									TUNEL TBM

REFERENCIAS INTERFERENCIAS:

- RED BT - MT -AT
- RED PLUVIAL
- RED CLOACAL
- RED DE AGUA CORRIENTE
- RED DE GAS
- RED DE FIBRA OPTICA
- RED TELEFÓNICA

NOTAS:

1- SISTEMA DE COORDENADAS DE LA CIUDAD DE BUENOS AIRES.

2- TODAS LAS MEDIDAS ESTÁN EXPRESADAS EN METROS, SALVO INDICACIÓN CONTRARIA

0 5 10m — ESCALA 1:200

0 50m — ESCALA 1:1.000

NOTAS: EL PRESENTE PLANO ES INDICATIVO. LA CONTRATISTA CONFECCIONARA LOS PLANOS DE DETALLE DEFINITIVO, QUE DEBERAN SER APROBADOS POR LA D.G.O.M.F. Y/ O LA INSPECCION DE OBRA, EL PLANO PRESENTADO POR LA CONTRATISTA DEBERA EN TODO EL ALCANCE CON LA NORMATIVA VIGENTE.
TODAS LAS MEDIDAS Y NIVELES SE VERIFICARAN EN OBRA POR EL CONTRATISTA.
TODOS LOS DETALLES CONSTRUCTIVOS SERAN COORDINADOS Y COMPATIBILIZADOS EN OBRA

PLANO NO APTO PARA CONSTRUCCION

Ing. Mariano Miculicich
DIRECTOR

MODIFICACIONES:

REVISION	FECHA	DESCRIPCION
0	14/01/2026	EMISIÓN INICIAL

Gobierno de la Ciudad de Buenos Aires

MINISTERIO DE INFRAESTRUCTURA
SUBSECRETARIA DE PROYECTOS Y OBRAS
DIRECCION GENERAL DE PROYECTOS

DGPRO

Obra: LINEA F — IF-2026-20223041-GCABA-APRA — Plano Nº 003

Plano: TRAZADO DE VÍAS - PLANIALTIMETRÍA VÍA ASCENDENTE - PR. 7+800 A 8+550 — LF-VI-T02-VIA-PL-003

Fecha: 14/01/2026 | Eq. de Proyecto: UPU-ATEC-IATASA | Dibujó: N.S. | Revisó: G.D.R. | Escala: Indicada

15/1/2026 10:44 a. m.
LF-VI-T02-VIA-PL-001-009 - PLANIALTIMETRIA T2 - VIA ASC.dwg

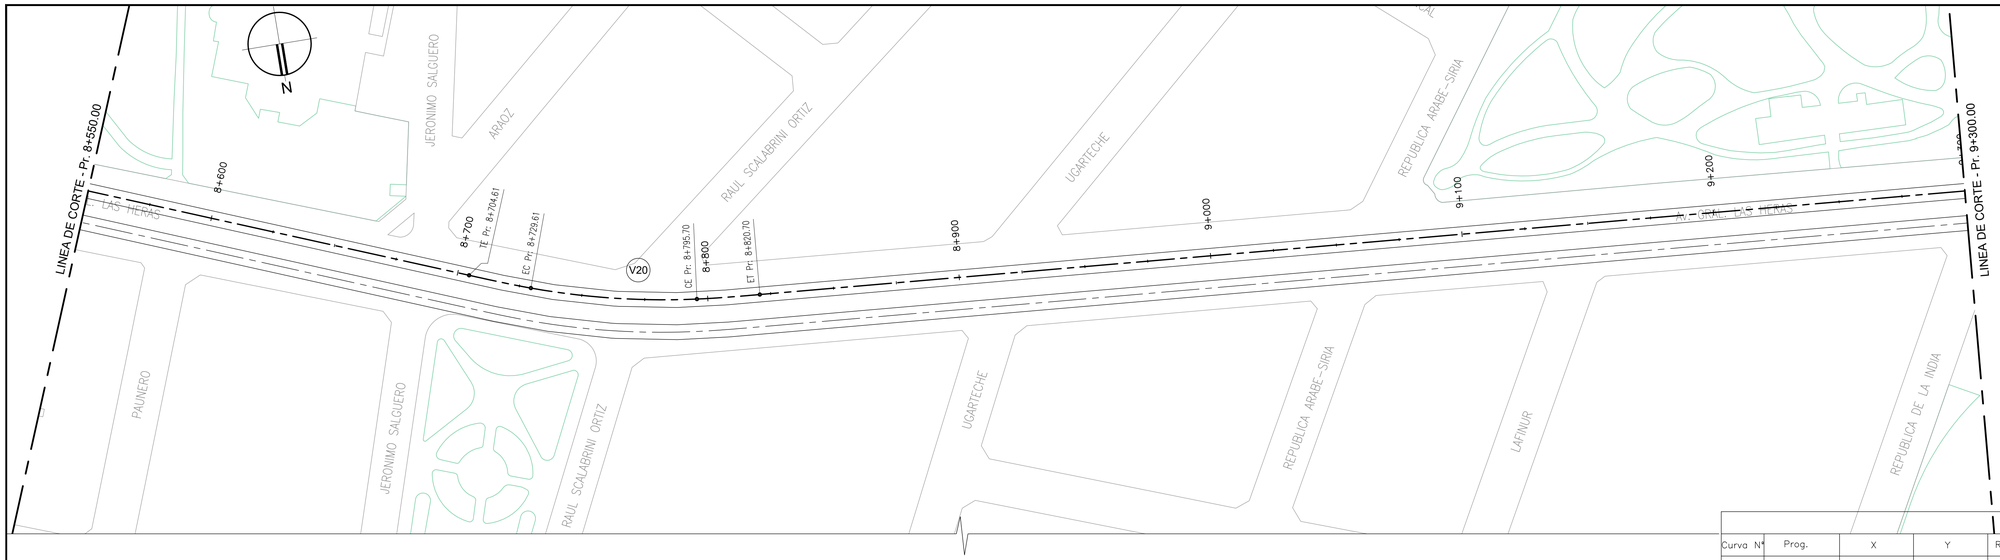

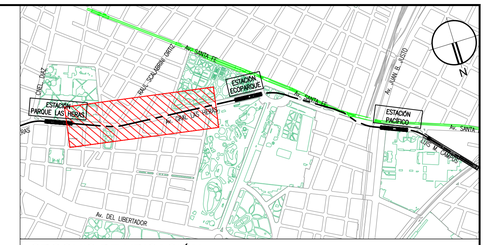

CROQUIS DE UBICACIÓN

CURVAS HORIZONTALES

Curva Nº	Prog.	X	Y	Rc (m)	Le (m)	Δ	Des (m)	Tan (m)	E (m)	VD (km/h)	PERALTE (mm)
V 20	8+763.02	4797.619	5244.046	300.00	25.00	17° 23' 47"	116.09	58.41	3.58	45	50

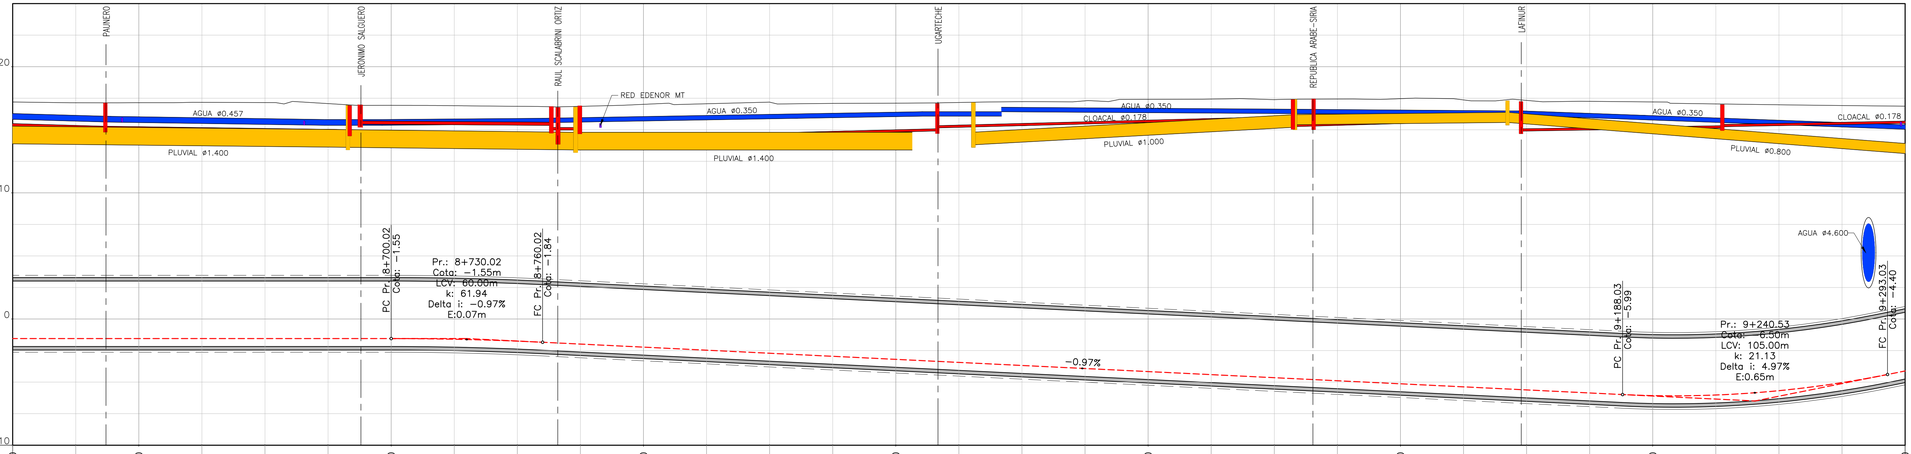

| | | |

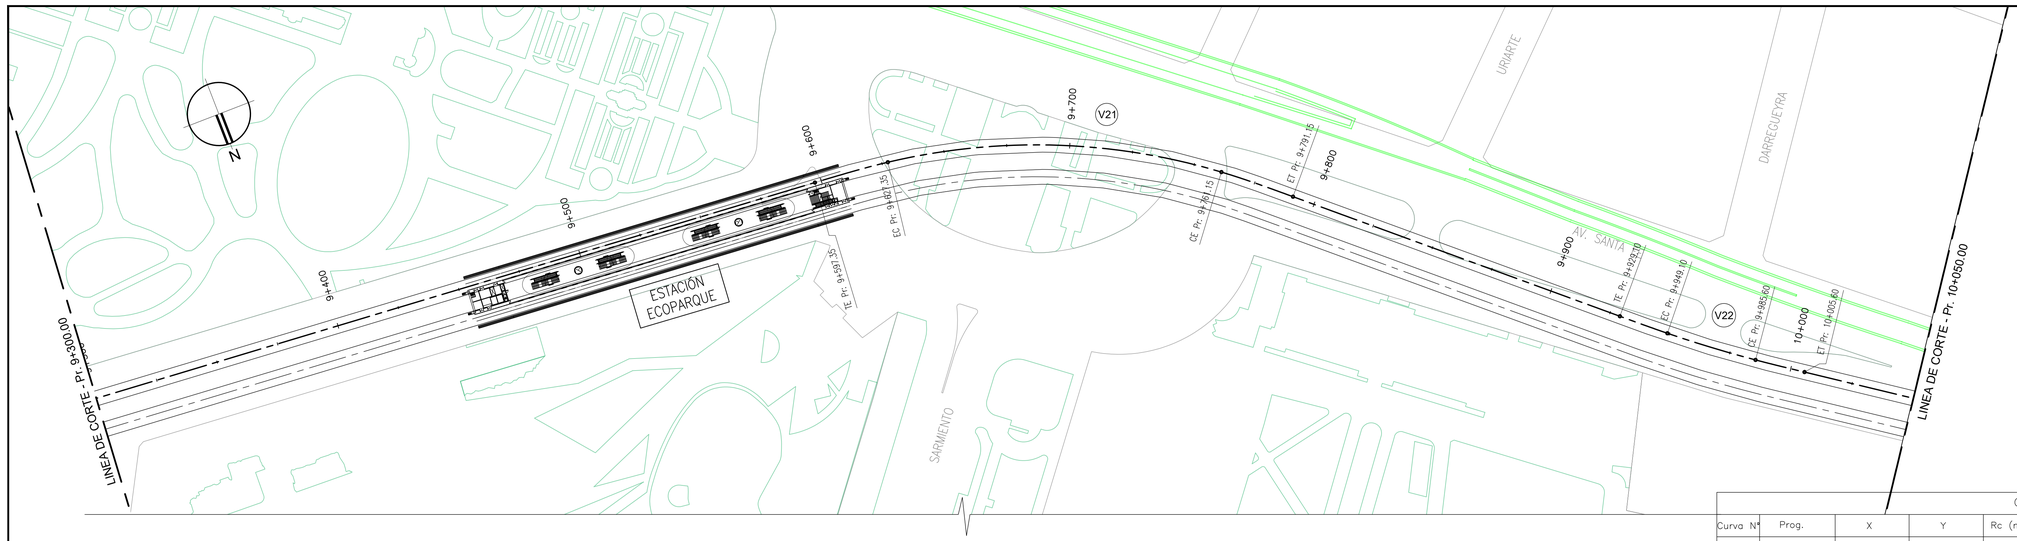

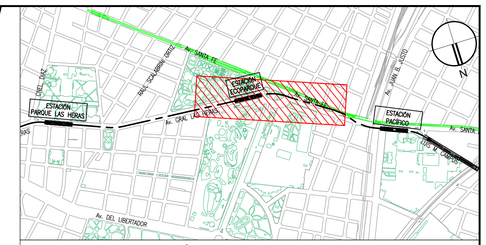

CROQUIS DE UBICACIÓN

CURVAS HORIZONTALES

Curva N°	Prog.	X	Y	Rc (m)	Le (m)	Δ	Des (m)	Tan (m)	E (m)	VD (km/h)	PERALTE (mm)
V 21	9+697.23	3865.453	5316.105	255.00	30.00	36° 48' 13"	193.80	99.88	13.90	45	59
V 22	9+967.38	3657.777	5498.065	495.00	20.00	6° 32' 24"	76.50	38.28	0.84	45	30

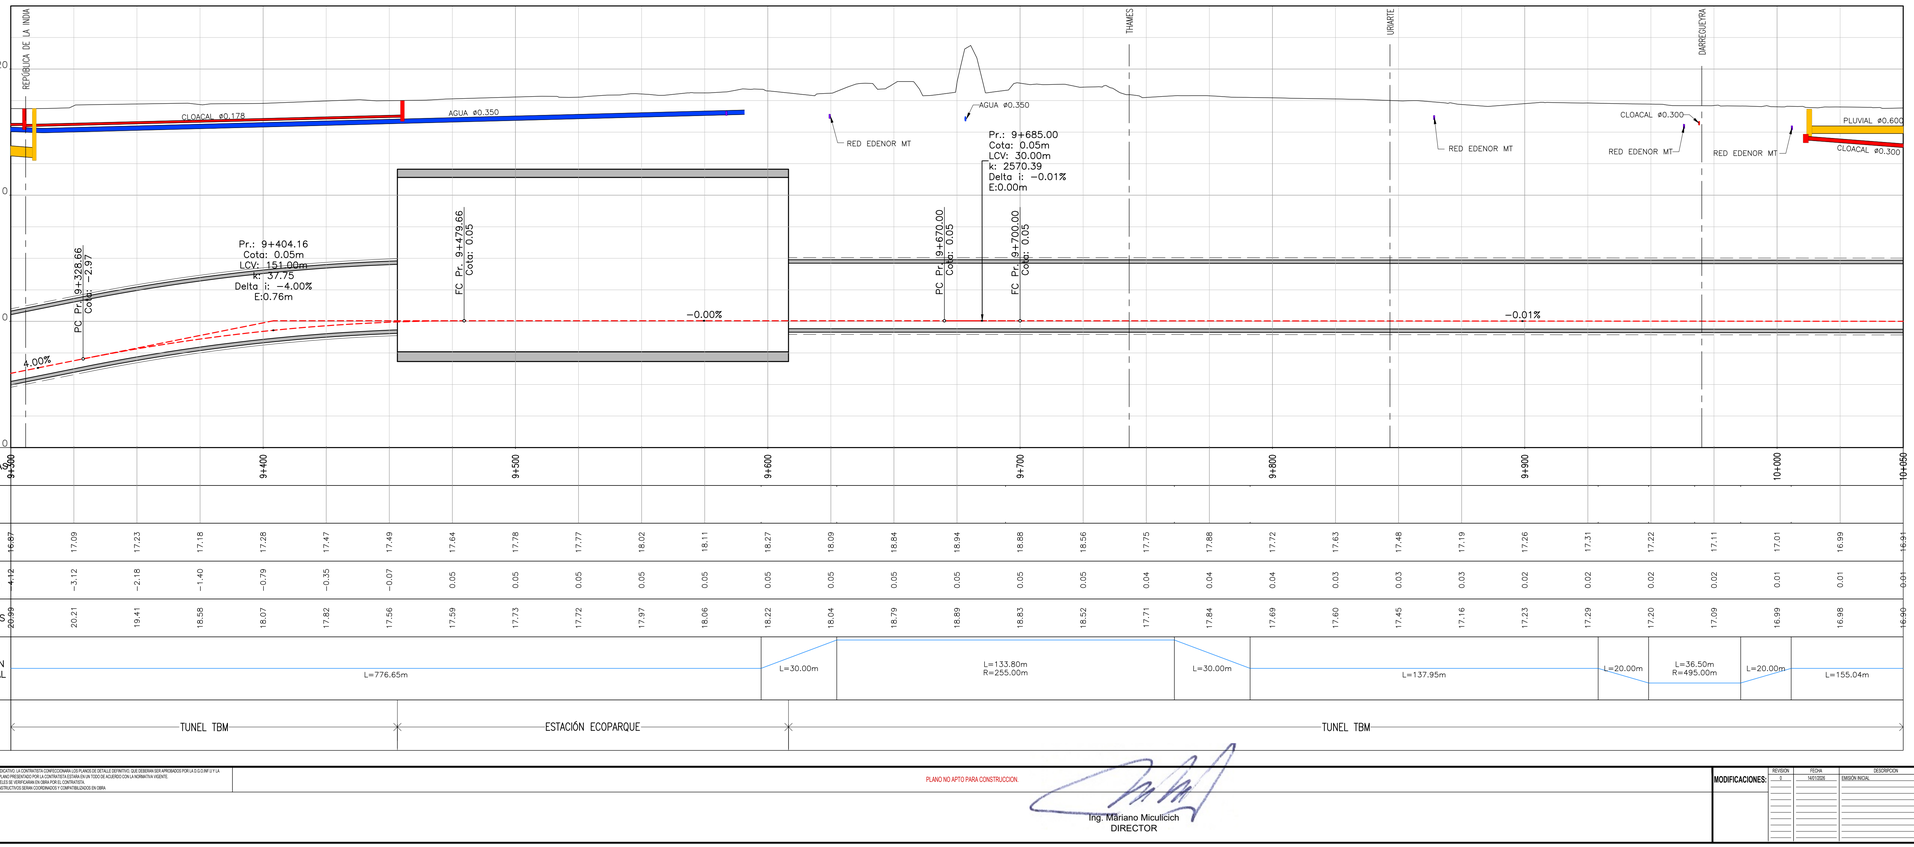

PROGRESIVAS	9+300	9+400	9+500	9+600	9+700	9+800	9+900	10+000	10+050
CAMBIO DE VIAS									
COTAS DE TERRENO	16.67	17.09 17.23 17.18 17.28 17.47 17.49 17.64 17.78 17.77 18.02 18.11 18.27 18.09 18.84 18.94 18.88 18.56 17.75 17.88 17.72 17.63 17.48 17.19 17.26 17.31 17.22 17.11 17.01 16.99							16.91
COTAS DE PROYECTO	−1.12	−3.12 −2.18 −1.40 −0.79 −0.35 −0.07 0.05 0.05 0.05 0.05 0.05 0.05 0.05 0.05 0.05 0.05 0.05 0.04 0.04 0.04 0.03 0.03 0.03 0.02 0.02 0.02 0.02 0.02 0.01 0.01							0.01
DIFERENCIAS	29.99	20.21 19.41 18.58 18.07 17.82 17.56 17.59 17.73 17.72 17.97 18.06 18.22 18.04 18.79 18.89 18.83 18.52 17.71 17.84 17.69 17.60 17.45 17.16 17.23 17.29 17.20 17.09 16.99 16.98							16.90
ALINEACIÓN HORIZONTAL		L=776.65m	L=30.00m	L=133.80m R=255.00m	L=30.00m	L=137.95m	L=20.00m	L=36.50m R=495.00m	L=20.00m	L=155.04m	
SECCIÓN		TUNEL TBM		ESTACIÓN ECOPARQUE		TUNEL TBM					

REFERENCIAS INTERFERENCIAS:

- RED BT - MT -AT
- RED PLUVIAL
- RED CLOACAL
- RED DE AGUA CORRIENTE
- RED DE GAS
- RED DE FIBRA OPTICA
- RED TELEFÓNICA

NOTAS:

1- SISTEMA DE COORDENADAS DE LA CIUDAD DE BUENOS AIRES.

2- TODAS LAS MEDIDAS ESTÁN EXPRESADAS EN METROS, SALVO INDICACIÓN CONTRARIA

0 5 10m — ESCALA 1:200

0 50m — ESCALA 1:1.000

NOTAS:

EL PRESENTE PLANO ES INDICATIVO. LA CONTRATISTA CONFECCIONARA LOS PLANOS DE DETALLE CONSTRUCTIVO, QUE DEBERAN SER APROBADOS POR LA D.O.O.IMF.3.71.A
INSPECCION DE OBRA, EL PLANO PRESENTADO POR LA CONTRATISTA ESTARA EN UN TODO DE ACUERDO CON LA NORMATIVA VIGENTE.
TODAS LAS MEDIDAS Y NIVELES SE VERIFICARAN EN OBRA POR EL CONTRATISTA.
TODOS LOS DETALLES CONSTRUCTIVOS SERAN COORDINADOS Y COMPATIBILIZADOS EN OBRA.

PLANO NO APTO PARA CONSTRUCCION.

Ing. Mariano Miculicich
DIRECTOR

MODIFICACIONES:

REVISION	FECHA	DESCRIPCION
0	14/1/2026	EMISION INICIAL

MINISTERIO DE INFRAESTRUCTURA
SUBSECRETARIA DE PROYECTOS Y OBRAS
DIRECCION GENERAL DE PROYECTOS

DGPRO

Obra: LÍNEA F			IF-2026-20223041-GCABA-APRA Plano N°
Plano: TRAZADO DE VÍAS - PLANIALTIMETRÍA VÍA ASCENDENTE - PR. 9+300 A 10+050			LF-VI-T02-VIA-PL-005
Fecha: 14/01/2026	Eq. de Proyecto: UPU-ATEC-IATASA	Dibujó: N.S.	Revisó: G.D.R. Escala: Indicada 005

15/1/2026 10:44 a. m.
LF-VI-T02-VIA-PL-005 - PLANIALTIMETRIA T2 - VIA ASC.dwg

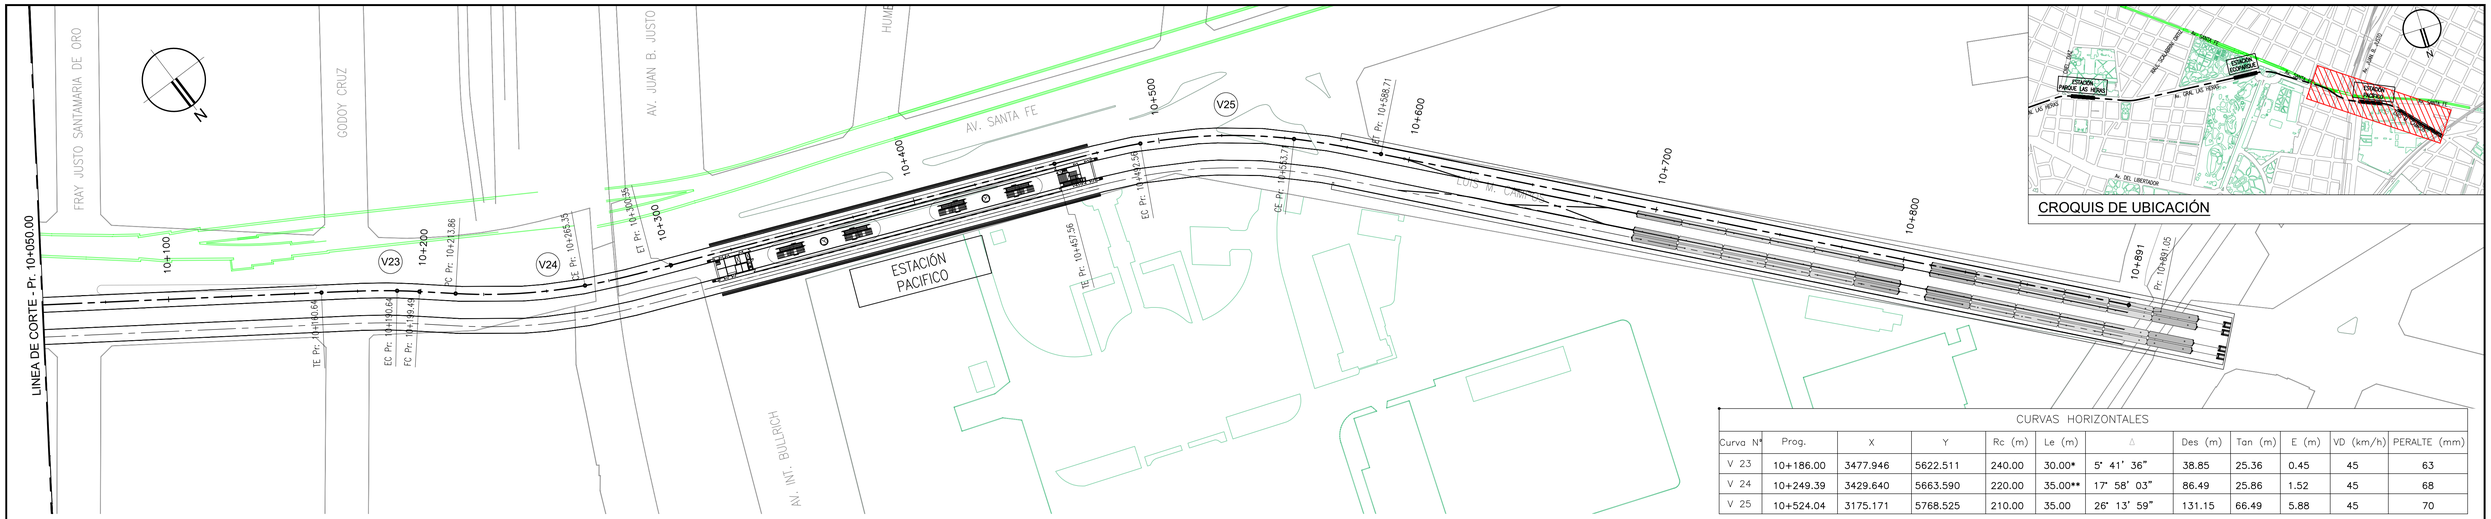

CROQUIS DE UBICACIÓN

CURVAS HORIZONTALES

Curva Nº	Prog.	X	Y	Rc (m)	Le (m)	Δ	Des (m)	Tan (m)	E (m)	VD (km/h)	PERALTE (mm)
V 23	10+186.00	3477.946	5622.511	240.00	30.00*	5° 41' 36"	38.85	25.36	0.45	45	63
V 24	10+249.39	3429.640	5663.590	220.00	35.00**	17° 58' 03"	86.49	25.86	1.52	45	68
V 25	10+524.04	3175.171	5768.525	210.00	35.00	26° 13' 59"	131.15	66.49	5.88	45	70

*: SOLO LONGITUD ESPIRAL DE ENTRADA
**: SOLO LONGITUD ESPIRAL DE SALIDA

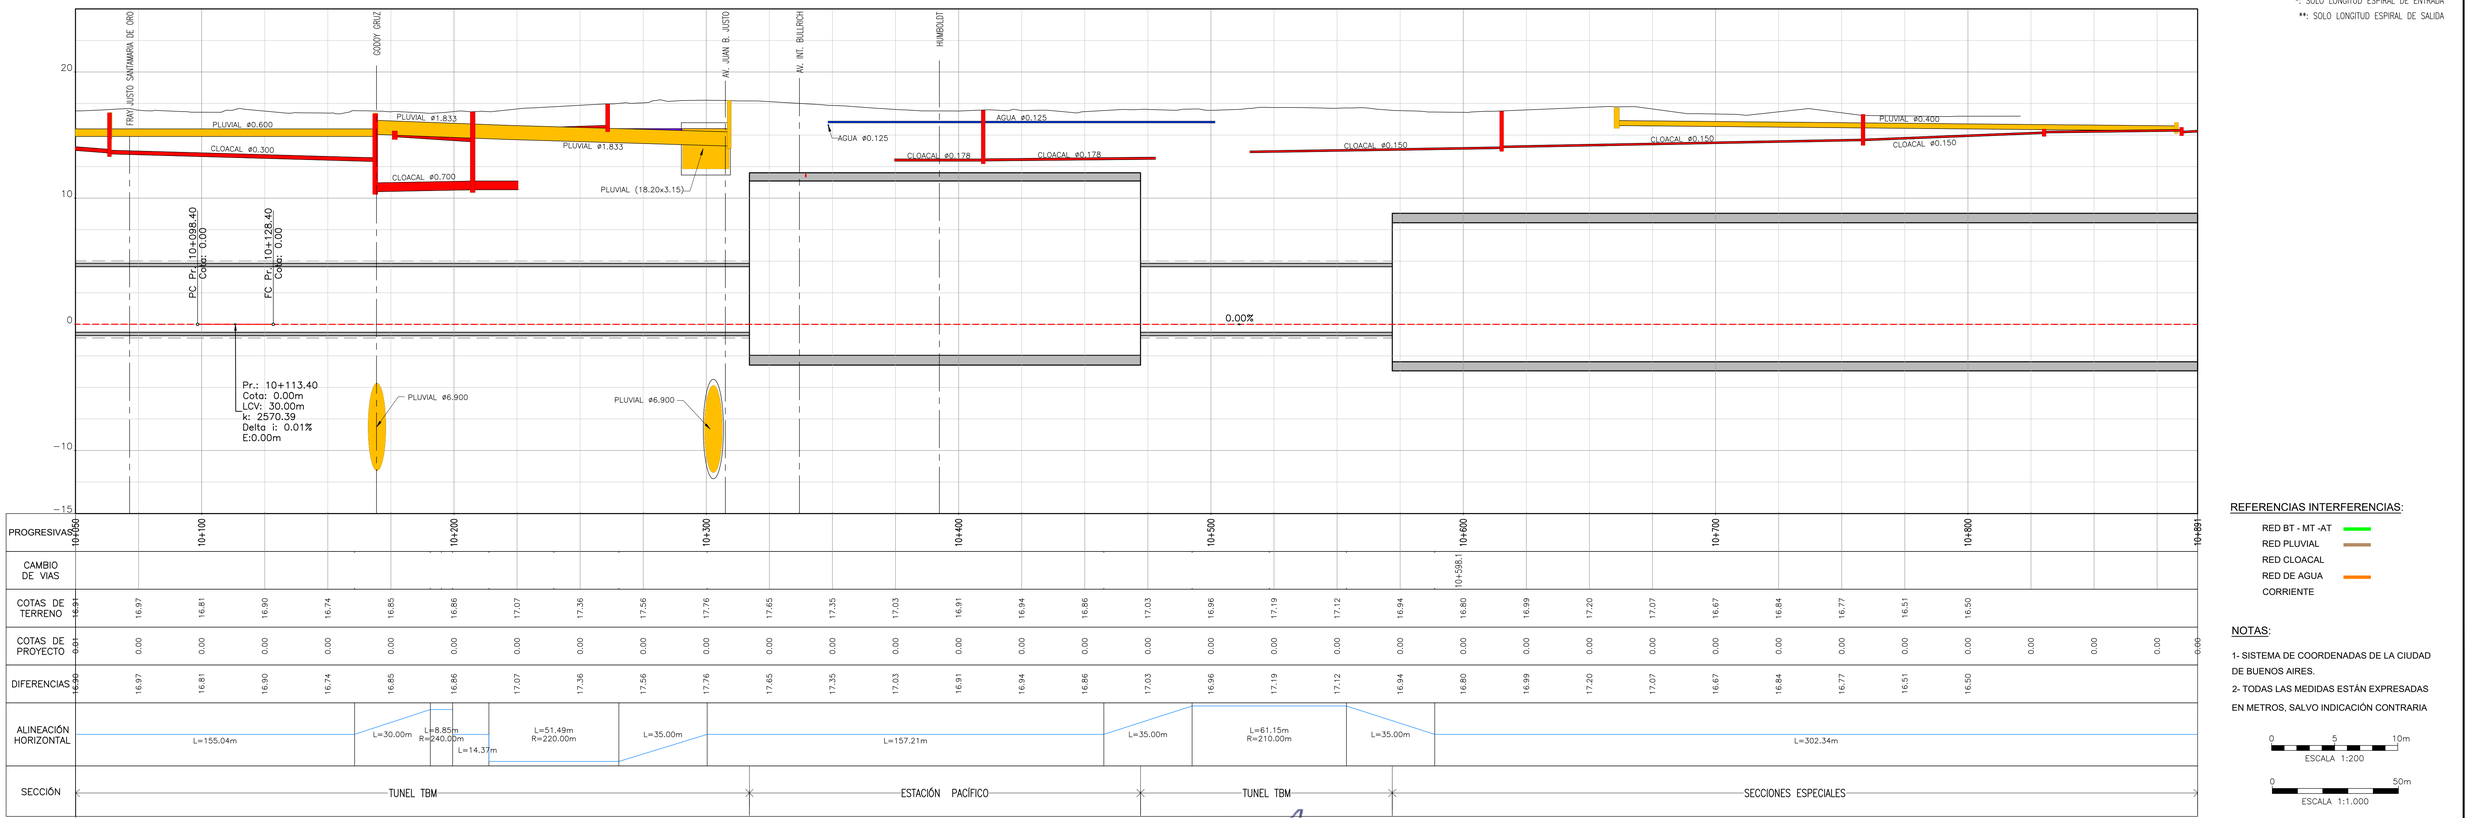

PROGRESIVAS	10+050	10+100	10+200	10+300	10+400	10+500	10+600	10+700	10+800	10+891
CAMBIO DE VIAS							10+598.1			
COTAS DE TERRENO	16.91	16.97 16.81 16.90 16.74 16.85 16.86 17.07 17.36 17.56 17.76			17.65 17.35 17.03 16.91 16.94 16.86 17.03 16.96 17.19 17.12 16.94		16.80 16.99 17.20 17.07 16.67 16.84 16.77 16.51 16.50			
COTAS DE PROYECTO	0.01	0.00 0.00 0.00 0.00 0.00 0.00 0.00 0.00 0.00 0.00			0.00 0.00 0.00 0.00 0.00 0.00 0.00 0.00 0.00 0.00 0.00		0.00 0.00 0.00 0.00 0.00 0.00 0.00 0.00 0.00 0.00			0.00
DIFERENCIAS	16.90	16.97 16.81 16.90 16.74 16.85 16.86 17.07 17.36 17.56 17.76			17.65 17.35 17.03 16.91 16.94 16.86 17.03 16.96 17.19 17.12 16.94		16.80 16.99 17.20 17.07 16.67 16.84 16.77 16.51 16.50			
ALINEACIÓN HORIZONTAL	L=155.04m	L=30.00m	L=8.85m R=240.00m	L=14.37m	L=51.49m R=220.00m	L=35.00m	L=157.21m	L=35.00m	L=61.15m R=210.00m	L=35.00m L=302.34m
SECCIÓN	TUNEL TBM				ESTACIÓN PACÍFICO		TUNEL TBM			SECCIONES ESPECIALES

REFERENCIAS INTERFERENCIAS:

- RED BT - MT -AT
- RED PLUVIAL
- RED CLOACAL
- RED DE AGUA
- CORRIENTE

NOTAS:

1- SISTEMA DE COORDENADAS DE LA CIUDAD DE BUENOS AIRES.

2- TODAS LAS MEDIDAS ESTÁN EXPRESADAS EN METROS, SALVO INDICACIÓN CONTRARIA

0 5 10m
ESCALA 1:200

0 50m
ESCALA 1:1.000

NOTAS:
EL PRESENTE PLANO ES INDICATIVO. LA CONTRATISTA CONFECCIONARÁ LOS PLANOS DE DETALLE DEFINITIVO, QUE DEBERÁN SER APROBADOS POR LA D.G.OBRAS Y LA INSPECCIÓN DE OBRA, EL PLANO PRESENTADO POR LA CONTRATISTA ESTARÁ EN UN TODO DE ACUERDO CON LA NORMATIVA VIGENTE.
TODAS LAS MEDIDAS Y NIVELES SE VERIFICARÁN EN OBRA POR EL CONTRATISTA.
TODOS LOS DETALLES CONSTRUCTIVOS SERÁN COORDINADOS Y COMPATIBILIZADOS EN OBRA

PLANO NO APTO PARA CONSTRUCCION

Ing. Mariano Miculicich
DIRECTOR

MODIFICACIONES:

REVISION	FECHA	DESCRIPCION
0	14/01/2026	EMISIÓN INICIAL

MINISTERIO DE INFRAESTRUCTURA
SUBSECRETARIA DE PROYECTOS Y OBRAS
DIRECCION GENERAL DE PROYECTOS

DGPRO

Obra: LINEA F — IF-2026-20223041-GCABA-APRA — Plano Nº 006
Plano: TRAZADO DE VÍAS - PLANIALTIMETRÍA VÍA ASCENDENTE - PR. 10+050 A 10+900 — LF-VI-T02-VIA-PL-006
Fecha: 14/01/2026 — Eq. de Proyecto: UPU-ATEC-IATASA — Dibujó: N.S. — Revisó: G.D.R. — Escala: Indicada

15/1/2026 10:44 a. m.
LF-VI-T02-VIA-PL-001-009 - PLANIALTIMETRIA T2 - VIA ASC.dwg

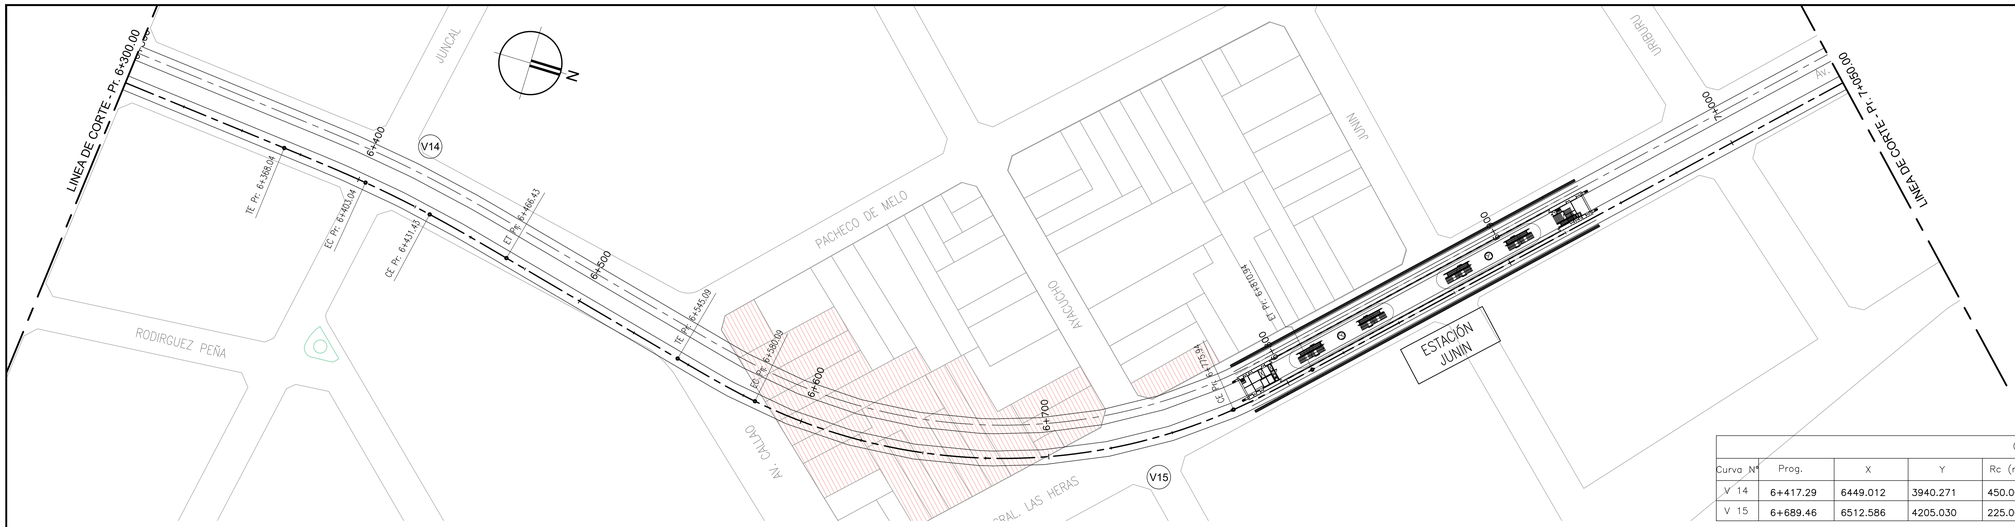

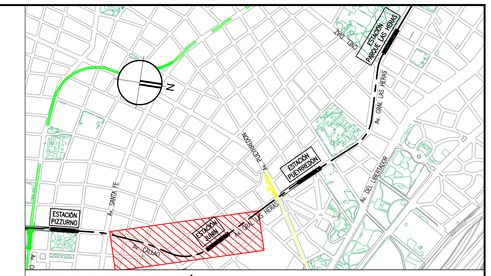

CROQUIS DE UBICACIÓN

CURVAS HORIZONTALES											
Curva N°	Prog.	X	Y	Rc (m)	Le (m)	Δ	Des (m)	Tan (m)	E (m)	VD (km/h)	PERALTE (mm)
V 14	6+417.29	6449.012	3940.271	450.00	35.00	8° 04' 14"	98.39	49.25	1.23	70	67
V 15	6+689.46	6512.586	4205.030	225.00	35.00	58° 47' 06"	265.85	144.37	33.50	45	67

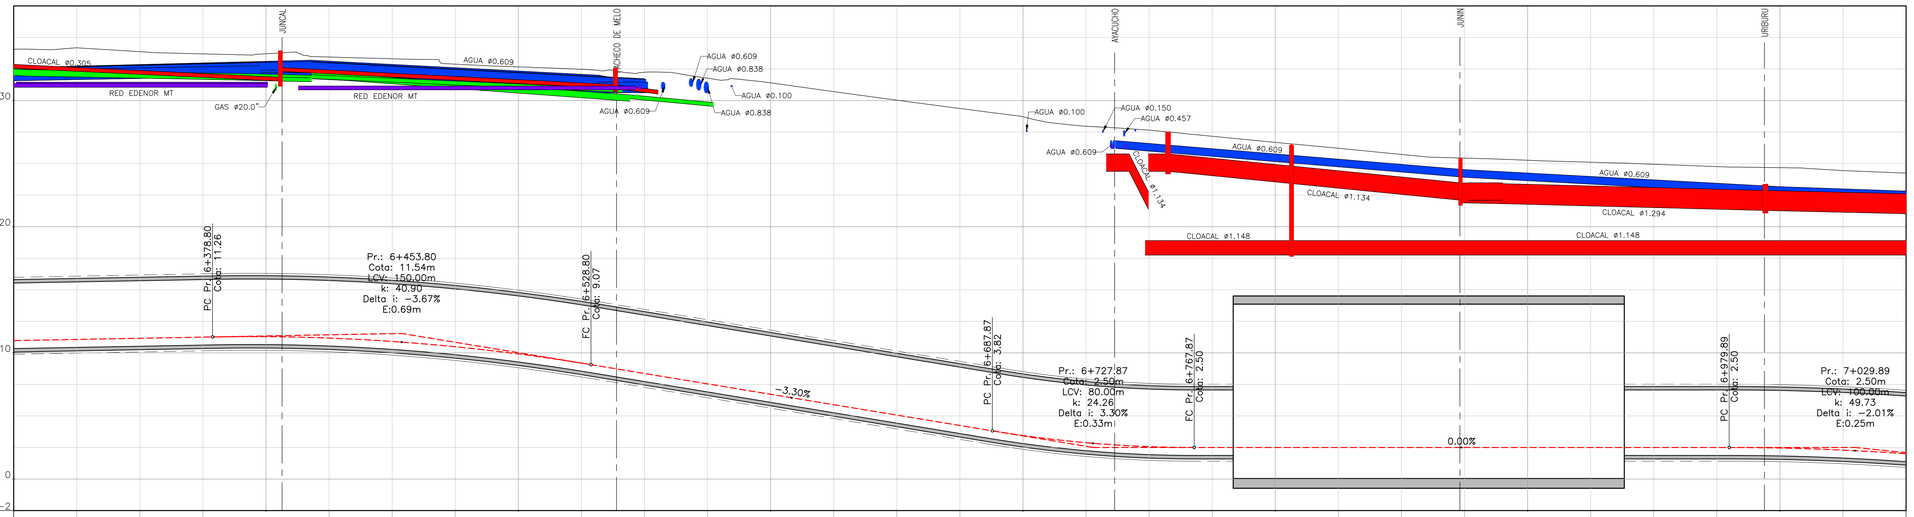

PROGRESIVAS	6+300	6+400	6+500	6+600	6+700	6+800	6+900	7+000	7+050
CAMBIO DE VIAS									
COTAS DE TERRENO	34.66 34.18 33.87 33.70 33.70 33.45 33.31 32.88 32.67 32.47 32.24 31.77 31.40 30.71 30.03 29.37 28.72 27.96 27.65 27.17 26.68 26.22 25.72 25.43 25.27 25.11 24.95 24.76 24.68 24.45 24.24								
COTAS DE PROYECTO	10.97 11.06 11.16 11.25 11.29 11.17 10.91 10.49 9.91 9.19 8.37 7.54 6.72 5.89 5.07 4.24 3.45 2.88 2.57 2.50 2.50 2.50 2.50 2.50 2.50 2.50 2.50 2.50 2.50 2.46 2.30 2.01 2.24								
DIFERENCIAS	23.69 23.11 22.72 22.45 22.42 22.28 22.40 22.40 22.75 23.29 23.87 24.22 24.68 24.81 24.96 25.13 25.27 25.08 25.09 24.67 24.18 23.72 23.22 22.93 22.77 22.61 22.45 22.26 22.22 22.15 22.24								
ALINEACIÓN HORIZONTAL	L=144.38m	L=35.00m	L=28.39m R=450.00m	L=35.00m	L=78.66m	L=35.00m	L=195.85m R=225.00m	L=35.00m	L=543.30m
SECCIÓN	TUNEL TBM					ESTACIÓN JUNIN		TUNEL TBM	

REFERENCIAS INTERFERENCIAS:

- RED BT - MT -AT
- RED PLUVIAL
- RED CLOACAL
- RED DE AGUA CORRIENTE
- RED DE GAS
- RED DE FIBRA OPTICA
- RED TELEFÓNICA

NOTAS:

1- SISTEMA DE COORDENADAS DE LA CIUDAD DE BUENOS AIRES.

2- TODAS LAS MEDIDAS ESTÁN EXPRESADAS EN METROS, SALVO INDICACIÓN CONTRARIA

0 5 10m — ESCALA 1:200

0 50m — ESCALA 1:1.000

NOTAS: EL PRESENTE PLANO ES INDICATIVO. LA CONTRATISTA CONFECCIONARA LOS PLANOS DE DETALLE CORRESPONDIENTES, QUE DEBERAN SER APROBADOS POR LA D.G.OBR.SY.T.U.A. PREVIO A SU INSPECCION DE OBRA. EL PLANO PRESENTADO POR LA CONTRATISTA ESTARA EN TODO DE ACUERDO CON LA NORMATIVA VIGENTE.
TODAS LAS MEDIDAS Y NIVELES SE VERIFICARAN EN OBRA POR EL CONTRATISTA.
TODOS LOS DETALLES CONSTRUCTIVOS SERAN COORDINADOS Y COMPATIBILIZADOS EN OBRA

PLANO NO APTO PARA CONSTRUCCION.

Ing. Mariano Miculicich
DIRECTOR

MODIFICACIONES:

REVISION	FECHA	DESCRIPCION
1	14/01/2026	EMISION INICIAL

MINISTERIO DE INFRAESTRUCTURA
SUBSECRETARIA DE PROYECTOS Y OBRAS
DIRECCION GENERAL DE PROYECTOS

DGPRO

Obra: LINEA F			IF-2026-20223041-GCABA-APRA Plano N°
Plano: TRAZADO DE VÍAS - PLANIALTIMETRÍA VÍA DESCENDENTE - PR. 6+300 A 7+050			LF-VI-T02-VIA-PL-007
Fecha: 14/01/2026	Eq. de Proyecto: UPU-ATEC-IATASA	Dibujó: N.S.	Revisó: G.D.R. Escala: Indicada 007

14/1/2026 16:56 p. m.
LF-VI-T02-VIA-PL-010-015 - PLANIALTIMETRIA T2 - VIA DESC.dwg

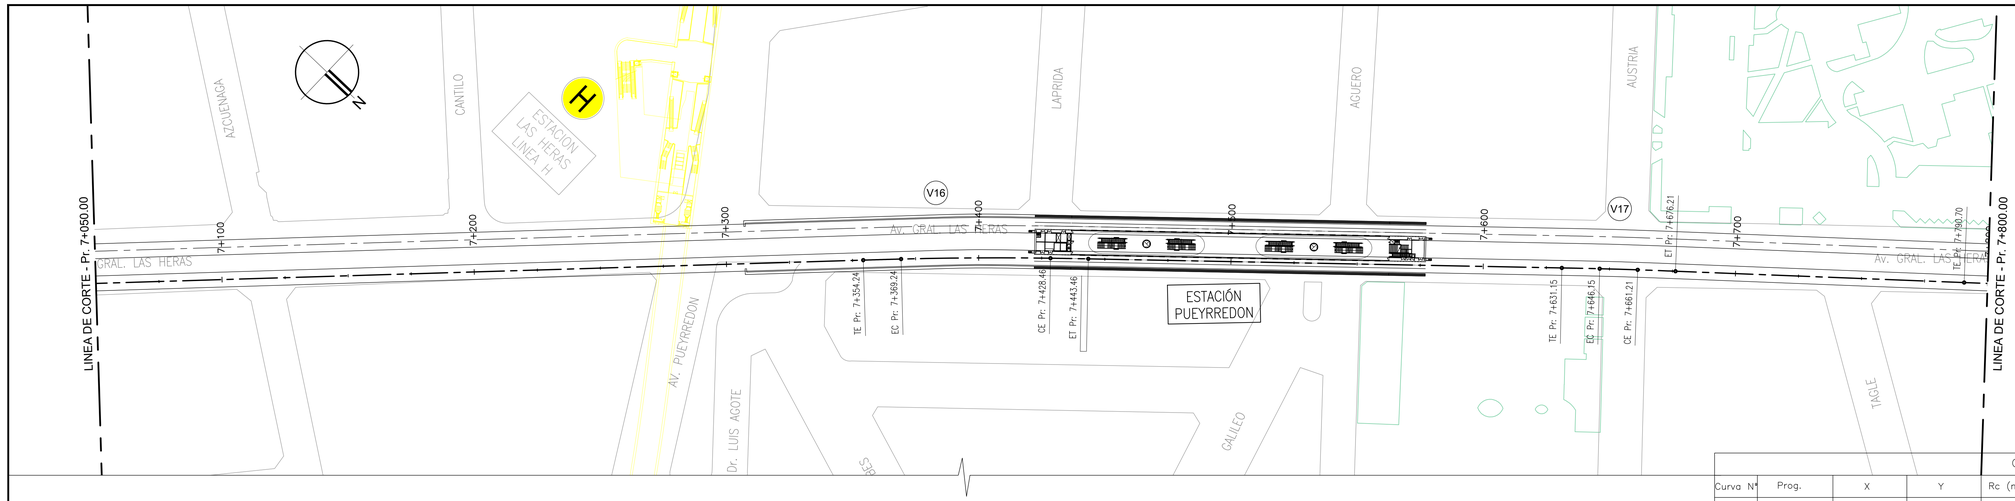

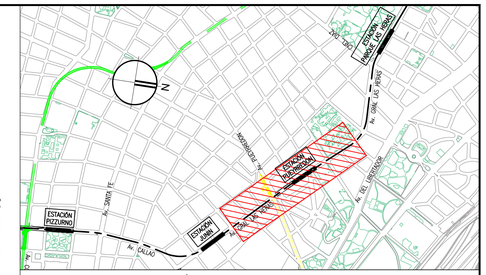

CROQUIS DE UBICACIÓN

CURVAS HORIZONTALES											
Curva N°	Prog.	X	Y	Rc (m)	Le (m)	Δ	Des (m)	Tan (m)	E (m)	VD (km/h)	PERALTE (mm)
V 16	7+398.86	5992.234	4720.269	1500.00	15.00	2° 50' 05"	89.21	44.61	0.47	90	30
V 17	7+653.68	5820.236	4908.312	1500.00	15.00	1° 08' 54"	45.07	22.53	0.08	90	30

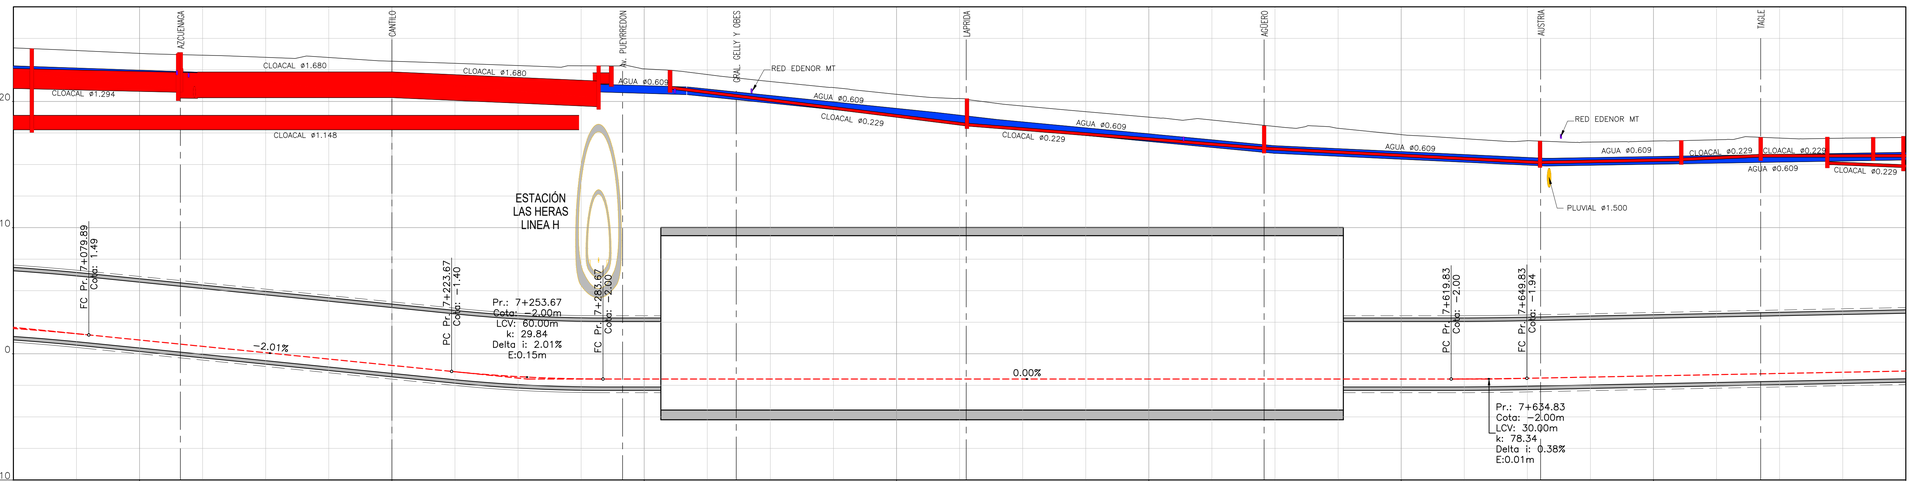

| | | | | | | | | | | |

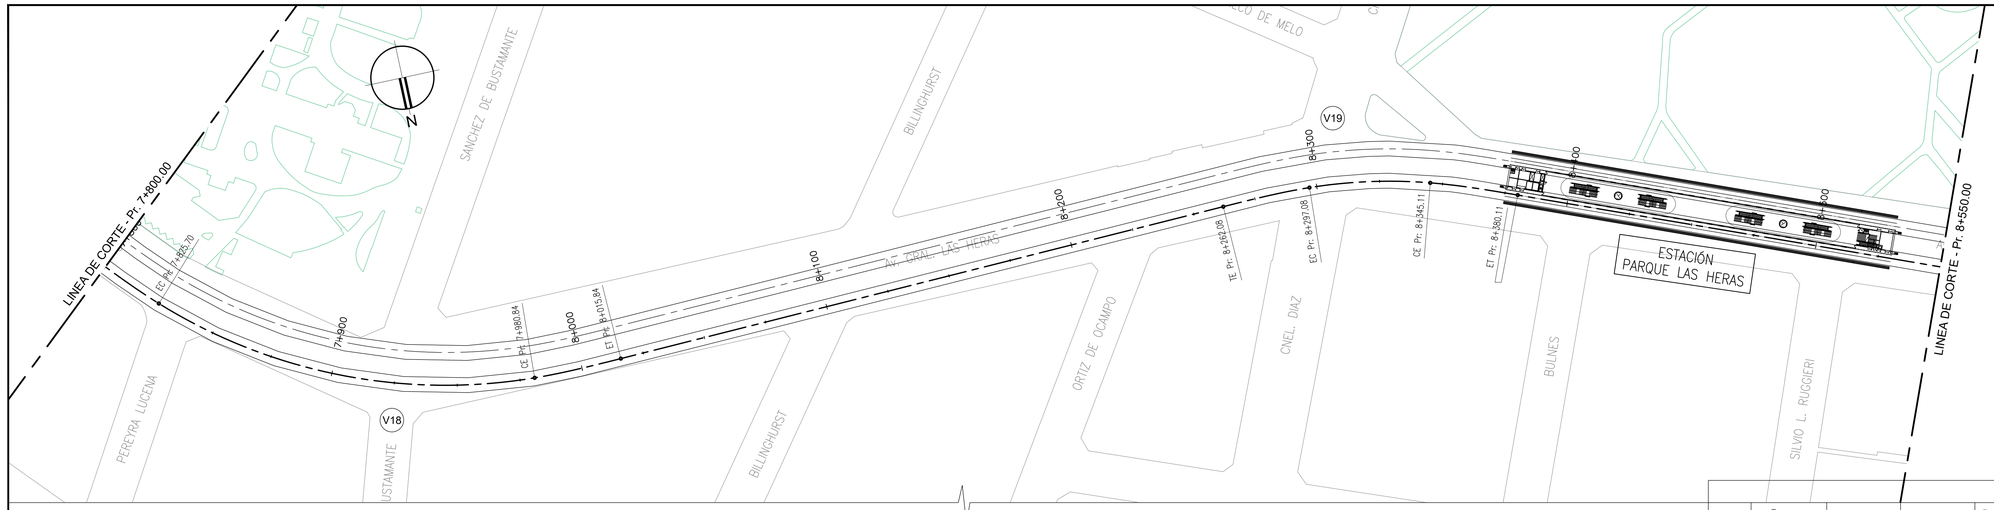

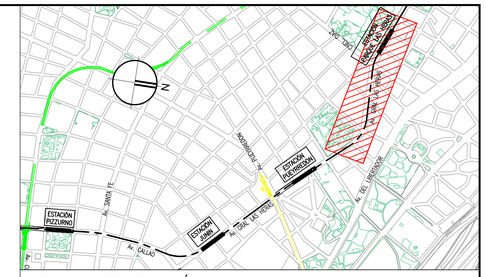

CROQUIS DE UBICACIÓN

CURVAS HORIZONTALES											
Curva Nº	Prog.	X	Y	Rc (m)	Le (m)	Δ	Des (m)	Tan (m)	E (m)	VD (km/h)	PERALTE (mm)
V 18	7+910.10	5650.998	5100.953	215.00	35.00	50° 40' 19"	225.14	119.40	23.14	45	70
V 19	8+321.75	5225.936	5086.320	200.00	35.00	23° 47' 18"	118.04	59.67	4.65	45	70

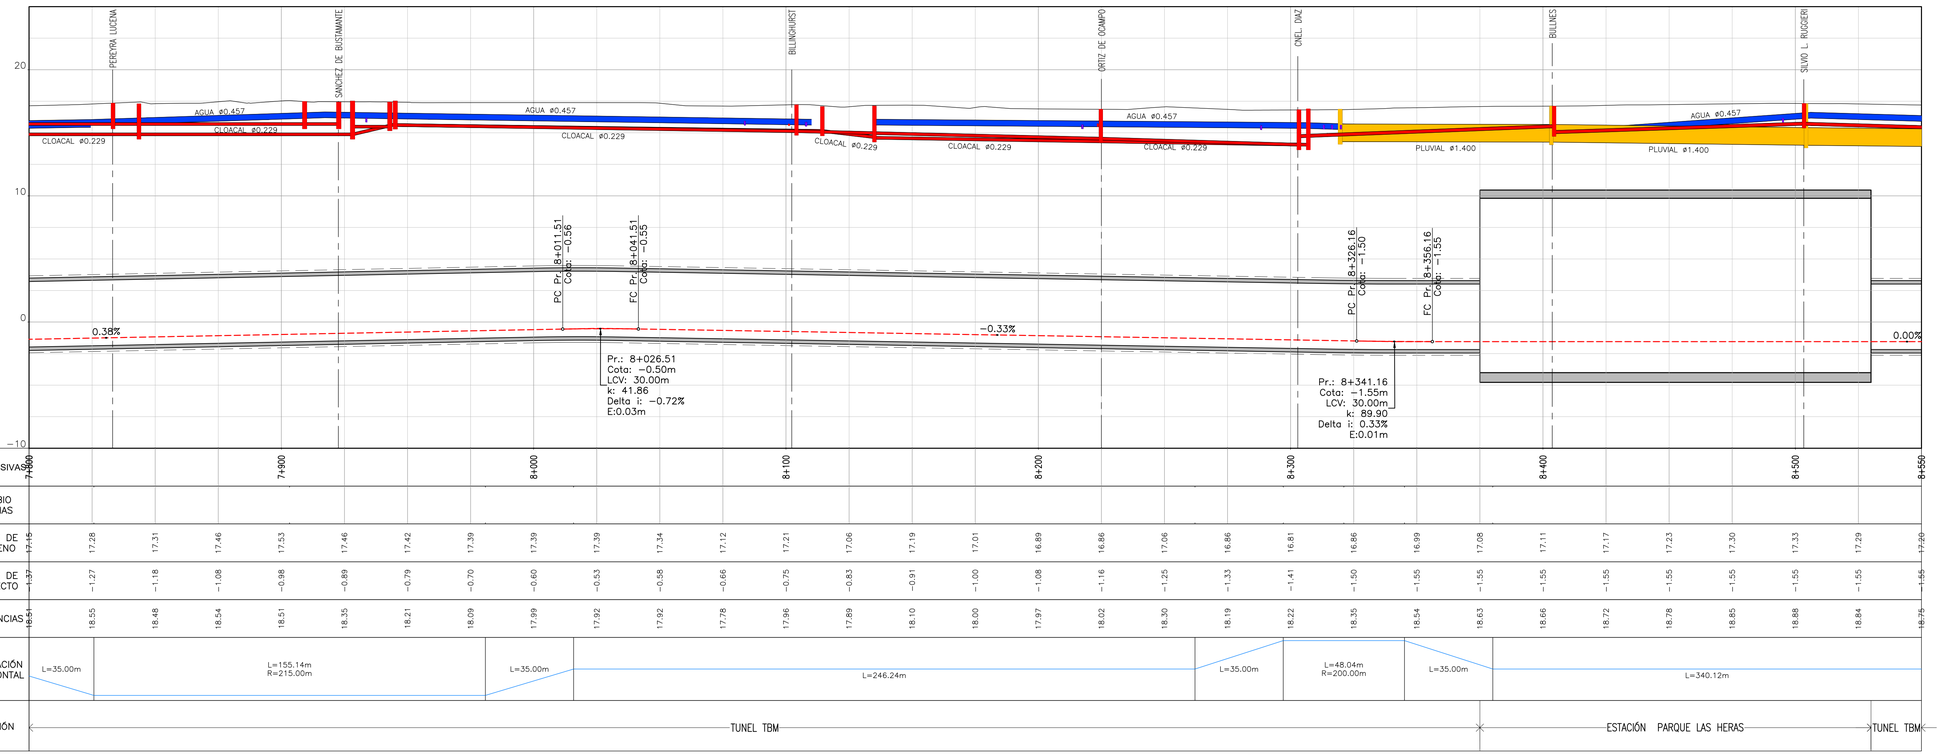

REFERENCIAS INTERFERENCIAS:

- RED BT - MT -AT
- RED PLUVIAL
- RED CLOACAL
- RED DE AGUA CORRIENTE
- RED DE GAS
- RED DE FIBRA OPTICA
- RED TELEFÓNICA

NOTAS:

1- SISTEMA DE COORDENADAS DE LA CIUDAD DE BUENOS AIRES.

2- TODAS LAS MEDIDAS ESTÁN EXPRESADAS EN METROS, SALVO INDICACIÓN CONTRARIA

0 5 10m — ESCALA 1:200

0 50m — ESCALA 1:1.000

NOTAS: EL PRESENTE PLANO ES INDICATIVO. LA CONTRATISTA CONFECCIONARA LOS PLANOS DE DETALLE DEFINITIVO, QUE DEBERAN SER APROBADOS POR LA D.G.OBR.U.Y LA INSPECCION DE OBRA. EL PLANO PRESENTADO POR LA CONTRATISTA ESTARA EN TODO DE ACUERDO CON LA NORMATIVA VIGENTE.
TODAS LAS MEDIDAS Y NIVELES SE VERIFICARAN EN OBRA POR EL CONTRATISTA.
TODOS LOS DETALLES CONSTRUCTIVOS SERAN COORDINADOS Y COMPATIBILIZADOS EN OBRA

PLANO NO APTO PARA CONSTRUCCION.

Ing. Mariano Miculicich
DIRECTOR

MODIFICACIONES:

REVISION	FECHA	DESCRIPCION
	MES/DIA	EMISION INICIAL

MINISTERIO DE INFRAESTRUCTURA
SUBSECRETARIA DE PROYECTOS Y OBRAS
DIRECCION GENERAL DE PROYECTOS

DGPRO

Obra: LINEA F — IF-2026-20223041-GCABA-APRA — Plano Nº 009

Plano: TRAZADO DE VÍAS - PLANIALTIMETRÍA VÍA DESCENDENTE - PR. 7+800 A 8+550 — LF-VI-T02-VIA-PL-009

Fecha: 14/01/2026 | Eq. de Proyecto: UPU-ATEC-IATASA | Dibujó: N.S. | Revisó: G.D.R. | Escala: Indicada

14/1/2026 16:56 p. m.
LF-VI-T02-VIA-PL-010-015 - PLANIALTIMETRIA T2 - VIA DESC.dwg

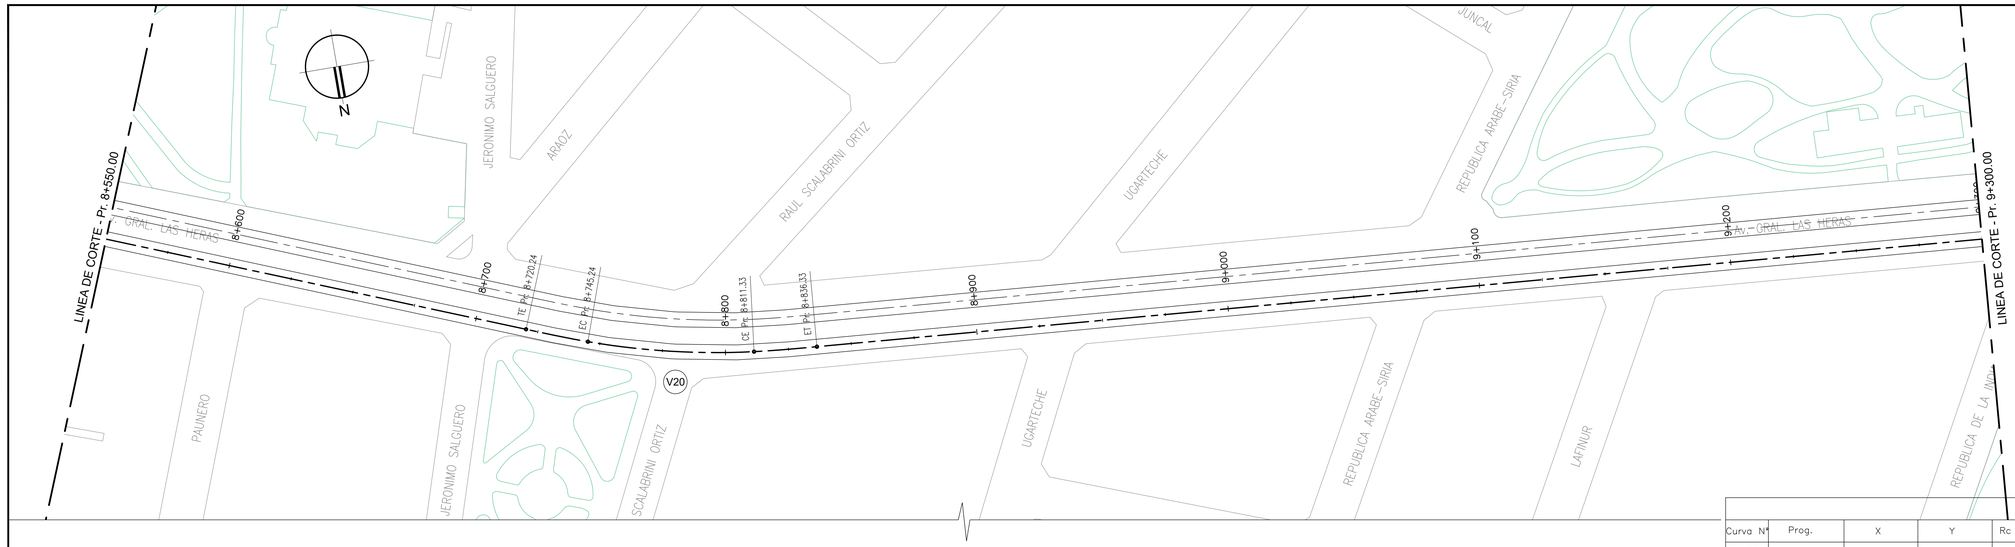

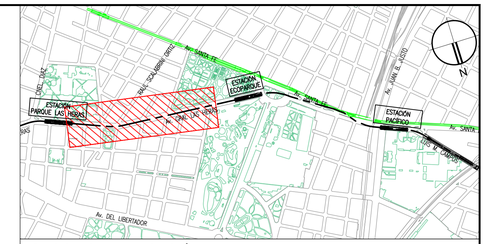

CROQUIS DE UBICACIÓN

CURVAS HORIZONTALES											
Curva N°	Prog.	X	Y	Rc (m)	Le (m)	Δ	Des (m)	Tan (m)	E (m)	VD (km/h)	PERALTE (mm)
V 20	8+778.65	4800.546	5256.608	300.00	25.00	17° 23' 47"	116.09	58.41	3.58	45	50

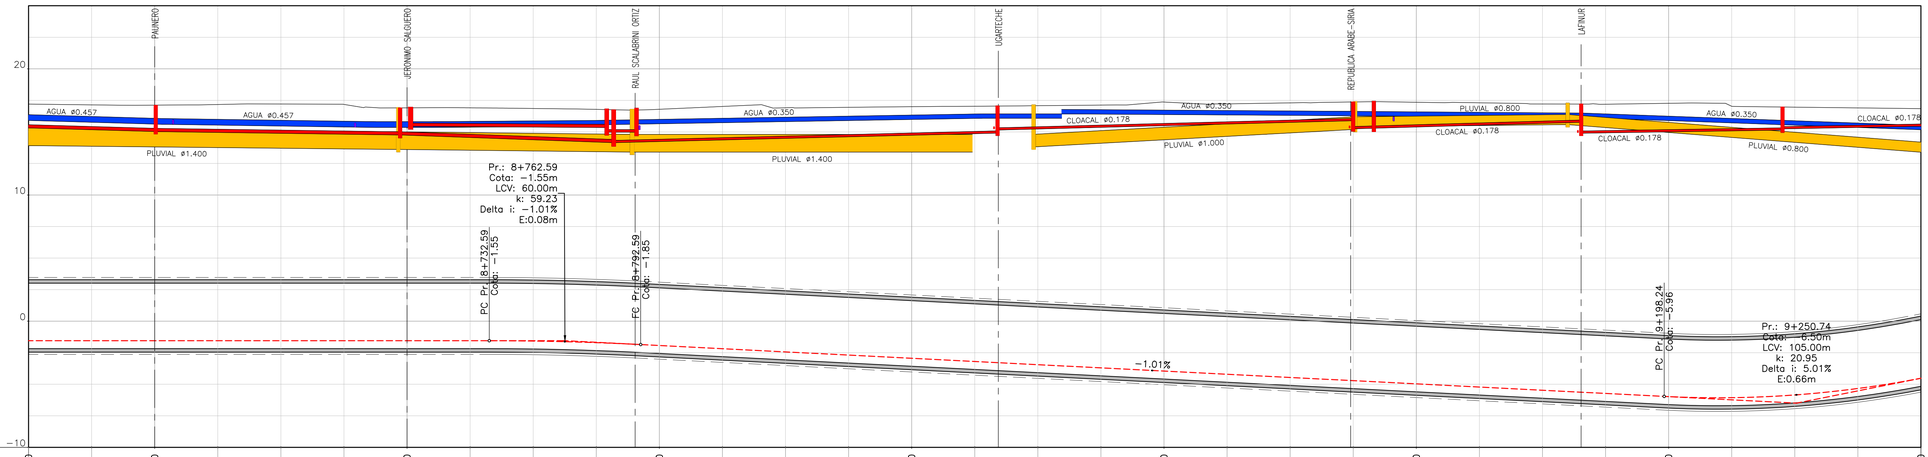

| | | | | | | | | | | |

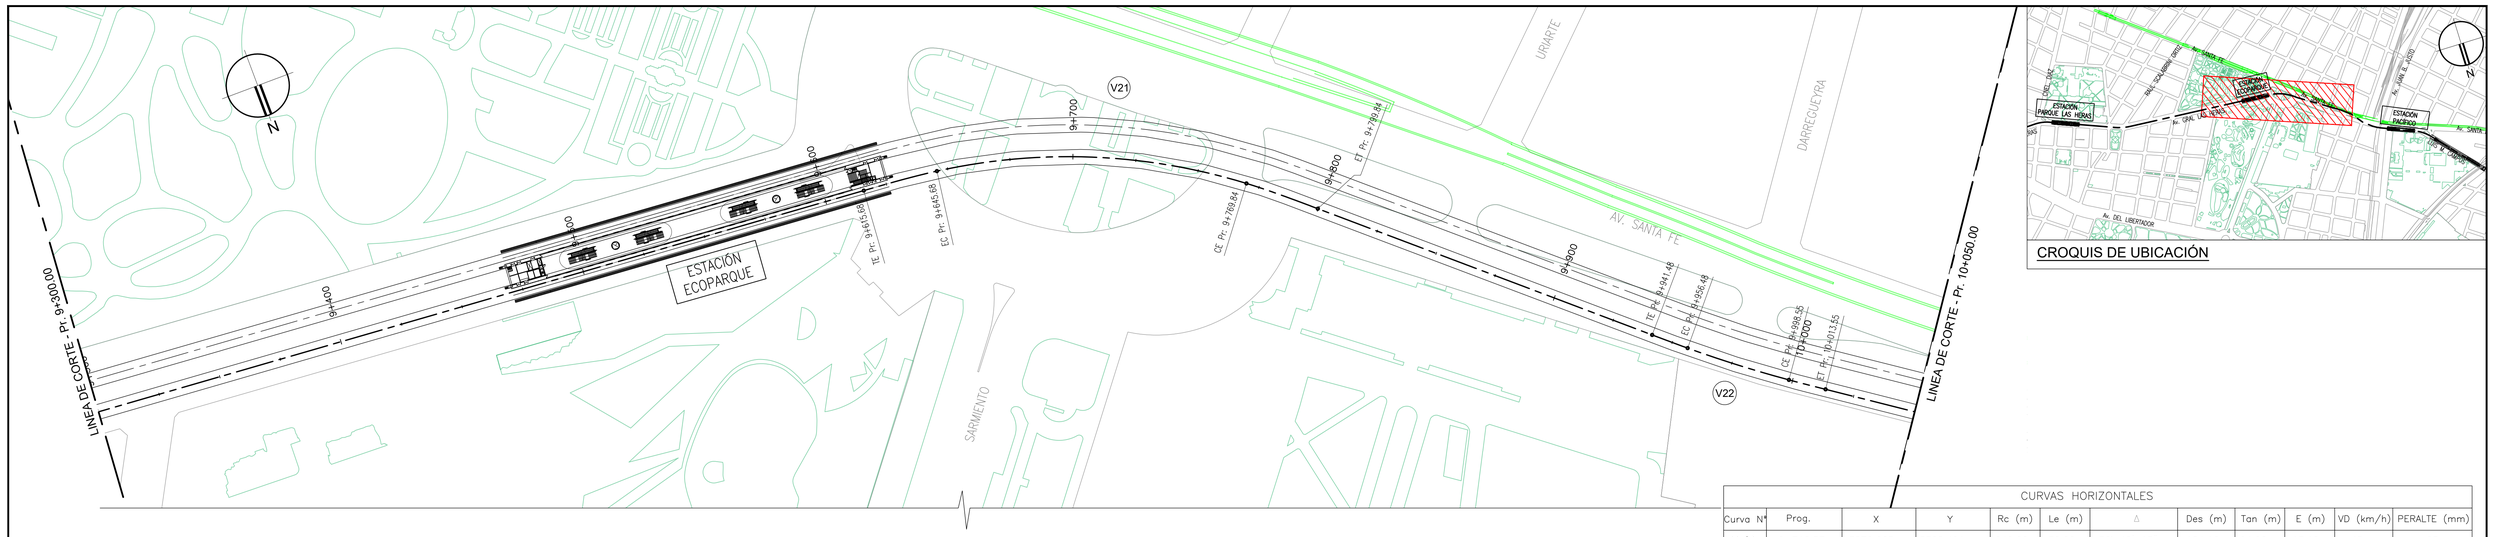

CROQUIS DE UBICACIÓN

CURVAS HORIZONTALES

Curva Nº	Prog.	X	Y	Rc (m)	Le (m)	Δ	Des (m)	Tan (m)	E (m)	VD (km/h)	PERALTE (mm)
V 21	9+710.57	3870.665	5328.491	240.00	30.00	36° 48' 13"	184.16	94.90	13.10	45	63
V 22	9+977.54	3665.631	5508.135	500.00	15.00	6° 32' 24"	72.07	36.07	0.83	45	30

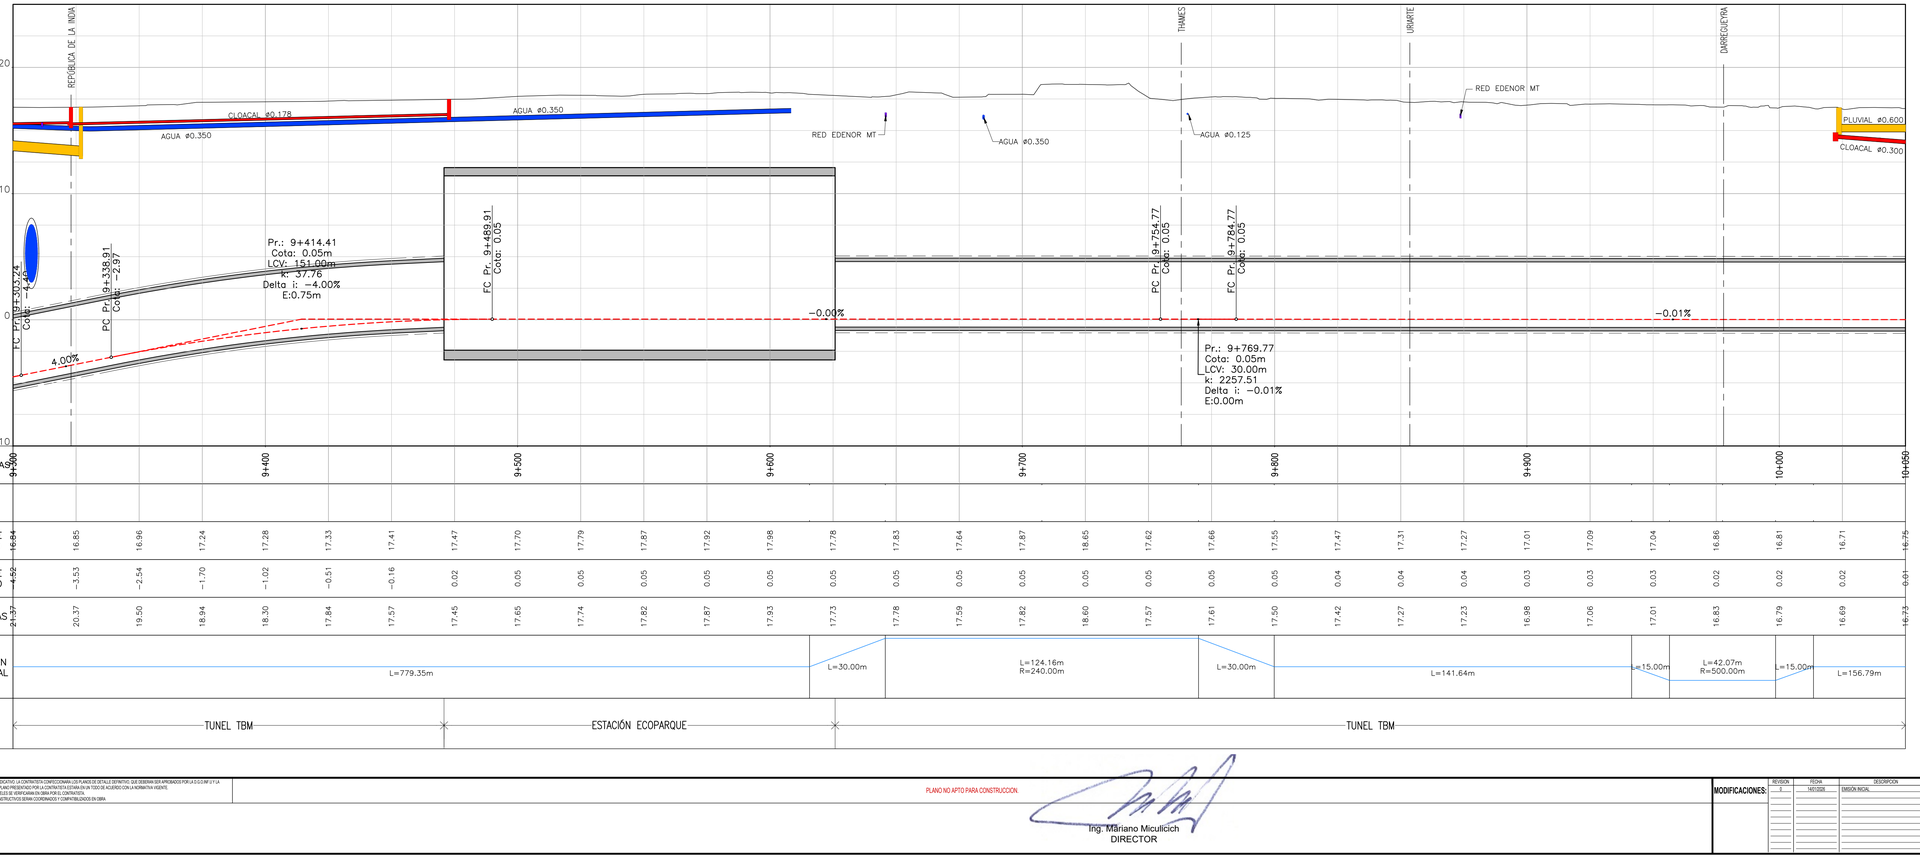

PROGRESIVA	9+300	9+400	9+500	9+600	9+700	9+800	9+900	10+000	10+050
CAMBIO DE VIAS									
COTAS DE TERRENO	16.84	16.85 16.96 17.24 17.28 17.33 17.41 17.47 17.70 17.79 17.87 17.92 17.98 17.78 17.83 17.64 17.87 18.65 17.62 17.66 17.55 17.47 17.31 17.27 17.01 17.09 17.04 16.86 16.81 16.71							16.75
COTAS DE PROYECTO	4.52	−3.53 −2.54 −1.70 −1.02 −0.51 −0.16 0.02 0.05 0.05 0.05 0.05 0.05 0.05 0.05 0.05 0.05 0.05 0.05 0.05 0.04 0.04 0.04 0.03 0.03 0.03 0.02 0.02 0.02							0.01
DIFERENCIAS	21.37	20.37 19.50 18.94 18.30 17.84 17.57 17.45 17.65 17.74 17.82 17.87 17.93 17.73 17.78 17.59 17.82 18.60 17.57 17.61 17.50 17.42 17.27 17.23 16.98 17.06 17.01 16.83 16.79 16.69							16.73
ALINEACIÓN HORIZONTAL		L=779.35m	L=30.00m	L=124.16m R=240.00m	L=30.00m	L=141.64m	L=15.00m	L=42.07m R=500.00m	L=15.00m	L=156.79m	
SECCIÓN		TUNEL TBM		ESTACIÓN ECOPARQUE		TUNEL TBM					

REFERENCIAS INTERFERENCIAS:

- RED BT - MT -AT
- RED PLUVIAL
- RED CLOACAL
- RED DE AGUA CORRIENTE
- RED DE GAS
- RED DE FIBRA OPTICA
- RED TELEFÓNICA

NOTAS:

1- SISTEMA DE COORDENADAS DE LA CIUDAD DE BUENOS AIRES.

2- TODAS LAS MEDIDAS ESTÁN EXPRESADAS EN METROS, SALVO INDICACIÓN CONTRARIA

0 5 10m — ESCALA 1:200

0 50m — ESCALA 1:1.000

NOTAS: EL PRESENTE PLANO ES INDICATIVO. LA CONTRATISTA CONFECCIONARA LOS PLANOS DE DETALLE CONSTRUCTIVO, QUE DEBERAN SER APROBADOS POR LA D.G.ISP. U.T.A. INSPECCION DE OBRA. EL PLANO PRESENTADO POR LA CONTRATISTA ESTARA EN TODO DE ACUERDO CON LA NORMATIVA VIGENTE. TODAS LAS MEDIDAS Y NIVELES SE VERIFICARAN EN OBRA POR EL CONTRATISTA. TODOS LOS DETALLES CONSTRUCTIVOS SERAN COORDINADOS Y COMPATIBILIZADOS EN OBRA.

PLANO NO APTO PARA CONSTRUCCION.

Ing. Mariano Miculicich
DIRECTOR

MODIFICACIONES:

REVISION	FECHA	DESCRIPCION
0	14/1/2026	EMISION INICIAL

MINISTERIO DE INFRAESTRUCTURA
SUBSECRETARIA DE PROYECTOS Y OBRAS
DIRECCION GENERAL DE PROYECTOS

DGPRO

Obra: LÍNEA F		IF-2026-20223041-GCABA-APRA	Plano N°
Plano: TRAZADO DE VÍAS - PLANIALTIMETRÍA VÍA DESCENDENTE - PR. 9+300 A 10+050		LF-VI-T02-VIA-PL-011	011
Fecha: 14/01/2026	Eq. de Proyecto: UPU-ATEC-IATASA	Dibujó: N.S.	Revisó: G.D.R.	Escala: Indicada

14/1/2026 16:56 p. m. - LF-VI-T02-VIA-PL-010-015 - PLANIALTIMETRIA 12 - VIA DESC.dwg

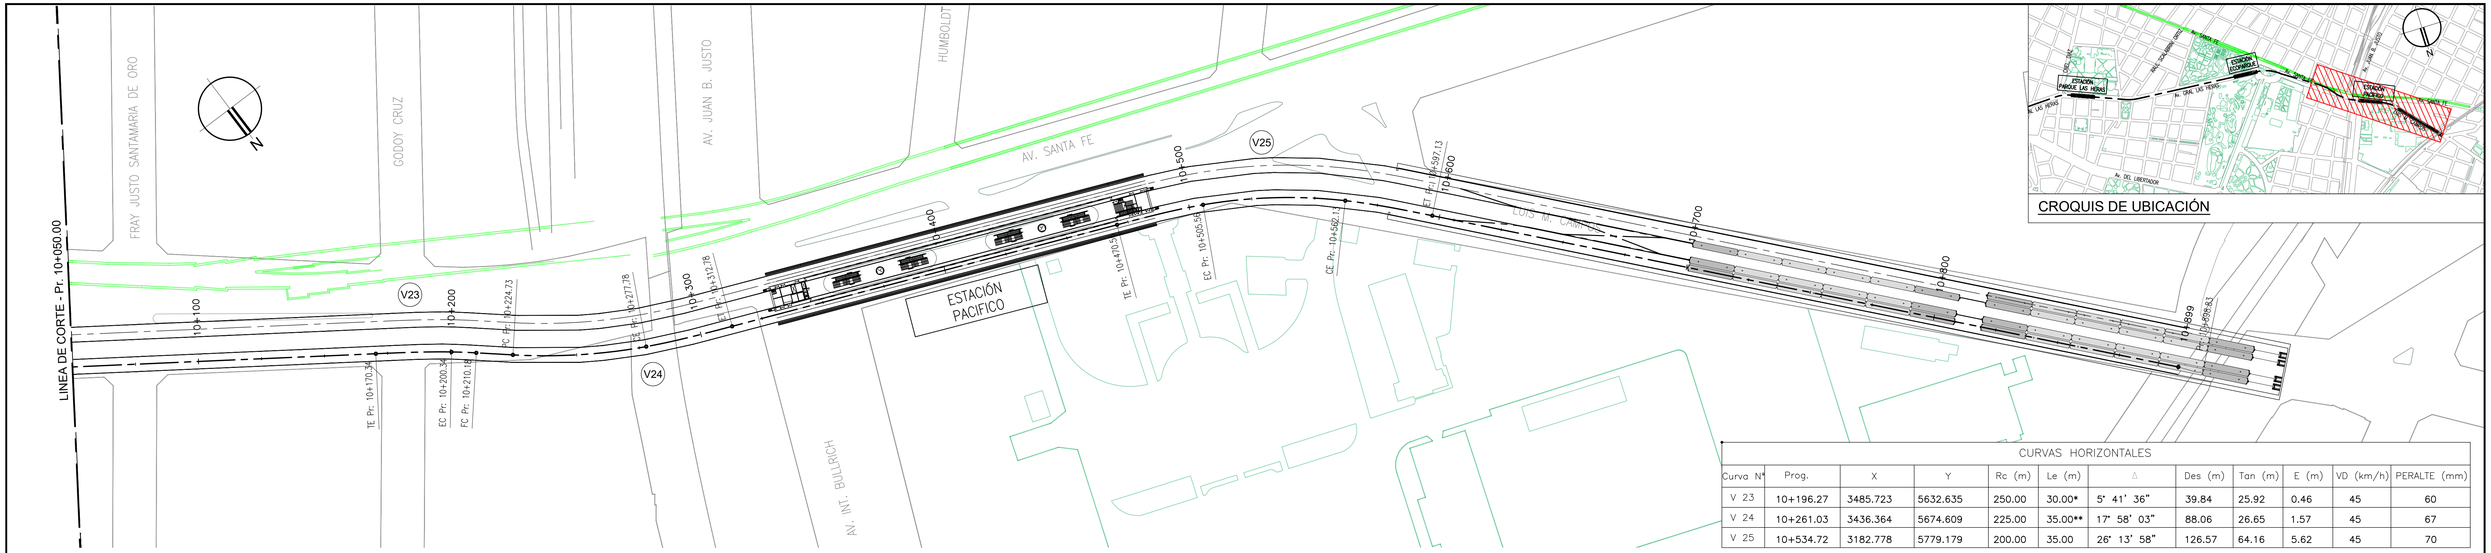

CROQUIS DE UBICACIÓN

CURVAS HORIZONTALES

Curva Nº	Prog.	X	Y	Rc (m)	Le (m)	Δ	Des (m)	Tan (m)	E (m)	VD (km/h)	PERALTE (mm)
V 23	10+196.27	3485.723	5632.635	250.00	30.00*	5° 41' 36"	39.84	25.92	0.46	45	60
V 24	10+261.03	3436.364	5674.609	225.00	35.00**	17° 58' 03"	88.06	26.65	1.57	45	67
V 25	10+534.72	3182.778	5779.179	200.00	35.00	26° 13' 58"	126.57	64.16	5.62	45	70

*: SOLO LONGITUD ESPIRAL DE ENTRADA
**: SOLO LONGITUD ESPIRAL DE SALIDA

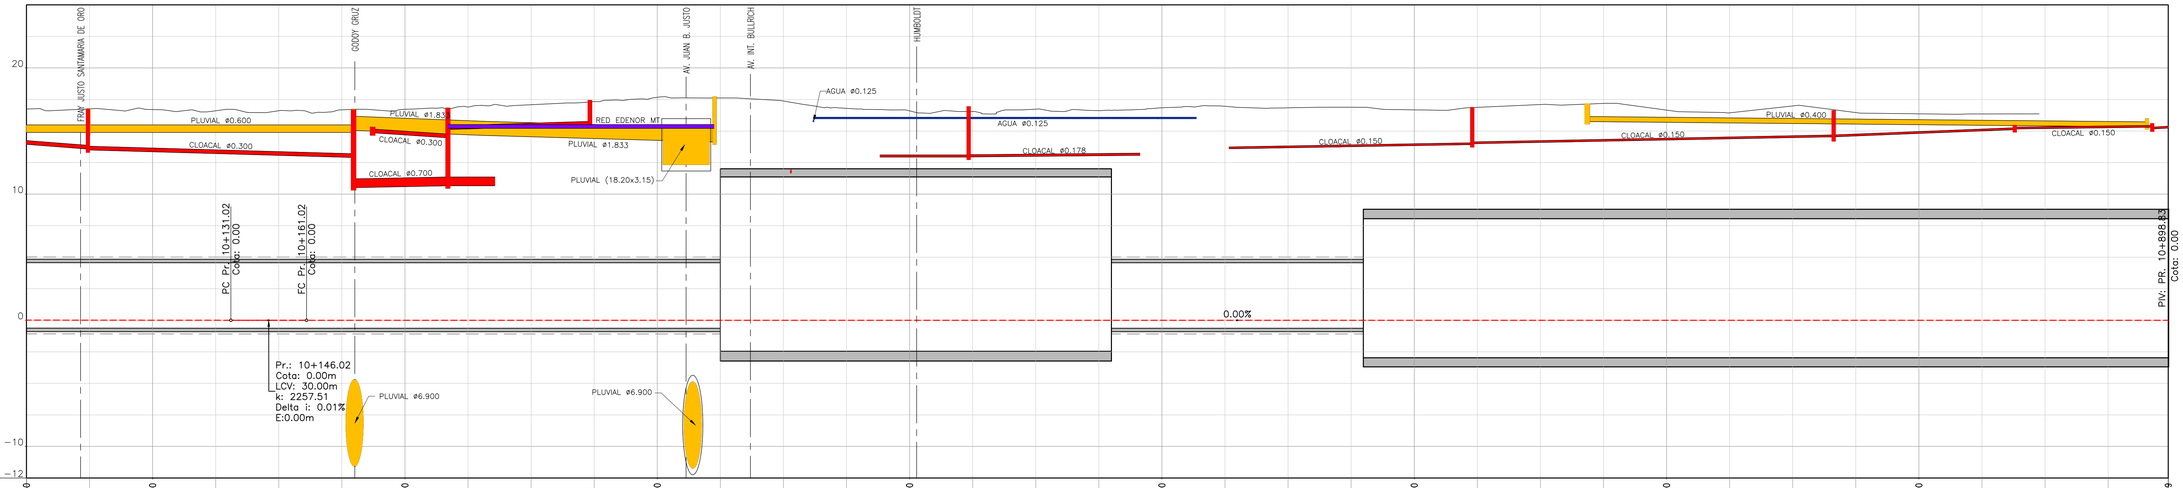

PROGRESIVAS	10+050	10+100	10+200	10+300	10+400	10+500	10+600	10+699	10+800	10+899
CAMBIO DE VIAS							10+606.1			
COTAS DE TERRENO	16.75	16.76	16.70	16.61	16.61	16.68	16.72	16.90	17.09	17.33	17.67	17.62	17.38	16.80	16.60	16.55	16.73	16.62	16.84	16.96	16.84	16.89	16.68	16.88	17.10	17.19	16.66	16.44	16.99	16.46	16.36	16.36			
COTAS DE PROYECTO	0.01	0.01	0.01	0.00	0.00	0.00	0.00	0.00	0.00	0.00	0.00	0.00	0.00	0.00	0.00	0.00	0.00	0.00	0.00	0.00	0.00	0.00	0.00	0.00	0.00	0.00	0.00	0.00	0.00	0.00	0.00	0.00	0.00	0.00	0.00
DIFERENCIAS	16.75	16.75	16.70	16.60	16.61	16.68	16.72	16.90	17.09	17.33	17.67	17.62	17.38	16.80	16.60	16.55	16.73	16.62	16.84	16.96	16.84	16.89	16.68	16.88	17.10	17.19	16.66	16.44	16.99	16.46	16.36	16.36			
ALINEACIÓN HORIZONTAL	L=156.79m					L=30.00m	R=250.00m L=9.84m L=14.54m	L=53.06m R=225.00m		L=35.00m	L=157.78m							L=35.00m	L=56.57m R=200.00m	L=35.00m	L=301.70m														
SECCIÓN	TUNEL TBM										ESTACIÓN PACÍFICO								TUNEL TBM															SECCIONES ESPECIALES		

REFERENCIAS INTERFERENCIAS:

RED BT - MT -AT	RED DE GAS
RED PLUVIAL	RED DE FIBRA OPTICA
RED CLOACAL	
RED DE AGUA CORRIENTE	RED TELEFÓNICA

NOTAS:

1- SISTEMA DE COORDENADAS DE LA CIUDAD DE BUENOS AIRES.

2- TODAS LAS MEDIDAS ESTÁN EXPRESADAS EN METROS, SALVO INDICACIÓN CONTRARIA

0 5 10m
ESCALA 1:200

0 50m
ESCALA 1:1.000

NOTAS: EL PRESENTE PLANO ES INDICATIVO. LA CONTRATISTA CONFECCIONARA LOS PLANOS DE DETALLE DEFINITIVO, QUE DEBERAN SER APROBADOS POR LA D.G.O.M.P.U Y LA INSPECCION DE OBRA. EL PLANO PRESENTADO POR LA CONTRATISTA DEBERA EN UN TODO DE ACUERDO CON LA NORMATIVA VIGENTE. TODAS LAS MEDIDAS Y NIVELES SE VERIFICARAN EN OBRA POR EL CONTRATISTA. TODOS LOS DETALLES CONSTRUCTIVOS SERAN COORDINADOS Y COMPATIBILIZADOS EN OBRA

PLANO NO APTO PARA CONSTRUCCION

Ing. Mariano Miculicich
DIRECTOR

MODIFICACIONES:

REVISIÓN	FECHA	DESCRIPCIÓN
0	14/01/2026	EMISIÓN INICIAL

MINISTERIO DE INFRAESTRUCTURA
SUBSECRETARIA DE PROYECTOS Y OBRAS
DIRECCION GENERAL DE PROYECTOS

DGPRO

Obra: LINEA F			IF-2026-20223041-GCABA-APRA	Plano N°:
Plano: TRAZADO DE VÍAS - PLANIALTIMETRÍA VÍA DESCENDENTE - PR. 10+050 A 10+900			LF-VI-T02-VIA-PL-012	012
Fecha: 14/01/2026	Eq. de Proyecto: UPU-ATEC-IATASA	Dibujó: N.S.	Revisó: G.D.R.	Escala: Indicada

14/1/2026 16:56 p. m.
LF-VI-T02-VIA-PL-010-015 - PLANIALTIMETRIA T2 - VIA DESC.dwg

INTERFERENCIAS
SERVICOS CLOACALES, PLUVIALES, AGUA CORRIENTE
ESCALA 1:500

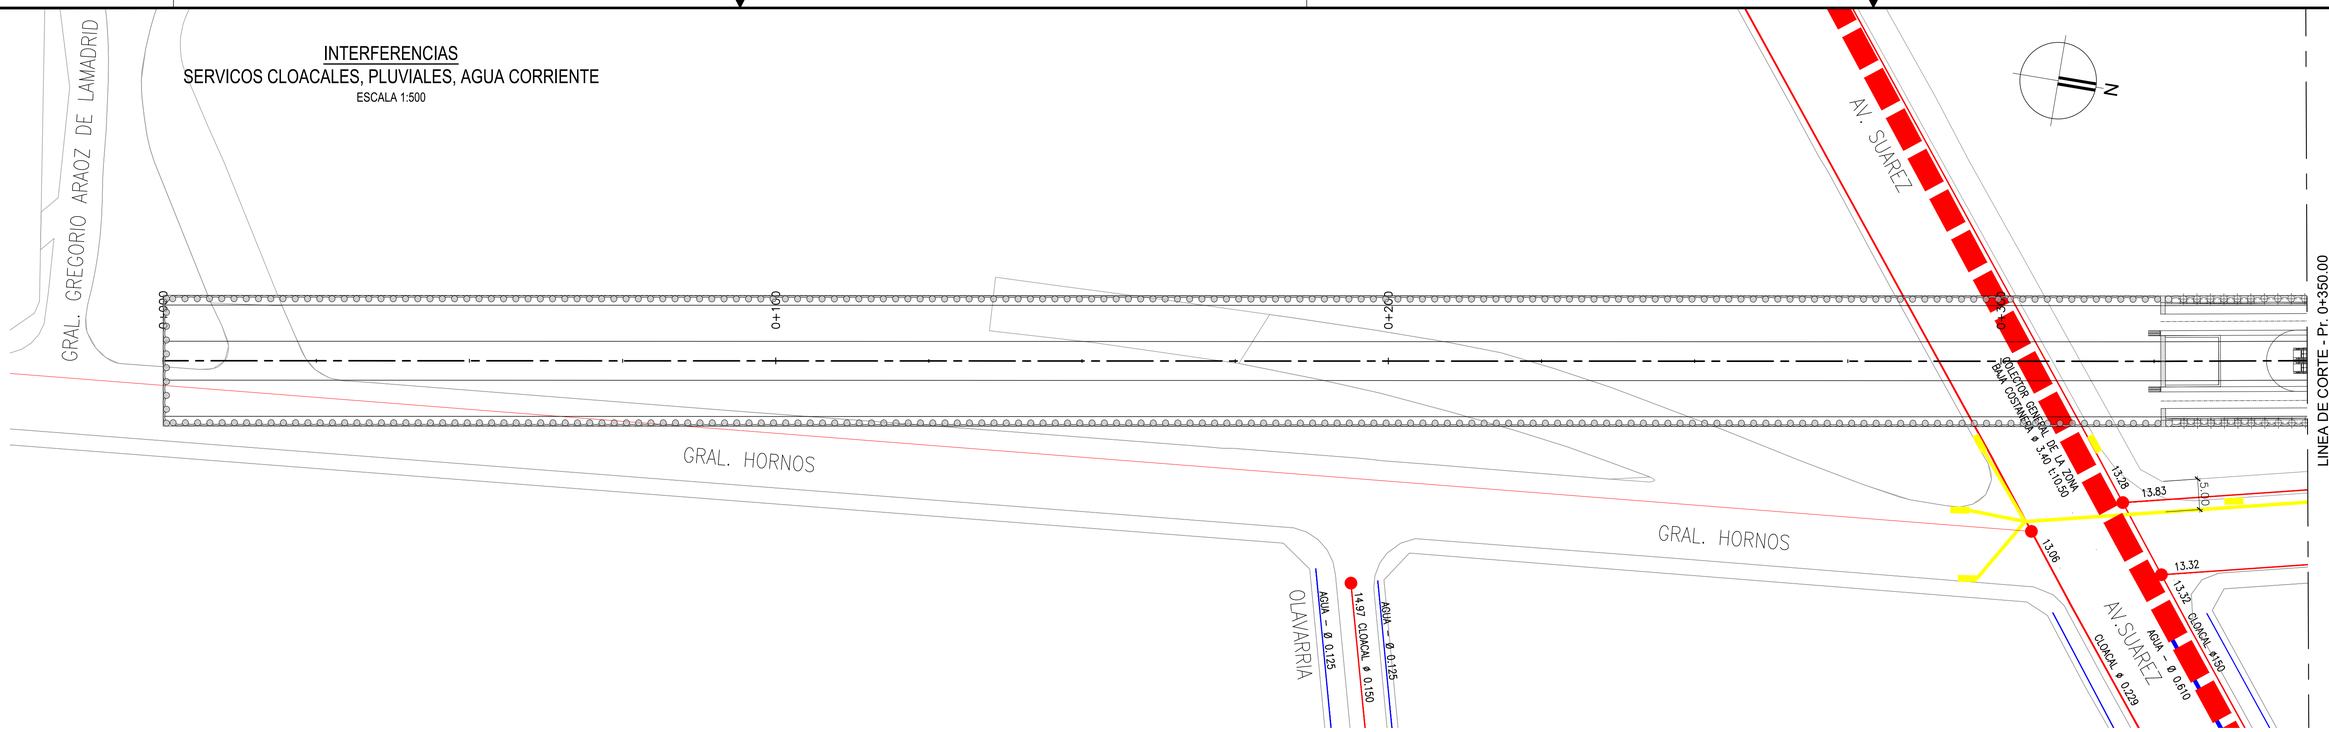

INTERFERENCIAS
GAS, TELEFONIA, ELECTRICIDAD, FIBRA OPTICA
ESCALA 1:500

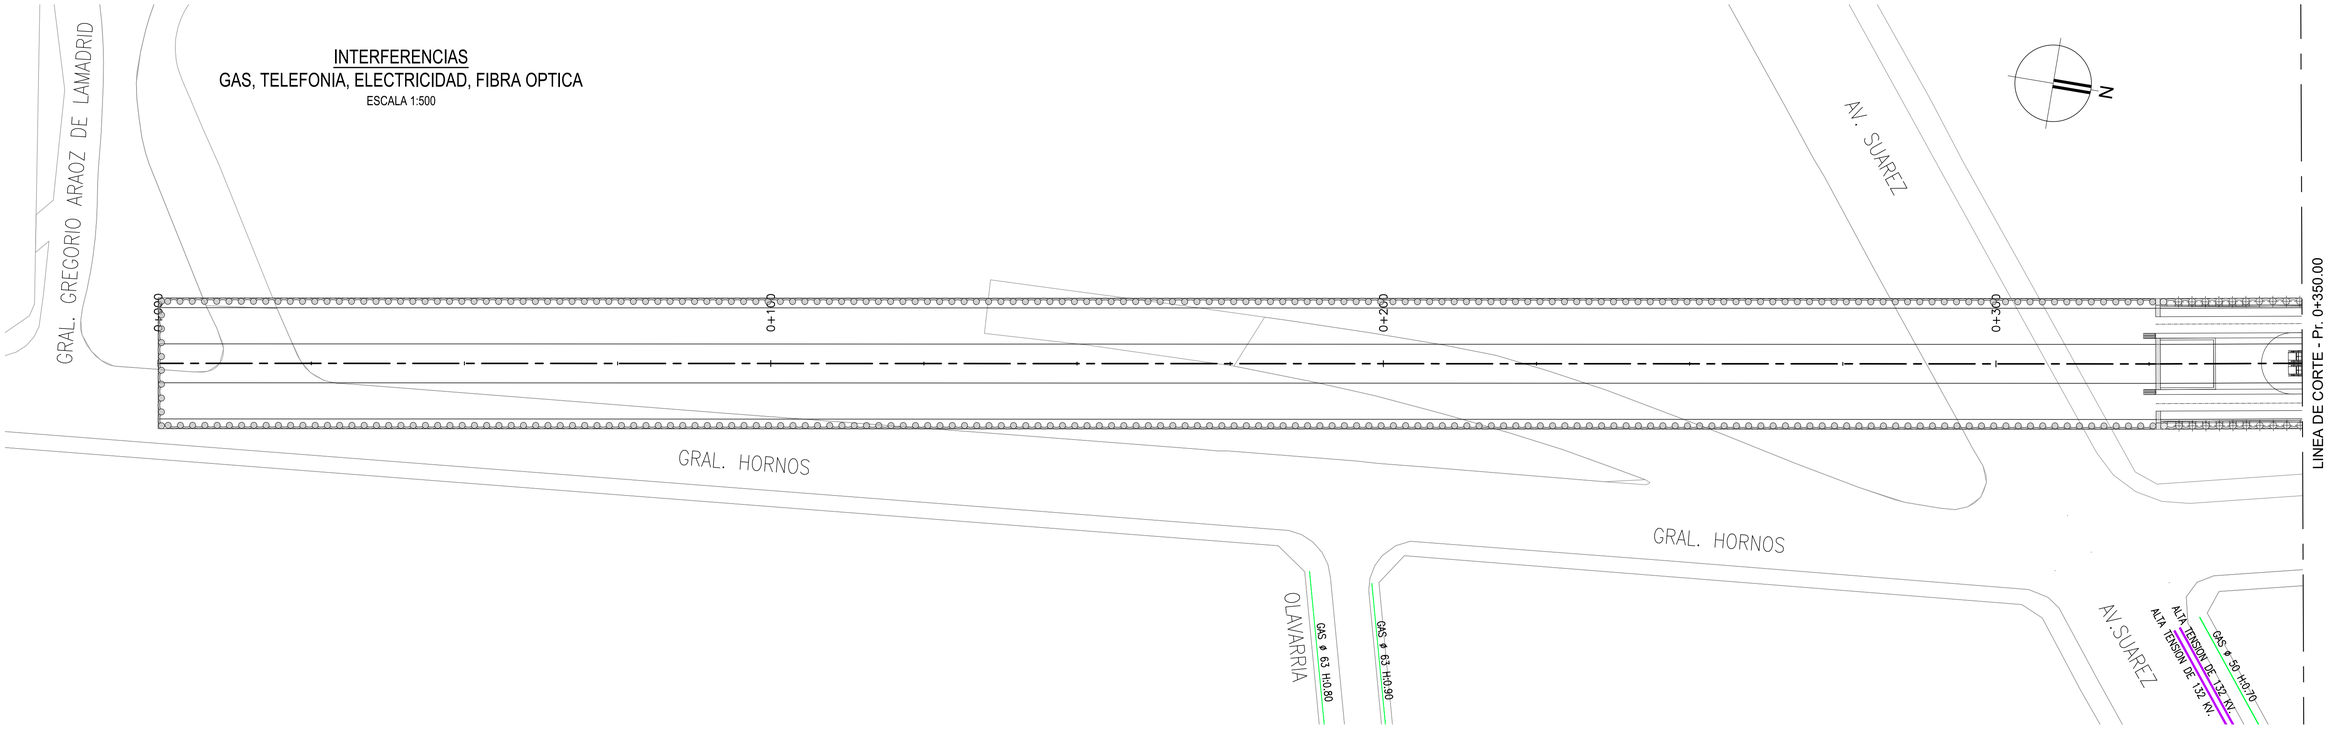

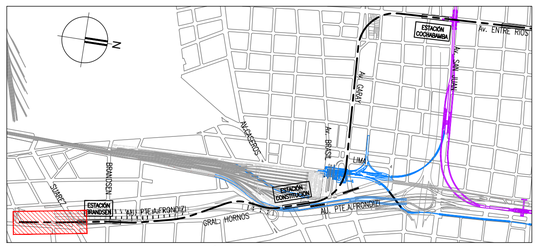

CROQUIS DE UBICACIÓN

REFERENCIAS
- RED CLOACAL
- RED PLUVIAL
- RED AGUA
- RED ELECTRICA
- RED GAS
- RED TELEFONICA
- RED FIBRA OPTICA MULTICANAL

0 10 20 30m
ESCALA 1:500

Ing. Mariano Miculicich
DIRECTOR

N°	DIBUJÓ	REVISÓ	APROBÓ	FECHA	DESCRIPCIÓN
0	D.B.	P.C.		SET. 2025	EMISIÓN INICIAL

REVISIONES

MINISTERIO DE INFRAESTRUCTURA

URGELL PENEDO URGELL
ARQUITECTOS LYNCH VAGO RODRIGUEZ

IATASA INGENIERIA

PROYECTO DE ARQUITECTURA E INGENIERÍA RELACIONADO A LA CONSTRUCCIÓN INTEGRAL DE LA LÍNEA F DE SUBTERRÁNEOS DE LA CIUDAD DE BUENOS AIRES

FECHA: SETIEMBRE 2025	TRAZADO DE TÚNEL
ESCALA:	INTERFERENCIAS TRAMO 1
HORIZ: 1:500	PLANIMETRÍA GENERAL - PROG. 0+000 A 0+350
VERTICAL: -	IF-2026-20223041-GCABA-APRA
FORMATO A1 / HOJA: 01/18	PLANO Nº: LF-GL-T01-INT-PL-001 / REV.: 0

19/9/2025 16:17 p. m.
LF-GL-T01-INT-PL-001g018_0.dwg

INTERFERENCIAS
SERVICOS CLOACALES, PLUVIALES, AGUA CORRIENTE
ESCALA 1:500

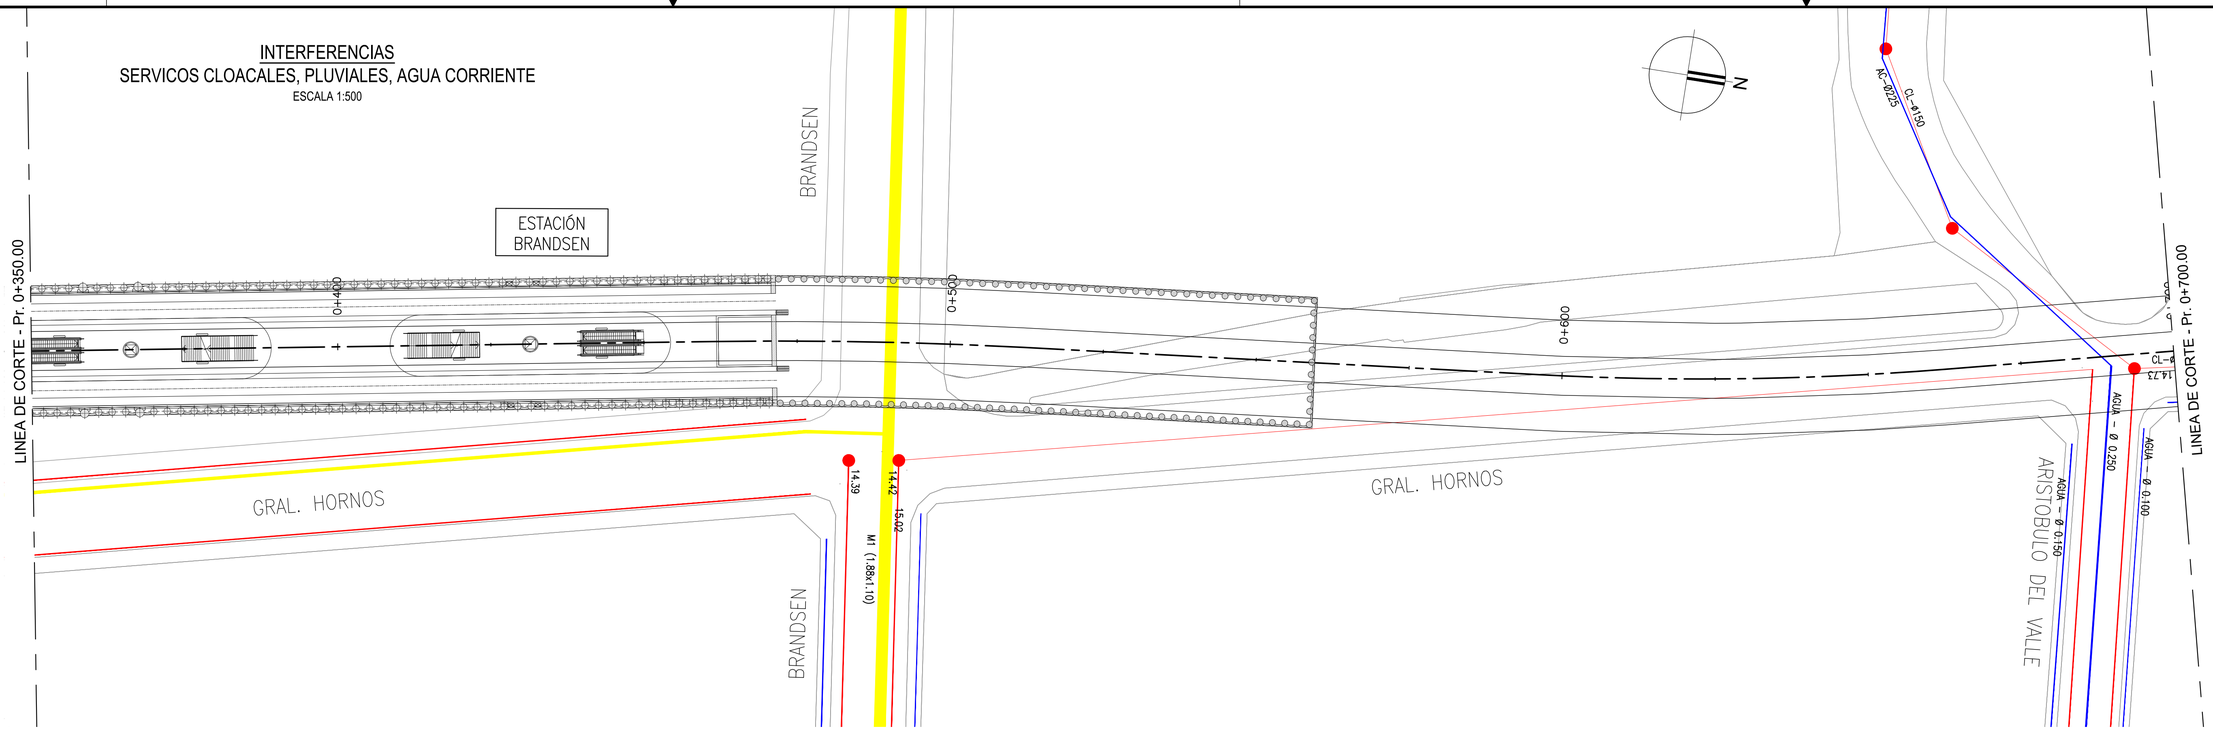

INTERFERENCIAS
GAS, TELEFONIA, ELECTRICIDAD, FIBRA OPTICA
ESCALA 1:500

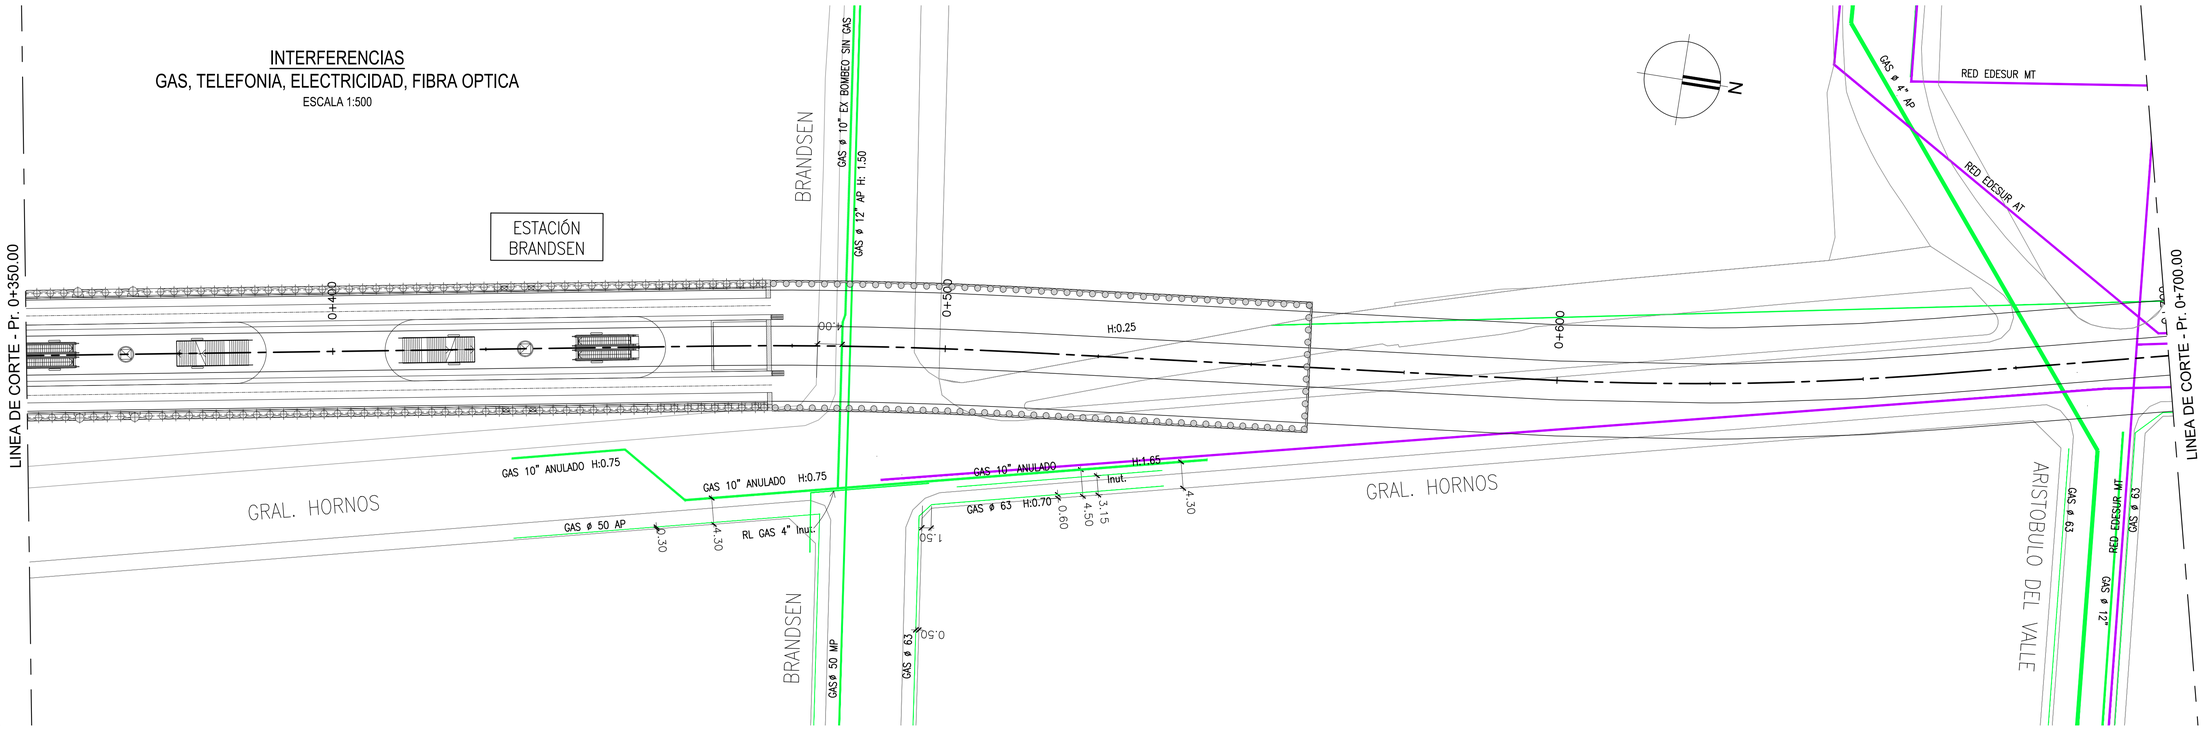

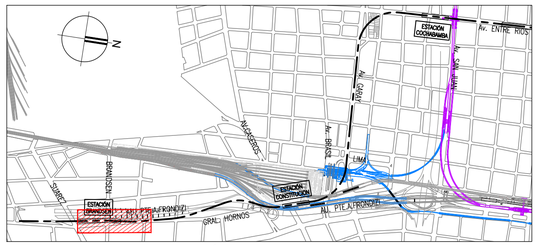

CROQUIS DE UBICACIÓN

REFERENCIAS

- RED CLOACAL
- RED PLUVIAL
- RED AGUA
- RED ELECTRICA
- RED GAS
- RED TELEFONICA
- RED FIBRA OPTICA MULTICANAL

0 10 20 30m
ESCALA 1:500

Ing. Mariano Miculicich
DIRECTOR

N°	DIBUJÓ	REVISÓ	APROBÓ	FECHA	DESCRIPCIÓN
0	D.B.	P.C.		SET. 2025	EMISIÓN INICIAL

REVISIONES

MINISTERIO DE INFRAESTRUCTURA

URGELL PENEDO URGELL
ARQUITECTOS LUNCI VAGO RODRIGUEZ

PROYECTO DE ARQUITECTURA E INGENIERÍA RELACIONADO A LA CONSTRUCCIÓN INTEGRAL DE LA LÍNEA F DE SUBTERRÁNEOS DE LA CIUDAD DE BUENOS AIRES

FECHA: SETIEMBRE 2025	TRAZADO DE TÚNEL
ESCALA: HORIZ: 1:500 VERTICAL: -	INTERFERENCIAS TRAMO 1
	PLANIMETRÍA GENERAL - PROG. 0+350 A 0+700
FORMATO A1 / HOJA: 02/18	PLANO Nº: LF-GL-T01-INT-PL-002 / REV.: 0

IF 2026 20223941 GCABA APRA

19/9/2025 16:17 p. m.
LF-GL-T01-INT-PL-002_0.dwg

INTERFERENCIAS
SERVICOS CLOACALES, PLUVIALES, AGUA CORRIENTE
ESCALA 1:500

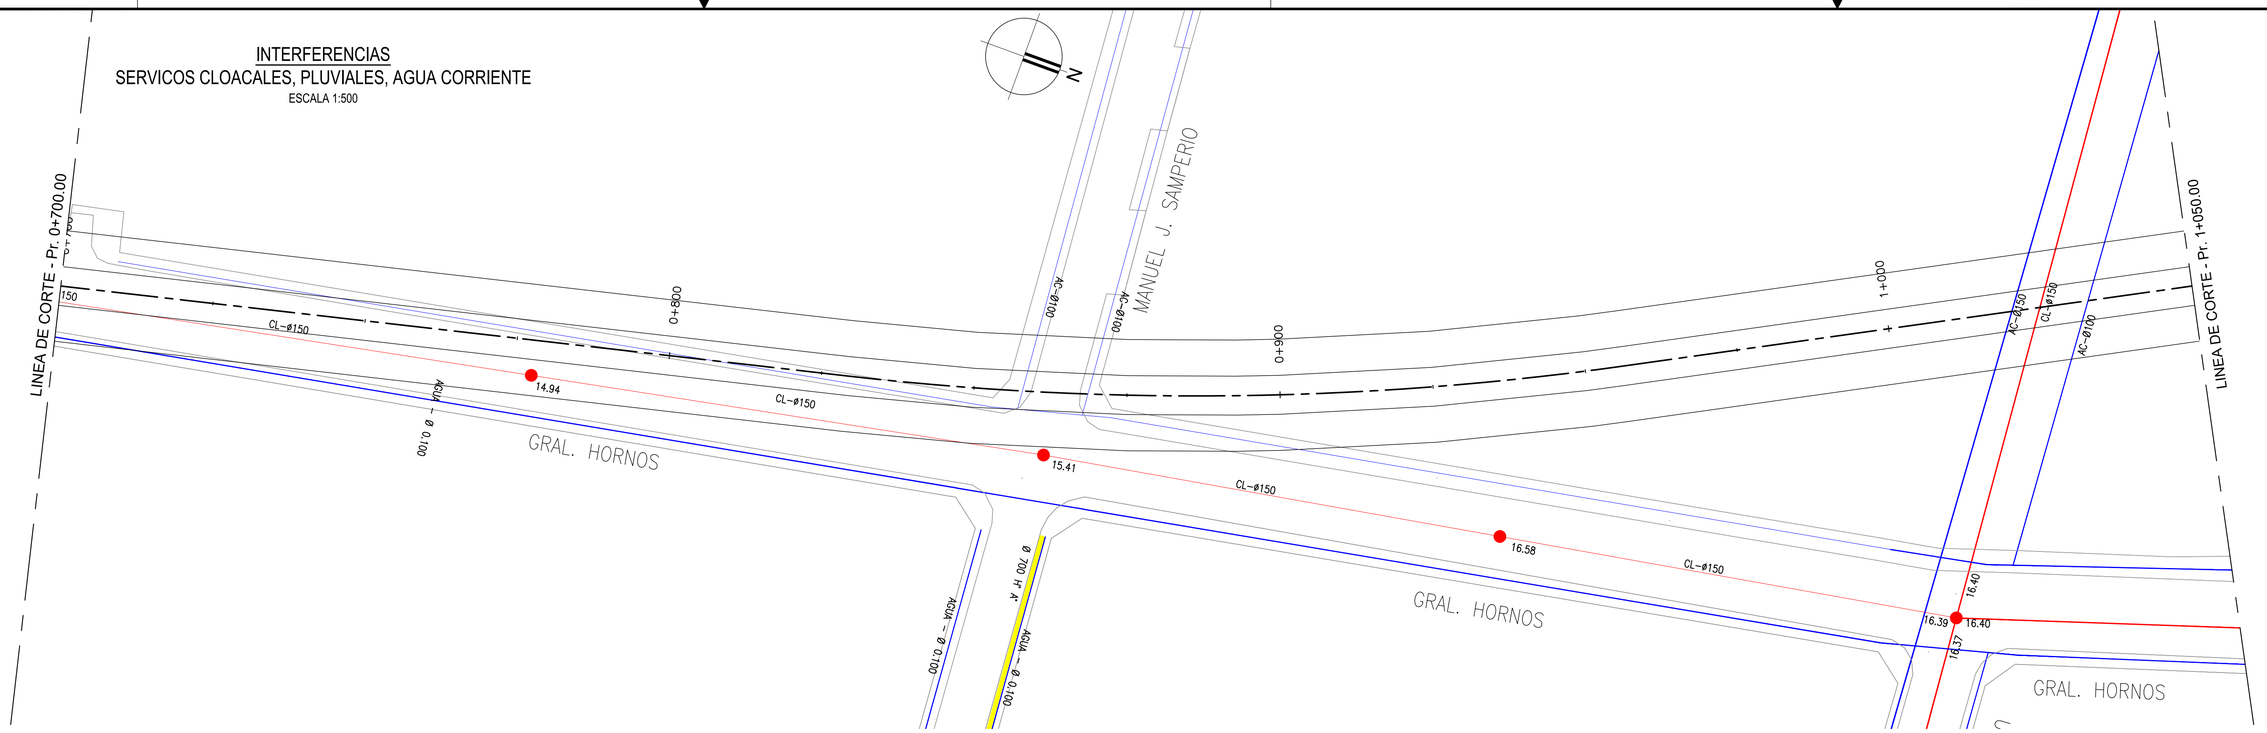

INTERFERENCIAS
GAS, TELEFONIA, ELECTRICIDAD, FIBRA OPTICA
ESCALA 1:500

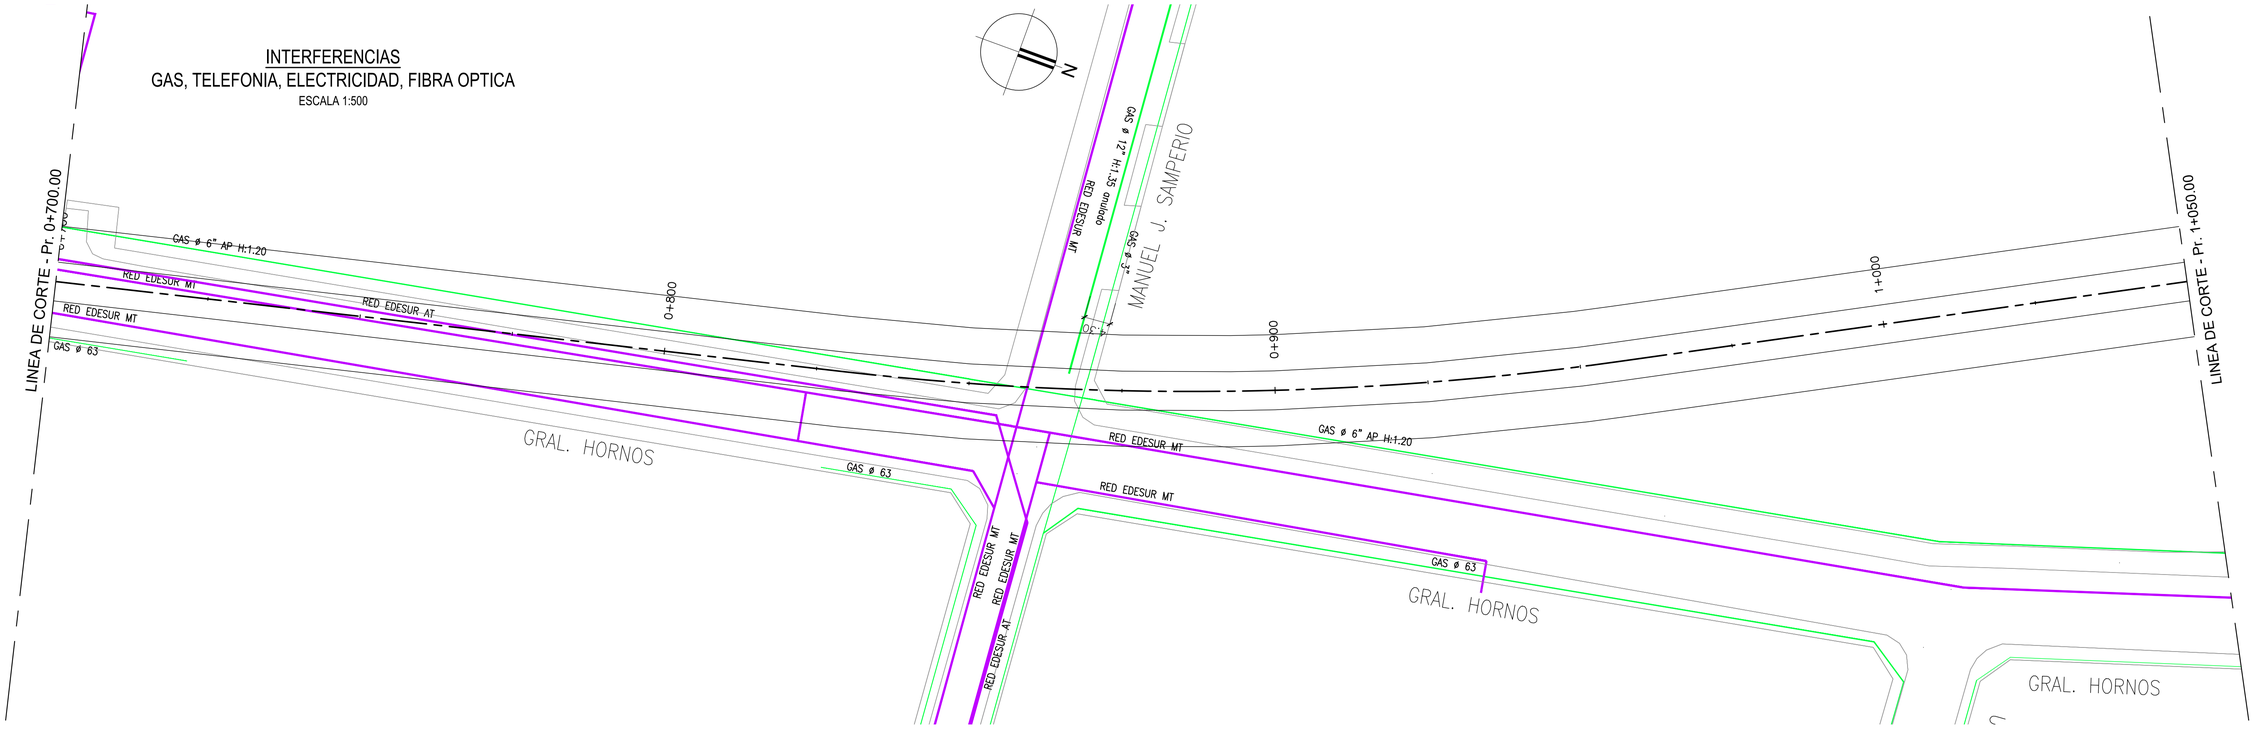

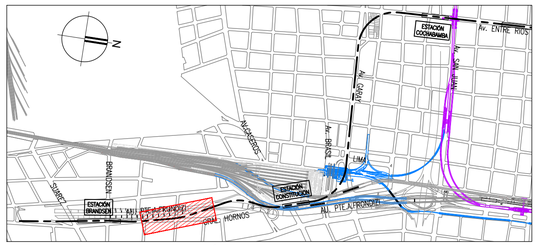

CROQUIS DE UBICACIÓN

Ing. Mariano Miculicich
DIRECTOR

REFERENCIAS

- RED CLOACAL
- RED PLUVIAL
- RED AGUA
- RED ELECTRICA
- RED GAS
- RED TELEFONICA
- RED FIBRA OPTICA MULTICANAL

0 10 20 30m
ESCALA 1:500

N°	DIBUJÓ	REVISÓ	APROBÓ	FECHA	DESCRIPCIÓN
0	D.B.	P.C.		SET. 2025	EMISIÓN INICIAL

REVISIONES

MINISTERIO DE INFRAESTRUCTURA

URGELL PENEDO URGELL
ARQUITECTOS LYNCH VAGO RODRIGUEZ

PROYECTO DE ARQUITECTURA E INGENIERÍA RELACIONADO A LA CONSTRUCCIÓN INTEGRAL DE LA LÍNEA F DE SUBTERRÁNEOS DE LA CIUDAD DE BUENOS AIRES

FECHA: SETIEMBRE 2025	TRAZADO DE TÚNEL
ESCALA: HORIZ: 1:500 VERTICAL: -	INTERFERENCIAS TRAMO 1
	PLANIMETRÍA GENERAL - PROG. 0+700 A 1+050
FORMATO A1 / HOJA: 03/18	PLANO Nº: **LF-GL-T01-INT-PL-003** / REV.: **0**

IF-2026-20223041-GCABA-APRA

19/9/2025 16:17 p. m.
LF-GL-T01-INT-PL-001-018_0.dwg

INTERFERENCIAS
SERVICOS CLOACALES, PLUVIALES, AGUA CORRIENTE
ESCALA 1:500

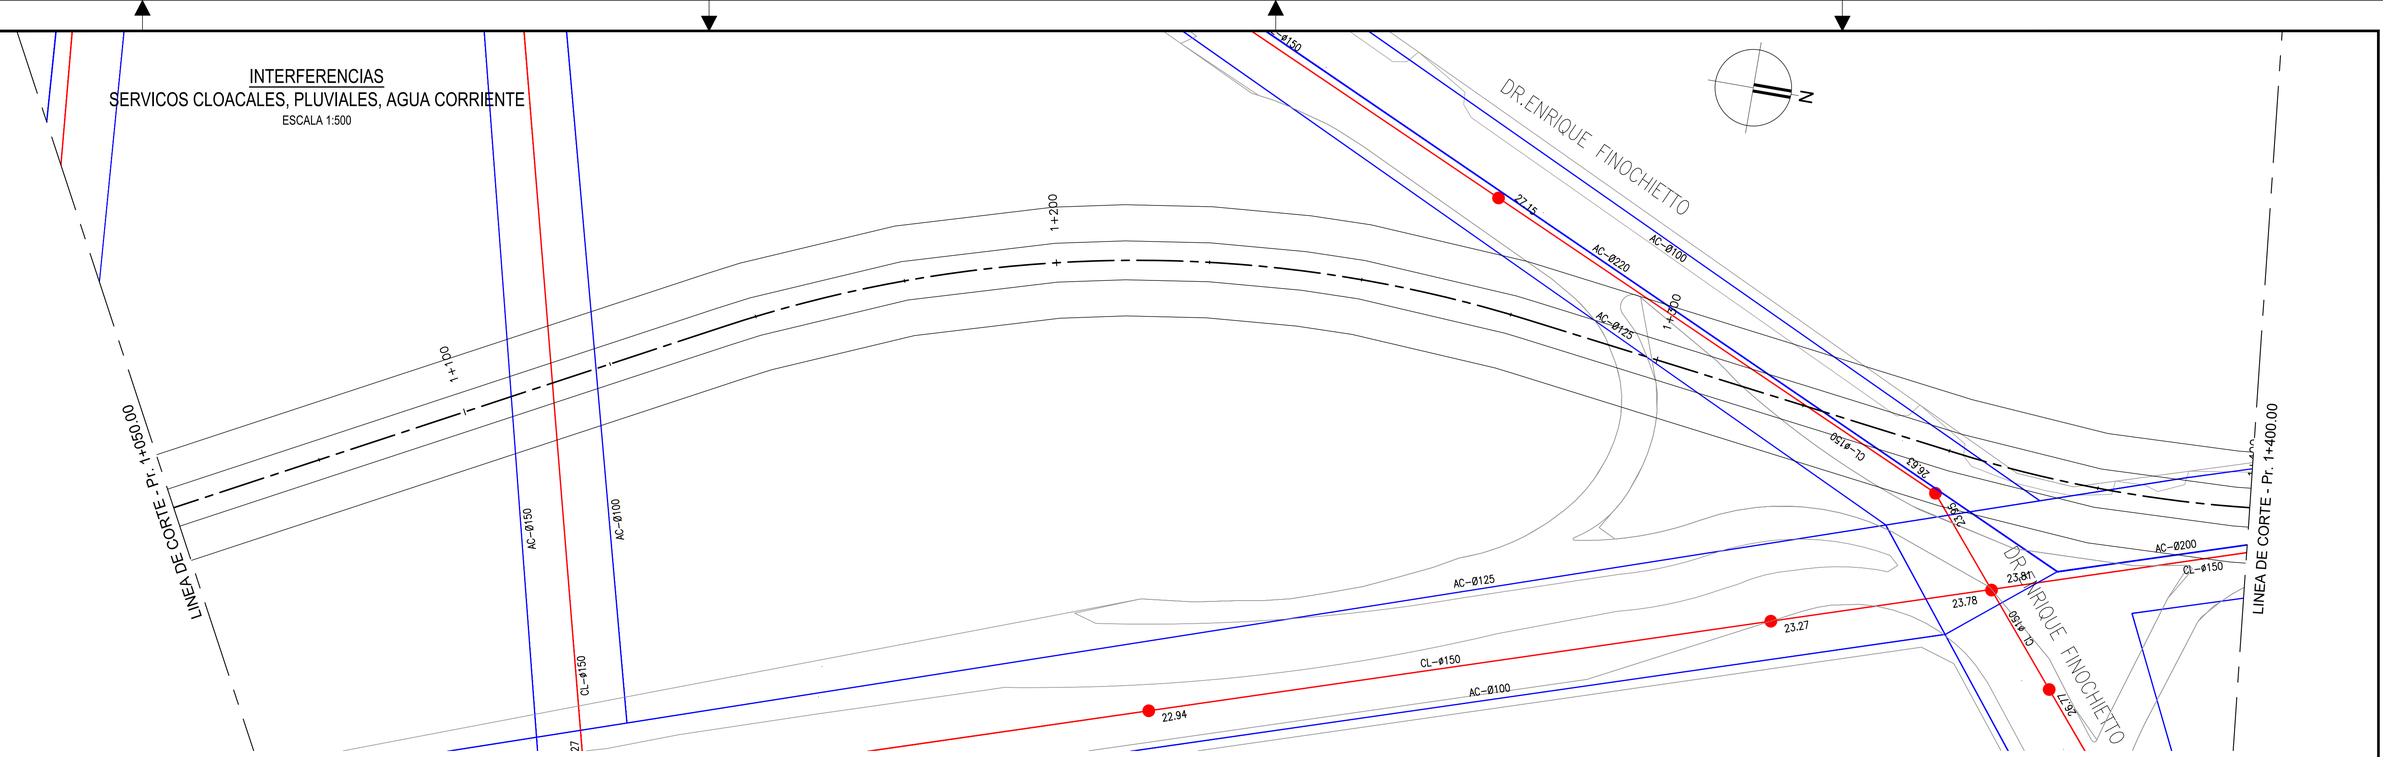

INTERFERENCIAS
GAS, TELEFONIA, ELECTRICIDAD, FIBRA OPTICA
ESCALA 1:500

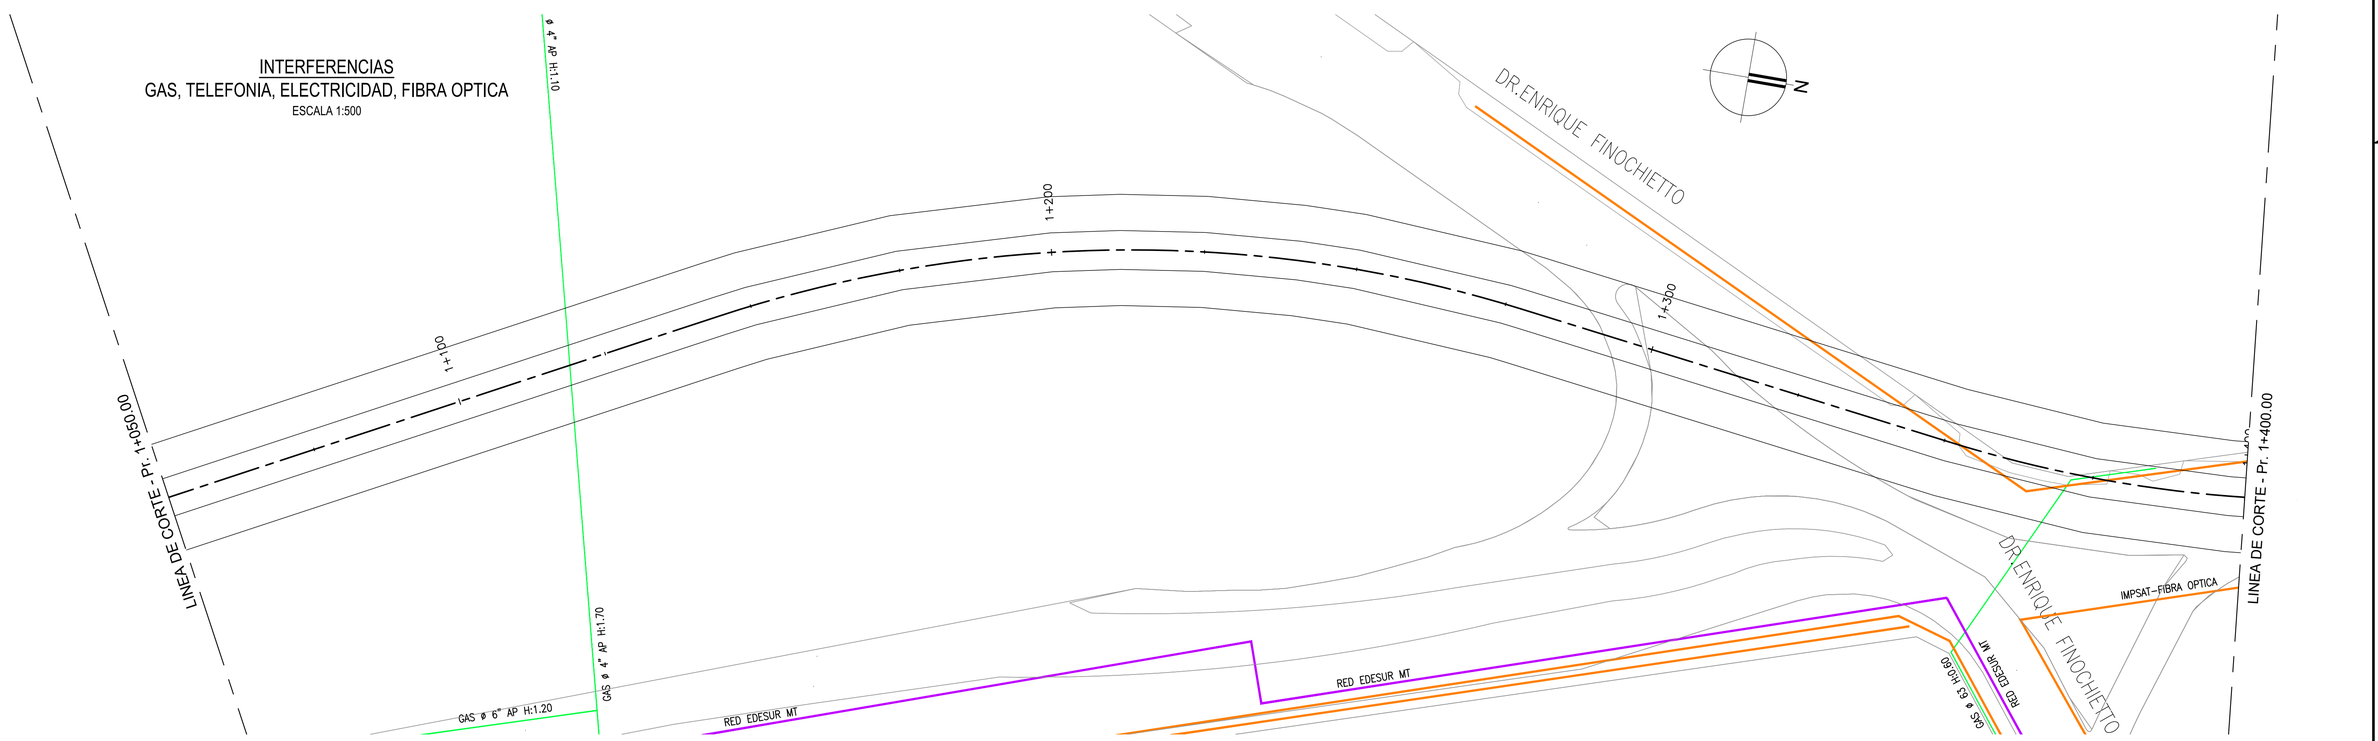

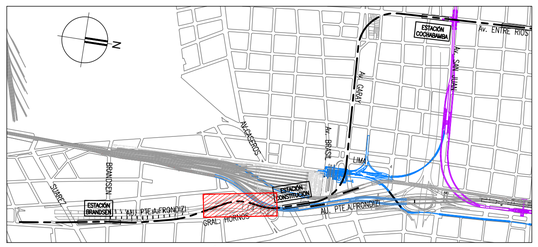

CROQUIS DE UBICACIÓN

REFERENCIAS

- RED CLOACAL
- RED PLUVIAL
- RED AGUA
- RED ELECTRICA
- RED GAS
- RED TELEFONICA
- RED FIBRA OPTICA MULTICANAL

0 10 20 30m
ESCALA 1:500

Ing. Mariano Micullich
DIRECTOR

N°	DIBUJÓ	REVISÓ	APROBÓ	FECHA	DESCRIPCIÓN
0	D.B.	P.C.		SET. 2025	EMISIÓN INICIAL

REVISIONES

MINISTERIO DE INFRAESTRUCTURA

URGELL PENEDO URGELL
ARQUITECTOS LYNCH VAGO RODRIGUEZ

PROYECTO DE ARQUITECTURA E INGENIERÍA RELACIONADO A LA CONSTRUCCIÓN INTEGRAL DE LA LÍNEA F DE SUBTERRÁNEOS DE LA CIUDAD DE BUENOS AIRES

FECHA: SETIEMBRE 2025	TRAZADO DE TÚNEL
ESCALA: HORIZ: 1:500 VERTICAL: -	INTERFERENCIAS TRAMO 1
FORMATO: A1	HOJA: 04/18
	PLANIMETRÍA GENERAL - PROG. 1+050 A 1+400
	IF-2026-20223041-GCABA-APRA
	PLANO Nº: LF-GL-T01-INT-PL-004
	REV.: 0

19/9/2025 16:17 p. m.
LF-GL-T01-INT-PL-003-018_0.dwg

INTERFERENCIAS
SERVICOS CLOACALES, PLUVIALES, AGUA CORRIENTE
ESCALA 1:500

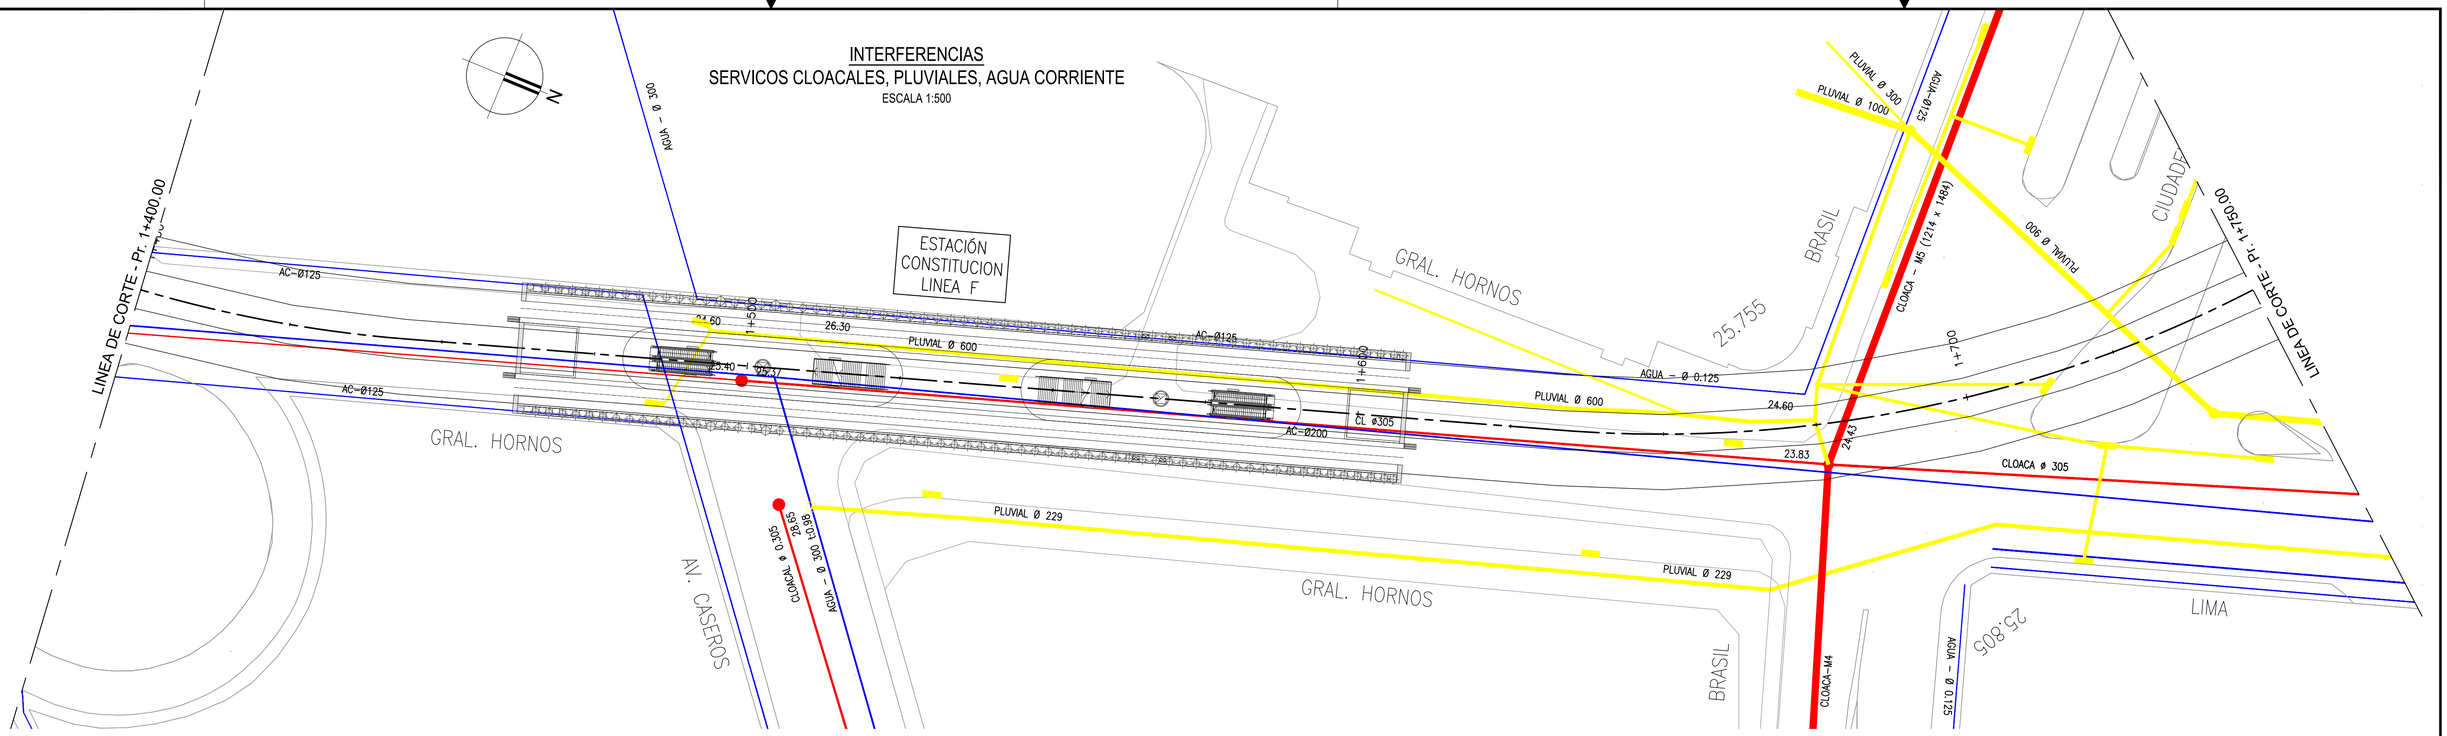

INTERFERENCIAS
GAS, TELEFONIA, ELECTRICIDAD, FIBRA OPTICA
ESCALA 1:500

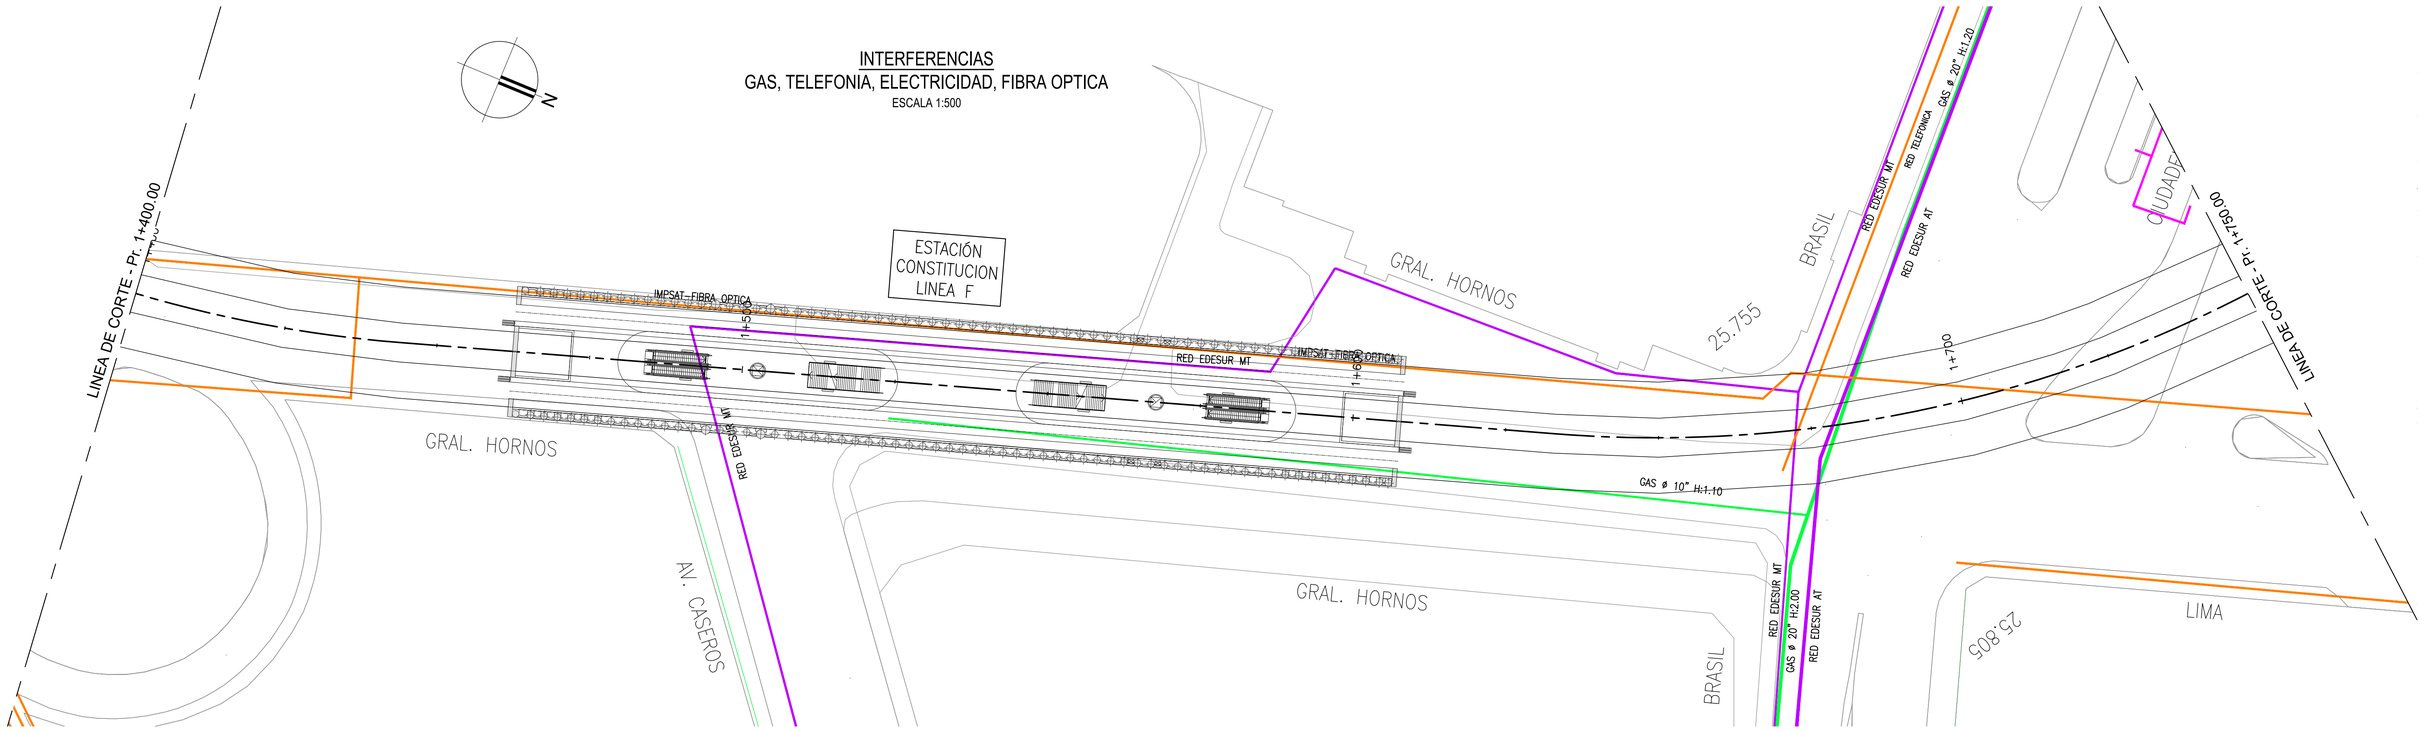

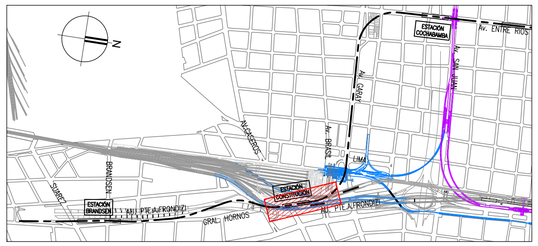

CROQUIS DE UBICACIÓN

REFERENCIAS

- RED CLOACAL
- RED PLUVIAL
- RED AGUA
- RED ELECTRICA
- RED GAS
- RED TELEFONICA
- RED FIBRA OPTICA MULTICANAL

0 10 20 30m
ESCALA 1:500

Ing. Mariano Miculicich
DIRECTOR

N°	DIBUJÓ	REVISÓ	APROBÓ	FECHA	DESCRIPCIÓN
0	D.B.	P.C.		SET. 2025	EMISIÓN INICIAL

REVISIONES

MINISTERIO DE INFRAESTRUCTURA

URGELL PENEDO URGELL
ARQUITECTOS LYNCH VAGO RODRIGUEZ

PROYECTO DE ARQUITECTURA E INGENIERÍA RELACIONADO A LA CONSTRUCCIÓN INTEGRAL DE LA LÍNEA F DE SUBTERRÁNEOS DE LA CIUDAD DE BUENOS AIRES

FECHA: SETIEMBRE 2025	TRAZADO DE TÚNEL
ESCALA: HORIZ: 1:500 VERTICAL: -	INTERFERENCIAS TRAMO 1
	PLANIMETRÍA GENERAL - PROG. 1+400 A 1+750
FORMATO A1 / HOJA: 05/18	PLANO Nº: **LF-GL-T01-INT-PL-005** / REV.: **0**

IF-2026-20223041-GCABA-APRA

19/9/2025 16:17 p. m.
LF-GL-T01-INT-PL-001-018_0.dwg

INTERFERENCIAS
SERVICOS CLOACALES, PLUVIALES, AGUA CORRIENTE
ESCALA 1:500

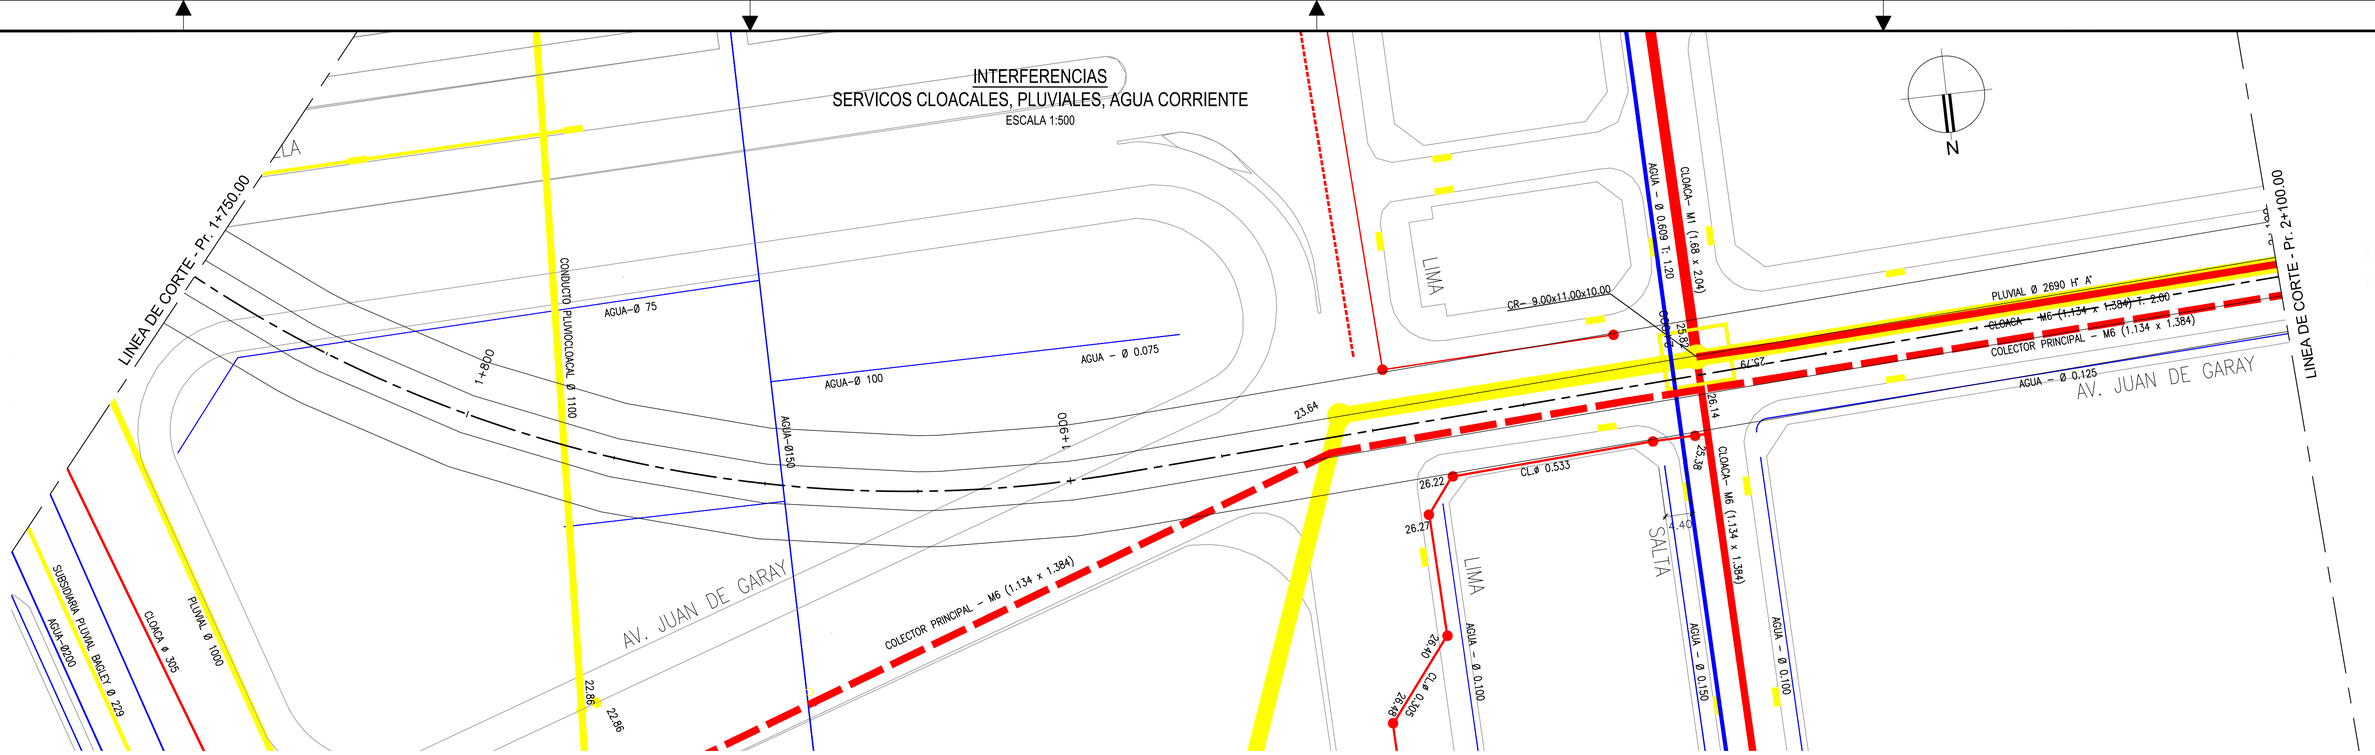

INTERFERENCIAS
GAS, TELEFONIA, ELECTRICIDAD, FIBRA OPTICA
ESCALA 1:500

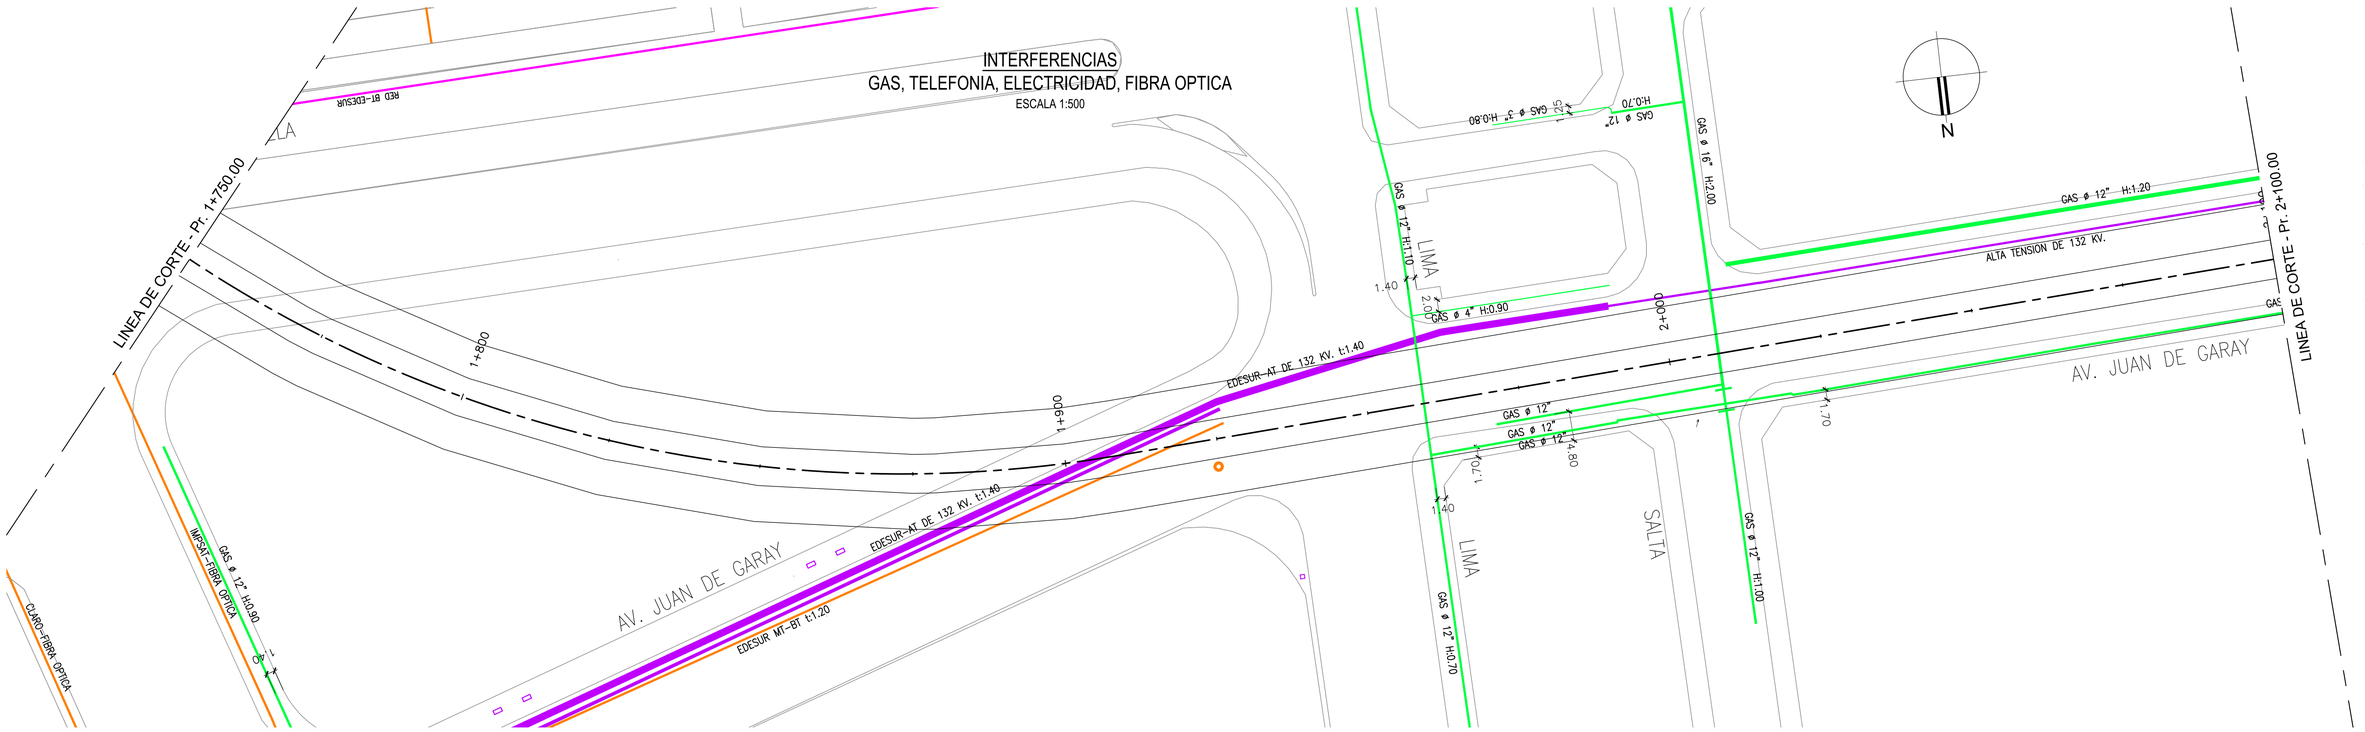

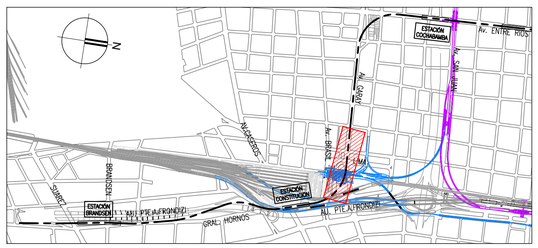

CROQUIS DE UBICACIÓN

REFERENCIAS

- RED CLOACAL
- RED PLUVIAL
- RED AGUA
- RED ELECTRICA
- RED GAS
- RED TELEFONICA
- RED FIBRA OPTICA MULTICANAL

0 10 20 30m
ESCALA 1:500

Ing. Mariano Micullicich
DIRECTOR

N°	DIBUJÓ	REVISÓ	APROBÓ	FECHA	DESCRIPCIÓN
0	D.B.	P.C.		SET. 2025	EMISIÓN INICIAL

REVISIONES

MINISTERIO DE INFRAESTRUCTURA

URGELL PENEDO URGELL
ARQUITECTOS LYNCH VAGO RODRIGUEZ

PROYECTO DE ARQUITECTURA E INGENIERÍA RELACIONADO A LA CONSTRUCCIÓN INTEGRAL DE LA LÍNEA F DE SUBTERRÁNEOS DE LA CIUDAD DE BUENOS AIRES

FECHA: 06/22	TRAZADO DE TÚNEL INTERFERENCIAS TRAMO 1 PLANIMETRÍA GENERAL - PROG. 1+750 A 2+100	
ESCALA: HORIZ.: 1:500 VERTICAL: -		
FORMATO: A1	HOJA: 06/18	PLANO Nº: LF-GL-T01-INT-PL-006
		REV.: 0

IF 2026 20223941 GCABA APRA

19/9/2025 16:17 p. m.
LF-GL-T01-INT-PL-001a018_0.dwg

INTERFERENCIAS
SERVICOS CLOACALES, PLUVIALES, AGUA CORRIENTE
ESCALA 1:500

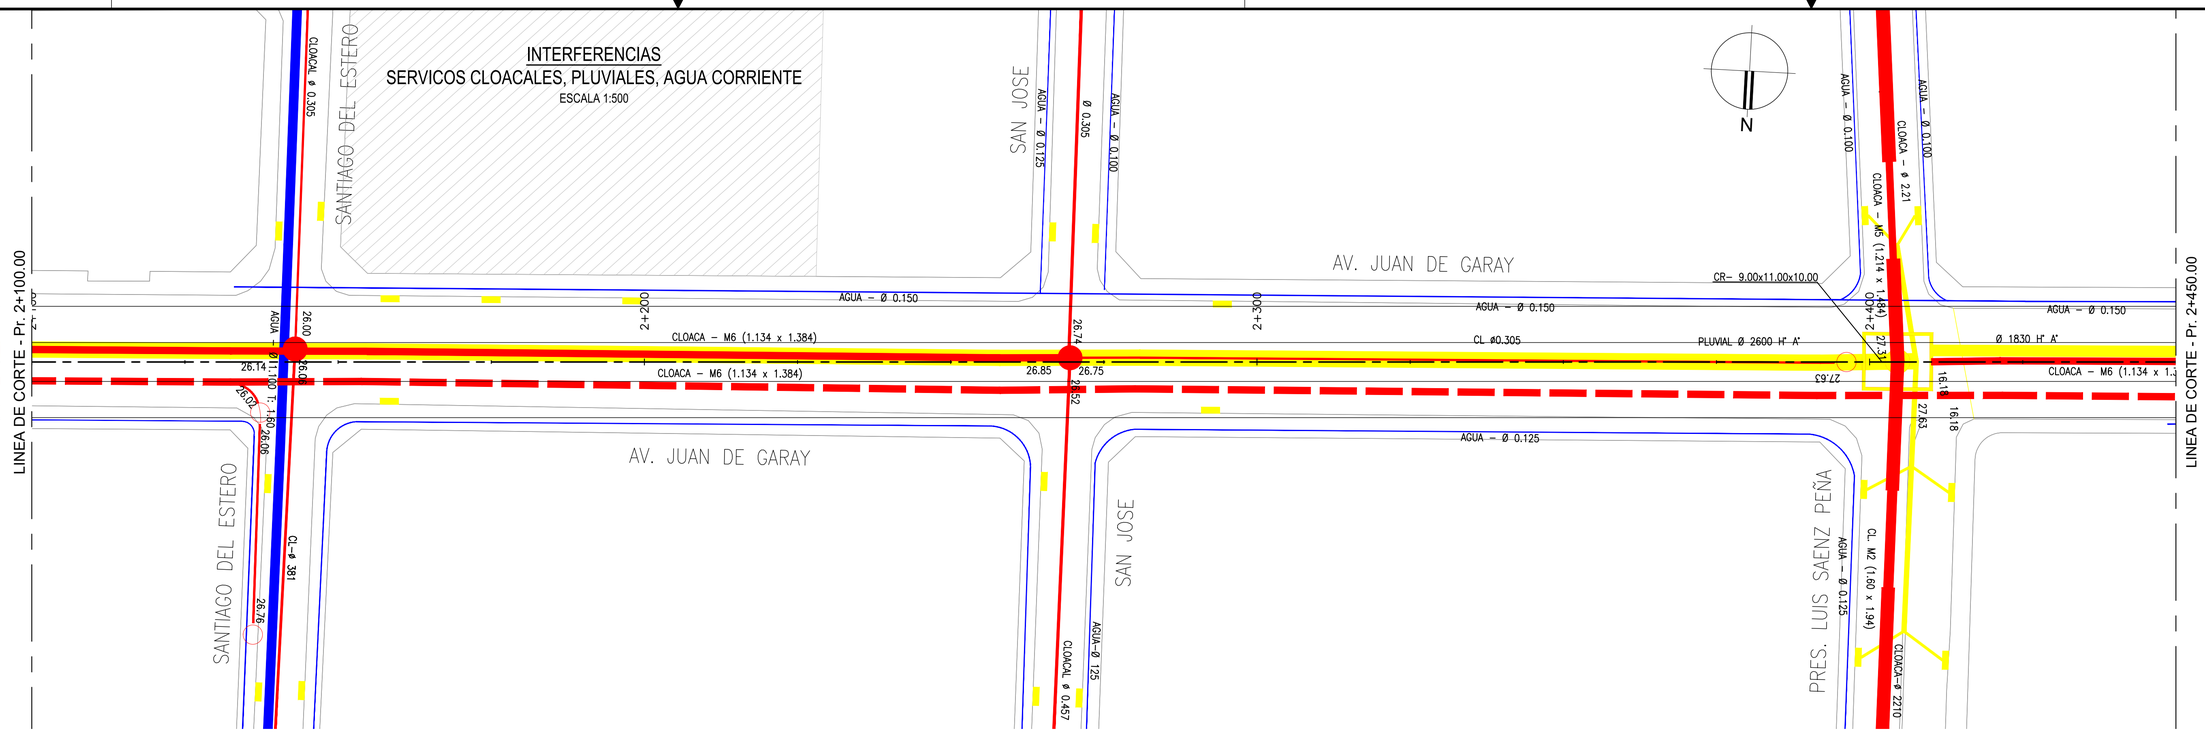

INTERFERENCIAS
GAS, TELEFONIA, ELECTRICIDAD, FIBRA OPTICA
ESCALA 1:500

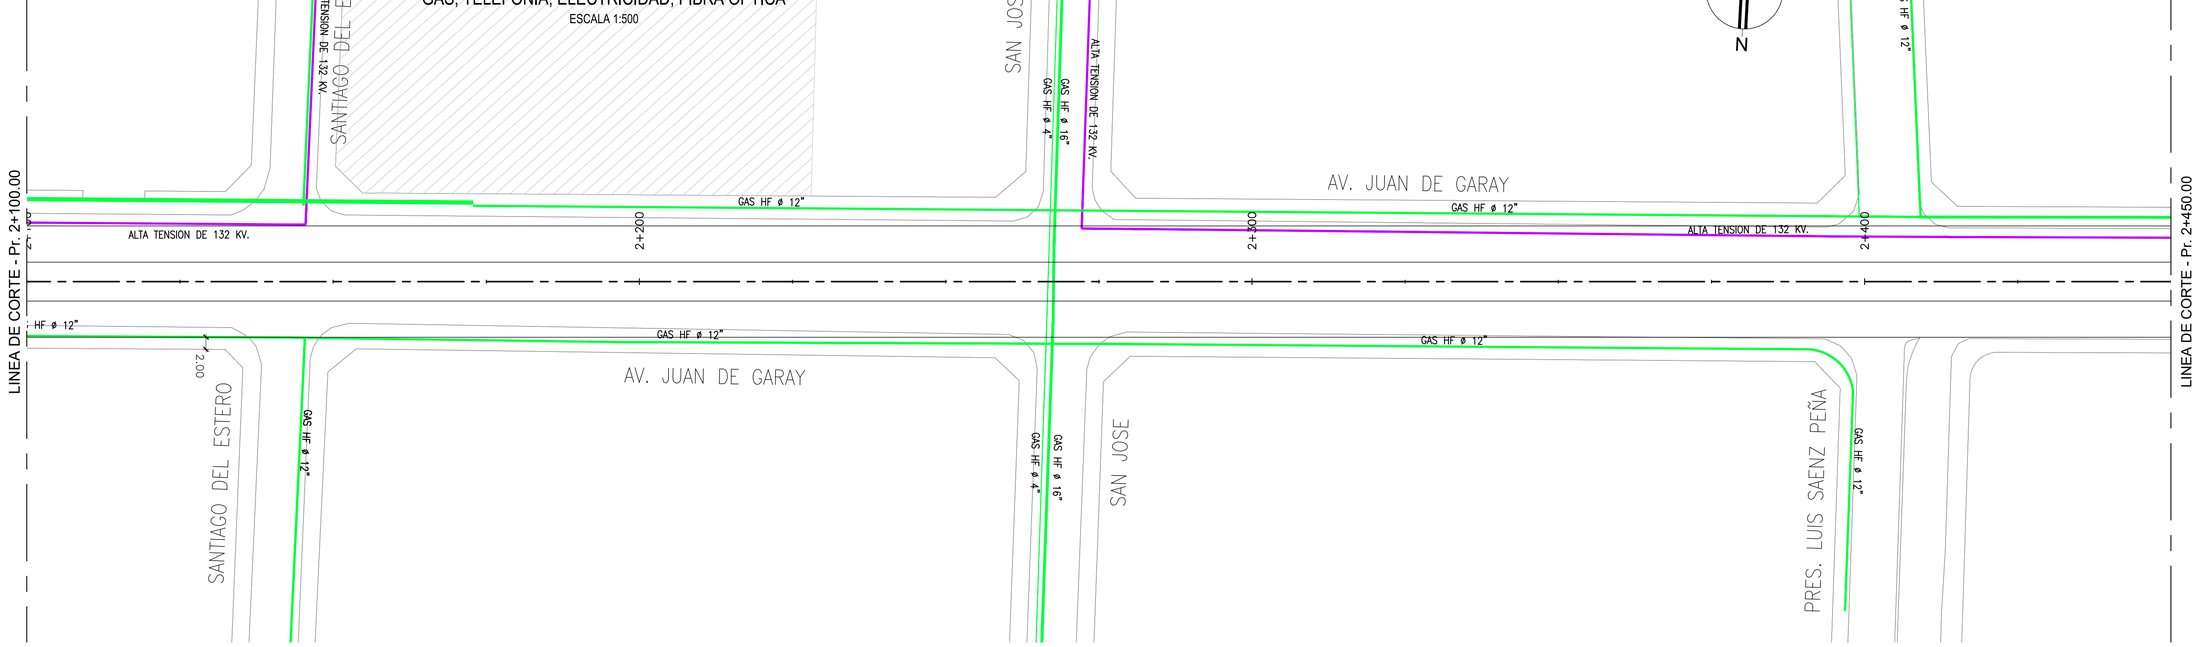

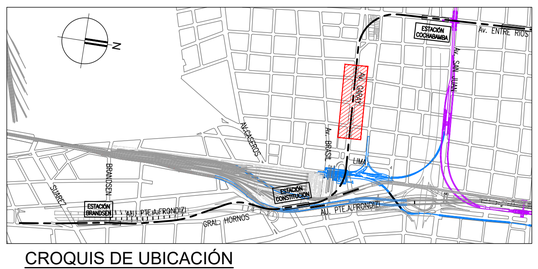

CROQUIS DE UBICACIÓN

REFERENCIAS

- RED CLOACAL
- RED PLUVIAL
- RED AGUA
- RED ELECTRICA
- RED GAS
- RED TELEFONICA
- RED FIBRA OPTICA MULTICANAL

0 10 20 30m
ESCALA 1:500

Ing. Mariano Miculicich
DIRECTOR

N°	DIBUJÓ	REVISÓ	APROBÓ	FECHA	DESCRIPCIÓN
0	D.B.	P.C.		SET. 2025	EMISIÓN INICIAL

REVISIONES

MINISTERIO DE INFRAESTRUCTURA

URGELL PENEDO URGELL
ARQUITECTOS LYNCH VAGO RODRIGUEZ

IATASA INGENIERIA

PROYECTO DE ARQUITECTURA E INGENIERÍA RELACIONADO A LA CONSTRUCCIÓN INTEGRAL DE LA LÍNEA F DE SUBTERRÁNEOS DE LA CIUDAD DE BUENOS AIRES

FECHA: SETIEMBRE 2025	TRAZADO DE TÚNEL
ESCALA:	INTERFERENCIAS TRAMO 1
HORIZ: 1:500	PLANIMETRÍA GENERAL - PROG. 2+100 A 2+450
VERTICAL: -	IF-2026-20223041-GCABA-APRA
FORMATO A1 / HOJA: 07/18	PLANO Nº: LF-GL-T01-INT-PL-007 / REV.: 0

19/9/2025 16:17 p. m.
LF-GL-T01-INT-PL-007a018_0.dwg

INTERFERENCIAS
SERVICOS CLOACALES, PLUVIALES, AGUA CORRIENTE
ESCALA 1:500

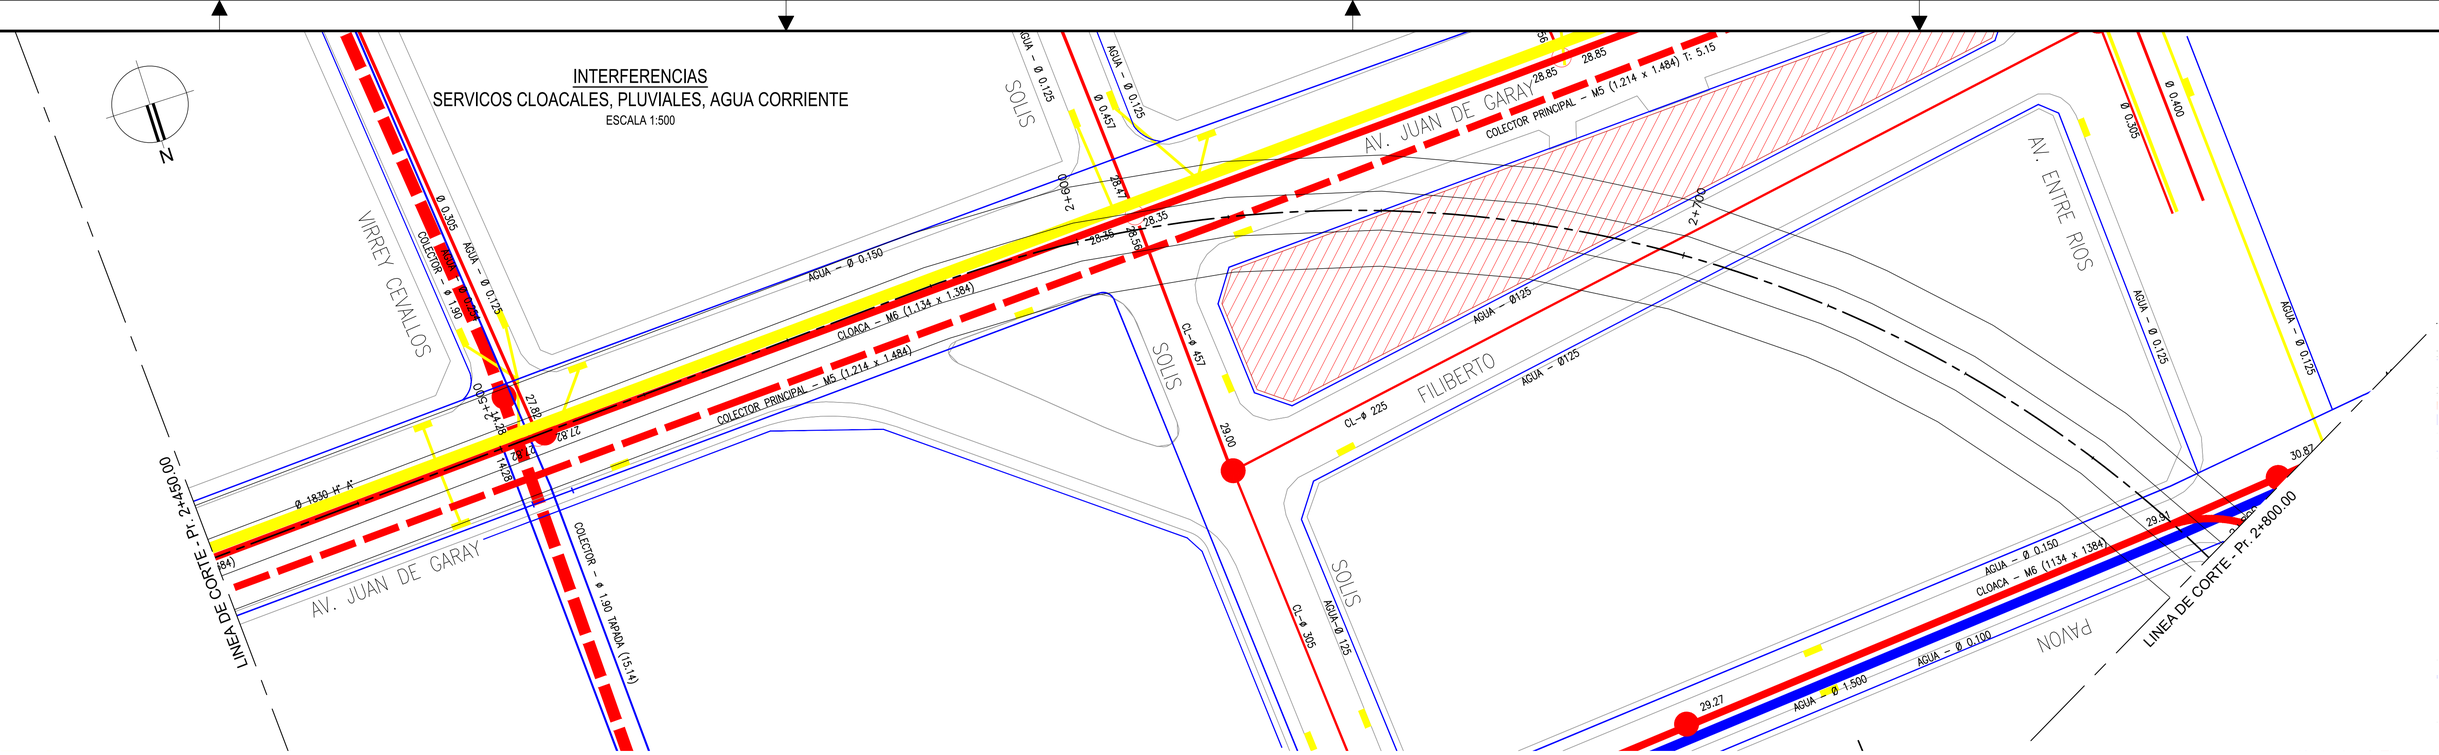

INTERFERENCIAS
GAS, TELEFONIA, ELECTRICIDAD, FIBRA OPTICA
ESCALA 1:500

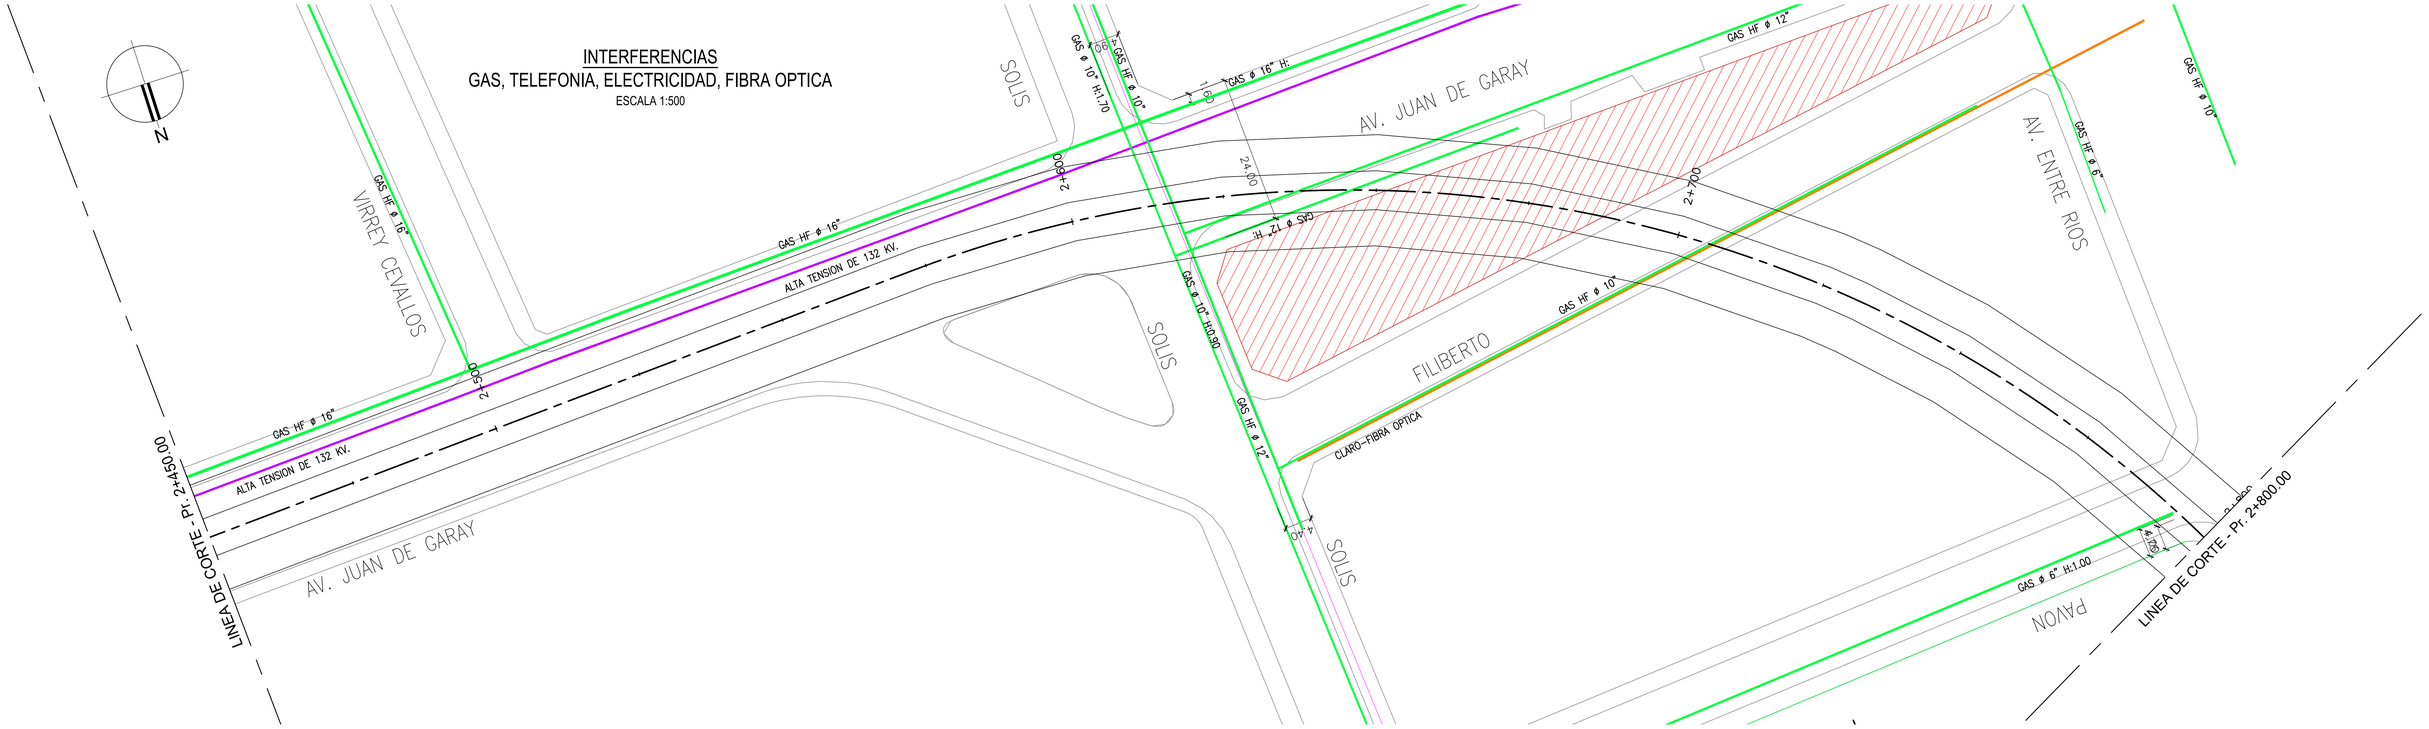

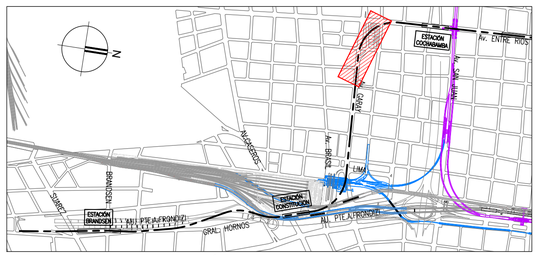

CROQUIS DE UBICACIÓN

Ing. Mariano Miculicich
DIRECTOR

REFERENCIAS

- RED CLOACAL
- RED PLUVIAL
- RED AGUA
- RED ELECTRICA
- RED GAS
- RED TELEFONICA
- RED FIBRA OPTICA MULTICANAL

0 10 20 30m
ESCALA 1:500

N°	DIBUJÓ	REVISÓ	APROBÓ	FECHA	DESCRIPCIÓN
0	D.B.	P.C.		SET. 2025	EMISIÓN INICIAL

REVISIONES

MINISTERIO DE INFRAESTRUCTURA

URGELL PENEDO URGELL
ARQUITECTOS LYNCH VAGO RODRIGUEZ

PROYECTO DE ARQUITECTURA E INGENIERÍA RELACIONADO A LA CONSTRUCCIÓN INTEGRAL DE LA LÍNEA F DE SUBTERRÁNEOS DE LA CIUDAD DE BUENOS AIRES

FECHA: SETIEMBRE 2025	TRAZADO DE TÚNEL INTERFERENCIAS TRAMO 1 PLANIMETRÍA GENERAL - PROG. 2+450 A 2+800
ESCALA: HORIZ: 1:500 VERTICAL: -	
FORMATO A1 / HOJA: 08/18	PLANO Nº: **LF-GL-T01-INT-PL-008** / REV.: **0**

IF-2026-20223041-GCABA-APRA

19/9/2025 16:17 p. m.
LF_GL_T01_INT_PL_008_0.dwg

INTERFERENCIAS
SERVICOS CLOACALES, PLUVIALES, AGUA CORRIENTE
ESCALA 1:500

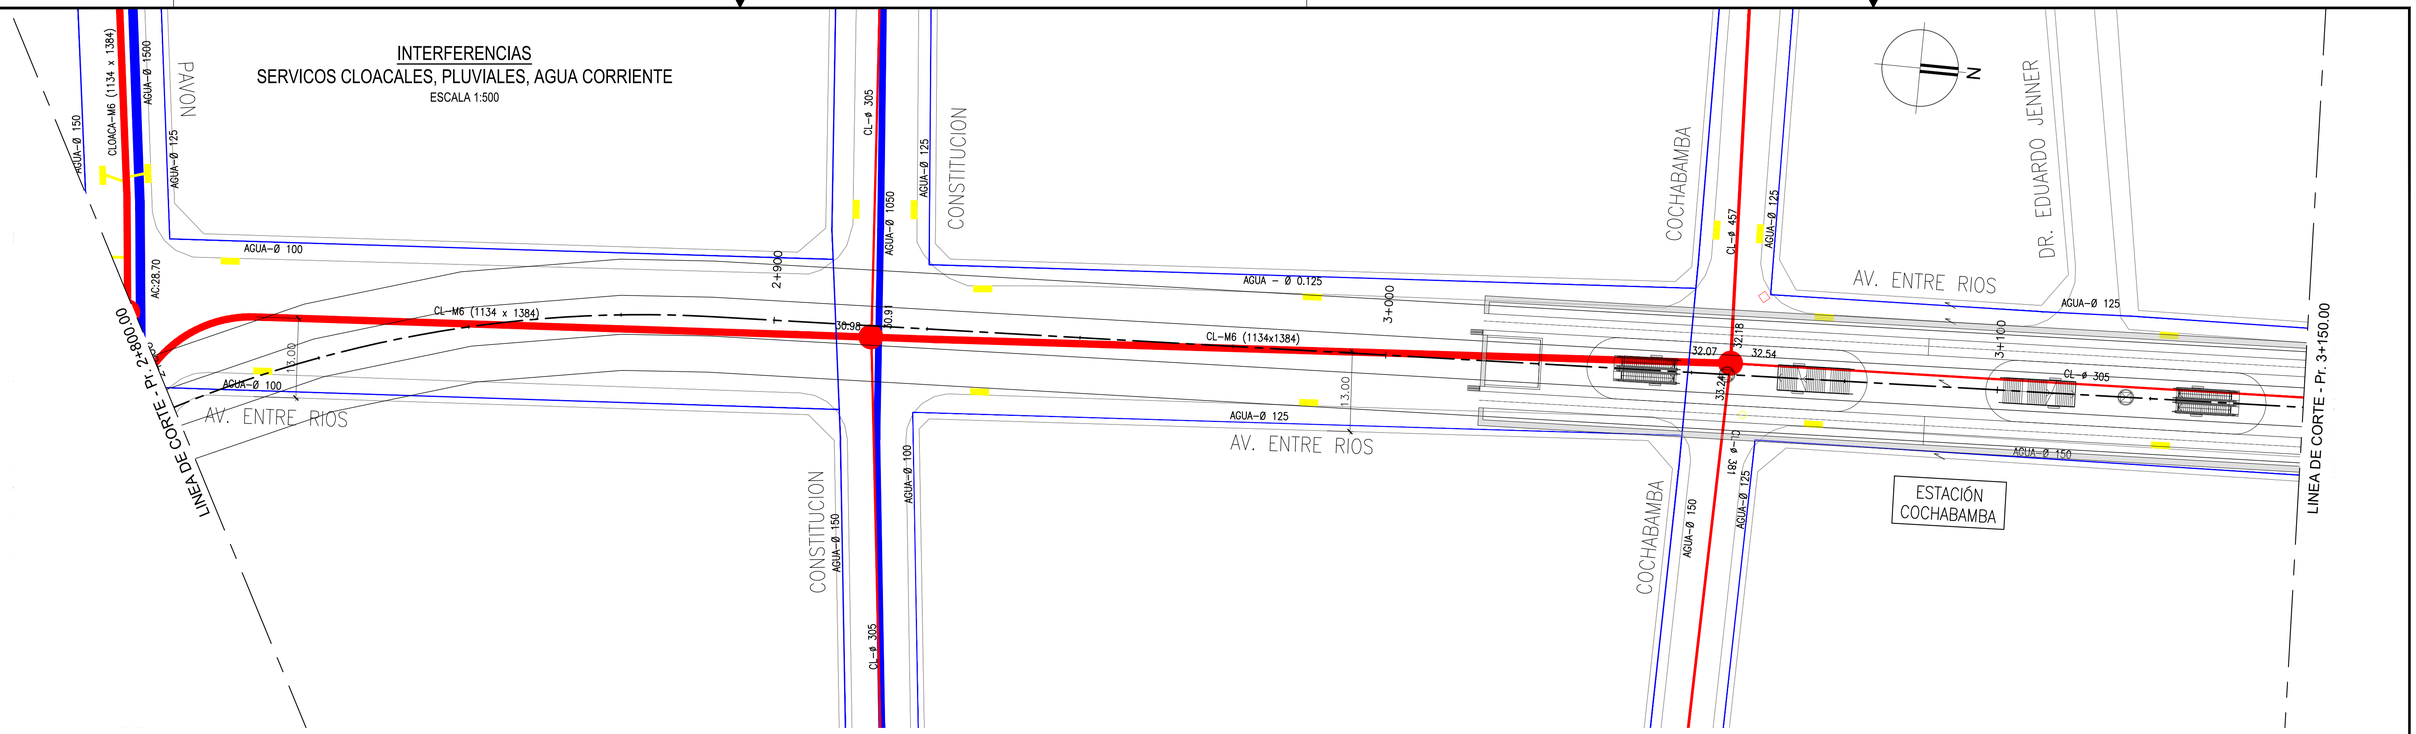

INTERFERENCIAS
GAS, TELEFONIA, ELECTRICIDAD, FIBRA OPTICA
ESCALA 1:500

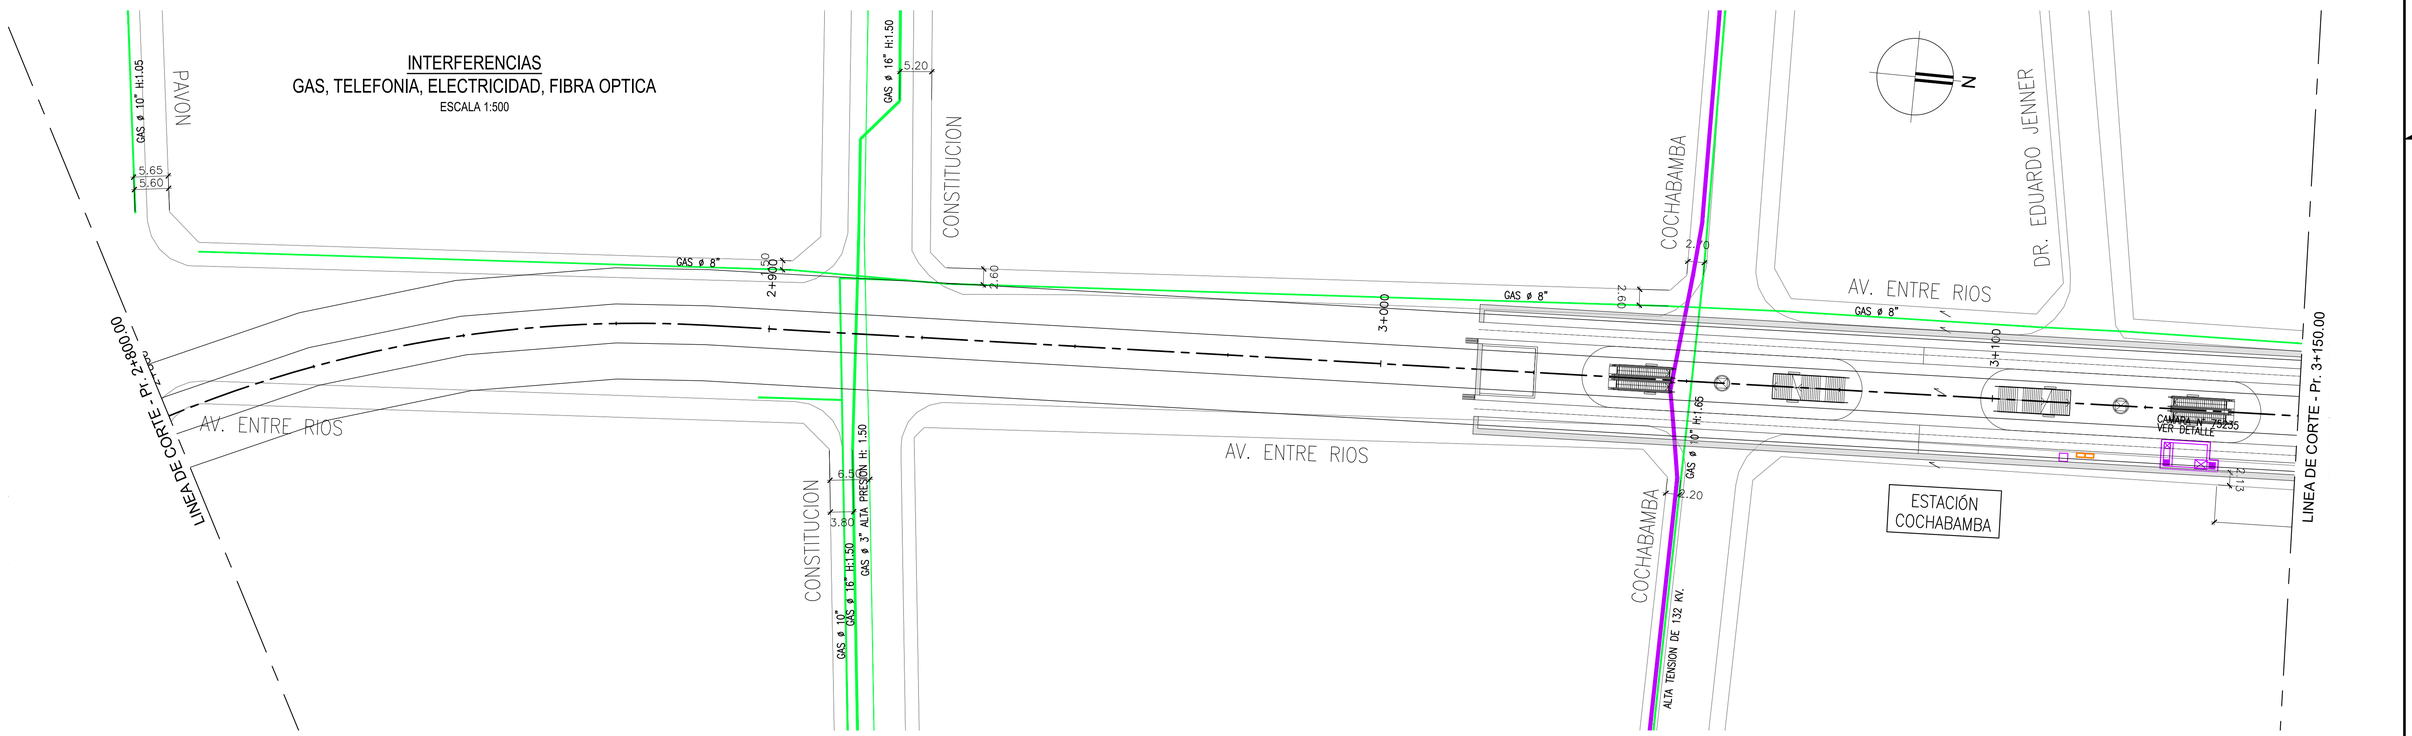

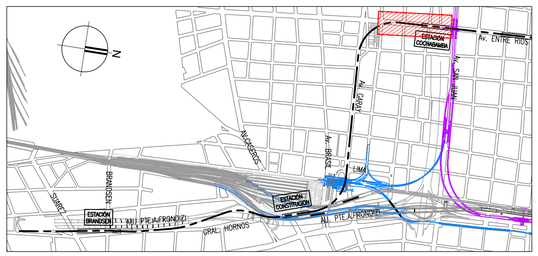

CROQUIS DE UBICACIÓN

REFERENCIAS

- RED CLOACAL
- RED PLUVIAL
- RED AGUA
- RED ELECTRICA
- RED GAS
- RED TELEFONICA
- RED FIBRA OPTICA MULTICANAL

0 10 20 30m
ESCALA 1:500

Ing. Mariano Micullich
DIRECTOR

N°	DIBUJÓ	REVISÓ	APROBÓ	FECHA	DESCRIPCIÓN
0	D.B.	P.C.		SET. 2025	EMISIÓN INICIAL

REVISIONES

MINISTERIO DE INFRAESTRUCTURA

URGELL PENEDO URGELL
ARQUITECTOS LYNCH VAGO RODRIGUEZ

PROYECTO DE ARQUITECTURA E INGENIERÍA RELACIONADO A LA CONSTRUCCIÓN INTEGRAL DE LA LÍNEA F DE SUBTERRÁNEOS DE LA CIUDAD DE BUENOS AIRES

FECHA: SETIEMBRE 2025	TRAZADO DE TÚNEL
ESCALA: HORIZ: 1:500 VERTICAL: -	INTERFERENCIAS TRAMO 1
	PLANIMETRÍA GENERAL - PROG. 2+800 A 3+150
FORMATO: A1	HOJA: 09/18
PLANO Nº: LF-GL-T01-INT-PL-009	REV.: 0

IF-2026-20223041-GCABA-APRA

19/9/2025 16:17 p. m.
LF-GL-T01-INT-PL-009.dwg

INTERFERENCIAS
SERVICOS CLOACALES, PLUVIALES, AGUA CORRIENTE
ESCALA 1:500

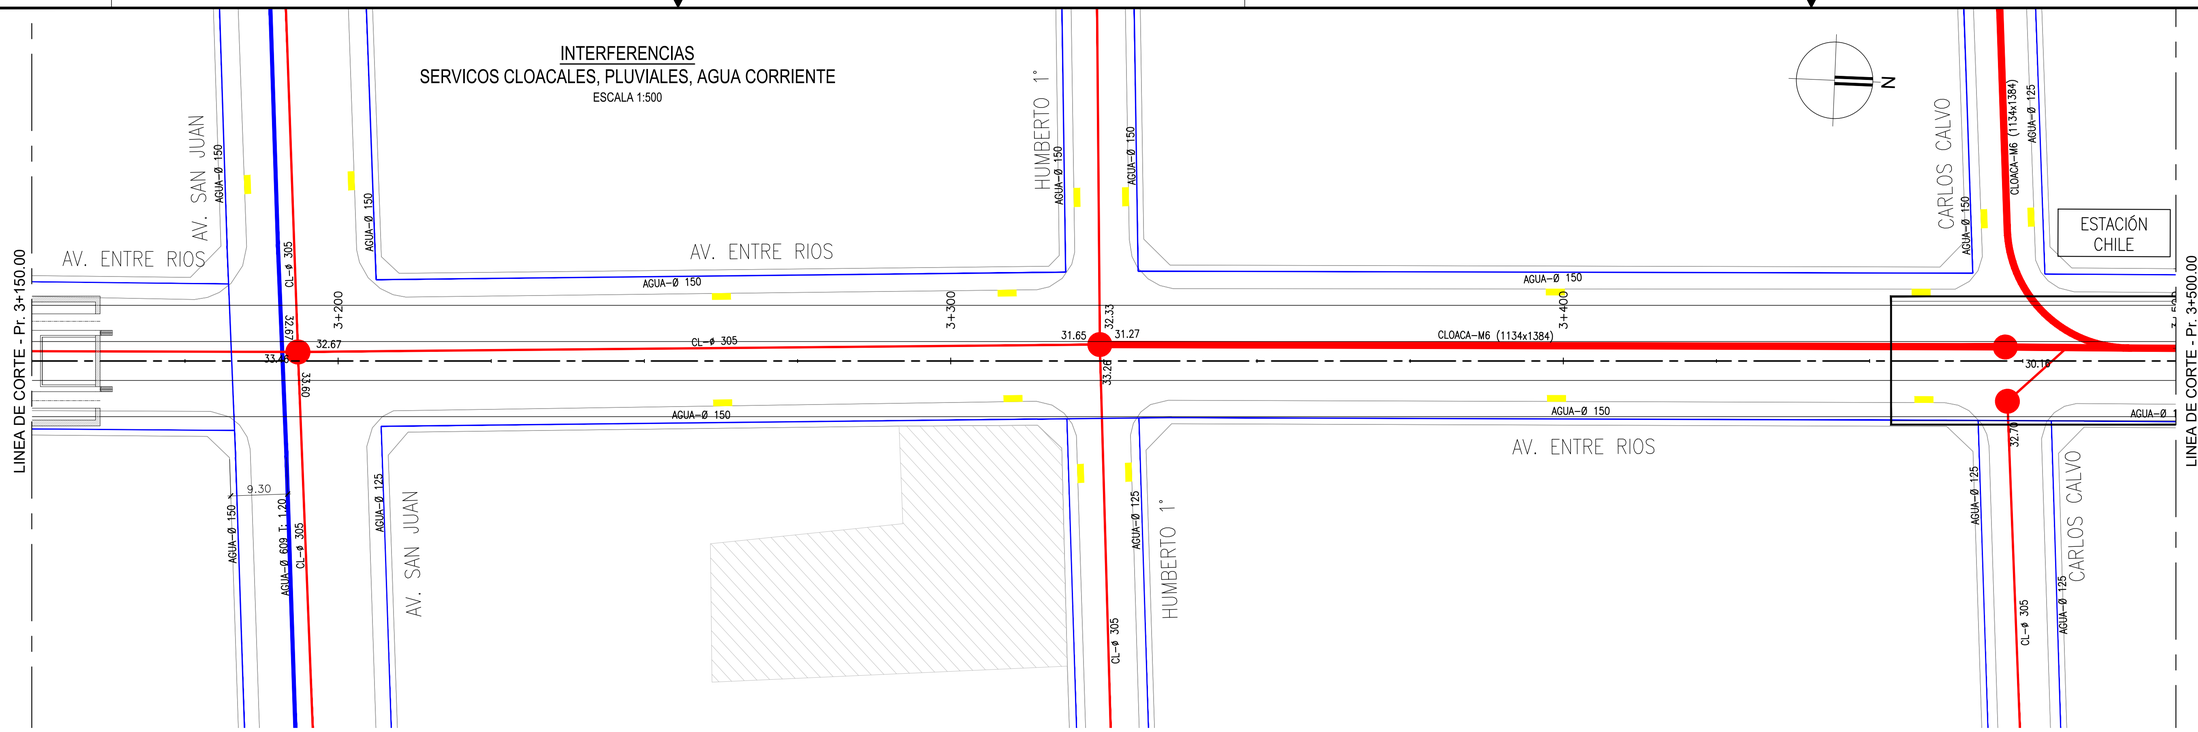

INTERFERENCIAS
GAS, TELEFONIA, ELECTRICIDAD, FIBRA OPTICA
ESCALA 1:500

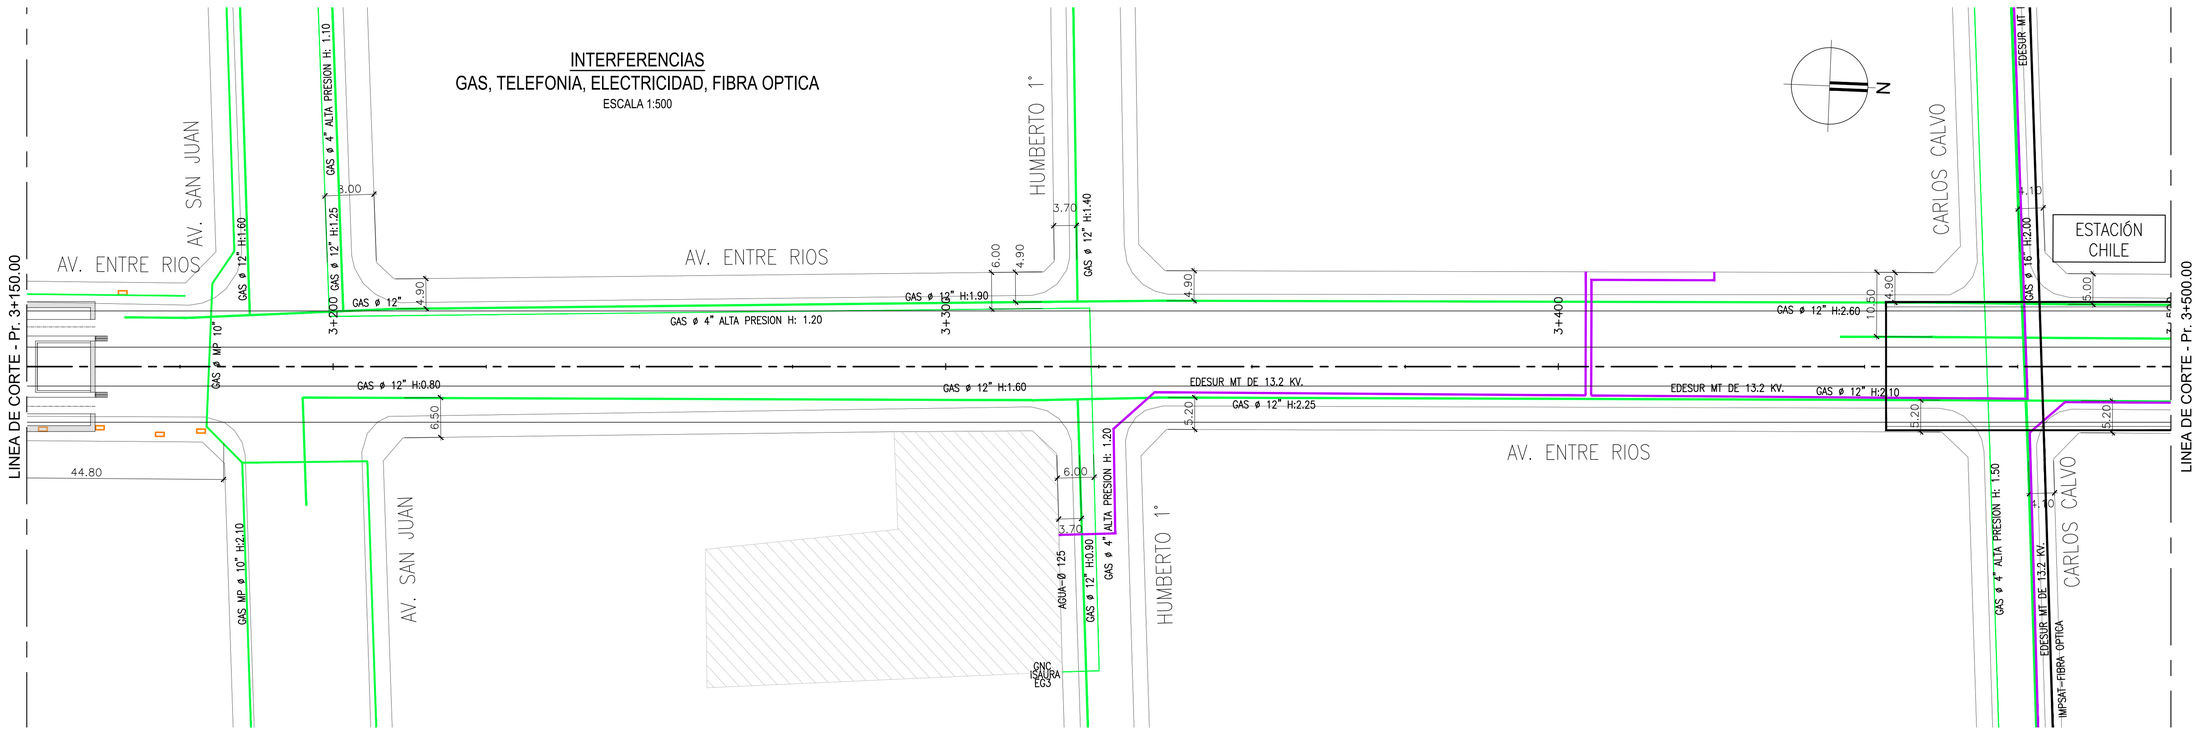

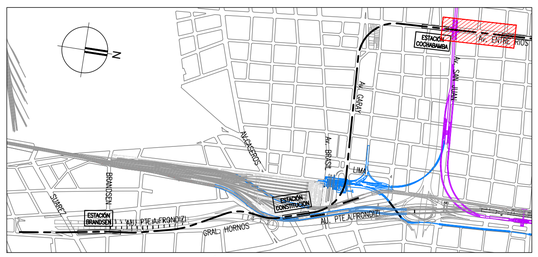

CROQUIS DE UBICACIÓN

REFERENCIAS

- RED CLOACAL
- RED PLUVIAL
- RED AGUA
- RED ELECTRICA
- RED GAS
- RED TELEFONICA
- RED FIBRA OPTICA MULTICANAL

0 10 20 30m
ESCALA 1:500

Ing. Mariano Miculicich
DIRECTOR

N°	DIBUJÓ	REVISÓ	APROBÓ	FECHA	DESCRIPCIÓN
0	D.B.	P.C.		SET. 2025	EMISIÓN INICIAL

REVISIONES

MINISTERIO DE INFRAESTRUCTURA

URGELL PENEDO URGELL
ARQUITECTOS LYNCH VAGO RODRIGUEZ

PROYECTO DE ARQUITECTURA E INGENIERÍA RELACIONADO A LA CONSTRUCCIÓN INTEGRAL DE LA LÍNEA F DE SUBTERRÁNEOS DE LA CIUDAD DE BUENOS AIRES

FECHA: SETIEMBRE 2025	TRAZADO DE TÚNEL
ESCALA:	INTERFERENCIAS TRAMO 1
HORIZ: 1:500	PLANIMETRÍA GENERAL - PROG. 3+150 A 3+500
VERTICAL: -	IF-2026-20223041-GCABA-APRA
FORMATO A1 / HOJA: 10/18	PLANO Nº: **LF-GL-T01-INT-PL-010** / REV.: **0**

19/9/2025 16:17 p. m.
LF-GL-T01-INT-PL-010.dwg

INTERFERENCIAS
SERVICOS CLOACALES, PLUVIALES, AGUA CORRIENTE
ESCALA 1:500

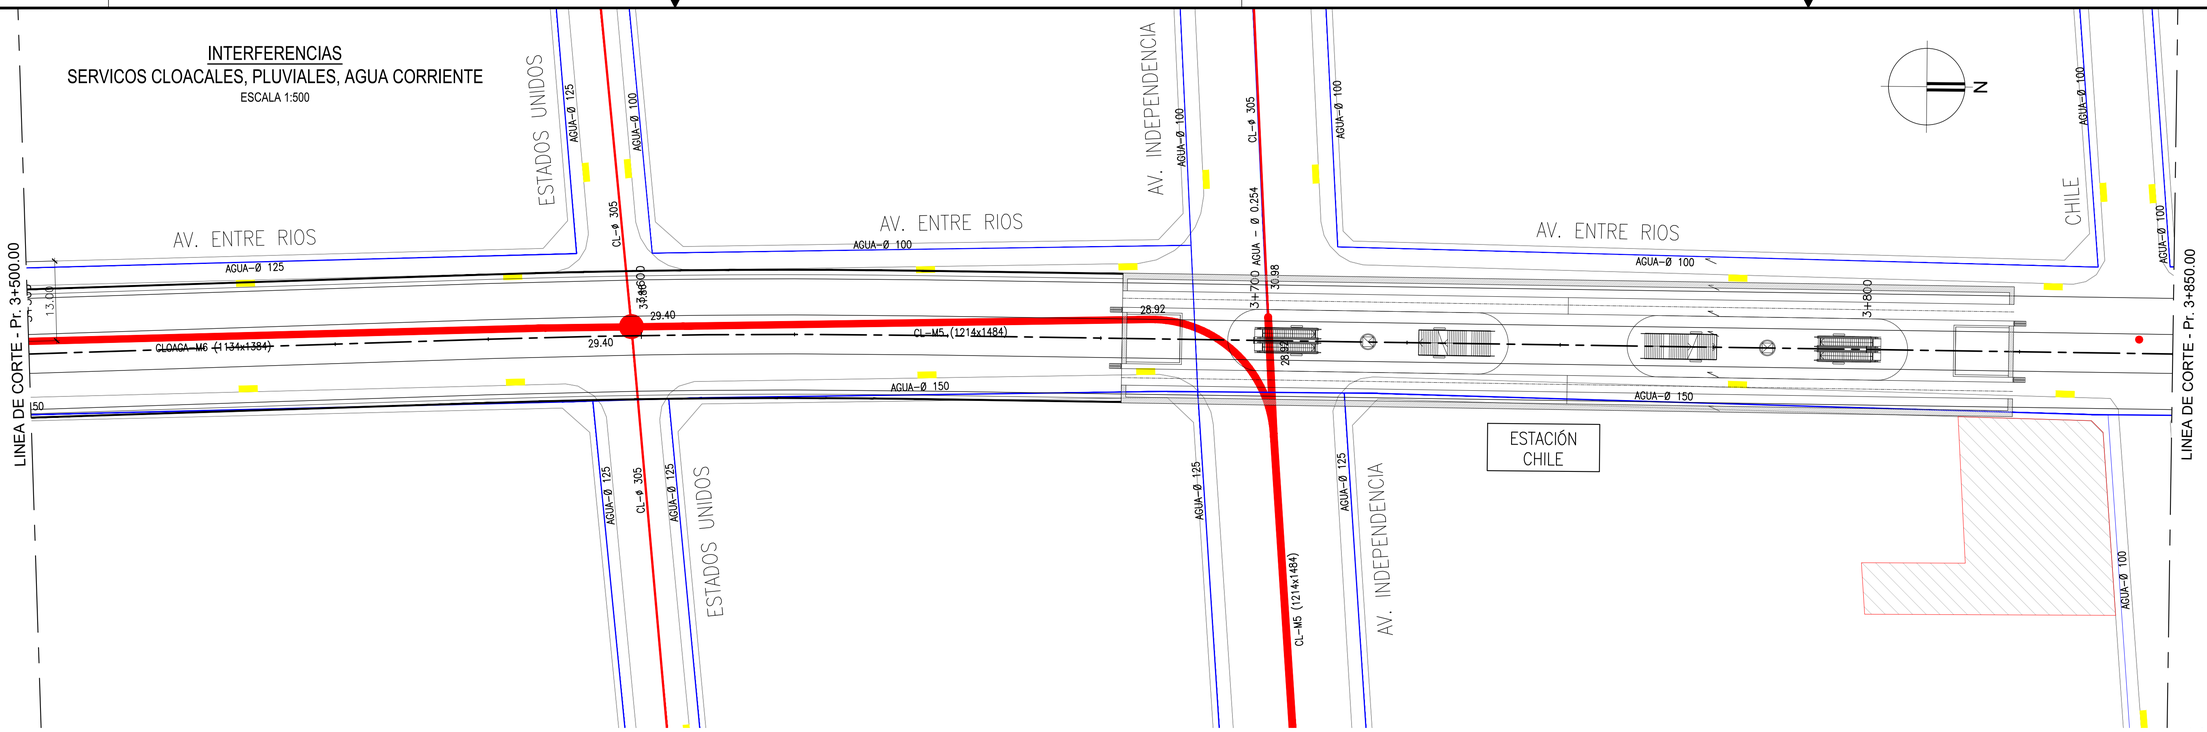

INTERFERENCIAS
GAS, TELEFONIA, ELECTRICIDAD, FIBRA OPTICA
ESCALA 1:500

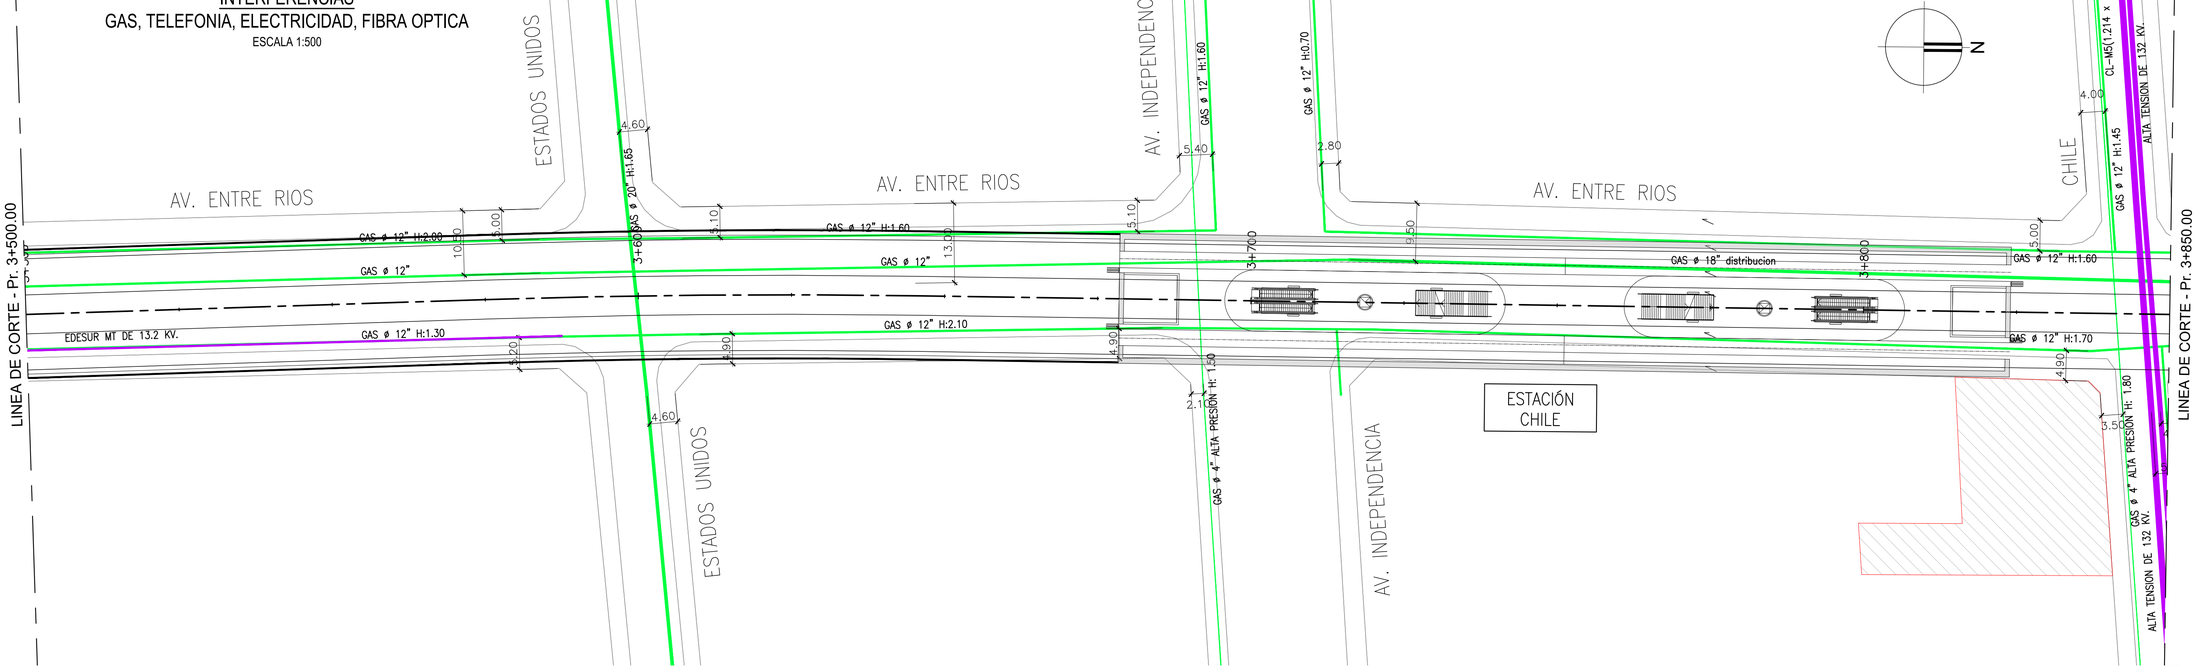

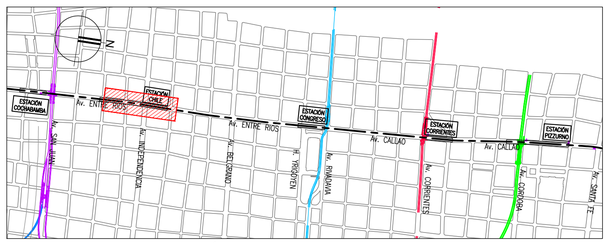

CROQUIS DE UBICACIÓN

REFERENCIAS
- RED CLOACAL
- RED PLUVIAL
- RED AGUA
- RED ELECTRICA
- RED GAS
- RED TELEFONICA
- RED FIBRA OPTICA MULTICANAL

0 10 20 30m
ESCALA 1:500

Ing. Mariano Miculicich
DIRECTOR

N°	DIBUJÓ	REVISÓ	APROBÓ	FECHA	DESCRIPCIÓN
0	D.B.	P.C.		SET. 2025	EMISIÓN INICIAL

REVISIONES

MINISTERIO DE INFRAESTRUCTURA

URGELL PENEDO URGELL
ARQUITECTOS LYNCH VAGO RODRIGUEZ

PROYECTO DE ARQUITECTURA E INGENIERÍA RELACIONADO A LA CONSTRUCCIÓN INTEGRAL DE LA LÍNEA F DE SUBTERRÁNEOS DE LA CIUDAD DE BUENOS AIRES

FECHA: SETIEMBRE 2025
ESCALA: HORIZ: 1:500 VERTICAL: -
FORMATO: A1
HOJA: 11/18

TRAZADO DE TÚNEL
INTERFERENCIAS TRAMO 1
PLANIMETRÍA GENERAL - PROG. 3+500 A 3+850

IF-2026-20223041-GCABA-APRA

PLANO Nº: **LF-GL-T01-INT-PL-011**
REV.: **0**

19/9/2025 16:17 p. m.
LF-GL-T01-INT-PL-003-0018_0.dwg

INTERFERENCIAS
SERVICOS CLOACALES, PLUVIALES, AGUA CORRIENTE
ESCALA 1:500

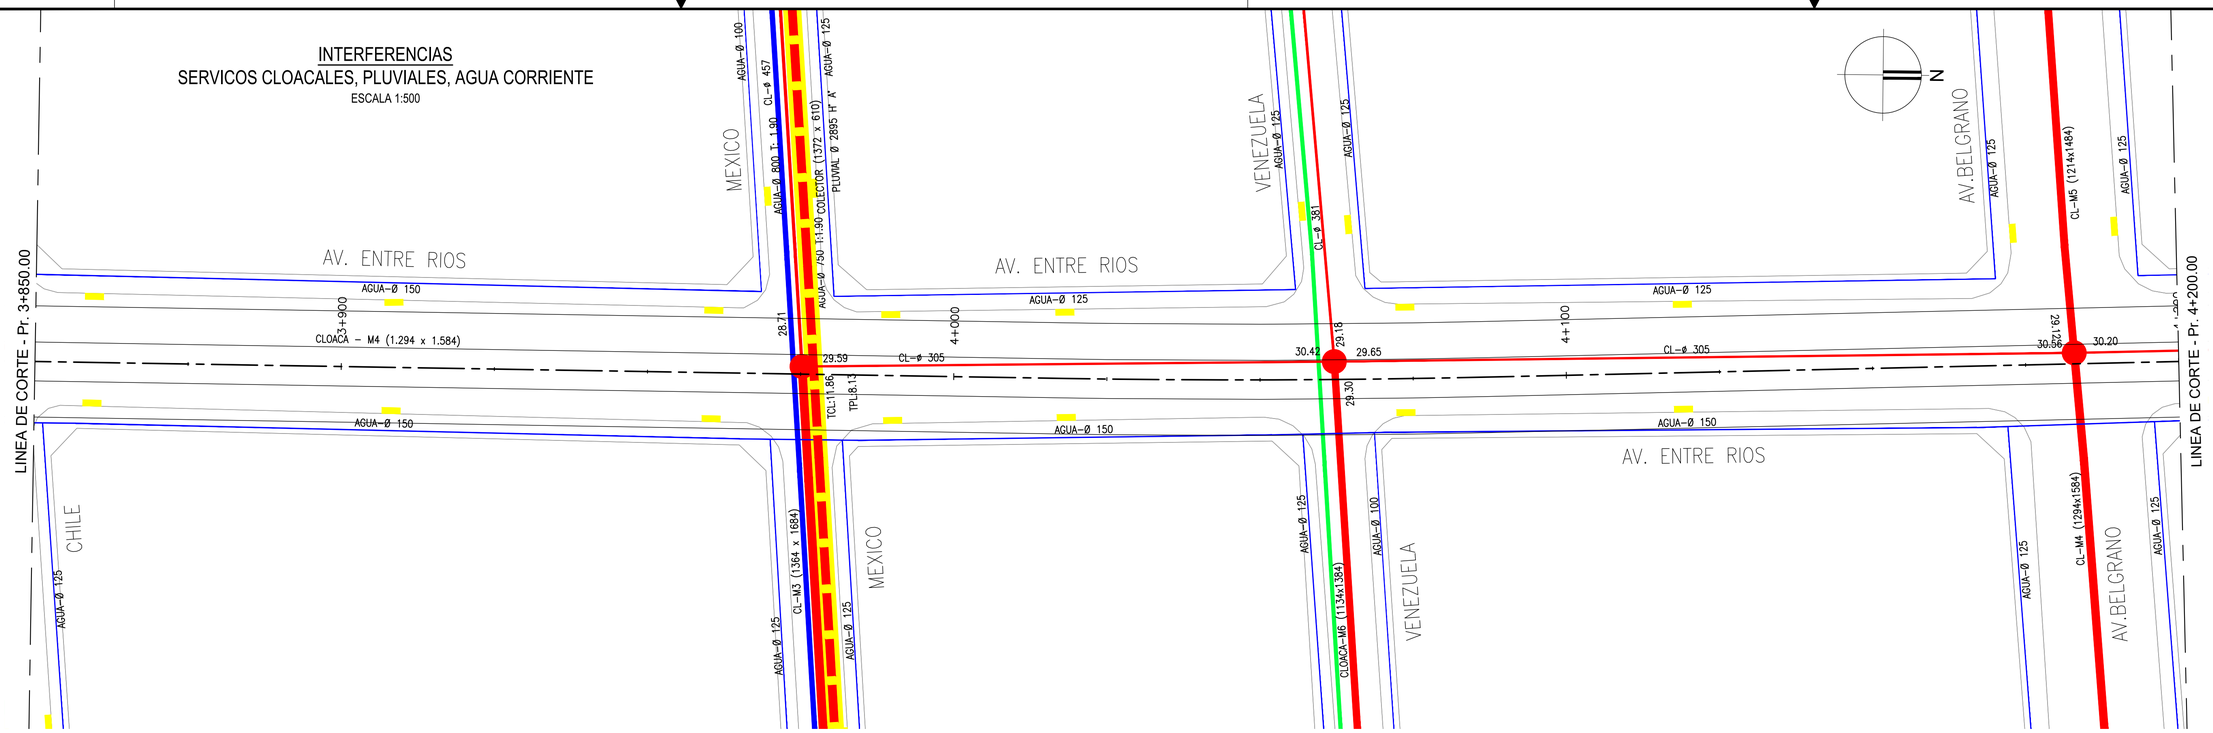

INTERFERENCIAS
GAS, TELEFONIA, ELECTRICIDAD, FIBRA OPTICA
ESCALA 1:500

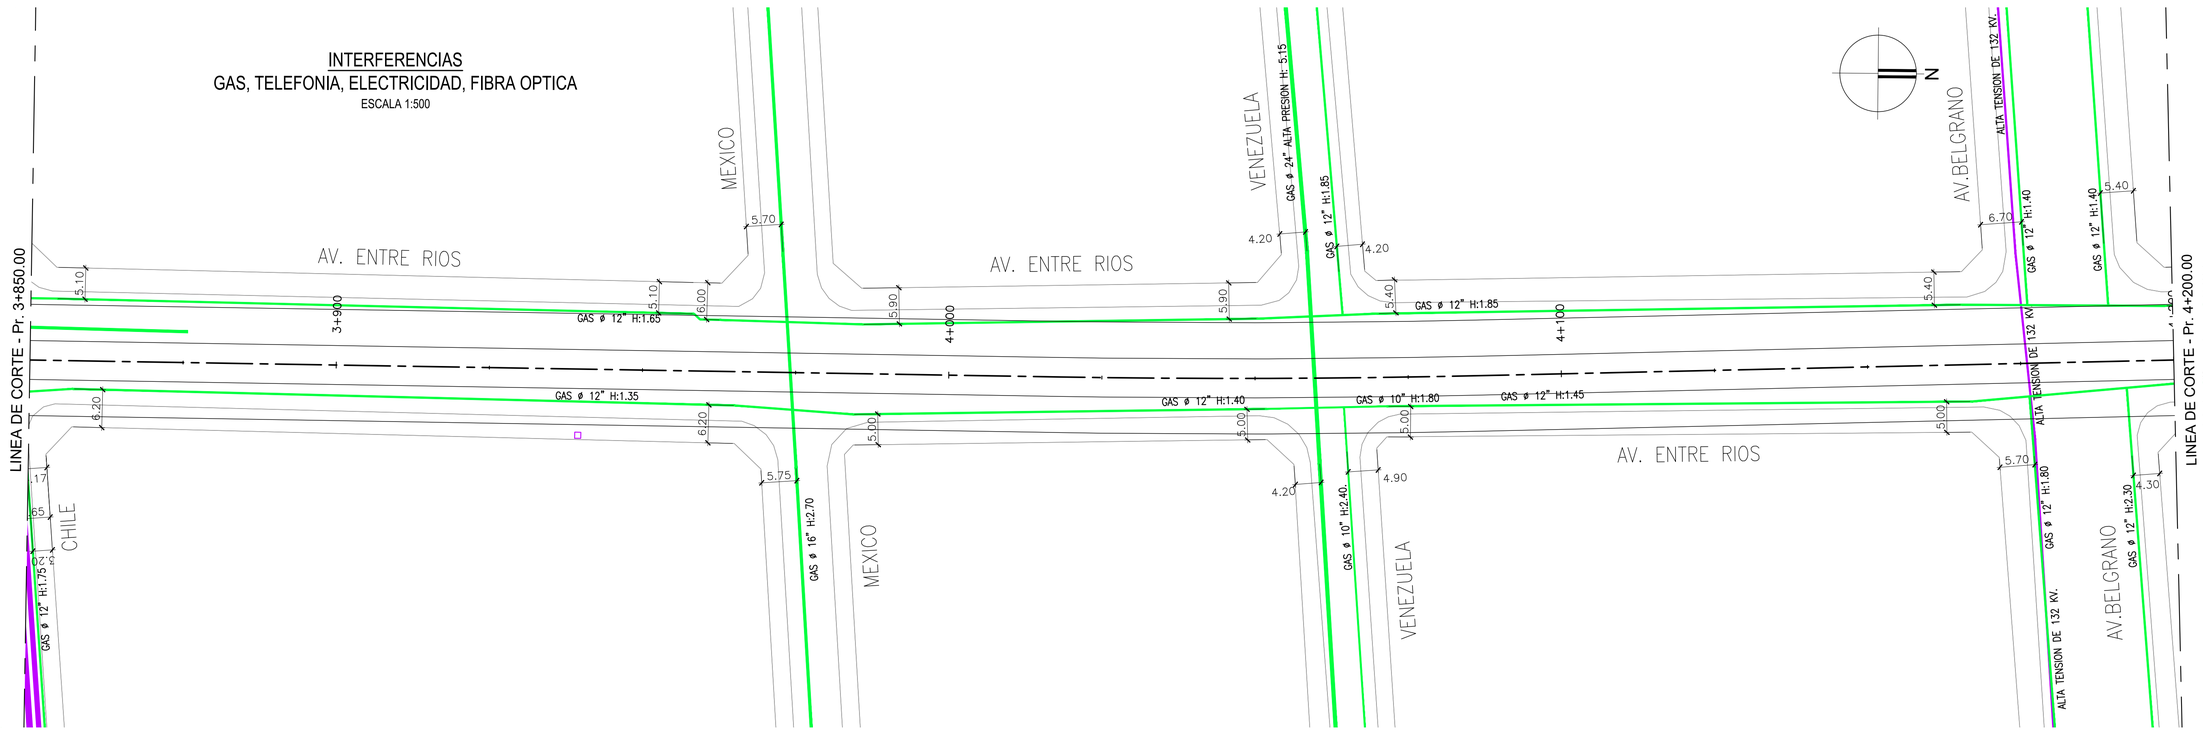

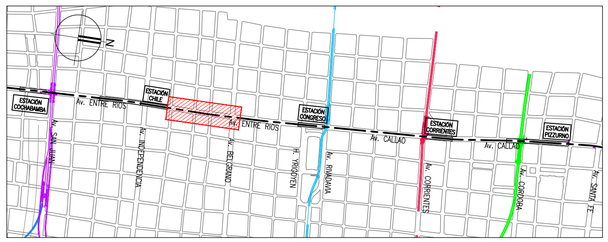

CROQUIS DE UBICACIÓN

REFERENCIAS

- RED CLOACAL
- RED PLUVIAL
- RED AGUA
- RED ELECTRICA
- RED GAS
- RED TELEFONICA
- RED FIBRA OPTICA MULTICANAL

0 10 20 30m
ESCALA 1:500

Ing. Mariano Micullicich
DIRECTOR

N°	DIBUJÓ	REVISÓ	APROBÓ	FECHA	DESCRIPCIÓN
0	D.B.	P.C.		SET. 2025	EMISIÓN INICIAL

REVISIONES

MINISTERIO DE INFRAESTRUCTURA

URGELL PENEDO URGELL
ARQUITECTOS LYNCH VAGO RODRIGUEZ

IATASA INGENIERIA

PROYECTO DE ARQUITECTURA E INGENIERÍA RELACIONADO A LA CONSTRUCCIÓN INTEGRAL DE LA LÍNEA F DE SUBTERRÁNEOS DE LA CIUDAD DE BUENOS AIRES

FECHA: SETIEMBRE 2025	TRAZADO DE TÚNEL
ESCALA: HORIZ: 1:500 VERTICAL: -	INTERFERENCIAS TRAMO 1
	PLANIMETRÍA GENERAL - PROG. 3+850 A 4+200
FORMATO A1 / HOJA: 12/18	PLANO Nº: LF-GL-T01-INT-PL-012 / REV.: 0

IF-2026-20223941-GCABA-APRA

19/9/2025 16:17 p. m.
LF-GL-T01-INT-PL-012_0.dwg

INTERFERENCIAS
SERVICIOS CLOACALES, PLUVIALES, AGUA CORRIENTE
ESCALA 1:500

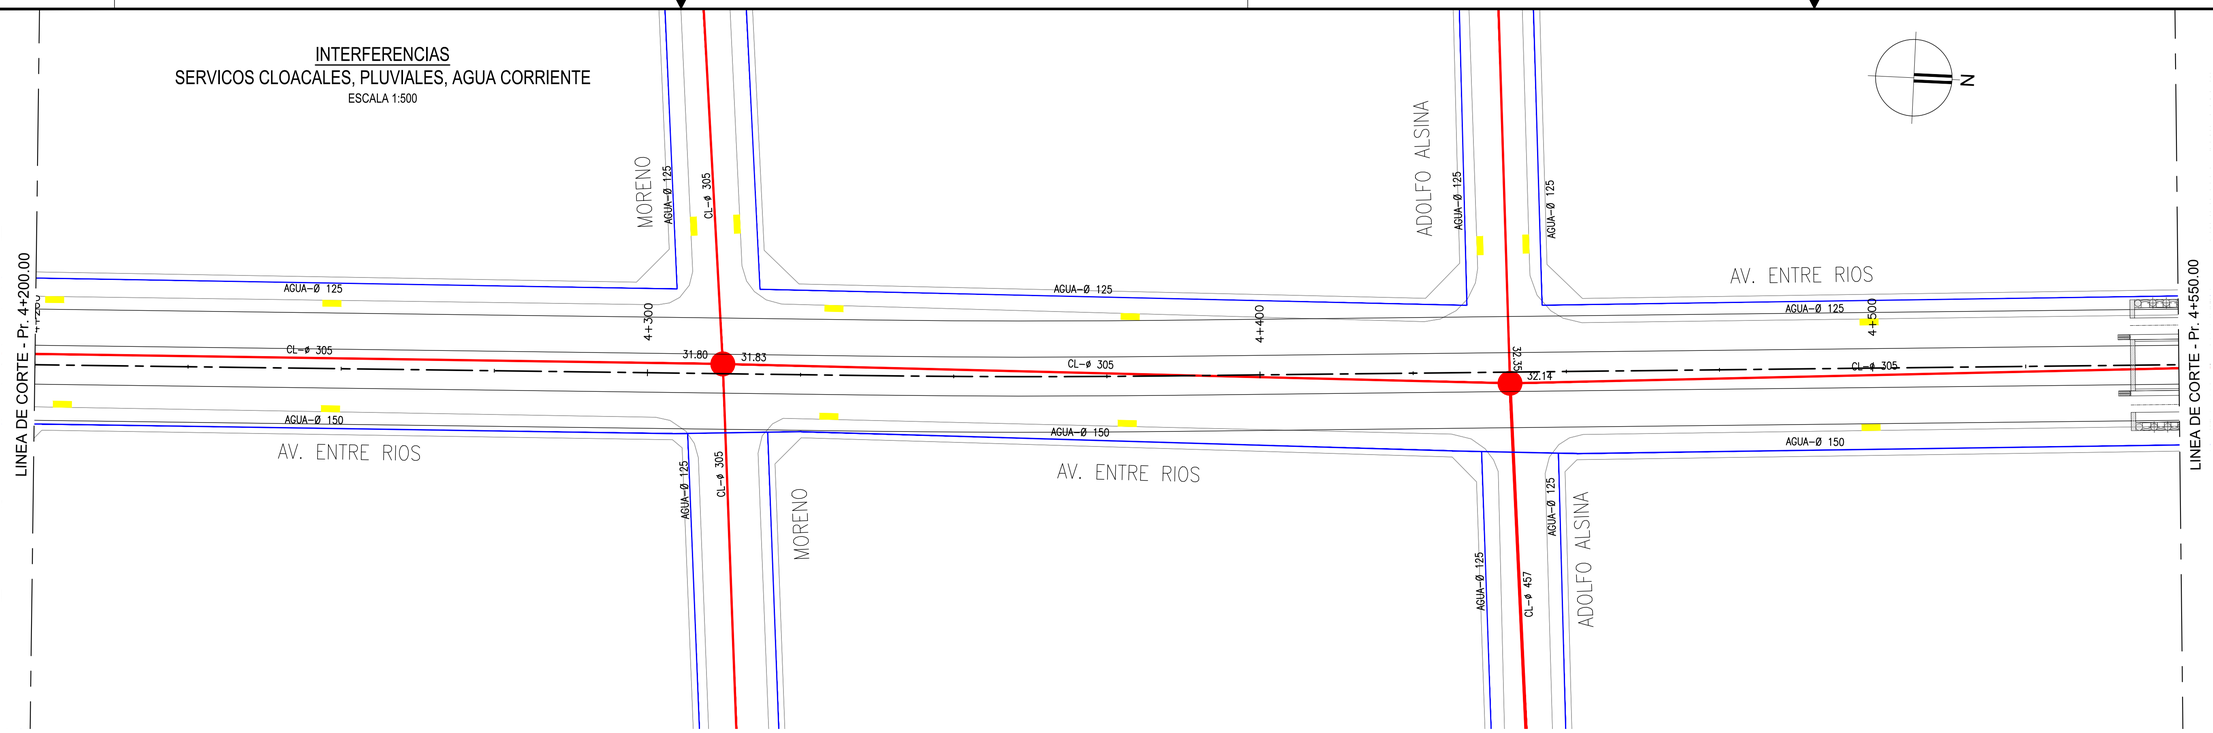

INTERFERENCIAS
GAS, TELEFONIA, ELECTRICIDAD, FIBRA OPTICA
ESCALA 1:500

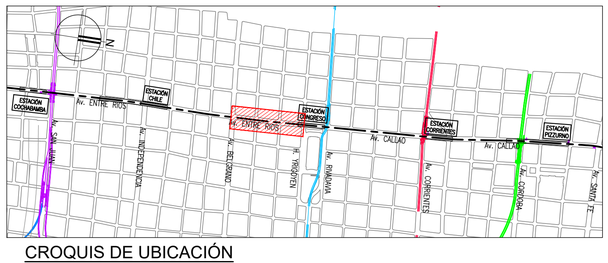

CROQUIS DE UBICACIÓN

REFERENCIAS

- RED CLOACAL
- RED PLUVIAL
- RED AGUA
- RED ELECTRICA
- RED GAS
- RED TELEFONICA
- RED FIBRA OPTICA MULTICANAL

0 10 20 30m
ESCALA 1:500

Ing. Mariano Miculicich
DIRECTOR

N°	DIBUJÓ	REVISÓ	APROBÓ	FECHA	DESCRIPCIÓN
0	D.B.	P.C.		SET. 2025	EMISIÓN INICIAL

REVISIONES

MINISTERIO DE INFRAESTRUCTURA

URGELL PENEDO URGELL
ARQUITECTOS LYNCH VAGO RODRIGUEZ

PROYECTO DE ARQUITECTURA E INGENIERÍA RELACIONADO A LA CONSTRUCCIÓN INTEGRAL DE LA LÍNEA F DE SUBTERRÁNEOS DE LA CIUDAD DE BUENOS AIRES

FECHA: SETIEMBRE 2025	TRAZADO DE TÚNEL
ESCALA:	INTERFERENCIAS TRAMO 1
HORIZ: 1:500	PLANIMETRÍA GENERAL - PROG. 4+200 A 4+550
VERTICAL: -	IF-2026-20223041-GCABA-APRA
FORMATO A1 / HOJA: 13/18	PLANO Nº: LF-GL-T01-INT-PL-013 / REV.: 0

19/9/2025 16:17 p. m.
LF-GL-T01-INT-PL-013.dwg

INTERFERENCIAS
SERVICOS CLOACALES, PLUVIALES, AGUA CORRIENTE
ESCALA 1:500

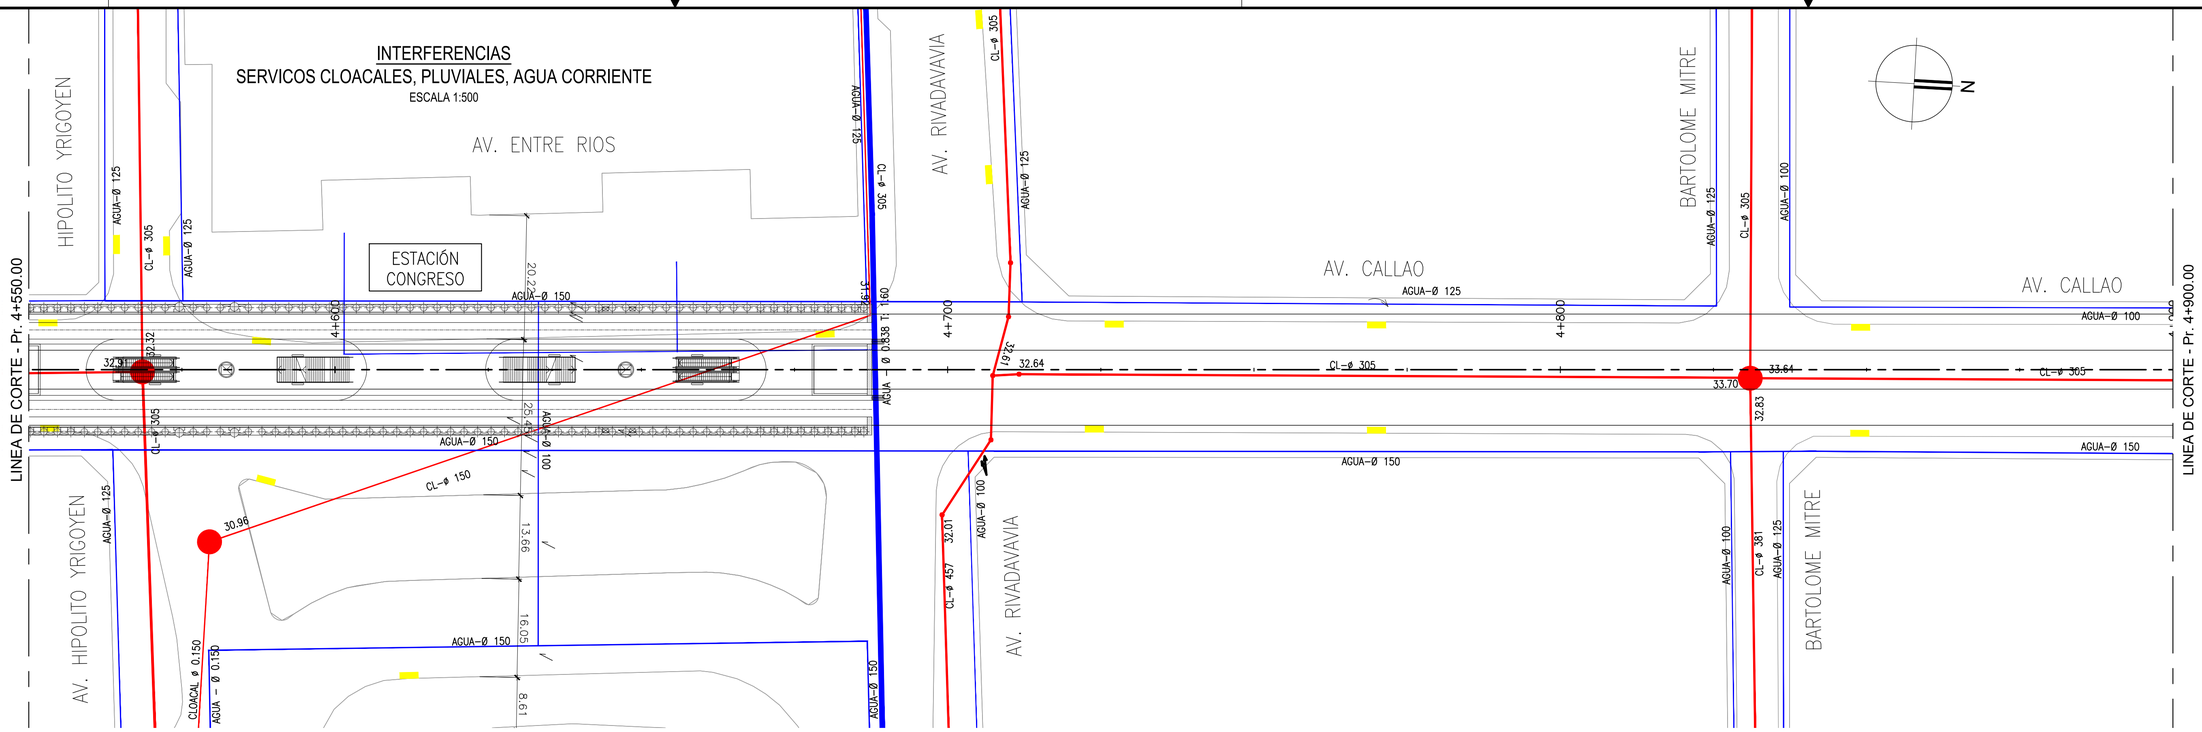

INTERFERENCIAS
GAS, TELEFONIA, ELECTRICIDAD, FIBRA OPTICA
ESCALA 1:500

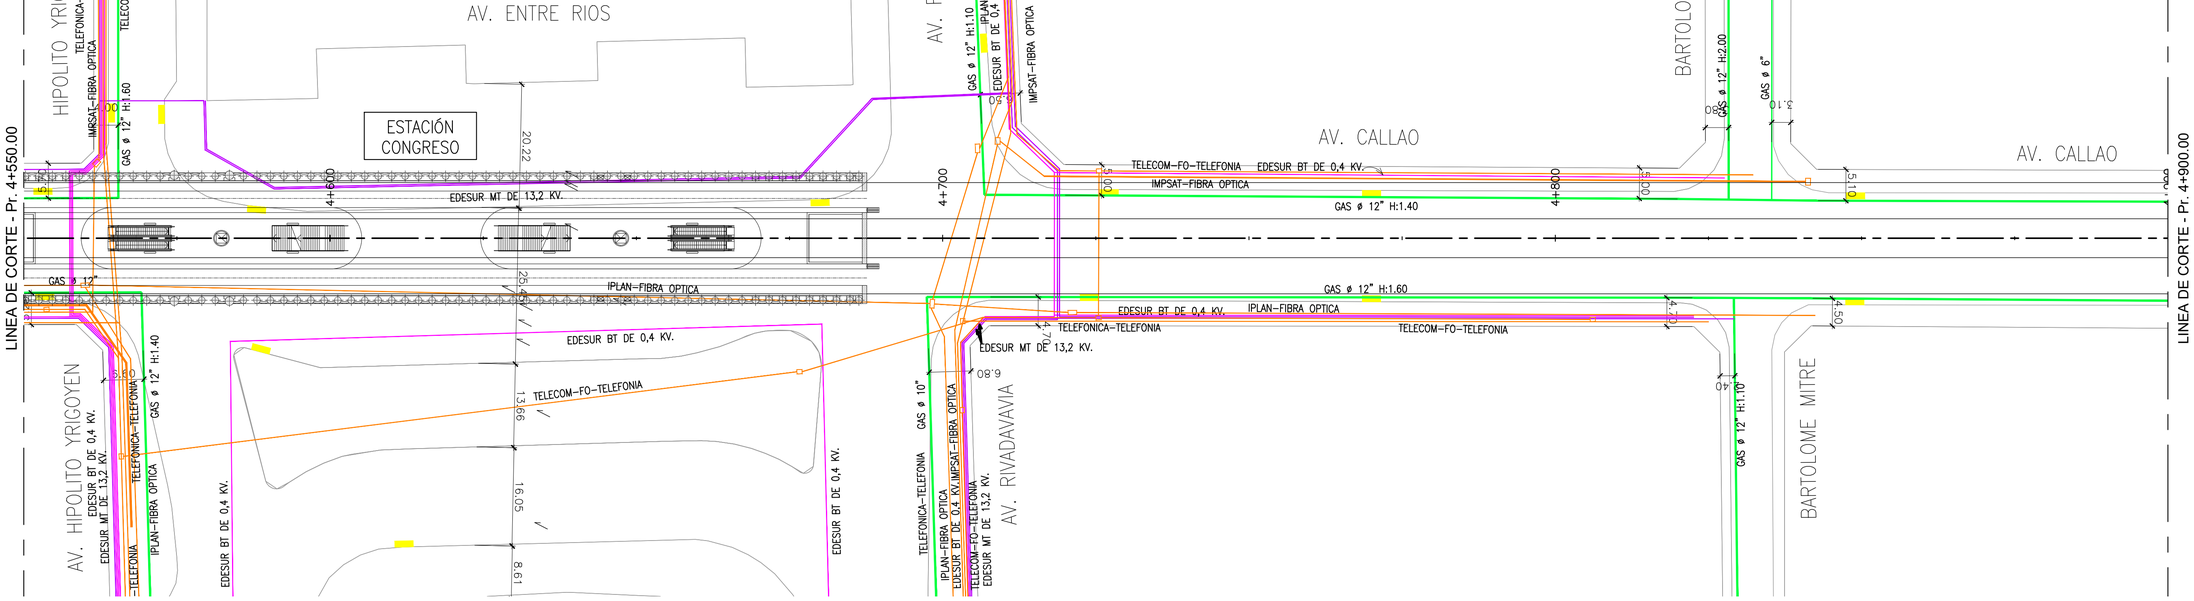

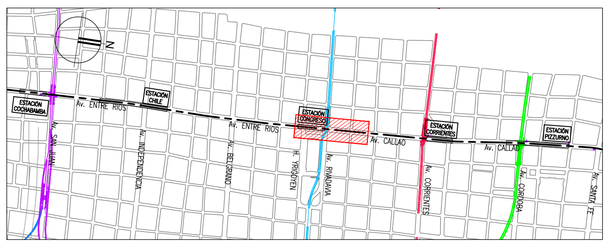

CROQUIS DE UBICACIÓN

REFERENCIAS
- RED CLOACAL
- RED PLUVIAL
- RED AGUA
- RED ELECTRICA
- RED GAS
- RED TELEFONICA
- RED FIBRA OPTICA MULTICANAL

0 10 20 30m
ESCALA 1:500

Ing. Mariano Miculicich
DIRECTOR

N°	DIBUJÓ	REVISÓ	APROBÓ	FECHA	DESCRIPCIÓN
0	D.B.	P.C.		SET. 2025	EMISIÓN INICIAL

REVISIONES

MINISTERIO DE INFRAESTRUCTURA
Subte
URGELL PENEDO URGELL ARQUITECTOS LYNCH VAGO RODRIGUEZ
IATASA INGENIERIA

PROYECTO DE ARQUITECTURA E INGENIERÍA RELACIONADO A LA CONSTRUCCIÓN INTEGRAL DE LA LÍNEA F DE SUBTERRÁNEOS DE LA CIUDAD DE BUENOS AIRES

FECHA: SETIEMBRE 2025	TRAZADO DE TÚNEL
ESCALA: HORIZ: 1:500 VERTICAL: -	INTERFERENCIAS TRAMO 1
	PLANIMETRÍA GENERAL - PROG. 4+550 A 4+900
FORMATO A1 / HOJA: 14/18	PLANO Nº: LF-GL-T01-INT-PL-014 / REV.: 0

IF-2026-20223041-GCABA-APRA

19/9/2025 16:17 p. m.
LF_GL_T01_INT_PL_000_0018_0.dwg

INTERFERENCIAS
SERVICOS CLOACALES, PLUVIALES, AGUA CORRIENTE
ESCALA 1:500

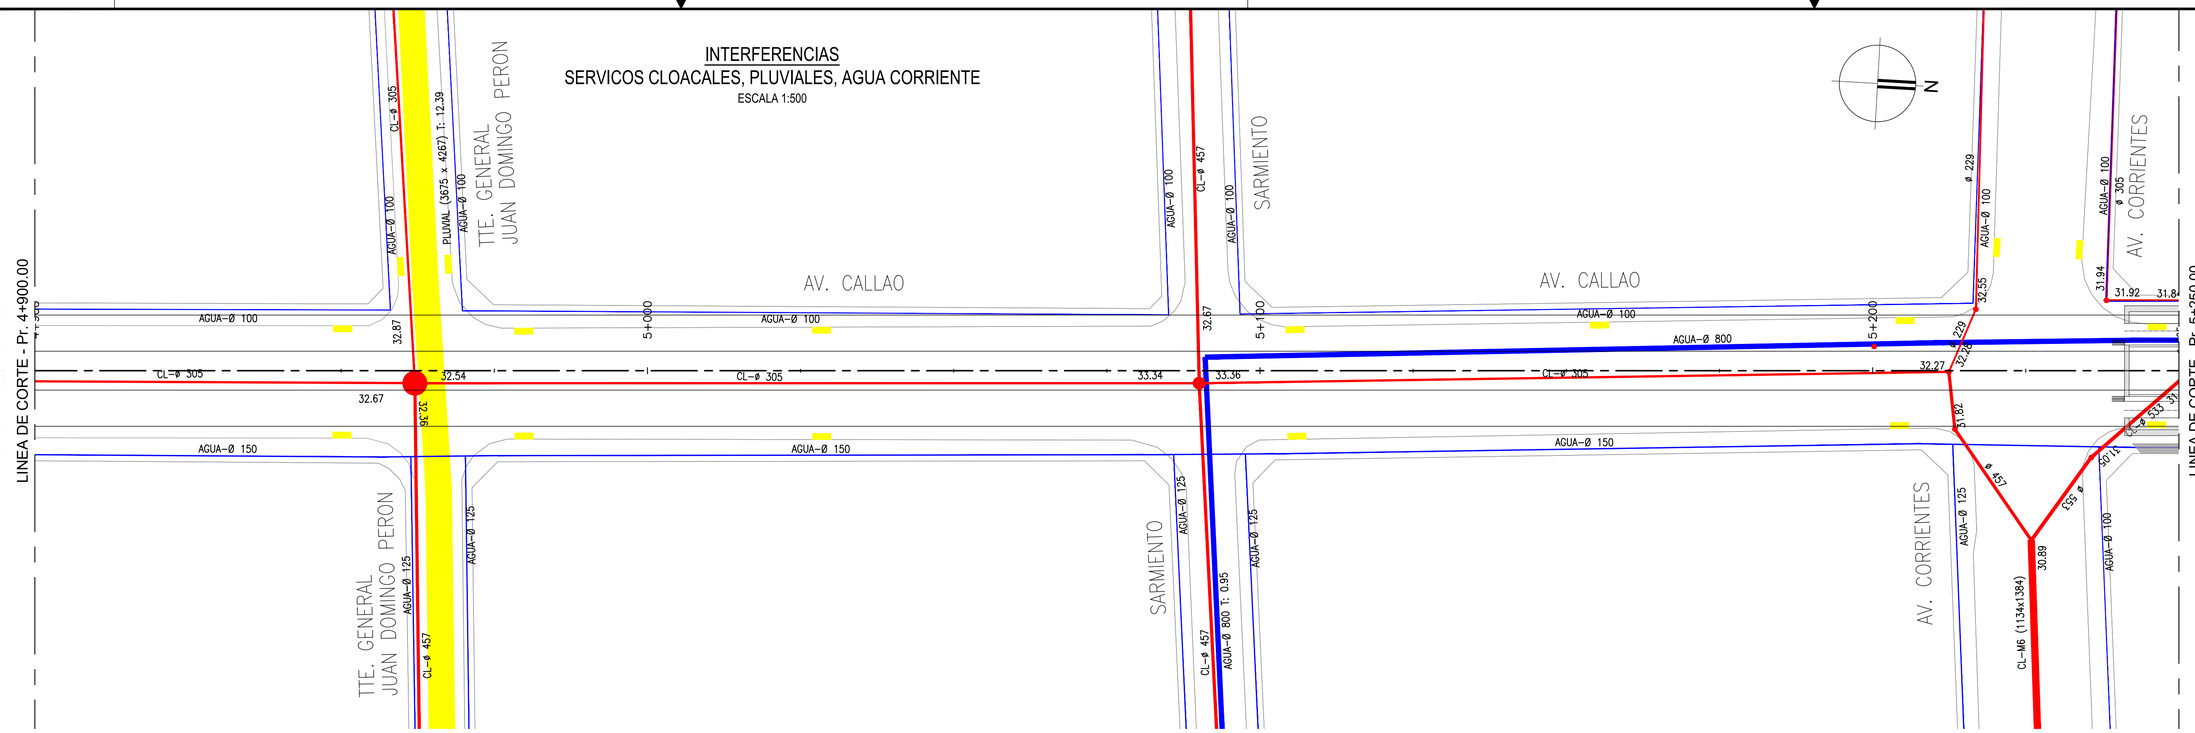

INTERFERENCIAS
GAS, TELEFONIA, ELECTRICIDAD, FIBRA OPTICA
ESCALA 1:500

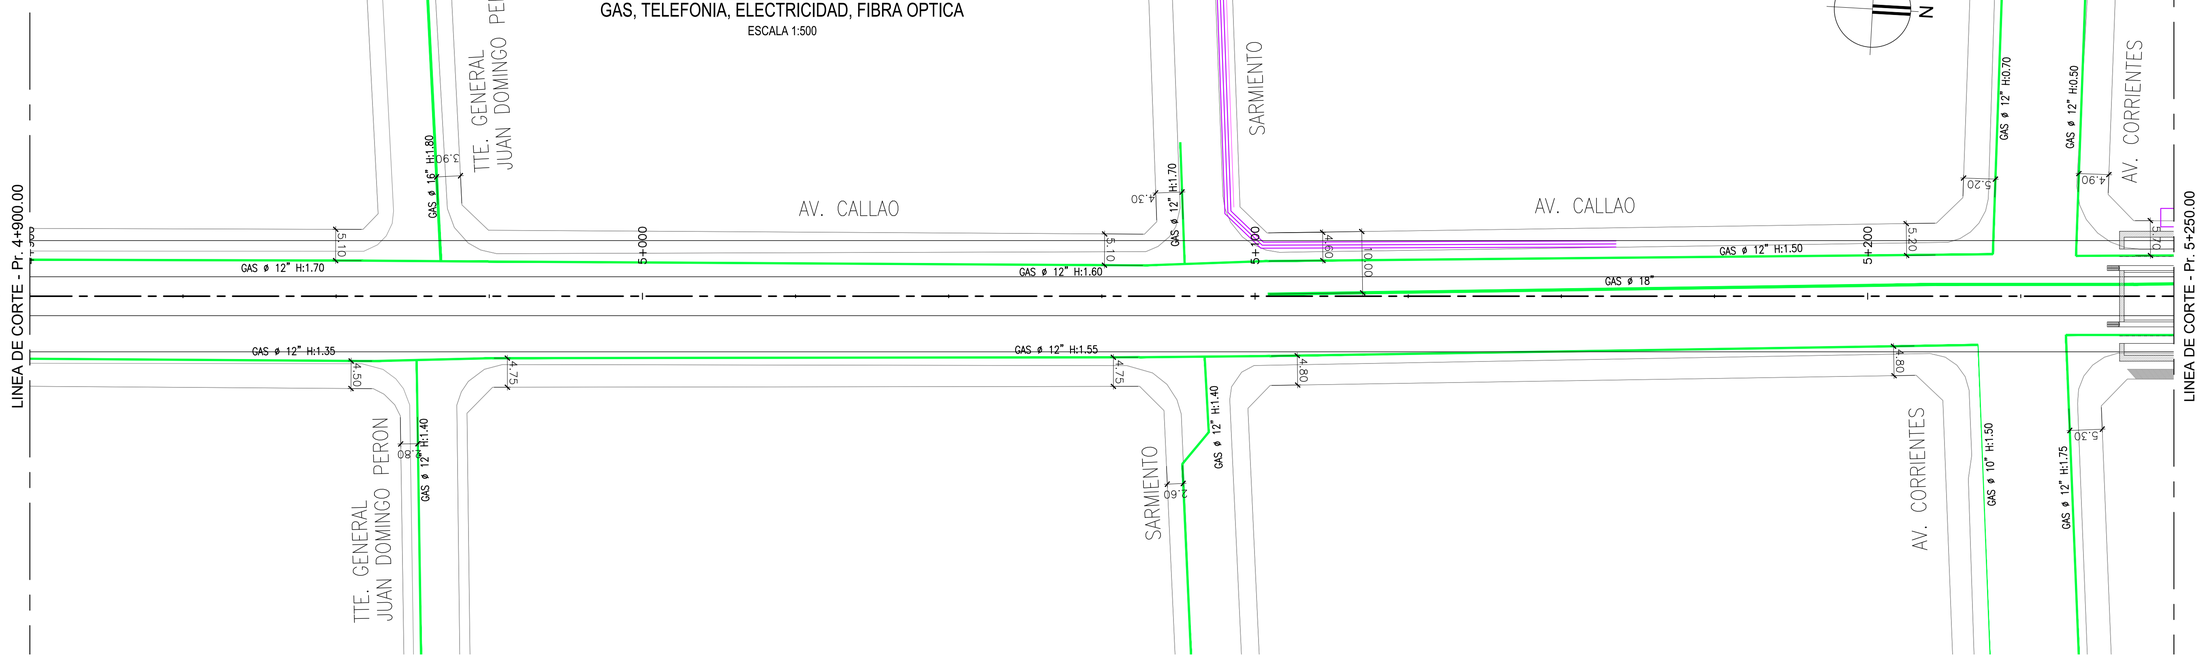

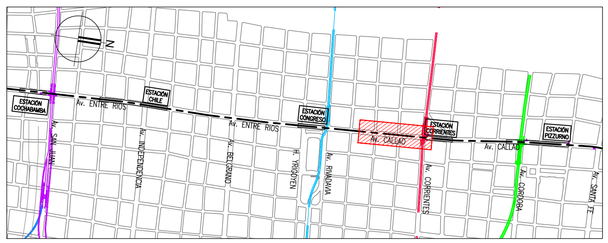

CROQUIS DE UBICACIÓN

REFERENCIAS

- RED CLOACAL
- RED PLUVIAL
- RED AGUA
- RED ELECTRICA
- RED GAS
- RED TELEFONICA
- RED FIBRA OPTICA MULTICANAL

0 10 20 30m
ESCALA 1:500

Ing. Mariano Miculicich
DIRECTOR

N°	DIBUJÓ	REVISÓ	APROBÓ	FECHA	DESCRIPCIÓN
0	D.B.	P.C.		SET. 2025	EMISIÓN INICIAL

REVISIONES

MINISTERIO DE INFRAESTRUCTURA

URGELL PENEDO URGELL
ARQUITECTOS LYNCH VAGO RODRIGUEZ

IATASA INGENIERIA

PROYECTO DE ARQUITECTURA E INGENIERÍA RELACIONADO A LA CONSTRUCCIÓN INTEGRAL DE LA LÍNEA F DE SUBTERRÁNEOS DE LA CIUDAD DE BUENOS AIRES

FECHA: SETIEMBRE 2025	TRAZADO DE TÚNEL
ESCALA: HORIZ: 1:500 VERTICAL: -	INTERFERENCIAS TRAMO 1
	PLANIMETRÍA GENERAL - PROG. 4+900 A 5+250
FORMATO A1 / HOJA: 15/18	PLANO Nº: LF-GL-T01-INT-PL-015 / REV.: 0

IF-2026-20223041-GCABA-APRA

19/9/2025 16:17 p. m.
LF-GL-T01-INT-PL-001-018_0.dwg

INTERFERENCIAS
SERVICOS CLOACALES, PLUVIALES, AGUA CORRIENTE
ESCALA 1:500

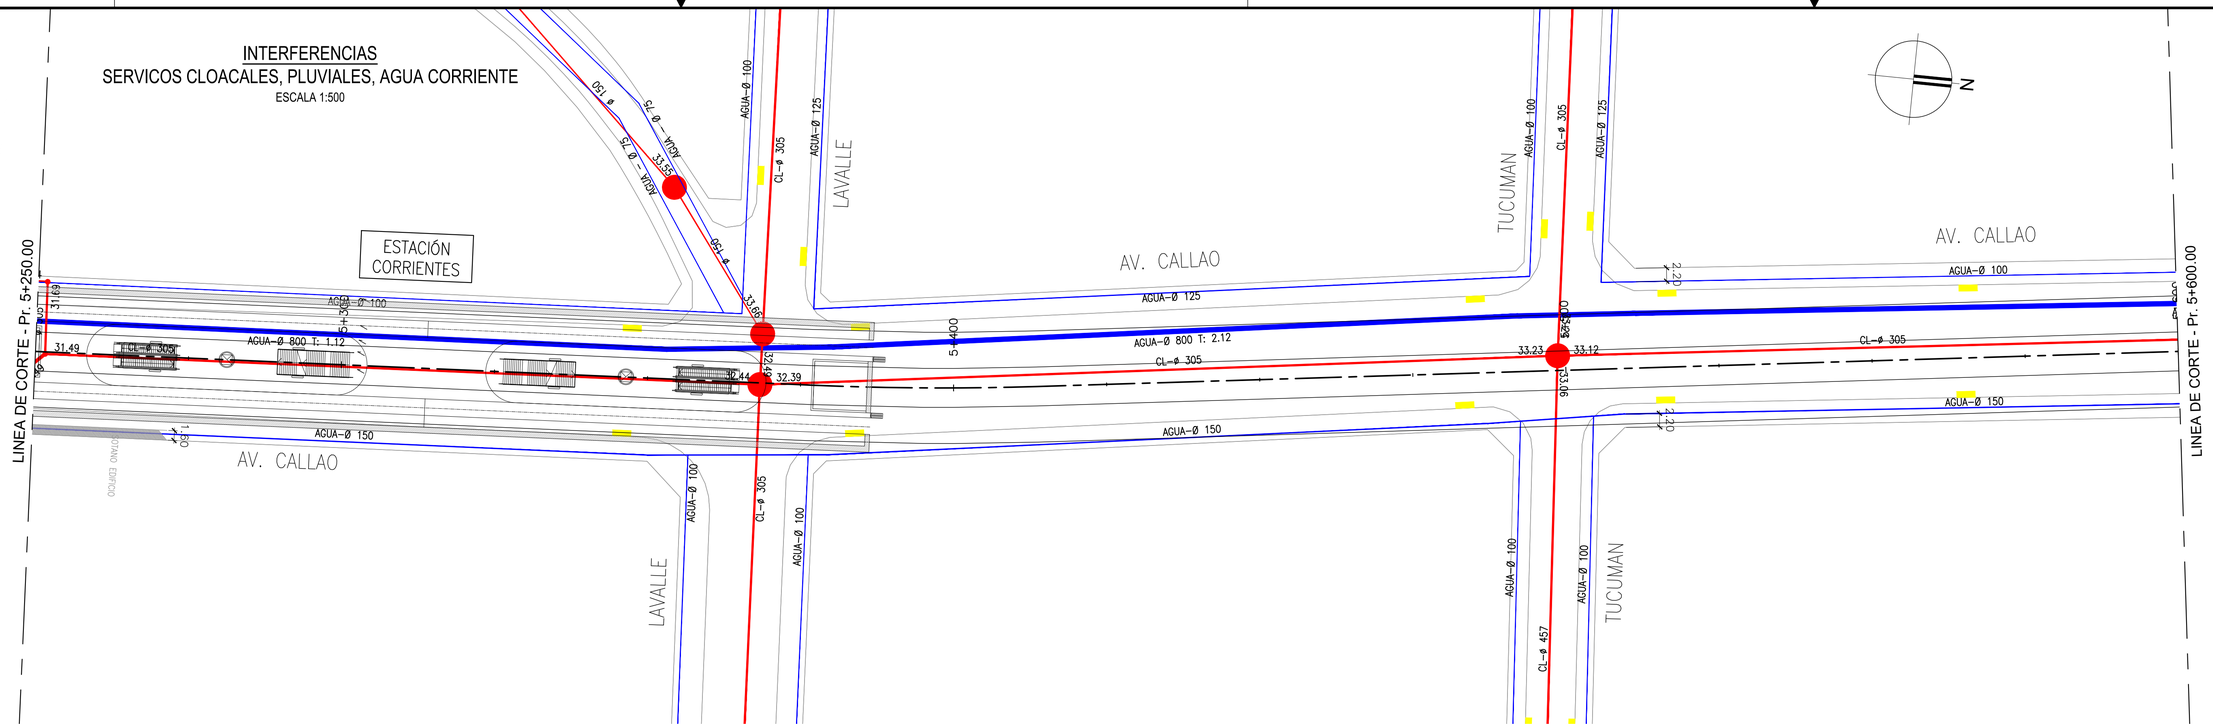

INTERFERENCIAS
GAS, TELEFONIA, ELECTRICIDAD, FIBRA OPTICA
ESCALA 1:500

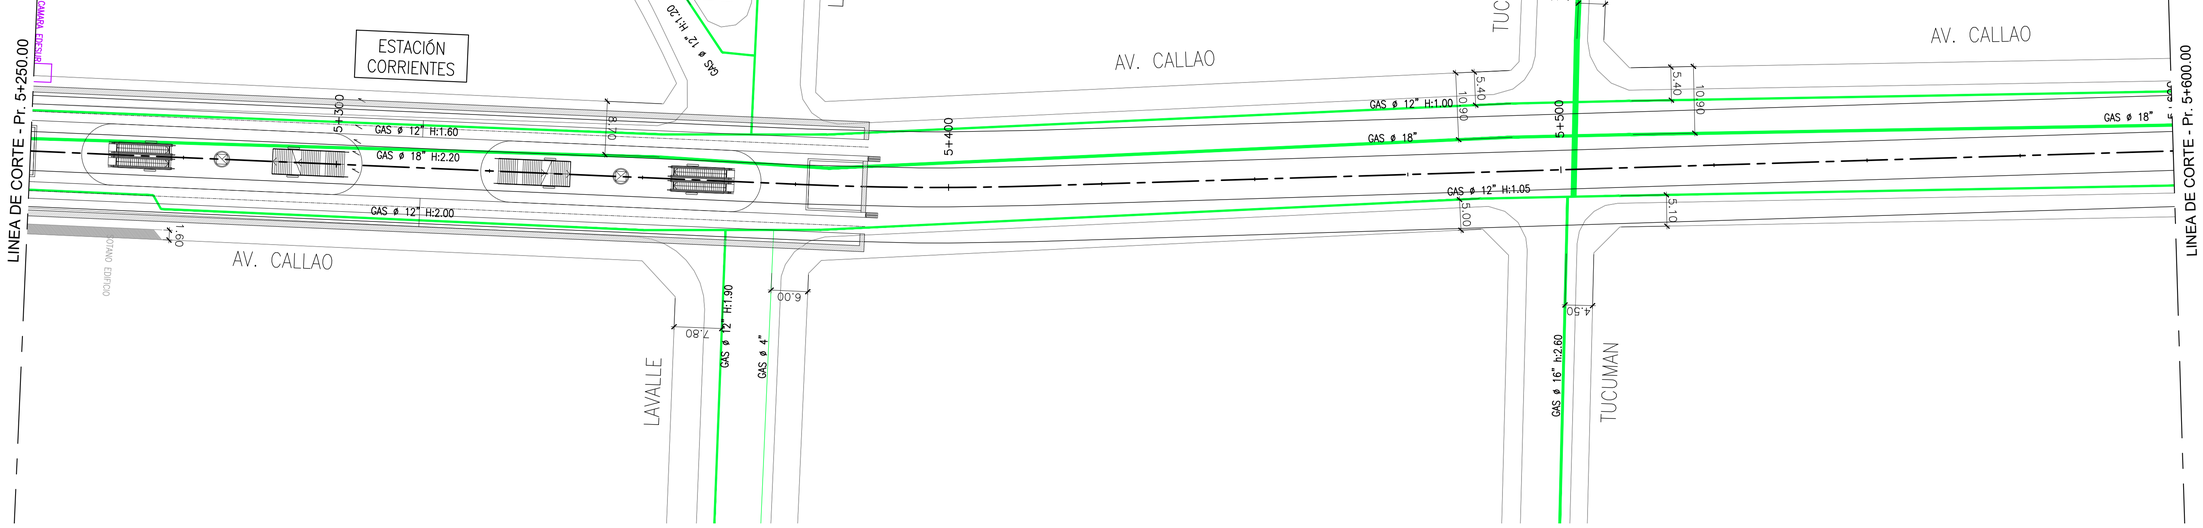

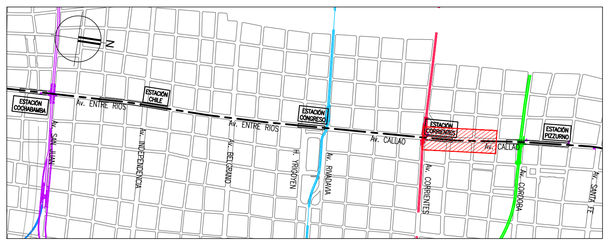

CROQUIS DE UBICACIÓN

Ing. Mariano Miculicich
DIRECTOR

REFERENCIAS

- RED CLOACAL
- RED PLUVIAL
- RED AGUA
- RED ELECTRICA
- RED GAS
- RED TELEFONICA
- RED FIBRA OPTICA MULTICANAL

0 10 20 30m
ESCALA 1:500

N°	DIBUJÓ	REVISÓ	APROBÓ	FECHA	DESCRIPCIÓN
0	D.B.	P.C.		SET. 2025	EMISIÓN INICIAL

REVISIONES

MINISTERIO DE INFRAESTRUCTURA

URGELL PENEDO URGELL
ARQUITECTOS LYNCH VAGO RODRIGUEZ

IATASA INGENIERIA

PROYECTO DE ARQUITECTURA E INGENIERÍA RELACIONADO A LA CONSTRUCCIÓN INTEGRAL DE LA LÍNEA F DE SUBTERRÁNEOS DE LA CIUDAD DE BUENOS AIRES

FECHA: SETIEMBRE 2025	TRAZADO DE TÚNEL
ESCALA: HORIZ: 1:500 VERTICAL: -	INTERFERENCIAS TRAMO 1
	PLANIMETRÍA GENERAL - PROG. 5+250 A 5+600
FORMATO A1 / HOJA: 16/18	PLANO Nº: LF-GL-T01-INT-PL-016 / REV.: 0

IF-2026-20223041-GCABA-APRA

19/9/2025 16:17 p. m.
LF-GL-T01-INT-PL-001a018_0.dwg

INTERFERENCIAS
SERVICOS CLOACALES, PLUVIALES, AGUA CORRIENTE
ESCALA 1:500

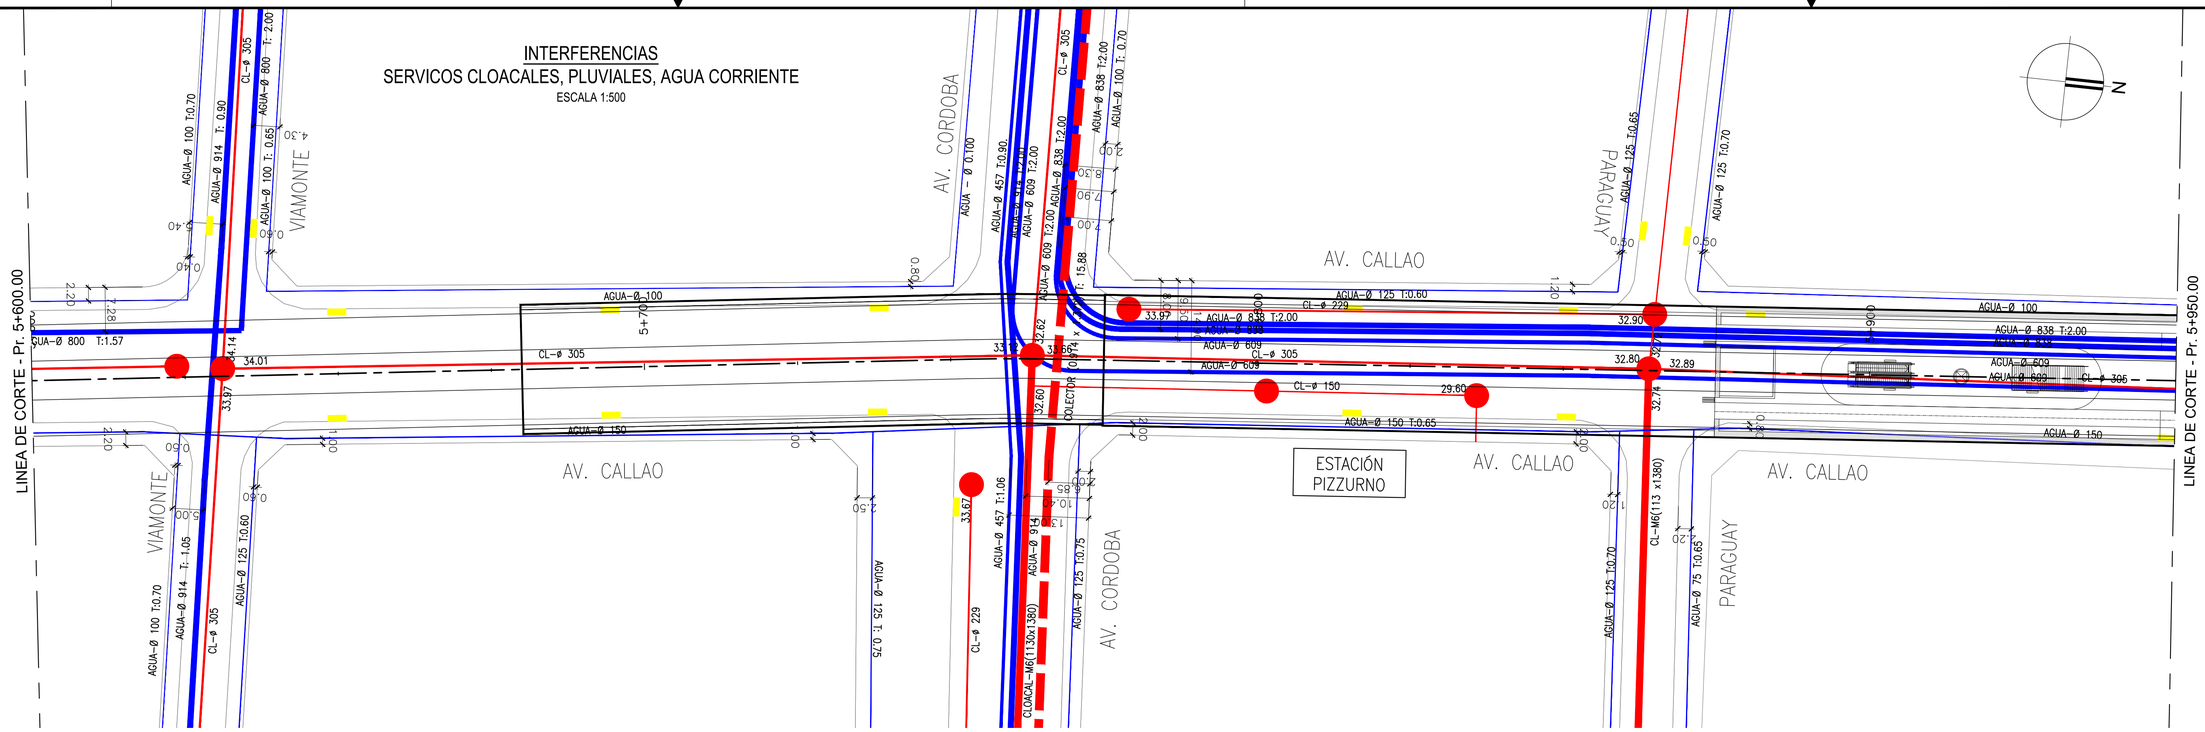

INTERFERENCIAS
GAS, TELEFONIA, ELECTRICIDAD, FIBRA OPTICA
ESCALA 1:500

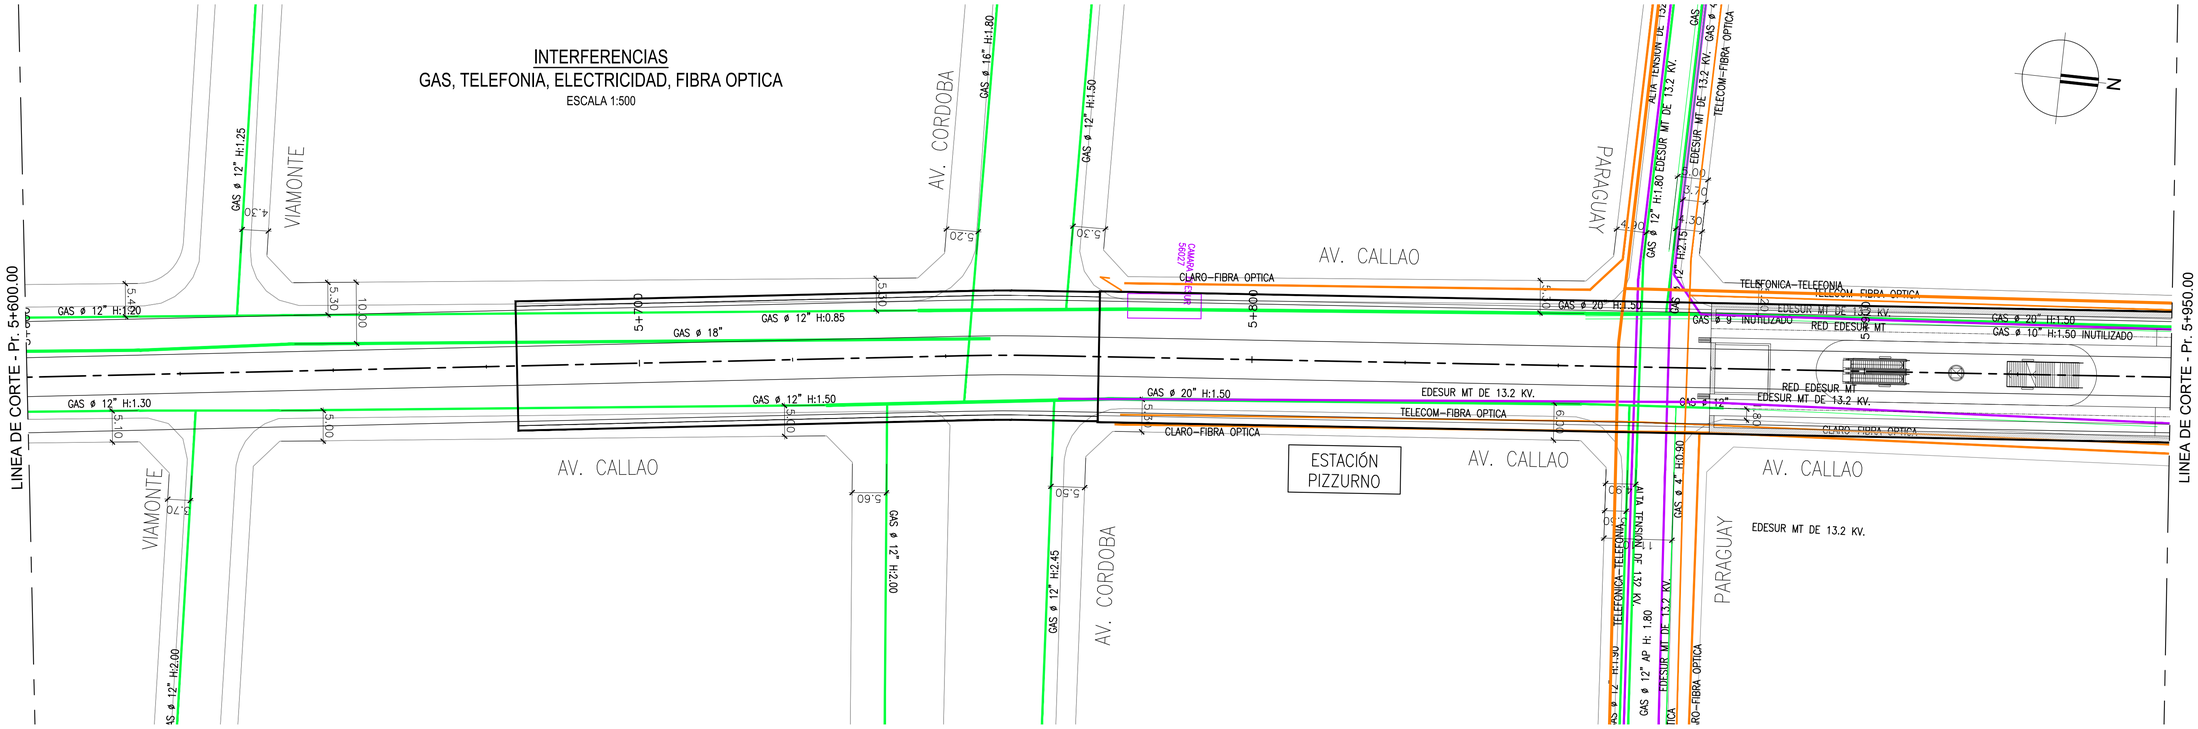

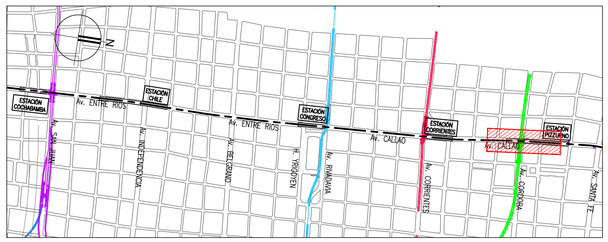

CROQUIS DE UBICACIÓN

REFERENCIAS
- RED CLOACAL
- RED PLUVIAL
- RED AGUA
- RED ELECTRICA
- RED GAS
- RED TELEFONICA
- RED FIBRA OPTICA MULTICANAL

0 10 20 30m
ESCALA 1:500

Ing. Mariano Miculicich
DIRECTOR

N°	DIBUJÓ	REVISÓ	APROBÓ	FECHA	DESCRIPCIÓN
0	D.B.	P.C.		SET. 2025	EMISIÓN INICIAL

REVISIONES

MINISTERIO DE INFRAESTRUCTURA

URGELL PENEDO URGELL
ARQUITECTOS LYNCH VAGO RODRIGUEZ

PROYECTO DE ARQUITECTURA E INGENIERÍA RELACIONADO A LA CONSTRUCCIÓN INTEGRAL DE LA LÍNEA F DE SUBTERRÁNEOS DE LA CIUDAD DE BUENOS AIRES

FECHA: SETIEMBRE 2025	TRAZADO DE TÚNEL
ESCALA: HORIZ: 1:500 VERTICAL: -	INTERFERENCIAS TRAMO 1
FORMATO A1	HOJA: 17/18
	PLANIMETRÍA GENERAL - PROG. 5+600 A 5+950
	IF-2026-20223041-GCABA-APRA
	PLANO Nº: LF-GL-T01-INT-PL-017
	REV.: 0

19/9/2025 16:17 p. m.
LF_GL-T01-INT-PL-001a018_0.dwg

INTERFERENCIAS
SERVICOS CLOACALES, PLUVIALES, AGUA CORRIENTE
ESCALA 1:500

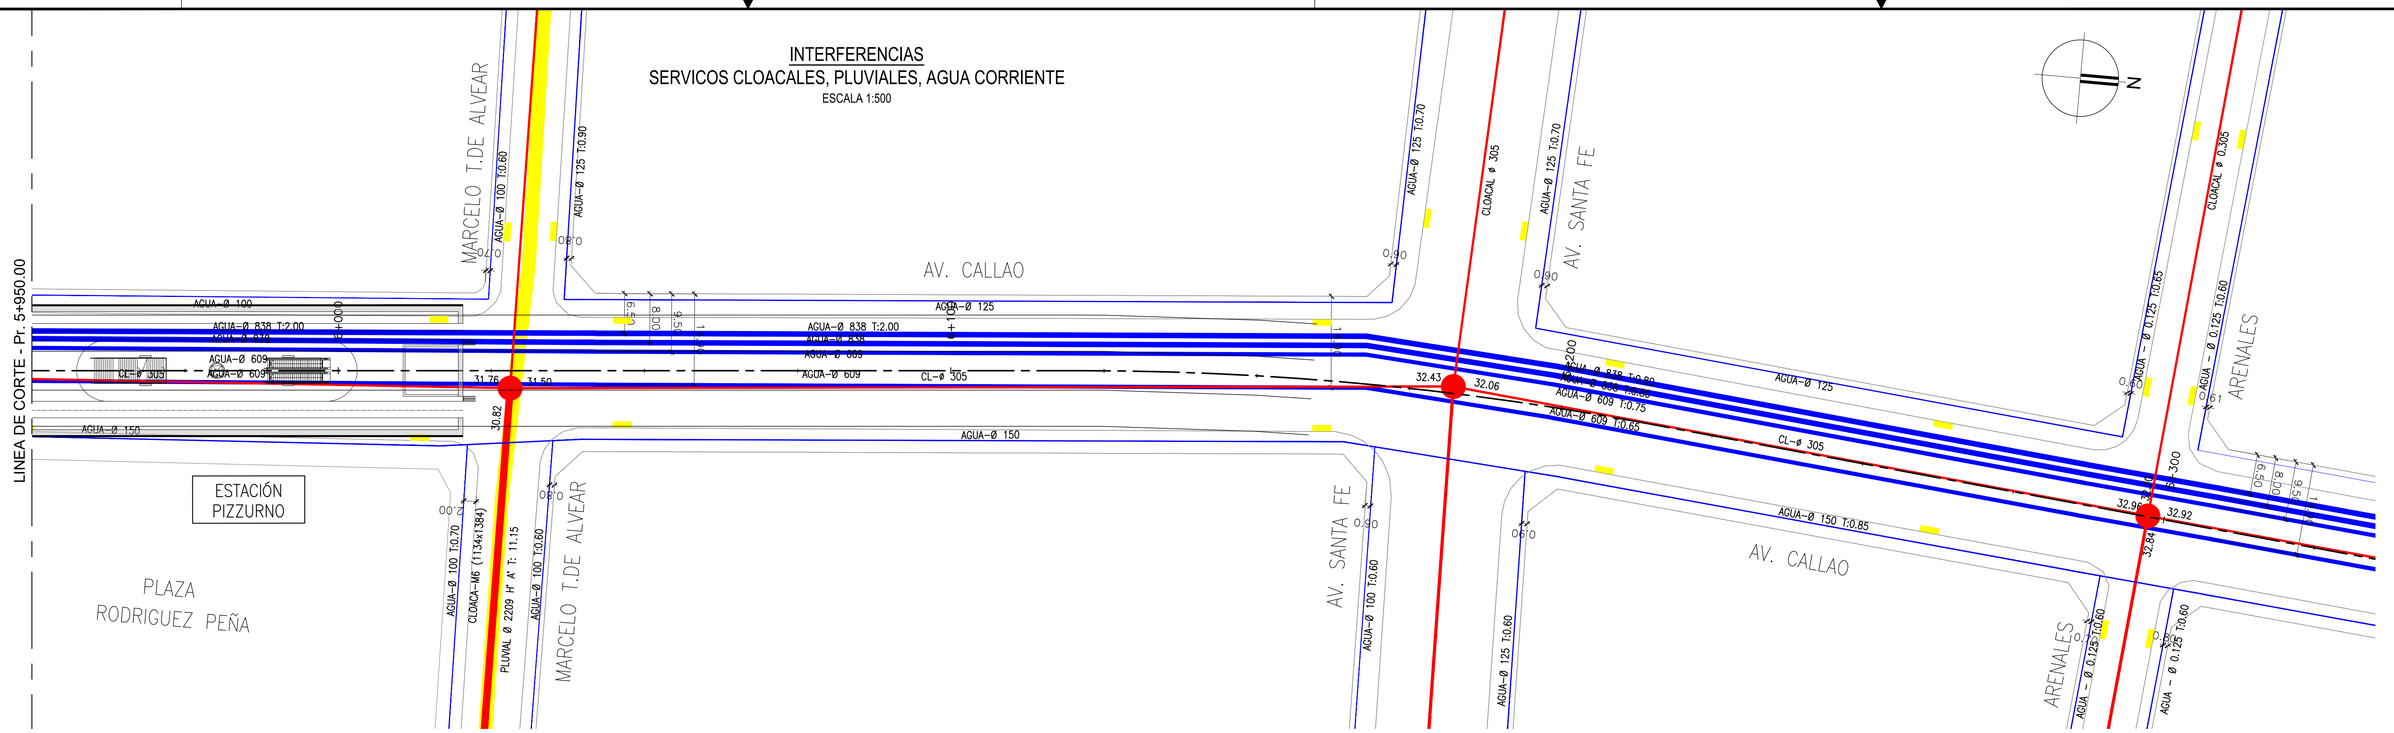

INTERFERENCIAS
GAS, TELEFONIA, ELECTRICIDAD, FIBRA OPTICA
ESCALA 1:500

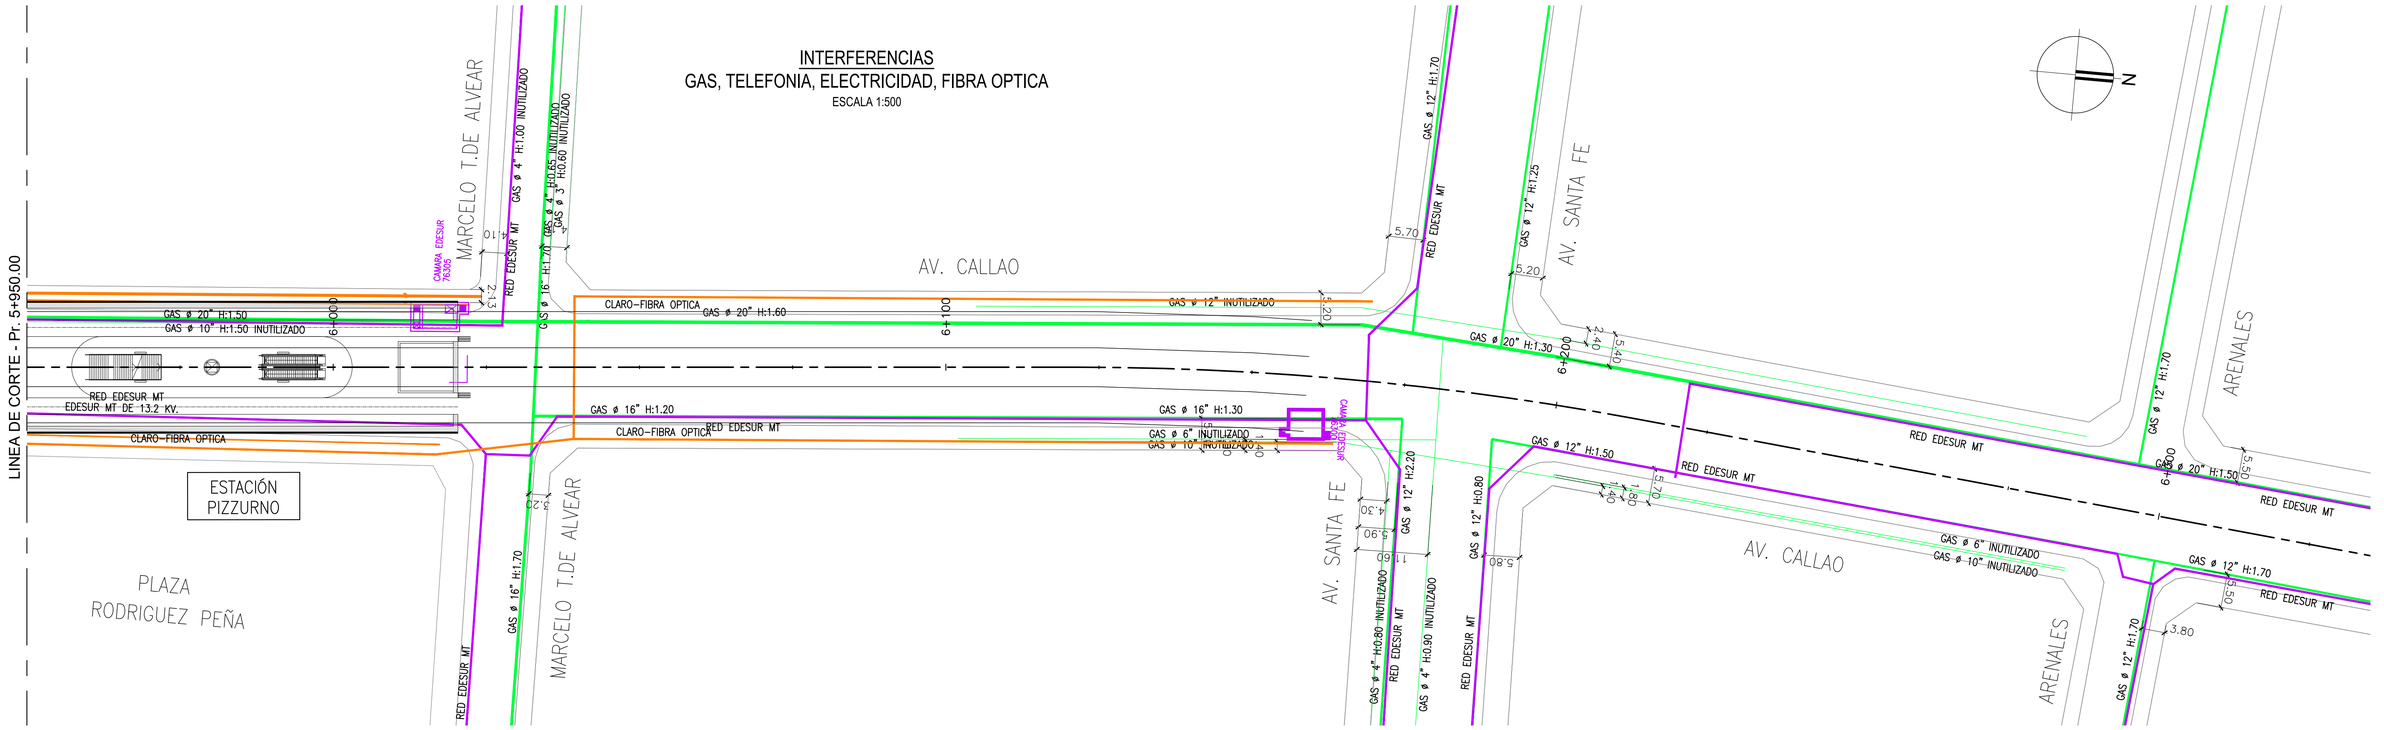

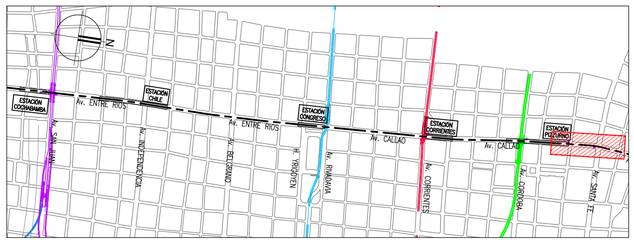

CROQUIS DE UBICACIÓN

REFERENCIAS

- RED CLOACAL
- RED PLUVIAL
- RED AGUA
- RED ELECTRICA
- RED GAS
- RED TELEFONICA
- RED FIBRA OPTICA MULTICANAL

0 10 20 30m
ESCALA 1:500

Ing. Mariano Miculicich
DIRECTOR

N°	DIBUJÓ	REVISÓ	APROBÓ	FECHA	DESCRIPCIÓN
0	D.B.	P.C.		SET. 2025	EMISIÓN INICIAL

REVISIONES

MINISTERIO DE INFRAESTRUCTURA

URGELL PENEDO URGELL
ARQUITECTOS LYNCH VAGO RODRIGUEZ

PROYECTO DE ARQUITECTURA E INGENIERÍA RELACIONADO A LA CONSTRUCCIÓN INTEGRAL DE LA LÍNEA F DE SUBTERRÁNEOS DE LA CIUDAD DE BUENOS AIRES

FECHA: SETIEMBRE 2025	TRAZADO DE TÚNEL
ESCALA: HORIZ: 1:500 VERTICAL: -	INTERFERENCIAS TRAMO 1
	PLANIMETRÍA GENERAL - PROG. 5+950 A 6+300
FORMATO A1 / HOJA: 18/18	PLANO Nº: LF-GL-T01-INT-PL-018 / REV.: 0

IF-2026-20223941-GCABA-APRA

19/9/2025 16:17 p. m.
LF-GL-T01-INT-PL-001-018_0.dwg

INTERFERENCIAS
SERVICOS CLOACALES, PLUVIALES, AGUA CORRIENTE
ESCALA 1:500

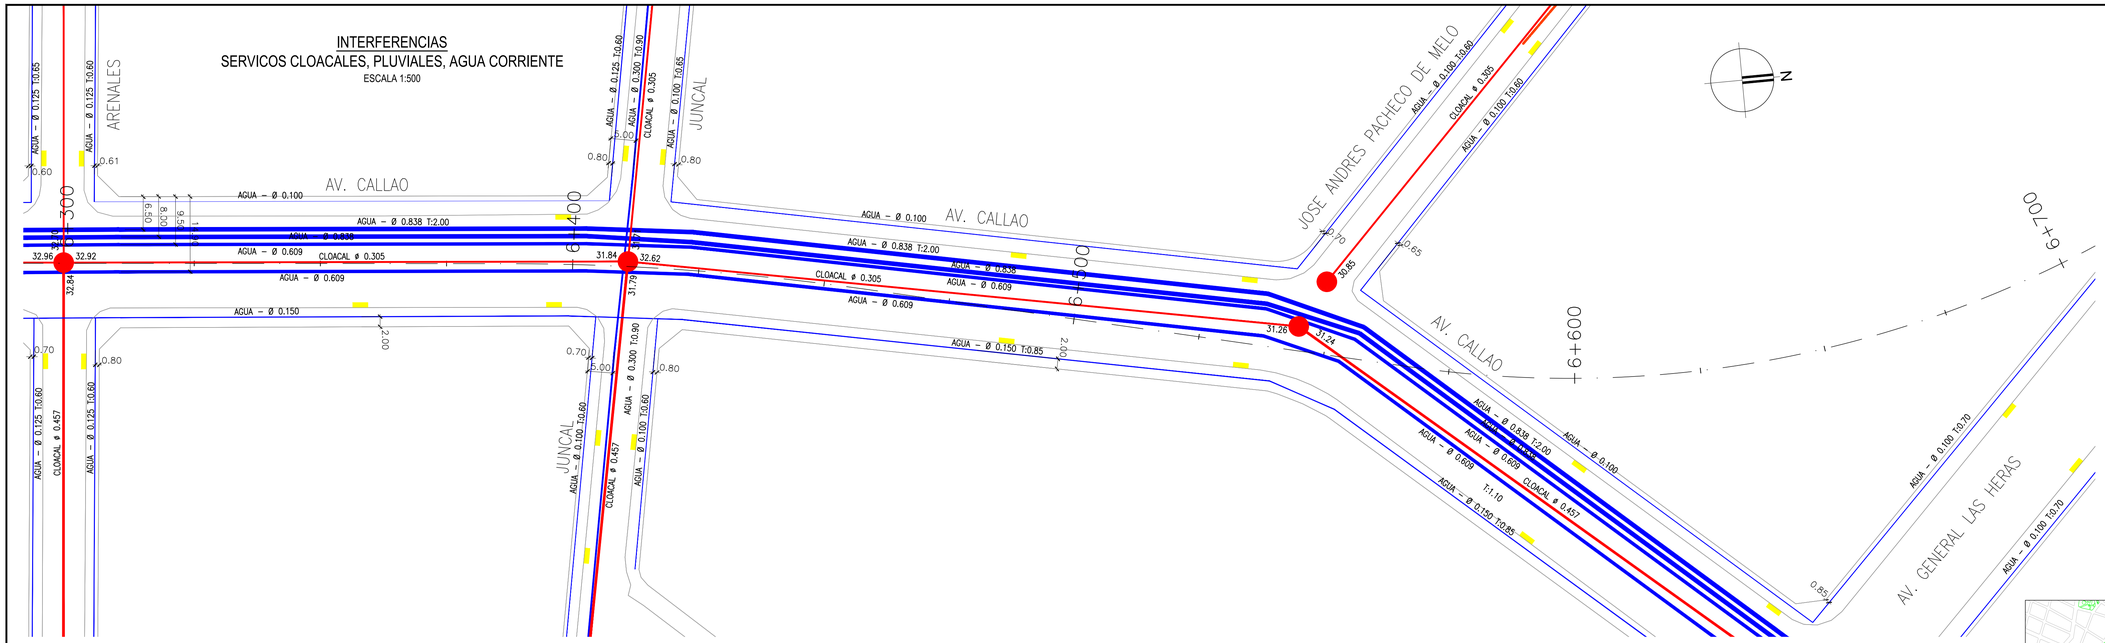

INTERFERENCIAS
GAS, TELEFONIA, ELECTRICIDAD, FIBRA OPTICA
ESCALA 1:500

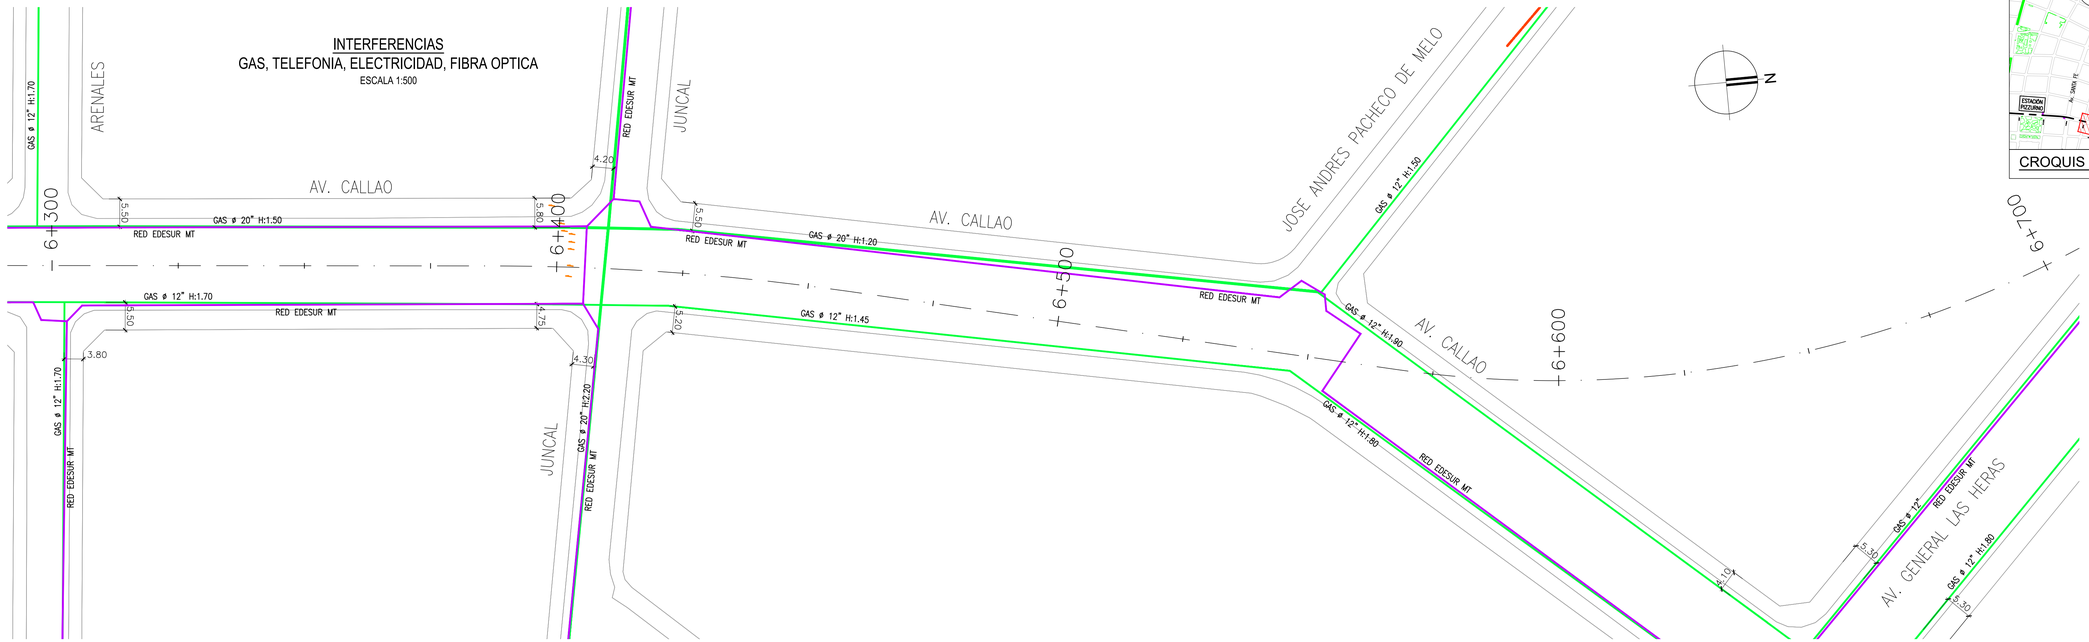

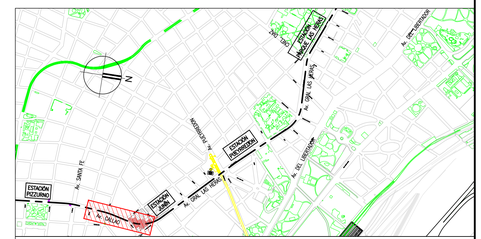
ESTACION RETIRO
ESTACION RETIRO
ESTACION RETIRO
ESTACION RETIRO
AV. DEL LIBERTADOR
AV. SAN MARTIN
AV. CRAMER
AV. ALVEAR
AV. DELLEPIANE
AV. DELLEPIANE
AV. DEL LIBERTADOR
AV. DEL LIBERTADOR
AV. DEL LIBERTADOR

INTERFERENCIAS
SERVICIOS CLOACALES, PLUVIALES, AGUA CORRIENTE
ESCALA 1:500

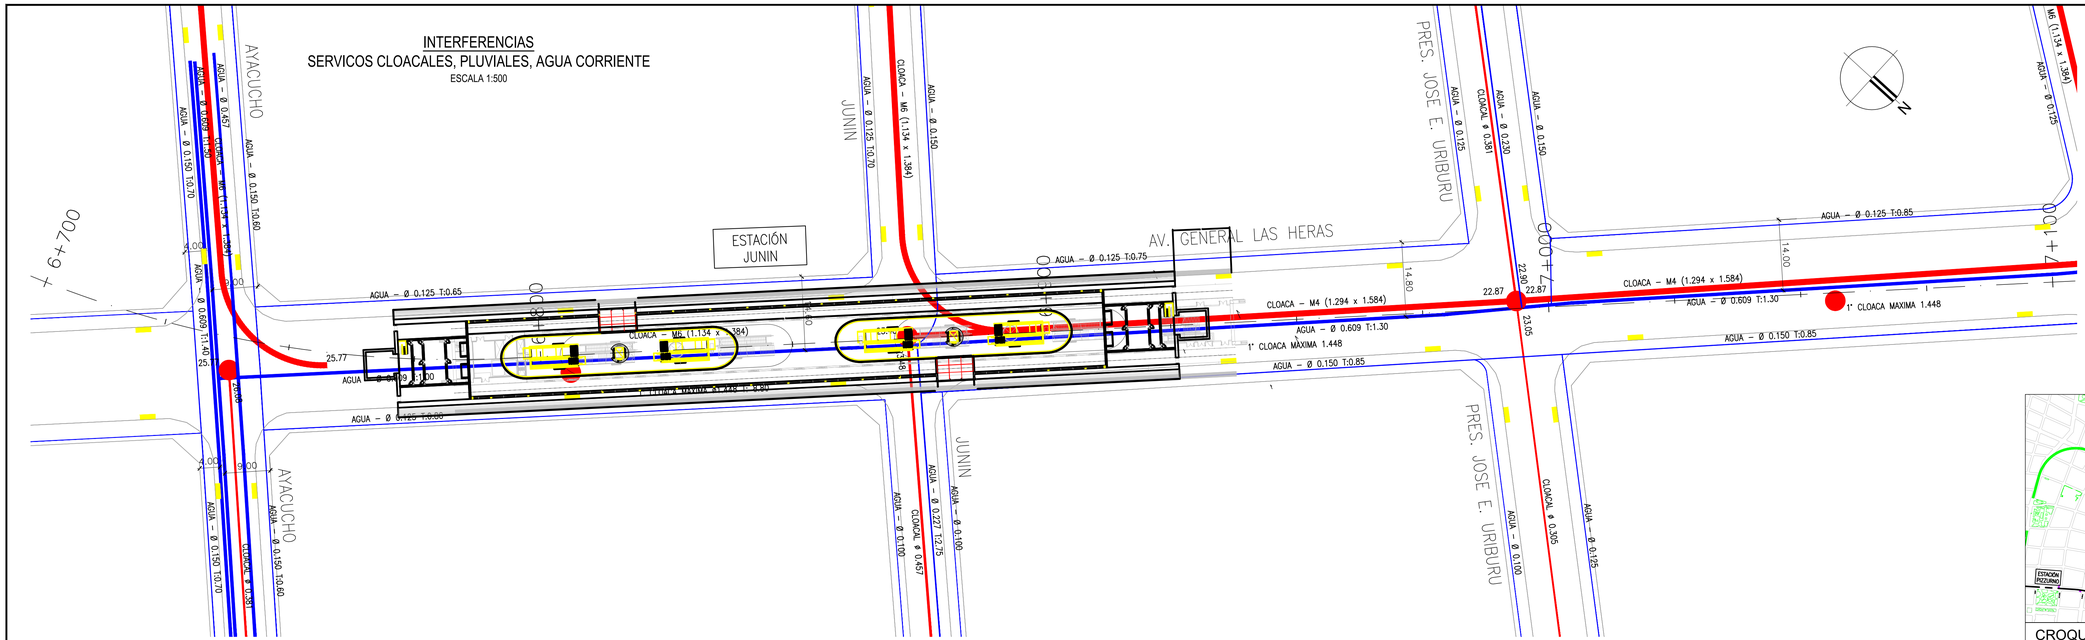

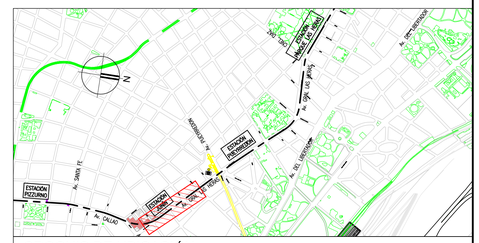

CROQUIS DE UBICACIÓN

INTERFERENCIAS
GAS, TELEFONIA, ELECTRICIDAD, FIBRA OPTICA
ESCALA 1:500

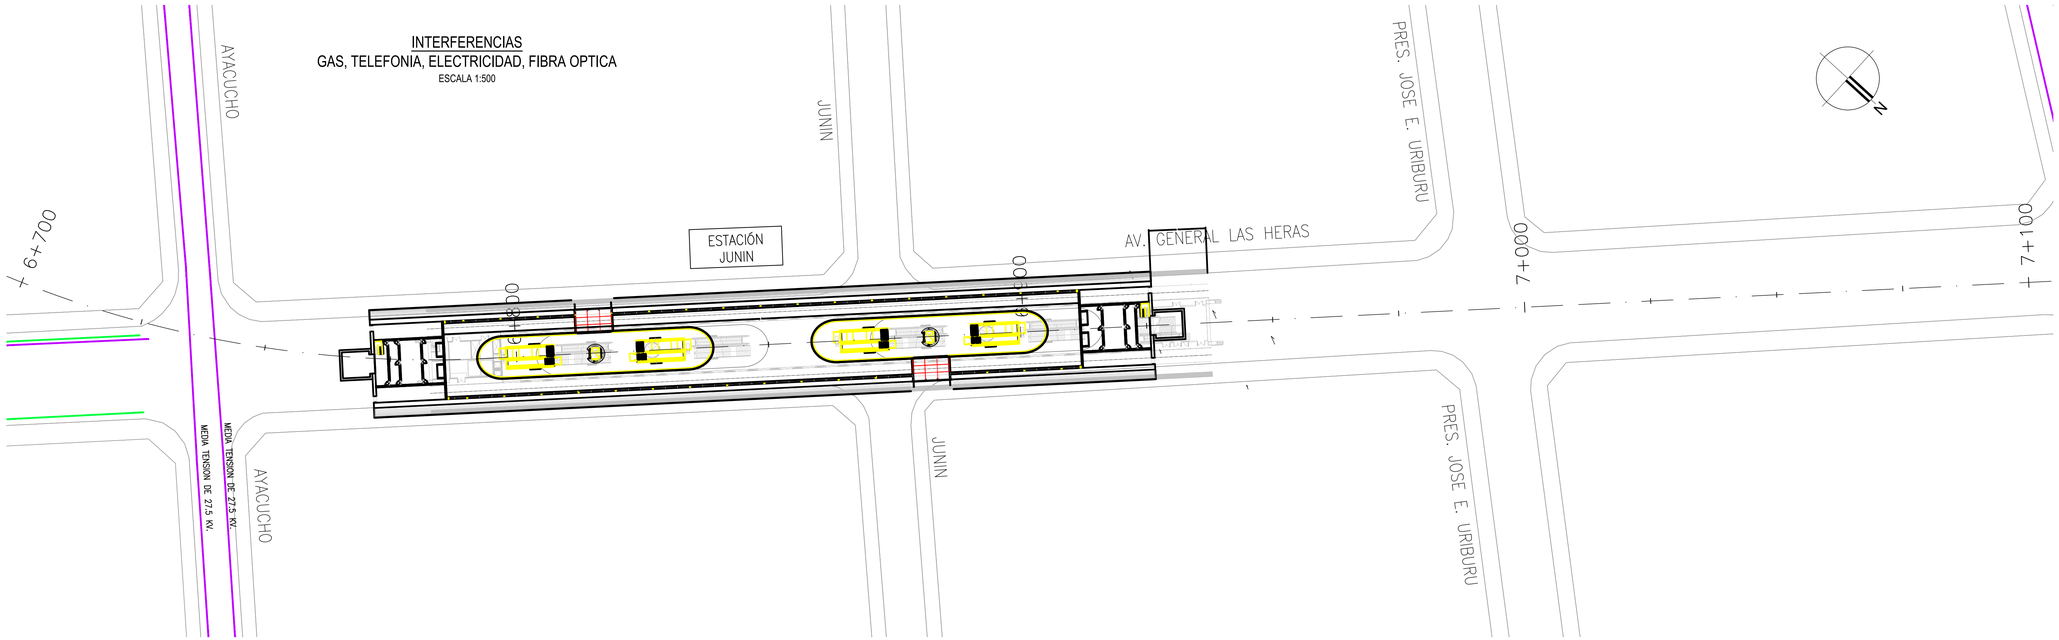

REFERENCIAS:
- RED CLOACAL
- RED PLUVIAL
- RED AGUA
- RED ELECTRICA
- RED GAS
- RED TELEFONICA
- RED FIBRA OPTICA MULTICANAL

NOTAS:
1- SISTEMA DE COORDENADAS DE LA CIUDAD DE BUENOS AIRES.
2- TODAS LAS MEDIDAS ESTÁN EXPRESADAS EN METROS, SALVO INDICACIÓN CONTRARIA

0 10 20 30m
ESCALA 1:500

NOTAS: EL PRESENTE PLANO ES INDICATIVO. LA CONTRATISTA CONFECCIONARA LOS PLANOS DE DETALLE DEFINITIVO QUE DEBERAN SER APROBADOS POR LA D.G.C.SIP.Q.Y.U.A. INSPECCION DE OBRA. EL PLANO PRESENTADO POR LA CONTRATISTA DEBERA EN UN TODO DE ACUERDO CON LA NORMATIVA VIGENTE. TODAS LAS MEDIDAS Y NIVELES SE VERIFICARAN EN OBRA POR EL CONTRATISTA. TODOS LOS DETALLES CONSTRUCTIVOS SERAN COORDINADOS Y CONFIRMADOS EN OBRA

PLANO NO APTO PARA CONSTRUCCION.

Ing. Mariano Miculicich
DIRECTOR

MODIFICACIONES:

REVISION	FECHA	DESCRIPCION
0	19/09/2025	EMISION INICIAL
1	11/12/2025	AJUSTE DE PROYECTO

Gobierno de la Ciudad de Buenos Aires

MINISTERIO DE INFRAESTRUCTURA
SUBSECRETARIA DE PROYECTOS Y OBRAS
DIRECCION GENERAL DE PROYECTOS

DGPRO

Obra: LÍNEA F				IF-2026-20223041-GCABA-APRA	Plano N°
Plano: TRAZADO DE TÚNEL - INTERFERENCIAS - PROG. 6+700 A 7+100				LF-GL-T02-INT-PL-002	002
Fecha: 11/12/2025	Eq. de Proyecto: UPU-ATEC-IATASA	Dibujó: D.B.	Revisó: P.C.	Escala: 1:500	

4/2/2026 12:49
Ver+estaciones.dwg

INTERFERENCIAS
SERVICOS CLOACALES, PLUVIALES, AGUA CORRIENTE
ESCALA 1:500

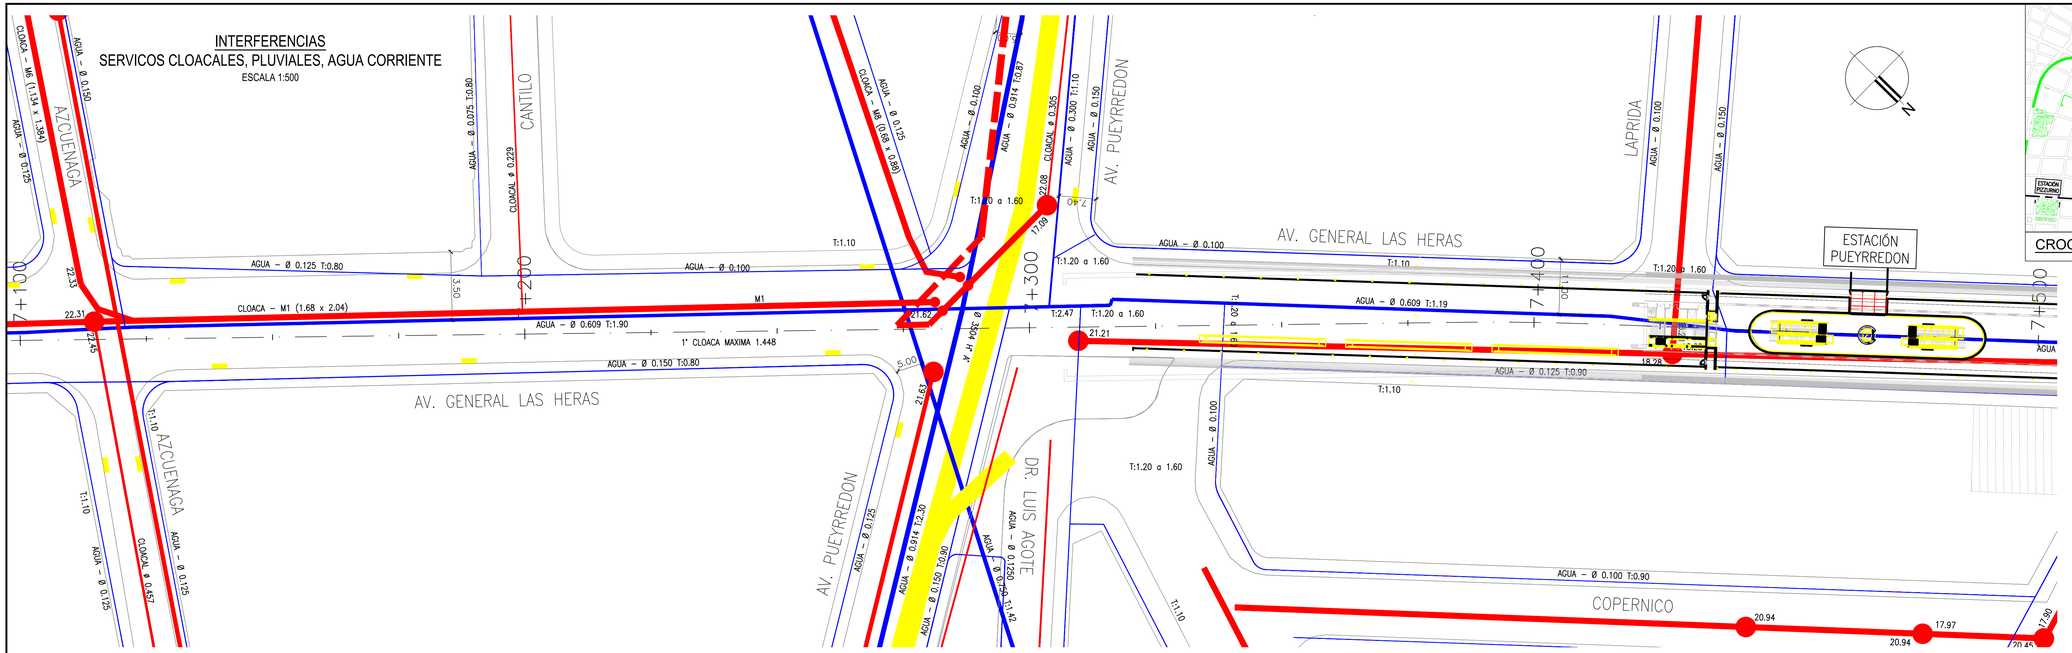

CROQUIS DE UBICACIÓN

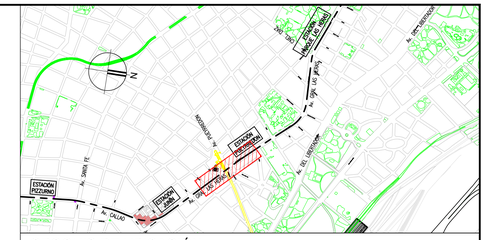

INTERFERENCIAS
GAS, TELEFONIA, ELECTRICIDAD, FIBRA OPTICA
ESCALA 1:500

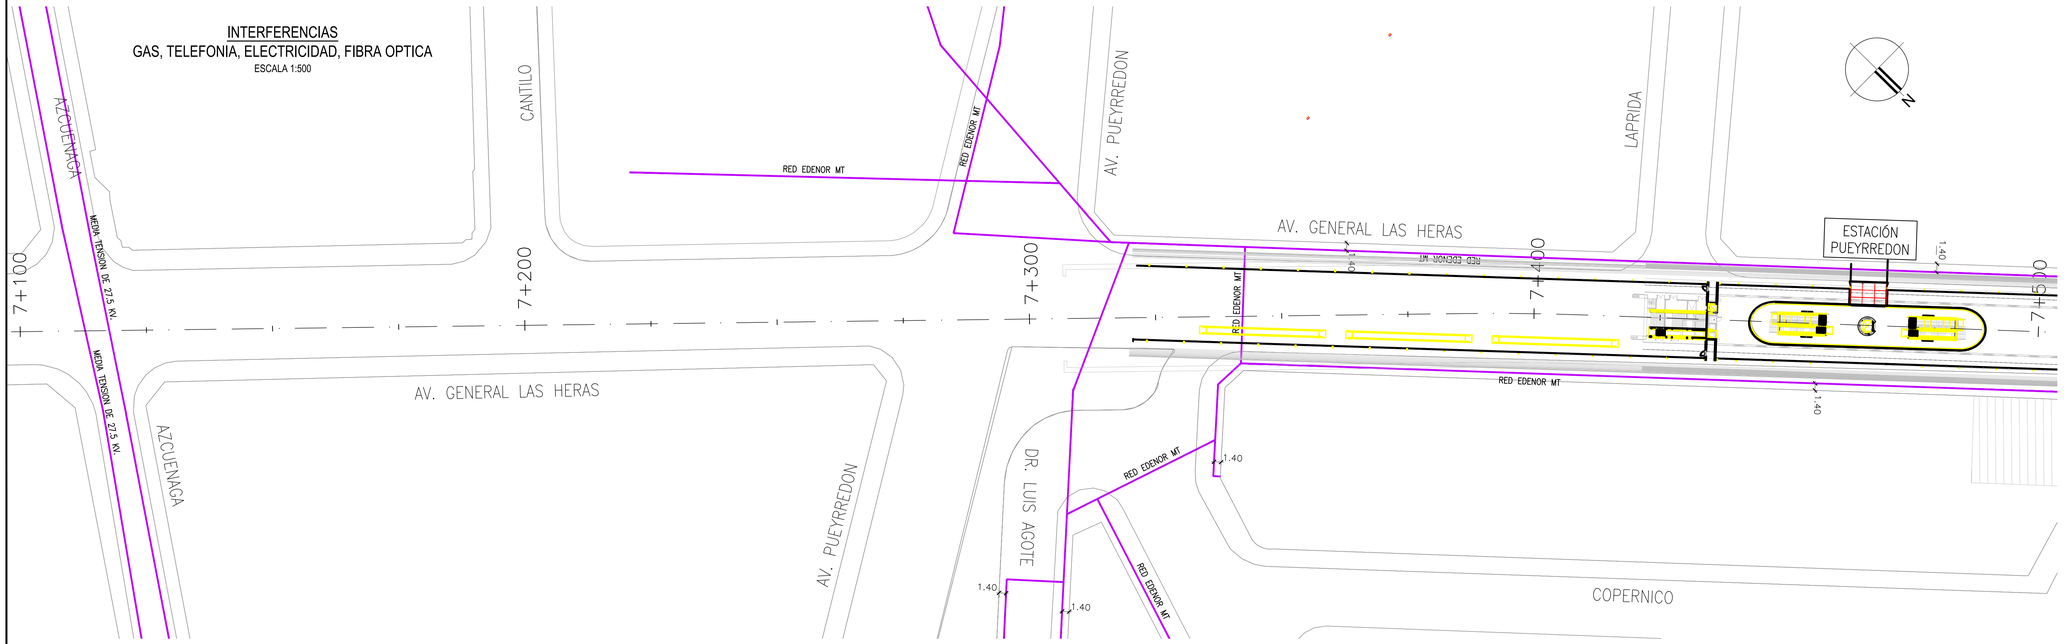

REFERENCIAS:
- RED CLOACAL
- RED PLUVIAL
- RED AGUA
- RED ELECTRICA
- RED GAS
- RED TELEFONICA
- RED FIBRA OPTICA MULTICANAL

NOTAS:
1- SISTEMA DE COORDENADAS DE LA CIUDAD DE BUENOS AIRES.
2- TODAS LAS MEDIDAS ESTÁN EXPRESADAS EN METROS, SALVO INDICACIÓN CONTRARIA

0 10 20 30m
ESCALA 1:500

NOTAS: EL PRESENTE PLANO ES INDICATIVO. LA CONTRATISTA CONFECCIONARA LOS PLANOS DE DETALLE DEFINITIVO, QUE DEBERAN SER APROBADOS POR LA D.G.S.M. Y LA D.G.I.M. PREVIO A LA EJECUCION DE LAS OBRAS. TODAS LAS MEDIDAS SON EN METROS Y ESTAN REFERIDAS A UN PLANO EN ESCALA 1:500 DE ACUERDO CON LA NORMATIVA VIGENTE.
TODAS LAS MEDIDAS Y DETALLES DE INTERFERENCIAS EN OBRA POR EL CONTRATISTA.
TODOS LOS DETALLES CONSTRUCTIVOS SERAN COORDINADOS Y CONFIRMADOS EN OBRA

PLANO NO APTO PARA CONSTRUCCION.

Ing. Mariano Miculicich
DIRECTOR

MODIFICACIONES:

REVISION	FECHA	DESCRIPCION
0	19/09/2025	EMISION INICIAL
1	11/12/2025	AJUSTE DE PROYECTO

MINISTERIO DE INFRAESTRUCTURA
SUBSECRETARIA DE PROYECTOS Y OBRAS
DIRECCION GENERAL DE PROYECTOS

DGPRO

Obra: LINEA F					Plano N° IF-2026-20223041-GCABA-APRA
Plano: TRAZADO DE TÚNEL - INTERFERENCIAS - PROG. 7+100 A 7+500					LF-GL-T02-INT-PL-003
Fecha: 11/12/2025	Eq. de Proyecto: UPU-ATEC-IATASA	Dibujó: D.B.	Revisó: P.C.	Escala: 1:500	003

4/12/2026 12:49
Xref-Interferencias.dwg

INTERFERENCIAS
SERVICOS CLOACALES, PLUVIALES, AGUA CORRIENTE
ESCALA 1:500

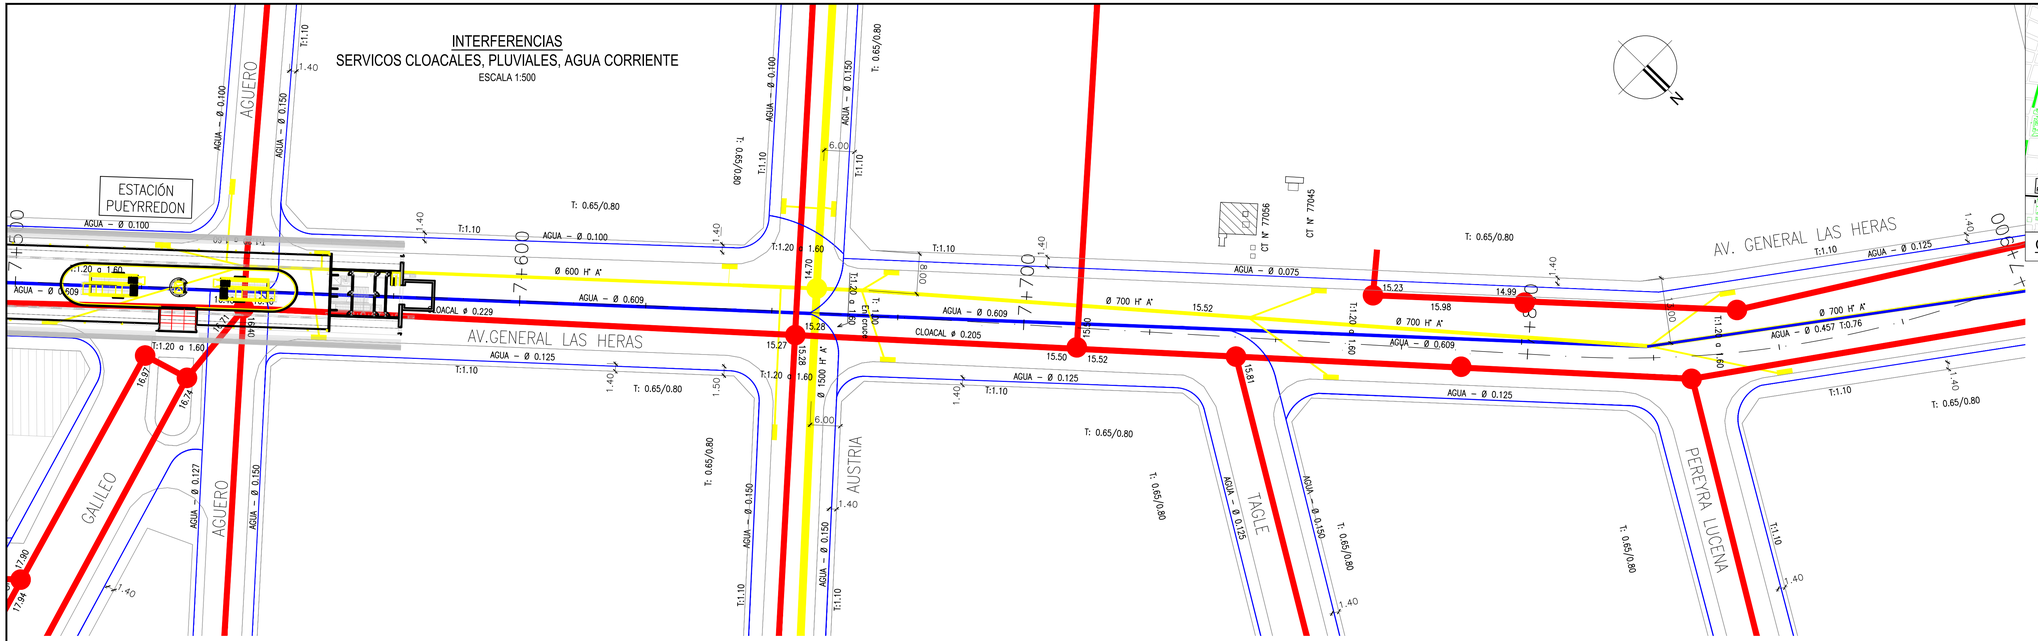

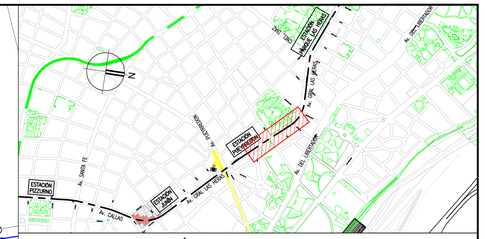

CROQUIS DE UBICACIÓN

INTERFERENCIAS
GAS, TELEFONIA, ELECTRICIDAD, FIBRA OPTICA
ESCALA 1:500

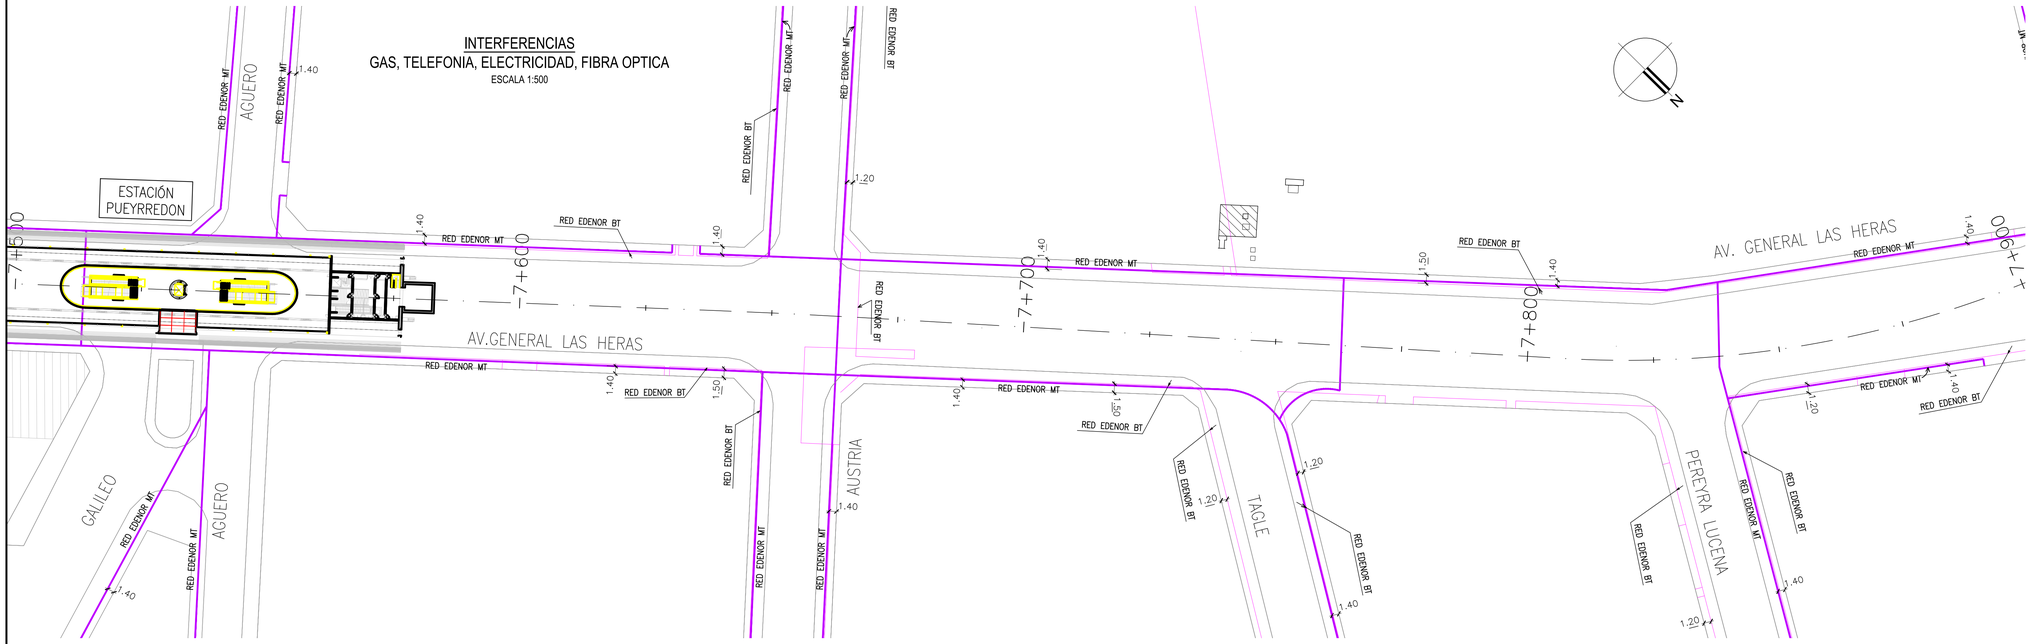

REFERENCIAS:
- RED CLOACAL
- RED PLUVIAL
- RED AGUA
- RED ELECTRICA
- RED GAS
- RED TELEFONICA
- RED FIBRA OPTICA MULTICANAL

NOTAS:
1- SISTEMA DE COORDENADAS DE LA CIUDAD DE BUENOS AIRES.
2- TODAS LAS MEDIDAS ESTÁN EXPRESADAS EN METROS, SALVO INDICACIÓN CONTRARIA

0 10 20 30m
ESCALA 1:500

NOTAS: EL PRESENTE PLANO ES INDICATIVO. LA CONTRATISTA CONFECCIONARA LOS PLANOS DE DETALLE DEFINITIVO QUE DEBERAN SER APROBADOS POR LA D.G.C.SAP.U Y LA INSPECCION DE OBRA. EL PLANO PRESENTADO POR LA CONTRATISTA DEBERA EN UN TODO DE ACUERDO CON LA NORMATIVA VIGENTE. TODAS LAS MEDIDAS Y NIVELES SE VERIFICARAN EN OBRA POR EL CONTRATISTA. TODOS LOS DETALLES CONSTRUCTIVOS SERAN COORDINADOS Y CONFIRMADOS EN OBRA

PLANO NO APTO PARA CONSTRUCCION.

Ing. Mariano Miculicich
DIRECTOR

MODIFICACIONES:

REVISIÓN	FECHA	DESCRIPCIÓN
0	19/09/2025	EMISIÓN INICIAL
1	11/12/2025	AJUSTE DE PROYECTO

Gobierno de la Ciudad de Buenos Aires

MINISTERIO DE INFRAESTRUCTURA
SUBSECRETARIA DE PROYECTOS Y OBRAS
DIRECCION GENERAL DE PROYECTOS

DGPRO

Obra: LÍNEA F				IF-2026-20223041-GCABA-APRA	Plano N°
Plano: TRAZADO DE TÚNEL - INTERFERENCIAS - PROG. 7+500 A 7+900				LF-GL-T02-INT-PL-004	004
Fecha: 11/12/2025	Eq. de Proyecto: UPU-ATEC-IATASA	Dibujó: D.B.	Revisó: P.C.	Escala: 1:500	

4/2/2026 12:49
\\vial-estaciones.dwg

INTERFERENCIAS
SERVICOS CLOACALES, PLUVIALES, AGUA CORRIENTE
ESCALA 1:500

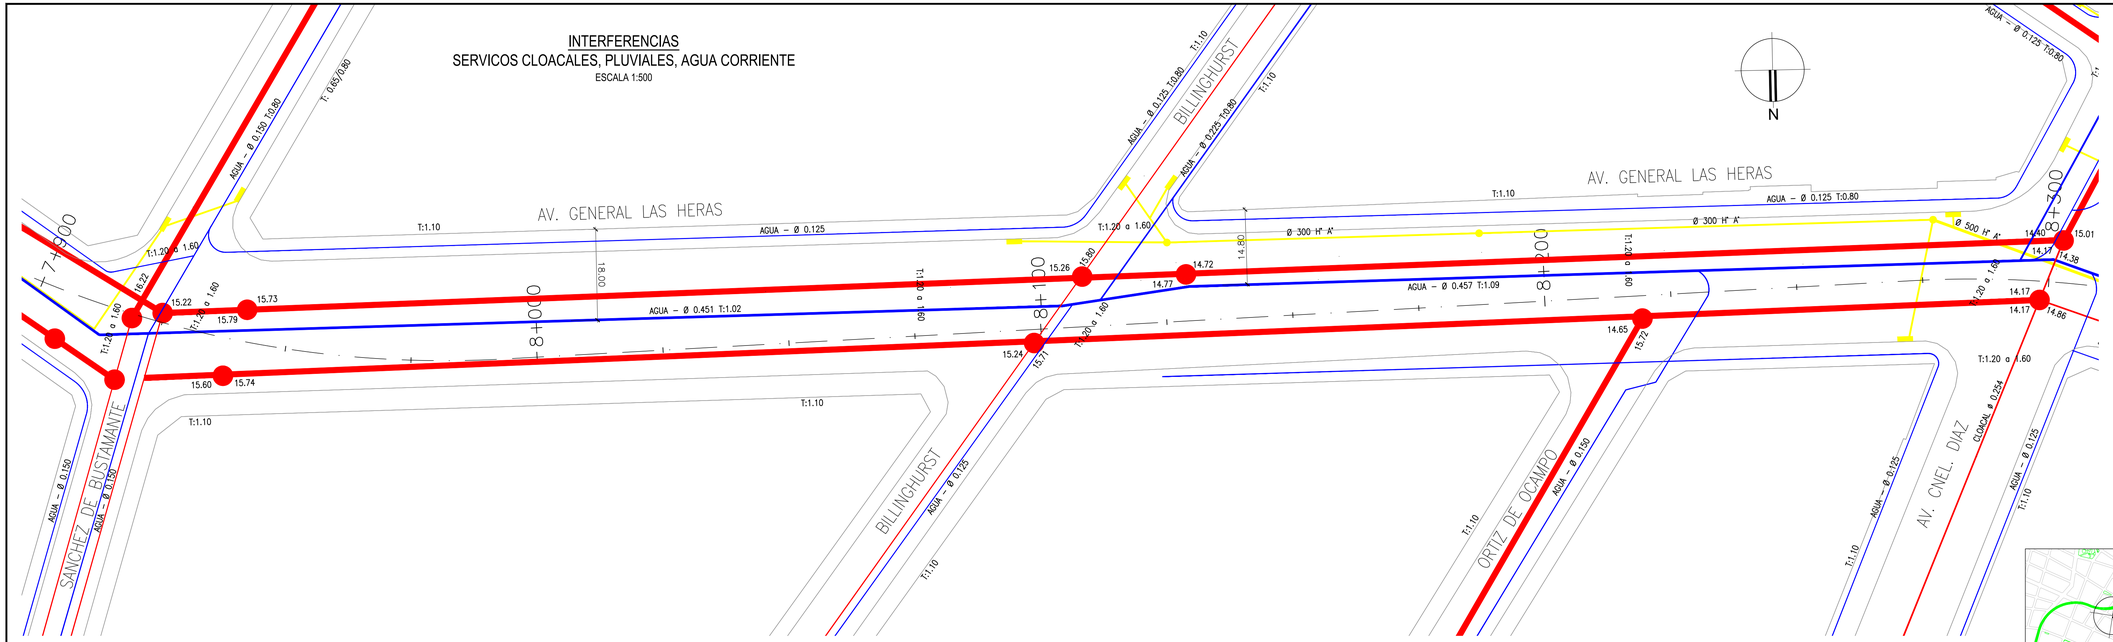

INTERFERENCIAS
GAS, TELEFONIA, ELECTRICIDAD, FIBRA OPTICA
ESCALA 1:500

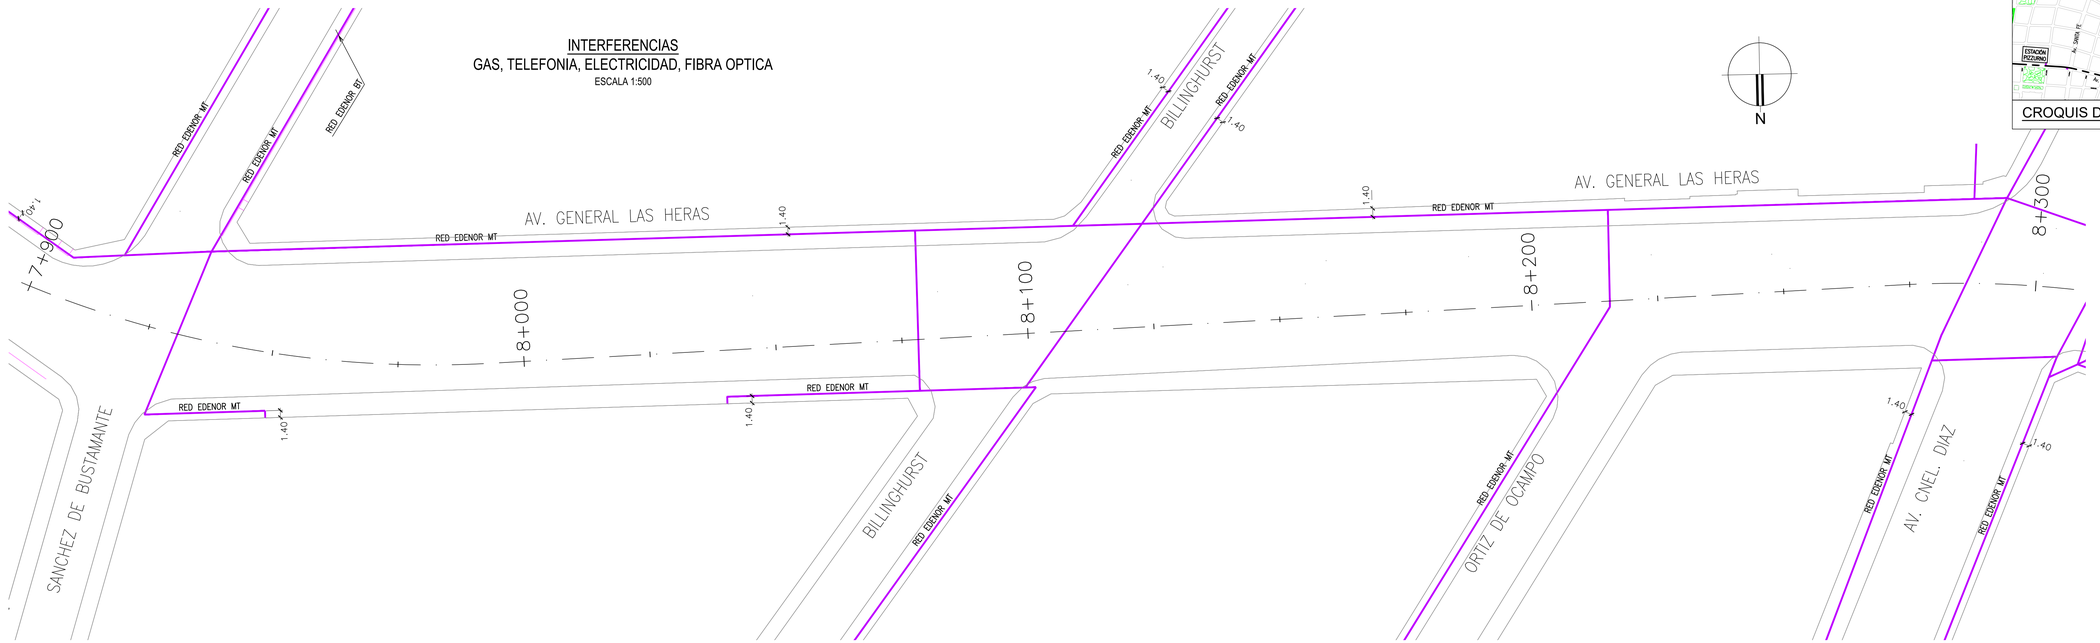

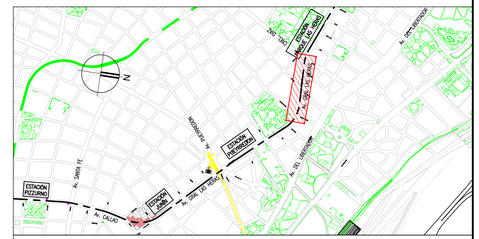

CROQUIS DE UBICACIÓN

REFERENCIAS:
- RED CLOACAL
- RED PLUVIAL
- RED AGUA
- RED ELECTRICA
- RED GAS
- RED TELEFONICA
- RED FIBRA OPTICA MULTICANAL

NOTAS:
1- SISTEMA DE COORDENADAS DE LA CIUDAD DE BUENOS AIRES.
2- TODAS LAS MEDIDAS ESTÁN EXPRESADAS EN METROS, SALVO INDICACIÓN CONTRARIA

0 10 20 30m
ESCALA 1:500

NOTAS: EL PRESENTE PLANO ES INDICATIVO. LA CONTRATISTA CONFECCIONARA LOS PLANOS DE DETALLE DEFINITIVO, QUE DEBERAN SER APROBADOS POR LA D.G.D.GIP.U Y LA INSPECCION DE OBRA. EL PLANO PRESENTADO POR LA CONTRATISTA ESTARA EN UN TODO DE ACUERDO CON LA NORMATIVA VIGENTE.
TODAS LAS MEDIDAS Y NIVELES DE VEREDA SERAN EN OBRA POR EL CONTRATISTA.
TODOS LOS DETALLES CONSTRUCTIVOS SERAN COORDINADOS Y CONFIRMADOS EN OBRA

PLANO NO APTO PARA CONSTRUCCION.

Ing. Mariano Miculicich
DIRECTOR

MODIFICACIONES:

REVISION	FECHA	DESCRIPCION
0	19/09/2025	EMISION INICIAL
1	11/12/2025	AJUSTE DE PROYECTO

Gobierno de la Ciudad de Buenos Aires

MINISTERIO DE INFRAESTRUCTURA
SUBSECRETARIA DE PROYECTOS Y OBRAS
DIRECCION GENERAL DE PROYECTOS

DGPRO

Obra: LÍNEA F
Plano: TRAZADO DE TÚNEL - INTERFERENCIAS - PROG. 7+900 A 8+300
Fecha: 11/12/2025 | Eq. de Proyecto: UPU-ATEC-IATASA | Dibujó: D.B. | Revisó: P.C. | Escala: 1:500

IF-2026-20223041-GCABA-APRA
LF-GL-T02-INT-PL-005
Plano N° 005

4/12/2026 12:49
\\ref-esto\cons.dwg

INTERFERENCIAS
SERVICOS CLOACALES, PLUVIALES, AGUA CORRIENTE
ESCALA 1:500

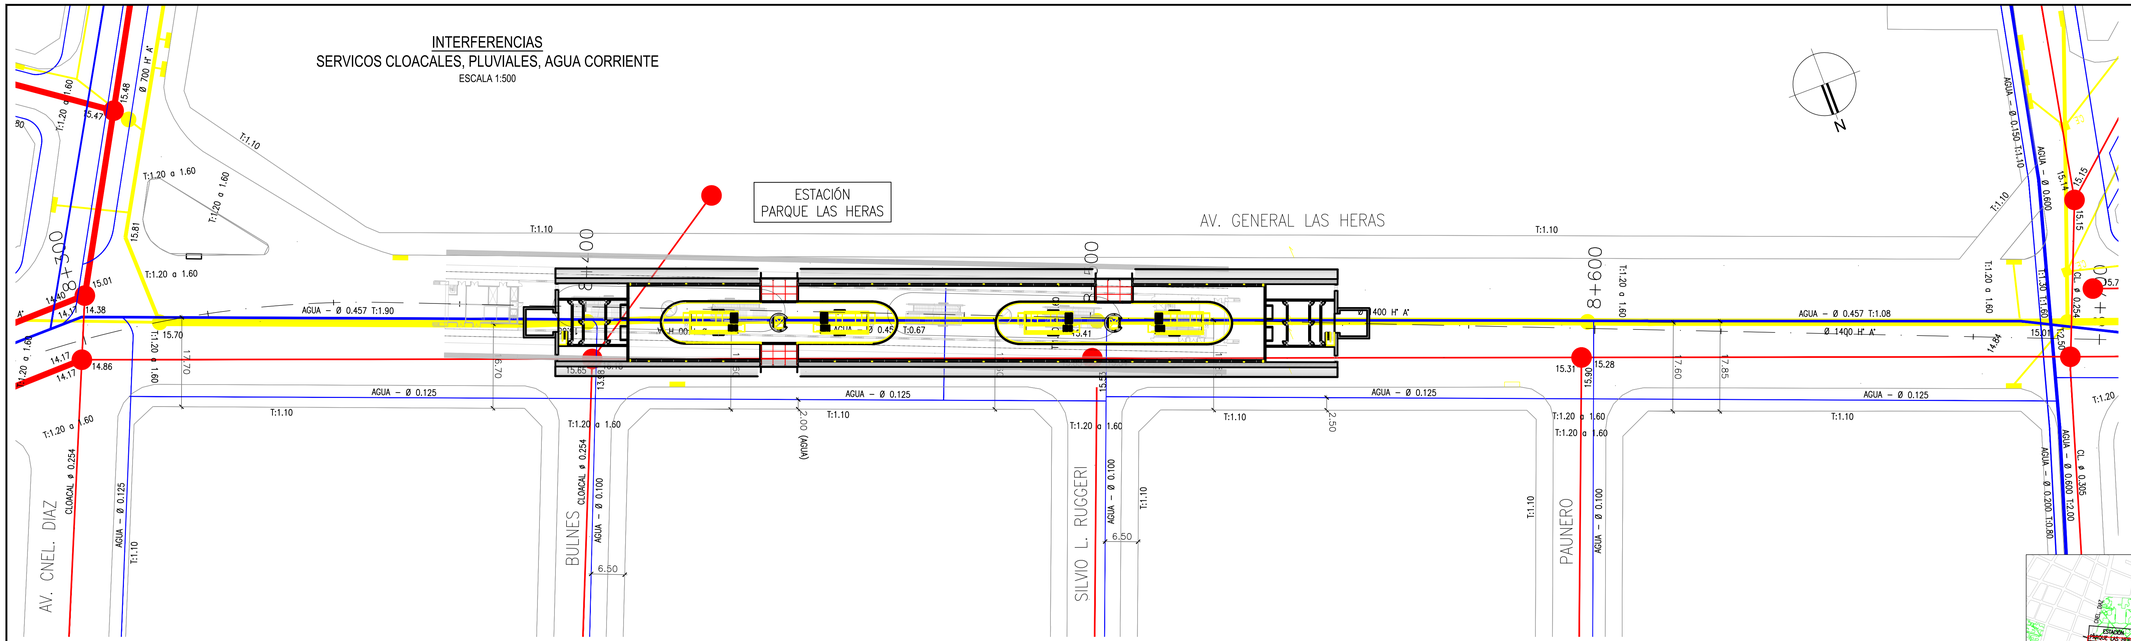

INTERFERENCIAS
GAS, TELEFONIA, ELECTRICIDAD, FIBRA OPTICA
ESCALA 1:500

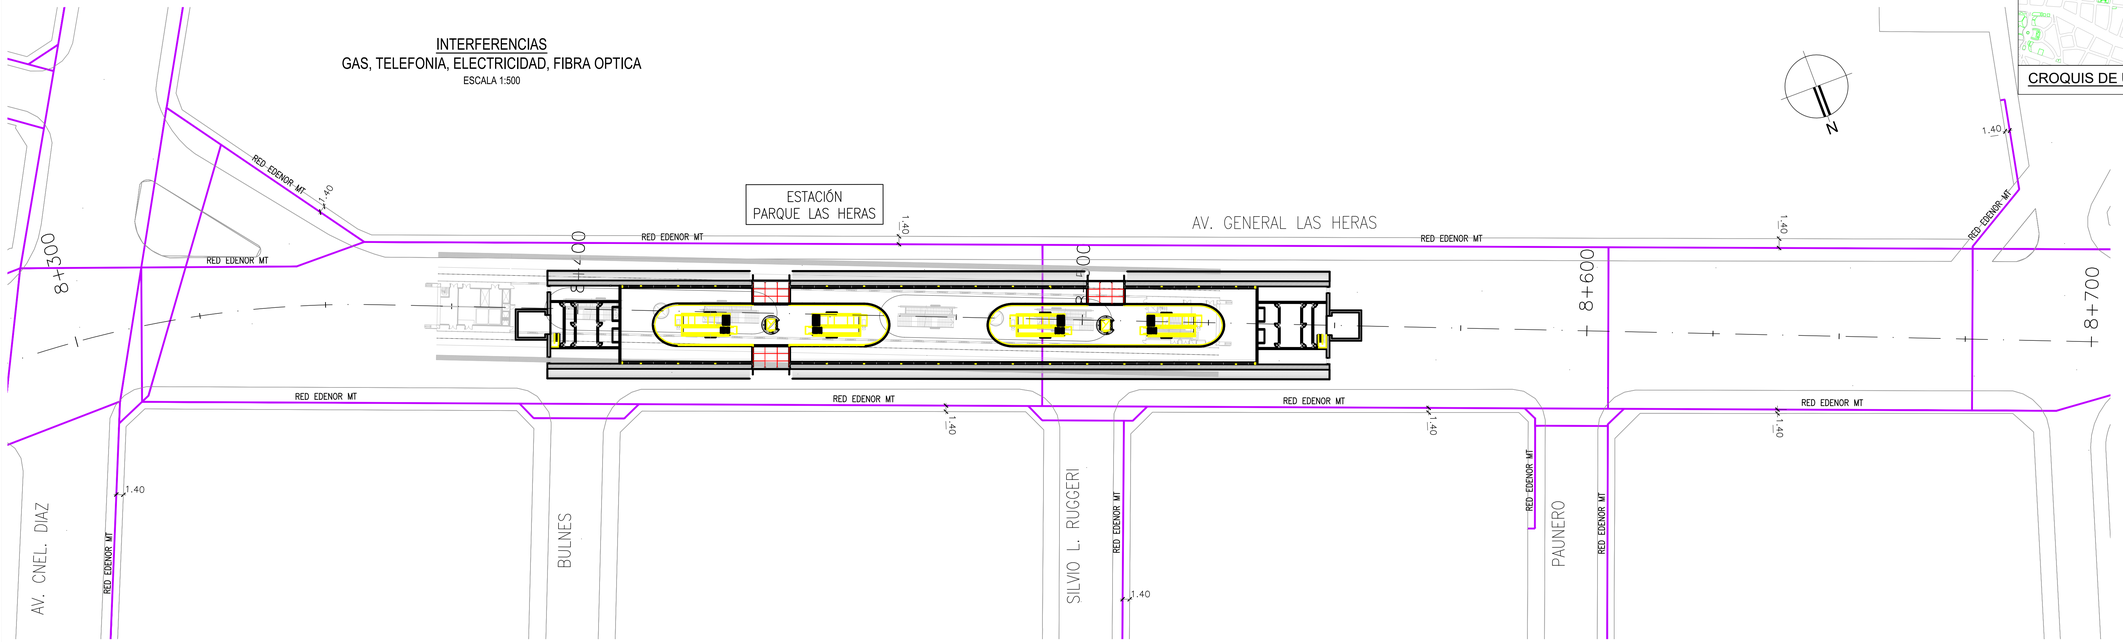

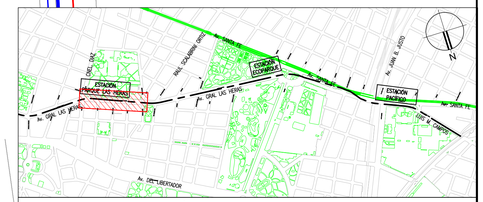

CROQUIS DE UBICACIÓN

REFERENCIAS:
- RED CLOACAL
- RED PLUVIAL
- RED AGUA
- RED ELECTRICA
- RED GAS
- RED TELEFONICA
- RED FIBRA OPTICA MULTICANAL

NOTAS:
1- SISTEMA DE COORDENADAS DE LA CIUDAD DE BUENOS AIRES.
2- TODAS LAS MEDIDAS ESTÁN EXPRESADAS EN METROS, SALVO INDICACIÓN CONTRARIA

0 10 20 30m
ESCALA 1:500

NOTAS:
EL PRESENTE PLANO ES INDICATIVO. LA CONTRATISTA CONFECCIONARA LOS PLANOS DE DETALLE CORRESPONDIENTES QUE DEBERAN SER APROBADOS POR LA D.G.O.SM° Y LA INSPECCION DE OBRA. EL PLANO PRESENTADO POR LA CONTRATISTA ESTARA EN UN TODO DE ACUERDO CON LA NORMATIVA VIGENTE.
TODAS LAS MEDIDAS Y NIVELES DE VERIFICARAN EN OBRA POR EL CONTRATISTA.
TODOS LOS DETALLES CONSTRUCTIVOS SERAN COORDINADOS Y CONFIRMADOS EN OBRA

PLANO NO APTO PARA CONSTRUCCION.

Ing. Mariano Miculicich
DIRECTOR

MODIFICACIONES:

NÚMERO	FECHA	DESCRIPCION
0	15/05/2025	EMISIÓN INICIAL
1	11/12/2025	AJUSTE DE PROYECTO

Gobierno de la Ciudad de Buenos Aires

MINISTERIO DE INFRAESTRUCTURA
SUBSECRETARIA DE PROYECTOS Y OBRAS
DIRECCION GENERAL DE PROYECTOS

DGPRO

Obra: LINEA F
Plano: TRAZADO DE TÚNEL - INTERFERENCIAS - PROG. 8+300 A 8+700
Fecha: 11/12/2025 | Eq. de Proyecto: UPU-ATEC-IATASA | Dibujó: D.B. | Revisó: P.C. | Escala: 1:500

IF-2026-20223041-GCABA-APRA
LF-GL-T02-INT-PL-006
Plano N° 006

4/1/2026 12:49
X:\el-estaciones.dwg

INTERFERENCIAS
SERVICIOS CLOACALES, PLUVIALES, AGUA CORRIENTE
ESCALA 1:500

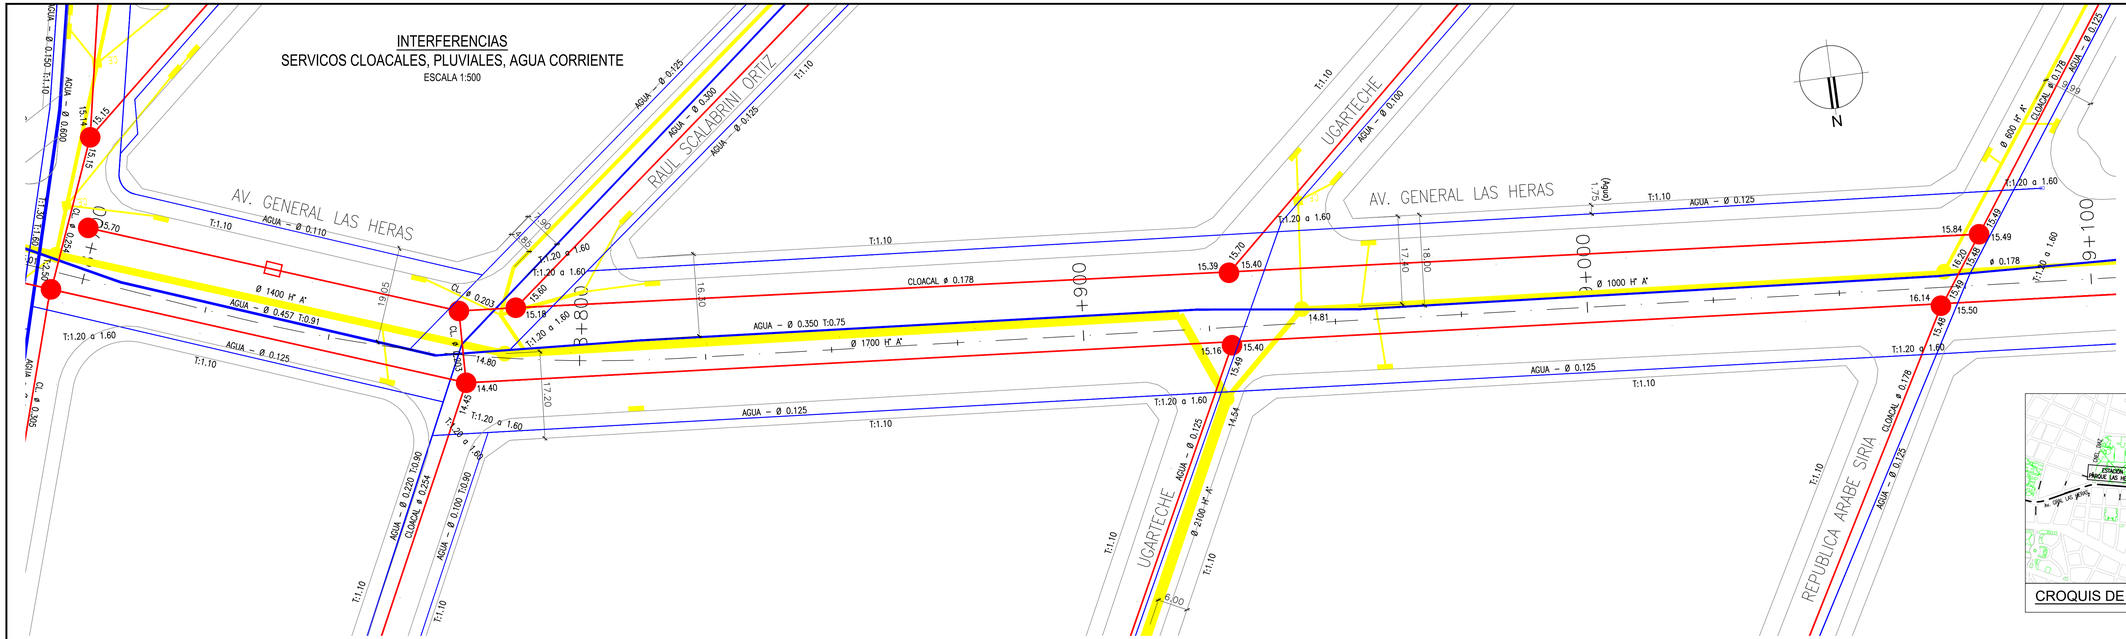

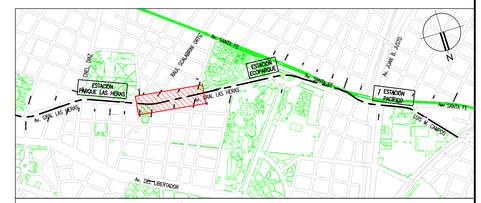

CROQUIS DE UBICACIÓN

INTERFERENCIAS
GAS, TELEFONIA, ELECTRICIDAD, FIBRA OPTICA
ESCALA 1:500

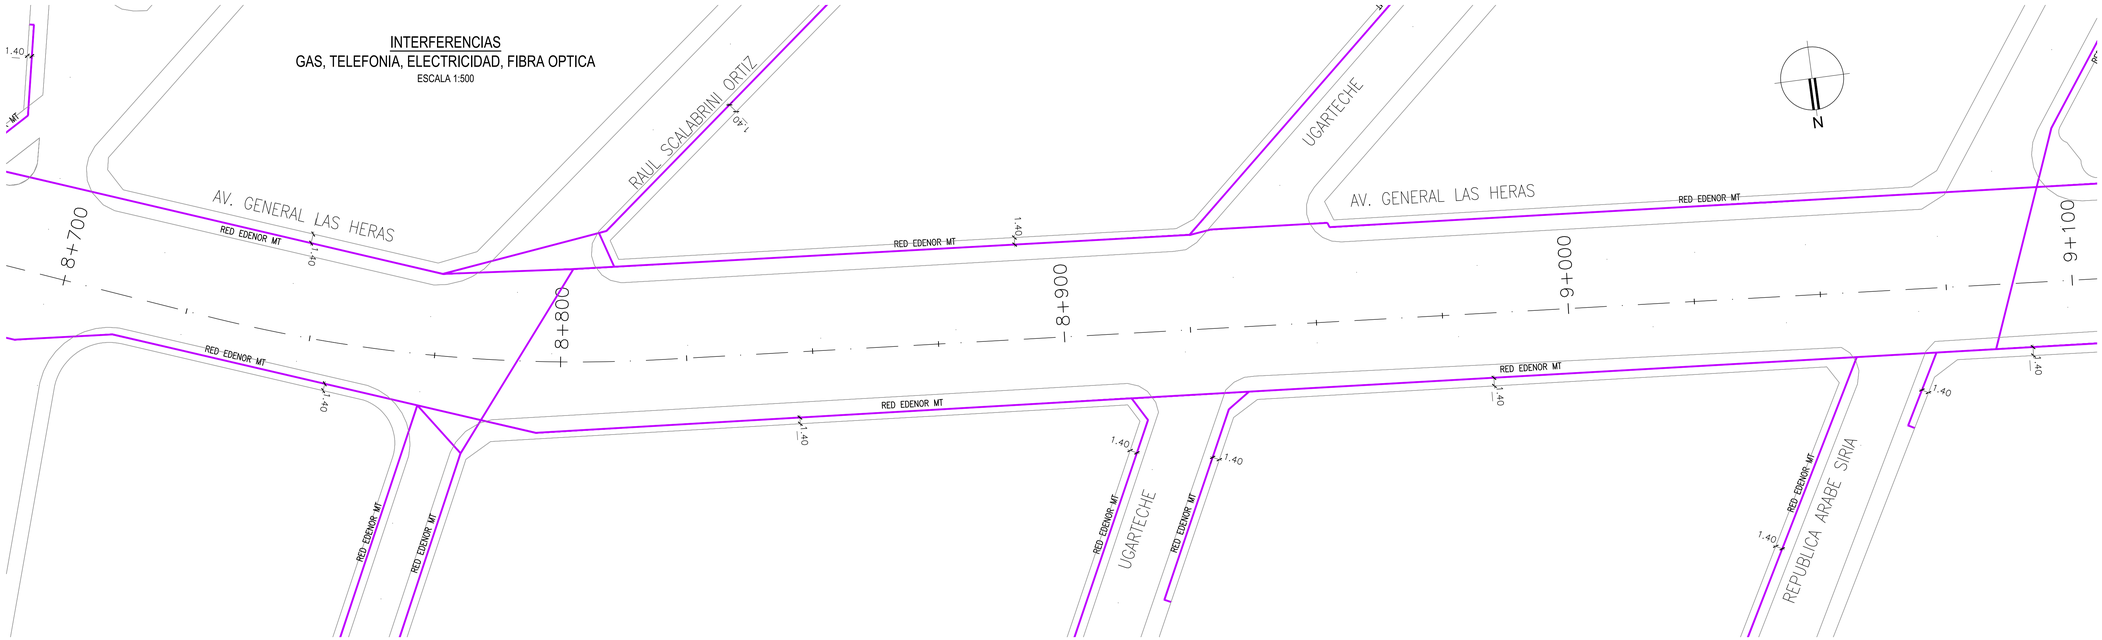

REFERENCIAS:
- RED CLOACAL
- RED PLUVIAL
- RED AGUA
- RED ELECTRICA
- RED GAS
- RED TELEFONICA
- RED FIBRA OPTICA MULTICANAL

NOTAS:
1- SISTEMA DE COORDENADAS DE LA CIUDAD DE BUENOS AIRES.
2- TODAS LAS MEDIDAS ESTÁN EXPRESADAS EN METROS, SALVO INDICACIÓN CONTRARIA

0 10 20 30m
ESCALA 1:500

NOTAS: EL PRESENTE PLANO ES INDICATIVO. LA CONTRATISTA CONFECCIONARA LOS PLANOS DE DETALLE DEFINITIVO QUE DEBERAN SER APROBADOS POR LA D.G.C.SIP.U Y LA INSPECCION DE OBRA. EL PLANO PRESENTADO POR LA CONTRATISTA DEBERA EN UN TODO DE ACUERDO CON LA NORMATIVA VIGENTE. TODAS LAS MEDIDAS Y NIVELES SE VERIFICARAN EN OBRA POR EL CONTRATISTA. TODOS LOS DETALLES CONSTRUCTIVOS SERAN COORDINADOS Y COMPATIBILIZADOS EN OBRA

PLANO NO APTO PARA CONSTRUCCION.

Ing. Mariano Miculicich
DIRECTOR

MODIFICACIONES:	REVISIÓN	FECHA	DESCRIPCIÓN
	0	19/09/2025	EMISIÓN INICIAL
	1	11/12/2025	AJUSTE DE PROYECTO

Gobierno de la Ciudad de Buenos Aires

MINISTERIO DE INFRAESTRUCTURA
SUBSECRETARIA DE PROYECTOS Y OBRAS
DIRECCION GENERAL DE PROYECTOS

DGPRO

Obra: LÍNEA F				IF-2026-20223041-GCABA-APRA	Plano N°
Plano: TRAZADO DE TÚNEL - INTERFERENCIAS - PROG. 8+700 A 9+100				LF-GL-T02-INT-PL-007	007
Fecha: 11/12/2025	Eq. de Proyecto: UPU-ATEC-IATASA	Dibujó: D.B.	Revisó: P.C.	Escala: 1:500	

4/2/2026 12:49
\\vial-estaciones.ar\

INTERFERENCIAS
SERVICOS CLOACALES, PLUVIALES, AGUA CORRIENTE
ESCALA 1:500

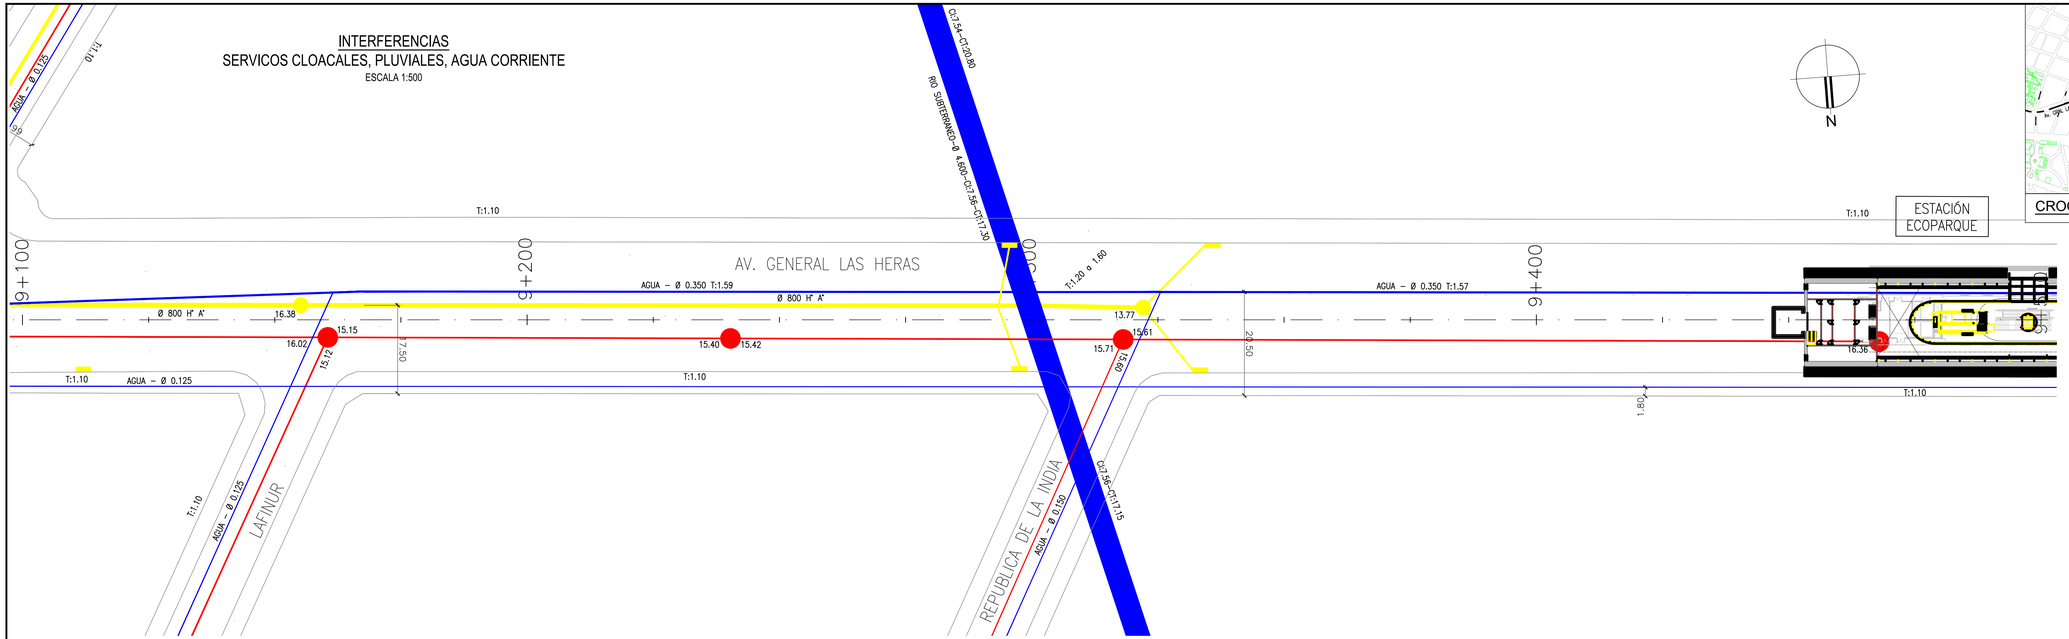

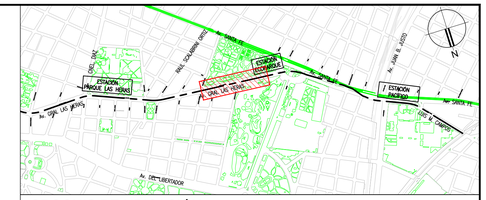

CROQUIS DE UBICACIÓN

INTERFERENCIAS
GAS, TELEFONIA, ELECTRICIDAD, FIBRA OPTICA
ESCALA 1:500

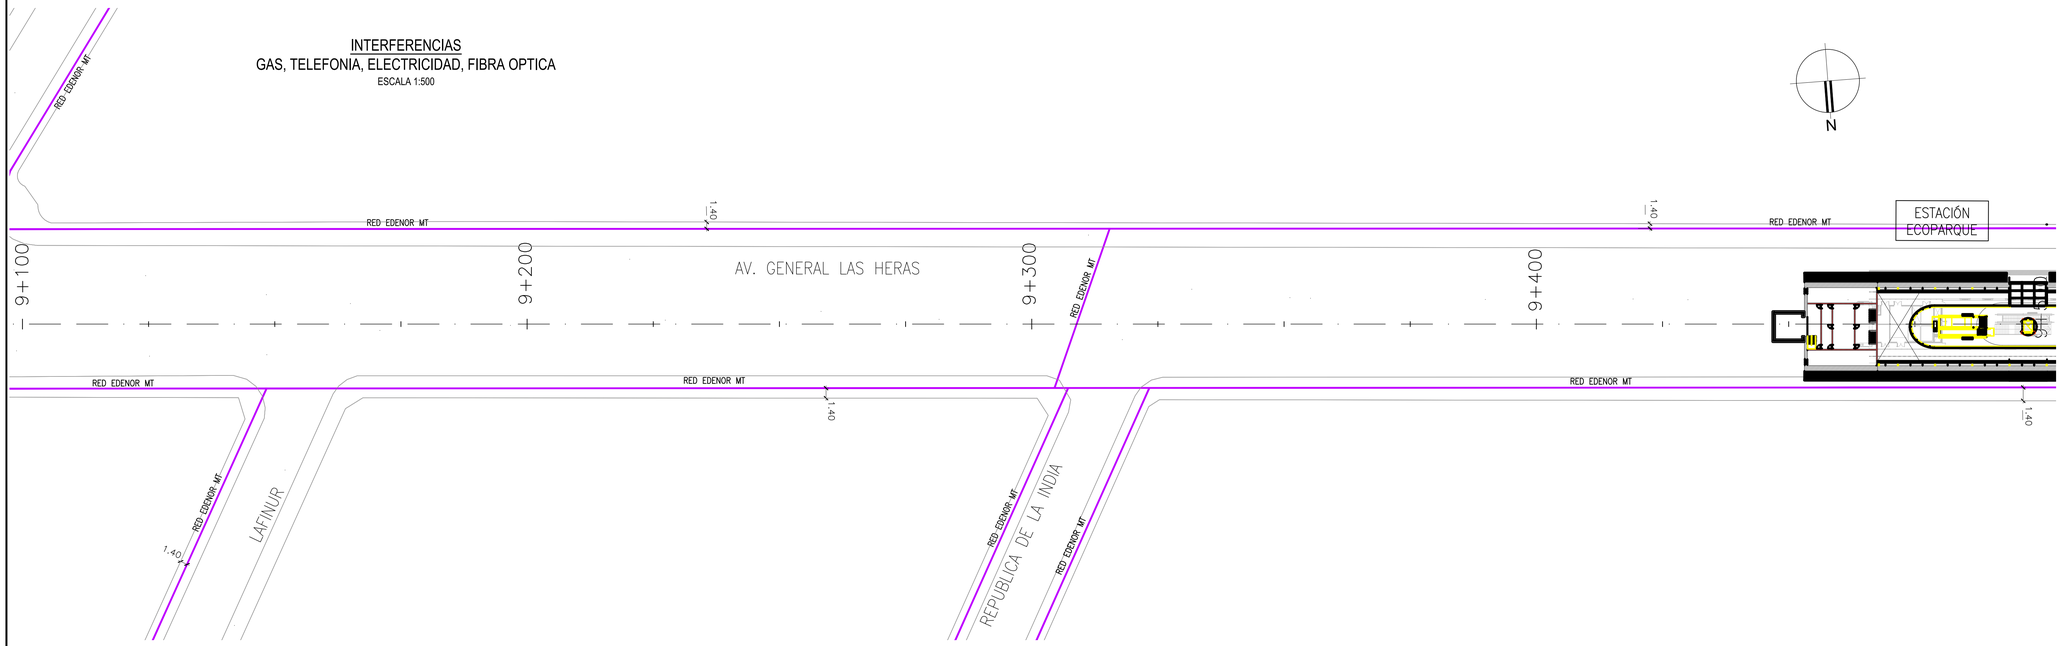

REFERENCIAS:
- RED CLOACAL
- RED PLUVIAL
- RED AGUA
- RED ELECTRICA
- RED GAS
- RED TELEFONICA
- RED FIBRA OPTICA MULTICANAL

NOTAS:
1- SISTEMA DE COORDENADAS DE LA CIUDAD DE BUENOS AIRES.
2- TODAS LAS MEDIDAS ESTÁN EXPRESADAS EN METROS, SALVO INDICACIÓN CONTRARIA

0 10 20 30m
ESCALA 1:500

NOTAS: EL PRESENTE PLANO ES INDICATIVO. LA CONTRATISTA CONFECCIONARA LOS PLANOS DE DETALLE DEFINITIVO QUE DEBERAN SER APROBADOS POR LA D.G.D.GIF.S.T.I.A. INSPECCION DE OBRA. EL PLANO PRESENTADO POR LA CONTRATISTA DEBERA EN UN TODO DE ACUERDO CON LA NORMATIVA VIGENTE. TODAS LAS MEDIDAS Y NIVELES SE VERIFICARAN EN OBRA POR EL CONTRATISTA. TODOS LOS DETALLES CONSTRUCTIVOS SERAN COORDINADOS Y COMPATIBILIZADOS EN OBRA

PLANO NO APTO PARA CONSTRUCCION.

Ing. Mariano Miculicich
DIRECTOR

MODIFICACIONES:	REVISION	FECHA	DESCRIPCION
	0	19/09/2025	EMISION INICIAL
	1	11/12/2025	AJUSTE DE PROYECTO

Gobierno de la Ciudad de Buenos Aires

MINISTERIO DE INFRAESTRUCTURA
SUBSECRETARIA DE PROYECTOS Y OBRAS
DIRECCION GENERAL DE PROYECTOS

DGPRO

Obra: LÍNEA F				IF-2026-20223041-GCABA-APRA	Plano N°
Plano: TRAZADO DE TÚNEL - INTERFERENCIAS - PROG. 9+100 A 9+500				LF-GL-T02-INT-PL-008	008
Fecha: 11/12/2025	Eq. de Proyecto: UPU-ATEC-IATASA	Dibujó: D.B.	Revisó: P.C.	Escala: 1:500	

4/2/2026 12:49
\\vial-estaciones.ar\g

INTERFERENCIAS
SERVICOS CLOACALES, PLUVIALES, AGUA CORRIENTE
ESCALA 1:500

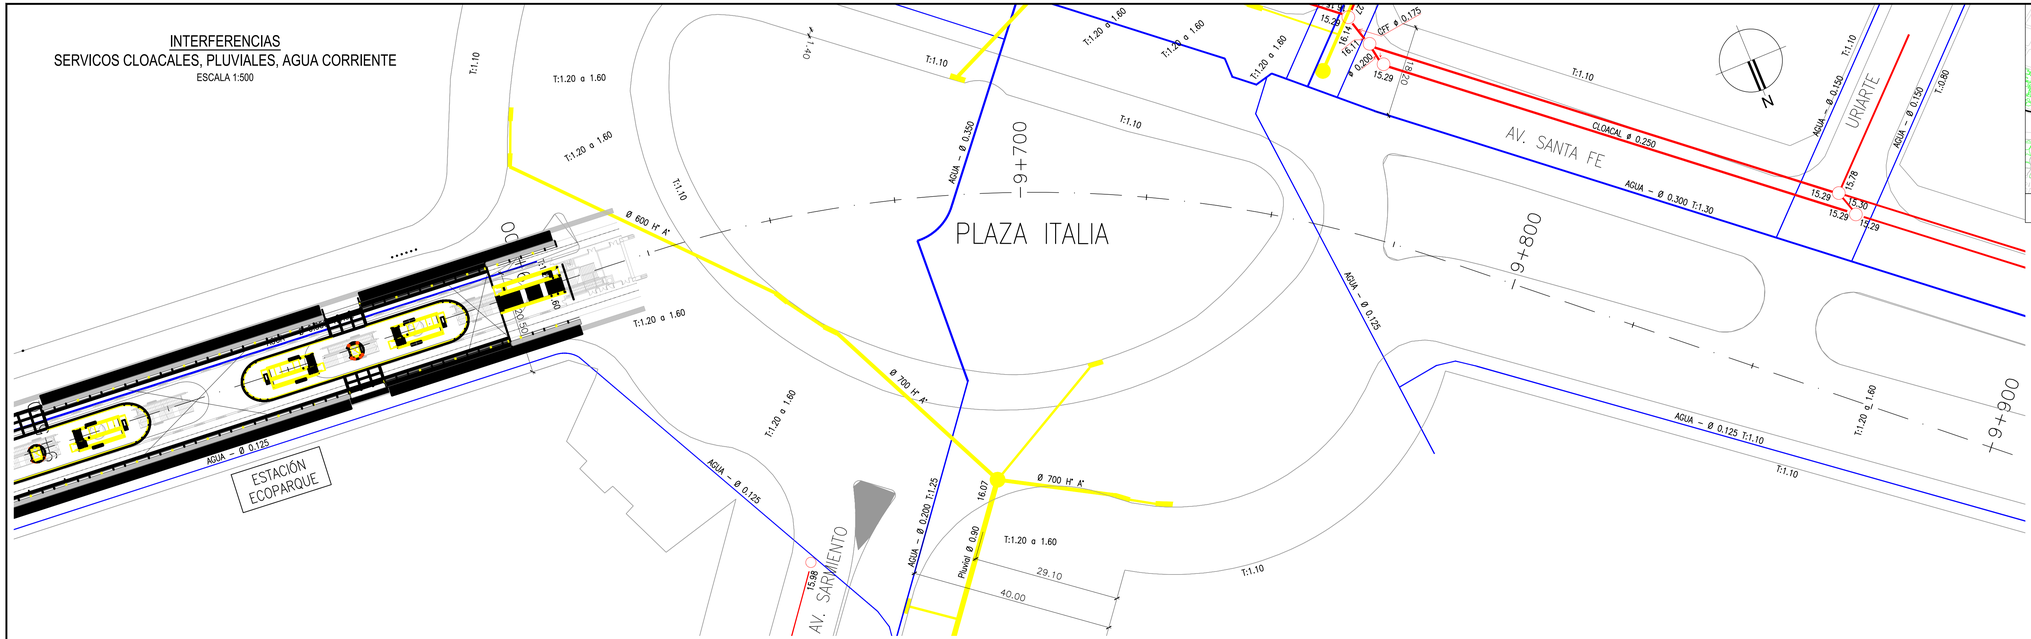

CROQUIS DE UBICACIÓN

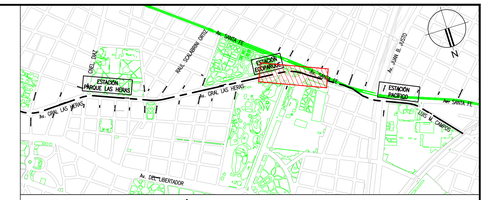

INTERFERENCIAS
GAS, TELEFONIA, ELECTRICIDAD, FIBRA OPTICA
ESCALA 1:500

REFERENCIAS:
- RED CLOACAL
- RED PLUVIAL
- RED AGUA
- RED ELECTRICA
- RED GAS
- RED TELEFONICA
- RED FIBRA OPTICA MULTICANAL

NOTAS:
1- SISTEMA DE COORDENADAS DE LA CIUDAD DE BUENOS AIRES.
2- TODAS LAS MEDIDAS ESTÁN EXPRESADAS EN METROS, SALVO INDICACIÓN CONTRARIA

0 10 20 30m
ESCALA 1:500

NOTAS: EL PRESENTE PLANO ES INDICATIVO. LA CONTRATISTA CONFECCIONARA LOS PLANOS DE DETALLE DEFINITIVO QUE DEBERAN SER APROBADOS POR LA D.G.O.SIP.U.Y LA INSPECCION DE OBRA. EL PLANO PRESENTADO POR LA CONTRATISTA DEBERA EN UN TODO DE ACUERDO CON LA NORMATIVA VIGENTE. TODAS LAS MEDIDAS Y NIVELES SE VERIFICARAN EN OBRA POR EL CONTRATISTA. TODOS LOS DETALLES CONSTRUCTIVOS SERAN COORDINADOS Y COMPATIBILIZADOS EN OBRA

PLANO NO APTO PARA CONSTRUCCION.

Ing. Mariano Miculicich
DIRECTOR

MODIFICACIONES:

REVISION	FECHA	DESCRIPCION
0	19/09/2025	EMISION INICIAL
1	11/12/2025	AJUSTE DE PROYECTO

Gobierno de la Ciudad de Buenos Aires

MINISTERIO DE INFRAESTRUCTURA
SUBSECRETARIA DE PROYECTOS Y OBRAS
DIRECCION GENERAL DE PROYECTOS

DGPRO

Obra: LÍNEA F — IF-2026-20223041-GCABA-APRA — Plano N°
Plano: TRAZADO DE TÚNEL - INTERFERENCIAS - PROG. 9+500 A 9+900 — LF-GL-T02-INT-PL-009 — 009
Fecha: 11/12/2025 | Eq. de Proyecto: UPU-ATEC-IATASA | Dibujó: D.B. | Revisó: P.C. | Escala: 1:500

4/12/2025 12:49
Ver1-estaciones.dwg

INTERFERENCIAS
SERVICOS CLOACALES, PLUVIALES, AGUA CORRIENTE
ESCALA 1:500

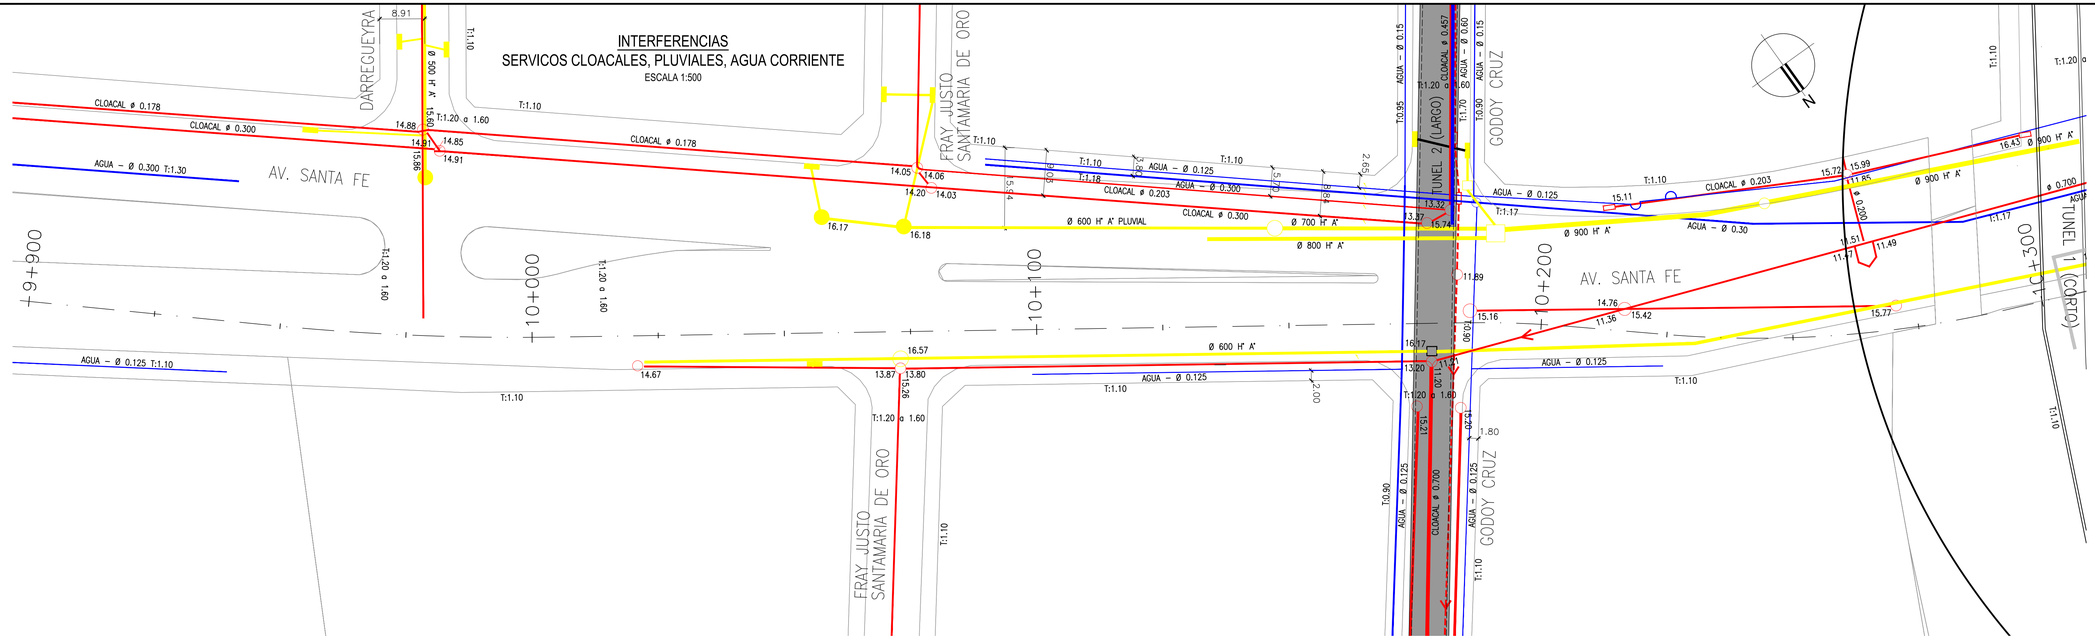

INTERFERENCIAS
GAS, TELEFONIA, ELECTRICIDAD, FIBRA OPTICA
ESCALA 1:500

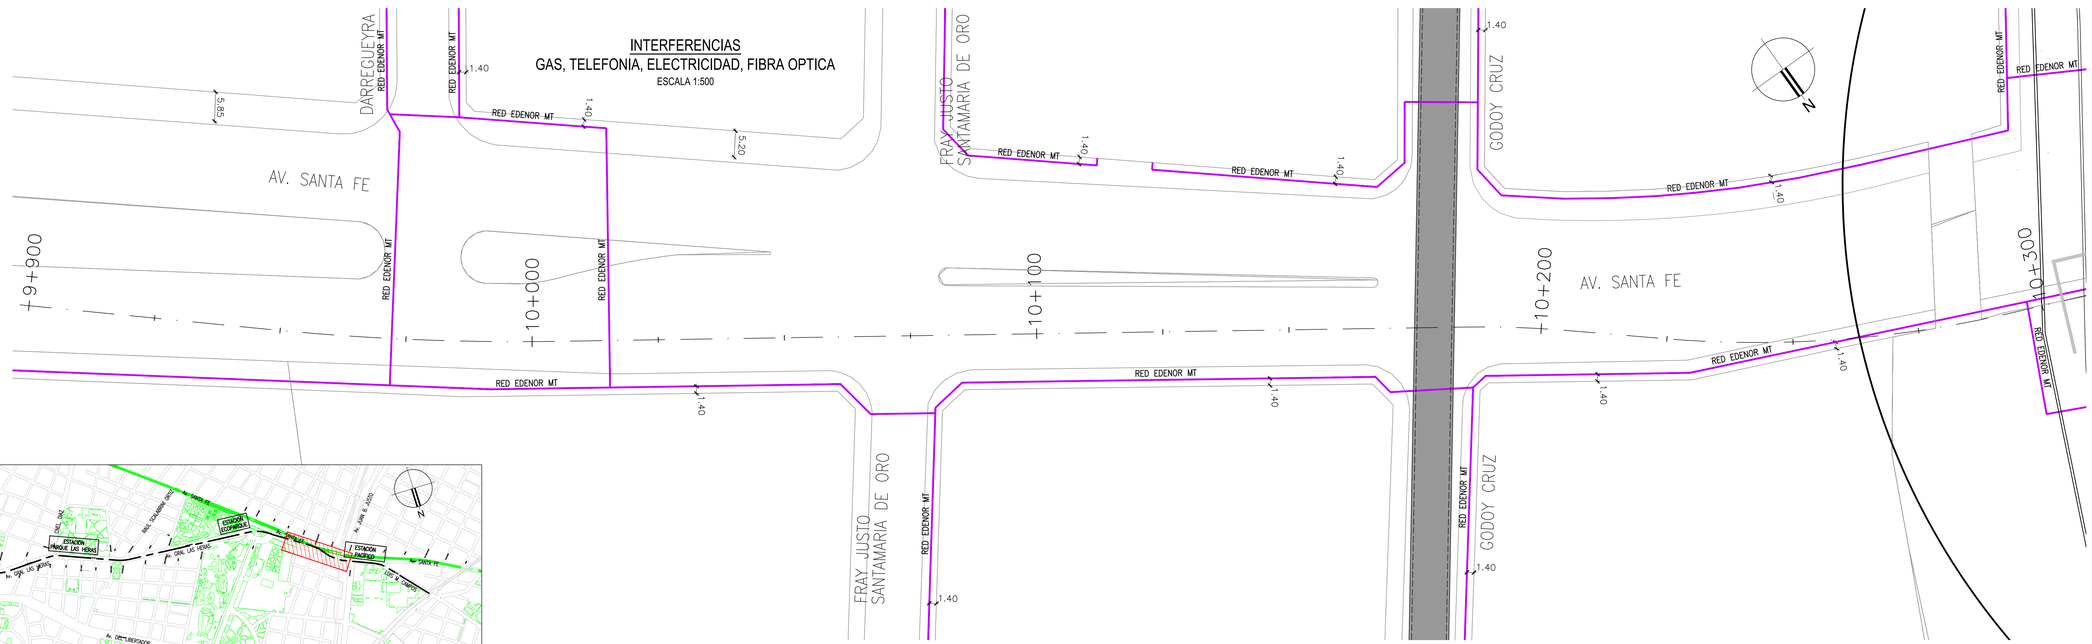

REFERENCIAS:
- RED CLOACAL
- RED PLUVIAL
- RED AGUA
- RED ELECTRICA
- RED GAS
- RED TELEFONICA
- RED FIBRA OPTICA MULTICANAL

NOTAS:
1- SISTEMA DE COORDENADAS DE LA CIUDAD DE BUENOS AIRES.
2- TODAS LAS MEDIDAS ESTÁN EXPRESADAS EN METROS, SALVO INDICACIÓN CONTRARIA

0 10 20 30m
ESCALA 1:500

CROQUIS DE UBICACIÓN

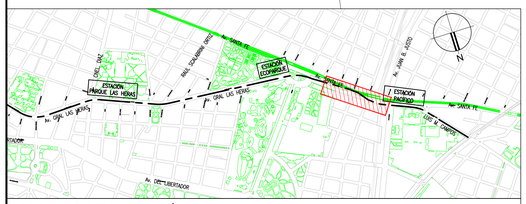

NOTAS: EL PRESENTE PLANO ES INDICATIVO. LA CONTRATISTA CONFECCIONARA LOS PLANOS DE DETALLE DEFINITIVO QUE DEBERAN SER APROBADOS POR LA D.G.C.SIP.S.T.U.A. INSPECCION DE OBRA, EL PLANO PRESENTADO POR LA CONTRATISTA DEBERA EN UN TODO DE ACUERDO CON LA NORMATIVA VIGENTE. TODAS LAS MEDIDAS Y NIVELES SE VERIFICARAN EN OBRA POR EL CONTRATISTA. TODOS LOS DETALLES CONSTRUCTIVOS SERAN COORDINADOS Y CONFIRMADOS EN OBRA

PLANO NO APTO PARA CONSTRUCCION.

Ing. Mariano Miculicich
DIRECTOR

MODIFICACIONES:

REVISION	FECHA	DESCRIPCION
0	19/09/25	EMISION INICIAL
1	11/12/25	AJUSTE DE PROYECTO

Gobierno de la Ciudad de Buenos Aires

MINISTERIO DE INFRAESTRUCTURA
SUBSECRETARIA DE PROYECTOS Y OBRAS
DIRECCION GENERAL DE PROYECTOS

DGPRO

Obra: LINEA F				IF-2026-20223041-GCABA-APRA	Plano N°
Plano: TRAZADO DE TÚNEL - INTERFERENCIAS - PROG. 9+900 A 10+300				LF-GL-T02-INT-PL-010	010
Fecha: 11/12/2025	Eq. de Proyecto: UPU-ATEC-IATASA	Dibujó: D.B.	Revisó: P.C.	Escala: 1:500	

4/2/2026 12:49
\\ref-estaciones.dwg

INTERFERENCIAS
SERVICOS CLOACALES, PLUVIALES, AGUA CORRIENTE
ESCALA 1:500

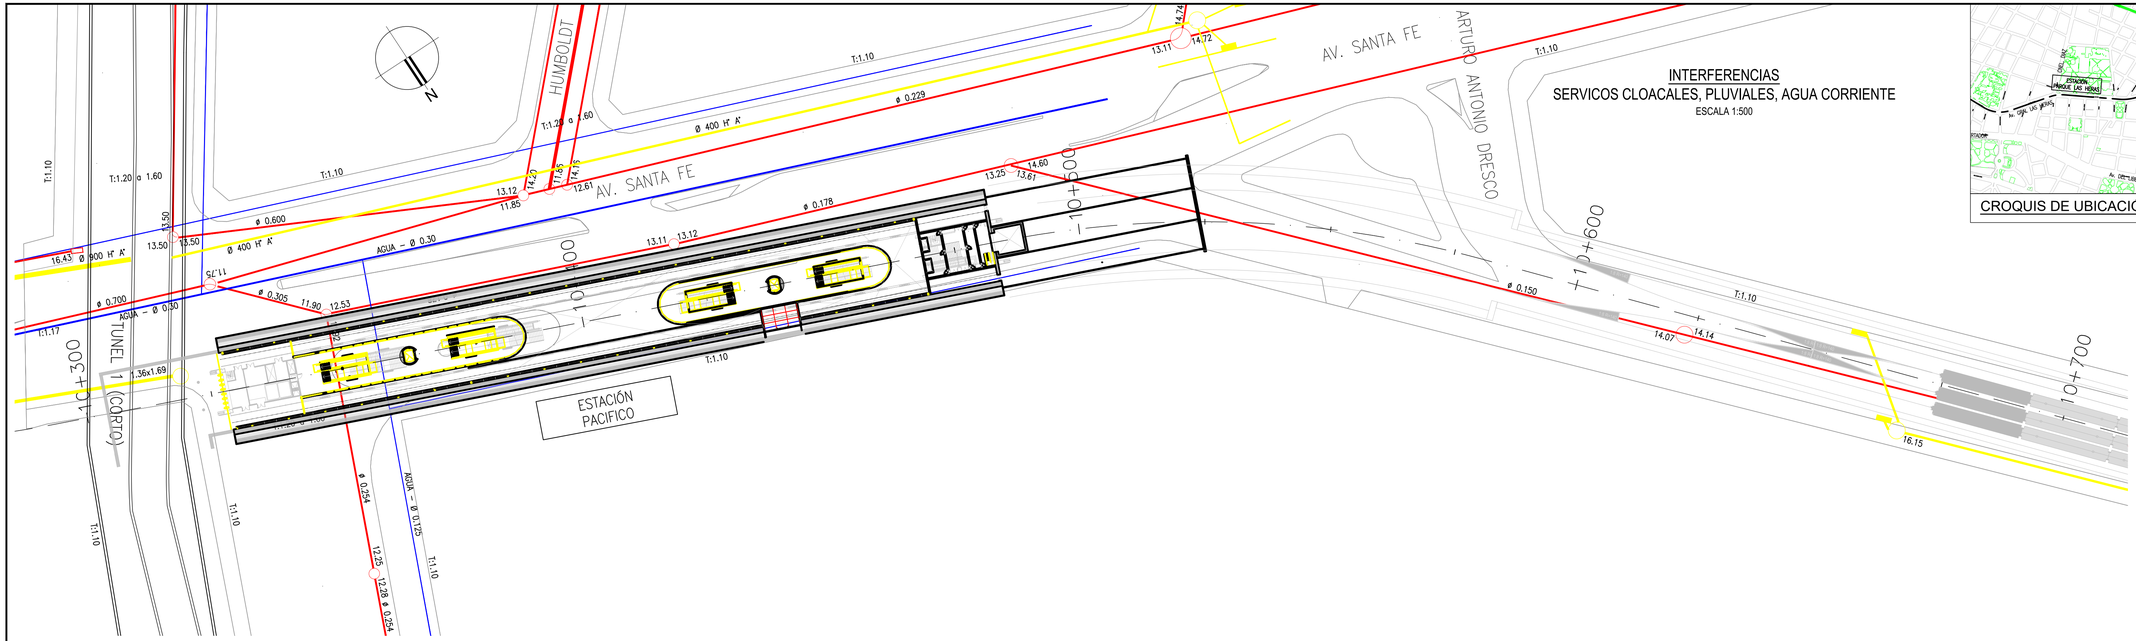

CROQUIS DE UBICACIÓN

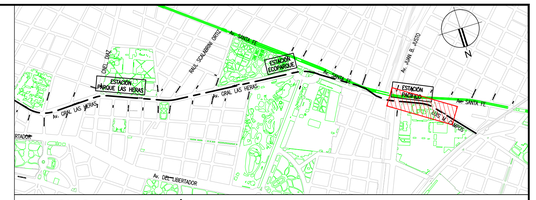

INTERFERENCIAS
GAS, TELEFONIA, ELECTRICIDAD, FIBRA OPTICA
ESCALA 1:500

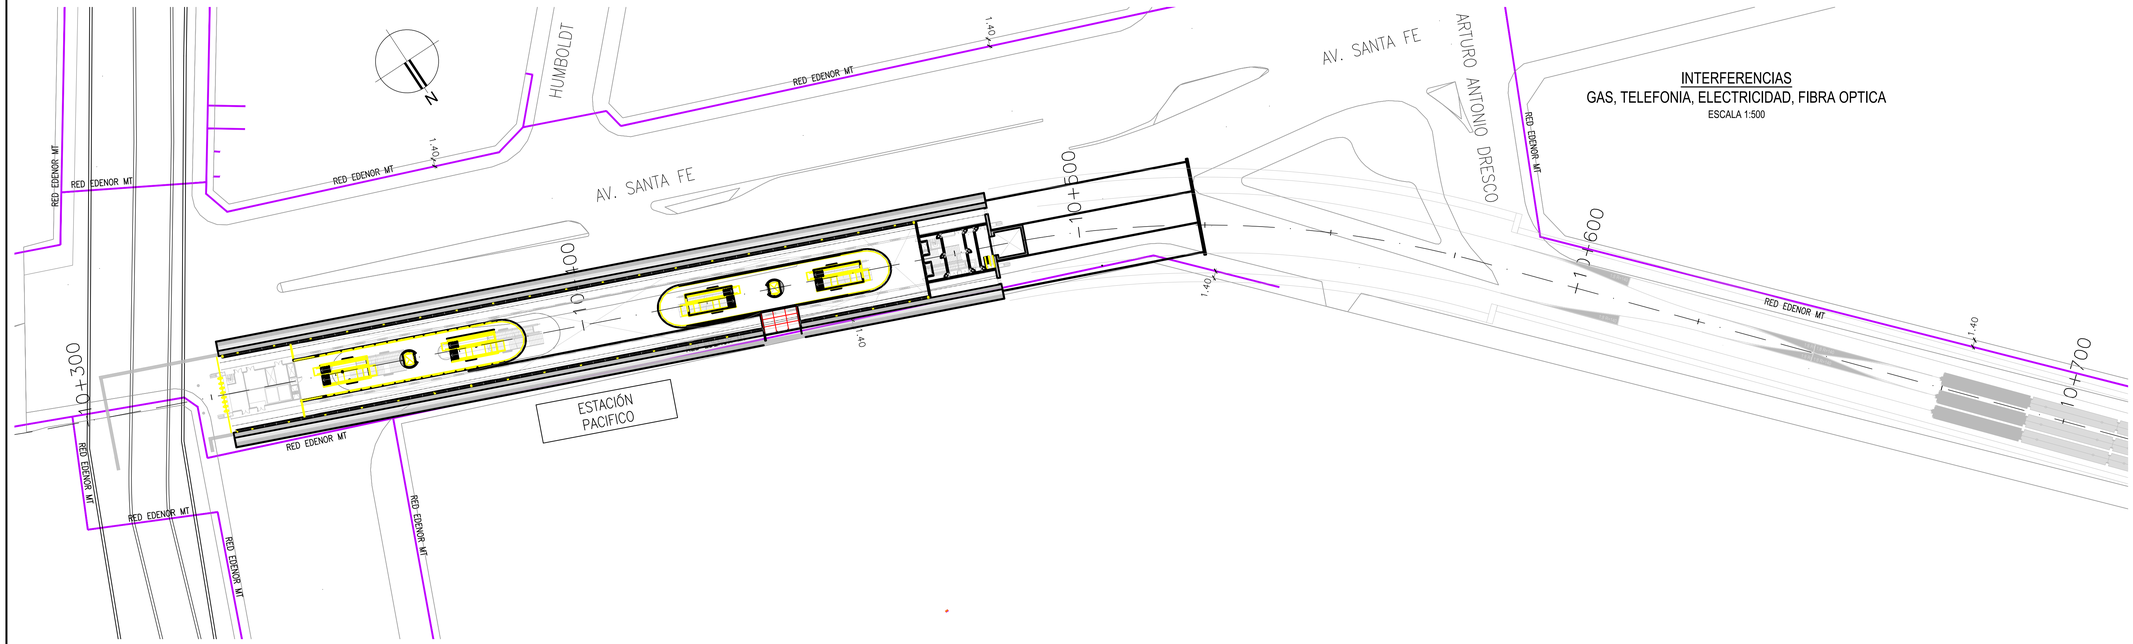

REFERENCIAS:
- RED CLOACAL
- RED PLUVIAL
- RED AGUA
- RED ELECTRICA
- RED GAS
- RED TELEFONICA
- RED FIBRA OPTICA MULTICANAL

NOTAS:
1- SISTEMA DE COORDENADAS DE LA CIUDAD DE BUENOS AIRES.
2- TODAS LAS MEDIDAS ESTÁN EXPRESADAS EN METROS, SALVO INDICACIÓN CONTRARIA

0 10 20 30m
ESCALA 1:500

NOTAS: EL PRESENTE PLANO ES INDICATIVO. LA CONTRATISTA CONFECCIONARA LOS PLANOS DE DETALLE DEFINITIVO QUE DEBERAN SER APROBADOS POR LA D.G.C.SIP.Q.Y LA INSPECCION DE OBRA. EL PLANO PRESENTADO POR LA CONTRATISTA DEBERA EN UN TODO DE ACUERDO CON LA NORMATIVA VIGENTE. TODAS LAS MEDIDAS Y NIVELES SE VERIFICARAN EN OBRA POR EL CONTRATISTA. TODOS LOS DETALLES CONSTRUCTIVOS SERAN COORDINADOS Y COMPATIBILIZADOS EN OBRA

PLANO NO APTO PARA CONSTRUCCION.

Ing. Mariano Miculicich
DIRECTOR

MODIFICACIONES:

REVISION	FECHA	DESCRIPCION
0	19/09/2025	EMISION INICIAL
1	11/12/2025	AJUSTE DE PROYECTO

Gobierno de la Ciudad de Buenos Aires

MINISTERIO DE INFRAESTRUCTURA
SUBSECRETARIA DE PROYECTOS Y OBRAS
DIRECCION GENERAL DE PROYECTOS

DGPRO

Obra: LINEA F				IF-2026-20223041-GCABA-APRA	Plano N°
Plano: TRAZADO DE TÚNEL - INTERFERENCIAS - PROG. 10+300 A 10+700				LF-GL-T02-INT-PL-011	011
Fecha: 11/12/2025	Eq. de Proyecto: UPU-ATEC-IATASA	Dibujó: D.B.	Revisó: P.C.	Escala: 1:500	

4/1/2026, 13:07
LF-GL-T02-INT-PL-001-b007_1.dwg

INTERFERENCIAS
SERVICOS CLOACALES, PLUVIALES, AGUA CORRIENTE
ESCALA 1:500

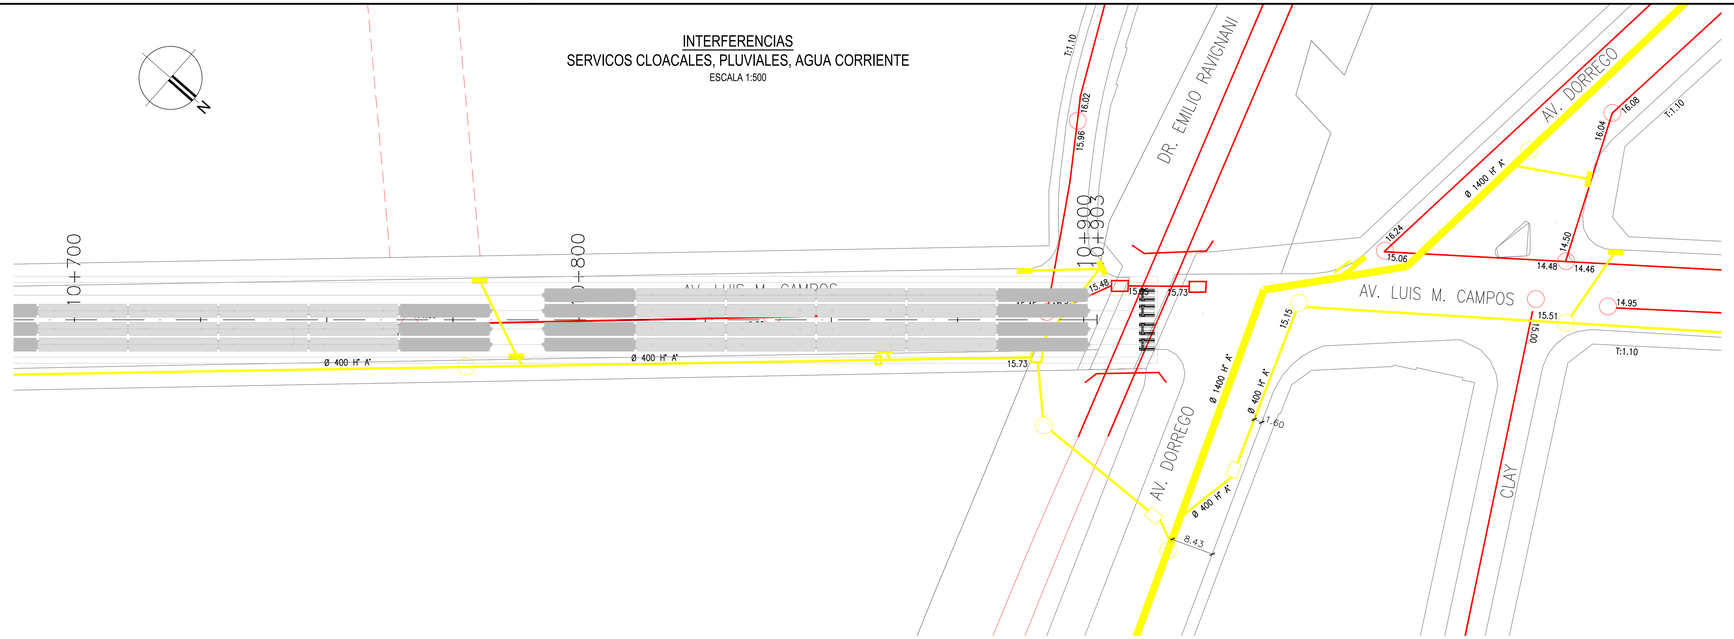

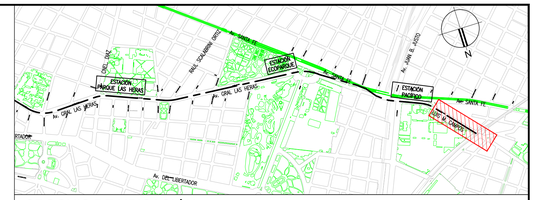

CROQUIS DE UBICACIÓN

INTERFERENCIAS
GAS, TELEFONIA, ELECTRICIDAD, FIBRA OPTICA
ESCALA 1:500

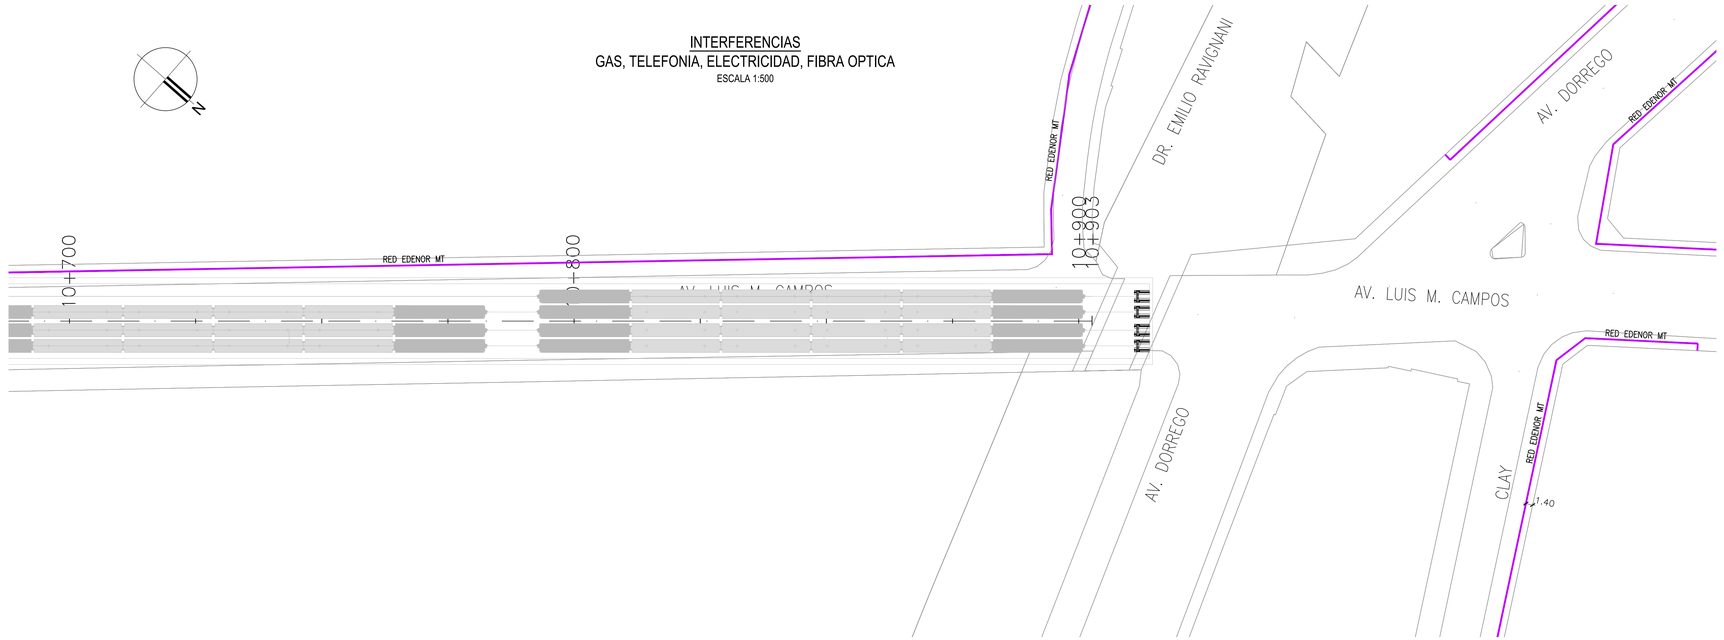

REFERENCIAS:
- RED CLOACAL
- RED PLUVIAL
- RED AGUA
- RED ELECTRICA
- RED GAS
- RED TELEFONICA
- RED FIBRA OPTICA MULTICANAL

NOTAS:
1- SISTEMA DE COORDENADAS DE LA CIUDAD DE BUENOS AIRES.
2- TODAS LAS MEDIDAS ESTÁN EXPRESADAS EN METROS, SALVO INDICACIÓN CONTRARIA

0 10 20 30m
ESCALA 1:500

NOTAS: EL PRESENTE PLANO ES INDICATIVO. LA CONTRATISTA CONFECCIONARA LOS PLANOS DE DETALLE DEFINITIVO QUE DEBERAN SER APROBADOS POR LA D.G.D.GIF.S.T.I.A. INSPECCION DE OBRA. EL PLANO PRESENTADO POR LA CONTRATISTA DEBERA EN UN TODO DE ACUERDO CON LA NORMATIVA VIGENTE. TODAS LAS MEDIDAS Y NIVELES SE VERIFICARAN EN OBRA POR EL CONTRATISTA. TODOS LOS DETALLES CONSTRUCTIVOS SERAN COORDINADOS Y COMPATIBILIZADOS EN OBRA

PLANO NO APTO PARA CONSTRUCCION.

Ing. Mariano Miculicich
DIRECTOR

MODIFICACIONES:

REVISIÓN	FECHA	DESCRIPCIÓN
0	19/09/25	EMISIÓN INICIAL
1	11/12/25	AJUSTE DE PROYECTO

MINISTERIO DE INFRAESTRUCTURA
SUBSECRETARIA DE PROYECTOS Y OBRAS
DIRECCION GENERAL DE PROYECTOS

DGPRO

Obra: LÍNEA F					IF-2026-20223041-GCABA-APRA	Plano N°
Plano: TRAZADO DE TÚNEL - INTERFERENCIAS - PROG. 10+700 A 10+900					LF-GL-T02-INT-PL-012	012
Fecha: 11/12/2025	Eq. de Proyecto: UPU-ATEC-IATASA	Dibujó: D.B.	Revisó: P.C.	Escala: 1:500		

4/2/2026 12:49
\\vial-estaciones.dwg

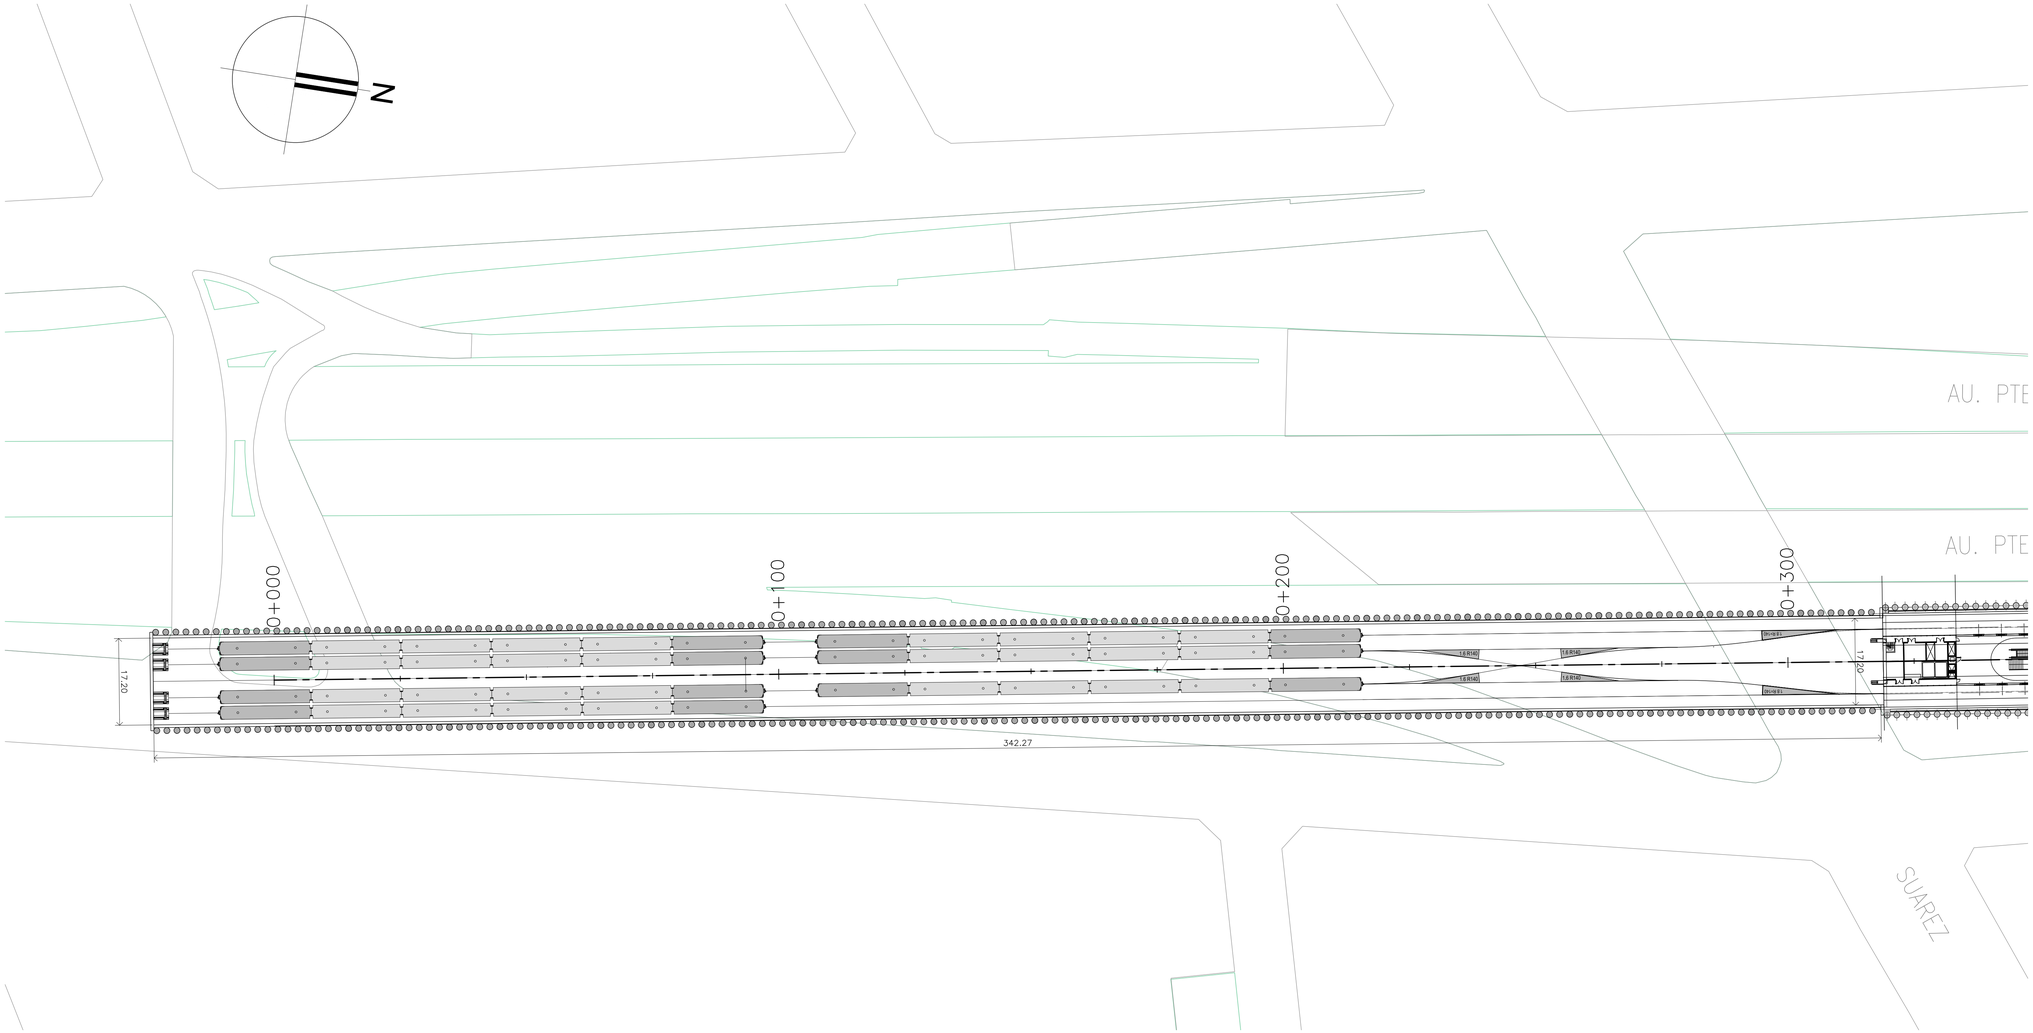

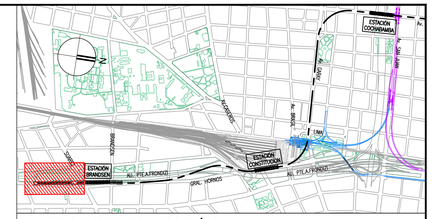

CROQUIS DE UBICACIÓN

NOTAS:

1- SISTEMA DE COORDENADAS DE LA CIUDAD DE BUENOS AIRES.

2- TODAS LAS MEDIDAS ESTÁN EXPRESADAS EN METROS, SALVO INDICACIÓN CONTRARIA

0 10 20 30m

ESCALA 1:500

NOTAS: EL PRESENTE PLANO ES INDICATIVO, LA CONTRATISTA CONFECCIONARA LOS PLANOS DE DETALLE CONTRACTUAL QUE DEBERAN SER APROBADOS POR LA D.O.O.IMF S.Y.P. INSPECCIÓN DE OBRA. EL PLANO PRESENTADO POR LA CONTRATISTA DEBERA SER VISTO EN LA TOTALIDAD ACUERDO CON LA NORMATIVA VIGENTE.
TODAS LAS MEDIDAS Y NIVELES DE VERIFICARAN EN OBRA POR EL CONTRATISTA.
TODOS LOS DETALLES CONSTRUCTIVOS SERAN COORDINADOS Y CONFIRMALIZADOS EN OBRA

PLANO NO APTO PARA CONSTRUCCION.

Ing. Mariano Miculicich
DIRECTOR

MODIFICACIONES:	ACUERDO	FECHA	DESCRIPCION
	1	30/01/2026	EMISIÓN INICIAL

MINISTERIO DE INFRAESTRUCTURA
SUBSECRETARIA DE PROYECTOS Y OBRAS
DIRECCION GENERAL DE PROYECTOS

DGPRO

Obra: LINEA F			IF-2026-20223041-GCABA-APRA Plano N°
Plano: COCHERA TRAMO 1 - BRANDSEN - PLANTA GENERAL			LF-CO-T01-TUN-PL-001 001
Fecha: 05/01/2026	Eq. de Proyecto: UPU-ATEC-IATASA	Dibujó: D.B.	Revisó: G.D.R. Escala: Indicada

5/1/2026 17:54
Plantas_Cocheras.dwg

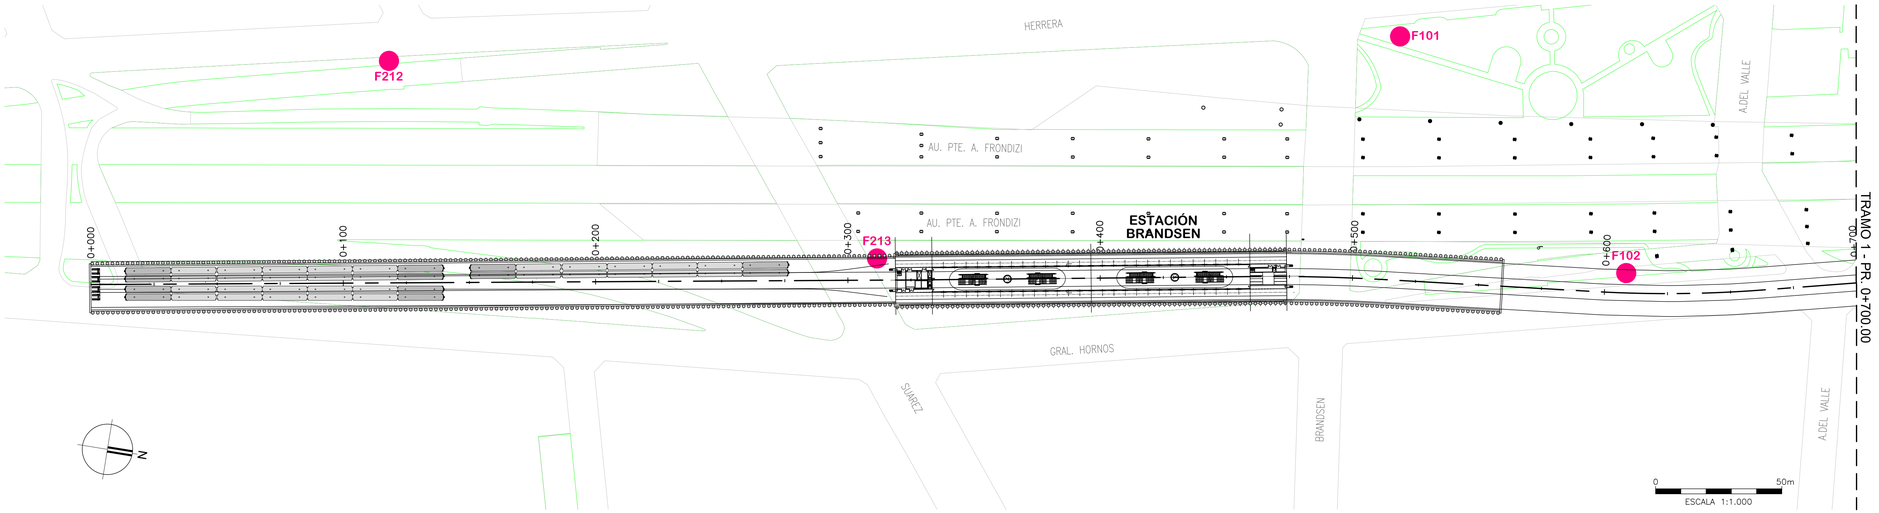

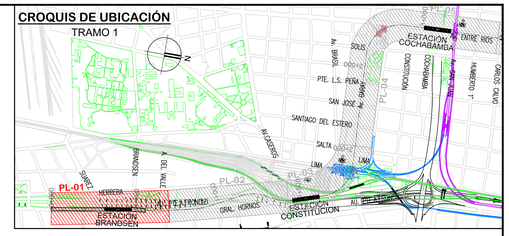

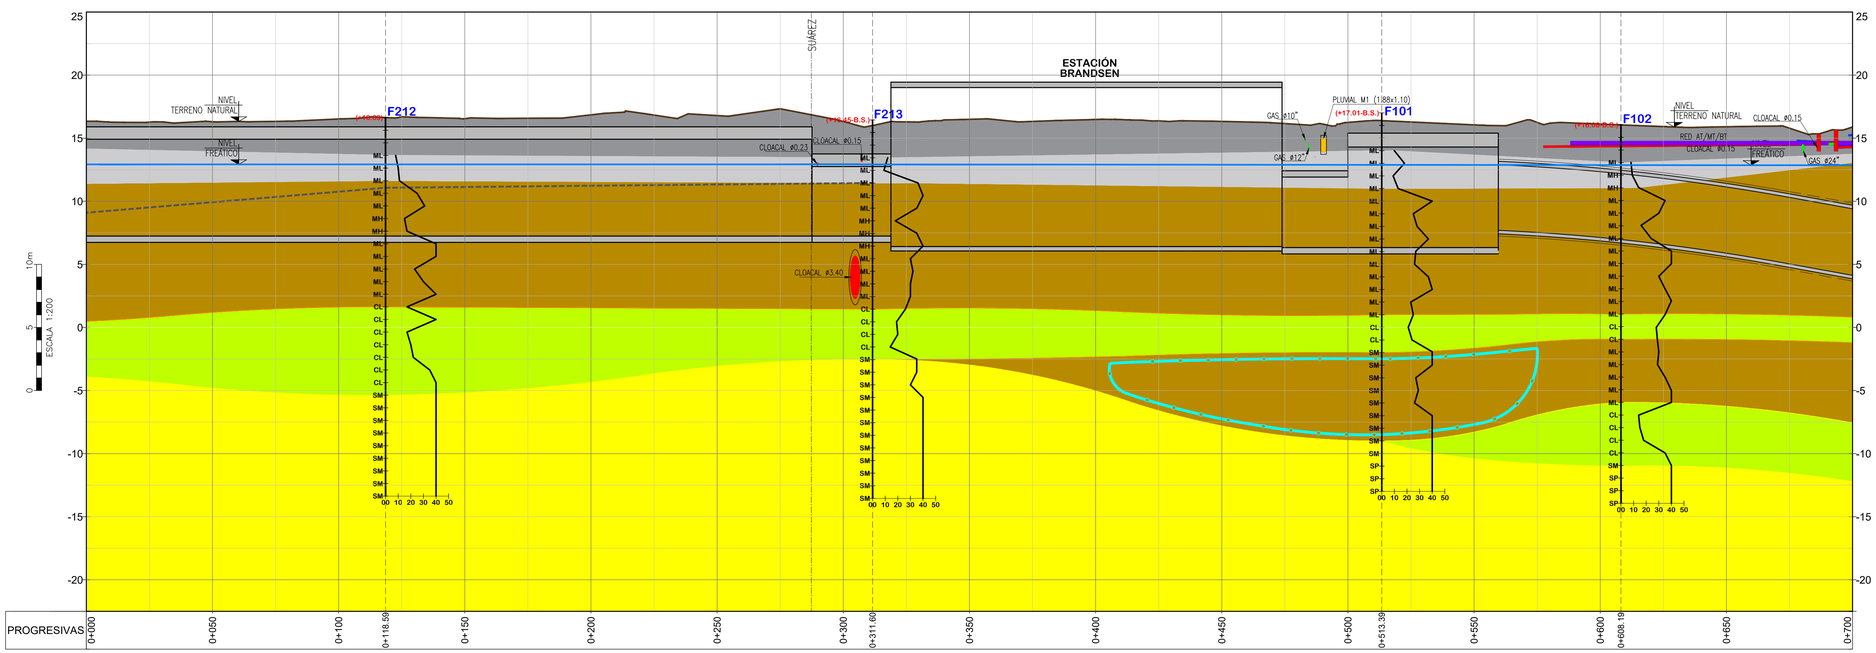

ALTIMETRÍA
ESC. HORIZ: 1:1.000
ESC. VERT: 1:200

REFERENCIAS INTERFERENCIAS:
- RED DE AGUA CORRIENTE
- RED CLOACAL
- RED DE FIBRA OPTICA
- RED BT - MT - AT
- RED DE GAS
- RED TELEFÓNICA
- RED PLUVIAL

REFERENCIAS SONDEOS:
- Fxx BOCA DE SONDEO MINAMÉRICA
- Fxx BOCA DE SONDEO MENDIGUREN
- Fxx BOCA DE SONDEO COPROGETTI

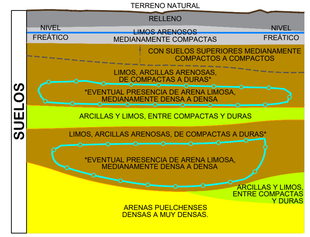

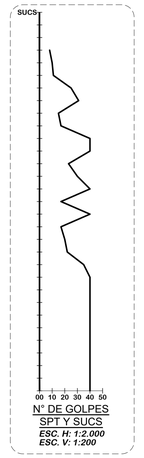

N° DE GOLPES
SPT Y SUCS
ESC. H: 1:2.000
ESC. V: 1:200

0 50 100m
ESCALA 1:2.000

NOTAS :
1- SISTEMA DE COORDENADAS DE LA CIUDAD DE BUENOS AIRES.
2- TODAS LAS MEDIDAS ESTÁN EXPRESADAS EN METROS, SALVO INDICACIÓN CONTRARIA

NOTAS:
EL PRESENTE PLANO ES INDICATIVO. LA CONTRATISTA CONFECCIONARA LOS PLANOS DE DETALLE DEFINITIVO QUE DEBERAN SER APROBADOS POR LA D.G.C.SIP.U.Y LA INSPECCION DE OBRA. EL PLANO PRESENTADO POR LA CONTRATISTA DEBERA EN UN TODO DE ACUERDO CON LA NORMATIVA VIGENTE.
TODAS LAS MEDIDAS Y NIVELES SE VERIFICARAN EN OBRA POR EL CONTRATISTA.
TODOS LOS DETALLES CONSTRUCTIVOS SERAN COORDINADOS Y COMPATIBILIZADOS EN OBRA

PLANO NO APTO PARA CONSTRUCCION.

Ing. Mariano Miculicich
DIRECTOR

MODIFICACIONES:

REVISIÓN	FECHA	DESCRIPCIÓN
0	22/09/25	EMISIÓN INICIAL
1	18/11/25	AJUSTE DE PROYECTO

MINISTERIO DE INFRAESTRUCTURA
SUBSECRETARIA DE PROYECTOS Y OBRAS
DIRECCION GENERAL DE PROYECTOS

DGPRO

Obra: LÍNEA F			IF-2026-20223041-GCABA-APRA Plano N°
Plano: GEOTECNIA - ESTRATIGRAFÍA TRAMO 1 - PROGR. 0+000 A 0+700			LF-GL-T01-GTA-PL-001
Fecha: 18/11/2025	Eq. de Proyecto: UPU-ATEC-IATASA	Dibujó: D.B.	Revisó: R.H.B. Escala: Indicadas 001

20/11/2025 12:42
LF-GL-T01-GTA-PL-001 A 009_1.dwg

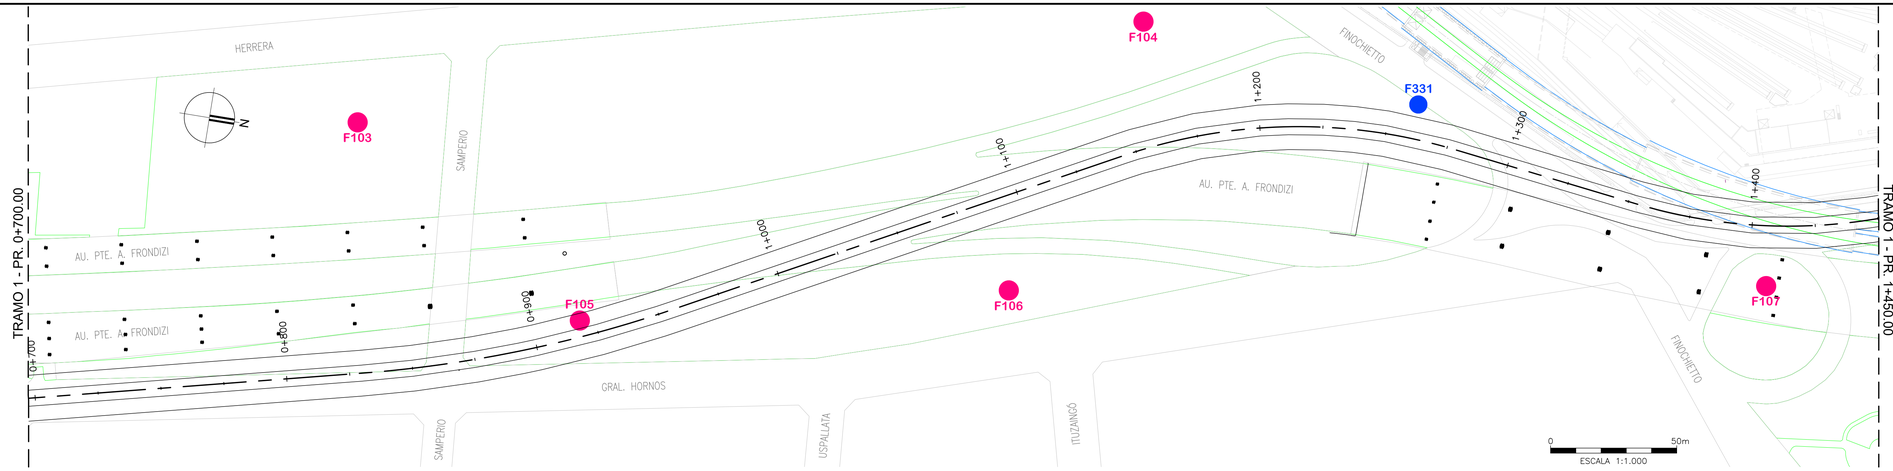
TRAMO 1 - PR. 0+700.00
TRAMO 1 - PR. 1+450.00
HERRERA
SAMPERO
AU. PTE. A. FRONDIZI
GRAL. HORNOS
USPALLATA
QUINQUELA
FINOCHIETTO
F103
F104
F105
F106
F107
F331
0+700
0+750
0+800
0+850
0+900
0+950
1+000
1+050
1+100
1+150
1+200
1+250
1+300
1+350
1+400
1+450
0
50m
ESCALA 1:1.000

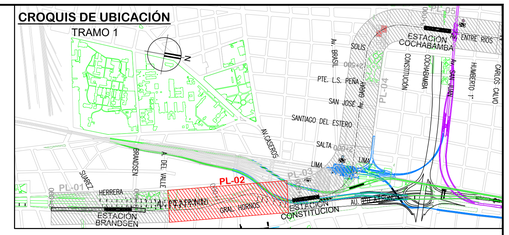
CROQUIS DE UBICACIÓN
TRAMO 1
N
ESTACIÓN COCHABAMBA
ENTRE RIOS
SOLIS
PTE. LS. PEÑA
SAN JOSE DE FLORES
SANTIAGO DEL ESTERO
AVELLANEDA
SALTA
LIMA
PL-01
PL-02
PL-03
PL-04
PL-05
PL-06
PL-07
PL-08
PL-09
PL-10
PL-11
PL-12
PL-13
PL-14
PL-15
PL-16
PL-17
PL-18
PL-19
PL-20
PL-21
PL-22
PL-23
PL-24
PL-25
PL-26
PL-27
PL-28
PL-29
PL-30
PL-31
PL-32
PL-33
PL-34
PL-35
PL-36
PL-37
PL-38
PL-39
PL-40

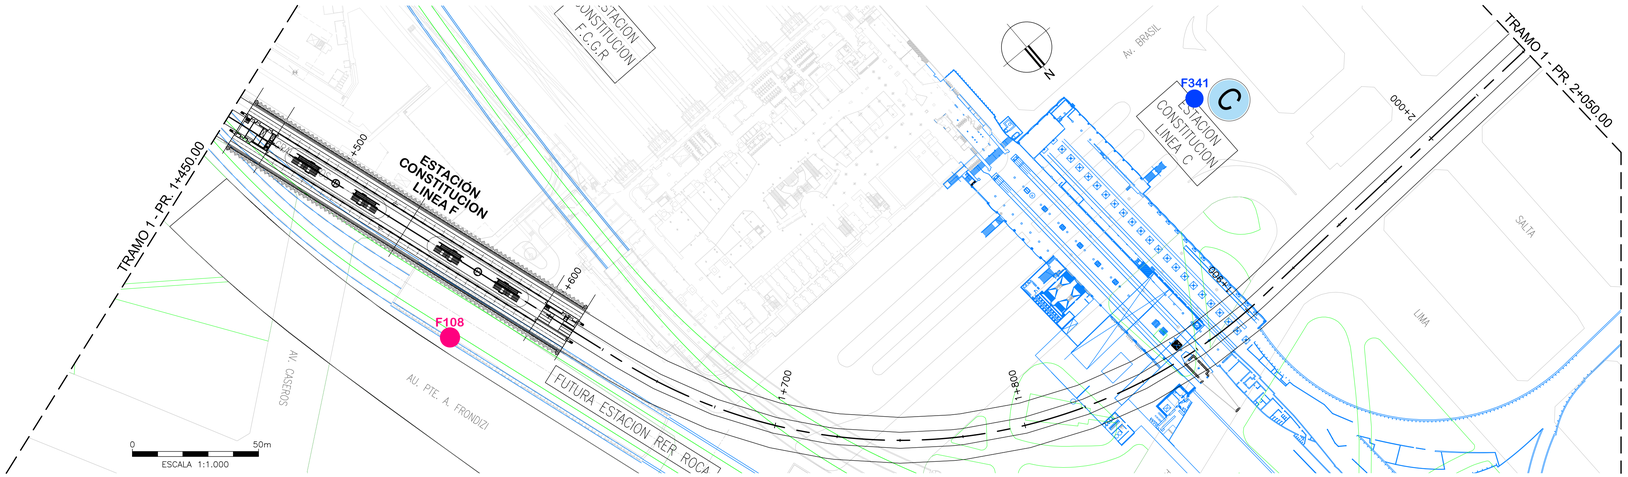

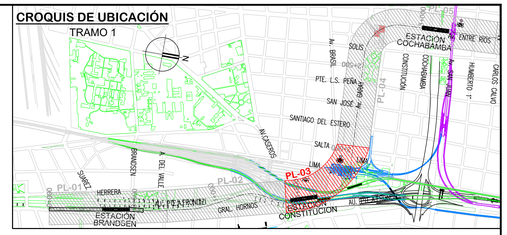

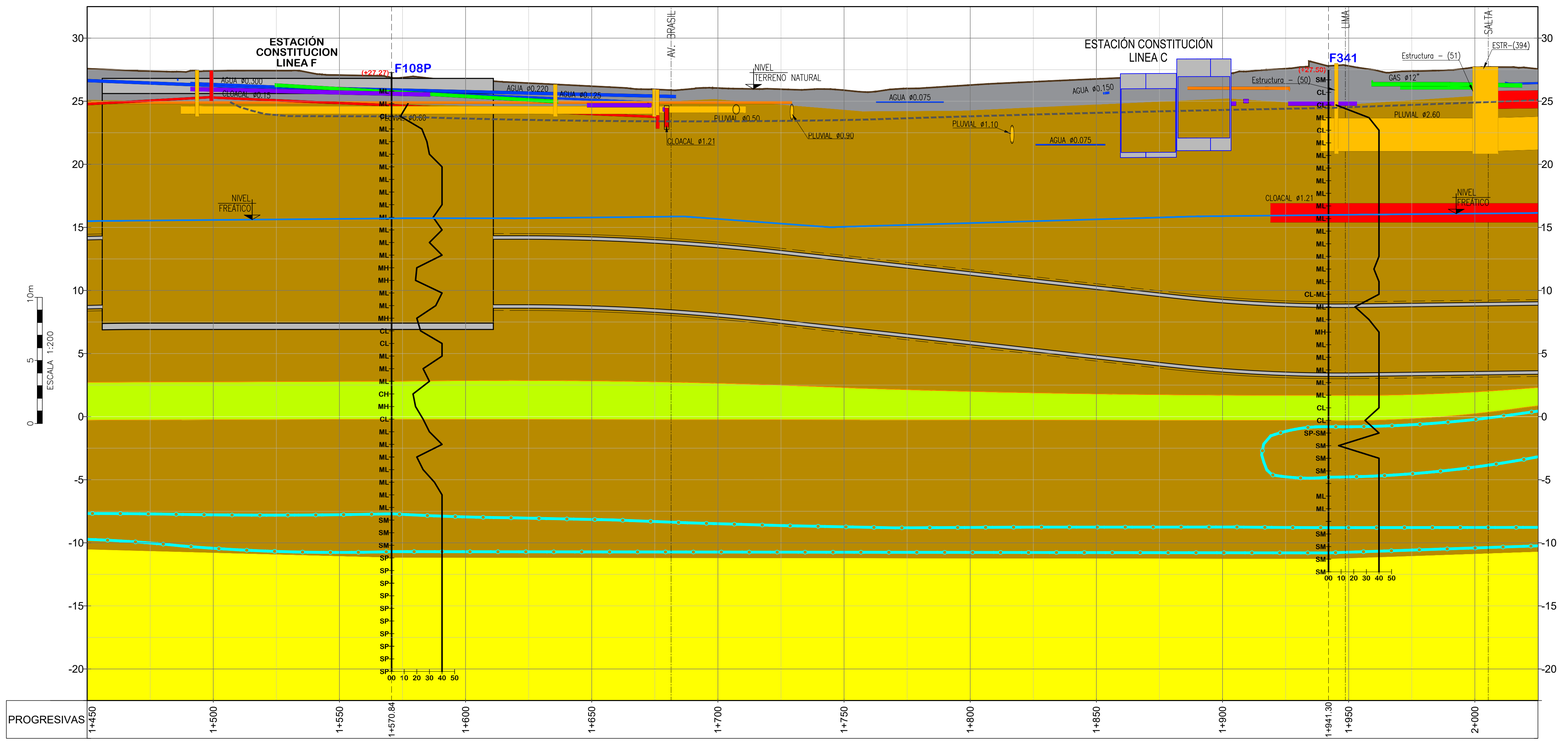

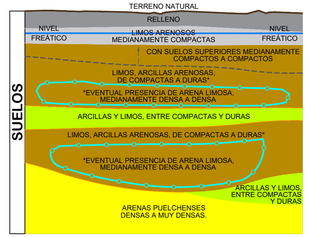

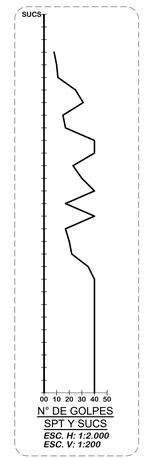

N° DE GOLPES
SPT Y SUCS
ESC. H: 1:2.000
ESC. V: 1:200

0 50 100m
ESCALA 1:2.000

REFERENCIAS SONDEOS:

- Fxx BOCA DE SONDEO MINAMÉRICA
- Fxx BOCA DE SONDEO MENDIGUREN
- Fxx BOCA DE SONDEO COPROGETTI

REFERENCIAS INTERFERENCIAS:

- RED DE AGUA CORRIENTE
- RED BT - MT - AT
- RED PLUVIAL
- RED CLOACAL
- RED DE GAS
- RED DE FIBRA OPTICA
- RED TELEFÓNICA

ALTIMETRÍA
ESC. HORIZ: 1:1.000
ESC. VERT: 1:200

NOTAS :

1- SISTEMA DE COORDENADAS DE LA CIUDAD DE BUENOS AIRES.

2- TODAS LAS MEDIDAS ESTÁN EXPRESADAS EN METROS, SALVO INDICACIÓN CONTRARIA

NOTAS: EL PRESENTE PLANO ES INDICATIVO, LA CONTRATISTA CONFECCIONARÁ LOS PLANOS DE DETALLE CONSTRUCTIVO, QUE DEBERÁN SER APROBADOS POR LA D.O.EM.P. Y / O LA INSPECCIÓN DE OBRA, EL PLANO PRESENTADO POR LA CONTRATISTA DEBERÁ EN UN TODO DE ACUERDO CON LA NORMATIVA VIGENTE.
TODAS LAS MEDIDAS Y NIVELES DE VERIFICARAN EN OBRA POR EL CONTRATISTA.
TODOS LOS DETALLES CONSTRUCTIVOS SERAN COORDINADOS Y CONFIRMADOS EN OBRA

PLANO NO APTO PARA CONSTRUCCION.

Ing. Mariano Miculicich
DIRECTOR

MODIFICACIONES:

NÚMERO	FECHA	DESCRIPCIÓN
2	22/05/025	DISEÑO INICIAL
1	18/11/2025	AJUSTE DE PROYECTO

Gobierno de la Ciudad de Buenos Aires

MINISTERIO DE INFRAESTRUCTURA
SUBSECRETARIA DE PROYECTOS Y OBRAS
DIRECCION GENERAL DE PROYECTOS

DGPRO

Obra: LINEA F				IF-2026-20223041-GCABA-APRA Plano N°
Plano: GEOTECNIA - ESTRATIGRAFÍA TRAMO 1 - PROGR. 1+450 A 2+050				LF-GL-T01-GTA-PL-003 003
Fecha: 18/11/2025	Eq. de Proyecto: UPU-ATEC-IATASA	Dibujó: D.B.	Revisó: R.H.B.	Escala: Indicadas

20/11/2025 12:42
LF-GL-T01-GTA-PL-001 A 009...1.dwg

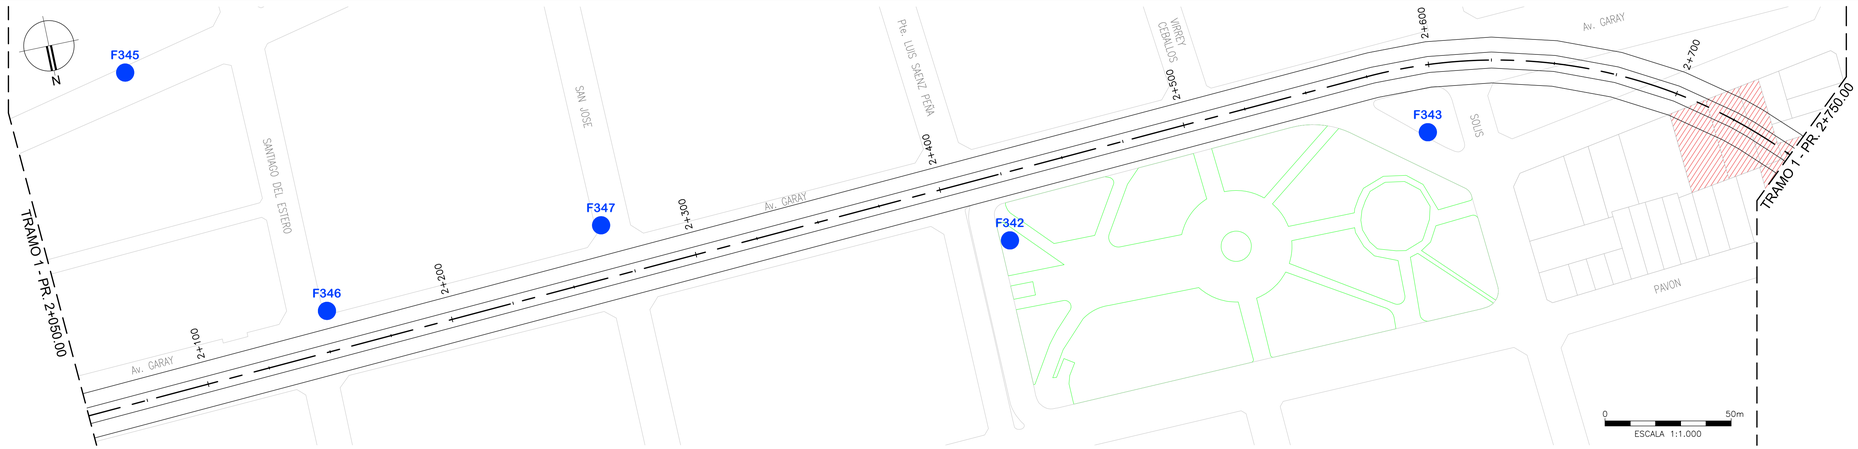

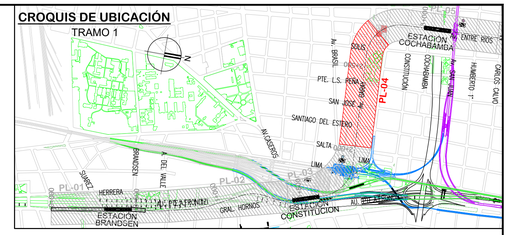

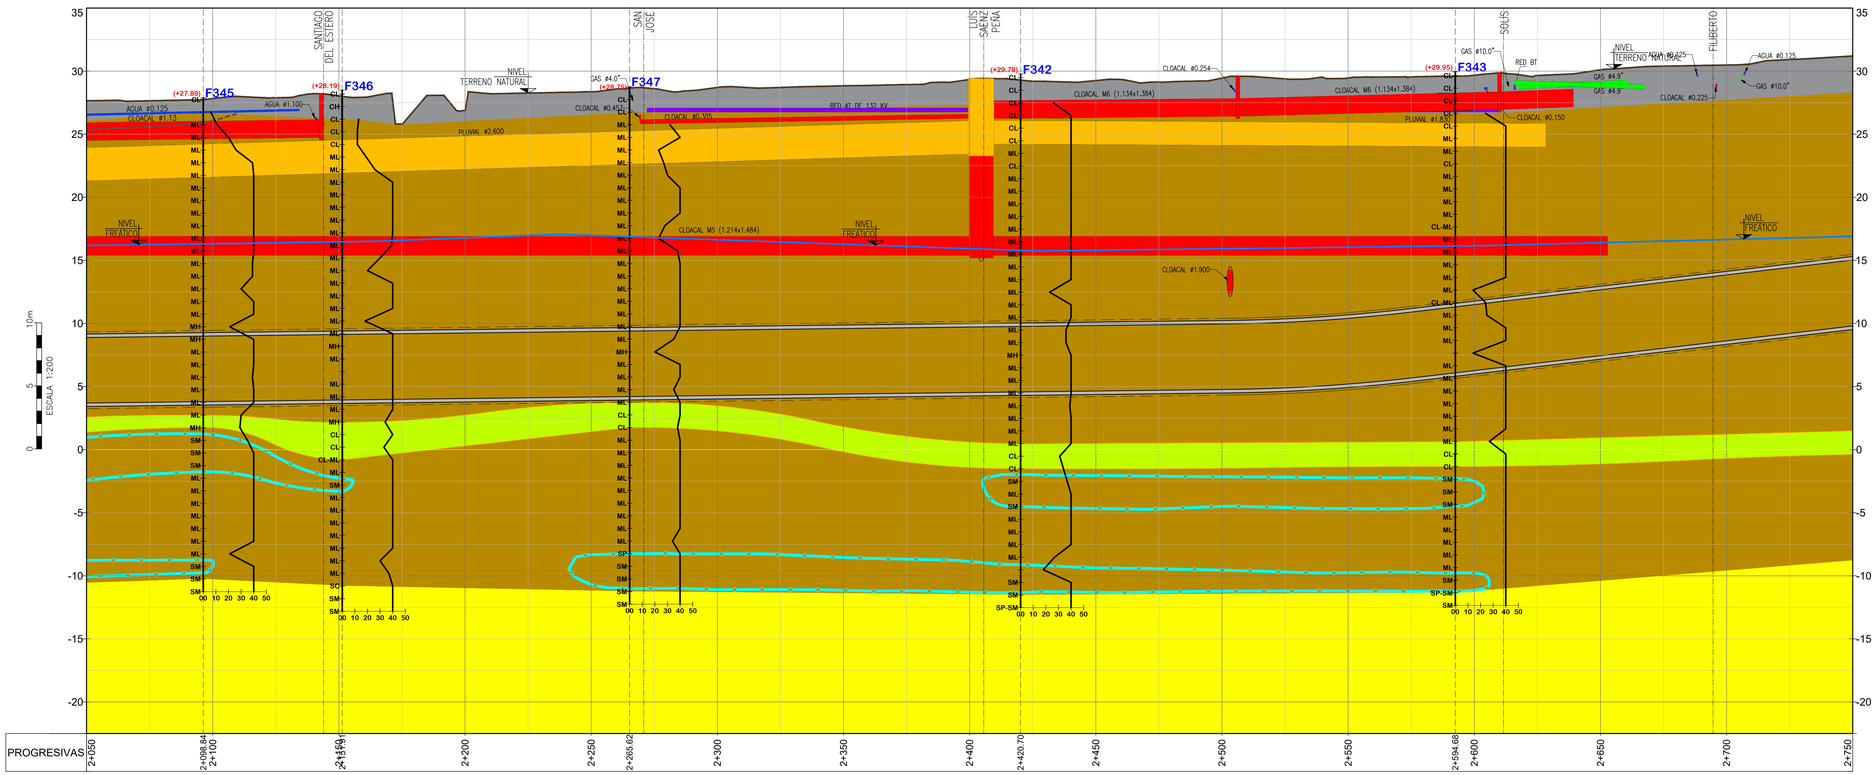

ALTIMETRÍA

ESC. HORIZ: 1:1.000
ESC. VERT: 1:200

REFERENCIAS INTERFERENCIAS:

- RED DE AGUA CORRIENTE
- RED BT - MT - AT
- RED PLUVIAL
- RED CLOACAL
- RED DE GAS
- RED DE FIBRA OPTICA
- RED TELEFÓNICA

REFERENCIAS SONDEOS:

- FXX BOCA DE SONDEO MINAMÉRICA
- FXX BOCA DE SONDEO MENDIGUREN
- FXX BOCA DE SONDEO COPROGETTI

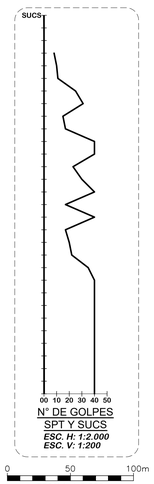

N° DE GOLPES
SPT Y SUCS
ESC. H: 1:2.000
ESC. V: 1:200

0 50 100m
ESCALA 1:2.000

NOTAS :

1- SISTEMA DE COORDENADAS DE LA CIUDAD DE BUENOS AIRES.
2- TODAS LAS MEDIDAS ESTÁN EXPRESADAS EN METROS, SALVO INDICACIÓN CONTRARIA

NOTAS:

EL PRESENTE PLANO ES REDACTADO, LA CONTRATISTA CONFECCIONARA LOS PLANOS DE DETALLE CONSTRUCTIVO, QUE DEBERAN SER APROBADOS POR LA D.O.EM Y LA INSPECCION DE OBRA, EL PLANO PRESENTADO POR LA CONTRATISTA DEBERA EN UN TODO SE AJUSTARSE CON LA NORMATIVA VIGENTE.
TODAS LAS MEDIDAS Y NIVELES DE VERIFICARAN EN OBRA POR EL CONTRATISTA.
TODOS LOS DETALLES CONSTRUCTIVOS SERAN COORDINADOS Y CONFIRMADOS EN OBRA

PLANO NO APTO PARA CONSTRUCCION.

Ing. Mariano Miculicich
DIRECTOR

MODIFICACIONES:

ACUERDO	FECHA	DESCRIPCION
2	22/05/025	DISEÑO PARCIAL
1	18/11/2025	AJUSTE DE PROYECTO

MINISTERIO DE INFRAESTRUCTURA
SUBSECRETARIA DE PROYECTOS Y OBRAS
DIRECCION GENERAL DE PROYECTOS

DGPRO

Obra: LINEA F				IF-2026-20223041-GCABA-APRA	Plano N°:
Plano: GEOTECNIA - ESTRATIGRAFÍA TRAMO 1 - PROGR. 2+050 A 2+750				LF-GL-T01-GTA-PL-004	004
Fecha: 18/11/2025	Eq. de Proyecto: UPU-ATEC-IATASA	Dibujó: D.B.	Revisó: R.H.B.	Escala: Indicadas	

20/11/2025 12:42
LF-GL-T01-GTA-PL-001 A 009...1.dwg

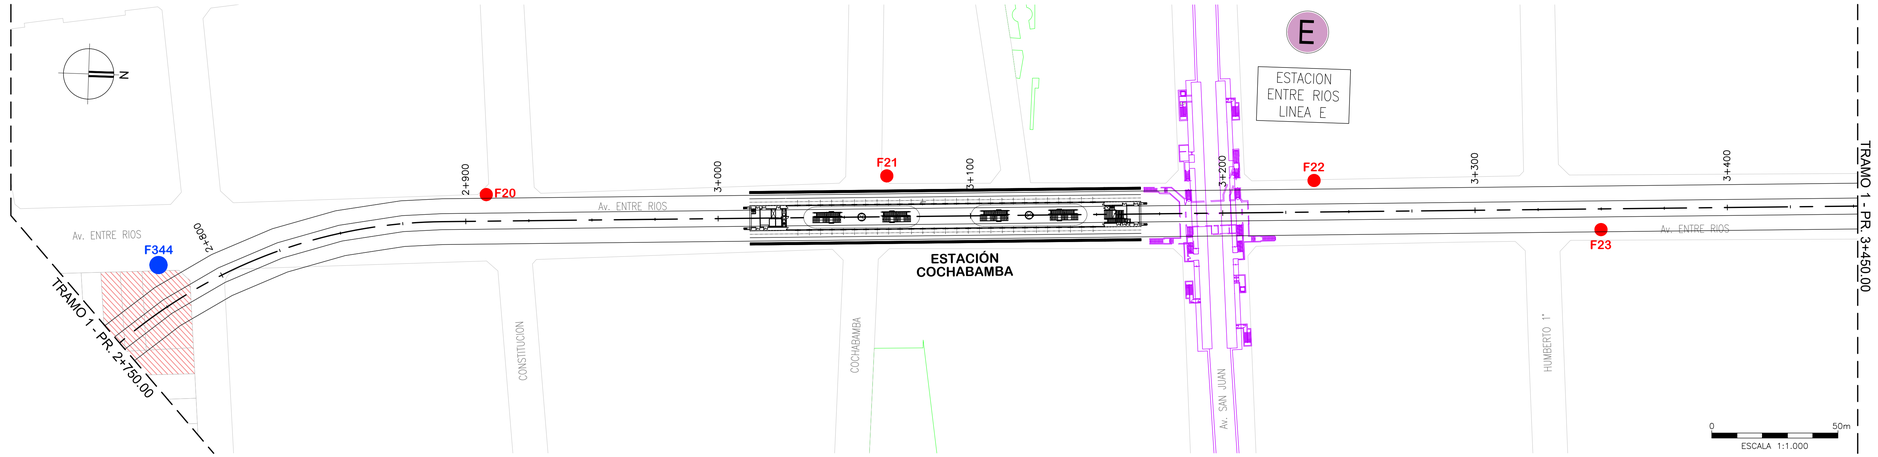

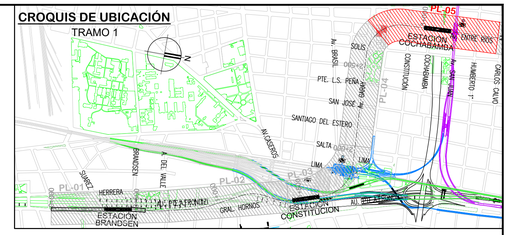

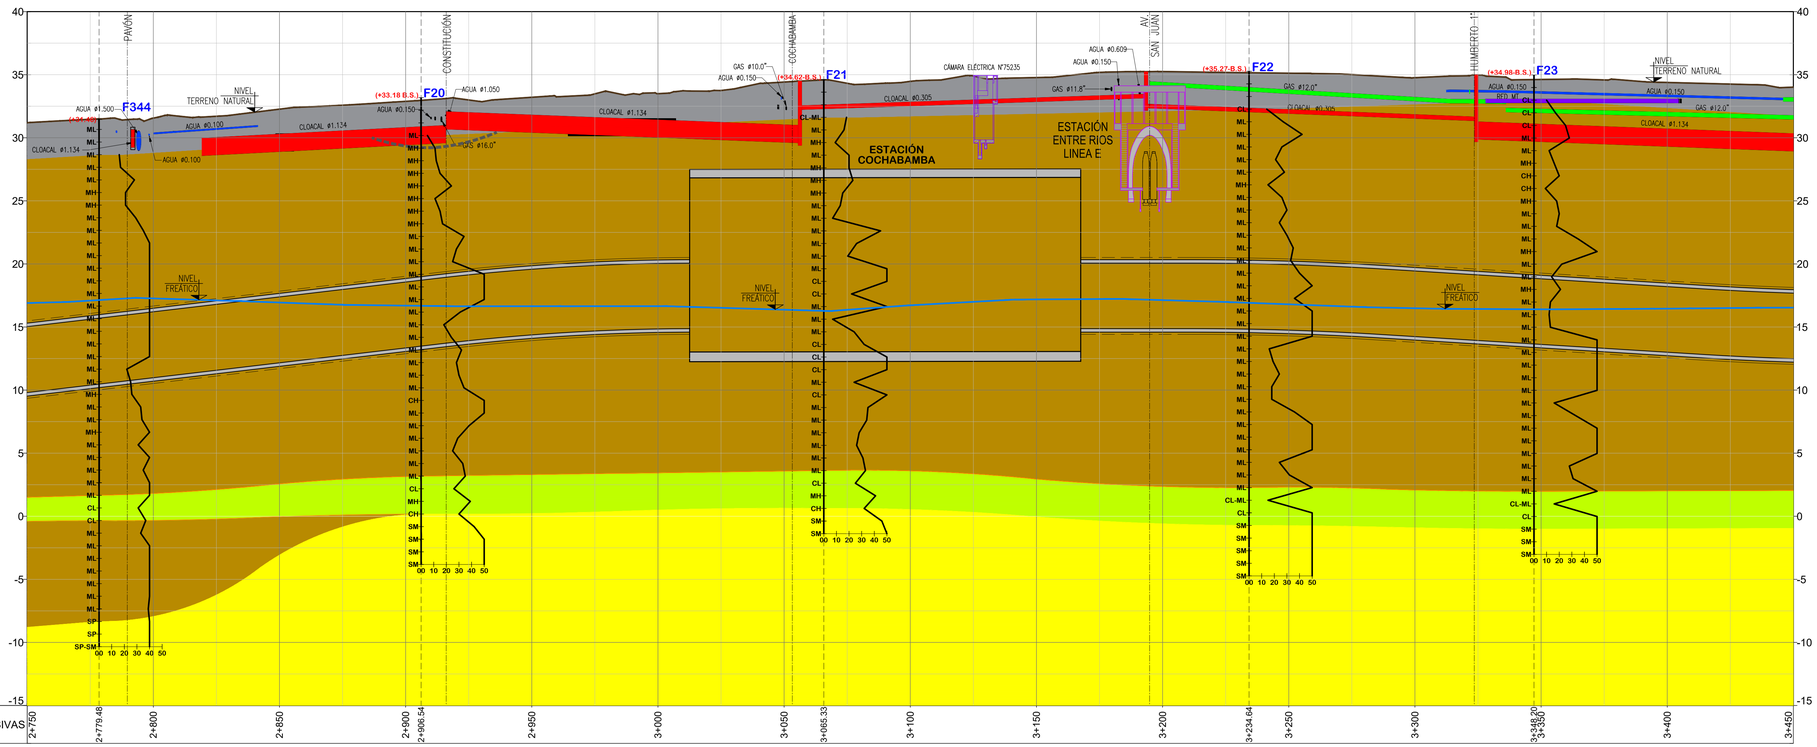

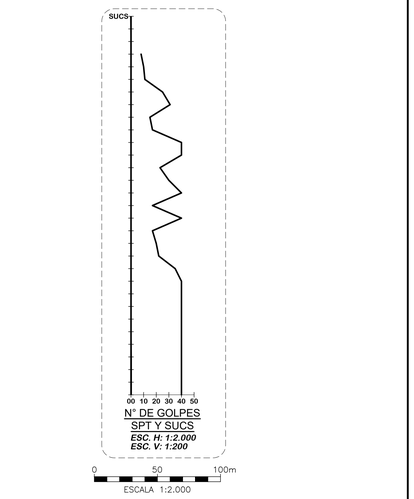

REFERENCIAS SONDEOS:

- Fxx BOCA DE SONDEO MINAMÉRICA
- Fxx BOCA DE SONDEO MENDIGUREN
- Fxx BOCA DE SONDEO COPROGETTI

REFERENCIAS INTERFERENCIAS:

- RED DE AGUA CORRIENTE
- RED CLOACAL
- RED DE FIBRA OPTICA
- RED BT - MT - AT
- RED DE GAS
- RED TELEFÓNICA
- RED PLUVIAL

ALTIMETRÍA
ESC. HORIZ: 1:1.000
ESC. VERT: 1:200

NOTAS :
1- SISTEMA DE COORDENADAS DE LA CIUDAD DE BUENOS AIRES.
2- TODAS LAS MEDIDAS ESTÁN EXPRESADAS EN METROS, SALVO INDICACIÓN CONTRARIA

NOTAS :
1- SISTEMA DE COORDENADAS DE LA CIUDAD DE BUENOS AIRES.
2- TODAS LAS MEDIDAS ESTÁN EXPRESADAS EN METROS, SALVO INDICACIÓN CONTRARIA

NOTAS: EL PRESENTE PLANO ES INDICATIVO. LA CONTRATISTA CONFECCIONARÁ LOS PLANOS DE DETALLE DEFINITIVO, QUE DEBERÁN SER APROBADOS POR LA D.G.D.SIF.2.1 LA INSPECCIÓN DE OBRA, EL PLANO PRESENTADO POR LA CONTRATISTA ESTARÁ EN UN TODO DE ACUERDO CON LA NORMATIVA VIGENTE. TODAS LAS MEDIDAS Y NIVELES SE VERIFICARÁN EN OBRA POR EL CONTRATISTA. TODOS LOS DETALLES CONSTRUCTIVOS SERÁN COORDINADOS Y CONVENCIONADOS EN OBRA

PLANO NO APTO PARA CONSTRUCCION.

Ing. Mariano Miculicich
DIRECTOR

MODIFICACIONES:	REVISIÓN	FECHA	DESCRIPCIÓN
	0	22/09/2025	EMISIÓN INICIAL
	1	18/11/2025	AJUSTE DE PROYECTO

MINISTERIO DE INFRAESTRUCTURA
SUBSECRETARIA DE PROYECTOS Y OBRAS
DIRECCION GENERAL DE PROYECTOS

DGPRO

Obra: LÍNEA F		IF-2026-20223041-GCABA-APRA	Plano N°: 005
Plano: GEOTECNIA - ESTRATIGRAFÍA TRAMO 1 - PROGR. 2+750 A 3+450		LF-GL-T01-GTA-PL-005	
Fecha: 18/11/2025	Eq. de Proyecto: UPU-ATEC-IATASA	Dibujó: D.B.	Revisó: R.H.B. Escala: Indicadas

20/11/2025, 12:42
LF-GL-T01-GTA-PL-001 A 009_1.dwg

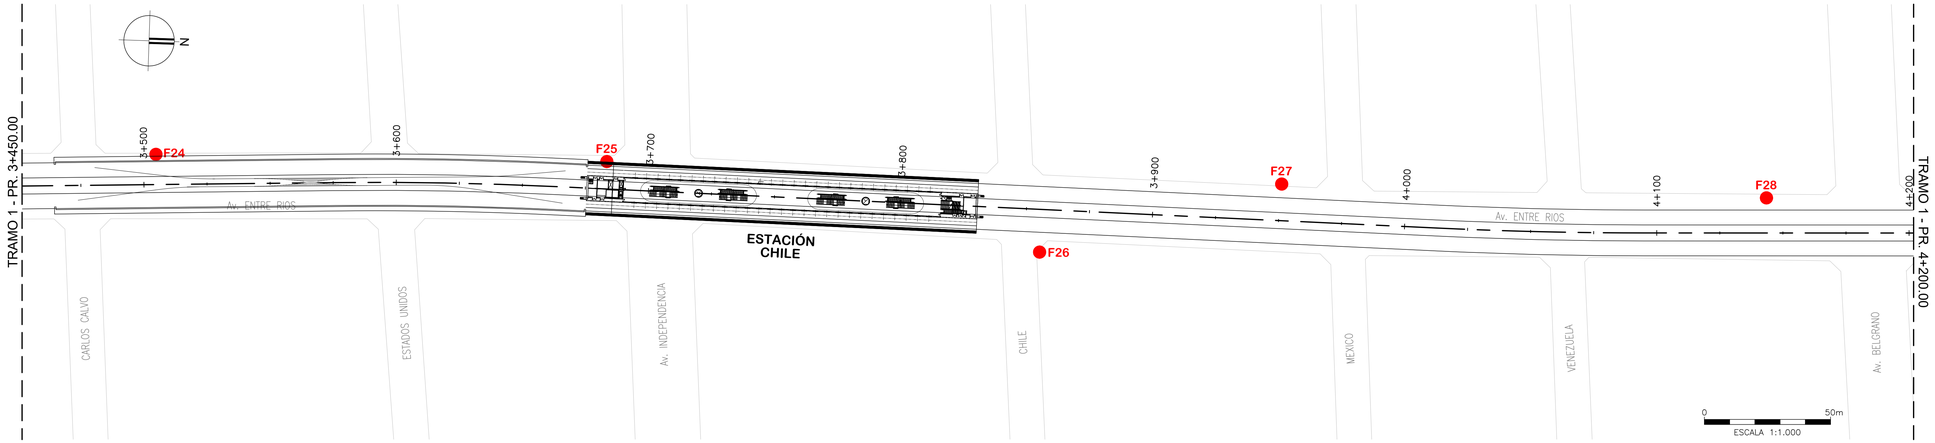

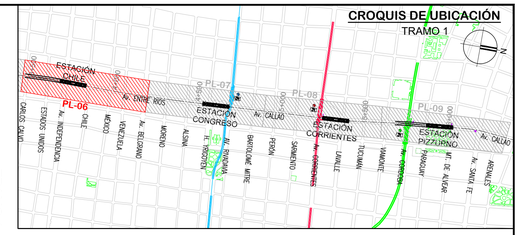

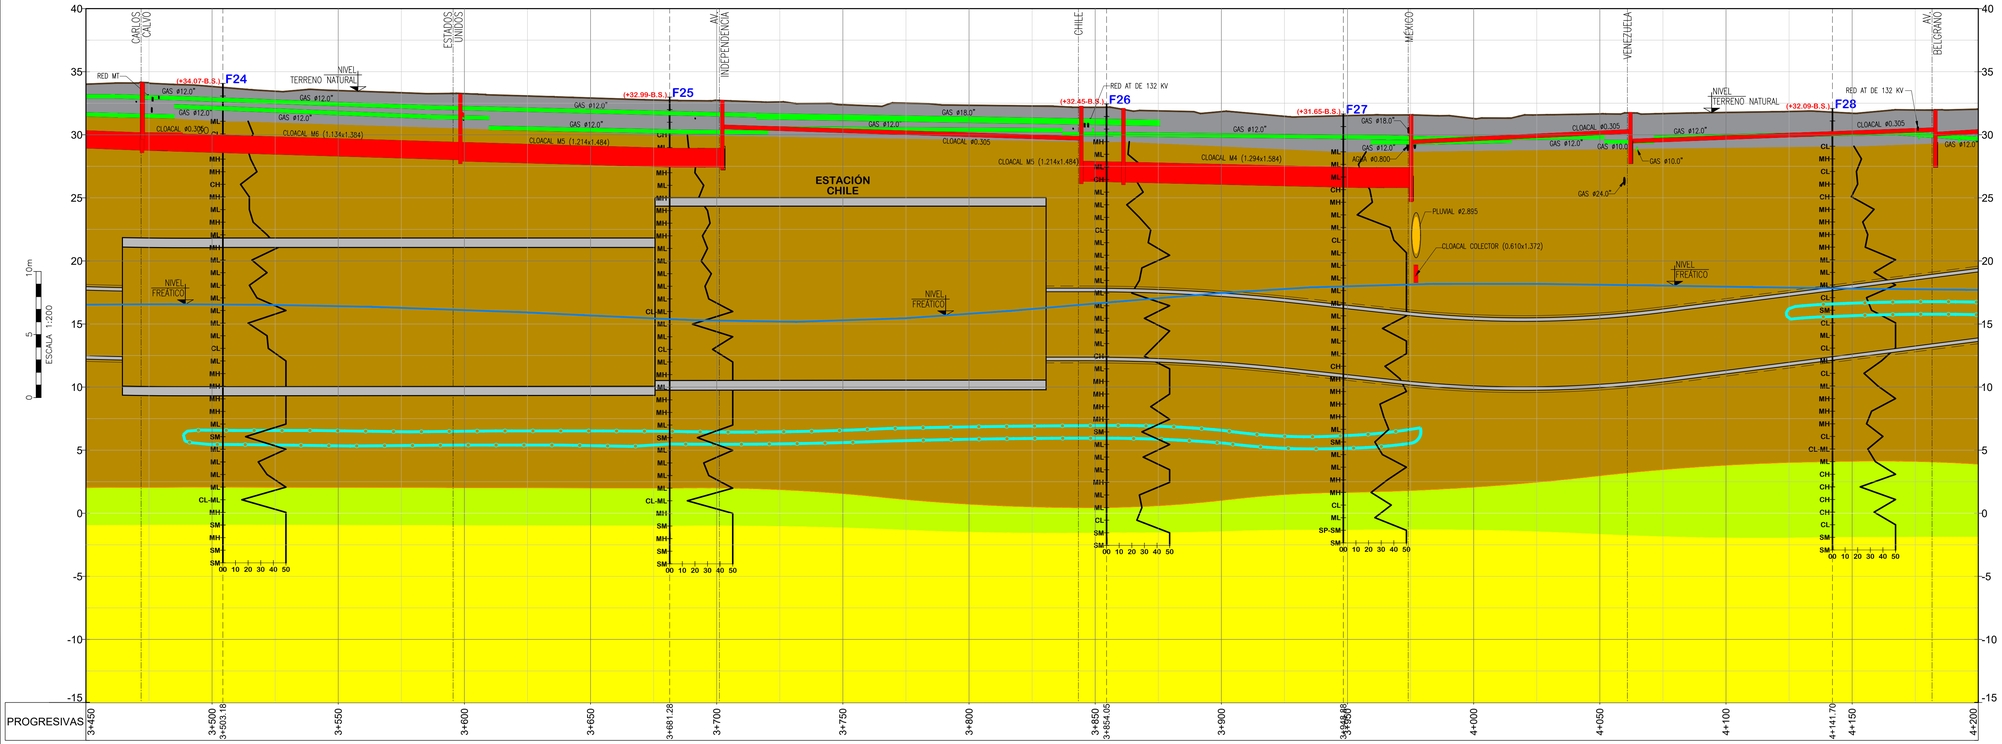

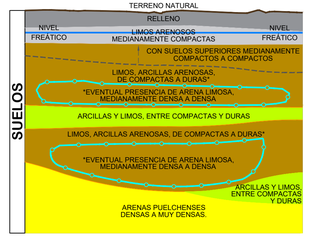

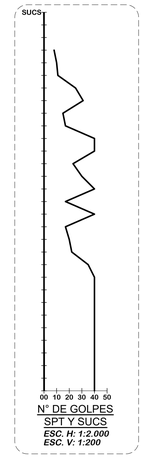

N° DE Ggolpes
SPT Y SUCS
ESC. H: 1:2.000
ESC. V: 1:200

0 50 100m
ESCALA 1:2.000

REFERENCIAS SONDEOS:

- Fxx BOCA DE SONDEO MINAMÉRICA
- Fxx BOCA DE SONDEO MENDIGUREN
- Fxx BOCA DE SONDEO COPROGETTI

REFERENCIAS INTERFERENCIAS:

- RED DE AGUA CORRIENTE
- RED BT - MT - AT
- RED PLUVIAL
- RED CLOACAL
- RED DE GAS
- RED DE FIBRA OPTICA
- RED TELEFÓNICA

ALTIMETRÍA
ESC. HORIZ: 1:1.000
ESC. VERT: 1:200

NOTAS :
1- SISTEMA DE COORDENADAS DE LA CIUDAD DE BUENOS AIRES.
2- TODAS LAS MEDIDAS ESTÁN EXPRESADAS EN METROS, SALVO INDICACIÓN CONTRARIA

NOTAS :
1- SISTEMA DE COORDENADAS DE LA CIUDAD DE BUENOS AIRES.
2- TODAS LAS MEDIDAS ESTÁN EXPRESADAS EN METROS, SALVO INDICACIÓN CONTRARIA

NOTAS: EL PRESENTE PLANO ES INDICATIVO. LA CONTRATISTA CONFECCIONARÁ LOS PLANOS DE DETALLE CONSTRUCTIVO, QUE DEBERÁN SER APROBADOS POR LA D.G.OBR.3° LA INSPECCIÓN DE OBRA, EL PLANO PRESENTADO POR LA CONTRATISTA DEBERÁ EN UN TODO DE ACUERDO CON LA NORMATIVA VIGENTE.
TODAS LAS MEDIDAS Y NIVELES DE VEREDA SERÁN EN OBRA POR EL CONTRATISTA.
TODOS LOS DETALLES CONSTRUCTIVOS SERÁN COORDINADOS Y CONFIRMADOS EN OBRA

PLANO NO APTO PARA CONSTRUCCION.

Ing. Mariano Miculicich
DIRECTOR

MODIFICACIONES:

ACUERDO	FECHA	DESCRIPCIÓN
2	22/05/025	EMISIÓN INICIAL
1	18/11/2025	AJUSTE DE PROYECTO

MINISTERIO DE INFRAESTRUCTURA
SUBSECRETARÍA DE PROYECTOS Y OBRAS
DIRECCIÓN GENERAL DE PROYECTOS

DGPRO

Obra: LINEA F				IF-2026-20223041-GCABA-APRA	Plano N° 006
Plano: GEOTECNIA - ESTRATIGRAFÍA TRAMO 1 - PROGR. 3+450 A 4+200				LF-GL-T01-GTA-PL-006	
Fecha: 18/11/2025	Eq. de Proyecto: UPU-ATEC-IATASA	Dibujó: D.B.	Revisó: R.H.B.	Escala: Indicadas	

20/11/2025 12:42
LF-GL-T01-GTA-PL-001 A 009...1.dwg

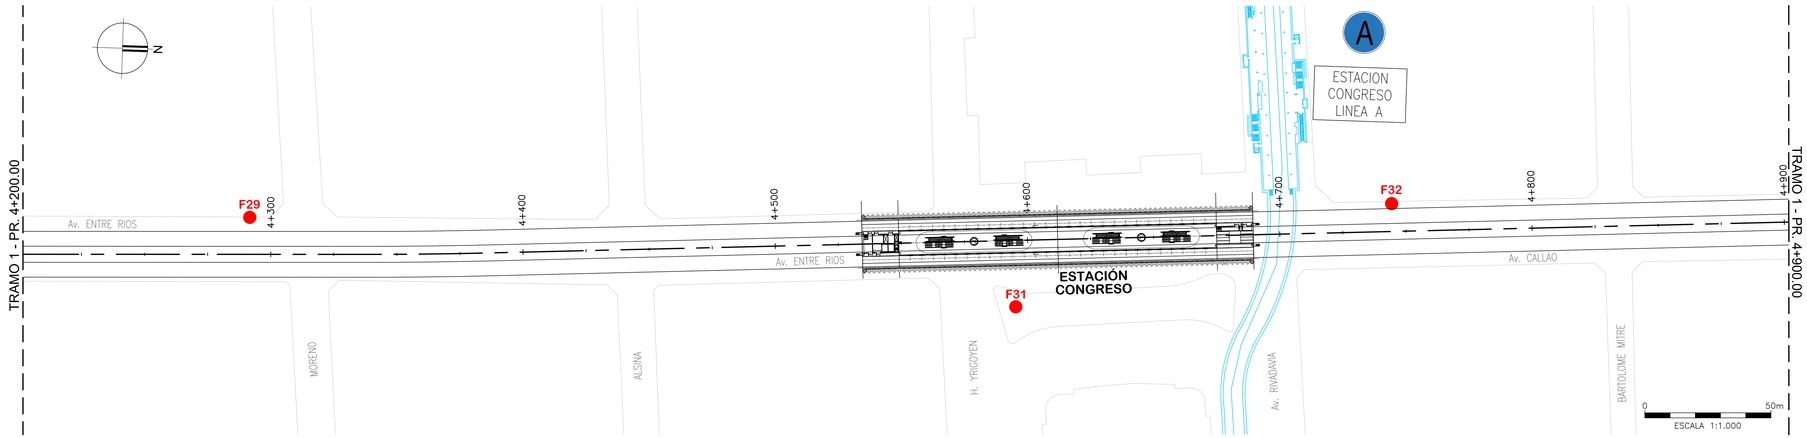

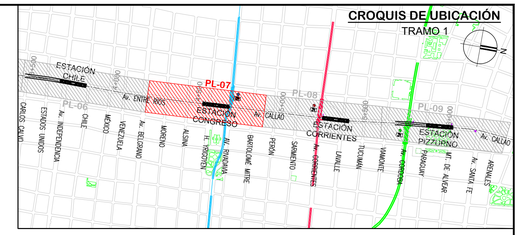

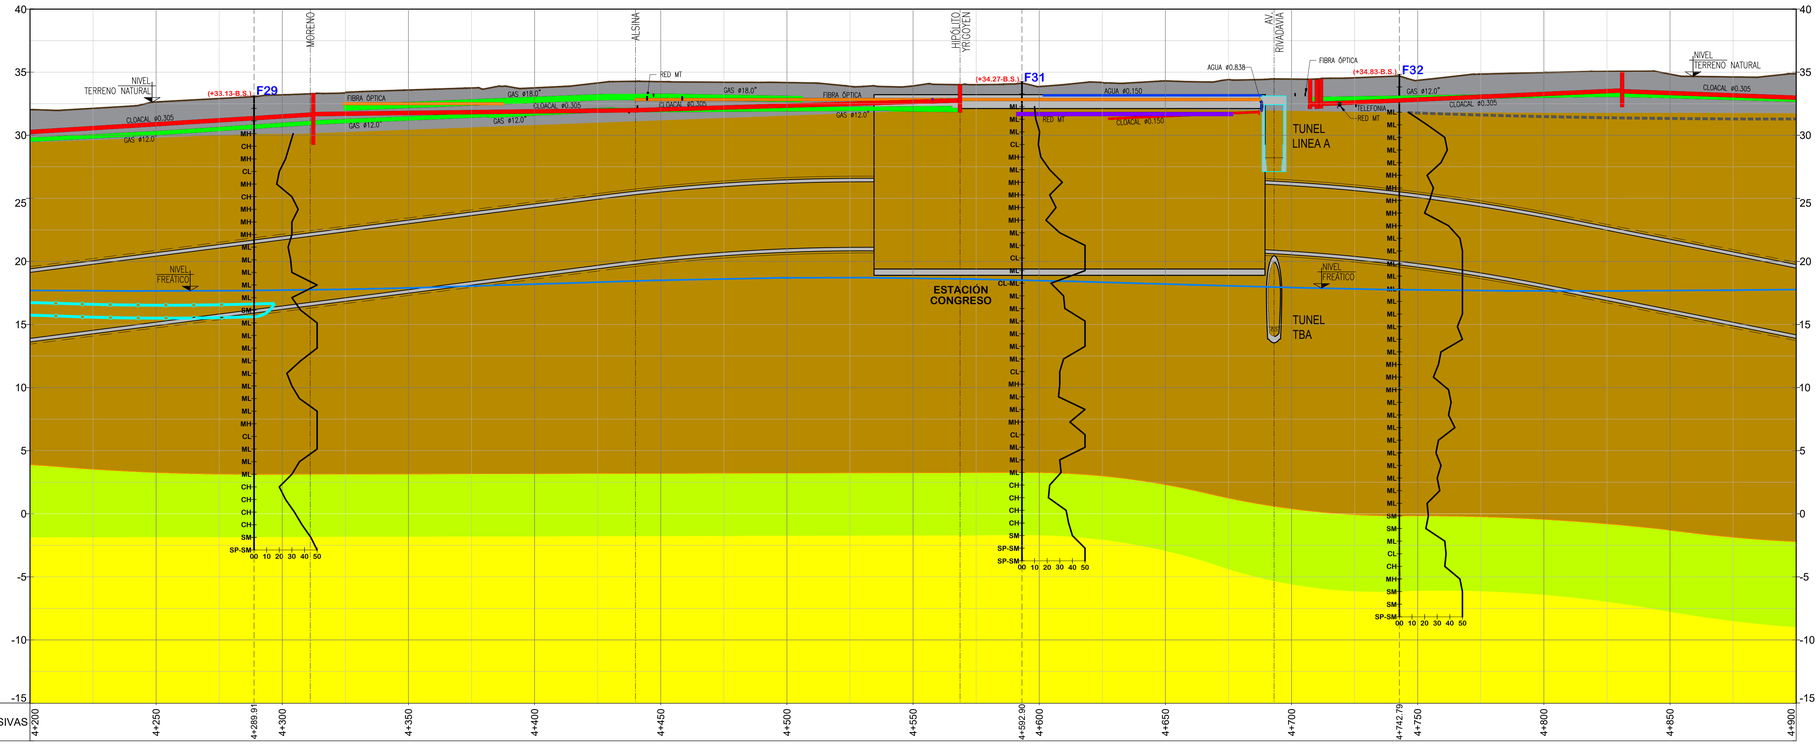

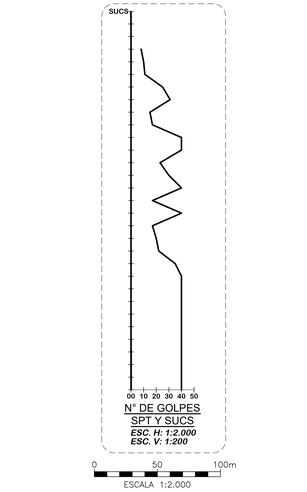

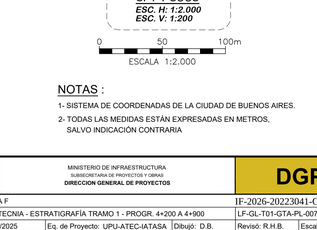

REFERENCIAS SONDEOS:

- Fxx BOCA DE SONDEO MINAMÉRICA
- Fxx BOCA DE SONDEO MENDIGUREN
- Fxx BOCA DE SONDEO COPROGETTI

REFERENCIAS INTERFERENCIAS:

- RED DE AGUA CORRIENTE
- RED CLOACAL
- RED DE FIBRA OPTICA
- RED BT - MT - AT
- RED DE GAS
- RED TELEFÓNICA
- RED PLUVIAL

ALTIMETRÍA

ESC. HORIZ. 1:1.000
ESC. VERT. 1:200

NOTAS :

1- SISTEMA DE COORDENADAS DE LA CIUDAD DE BUENOS AIRES.

2- TODAS LAS MEDIDAS ESTÁN EXPRESADAS EN METROS, SALVO INDICACIÓN CONTRARIA

NOTAS :

1- SISTEMA DE COORDENADAS DE LA CIUDAD DE BUENOS AIRES.

2- TODAS LAS MEDIDAS ESTÁN EXPRESADAS EN METROS, SALVO INDICACIÓN CONTRARIA

NOTAS: EL PRESENTE PLANO ES INDICATIVO. LA CONTRATISTA CONFECCIONARA LOS PLANOS DE DETALLE CORRECTIVO, QUE DEBERAN SER APROBADOS POR LA D.G.OBR. LA INSPECCION DE OBRA, EL PLANO PRESENTADO POR LA CONTRATISTA ESTARA EN UN TODO DE ACUERDO CON LA NORMATIVA VIGENTE.
TODAS LAS MEDIDAS Y NIVELES SE VERIFICARAN EN OBRA POR EL CONTRATISTA.
TODOS LOS DETALLES CONSTRUCTIVOS SERAN COORDINADOS Y CONVENCIONADOS EN OBRA

PLANO NO APTO PARA CONSTRUCCION.

Ing. Mariano Miculicich
DIRECTOR

MODIFICACIONES:	REVISION	FECHA	DESCRIPCION
	0	22/05/25	EMISION INICIAL
	1	18/11/2025	AJUSTE DE PROYECTO

MINISTERIO DE INFRAESTRUCTURA
SUBSECRETARIA DE PROYECTOS Y OBRAS
DIRECCION GENERAL DE PROYECTOS

DGPRO

Obra: LÍNEA F			IF-2026-20223041-GCABA-APRA Plano N°
Plano: GEOTECNIA - ESTRATIGRAFÍA TRAMO 1 - PROGR. 4+200 A 4+900			LF-GL-T01-GTA-PL-007 007
Fecha: 18/11/2025	Eq. de Proyecto: UPU-ATEC-IATASA	Dibujó: D.B.	Revisó: R.H.B. Escala: Indicadas

20/11/2025 12:42
LF-GL-T01-GTA-PL-001 A 099_1.dwg

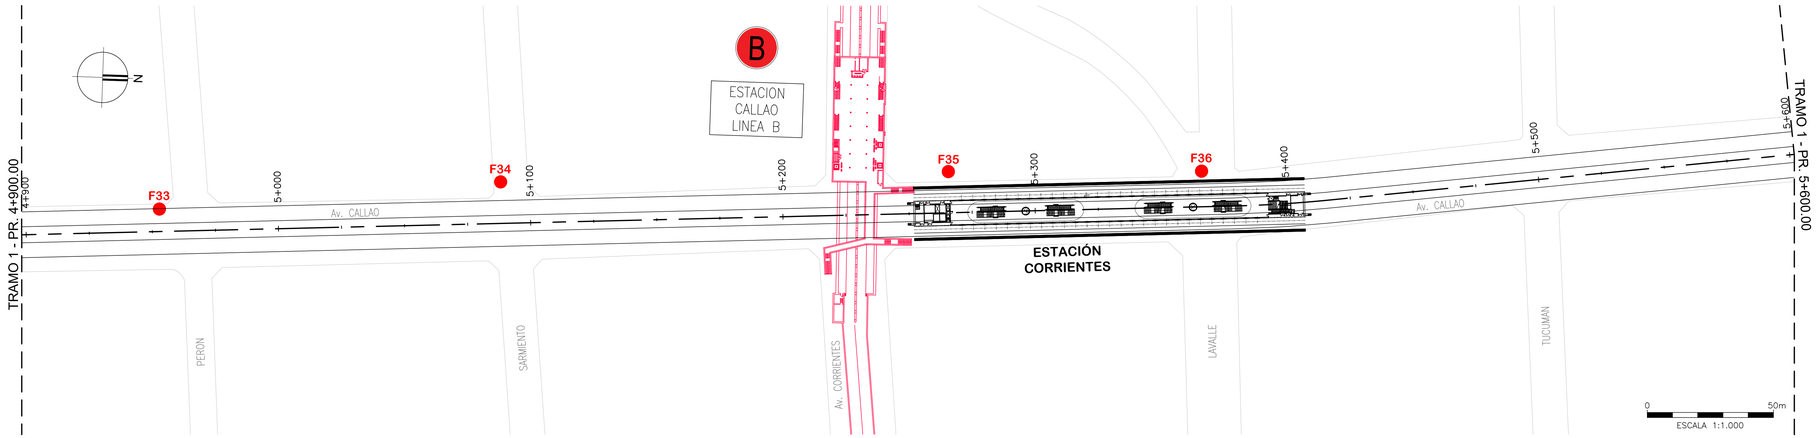

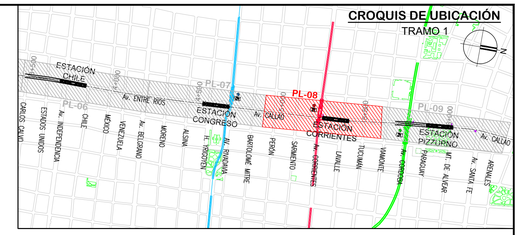

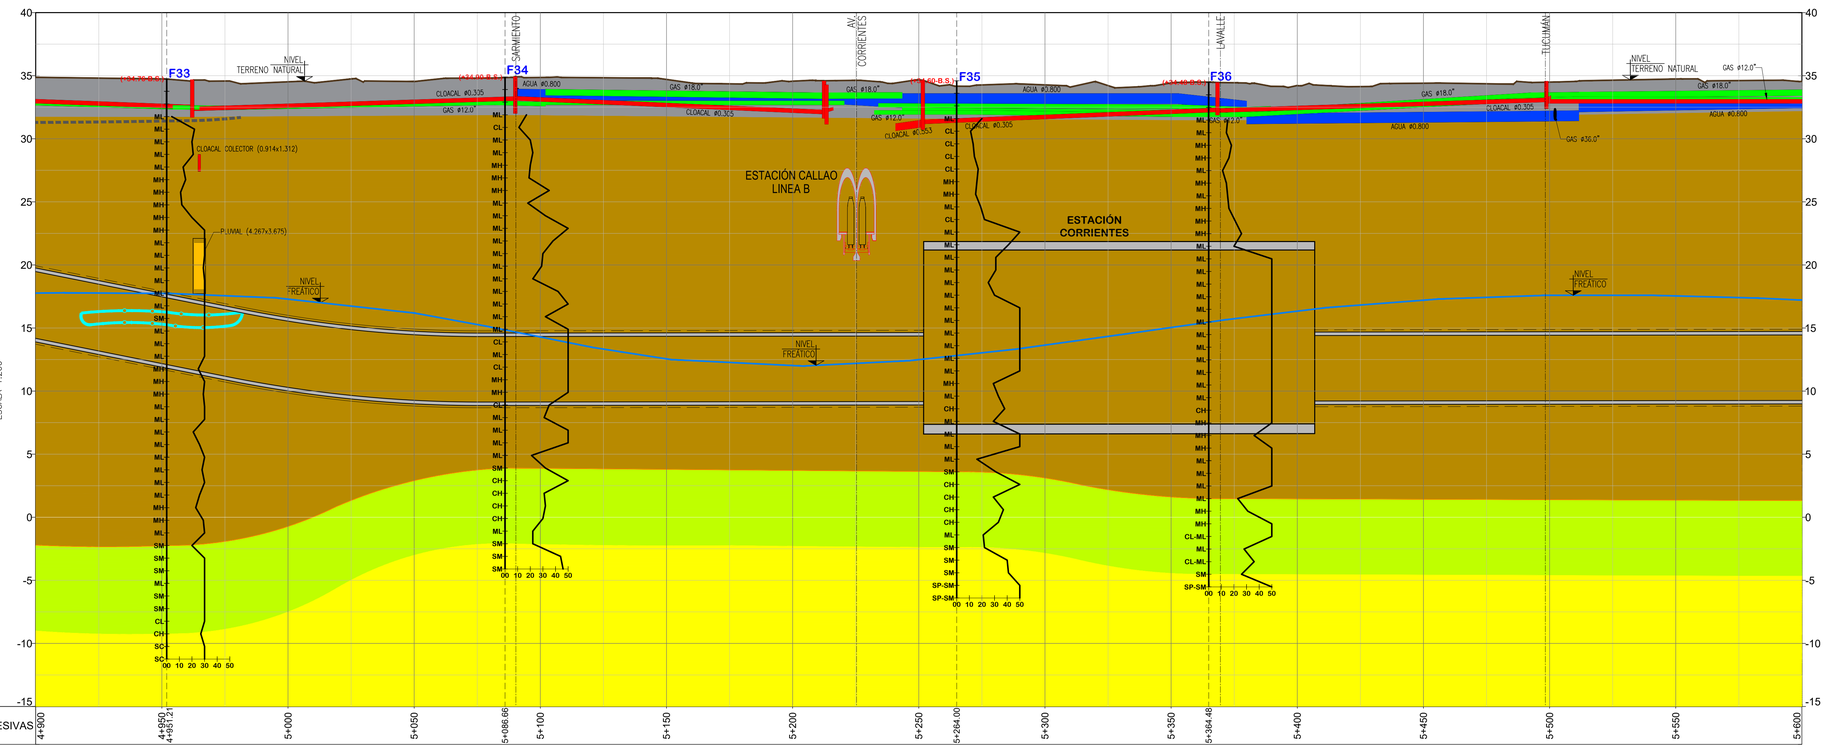

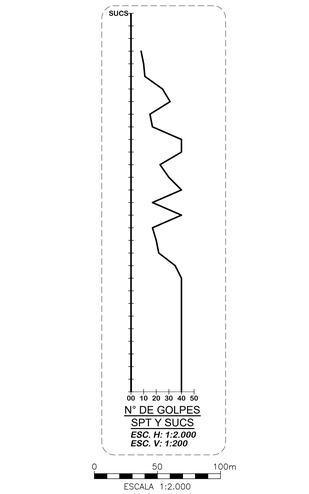

REFERENCIAS SONDEOS:

- FXX BOCA DE SONDEO MINAMÉRICA
- FXX BOCA DE SONDEO MENDIGUREN
- FXX BOCA DE SONDEO COPROGETTI

REFERENCIAS INTERFERENCIAS:

- RED DE AGUA CORRIENTE
- RED CLOACAL
- RED DE FIBRA OPTICA
- RED BT - MT - AT
- RED DE GAS
- RED TELEFÓNICA
- RED PLUVIAL

ALTIMETRÍA

ESC. HORIZ: 1:1.000
ESC. VERT: 1:200

NOTAS :

1- SISTEMA DE COORDENADAS DE LA CIUDAD DE BUENOS AIRES.
2- TODAS LAS MEDIDAS ESTÁN EXPRESADAS EN METROS, SALVO INDICACIÓN CONTRARIA

NOTAS :

1- SISTEMA DE COORDENADAS DE LA CIUDAD DE BUENOS AIRES.
2- TODAS LAS MEDIDAS ESTÁN EXPRESADAS EN METROS, SALVO INDICACIÓN CONTRARIA

NOTAS: EL PRESENTE PLANO ES INDICATIVO. LA CONTRATISTA CONFECCIONARÁ LOS PLANOS DE DETALLE DEFINITIVO, QUE DEBERÁN SER APROBADOS POR LA D.G.INF.U Y LA INSPECCIÓN DE OBRA, EL CUAL NO DEBE CONSTRUIR SIN LA CONFORMIDAD ESTAMPADA EN UN TUBO DE ACUERDO CON LA NORMATIVA VIGENTE.
TODAS LAS MEDIDAS Y NIVELES SE VERIFICARÁN EN OBRA POR EL CONTRATISTA.
TODOS LOS DETALLES CONSTRUCTIVOS SERÁN COORDINADOS Y COMPATIBILIZADOS EN OBRA.

PLANO NO APTO PARA CONSTRUCCION.

Ing. Mariano Miculicich
DIRECTOR

MODIFICACIONES:

REVISIÓN	FECHA	DESCRIPCIÓN
0	22/09/25	EMISIÓN INICIAL
1	18/11/25	AJUSTE DE PROYECTO

Gobierno de la Ciudad de Buenos Aires

MINISTERIO DE INFRAESTRUCTURA
SUBSECRETARIA DE PROYECTOS Y OBRAS
DIRECCION GENERAL DE PROYECTOS

DGPRO

Obra: LÍNEA F			IF-2026-20223041-GCABA-APRA Plano N°
Plano: GEOTECNIA - ESTRATIGRAFÍA TRAMO 1 - PROGR. 4+900 A 5+600			LF-GL-T01-GTA-PL-008 008
Fecha: 18/11/2025	Eq. de Proyecto: UPU-ATEC-IATASA	Dibujó: D.B.	Revisó: R.H.B. Escala: Indicadas

20/11/2025, 12:42
LF-GL-T01-GTA-PL-001 A 009_1.dwg

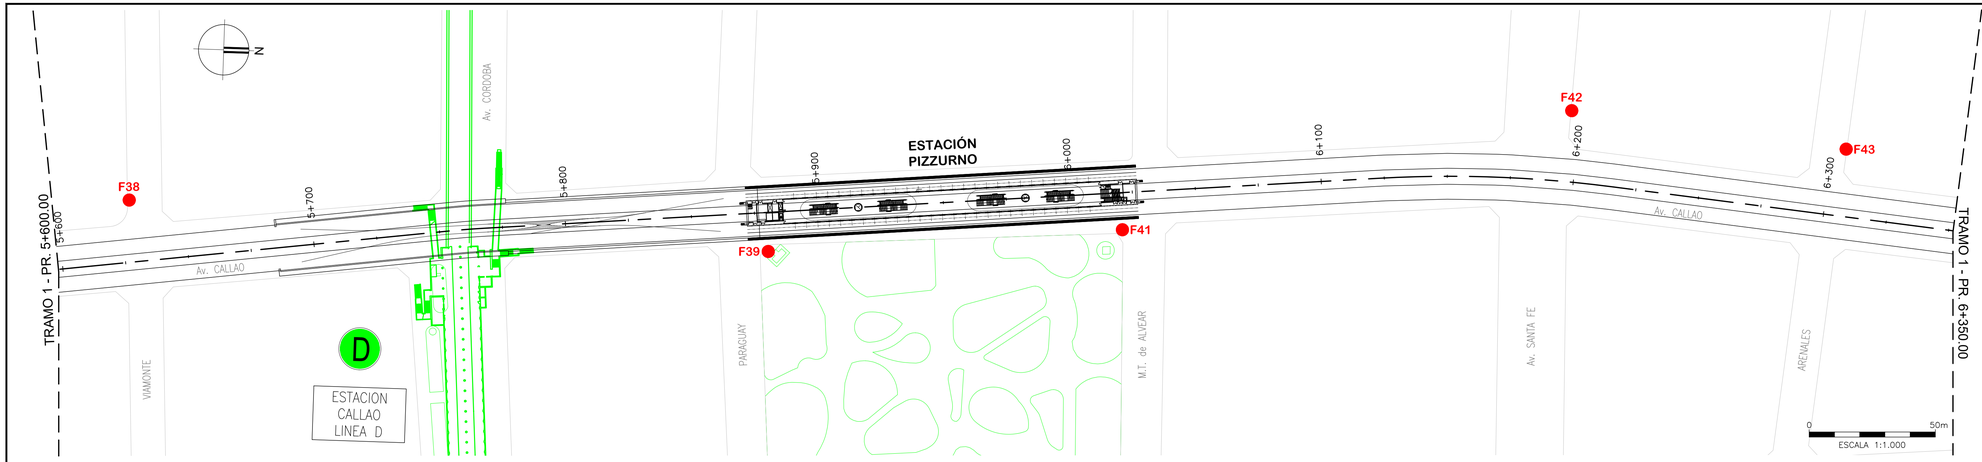

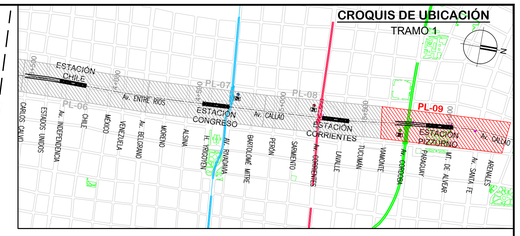

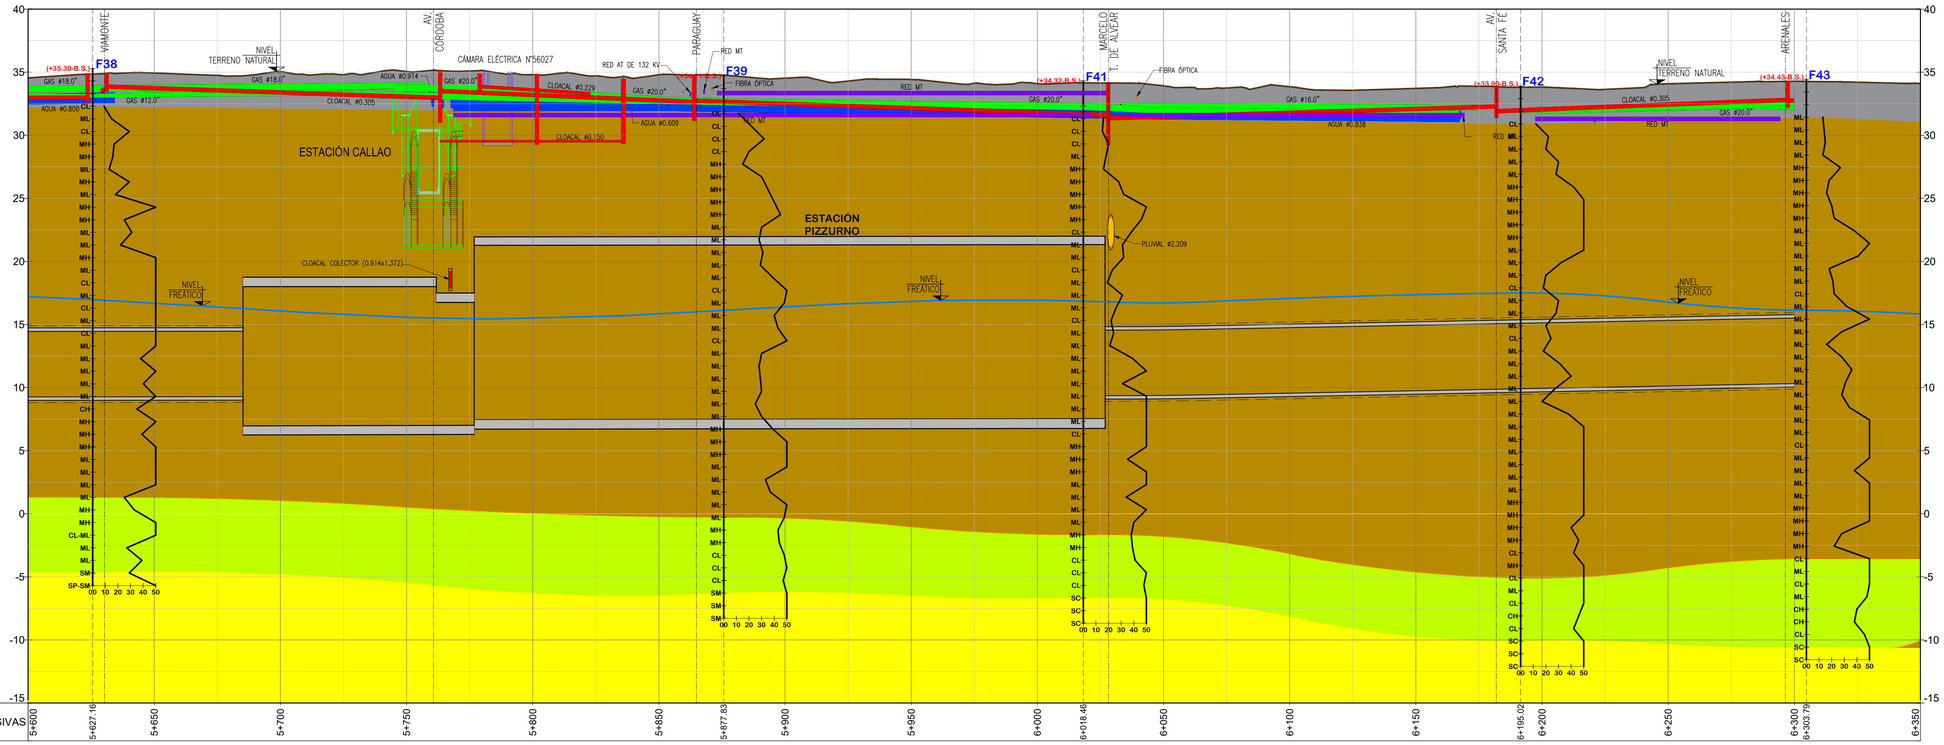

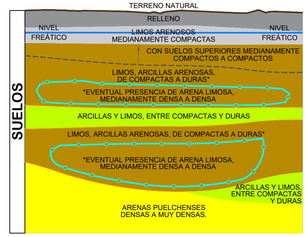

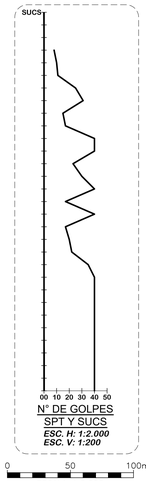

N° DE GOLPES
SPT Y SUCS
ESC. H: 1:2.000
ESC. V: 1:200

REFERENCIAS SONDEOS:

- Fxx BOCA DE SONDEO MINAMÉRICA
- Fxx BOCA DE SONDEO MENDIGUREN
- Fxx BOCA DE SONDEO COPROGETTI

REFERENCIAS INTERFERENCIAS:

- RED DE AGUA CORRIENTE
- RED CLOACAL
- RED DE FIBRA OPTICA
- RED BT - MT - AT
- RED DE GAS
- RED TELEFÓNICA
- RED PLUVIAL

ALTIMETRÍA
ESC. HORIZ: 1:1.000
ESC. VERT: 1:200

NOTAS :
1- SISTEMA DE COORDENADAS DE LA CIUDAD DE BUENOS AIRES.
2- TODAS LAS MEDIDAS ESTÁN EXPRESADAS EN METROS, SALVO INDICACIÓN CONTRARIA

NOTAS :
1- SISTEMA DE COORDENADAS DE LA CIUDAD DE BUENOS AIRES.
2- TODAS LAS MEDIDAS ESTÁN EXPRESADAS EN METROS, SALVO INDICACIÓN CONTRARIA

NOTAS: EL PRESENTE PLANO ES INDICATIVO. LA CONTRATISTA CONFECCIONARÁ LOS PLANOS DE DETALLE DEFINITIVO, QUE DEBERÁN SER APROBADOS POR LA D.G.S.M. Y LA D.G.I.M. PREVIO A LA EJECUCIÓN DE LAS OBRAS. EL PRESENTE PLANO DEBE SER LEÍDO EN CONJUNTO CON LA TOTALIDAD DE LA DOCUMENTACIÓN TÉCNICA Y ADMINISTRATIVA QUE INTEGRA EL CONTRATO. TODOS LOS ANTECEDENTES, PLANOS DE REFERENCIA EN OBRA POR EL CONTRATISTA. TODOS LOS DETALLES CONSTRUCTIVOS SERÁN COORDINADOS Y CONFIRMADOS EN OBRA

PLANO NO APTO PARA CONSTRUCCION.

Ing. Mariano Miculicich
DIRECTOR

MODIFICACIONES:

REVISIÓN	FECHA	DESCRIPCIÓN
2	22/09/2025	EMISIÓN INICIAL
1	19/11/2025	AJUSTE DE PROYECTO

MINISTERIO DE INFRAESTRUCTURA
SUBSECRETARÍA DE PROYECTOS Y OBRAS
DIRECCIÓN GENERAL DE PROYECTOS

DGPRO

Obra: LINEA F			IF-2026-20223041-GCABA-APRA
Plano: GEOTECNIA - ESTRATIGRAFÍA TRAMO 1 - PROGR. 5+600 A 6+350			LF-GL-T01-GTA-PL-009
Fecha: 22/09/2025	Eq. de Proyecto: UPU-ATEC-IATASA	Dibujó: D.B.	Revisó: R.H.B. Escala: Indicadas

Plano N° 009

20/11/2025 12:42
LF-GL-T01-GTA-PL-001 A 009_1.dwg

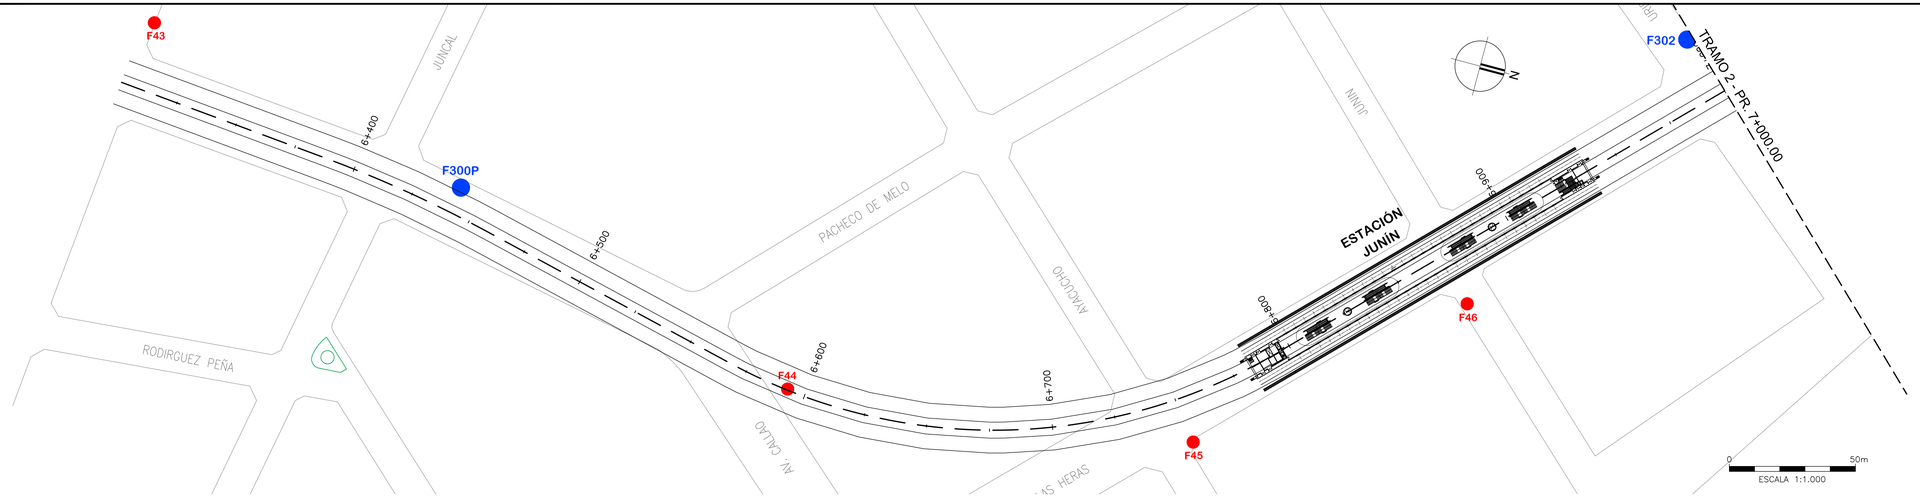

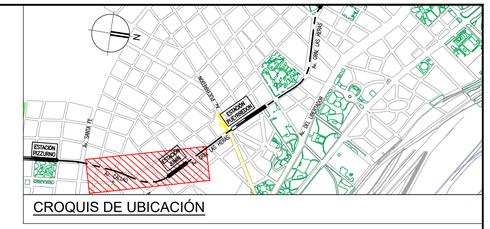

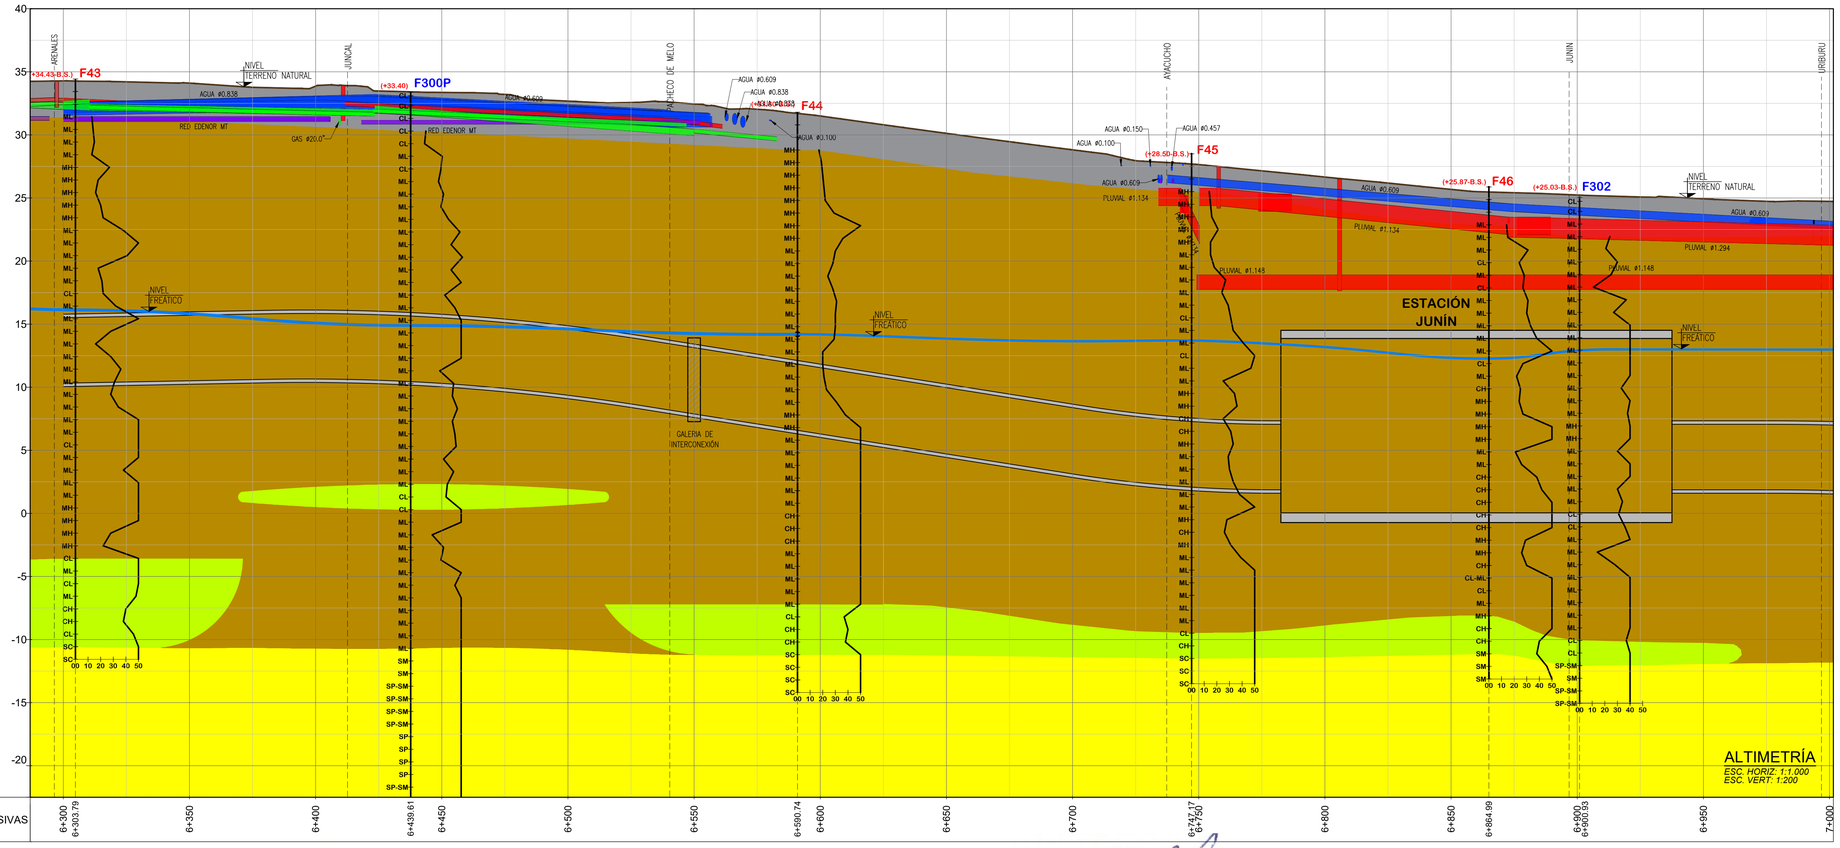

REFERENCIAS SONDEOS:

- Fxx BOCA DE SONDEO MINAMÉRICA
- Fxx BOCA DE SONDEO MENDIGUREN

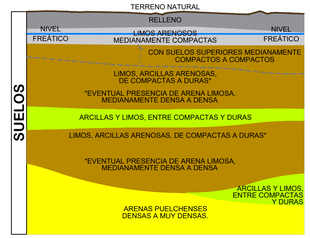

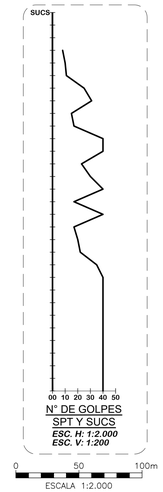

REFERENCIAS INTERFERENCIAS:

- RED DE AGUA CORRIENTE
- RED CLOACAL
- RED DE FIBRA OPTICA
- RED BT - MT - AT
- RED DE GAS
- RED TELEFÓNICA
- RED PLUVIAL

NOTAS :

1- SISTEMA DE COORDENADAS DE LA CIUDAD DE BUENOS AIRES.

2- TODAS LAS MEDIDAS ESTÁN EXPRESADAS EN METROS, SALVO INDICACIÓN CONTRARIA

NOTAS: EL PRESENTE PLANO ES INDICATIVO. LA CONTRATISTA CONFECCIONARÁ LOS PLANOS DE DETALLE DEFINITIVO, QUE DEBERÁN SER APROBADOS POR LA D.G.OBR.S.T.U.A. PREVIO A LA INSPECCIÓN DE OBRA, EL PLANO PRESENTADO POR LA CONTRATISTA ESTARÁ EN VISTO DE ACUERDO CON LA NORMATIVA VIGENTE. TODAS LAS MEDIDAS Y NIVELES SE VERIFICARÁN EN OBRA POR EL CONTRATISTA. TODOS LOS DETALLES CONSTRUCTIVOS SERÁN COORDINADOS Y CONFIRMADOS EN OBRA

PLANO NO APTO PARA CONSTRUCCION.

Ing. Mariano Miculicich
DIRECTOR

MODIFICACIONES:

REVISIÓN	FECHA	DESCRIPCIÓN
0	30/10/25	EMISIÓN INICIAL
1	19/11/2025	AJUSTE DE PROYECTO

MINISTERIO DE INFRAESTRUCTURA
SUBSECRETARIA DE PROYECTOS Y OBRAS
DIRECCION GENERAL DE PROYECTOS

DGPRO

Obra: LÍNEA F				IF-2026-20223041-GCABA-APRA	Plano N°
Plano: GEOTECNIA - ESTRATIGRAFÍA TRAMO 2 - PROGR. 6+300 A 7+000				LF-GL-T02-GTA-PL-001	001
Fecha: 19/11/2025	Eq. de Proyecto: UPU-ATEC-IATASA	Dibujó: D.B.	Revisó: R.H.B.	Escala: 1:1000	

20/11/2025 12:27
LF-GL-T02-GTA-PL-001-001_1.dwg

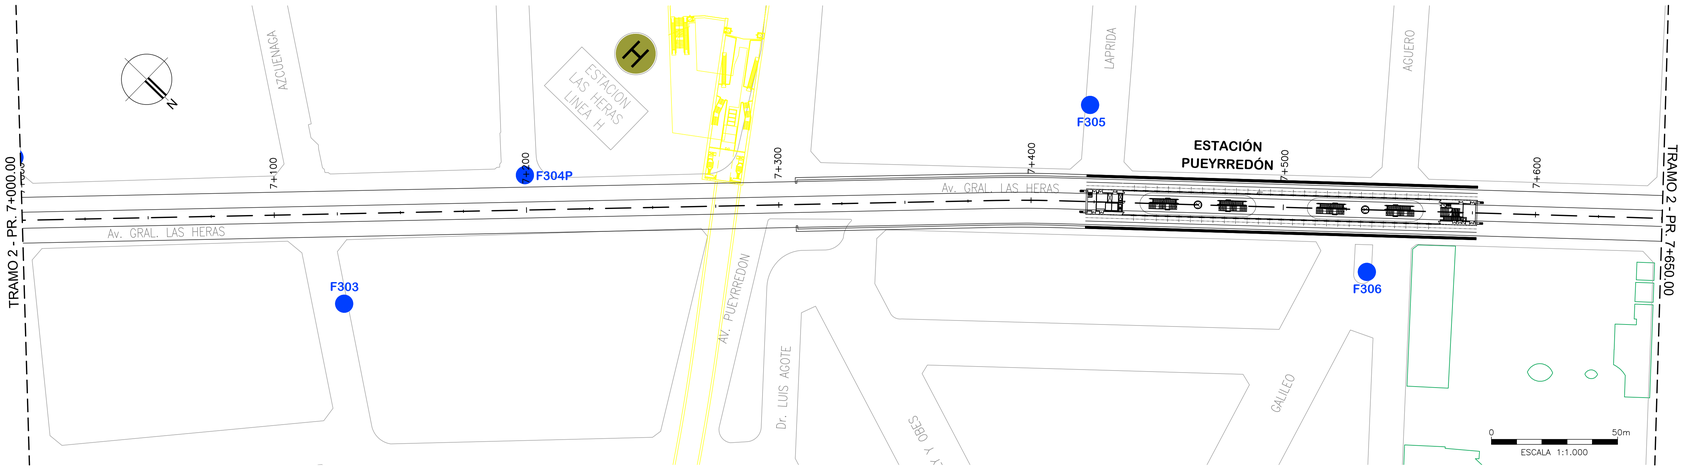

CROQUIS DE UBICACIÓN

REFERENCIAS SONDEOS:

Fxx BOCA DE SONDEO MINAMÉRICA

Fxx BOCA DE SONDEO MENDIGUREN

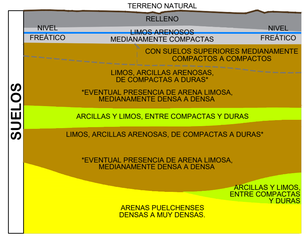

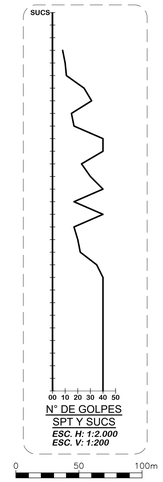

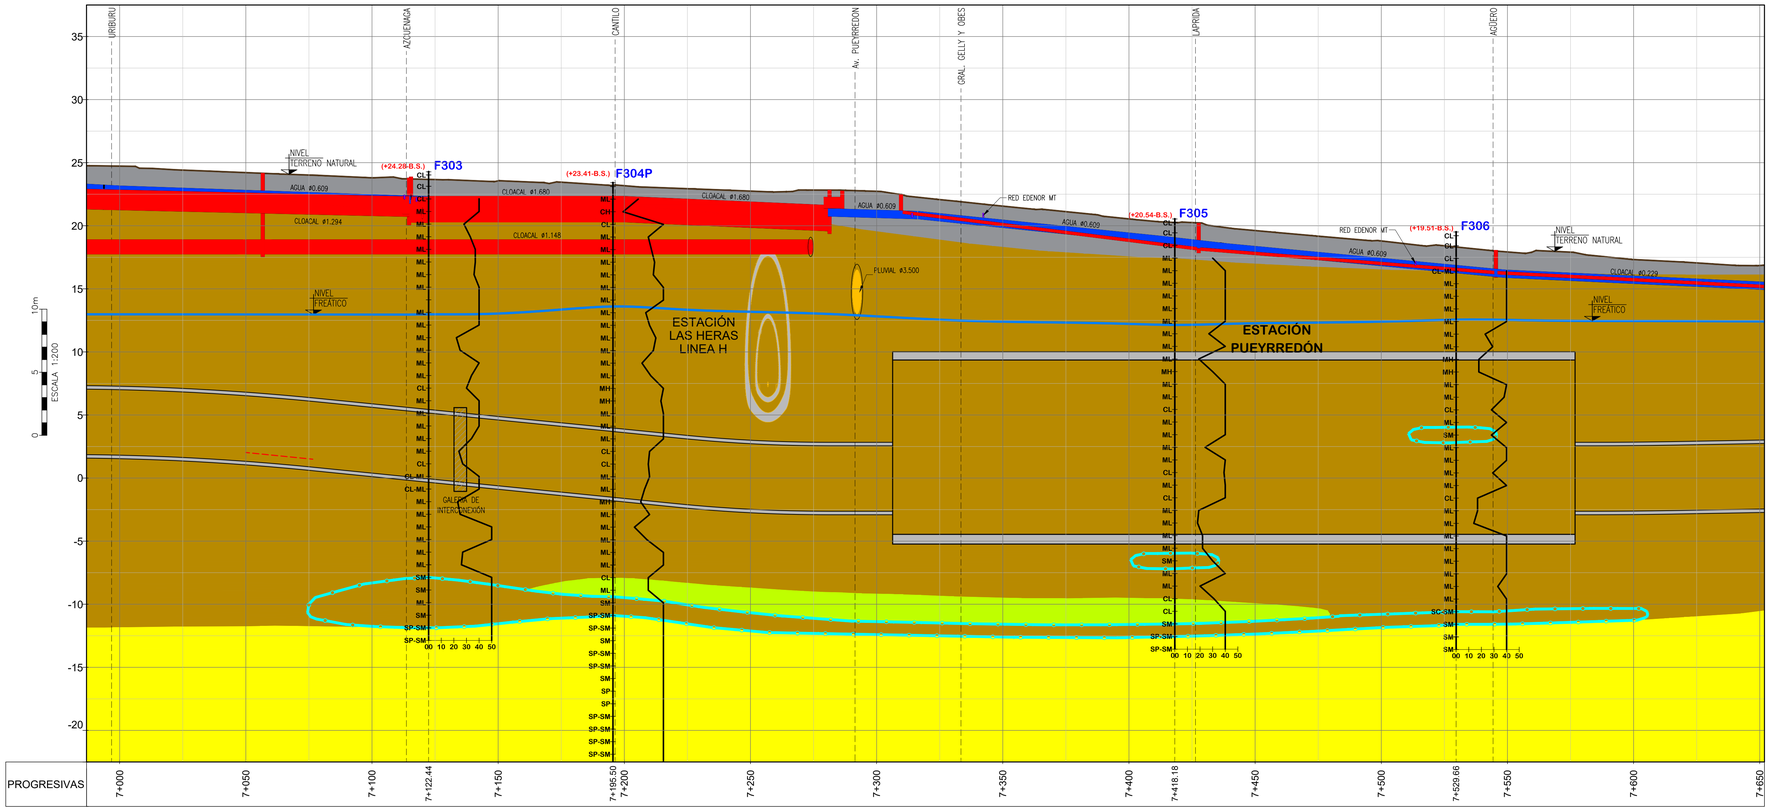

ALTIMETRÍA

ESC. HORIZ: 1:1.000
ESC. VERT: 1:200

REFERENCIAS INTERFERENCIAS:

- RED DE AGUA CORRIENTE
- RED CLOACAL
- RED DE FIBRA OPTICA
- RED BT - MT - AT
- RED DE GAS
- RED TELEFÓNICA
- RED PLUVIAL

NOTAS :

1- SISTEMA DE COORDENADAS DE LA CIUDAD DE BUENOS AIRES.

2- TODAS LAS MEDIDAS ESTÁN EXPRESADAS EN METROS, SALVO INDICACIÓN CONTRARIA

NOTAS: EL PRESENTE PLANO ES INDICATIVO. LA CONTRATISTA CONFECCIONARA LOS PLANOS DE DETALLE DEFINITIVO, QUE DEBERAN SER APROBADOS POR LA D.G.D.M.P. O Y LA INSPECCION DE OBRA, EL PLANO PRESENTADO POR LA CONTRATISTA ESTARA EN UN TODO DE ACUERDO CON LA NORMATIVA VIGENTE. TODAS LAS MEDIDAS Y NIVELES DE VEREDAS PARA OBRA POR EL CONTRATISTA. TODOS LOS DETALLES CONSTRUCTIVOS SERAN COORDINADOS Y CONFIRMADOS EN OBRA

PLANO NO APTO PARA CONSTRUCCION.

Ing. Mariano Miculicich
DIRECTOR

MODIFICACIONES:

REVISIÓN	FECHA	DESCRIPCIÓN
0	28/10/2025	EMISIÓN INICIAL
1	19/11/2025	AJUSTE DE PROYECTO

MINISTERIO DE INFRAESTRUCTURA
SUBSECRETARIA DE PROYECTOS Y OBRAS
DIRECCION GENERAL DE PROYECTOS

DGPRO

Obra: LÍNEA F				IF-2026-20223041-GCABA-APRA	Plano N°: 002
Plano: GEOTECNIA - ESTRATIGRAFÍA TRAMO 2 - PROGR. 7+000 A 7+650				LF-GL-T02-GTA-PL-002	
Fecha: 19/11/2025	Eq. de Proyecto: UPU-ATEC-IATASA	Dibujó: D.B.	Revisó: R.H.B.	Escala: 1:1000	

20/11/2025 12:27
LF-GL-T02-GTA-PL-001-007_1.dwg

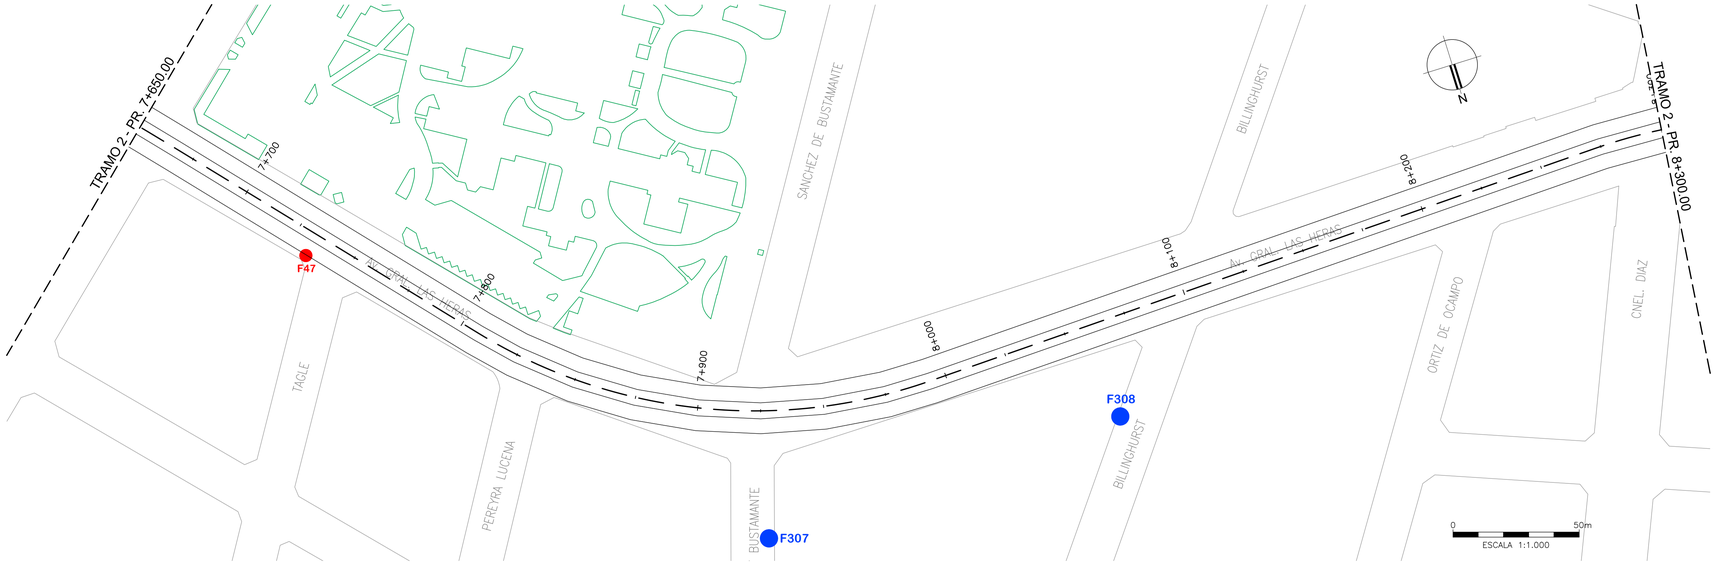

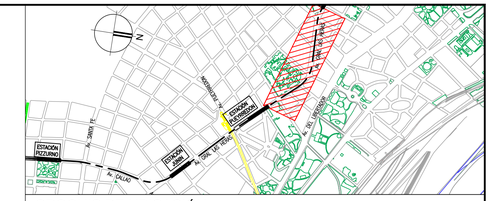

CROQUIS DE UBICACIÓN

REFERENCIAS SONDEOS:

Fxx BOCA DE SONDEO MINAMÉRICA

Fxx BOCA DE SONDEO MENDIGUREN

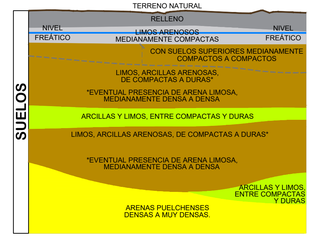

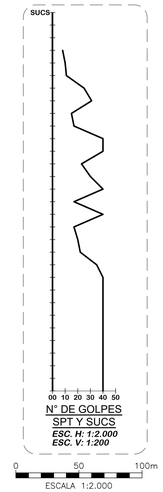

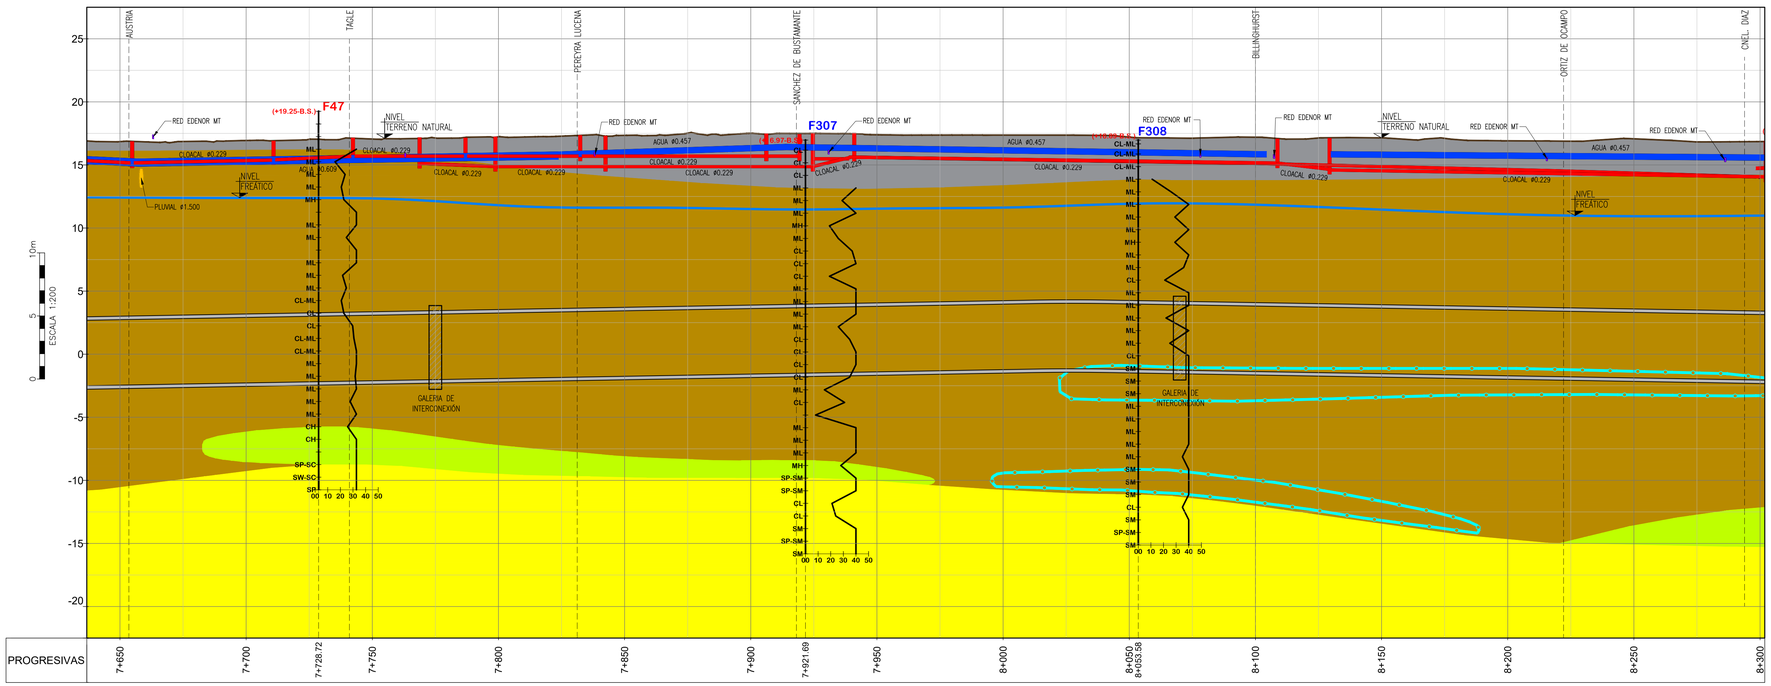

ALTIMETRÍA

ESC. HORIZ. 1:1.000
ESC. VERT: 1:200

REFERENCIAS INTERFERENCIAS:

- RED DE AGUA CORRIENTE
- RED CLOACAL
- RED DE FIBRA OPTICA
- RED BT - MT - AT
- RED DE GAS
- RED TELEFÓNICA
- RED PLUVIAL

NOTAS :

1- SISTEMA DE COORDENADAS DE LA CIUDAD DE BUENOS AIRES.

2- TODAS LAS MEDIDAS ESTÁN EXPRESADAS EN METROS, SALVO INDICACIÓN CONTRARIA

NOTAS: EL PRESENTE PLANO ES INDICATIVO. LA CONTRATISTA CONFECCIONARA LOS PLANOS DE DETALLE DEFINITIVO QUE DEBERAN SER APROBADOS POR LA D.G.CIMP.S.Y LA INSPECCION DE OBRA. EL PLANO PRESENTADO POR LA CONTRATISTA DEBERA EN UN TODO DE ACUERDO CON LA NORMATIVA VIGENTE. TODAS LAS MEDIDAS Y NIVELES SE VERIFICARAN EN OBRA POR EL CONTRATISTA. TODOS LOS DETALLES CONSTRUCTIVOS DEBRAN COORDINADOS Y COMPATIBILIZADOS EN OBRA

PLANO NO APTO PARA CONSTRUCCION.

Ing. Mariano Miculicich
DIRECTOR

MODIFICACIONES:

REVISIÓN	FECHA	DESCRIPCIÓN
0	28/10/2025	EMISIÓN INICIAL
1	19/11/2025	AJUSTE DE PROYECTO

MINISTERIO DE INFRAESTRUCTURA
SUBSECRETARIA DE PROYECTOS Y OBRAS
DIRECCION GENERAL DE PROYECTOS

DGPRO

Obra: LÍNEA F			IF-2026-20223041-GCABA-APRA
Plano: GEOTECNIA - ESTRATIGRAFÍA TRAMO 2 - PROGR. 7+650 A 8+300			LF-GL-T02-GTA-PL-003
Fecha: 19/11/2025	Eq. de Proyecto: UPU-ATEC-IATASA	Dibujó: D.B.	Revisó: R.H.B. / Escala: 1:1000

Plano N° 003

20/11/2025 12:27
LF-GL-T02-GTA-PL-001-007_1.dwg

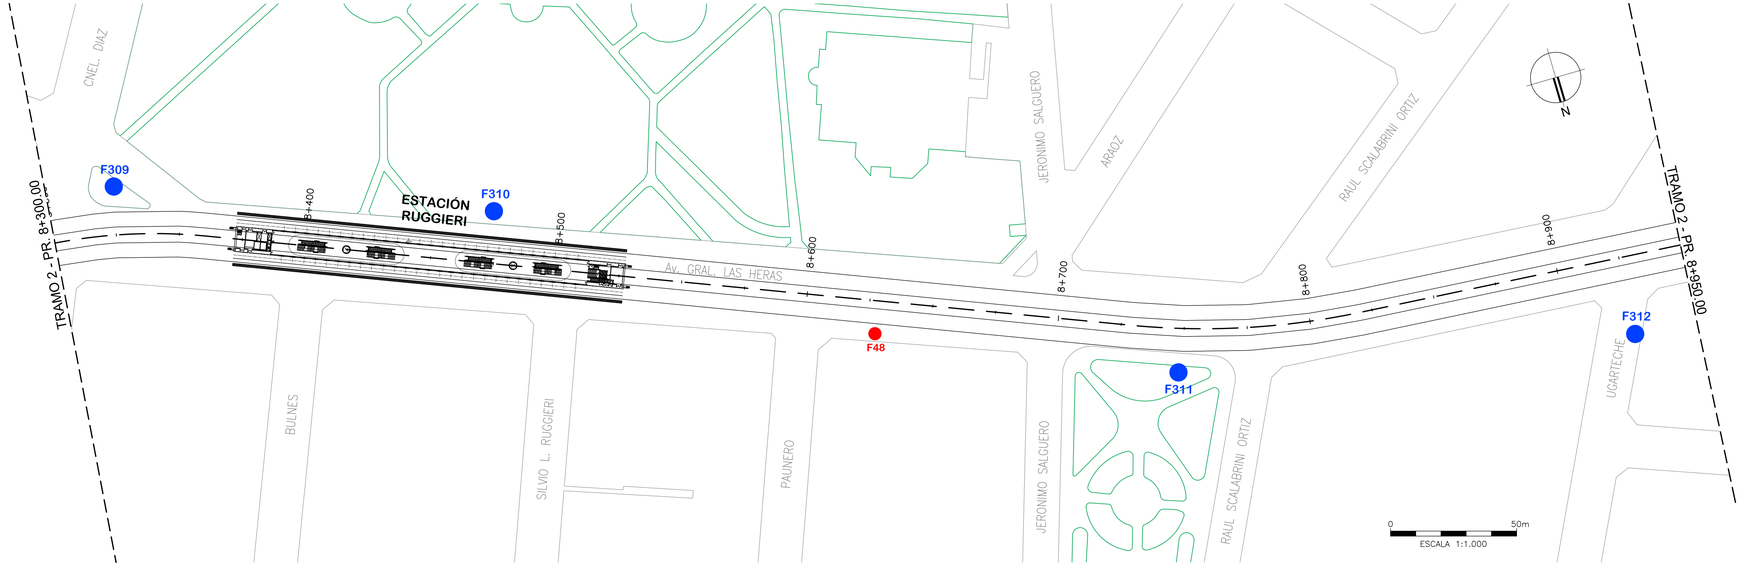

CROQUIS DE UBICACIÓN

REFERENCIAS SONDEOS:

Fxx BOCA DE SONDEO MINAMÉRICA

Fxx BOCA DE SONDEO MENDIGUREN

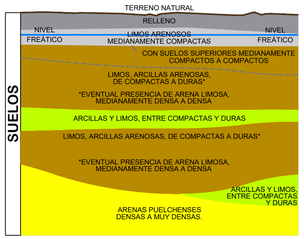

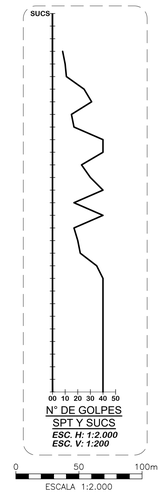

N° DE GOLPES SPT Y SUCS

ESC. H: 1:2.000

ESC. V: 1:200

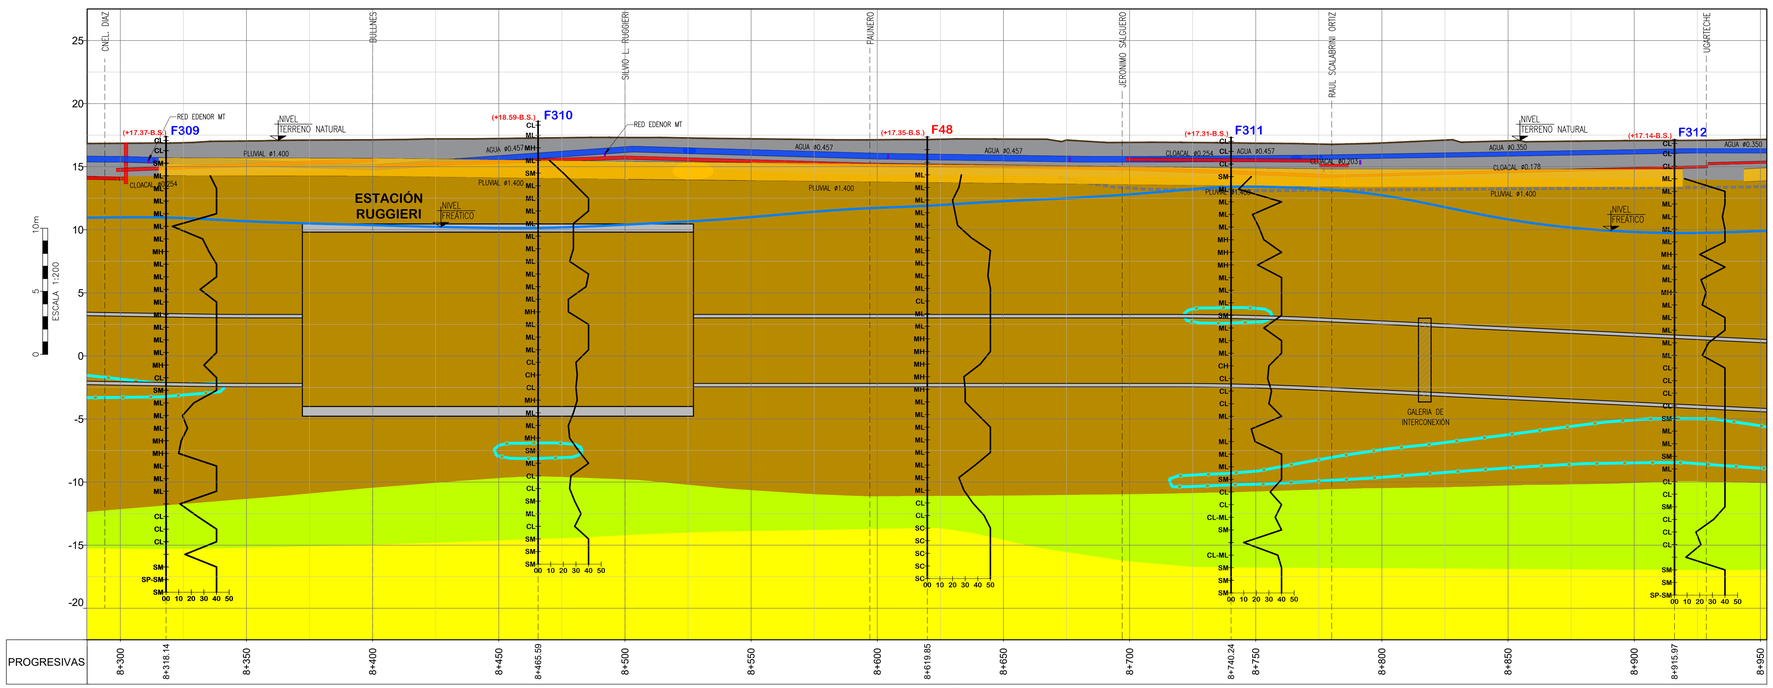

ALTIMETRÍA

ESC. HORIZ. 1:1.000

ESC. VERT. 1:200

REFERENCIAS INTERFERENCIAS:

- RED DE AGUA CORRIENTE
- RED CLOACAL
- RED DE FIBRA OPTICA
- RED BT - MT - AT
- RED DE GAS
- RED TELEFÓNICA
- RED PLUVIAL

NOTAS :

1- SISTEMA DE COORDENADAS DE LA CIUDAD DE BUENOS AIRES.

2- TODAS LAS MEDIDAS ESTÁN EXPRESADAS EN METROS, SALVO INDICACIÓN CONTRARIA

NOTAS: EL PRESENTE PLANO ES INDICATIVO, LA CONTRATISTA CONFECCIONARA LOS PLANOS DE DETALLE CONTRACTUAL QUE DEBERAN SER APROBADOS POR LA D.G.DIF. Y T. LA INSPECCION DE OBRA, EL PLANO PRESENTADO POR LA CONTRATISTA DEBERA EN LA TODO SE AJUSTADO CON LA NORMATIVA VIGENTE.
TODAS LAS MEDIDAS Y NIVELES SE VERIFICARAN EN OBRA POR EL CONTRATISTA.
TODOS LOS DETALLES CONSTRUCTIVOS SERAN COORDINADOS Y CONFIRMADOS EN OBRA

PLANO NO APTO PARA CONSTRUCCION.

Ing. Mariano Miculicich
DIRECTOR

MODIFICACIONES:

ACUERDO	FECHA	DESCRIPCION
0	28/10/2025	EMISIÓN INICIAL
1	19/11/2025	AJUSTE DE PROYECTO

MINISTERIO DE INFRAESTRUCTURA
SUBSECRETARIA DE PROYECTOS Y OBRAS
DIRECCION GENERAL DE PROYECTOS

DGPRO

Obra: LINEA F — IF-2026-20223041-GCABA-APRA — Plano N°: 004

Plano: GEOTECNIA - ESTRATIGRAFÍA TRAMO 2 - PROGR. 8+300 A 8+950 — LF-GL-T02-GTA-PL-004

Fecha: 19/11/2025 | Eq. de Proyecto: UPU-ATEC-IATASA | Dibujó: D.B. | Revisó: R.H.B. | Escala: 1:1000

20/11/2025 12:27
LF-GL-T02-GTA-PL-001-007_1.dwg

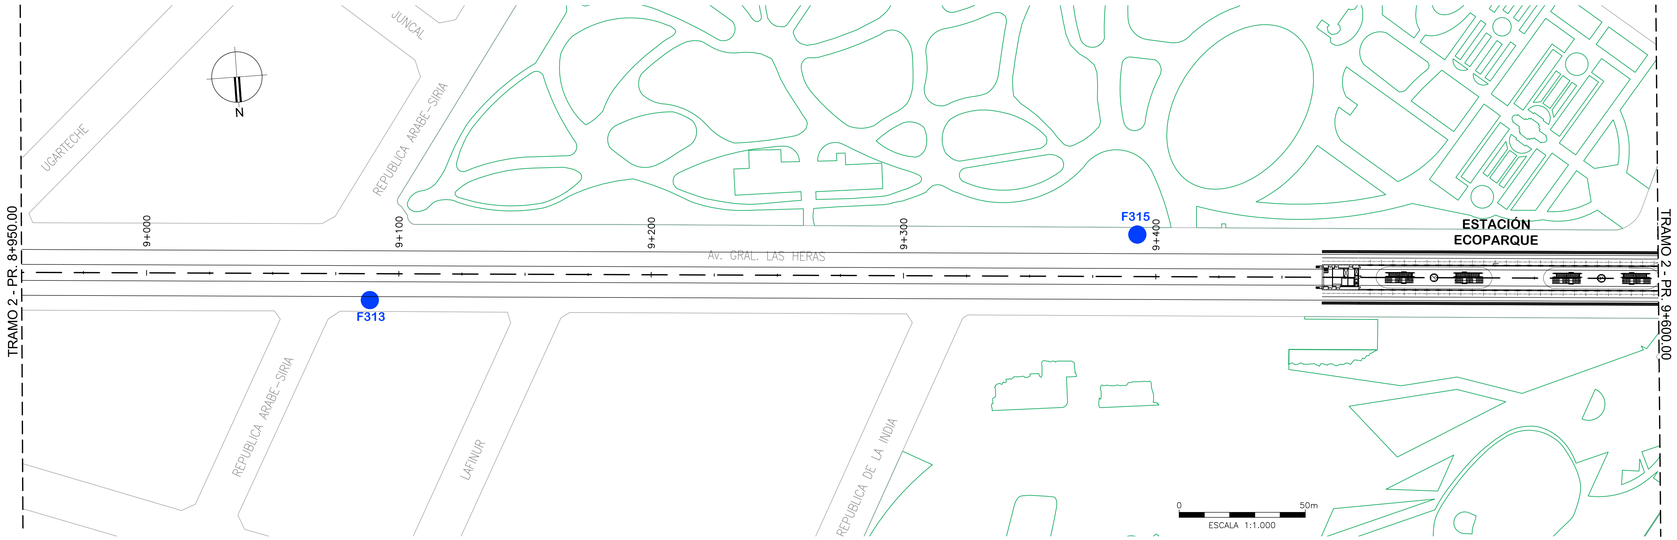

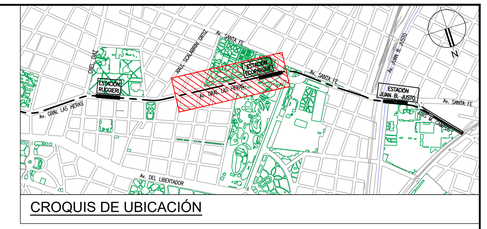

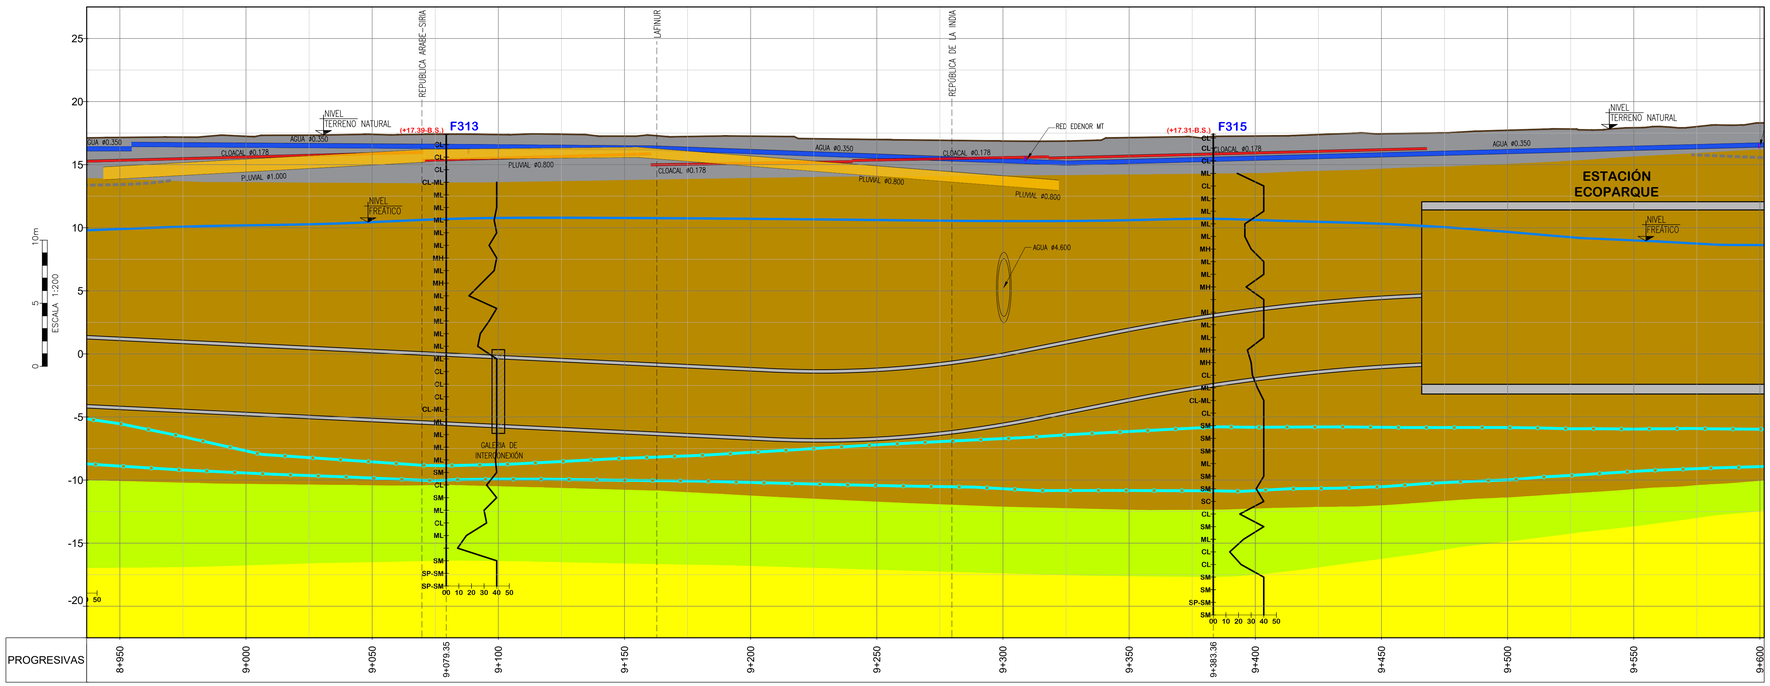

ALTIMETRÍA

ESC. HORIZ. 1:1.000
ESC. VERT. 1:200

REFERENCIAS SONDEOS:

Fxx BOCA DE SONDEO MINAMÉRICA

Fxx BOCA DE SONDEO MENDIGUREN

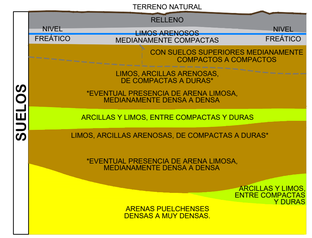

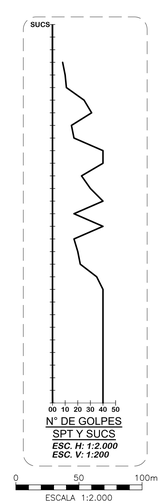

REFERENCIAS INTERFERENCIAS:

- RED DE AGUA CORRIENTE
- RED CLOACAL
- RED DE FIBRA OPTICA
- RED BT - MT - AT
- RED DE GAS
- RED TELEFÓNICA
- RED PLUVIAL

NOTAS :

1- SISTEMA DE COORDENADAS DE LA CIUDAD DE BUENOS AIRES.

2- TODAS LAS MEDIDAS ESTÁN EXPRESADAS EN METROS, SALVO INDICACIÓN CONTRARIA

NOTAS: EL PRESENTE PLANO ES INDICATIVO. LA CONTRATISTA CONFECCIONARA LOS PLANOS DE DETALLE DEFINITIVO, QUE DEBERAN SER APROBADOS POR LA I.G.S.S.M.P. U.T.U.A. TODAS LAS MEDIDAS ESTAN EXPRESADAS EN METROS, SALVO INDICACION CONTRARIA. TODAS LAS MEDIDAS A VERIFICAR EN OBRA POR EL CONTRATISTA. TODOS LOS DETALLES CONSTRUCTIVOS SERAN COORDINADOS Y CONFIRMADOS EN OBRA

PLANO NO APTO PARA CONSTRUCCION.

Ing. Mariano Miculicich
DIRECTOR

MODIFICACIONES:

REVISIÓN	FECHA	DESCRIPCIÓN
2	28/10/25	DISEÑO INICIAL
1	19/11/2025	AJUSTE DE PROYECTO

MINISTERIO DE INFRAESTRUCTURA
SUBSECRETARIA DE PROYECTOS Y OBRAS
DIRECCION GENERAL DE PROYECTOS

DGPRO

Obra: LINEA F			IF-2026-20223041-GCABA-APRA Plano N°
Plano: GEOTECNIA - ESTRATIGRAFÍA TRAMO 2 - PROGR. 8+950 A 9+600			LF-GL-T02-GTA-PL-005 005
Fecha: 19/11/2025	Eq. de Proyecto: UPU-ATEC-IATASA	Dibujó: D.B.	Revisó: R.H.B. Escala: 1:1000

20/11/2025 12:27
LF-GL-T02-GTA-PL-001-007_1.dwg

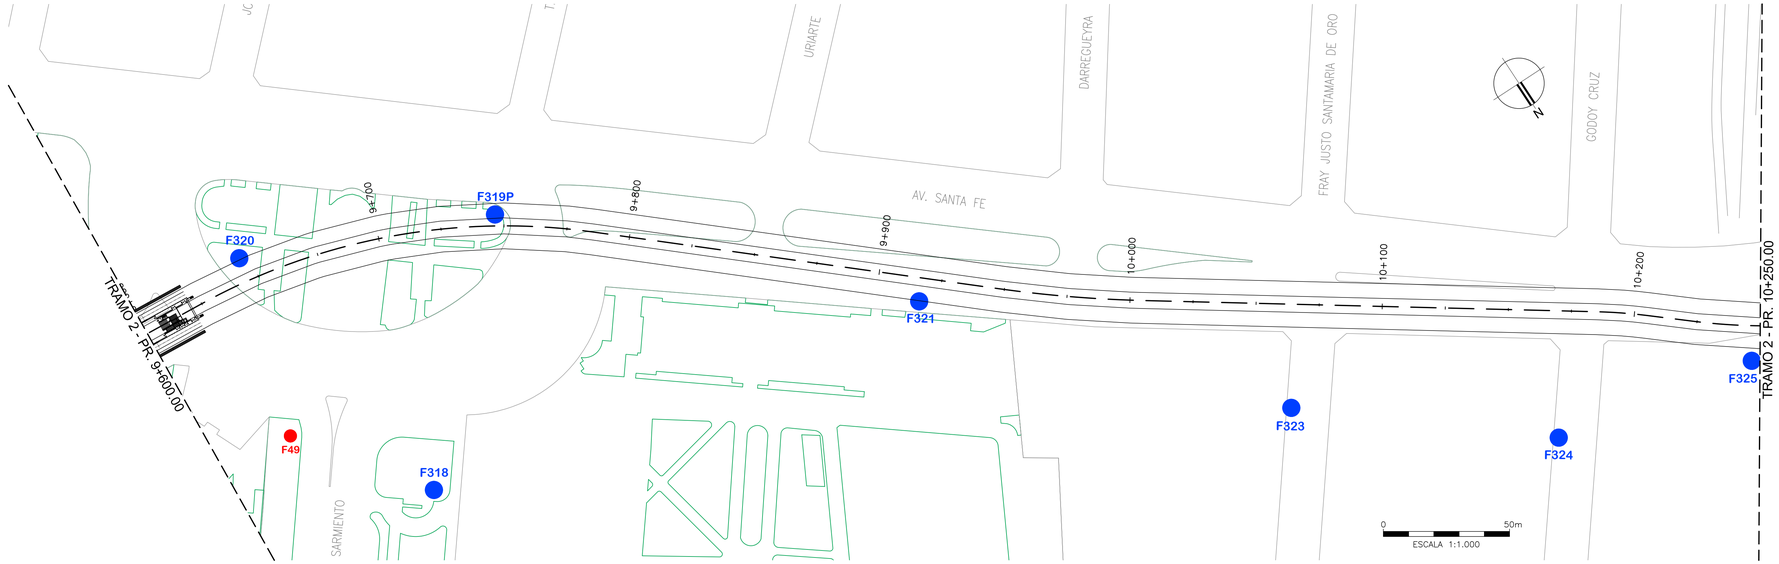

CROQUIS DE UBICACIÓN

REFERENCIAS SONDEOS:

Fxx BOCA DE SONDEO MINAMÉRICA

Fxx BOCA DE SONDEO MENDIGUREN

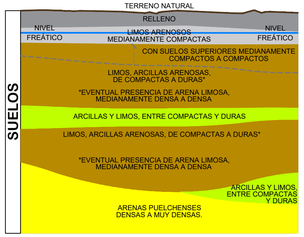

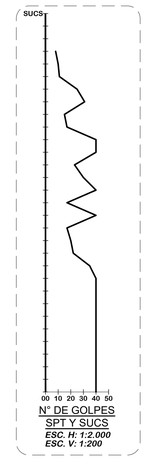

N° DE GOLPES SPT Y SUCS

ESC. H: 1:2.000
ESC. V: 1:200

0 50 100m

ESCALA 1:2.000

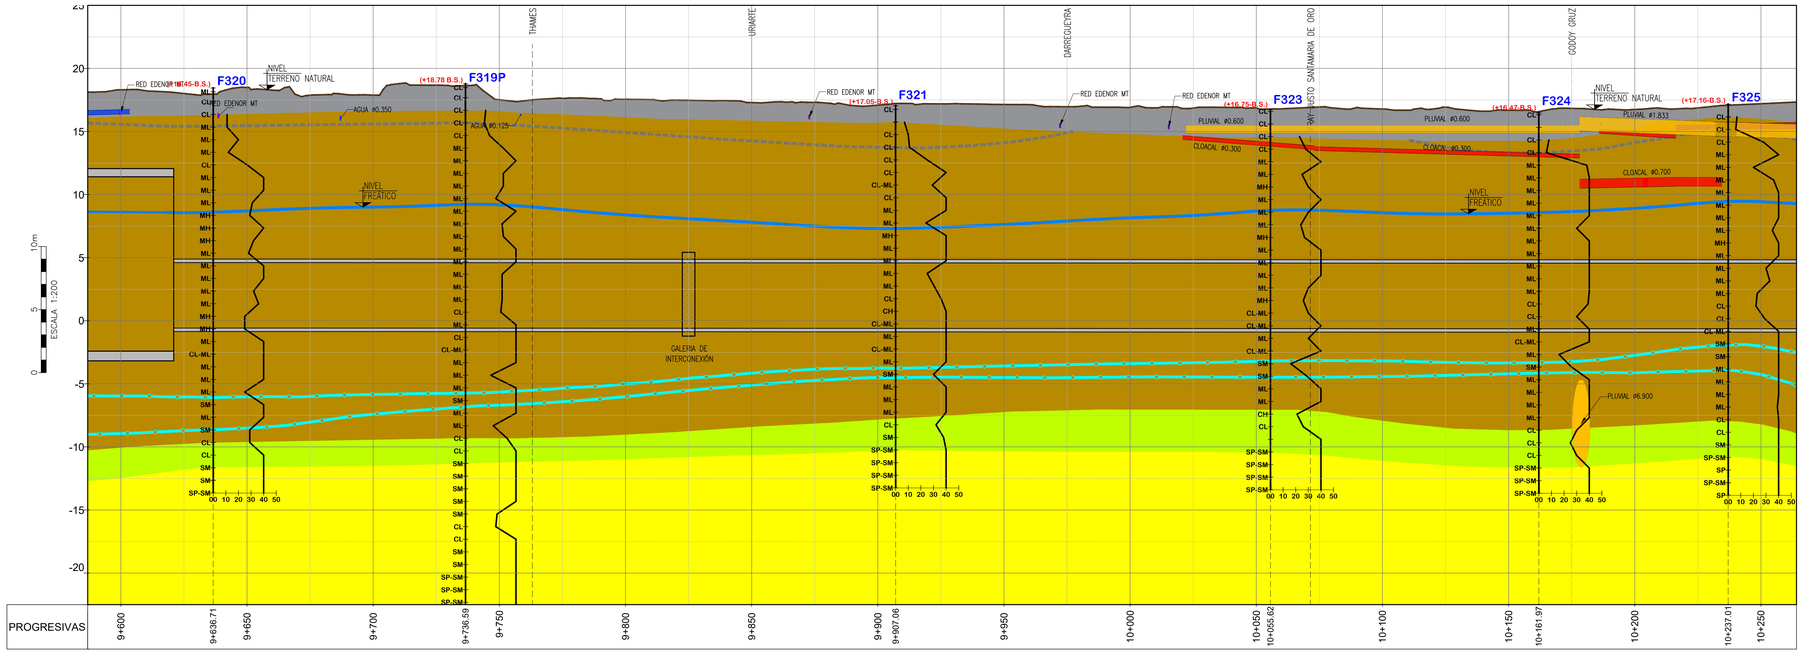

ALTIMETRÍA

ESC. HORIZ. 1:1.000
ESC. VERT. 1:200

REFERENCIAS INTERFERENCIAS:

- RED DE AGUA CORRIENTE
- RED CLOACAL
- RED DE FIBRA OPTICA
- RED BT - MT - AT
- RED DE GAS
- RED TELEFÓNICA
- RED PLUVIAL

NOTAS :

1- SISTEMA DE COORDENADAS DE LA CIUDAD DE BUENOS AIRES.

2- TODAS LAS MEDIDAS ESTÁN EXPRESADAS EN METROS, SALVO INDICACIÓN CONTRARIA

NOTAS: EL PRESENTE PLANO ES INDICATIVO. LA CONTRATISTA CONFECCIONARÁ LOS PLANOS DE DETALLE DEFINITIVO, QUE DEBERÁN SER APROBADOS POR LA D.G.SIP. ET LA INSPECCIÓN DE OBRA, EL PLANO PRESENTADO POR LA CONTRATISTA ESTARÁ EN UN TODO DE ACUERDO CON LA NORMATIVA VIGENTE.
TODAS LAS MEDIDAS Y NIVELES SE VERIFICARÁN EN OBRA POR EL CONTRATISTA.
TODOS LOS DETALLES CONSTRUCTIVOS SERÁN COORDINADOS Y CONFIRMADOS EN OBRA

PLANO NO APTO PARA CONSTRUCCION.

Ing. Mariano Miculicich
DIRECTOR

MODIFICACIONES:

REVISIÓN	FECHA	DESCRIPCIÓN
0	28/10/2025	EMISIÓN INICIAL
1	19/11/2025	AJUSTE DE PROYECTO

MINISTERIO DE INFRAESTRUCTURA
SUBSECRETARIA DE PROYECTOS Y OBRAS
DIRECCION GENERAL DE PROYECTOS

DGPRO

Obra: LÍNEA F			IF-2026-20223041-GCABA-APRA Plano N°
Plano: GEOTECNIA - ESTRATIGRAFÍA TRAMO 2 - PROGR. 9+600 A 10+250			LF-GL-T02-GTA-PL-006 006
Fecha: 19/11/2025	Eq. de Proyecto: UPU-ATEC-IATASA	Dibujó. D.B.	Revisó. R.H.B. Escala: 1:1000

20/11/2025 12:27
LF-GL-T02-GTA-PL-001-007_1.dwg

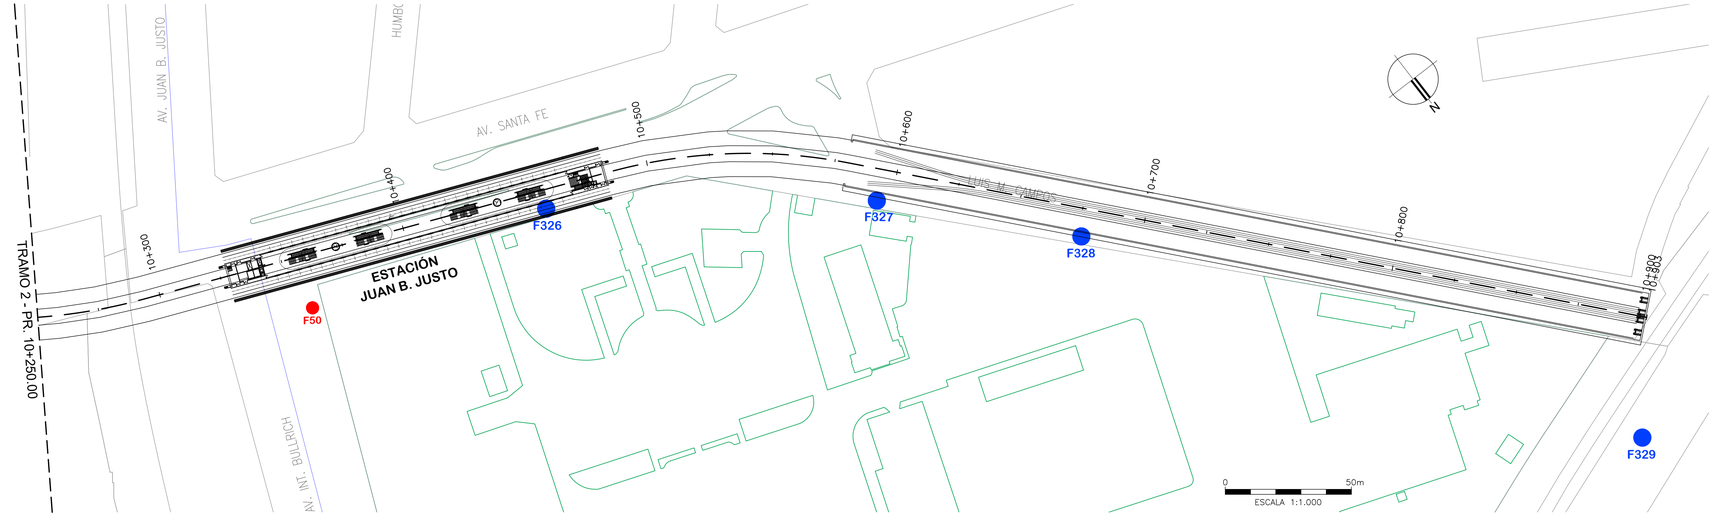

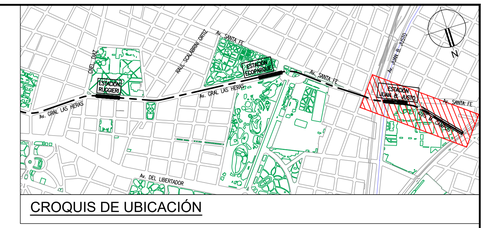

REFERENCIAS SONDEOS:

Fxx BOCA DE SONDEO MINAMÉRICA

Fxx BOCA DE SONDEO MENDIGUREN

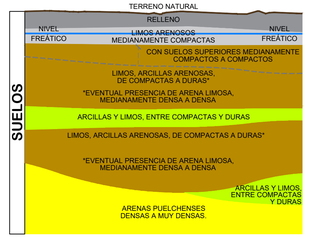

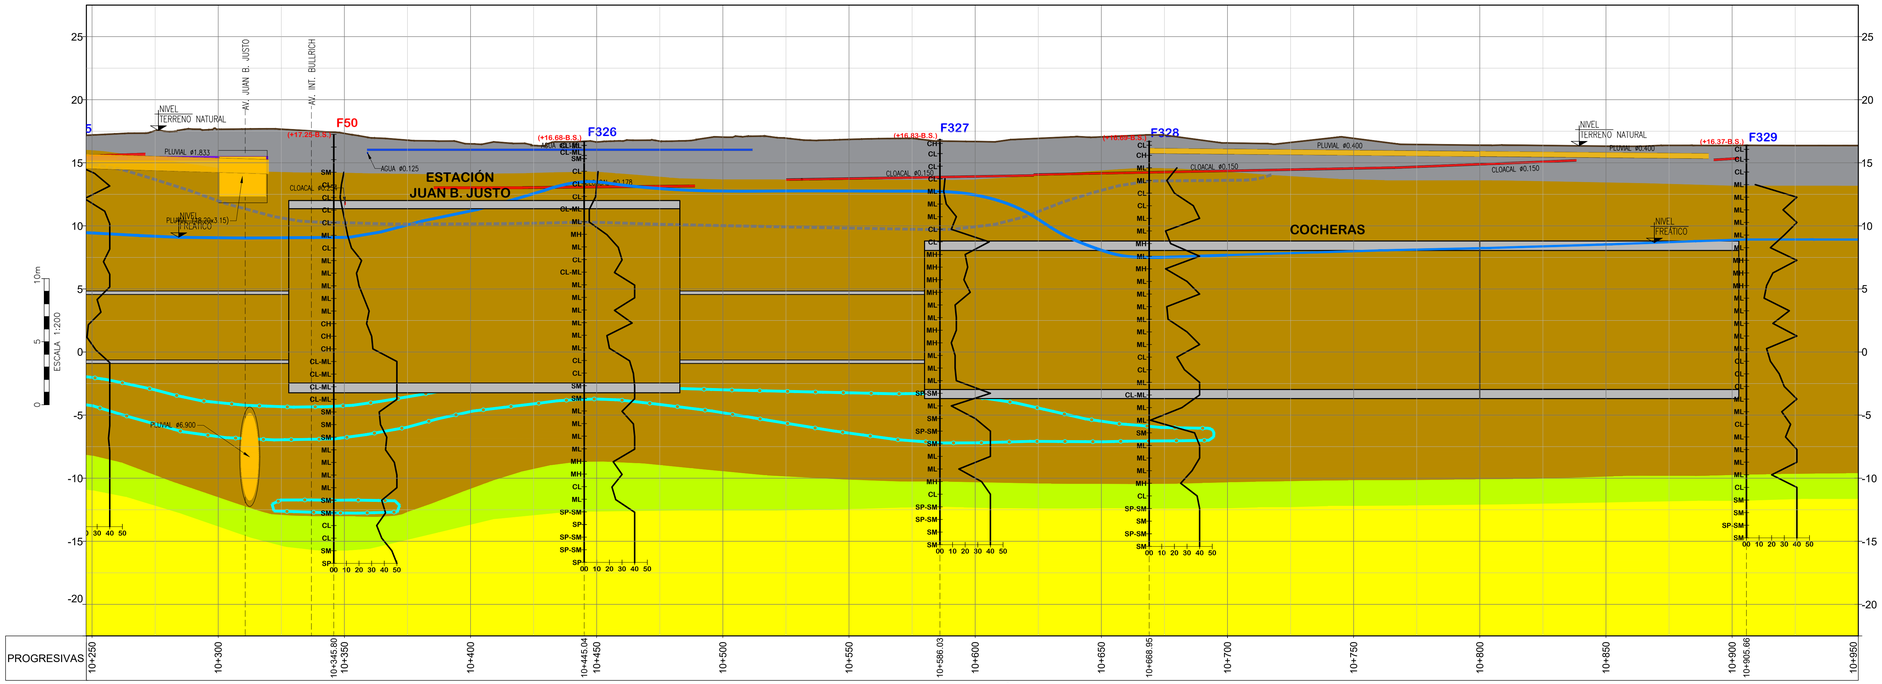

ALTIMETRÍA

ESC. HORIZ. 1:1.000
ESC. VERT. 1:200

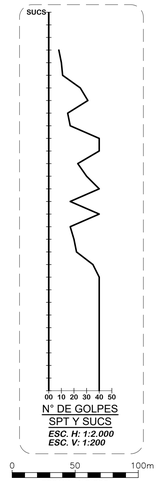

N° DE GOLPES SPT Y SUCS

ESC. H: 1:2.000
ESC. V: 1:200

0 50 100m
ESCALA 1:2.000

REFERENCIAS INTERFERENCIAS:

- RED DE AGUA CORRIENTE
- RED CLOACAL
- RED DE FIBRA OPTICA
- RED BT - MT - AT
- RED DE GAS
- RED TELEFÓNICA
- RED PLUVIAL

NOTAS :

1- SISTEMA DE COORDENADAS DE LA CIUDAD DE BUENOS AIRES.

2- TODAS LAS MEDIDAS ESTÁN EXPRESADAS EN METROS, SALVO INDICACIÓN CONTRARIA

NOTAS: EL PRESENTE PLANO ES INDICATIVO. LA CONTRATISTA CONFECCIONARA LOS PLANOS DE DETALLE DISTINTIVO, QUE DEBERAN SER APROBADOS POR LA D.G.SMF.,Y LA INSPECCION DE OBRA. EL PLANO PRESENTADO POR LA CONTRATISTA ESTARA EN UN TODO DE ACUERDO CON LA NORMATIVA VIGENTE. TODAS LAS MEDIDAS Y NIVELES SE VERIFICARAN EN OBRA POR EL CONTRATISTA. TODOS LOS DETALLES CONSTRUCTIVOS SERAN COORDINADOS Y CONVENCIONADOS EN OBRA

PLANO NO APTO PARA CONSTRUCCION.

Ing. Mariano Miculicich
DIRECTOR

MODIFICACIONES:	REVISIÓN	FECHA	DESCRIPCIÓN
	0	28/10/25	OBRA NUEVA
	1	19/11/25	AJUSTE DE PROYECTO

MINISTERIO DE INFRAESTRUCTURA
SUBSECRETARIA DE PROYECTOS Y OBRAS
DIRECCION GENERAL DE PROYECTOS

DGPRO

Obra: LÍNEA F			IF-2026-20223041-GCABA-APRA Plano N° 007
Plano: GEOTECNIA - ESTRATIGRAFÍA TRAMO 2 - PROGR. 10+250 A 10+900			LF-GL-T02-GTA-PL-007
Fecha: 19/11/2025	Eq. de Proyecto: UPU-ATEC-IATASA	Dibujó: D.B.	Revisó: R.H.B. Escala: 1:1000

20/11/2025 12:27
LF-GL-T02-GTA-PL-001-007_1.dwg

ESQUEMA UNIFILAR TÍPICO DE CENTRO DE POTENCIA

13,2kV – 300 MVA – 1250A

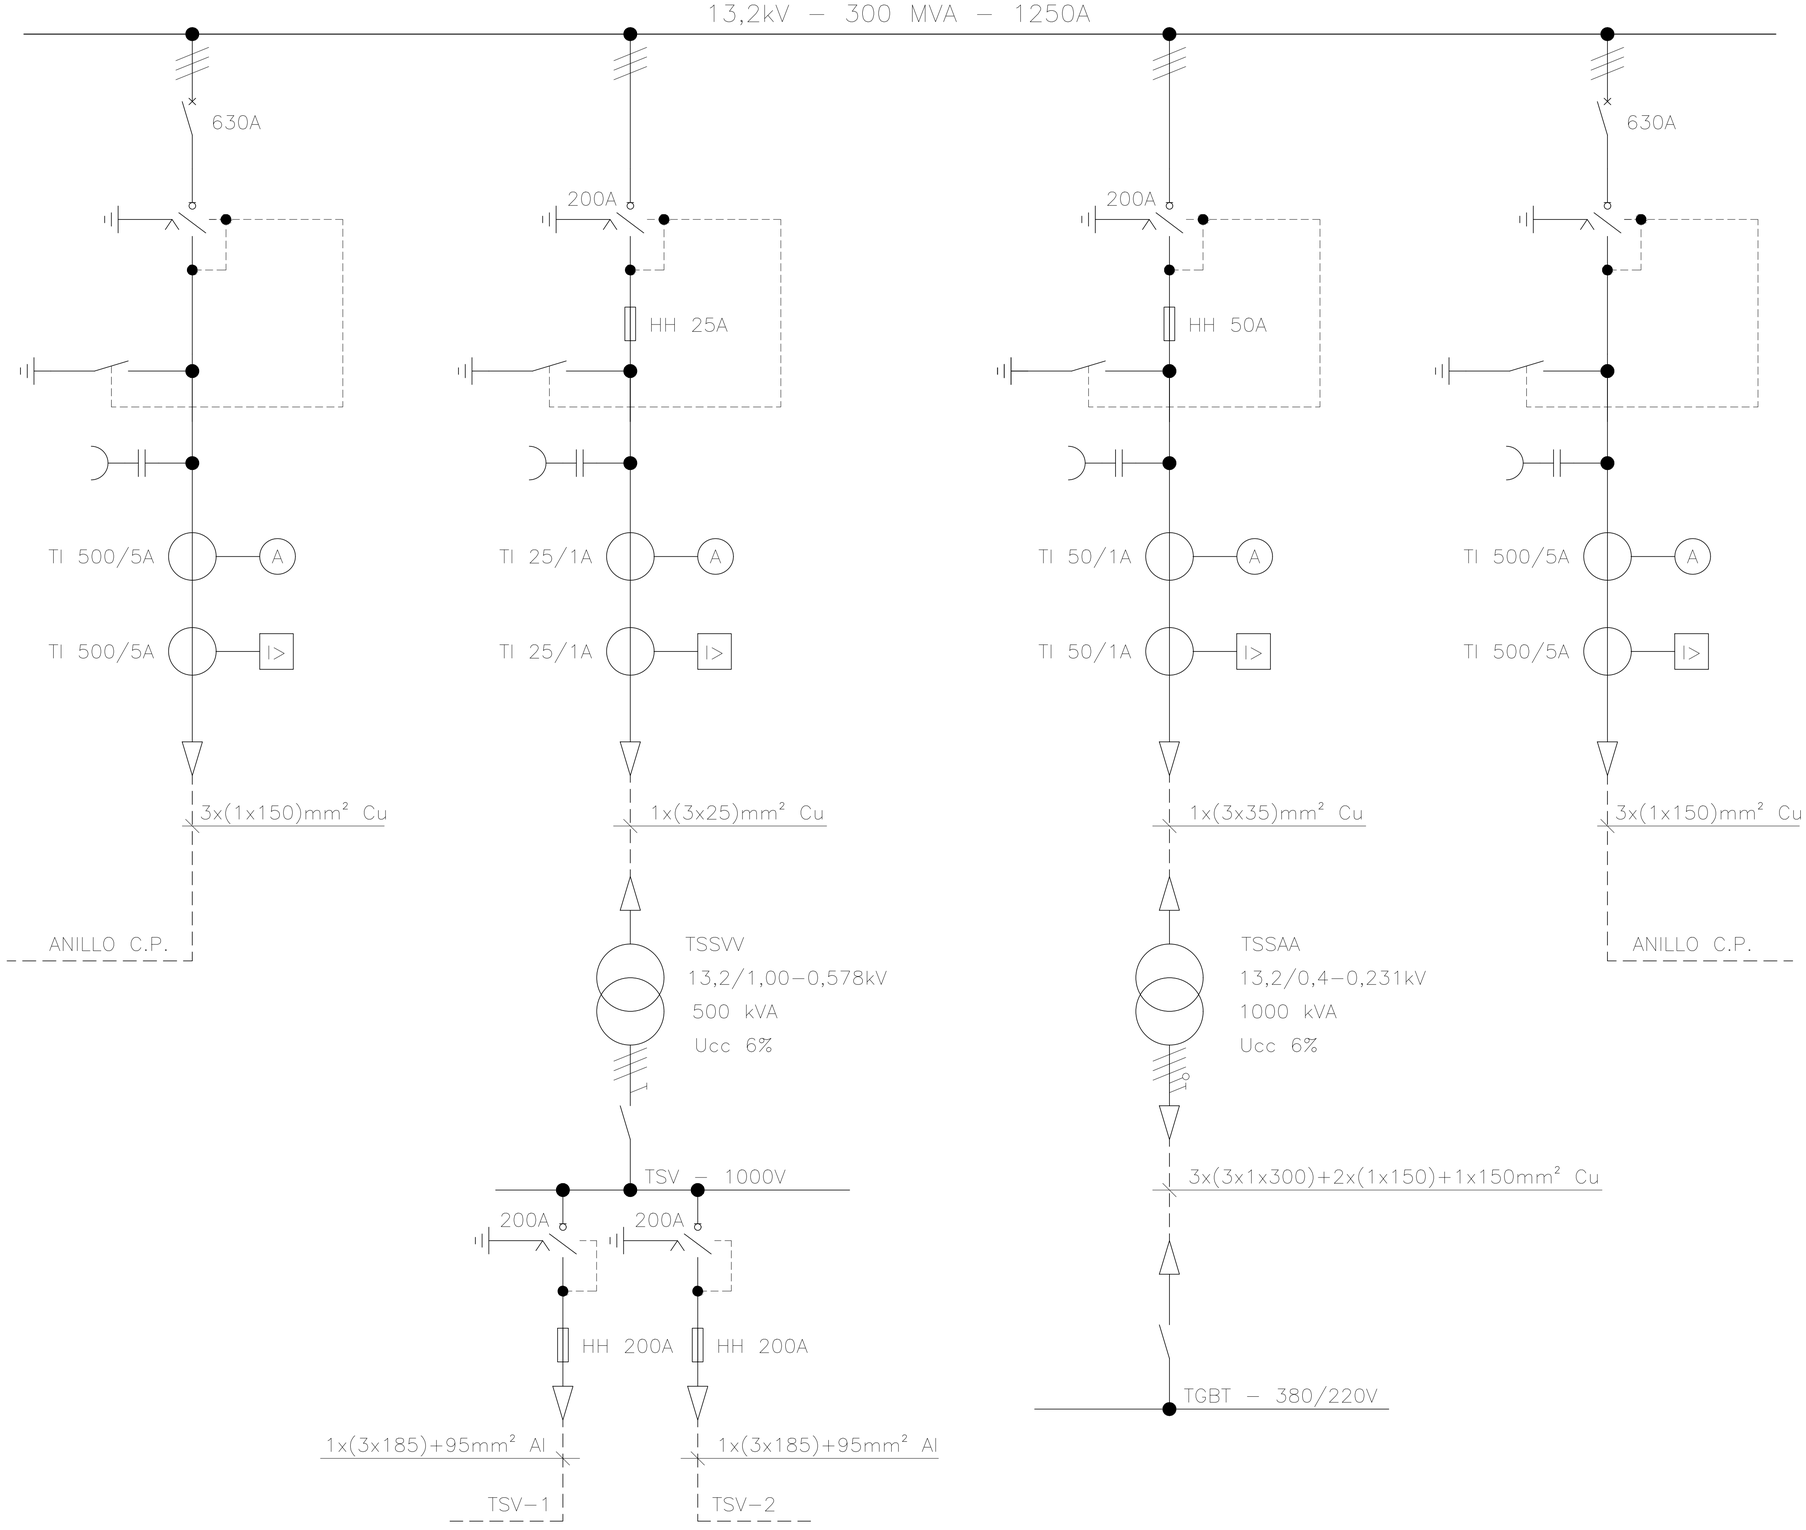

REFERENCIAS

- INTERRUPTOR DE VACIO 630A
- SECCIONADOR DE TRES POSICIONES
- DETECTOR DE TENSION CAPACITIVO CON CONTACTO INDICADOR Y DISPLAY
- SECCIONADOR DE PUESTA A TIERRA
- HH — FUSIBLE MT
- TI — TRANSFORMADOR DE CORRIENTE
- A — MEDICION AMPEROMÉTRICA
- I> — PROTECCION DE SOBRECORRIENTE

NOTAS:

EL PRESENTE PLANO ES INDICATIVO. LA CONTRATISTA CONFECCIONARA LOS PLANOS DE DETALLE DEFINITIVO, QUE DEBERAN SER APROBADOS POR LA D.G.O.INF.U Y LA INSPECCION DE OBRA. EL PLANO PRESENTADO POR LA CONTRATISTA ESTARA EN UN TODO DE ACUERDO CON LA NORMATIVA VIGENTE.
TODAS LAS MEDIDAS Y NIVELES SE VERIFICARAN EN OBRA POR EL CONTRATISTA.
TODOS LOS DETALLES CONSTRUCTIVOS SERAN COORDINADOS Y COMPATIBILIZADOS EN OBRA.

PLANO NO APTO PARA CONSTRUCCION.

Ing. Mariano Miculicich
DIRECTOR

MODIFICACIONES:

REVISION	FECHA	DESCRIPCION
0	29/09/2025	EMISIÓN INICIAL
1	08/10/2025	PRIMERA REVISIÓN
2	06/02/2026	SEGUNDA REVISIÓN

Gobierno de la Ciudad de Buenos Aires

MINISTERIO DE INFRAESTRUCTURA
SUBSECRETARIA DE PROYECTOS Y OBRAS
DIRECCION GENERAL DE PROYECTOS

DGPRO

Obra: LÍNEA F			IF-2026-20223041-GCABA-APRA Plano N°
Plano: ESQUEMA UNIFILAR TÍPICO - CENTRO DE POTENCIA			LF-CP-GEN-POT-UF-001 1/1
Fecha: 06/02/2026	Eq. de Proyecto: UPU-ATEC-IATASA	Dibujó: N.V.	Revisó: M.M. Escala: S/E

6/2/2026 16:58 p. m.
LF-CP-GEN-POT-UF-001_2.dwg

CATENARIA RÍGIDA
SECTORES DE ALIMENTACIÓN Y DISTRIBUCIÓN ALIMENTADORES

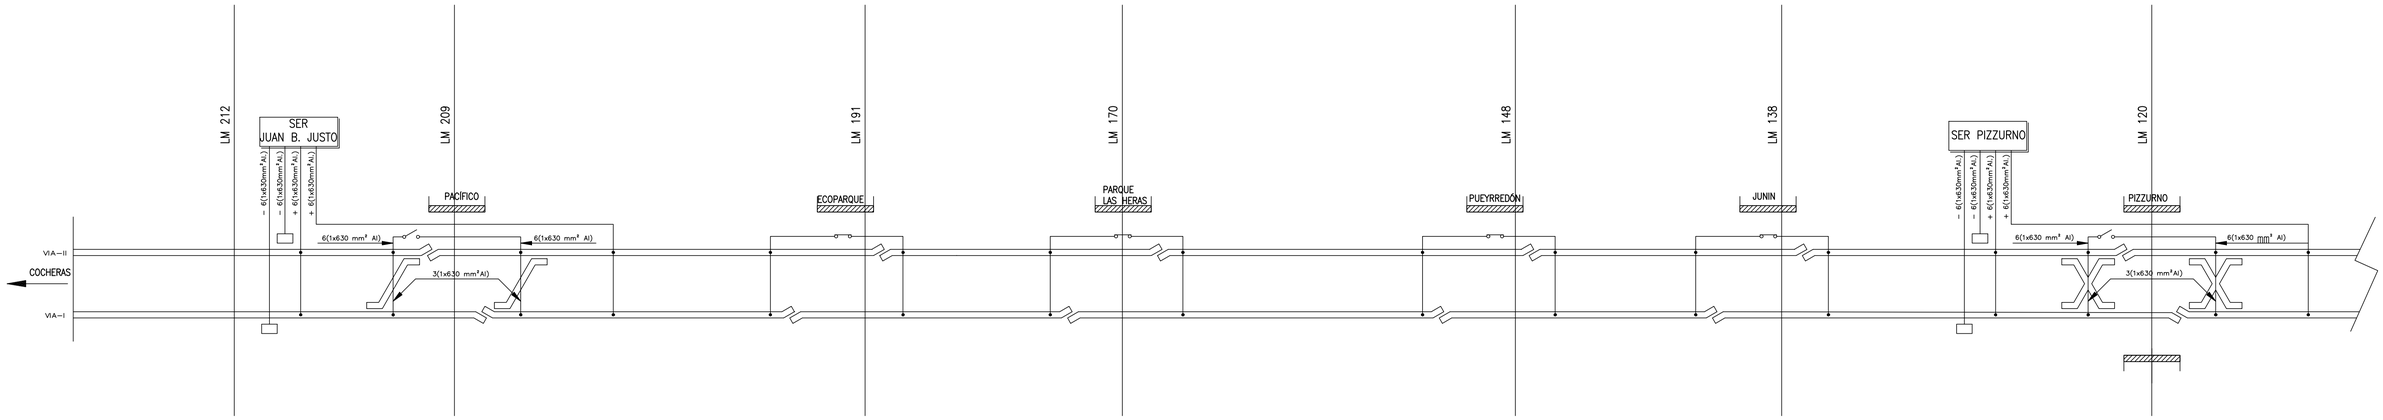

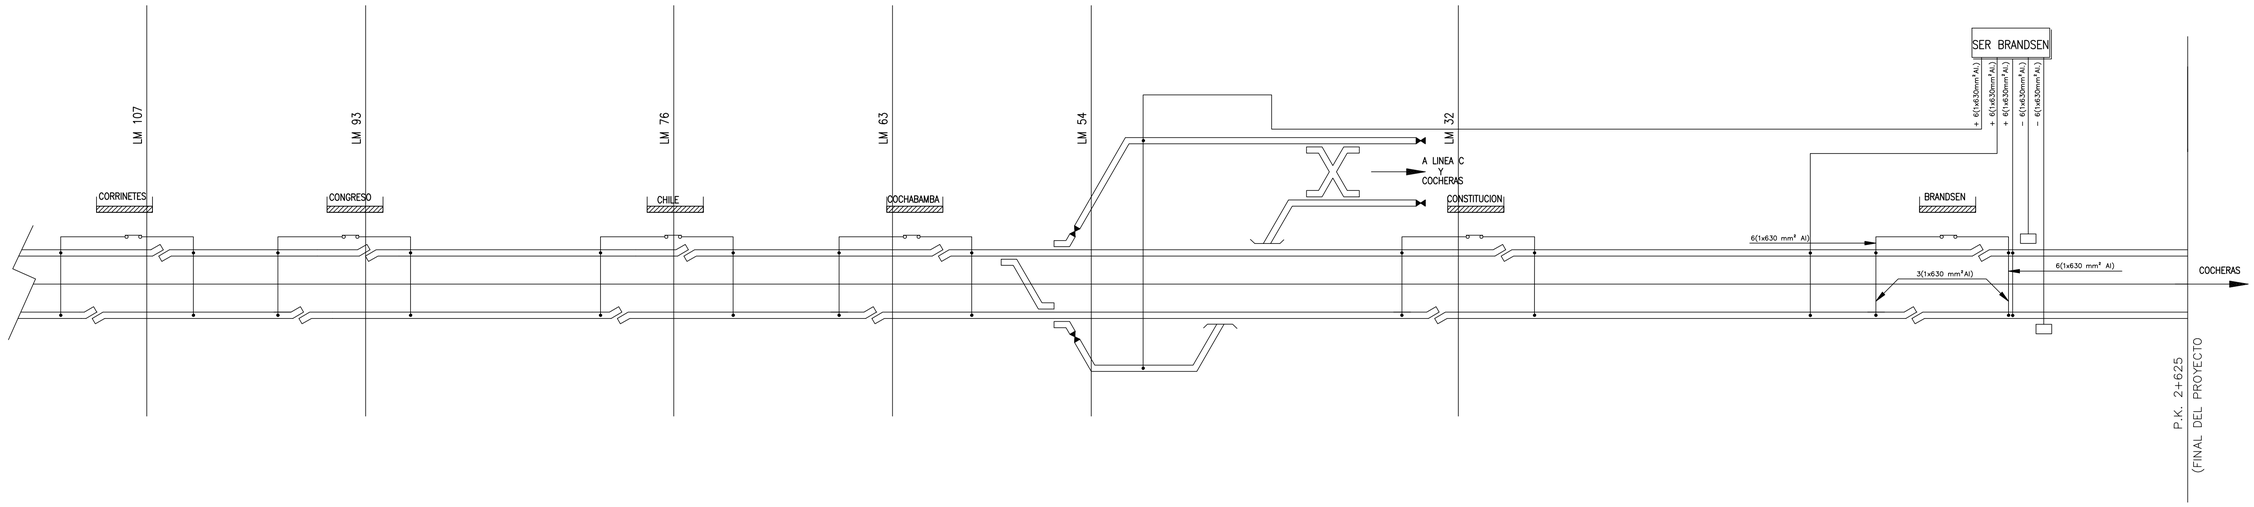

SIMBOLOGIA

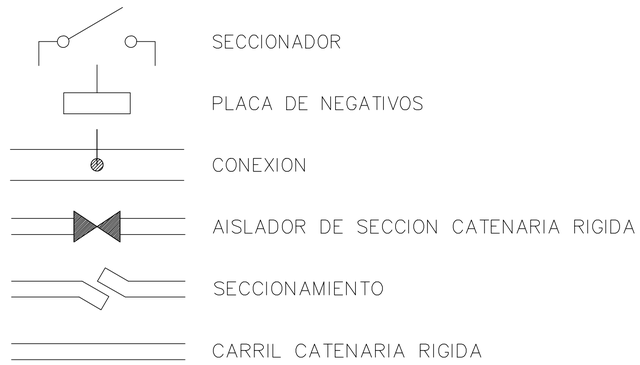

NOTAS:
EL PRESENTE PLANO ES INDICATIVO. LA CONTRATISTA CONFECCIONARA LOS PLANOS DE DETALLE DEFINITIVO, QUE DEBERAN SER APROBADOS POR LA D.G.IM.U.Y LA INSPECCION DE OBRA. EL PLANO PRESENTADO POR LA CONTRATISTA ESTARA EN UN TODO DE ACUERDO CON LA NORMATIVA VIGENTE
TODAS LAS MEDIDAS Y NIVELES SE VERIFICARAN EN OBRA POR EL CONTRATISTA
TODOS LOS DETALLES CONSTRUCTIVOS SERAN COORDINADOS Y COMPATIBILIZADOS EN OBRA

PLANO NO APTO PARA CONSTRUCCION.

Ing. Mariano Miculicich
DIRECTOR

MODIFICACIONES:

REVISION	FECHA	DESCRIPCION
0	06/02/2026	EMISIÓN INICIAL

Gobierno de la Ciudad de Buenos Aires

MINISTERIO DE INFRAESTRUCTURA
SUBSECRETARIA DE PROYECTOS Y OBRAS
DIRECCION GENERAL DE PROYECTOS

DGPRO

Obra: LÍNEA F				IF-2026-20223041-GCABA-APRA	Plano N°
Plano: SECTORES DE ALIMENTACIÓN Y DISTRIBUCIÓN ALIMENTADORES				LF-GL-GEN-POT-PL-001	1/1
Fecha: 06/02/2026	Eq. de Proyecto: UPU-ATEC-IATASA	Dibujó: N.V.	Revisó: M.M.	Escala: S/E	

5/2/2026 10:49 a. m.
LF-GL-GEN-POT-PL-001_ 0.dwg

ESQUEMA UNIFILAR SUBESTACIÓN RECTIFICADORA BRANDSEN

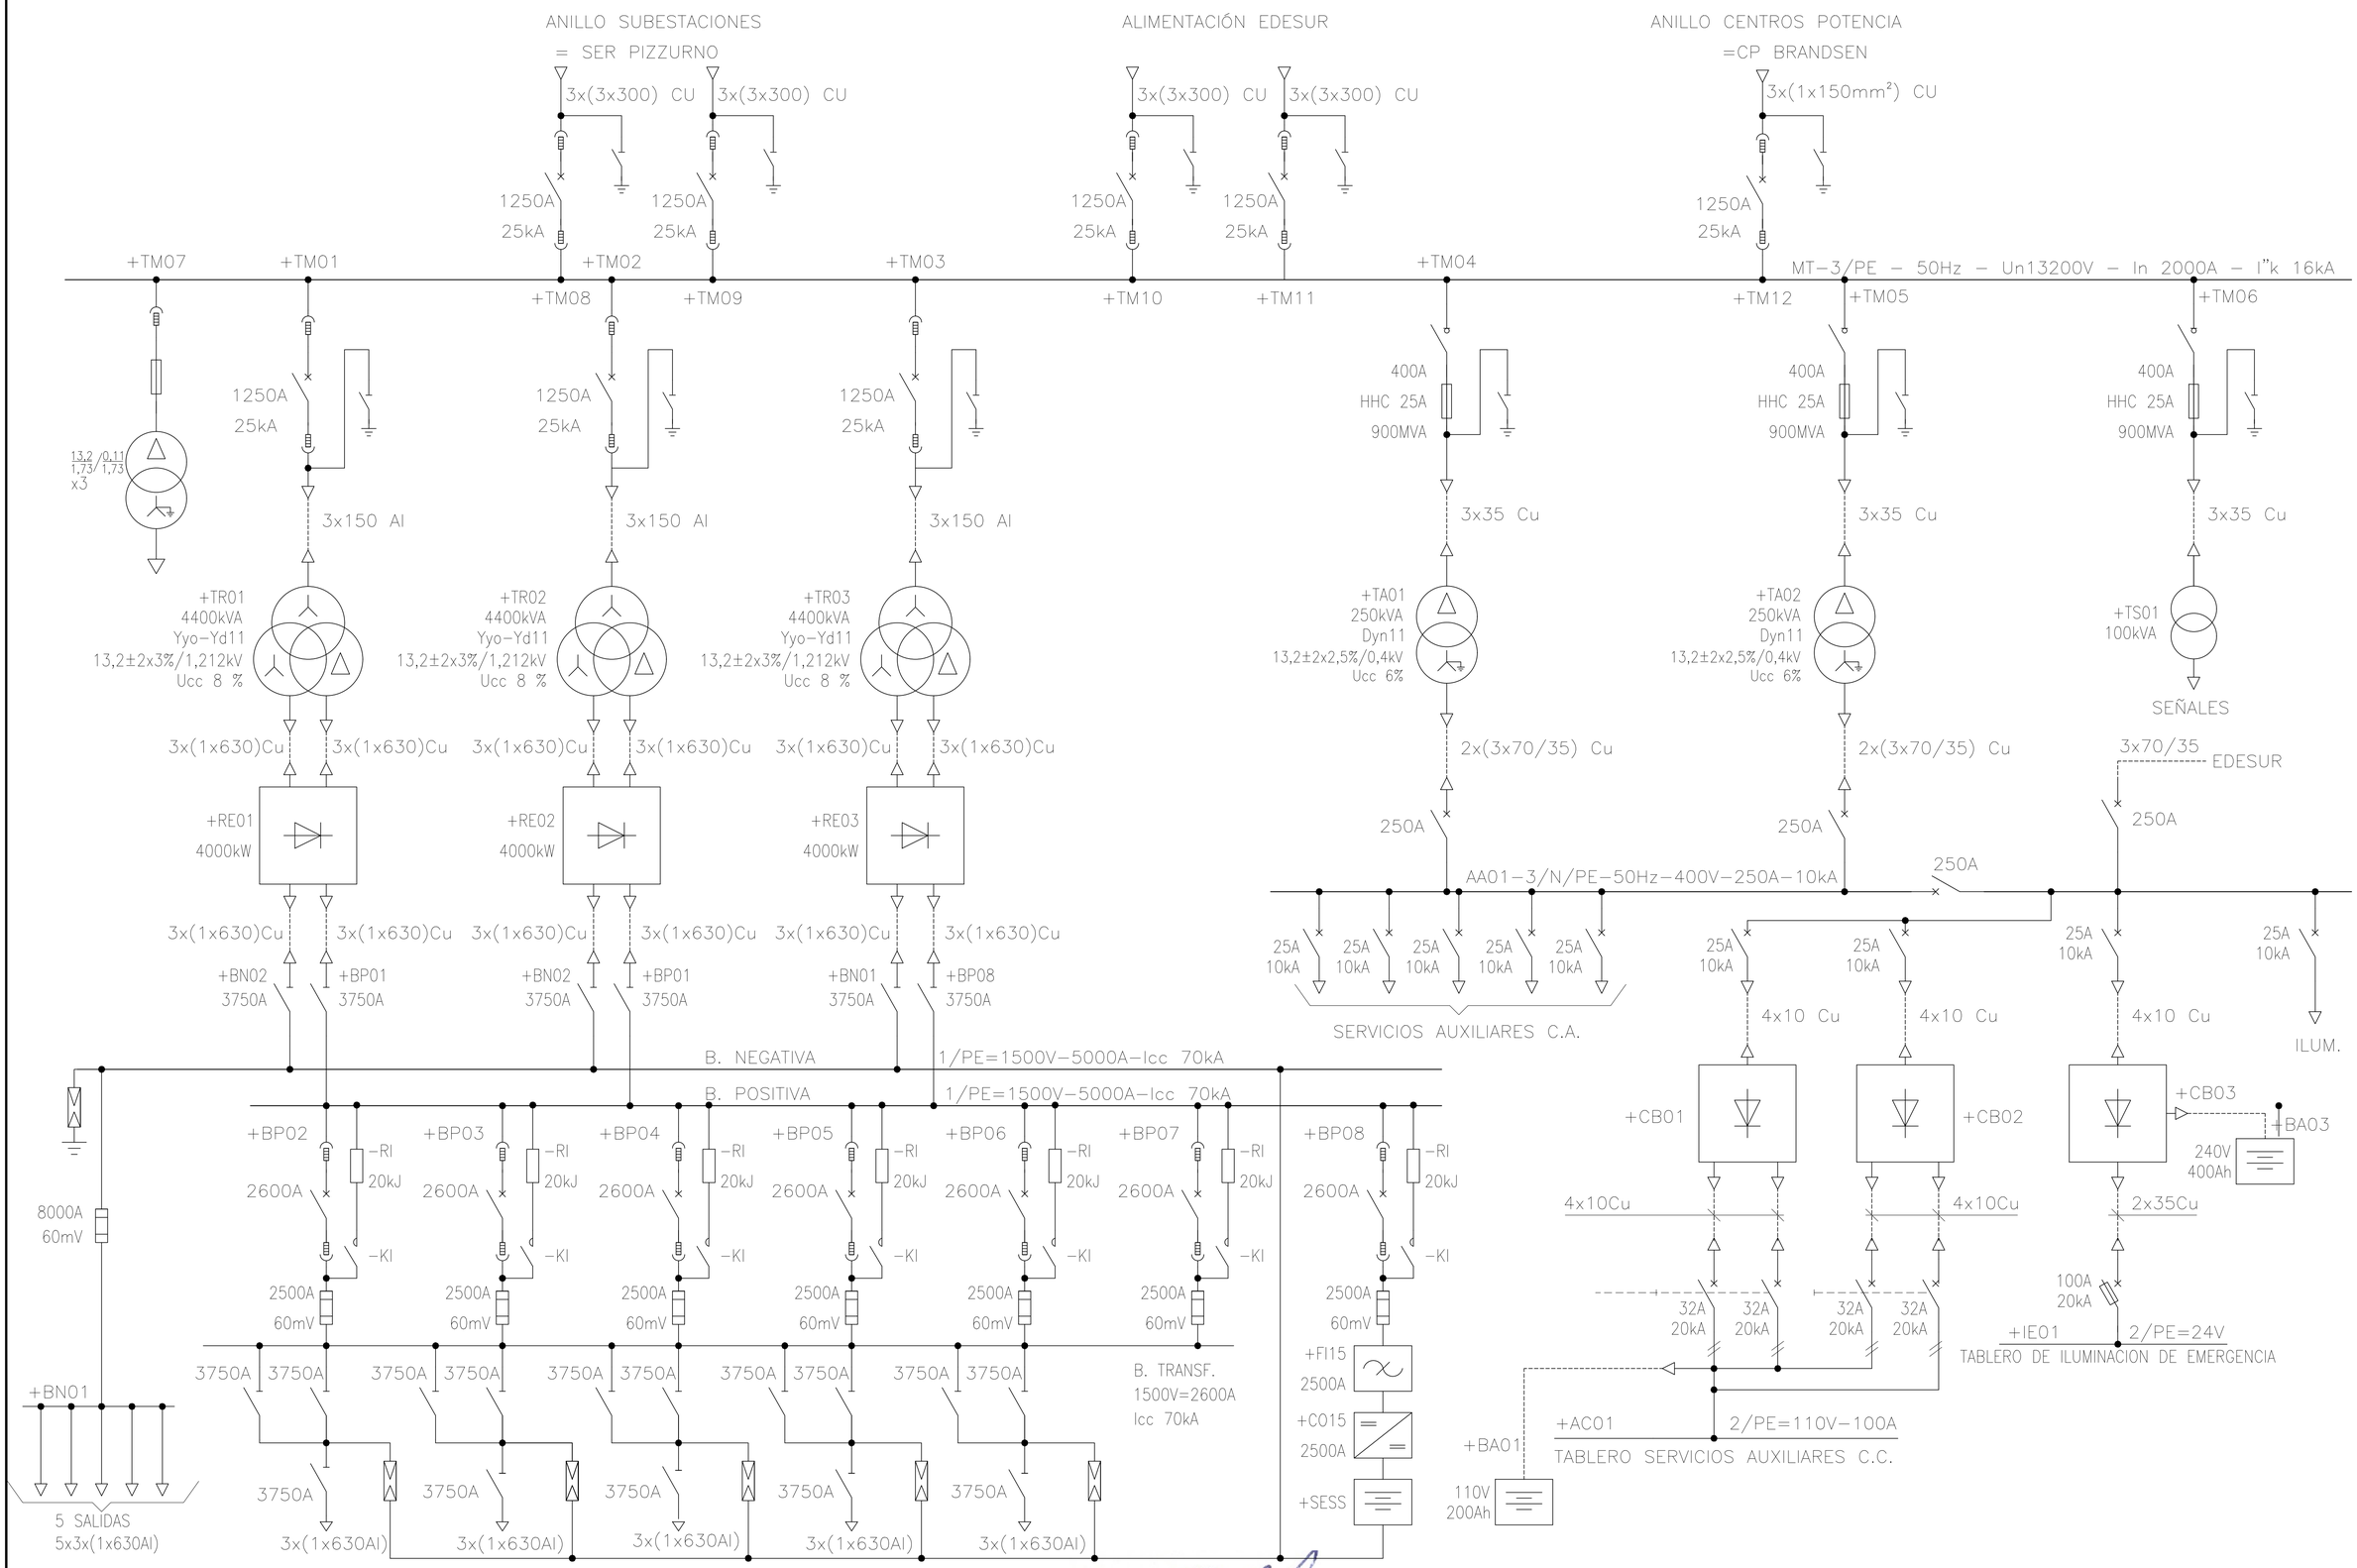

NOTAS:
EL PRESENTE PLANO ES INDICATIVO. LA CONTRATISTA CONFECCIONARA LOS PLANOS DE DETALLE DEFINITIVO, QUE DEBERAN SER APROBADOS POR LA D.G.O.INF.U Y LA INSPECCION DE OBRA. EL PLANO PRESENTADO POR LA CONTRATISTA ESTARA EN UN TODO DE ACUERDO CON LA NORMATIVA VIGENTE.
TODAS LAS MEDIDAS Y NIVELES SE VERIFICARAN EN OBRA POR EL CONTRATISTA.
TODOS LOS DETALLES CONSTRUCTIVOS SERAN COORDINADOS Y COMPATIBILIZADOS EN OBRA.

PLANO NO APTO PARA CONSTRUCCION.

Ing. Mariano Miculicich
DIRECTOR

MODIFICACIONES:

REVISION	FECHA	DESCRIPCION
0	29/09/2023	EMISIÓN INICIAL
1	08/10/2025	PRIMERA REVISIÓN
2	06/02/2026	SEGUNDA REVISIÓN

Gobierno de la Ciudad de Buenos Aires

MINISTERIO DE INFRAESTRUCTURA
SUBSECRETARIA DE PROYECTOS Y OBRAS
DIRECCION GENERAL DE PROYECTOS

DGPRO

Obra: LÍNEA F			IF-2026-20223041-GCABA-APRA Plano N°
Plano: ESQUEMA UNIFILAR - SUBESTACIÓN RECTIFICADORA BRANDSEN			LF-SE-GEN-POT-UF-001
Fecha: 06/02/2026	Eq. de Proyecto: UPU-ATEC-IATASA	Dibujó: N.V.	Revisó: M.M. Escala: S/E 1/1

6/2/2026 16:45 p. m.
LF-SE-GEN-POT-UF-001_2.dwg

ESQUEMA UNIFILAR SUBESTACIÓN RECTIFICADORA PIZZURNO

ANILLO SUBESTACIONES
= SER JUAN B. JUSTO

ALIMENTACIÓN EDENOR

ANILLO SUBESTACIONES
= SER BRANDSEN

ANILLO CENTROS POTENCIA
=CP JUNÍN =CP PIZZURNO

3x(3x300) CU | 3x(3x300) CU | 3x(3x300) CU | 3x(3x300) CU | 3x(3x300) CU | 3x(3x300) CU | 3x(1x150) CU | 3x(1x150) CU

1250A 25kA

+TM07 +TM08 +TM01 +TM09 +TM02 +TM10 +TM03 +TM11 +TM12 +TM13 +TM04 +TM14 +TM15 +TM05 +TM06

MT–3/PE – 50Hz – Un13200V – In 2000A – I"k 16kA

13,2 /0,11
1,73/ 1,73
x3

3x150 Al

+TR01 +TR02 +TR03
4400kVA
Yyo–Yd11
13,2±2x3%/1,212kV
Ucc 8 %

3x(1x630)Cu

+RE01 +RE02 +RE03
4000kW

+BN02 +BP01 +BN01 +BP08
3750A

B. NEGATIVA 1/PE=1500V–5000A–Icc 70kA

B. POSITIVA 1/PE=1500V–5000A–Icc 70kA

+BP02 +BP03 +BP04 +BP05 +BP06 +BP07

–RI 20kJ –KI

2600A

2500A
60mV

3750A

3x(1x630Al)

8000A
60mV

+BN01

4 SALIDAS
4x3x(1x630Al)

B. TRANSF.
1500V=2600A
Icc 70kA

+FI15 2500A

+C015 2500A

+SESS

400A
HHC 25A
900MVA

3x35 Cu

+TA01
250kVA
Dyn11
13,2±2x2,5%/0,4kV
Ucc 6%

2x(3x70/35) Cu

250A

AA01–3/N/PE–50Hz–400V–250A–10kA

25A 10kA

SERVICIOS AUXILIARES C.A.

+TA02
250kVA
Dyn11
13,2±2x2,5%/0,4kV
Ucc 6%

4x10 Cu

4x10Cu

32A 20kA

+AC01 2/PE=110V–100A
TABLERO SERVICIOS AUXILIARES C.C.

+BA01
110V
200Ah

+TS01
100kVA

SEÑALES

3x70/35 EDESUR

+CB01 +CB02 +CB03

+BA03
240V
400Ah

2x35Cu

100A
20kA

+IE01 2/PE=24V
TABLERO DE ILUMINACION DE EMERGENCIA

ILUM.

NOTAS:
1. EL PRESENTE PLANO ES INDICATIVO. LA CONTRATISTA CONFECCIONARA LOS PLANOS DE DETALLE DEFINITIVO, QUE DEBERAN SER APROBADOS POR LA D.G.O.INF.U Y LA INSPECCION DE OBRA. EL PLANO PRESENTADO POR LA CONTRATISTA ESTARA EN UN TODO DE ACUERDO CON LA NORMATIVA VIGENTE.
2. TODAS LAS MEDIDAS Y NIVELES SE VERIFICARAN EN OBRA POR EL CONTRATISTA.
3. TODOS LOS DETALLES CONSTRUCTIVOS SERAN COORDINADOS Y COMPATIBILIZADOS EN OBRA.

PLANO NO APTO PARA CONSTRUCCION.

Ing. Mariano Miculicich
DIRECTOR

MODIFICACIONES:

REVISION	FECHA	DESCRIPCION
0	29/09/2025	EMISIÓN INICIAL
1	08/10/2025	PRIMERA REVISIÓN
2	06/02/2026	SEGUNDA REVISIÓN

Gobierno de la Ciudad de Buenos Aires

MINISTERIO DE INFRAESTRUCTURA
SUBSECRETARIA DE PROYECTOS Y OBRAS
DIRECCION GENERAL DE PROYECTOS

DGPRO

Obra: LÍNEA F				IF-2026-20223041-GCABA-APRA	Plano N°
Plano: ESQUEMA UNIFILAR - SUBESTACIÓN RECTIFICADORA PIZZURNO				LF-SE-GEN-POT-PL-002	1/1
Fecha: 06/02/2026	Eq. de Proyecto: UPU-ATEC-IATASA	Dibujó: N.V.	Revisó: M.M.	Escala: S/E	

6/2/2026 16:34 p. m.
LF-SE-GEN-POT-UF-002_2.dwg

ESQUEMA UNIFILAR SUBESTACIÓN RECTIFICADORA JUAN B. JUSTO

ANILLO CENTROS POTENCIA
= CP JUAN B. JUSTO

ALIMENTACIÓN EDENOR

ANILLO SUBESTACIONES
= SER PIZZURNO

3x(1x150mm²) CU
3x(3x300) CU
3x(3x300) CU
3x(3x300) CU
3x(3x300) CU

1250A 25kA

+TM07 +TM01 +TM02 +TM08 +TM03 +TM09 +TM10 +TM04 +TM11 +TM12 +TM05 +TM06

MT–3/PE – 50Hz – Un 13200V – In 2000A – I"k 16kA

13,2 /0,11
1,73/ 1,73
x3

400A HHC 25A 900MVA

3x150 Al
3x35 Cu

+TR01 +TR02 +TR03
4400kVA
Yyo–Yd11
13,2±2x3%/1,212kV
Ucc 8 %

+TA01 +TA02
250kVA
Dyn11
13,2±2x2,5%/0,4kV
Ucc 6%

+TS01
100kVA
SEÑALES

3x(1x630)Cu
2x(3x70/35) Cu
3x70/35
EDESUR

+RE01 +RE02 +RE03
4000kW

250A
AA01–3/N/PE–50Hz–400V–250A–10kA

25A 10kA
SERVICIOS AUXILIARES C.A.

+BN02 +BP01 +BN02 +BP01 +BN01 +BP08
3750A

4x10 Cu
ILUM.

B. NEGATIVA 1/PE=1500V–5000A–Icc 70kA
B. POSITIVA 1/PE=1500V–5000A–Icc 70kA

+CB01 +CB02 +CB03

+BA03
240V
400Ah

2x35Cu

+BP02 +BP03 +BP04 +BP05 +BP06 +BP07
–RI 20kJ
–KI
2600A
2500A 60mV

4x10Cu

100A 20kA
+IE01 2/PE=24V
TABLERO DE ILUMINACION DE EMERGENCIA

32A 20kA

8000A 60mV

+BN01
4 SALIDAS
4x3x(1x630Al)

3750A
3x(1x630Al)

B. TRANSF.
1500V=2600A
Icc 70kA

+FI15 2500A
+C015 2500A
+SESS

+AC01 2/PE=110V–100A
TABLERO SERVICIOS AUXILIARES C.C.

+BA01
110V
200Ah

NOTAS:
EL PRESENTE PLANO ES INDICATIVO. LA CONTRATISTA CONFECCIONARA LOS PLANOS DE DETALLE DEFINITIVO, QUE DEBERAN SER APROBADOS POR LA D.G.INF.U Y LA INSPECCION DE OBRA. EL PLANO PRESENTADO POR LA CONTRATISTA ESTARA EN UN TODO DE ACUERDO CON LA NORMATIVA VIGENTE.
TODAS LAS MEDIDAS Y NIVELES SE VERIFICARAN EN OBRA POR EL CONTRATISTA.
TODOS LOS DETALLES CONSTRUCTIVOS SERAN COORDINADOS Y COMPATIBILIZADOS EN OBRA.

PLANO NO APTO PARA CONSTRUCCION.

Ing. Mariano Miculicich
DIRECTOR

MODIFICACIONES:

REVISION	FECHA	DESCRIPCION
0	06/10/2023	EMISIÓN INICIAL
1	06/02/2026	PRIMERA REVISIÓN

Gobierno de la Ciudad de Buenos Aires

MINISTERIO DE INFRAESTRUCTURA
SUBSECRETARIA DE PROYECTOS Y OBRAS
DIRECCION GENERAL DE PROYECTOS

DGPRO

Obra: LÍNEA F.
IF-2026-20223041-GCABA-APRA
Plano: ESQUEMA UNIFILAR - SUBESTACIÓN RECTIFICADORA JUAN B. JUSTO
LF-SE-GEN-POT-UF-003
Fecha: 06/02/2026 | Eq. de Proyecto: UPU-ATEC-IATASA | Dibujó: N.V. | Revisó: M.M. | Escala: S/E
Plano N° 1/1

6/2/2026 16:34 p. m.
LF-SE-GEN-POT-UF-003_1.dwg

G O B I E R N O DE LA C I U D A D DE B U E N O S A I R E S

"2026 - Año del 30° Aniversario de la sanción de la Constitución de la Ciudad Autónoma de Buenos Aires"

Hoja Adicional de Firmas
Informe gráfico

Número: IF-2026-20223041-GCABA-APRA

Buenos Aires, Miércoles 29 de Abril de 2026

Referencia: AMB25012-GCBA-LINEA F SUBTE-EIA-Cap10 Anexos - Planos- R0

El documento fue importado por el sistema GEDO con un total de 82 pagina/s.

Digitally signed by Comunicaciones Oficiales
Date: 2026.04.29 11:29:44 -03:00

Emiliano Guzman
Asesor administrativo
AGENCIA DE PROTECCIÓN AMBIENTAL
AREA VICEJEFE DE GOBIERNO

Digitally signed by Comunicaciones Oficiales
Date: 2026.04.29 11:29:50 -03:00