INTERFERENCIAS
SERVICOS CLOACALES, PLUVIALES, AGUA CORRIENTE
ESCALA 1:500

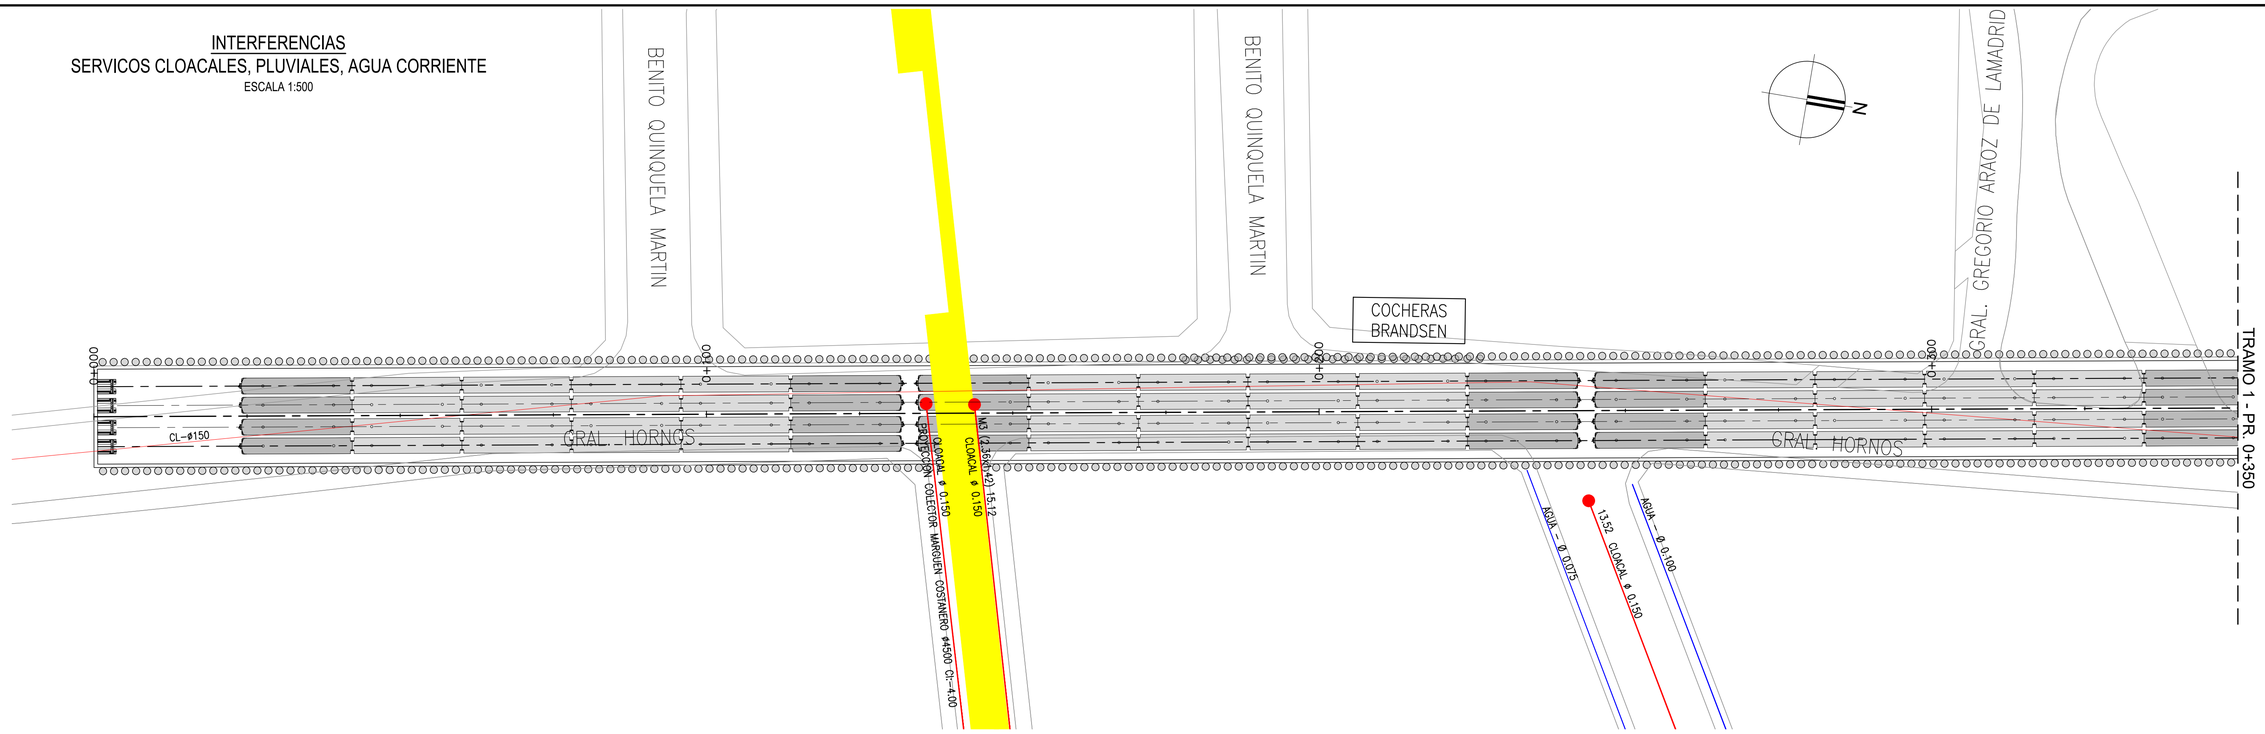

INTERFERENCIAS
GAS, TELEFONIA, ELECTRICIDAD, FIBRA OPTICA
ESCALA 1:500

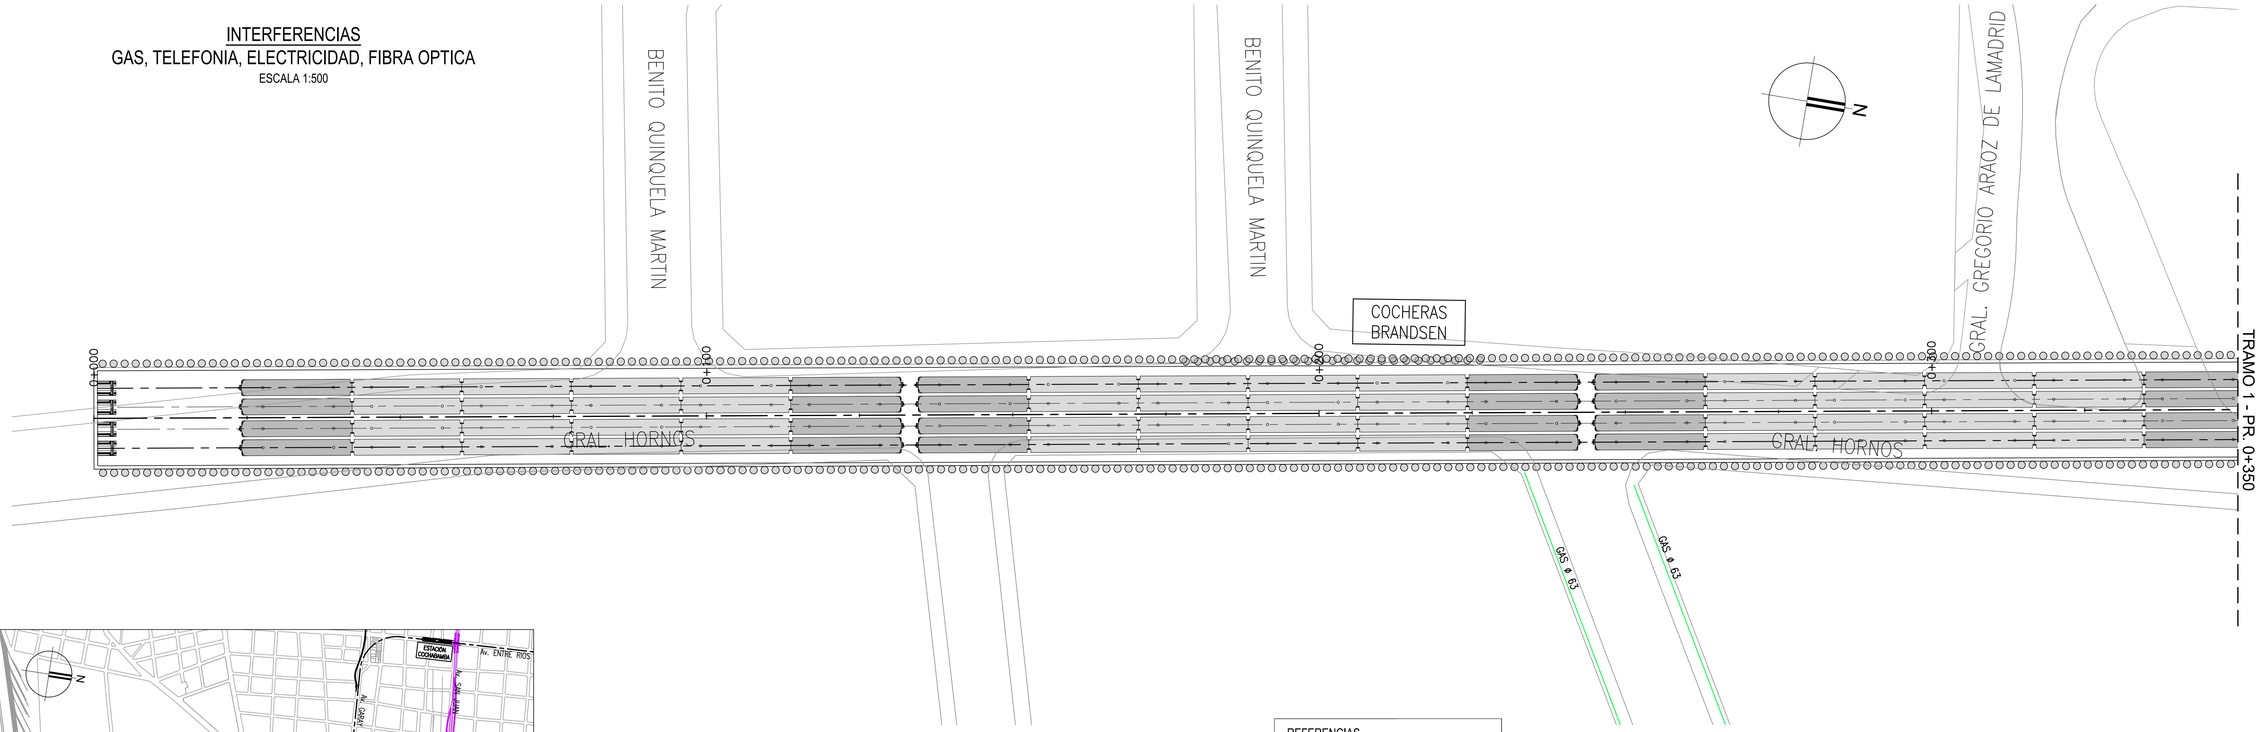

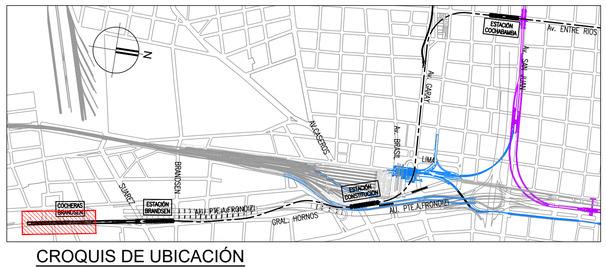

CROQUIS DE UBICACIÓN

REFERENCIAS
- RED CLOACAL
- RED PLUVIAL
- RED AGUA
- RED ELECTRICA
- RED GAS
- RED TELEFONICA
- RED FIBRA OPTICA MULTICANAL

0 10 20 30m
ESCALA 1:500

NOTAS:
EL PRESENTE PLANO ES INDICATIVO; LA CONTRATISTA CONFECCIONARA LOS PLANOS DE DETALLE DEFINITIVO, QUE DEBERAN SER APROBADOS POR LA D.G.O.INF.U Y LA INSPECCION DE OBRA. EL PLANO PRESENTADO POR LA CONTRATISTA ESTARA EN LA TODO DE ACUERDO CON LA NORMATIVA VIGENTE.
TODAS LAS MEDIDAS Y NIVELES SE VERIFICARAN EN OBRA POR EL CONTRATISTA.
TODOS LOS DETALLES CONSTRUCTIVOS SERAN COORDINADOS Y COMPATIBILIZADOS EN OBRA

PLANO NO APTO PARA CONSTRUCCION.

MODIFICACIONES:

REVISION	FECHA	DESCRIPCION
0	19/05/2025	EMISION INICIAL
1	06/05/2026	REVISIÓN DE PROYECTO

Gobierno de la Ciudad de Buenos Aires

MINISTERIO DE INFRAESTRUCTURA
SUBSECRETARIA DE PROYECTOS Y OBRAS
DIRECCION GENERAL DE PROYECTOS

DGPRO

Obra: LÍNEA F				IF-2026-28525919-GCABA-DGPRO	Plano N° 001
Plano: INTERFERENCIAS TRAMO 1 - PLANIMETRÍA GENERAL - PROG. 0+000 A 0+350				LF-GL-T01-INT-PL-001	
Fecha: 06/05/2026	Eq. de Proyecto: UPU-ATEC-IATASA	Dibujó: D.B.	Revisó: P.C.	Escala: 1:500	

8/5/2026 14:51 p. m.
LF-GL-T01-INT-PL-001a019_1.dwg

INTERFERENCIAS
SERVICOS CLOACALES, PLUVIALES, AGUA CORRIENTE
ESCALA 1:500

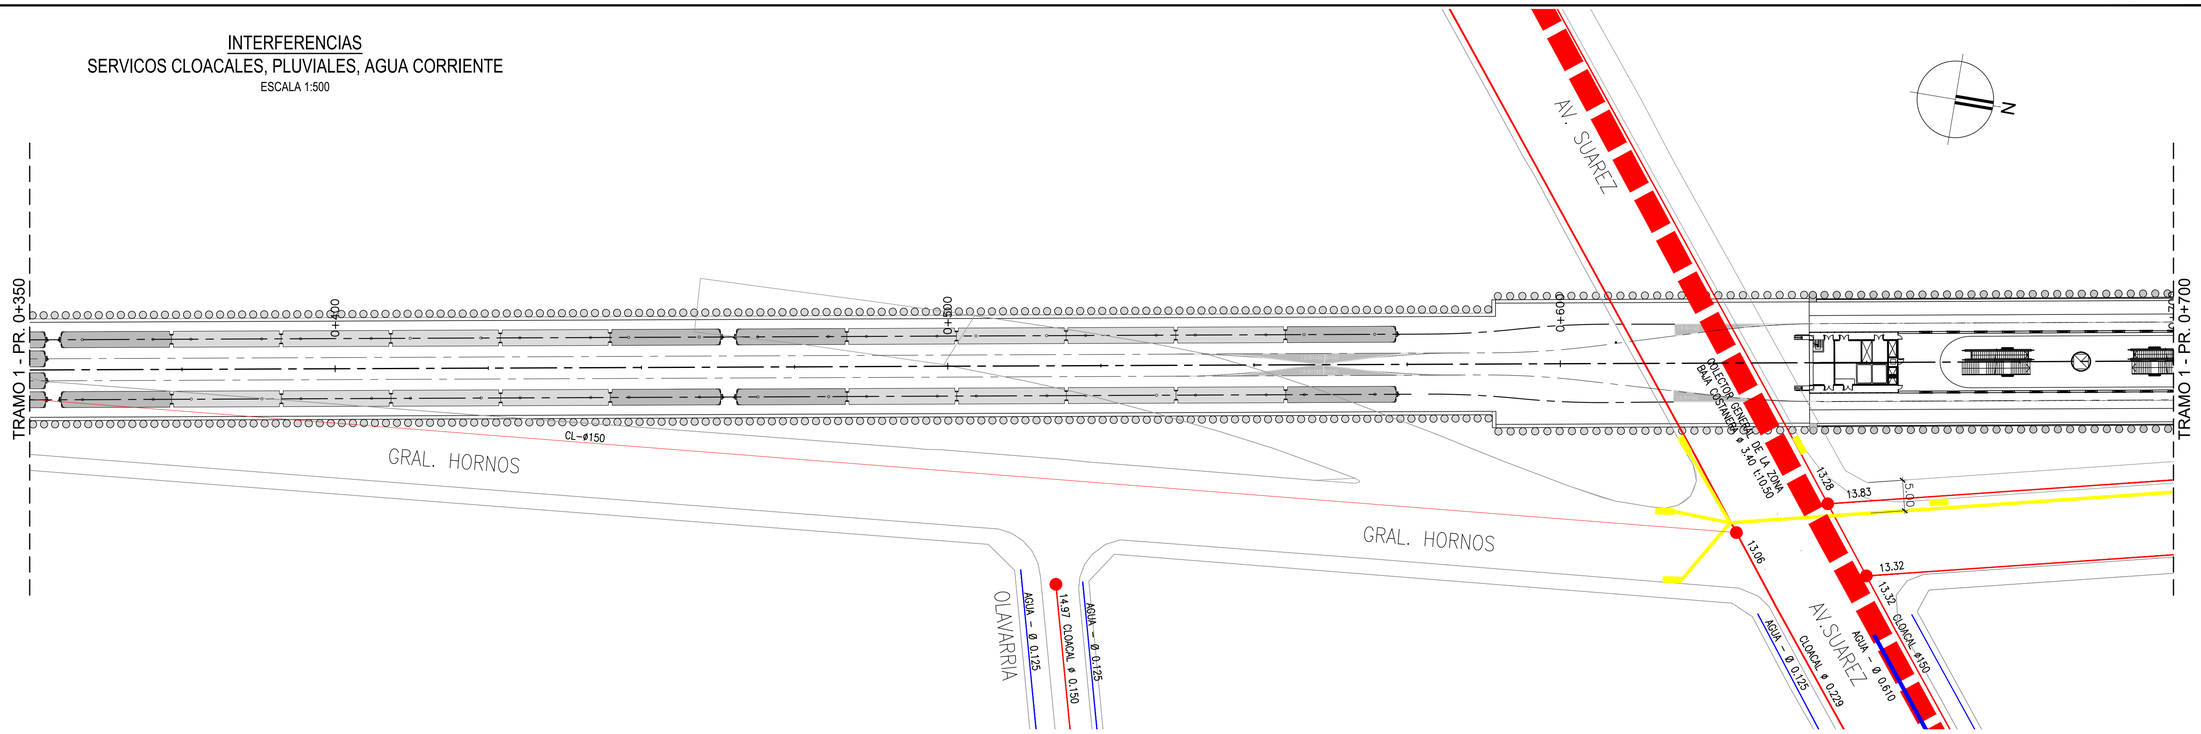

INTERFERENCIAS
GAS, TELEFONIA, ELECTRICIDAD, FIBRA OPTICA
ESCALA 1:500

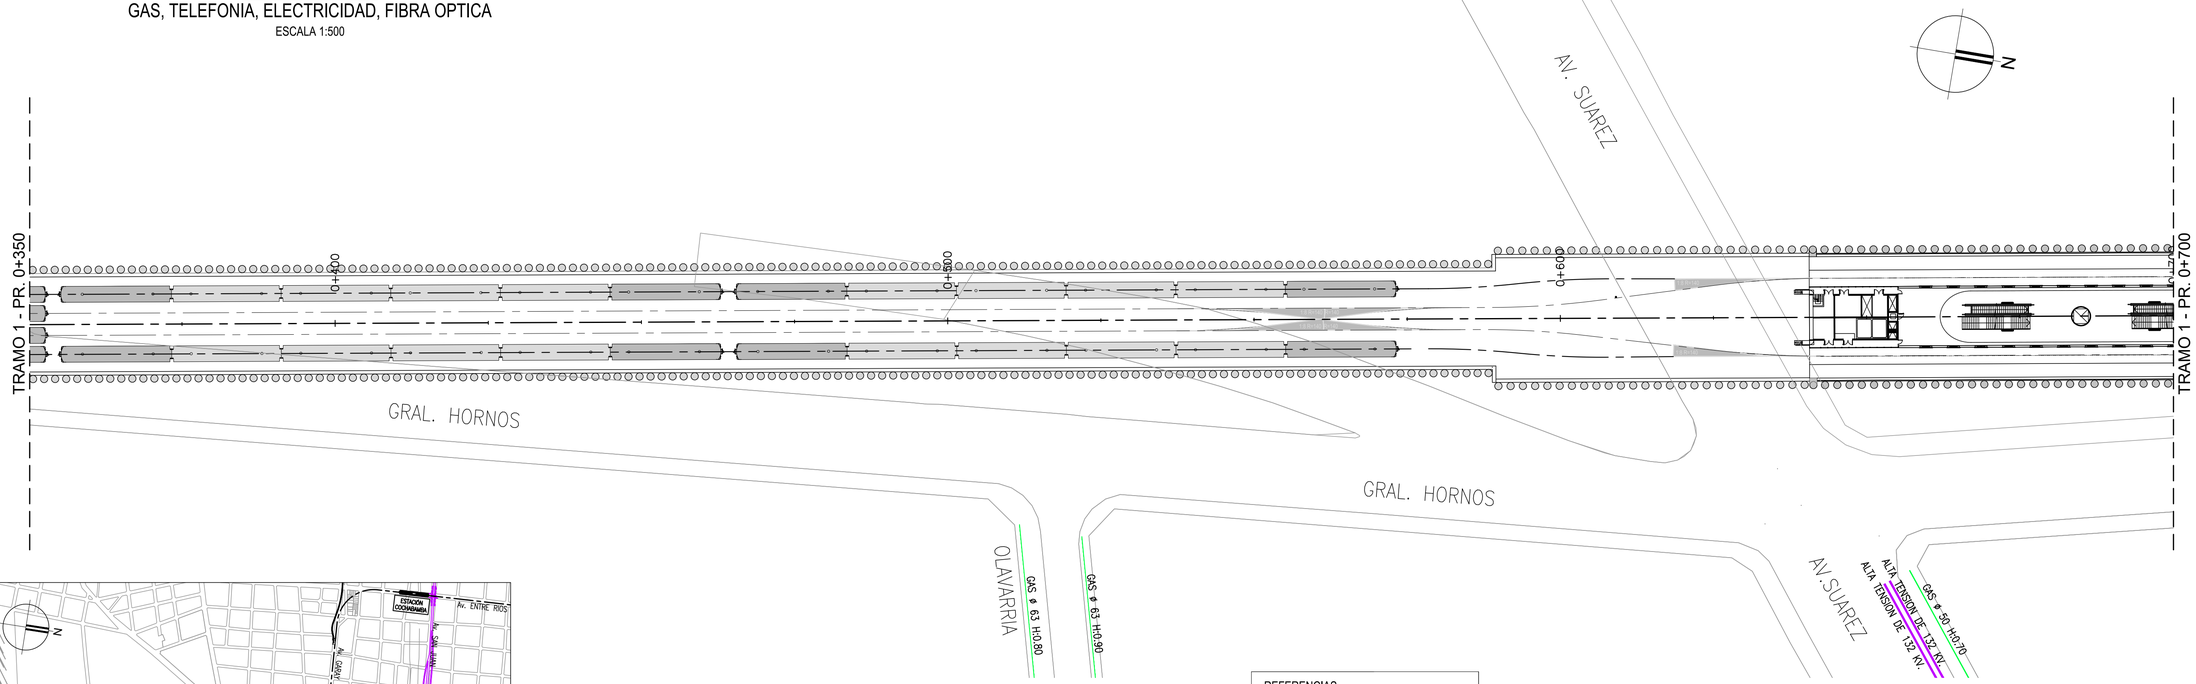

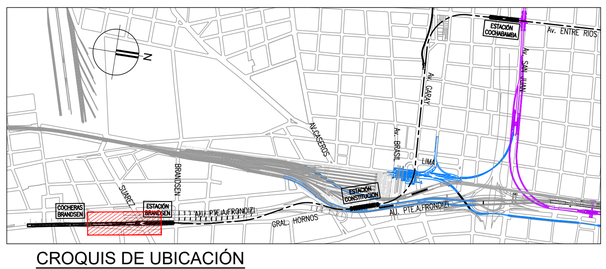

CROQUIS DE UBICACIÓN

REFERENCIAS
- RED CLOACAL
- RED PLUVIAL
- RED AGUA
- RED ELECTRICA
- RED GAS
- RED TELEFONICA
- RED FIBRA OPTICA MULTICANAL

0 10 20 30m
ESCALA 1:500

NOTAS:
EL PRESENTE PLANO ES INDICATIVO. LA CONTRATISTA CONFECCIONARA LOS PLANOS DE DETALLE DEFINITIVO, QUE DEBERAN SER APROBADOS POR LA D.G.O.INF.U Y LA INSPECCION DE OBRA. EL PLANO PRESENTADO POR LA CONTRATISTA ESTARA EN UN TODO DE ACUERDO CON LA NORMATIVA VIGENTE.
TODAS LAS MEDIDAS Y NIVELES SE VERIFICARAN EN OBRA POR EL CONTRATISTA.
TODOS LOS DETALLES CONSTRUCTIVOS SERAN COORDINADOS Y COMPATIBILIZADOS EN OBRA

PLANO NO APTO PARA CONSTRUCCION.

MODIFICACIONES:

REVISIÓN	FECHA	DESCRIPCION
0	19/05/2025	EMISION INICIAL
1	06/05/2026	REVISIÓN DE PROYECTO

Gobierno de la Ciudad de Buenos Aires

MINISTERIO DE INFRAESTRUCTURA
SUBSECRETARIA DE PROYECTOS Y OBRAS
DIRECCION GENERAL DE PROYECTOS

DGPRO

Obra: LÍNEA F				IF-2026-28525919-GCABA-DGPR	Plano N°
Plano: INTERFERENCIAS TRAMO 1 - PLANIMETRÍA GENERAL - PROG. 0+350 A 0+700				LF-GL-T01-INT-PL-002	002
Fecha: 06/05/2026	Eq. de Proyecto: UPU-ATEC-IATASA	Dibujó: D.B.	Revisó: P.C.	Escala: 1:500	

8/5/2026, 14:51 p. m.
LF-GL-T01-INT-PL-001a019_1.dwg

INTERFERENCIAS
SERVICOS CLOACALES, PLUVIALES, AGUA CORRIENTE
ESCALA 1:500

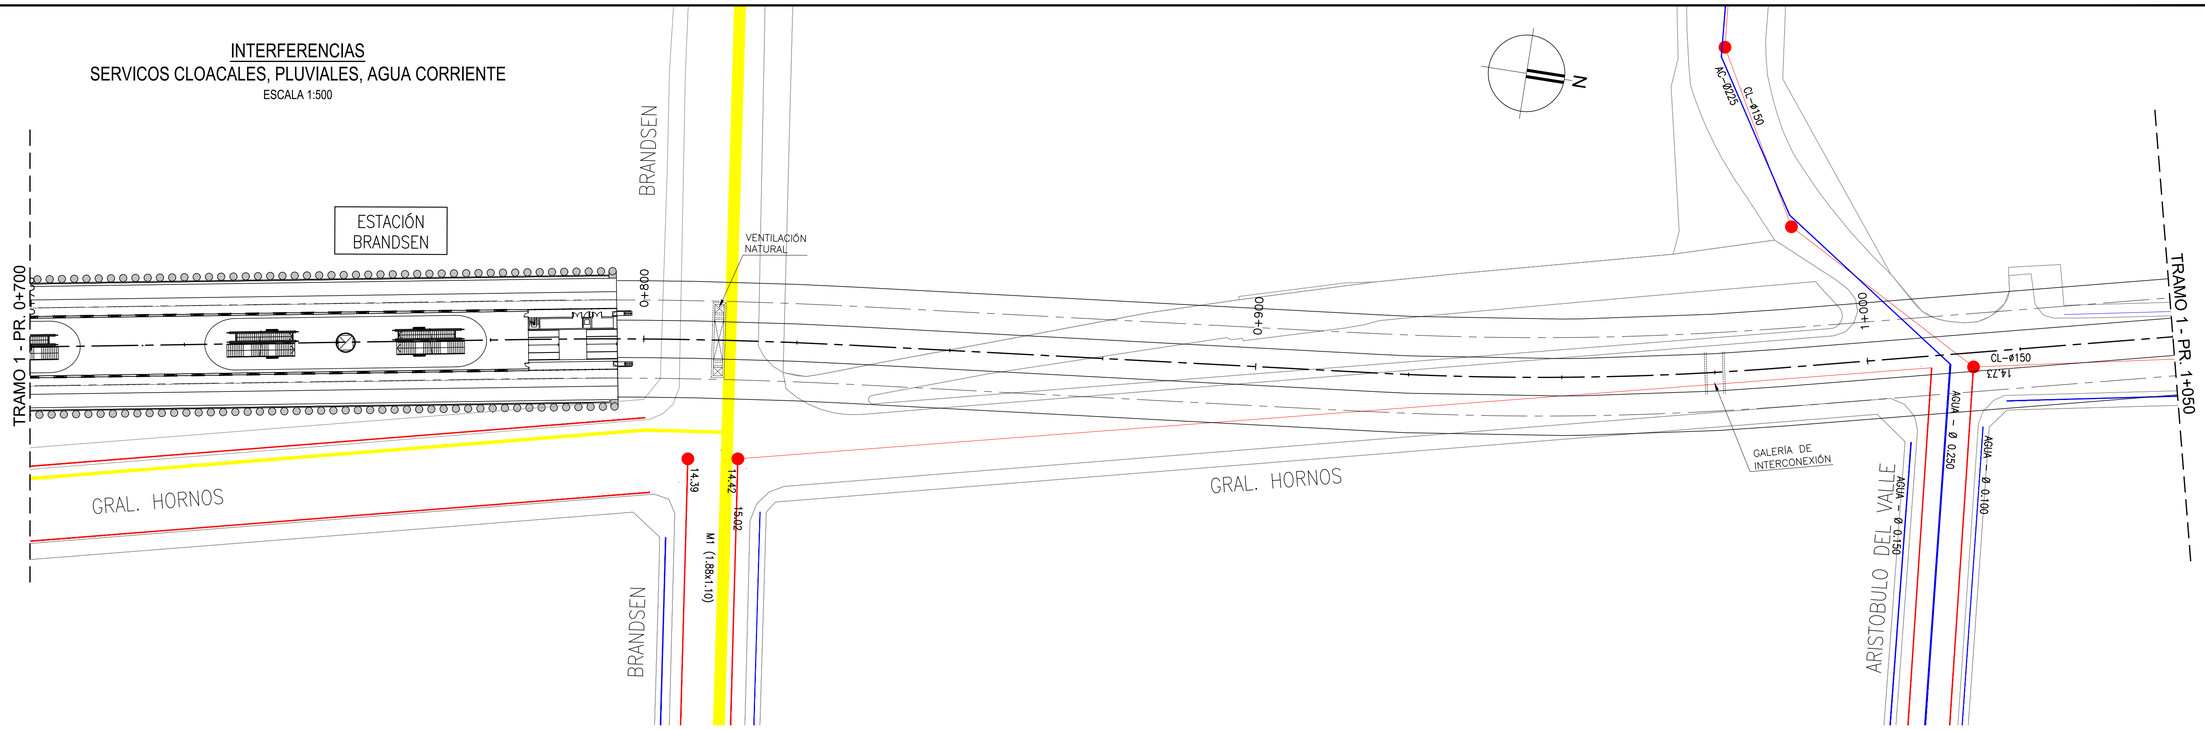

INTERFERENCIAS
GAS, TELEFONIA, ELECTRICIDAD, FIBRA OPTICA
ESCALA 1:500

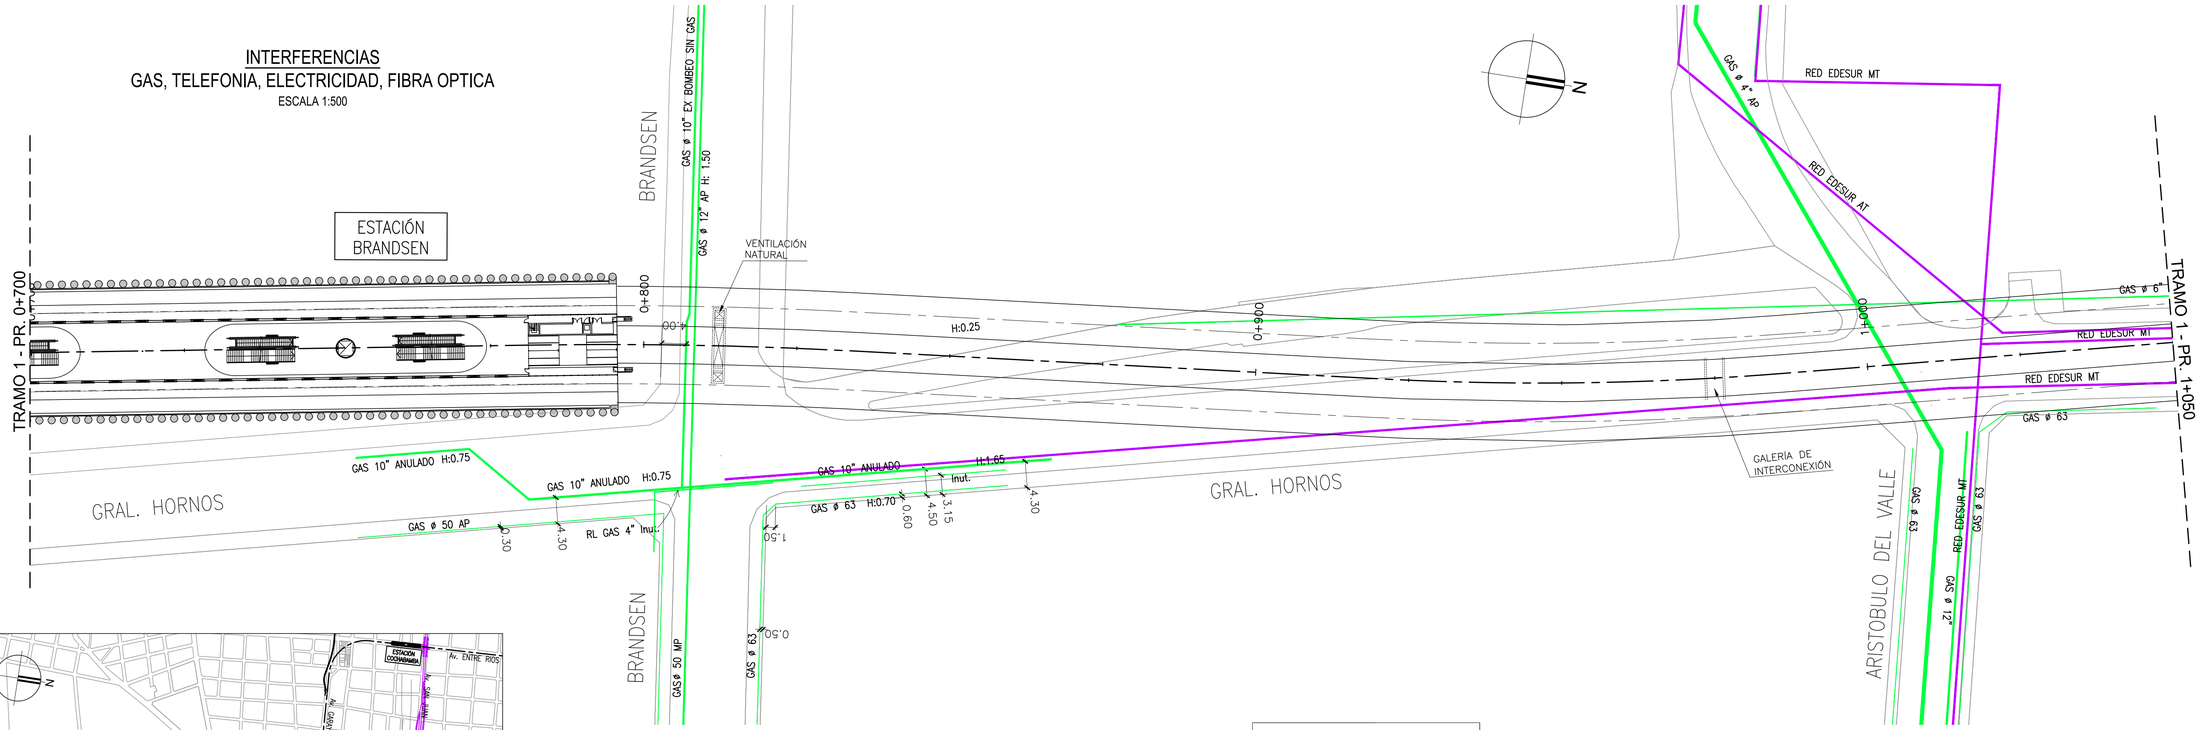

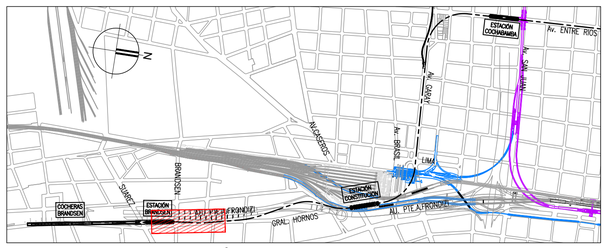

CROQUIS DE UBICACIÓN

REFERENCIAS
- RED CLOACAL
- RED PLUVIAL
- RED AGUA
- RED ELECTRICA
- RED GAS
- RED TELEFONICA
- RED FIBRA OPTICA MULTICANAL

0 10 20 30m
ESCALA 1:500

NOTAS:
EL PRESENTE PLANO ES INDICATIVO. LA CONTRATISTA CONFECCIONARA LOS PLANOS DE DETALLE DEFINITIVO, QUE DEBERAN SER APROBADOS POR LA D.G.D.INF.U Y LA INSPECCION DE OBRA. EL PLANO PRESENTADO POR LA CONTRATISTA ESTARA EN UN TODO DE ACUERDO CON LA NORMATIVA VIGENTE.
TODAS LAS MEDIDAS Y NIVELES SE VERIFICARAN EN OBRA POR EL CONTRATISTA.
TODOS LOS DETALLES CONSTRUCTIVOS SERAN COORDINADOS Y COMPATIBILIZADOS EN OBRA

PLANO NO APTO PARA CONSTRUCCION.

MODIFICACIONES:

REVISION	FECHA	DESCRIPCION
0	19/09/2025	EMISION INICIAL
1	06/05/2026	REVISION DE PROYECTO

Gobierno de la Ciudad de Buenos Aires
MINISTERIO DIE INFRAESTRUCTURA
SUBSECRETARIA DE PROYECTOS Y OBRAS
DIRECCION GENERAL DE PROYECTOS

DGPRO

Obra: LÍNEA F
IF-2026-28525919-GCABA-DGPRO
Plano: INTERFERENCIAS TRAMO 1 - PLANIMETRÍA GENERAL - PROG. 0+700 A 1+050 | LF-GL-T01-INT-PL-003
Fecha: 06/05/2026 | Eq. de Proyecto: UPU-ATEC-IATASA | Dibujó: D.B. | Revisó: P.C. | Escala: 1:500
Plano N° 003

8/5/2026 14:51 p. m.
LF-GL-T01-INT-PL-0016019_1.dwg

INTERFERENCIAS
SERVICOS CLOACALES, PLUVIALES, AGUA CORRIENTE
ESCALA 1:500

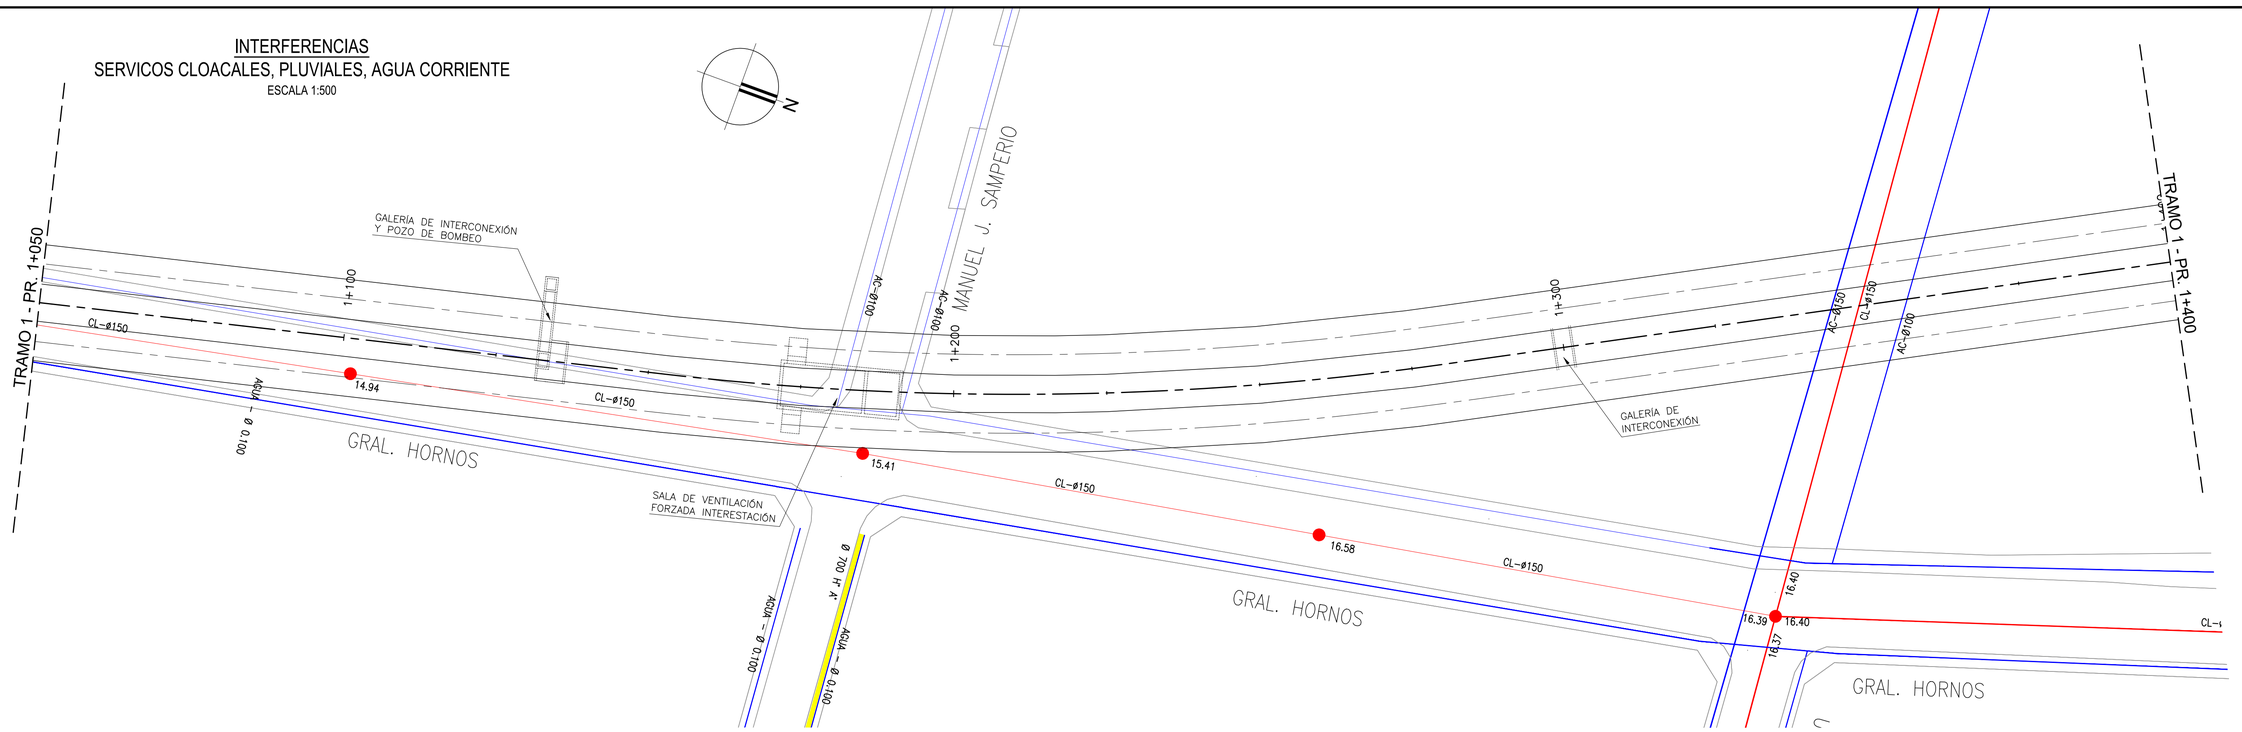

INTERFERENCIAS
GAS, TELEFONIA, ELECTRICIDAD, FIBRA OPTICA
ESCALA 1:500

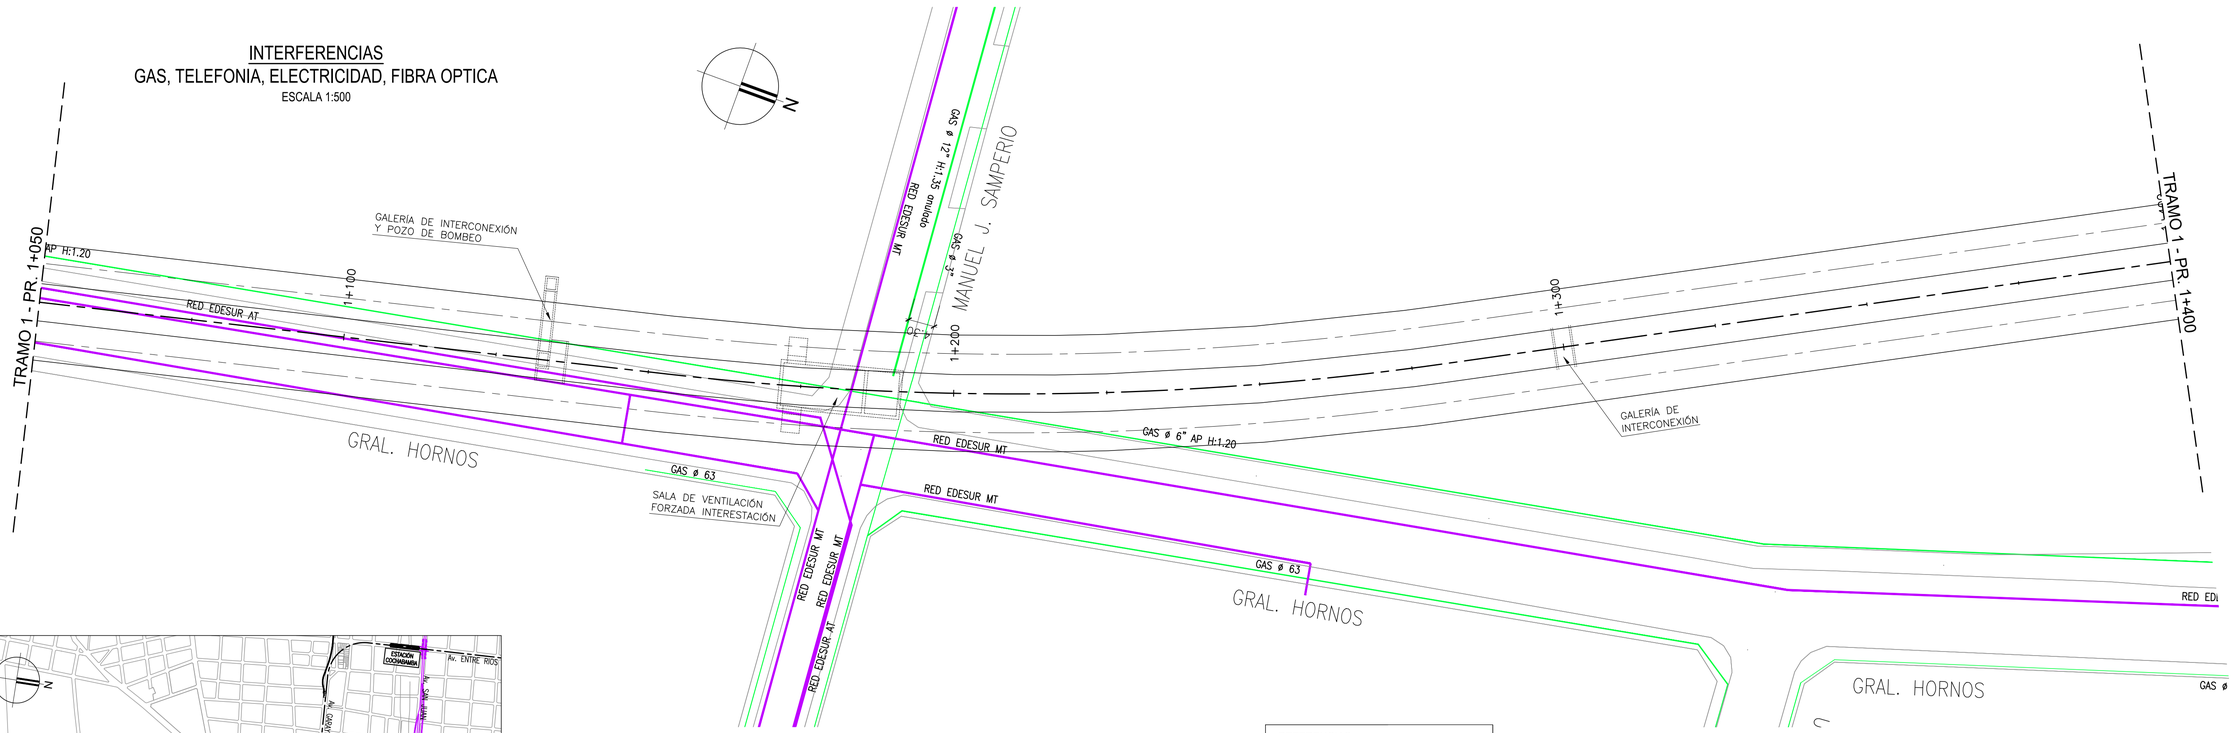
N
TRAMO 1 - PR: 1+050
TRAMO 1 - PR: 1+400
GALERÍA DE INTERCONEXIÓN Y POZO DE BOMBEO
GALERÍA DE INTERCONEXIÓN
SALA DE VENTILACIÓN FORZADA INTERESTACIÓN
MANUEL J. SAMPERIO
GRAL. HORNOS
1+100
1+200
1+300
AP H:1.20
RED EDESUR AT
RED EDESUR MT
GAS ø 6" AP H:1.20
GAS ø 63
GAS ø 12" H:1.35 ovalado
RED EDESUR MT
RED EDESUR AT
RED EDESUR MT
RED EDESUR MT
RED EDESUR AT
GAS ø 63
RED EDESUR MT
RED EDESUR MT
RED EDESUR AT
RED EDESUR AT
RED EDESUR MT
RED EDESUR MT
RED EDESUR M

INTERFERENCIAS
SERVICOS CLOACALES, PLUVIALES, AGUA CORRIENTE
ESCALA 1:500

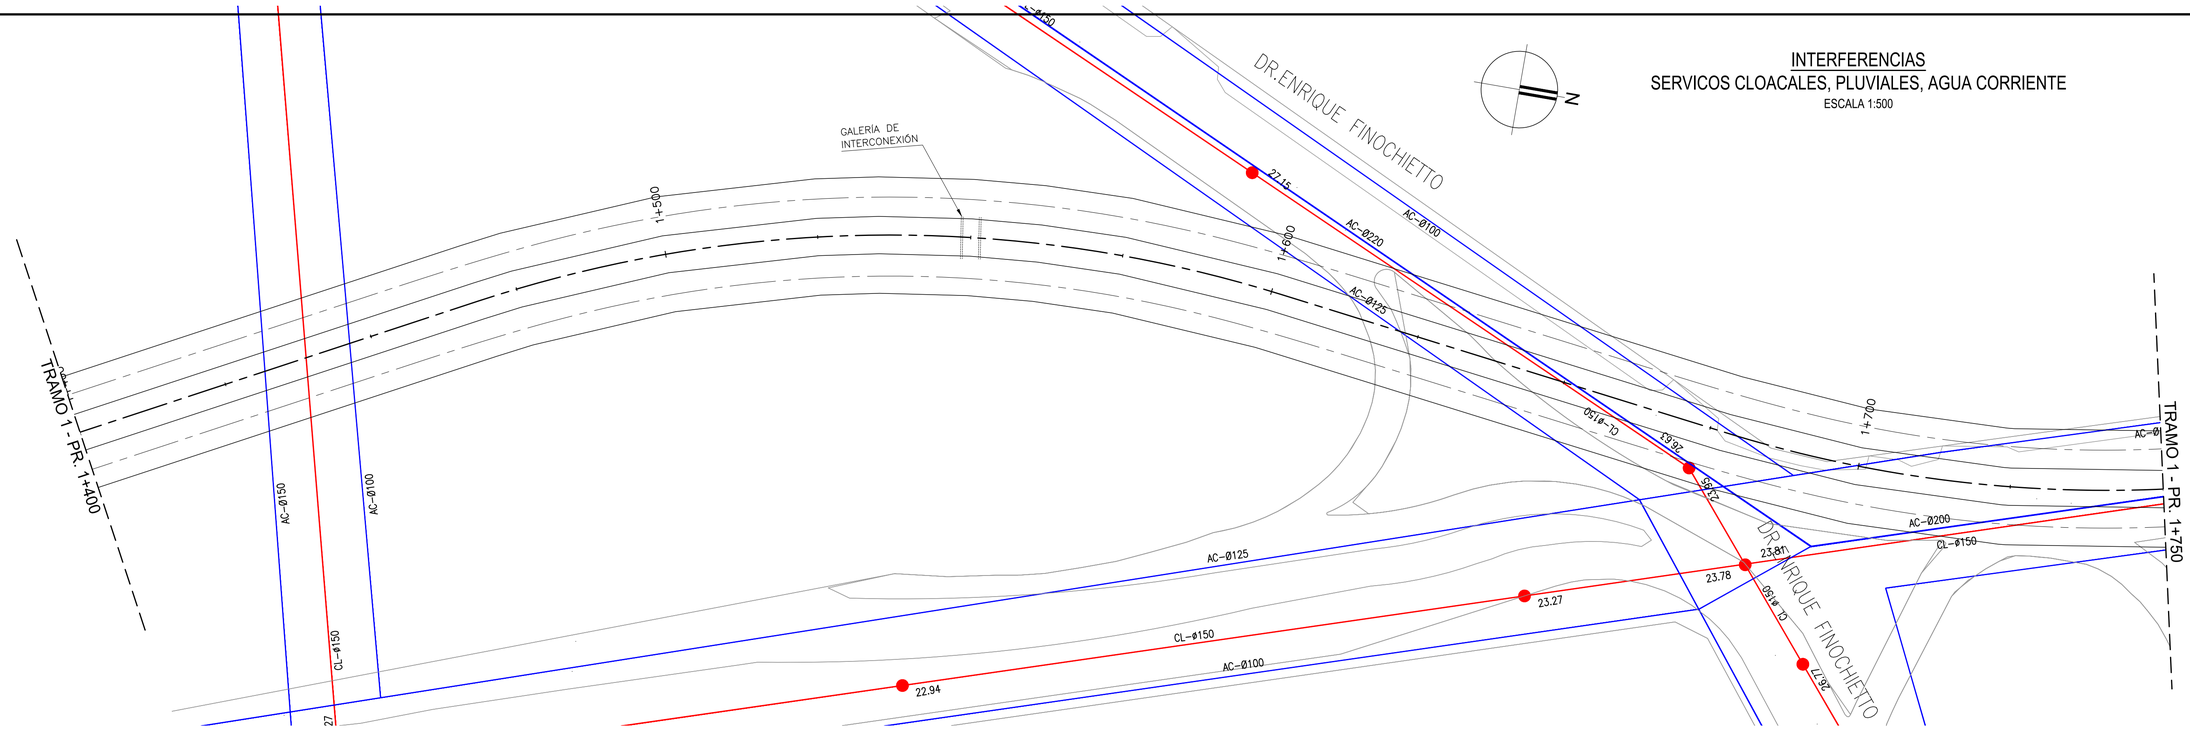

INTERFERENCIAS
GAS, TELEFONIA, ELECTRICIDAD, FIBRA OPTICA
ESCALA 1:500

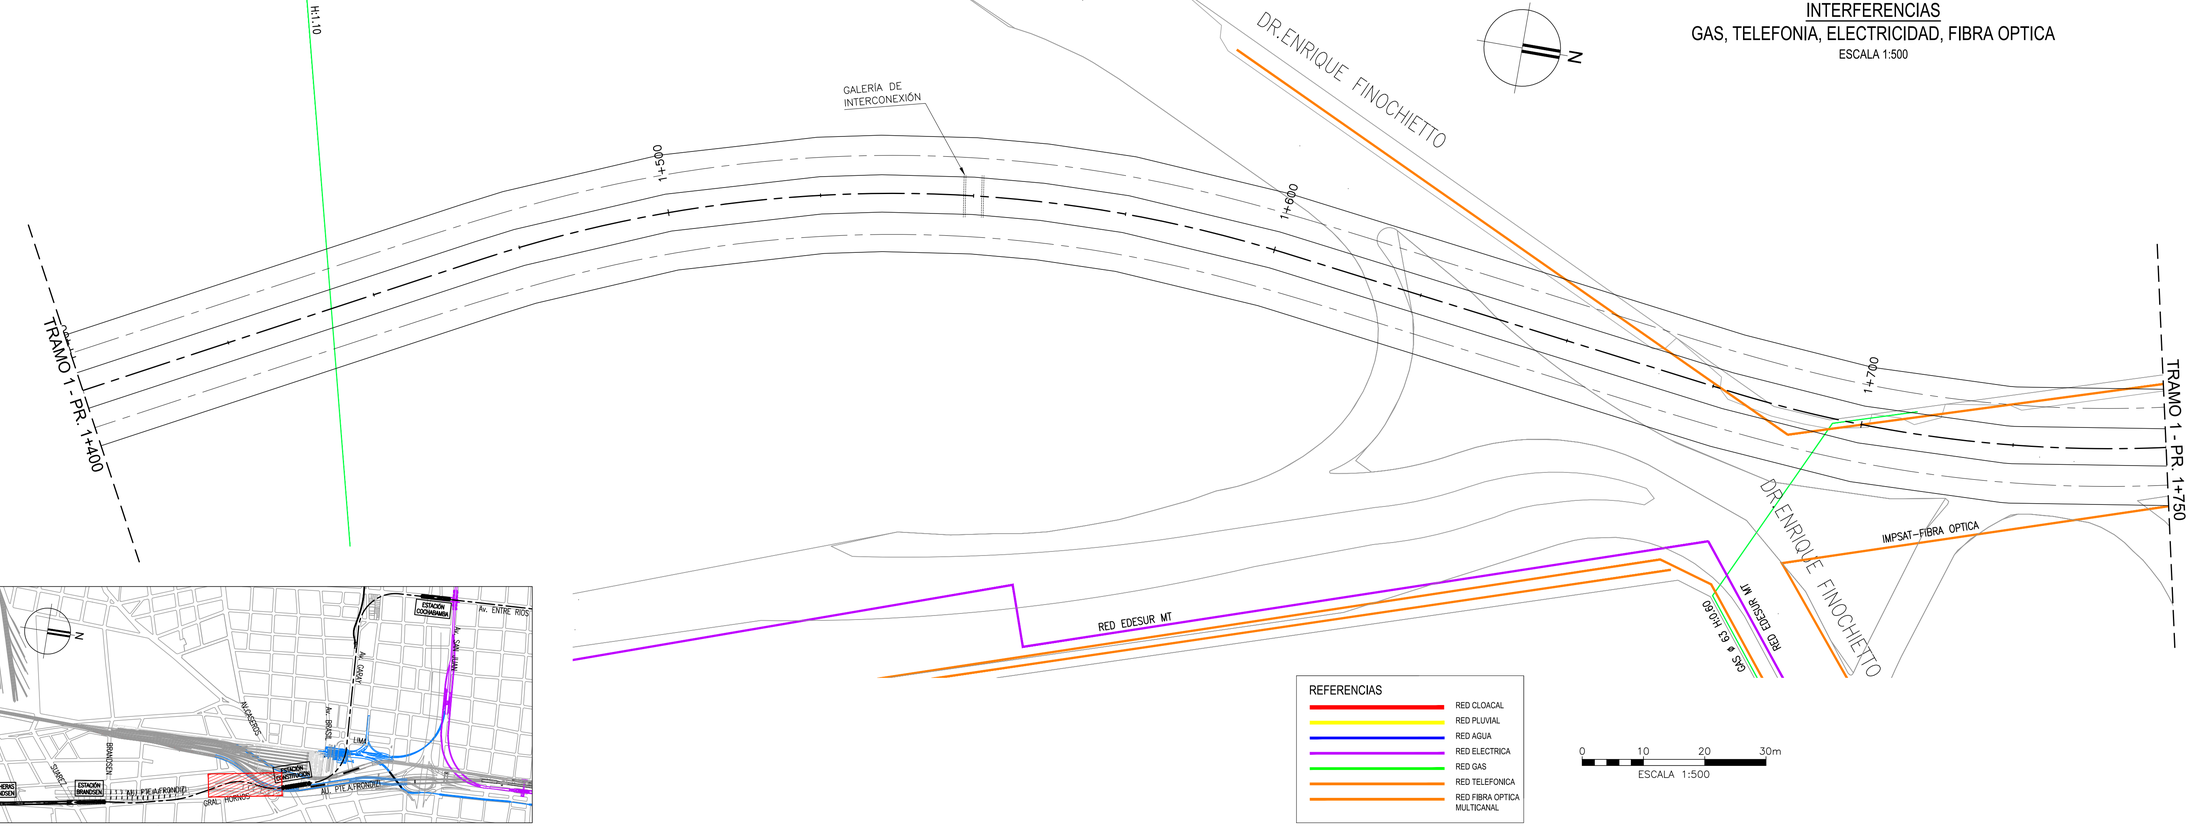

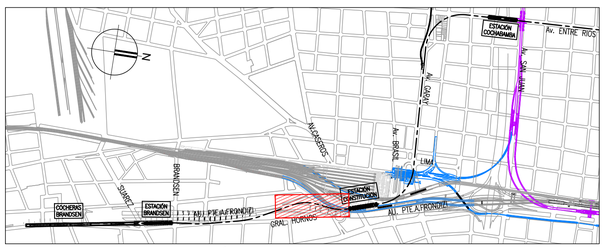

CROQUIS DE UBICACIÓN

NOTAS:
EL PRESENTE PLANO ES INDICATIVO. LA CONTRATISTA CONFECCIONARA LOS PLANOS DE DETALLE DEFINITIVO, QUE DEBERAN SER APROBADOS POR LA D.G.O.INF.U Y LA INSPECCION DE OBRA. EL PLANO PRESENTADO POR LA CONTRATISTA ESTARA EN UN TODO DE ACUERDO CON LA NORMATIVA VIGENTE.
TODAS LAS MEDIDAS Y NIVELES SE VERIFICARAN EN OBRA POR EL CONTRATISTA.
TODOS LOS DETALLES CONSTRUCTIVOS SERAN COORDINADOS Y COMPATIBILIZADOS EN OBRA

PLANO NO APTO PARA CONSTRUCCION.

MODIFICACIONES:

REVISION	FECHA	DESCRIPCION
0	19/09/2025	EMISION INICIAL
1	06/05/2026	REVISION DE PROYECTO

Gobierno de la Ciudad de Buenos Aires
MINISTERIO DIE INFRAESTRUCTURA
SUBSECRETARIA DE PROYECTOS Y OBRAS
DIRECCION GENERAL DE PROYECTOS

DGPRO

Obra: LÍNEA F
IF-2026-28525919-GCABA-DGPRO
Plano: INTERFERENCIAS TRAMO 1 - PLANIMETRÍA GENERAL - PROG. 1+400 A 1+750 | LF-GL-T01-INT-PL-005
Fecha: 06/05/2026 | Eq. de Proyecto: UPU-ATEC-IATASA | Dibujó: D.B. | Revisó: P.C. | Escala: 1:500
Plano N° 005

8/5/2026 14:51 p. m.
LF-GL-T01-INT-PL_0016019_1.dwg

INTERFERENCIAS
SERVICOS CLOACALES, PLUVIALES, AGUA CORRIENTE
ESCALA 1:500

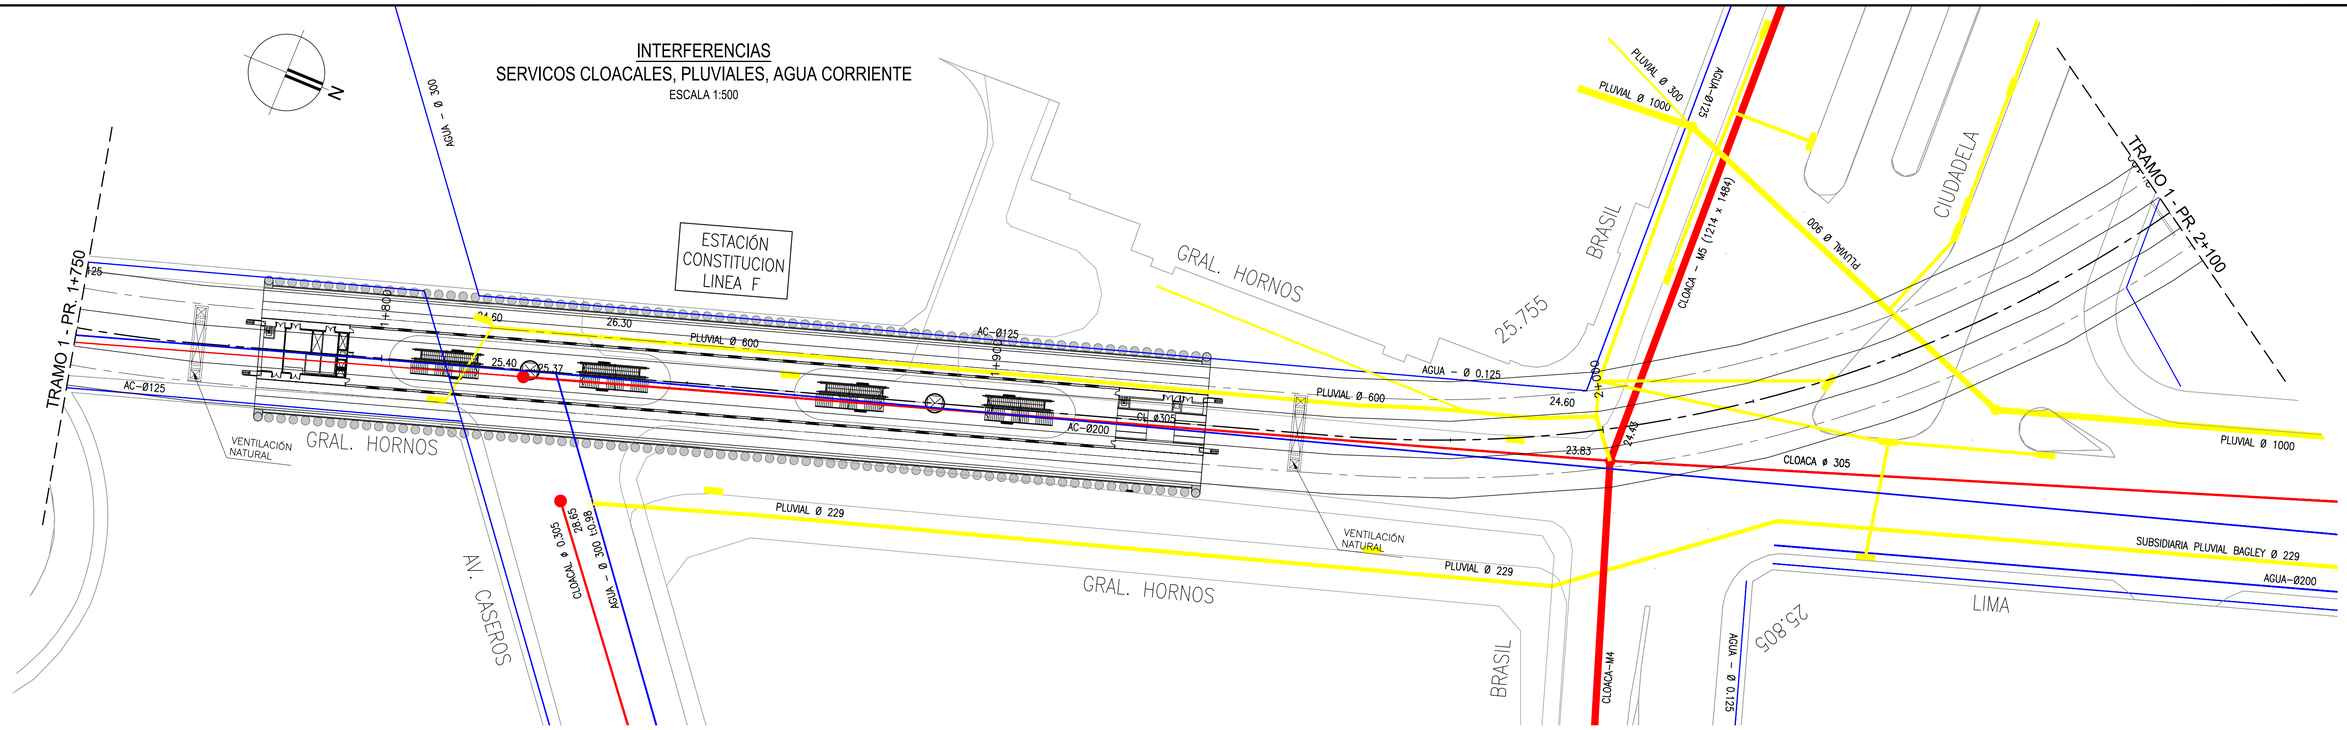

INTERFERENCIAS
GAS, TELEFONIA, ELECTRICIDAD, FIBRA OPTICA
ESCALA 1:500

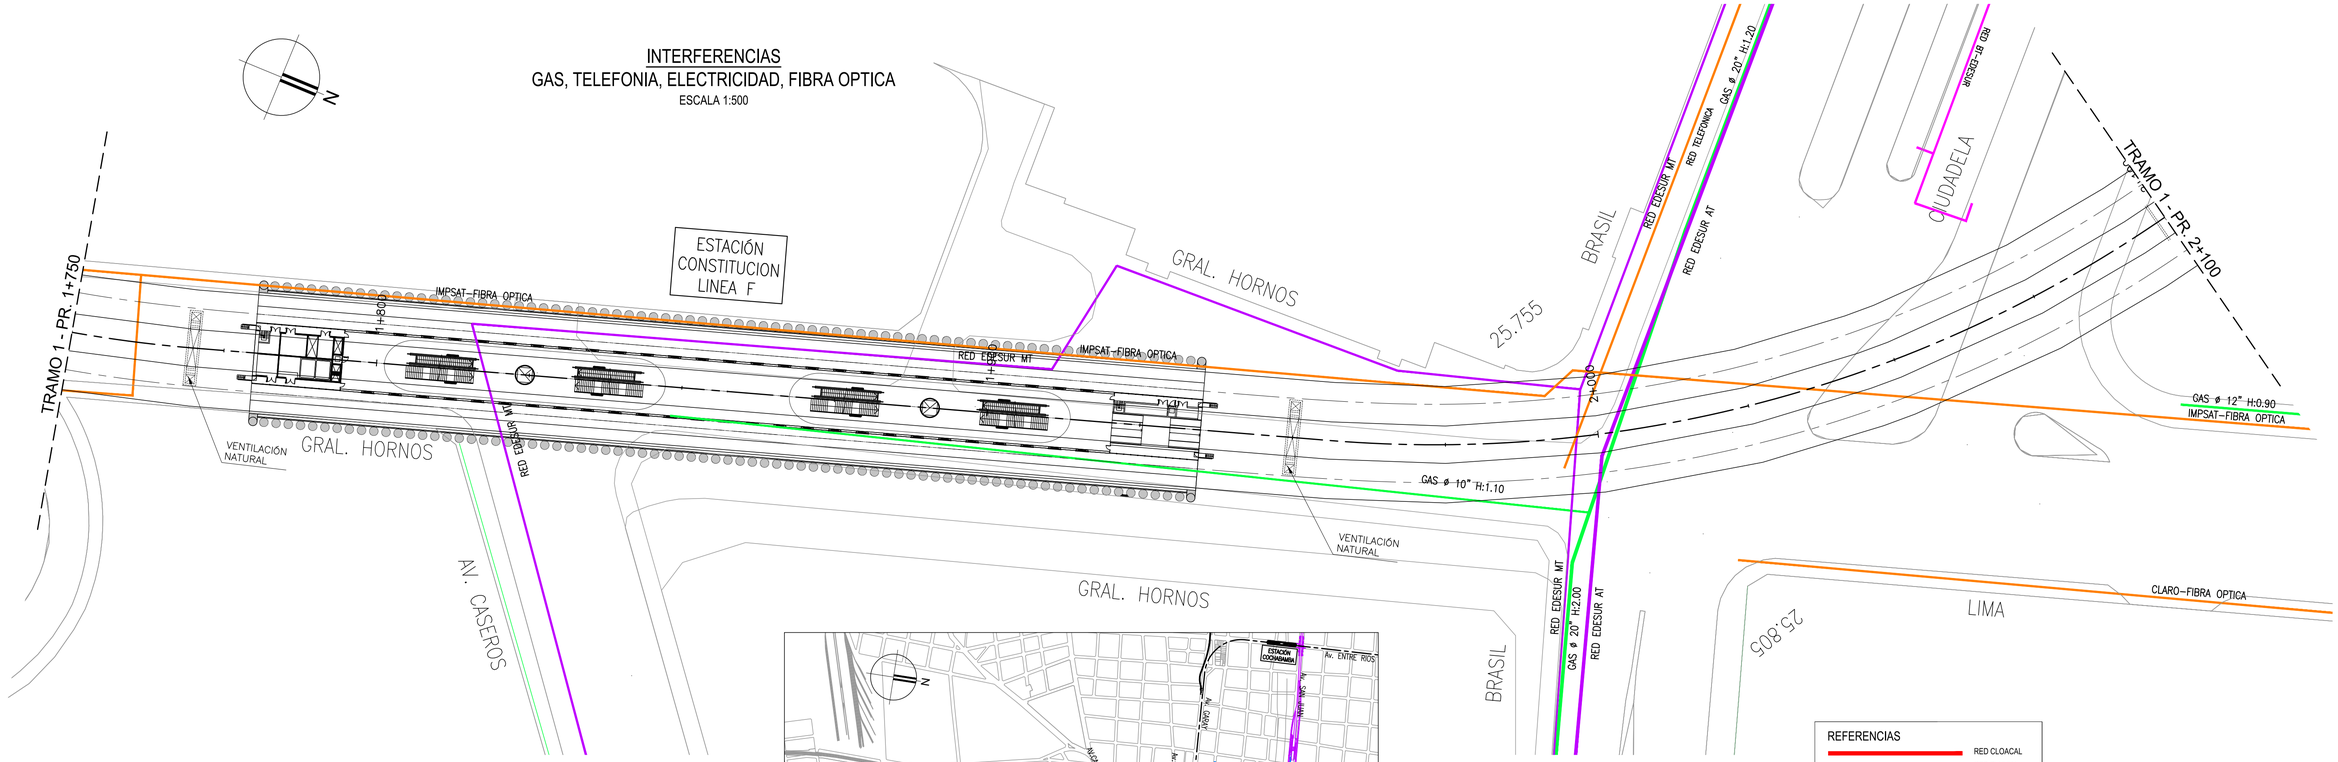

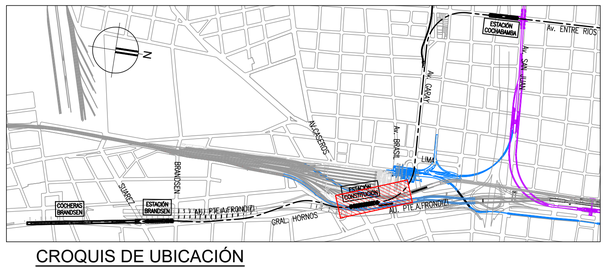

CROQUIS DE UBICACIÓN

REFERENCIAS
- RED CLOACAL
- RED PLUVIAL
- RED AGUA
- RED ELECTRICA
- RED GAS
- RED TELEFONICA
- RED FIBRA OPTICA MULTICANAL

0 10 20 30m
ESCALA 1:500

NOTAS:
EL PRESENTE PLANO ES INDICATIVO LA CONTRATISTA CONFECCIONARA LOS PLANOS DE DETALLE DEFINITIVO, QUE DEBERAN SER APROBADOS POR LA D.G.D.IMF.U Y LA INSPECCION DE OBRA. EL PLANO PRESENTADO POR LA CONTRATISTA ESTARA EN LA TODO DE ACUERDO CON LA NORMATIVA VIGENTE.
TODAS LAS MEDIDAS Y NIVELES SE VERIFICARAN EN OBRA POR EL CONTRATISTA.
TODOS LOS DETALLES CONSTRUCTIVOS SERAN COORDINADOS Y COMPATIBILIZADOS EN OBRA

PLANO NO APTO PARA CONSTRUCCION.

MODIFICACIONES:

REVISION	FECHA	DESCRIPCION
0	19/05/2025	EMISION INICIAL
1	06/05/2026	REVISION DE PROYECTO

Gobierno de la Ciudad de Buenos Aires

MINISTERIO DE INFRAESTRUCTURA
SUBSECRETARIA DE PROYECTOS Y OBRAS
DIRECCION GENERAL DE PROYECTOS

DGPRO

Obra: LÍNEA F
Plano: INTERFERENCIAS TRAMO 1 - PLANIMETRÍA GENERAL - PROG. 1+750 A 2+100
Fecha: 06/05/2026 | Eq. de Proyecto: UPU-ATEC-IATASA | Dibujó: D.B. | Revisó: P.C. | Escala: 1:500

IF-2026-28525919-GCABA-DGPRO
LF-GL-T01-INT-PL-006
Plano N°: 006

8/5/2026 14:51 p. m.
LF-GL-T01-INT-PL-001a019_1.dwg

INTERFERENCIAS
SERVICOS CLOACALES, PLUVIALES, AGUA CORRIENTE
ESCALA 1:500

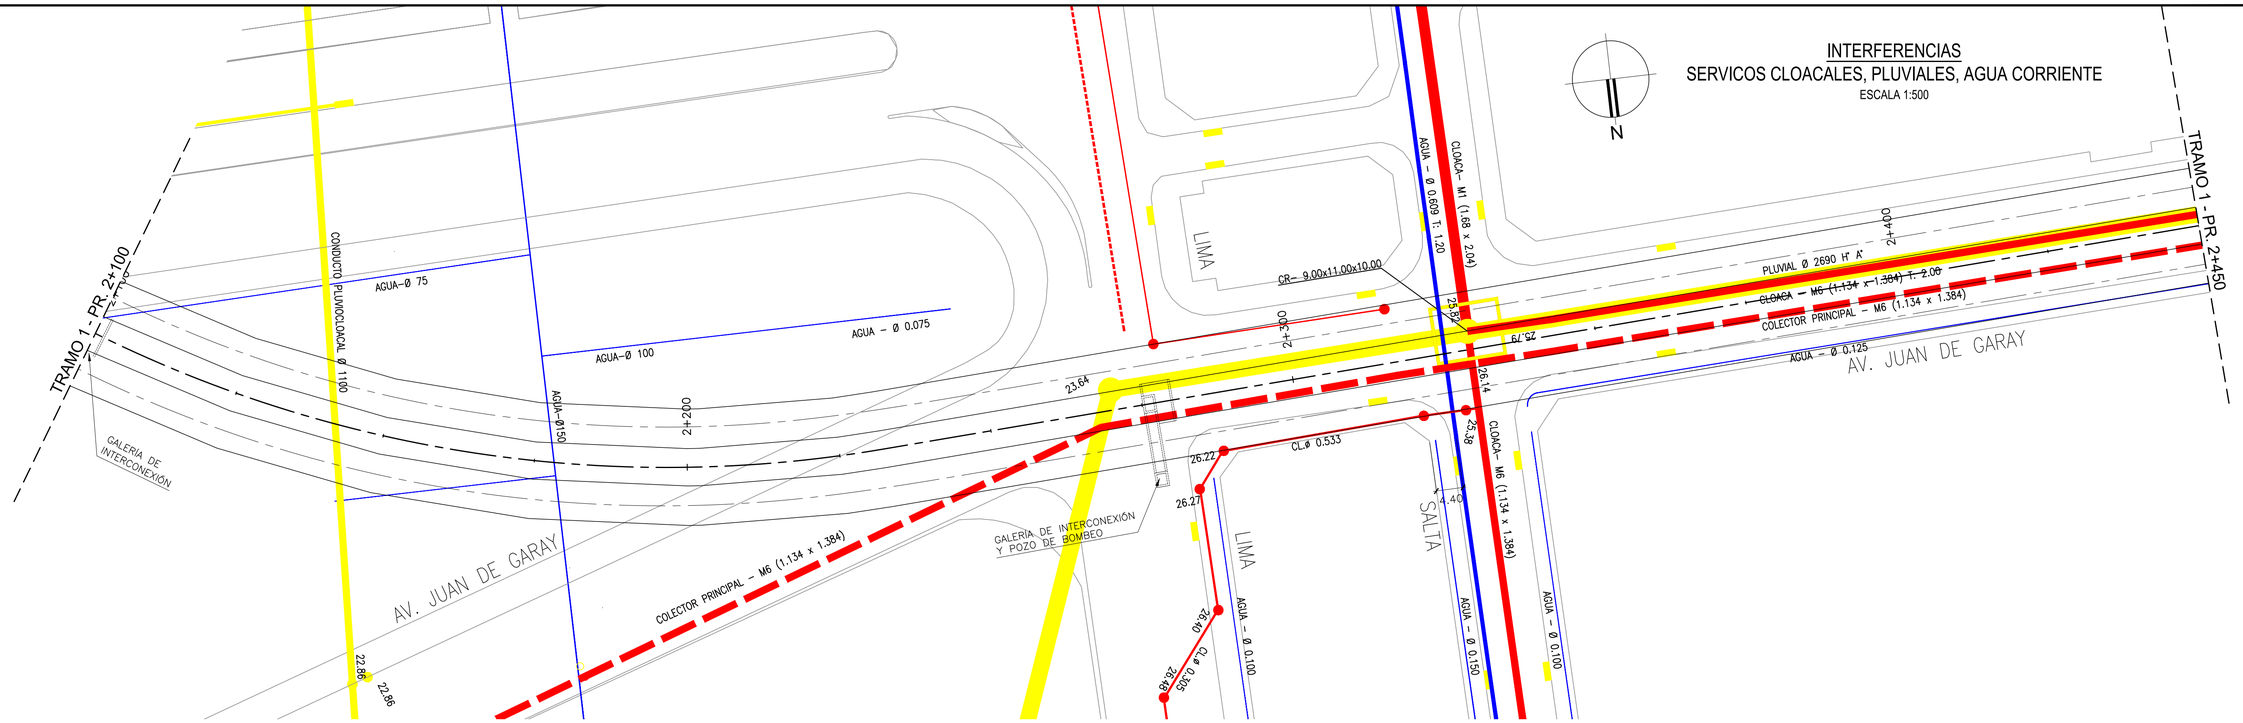

INTERFERENCIAS
GAS, TELEFONIA, ELECTRICIDAD, FIBRA OPTICA
ESCALA 1:500

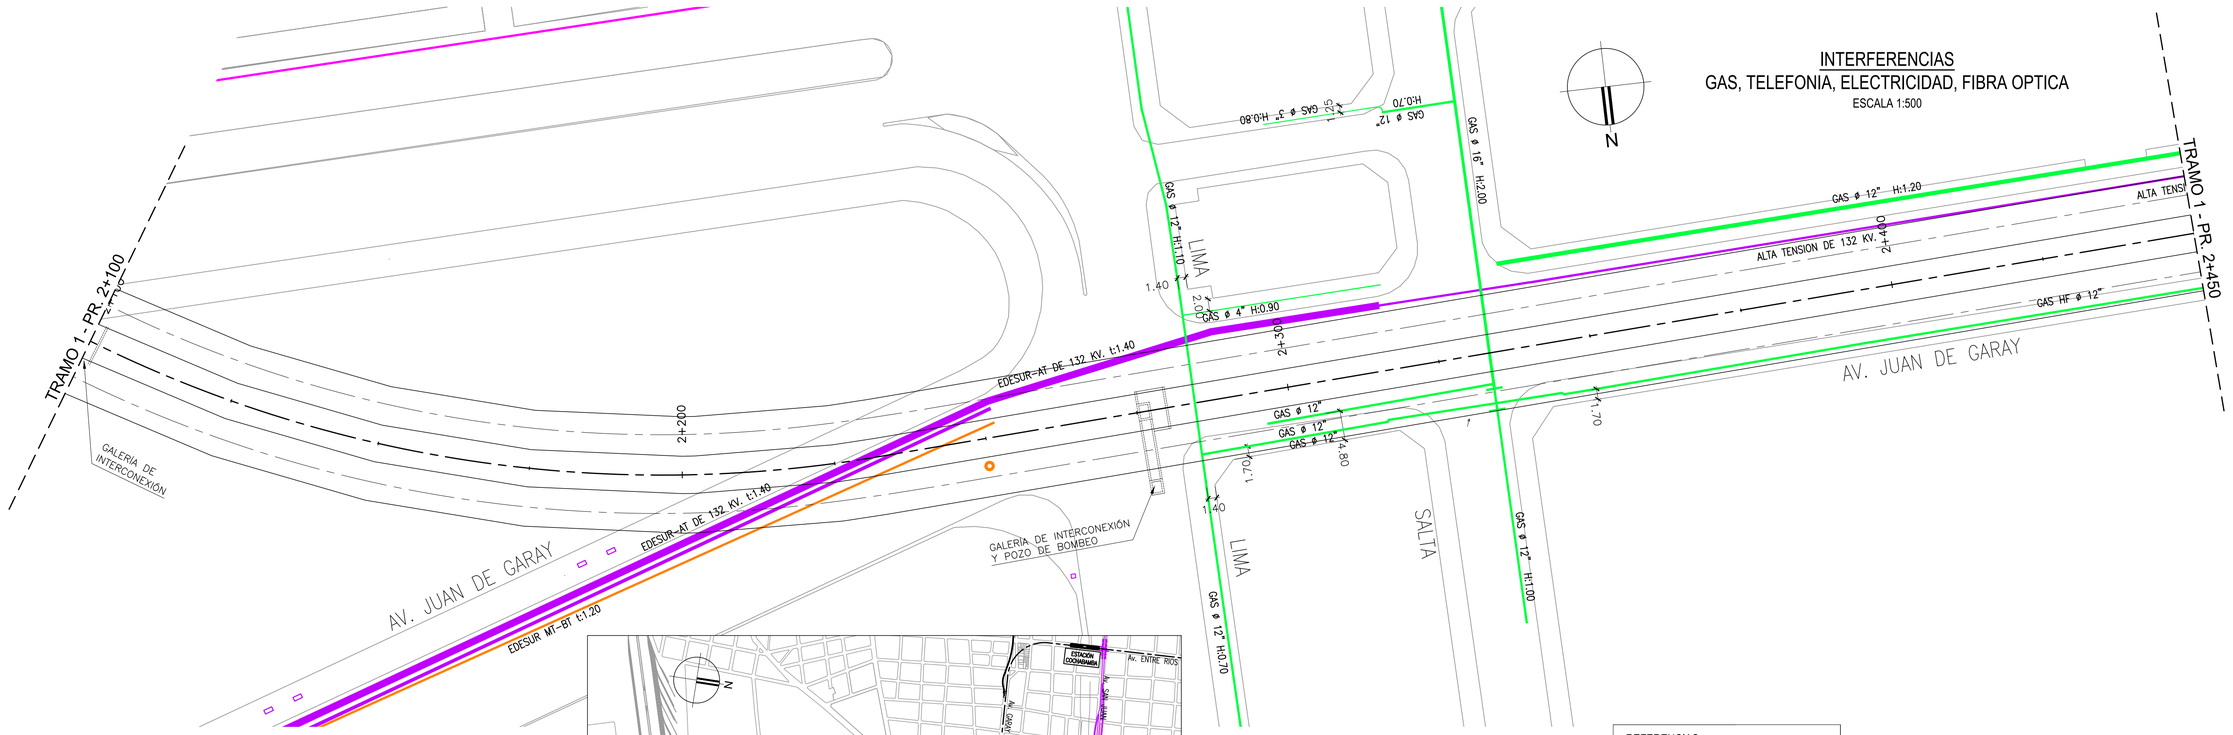

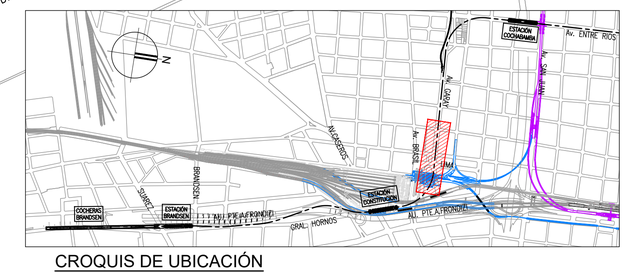

CROQUIS DE UBICACIÓN

REFERENCIAS
- RED CLOACAL
- RED PLUVIAL
- RED AGUA
- RED ELECTRICA
- RED GAS
- RED TELEFONICA
- RED FIBRA OPTICA MULTICANAL

0 10 20 30m
ESCALA 1:500

NOTAS:
EL PRESENTE PLANO ES INDICATIVO. LA CONTRATISTA CONFECCIONARA LOS PLANOS DE DETALLE DEFINITIVO, QUE DEBERÁN SER APROBADOS POR LA D.G.O.INF.U Y LA INSPECCION DE OBRA. EL PLANO PRESENTADO POR LA CONTRATISTA ESTARA EN UN TODO DE ACUERDO CON LA NORMATIVA VIGENTE.
TODAS LAS MEDIDAS Y NIVELES SE VERIFICARAN EN OBRA POR EL CONTRATISTA.
TODOS LOS DETALLES CONSTRUCTIVOS SERAN COORDINADOS Y COMPATIBILIZADOS EN OBRA

PLANO NO APTO PARA CONSTRUCCION.

MODIFICACIONES:

REVISION	FECHA	DESCRIPCION
0	19/05/2025	EMISION INICIAL
1	06/05/2026	REVISION DE PROYECTO

MINISTERIO DE INFRAESTRUCTURA
SUBSECRETARIA DE PROYECTOS Y OBRAS
DIRECCION GENERAL DE PROYECTOS

DGPRO

Obra: LÍNEA F					IF-2026-28525919-GCABA-DGPRO
Plano: INTERFERENCIAS TRAMO 1 - PLANIMETRÍA GENERAL - PROG. 2+100 A 2+450					LF-GL-T01-INT-PL-007
Fecha: 06/05/2026	Eq. de Proyecto: UPU-ATEC-IATASA	Dibujó: D.B.	Revisó: P.C.	Escala: 1:500	Plano N° 007

8/5/2026 14:51 p. m.
LF-GL-T01-INT-PL-001d19_1.dwg

INTERFERENCIAS
SERVICOS CLOACALES, PLUVIALES, AGUA CORRIENTE
ESCALA 1:500

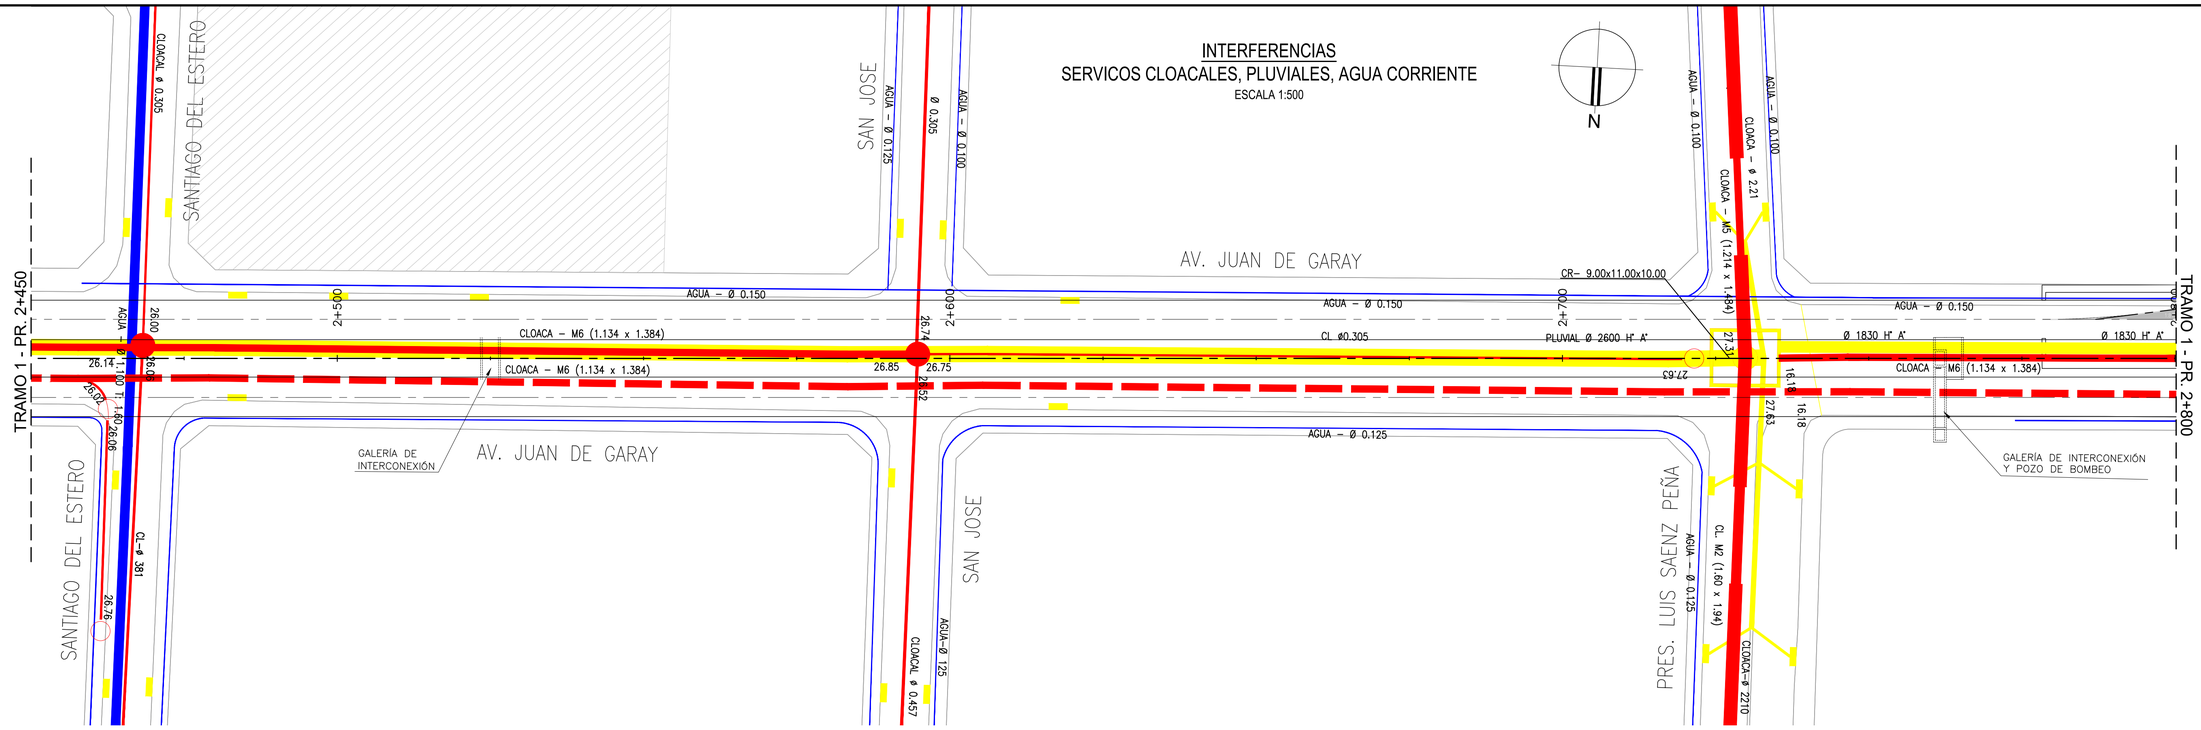

INTERFERENCIAS
GAS, TELEFONIA, ELECTRICIDAD, FIBRA OPTICA
ESCALA 1:500

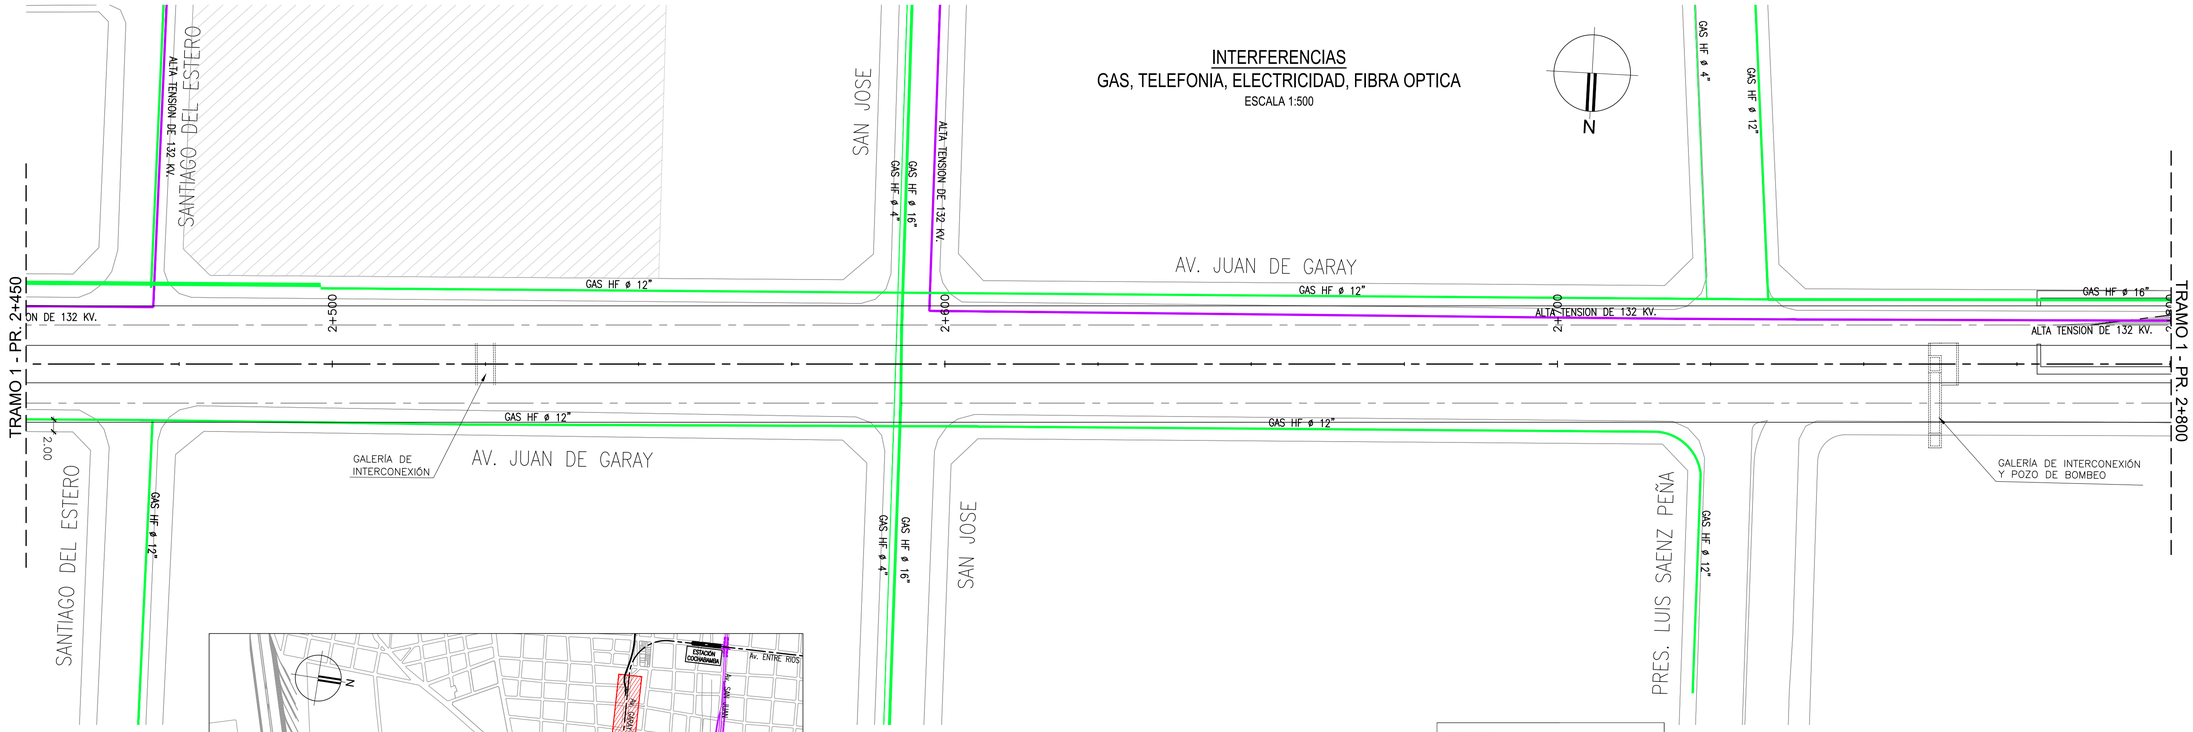

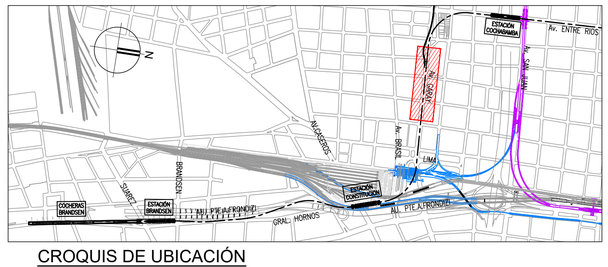

CROQUIS DE UBICACIÓN

REFERENCIAS
- RED CLOACAL
- RED PLUVIAL
- RED AGUA
- RED ELECTRICA
- RED GAS
- RED TELEFONICA
- RED FIBRA OPTICA MULTICANAL

0 10 20 30m
ESCALA 1:500

NOTAS: EL PRESENTE PLANO ES INDICATIVO. LA CONTRATISTA CONFECCIONARA LOS PLANOS DE DETALLE DEFINITIVO, QUE DEBERAN SER APROBADOS POR LA D.G.O.INF.U Y LA INSPECCION DE OBRA. EL PLANO PRESENTADO POR LA CONTRATISTA ESTARA EN UN TODO DE ACUERDO CON LA NORMATIVA VIGENTE.
TODAS LAS MEDIDAS Y NIVELES SE VERIFICARAN EN OBRA POR EL CONTRATISTA.
TODOS LOS DETALLES CONSTRUCTIVOS SERAN COORDINADOS Y COMPATIBILIZADOS EN OBRA

PLANO NO APTO PARA CONSTRUCCION.

MODIFICACIONES:

REVISION	FECHA	DESCRIPCION
0	19/09/2025	EMISION INICIAL
1	06/05/2026	REVISION DE PROYECTO

MINISTERIO DE INFRAESTRUCTURA
SUBSECRETARIA DE PROYECTOS Y OBRAS
DIRECCION GENERAL DE PROYECTOS

DGPRO

Obra: LÍNEA F				IF-2026-28525919-GCABA-DGPRO
Plano: INTERFERENCIAS TRAMO 1 - PLANIMETRÍA GENERAL - PROG. 2+450 A 2+800				LF-GL-T01-INT-PL-008
Fecha: 06/05/2026	Eq. de Proyecto: UPU-ATEC-IATASA	Dibujó: D.B.	Revisó: P.C.	Escala: 1:500

Plano N° 008

11/5/2026 14:57 p. m.
LF-GL-T01-INT-PL-001a019_1.dwg

INTERFERENCIAS
SERVICIOS CLOACALES, PLUVIALES, AGUA CORRIENTE
ESCALA 1:500

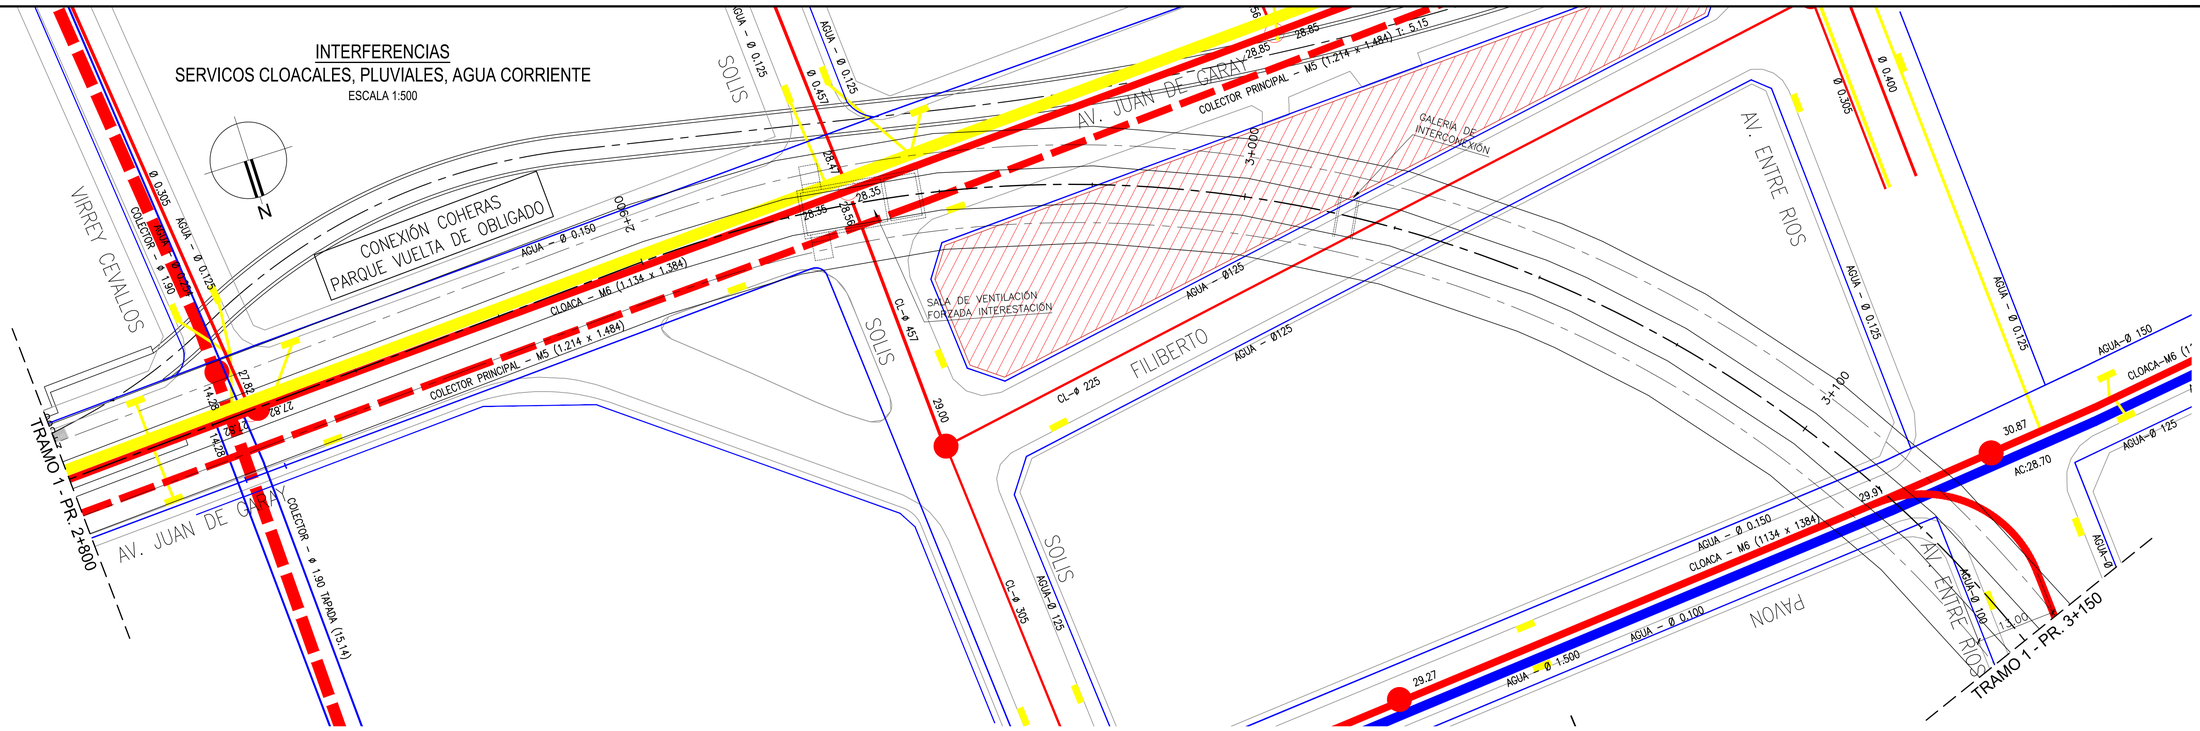

INTERFERENCIAS
GAS, TELEFONIA, ELECTRICIDAD, FIBRA OPTICA
ESCALA 1:500

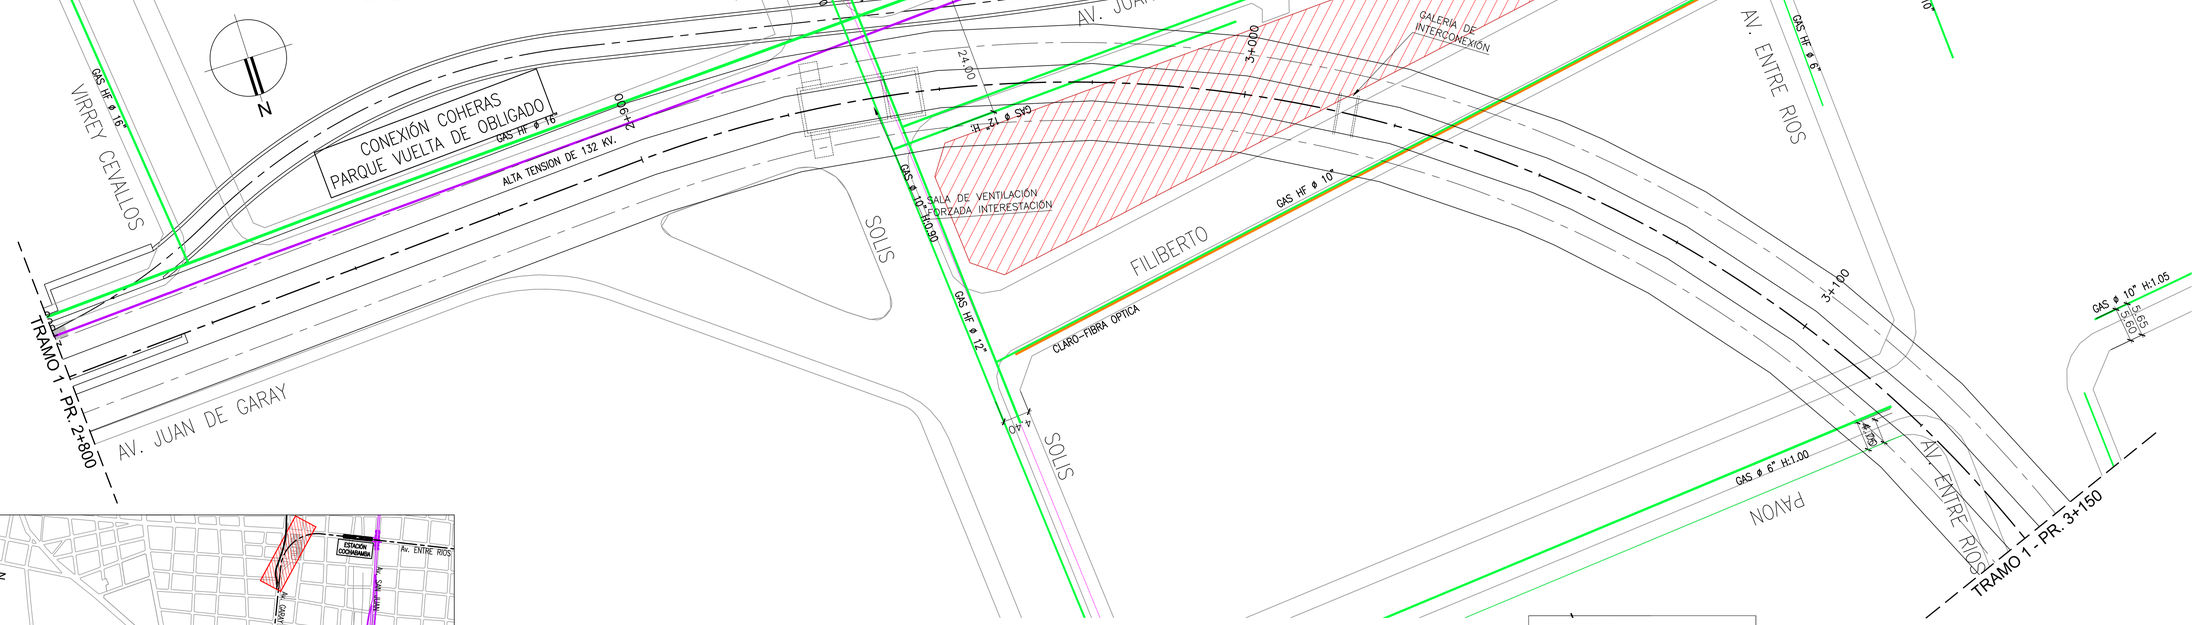

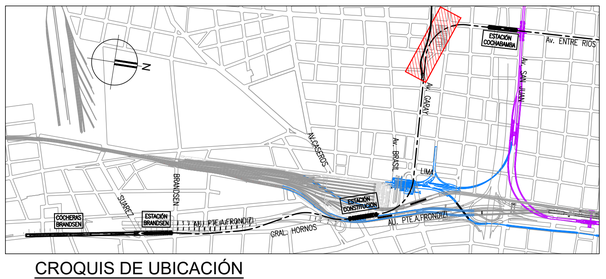

CROQUIS DE UBICACIÓN

REFERENCIAS
- RED CLOACAL
- RED PLUVIAL
- RED AGUA
- RED ELECTRICA
- RED GAS
- RED TELEFONICA
- RED FIBRA OPTICA MULTICANAL

0 10 20 30m
ESCALA 1:500

NOTAS:
EL PRESENTE PLANO ES INDICATIVO. LA CONTRATISTA CONFECCIONARA LOS PLANOS DE DETALLE DEFINITIVO, QUE DEBERAN SER APROBADOS POR LA D.G.O.IMF.U Y LA INSPECCION DE OBRA. EL PLANO PRESENTADO POR LA CONTRATISTA ESTARA EN UN TODO DE ACUERDO CON LA NORMATIVA VIGENTE.
TODAS LAS MEDIDAS Y NIVELES SE VERIFICARAN EN OBRA POR EL CONTRATISTA.
TODOS LOS DETALLES CONSTRUCTIVOS SERAN COORDINADOS Y COMPATIBILIZADOS EN OBRA

PLANO NO APTO PARA CONSTRUCCION.

MODIFICACIONES:

REVISION	FECHA	DESCRIPCION
0	19/05/2025	EMISION INICIAL
1	06/05/2026	REVISION DE PROYECTO

MINISTERIO DE INFRAESTRUCTURA
SUBSECRETARIA DE PROYECTOS Y OBRAS
DIRECCION GENERAL DE PROYECTOS

DGPRO

Obra: LÍNEA F						IF-2026-28525919-GCABA-DGPRO Plano N°
Plano: INTERFERENCIAS TRAMO 1 - PLANIMETRÍA GENERAL - PROG. 2+800 A 3+150					LF-GL-T01-INT-PL-009	009
Fecha: 06/05/2026	Eq. de Proyecto: UPU-ATEC-IATASA		Dibujó: D.B.	Revisó: P.C.	Escala: 1:500	

8/5/2026 14:51 p. m.
LF-GL-T01-INT-PL-001ed19_1.dwg

INTERFERENCIAS
SERVICOS CLOACALES, PLUVIALES, AGUA CORRIENTE
ESCALA 1:500

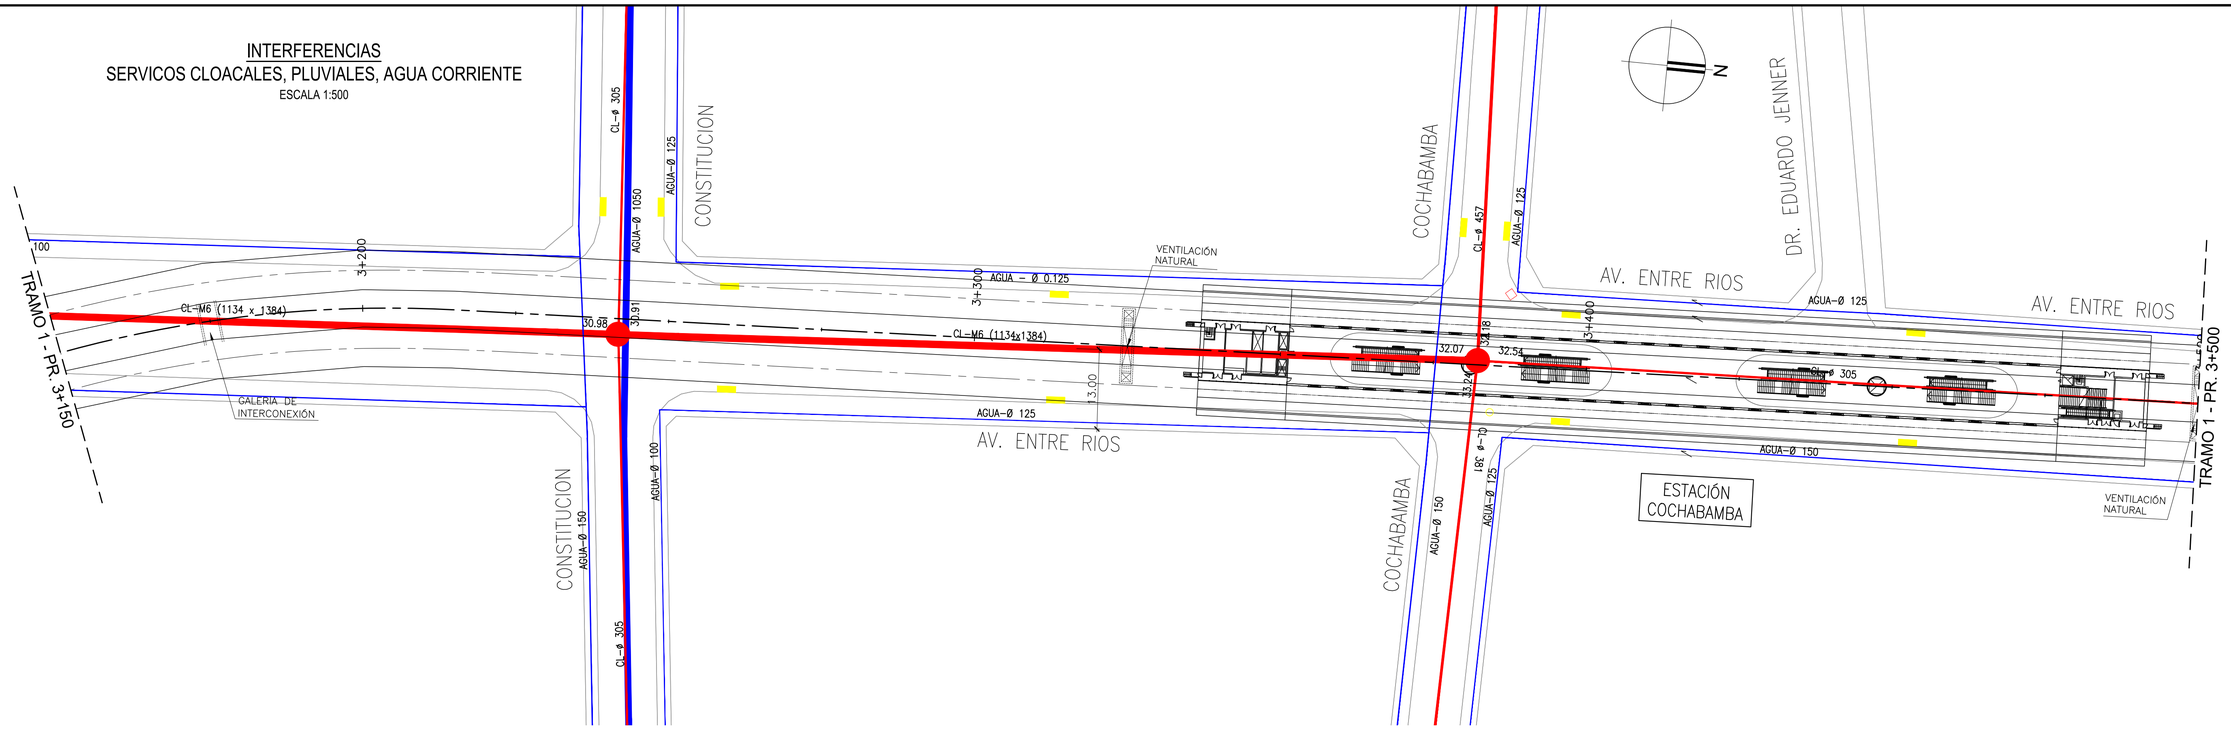

INTERFERENCIAS
GAS, TELEFONIA, ELECTRICIDAD, FIBRA OPTICA
ESCALA 1:500

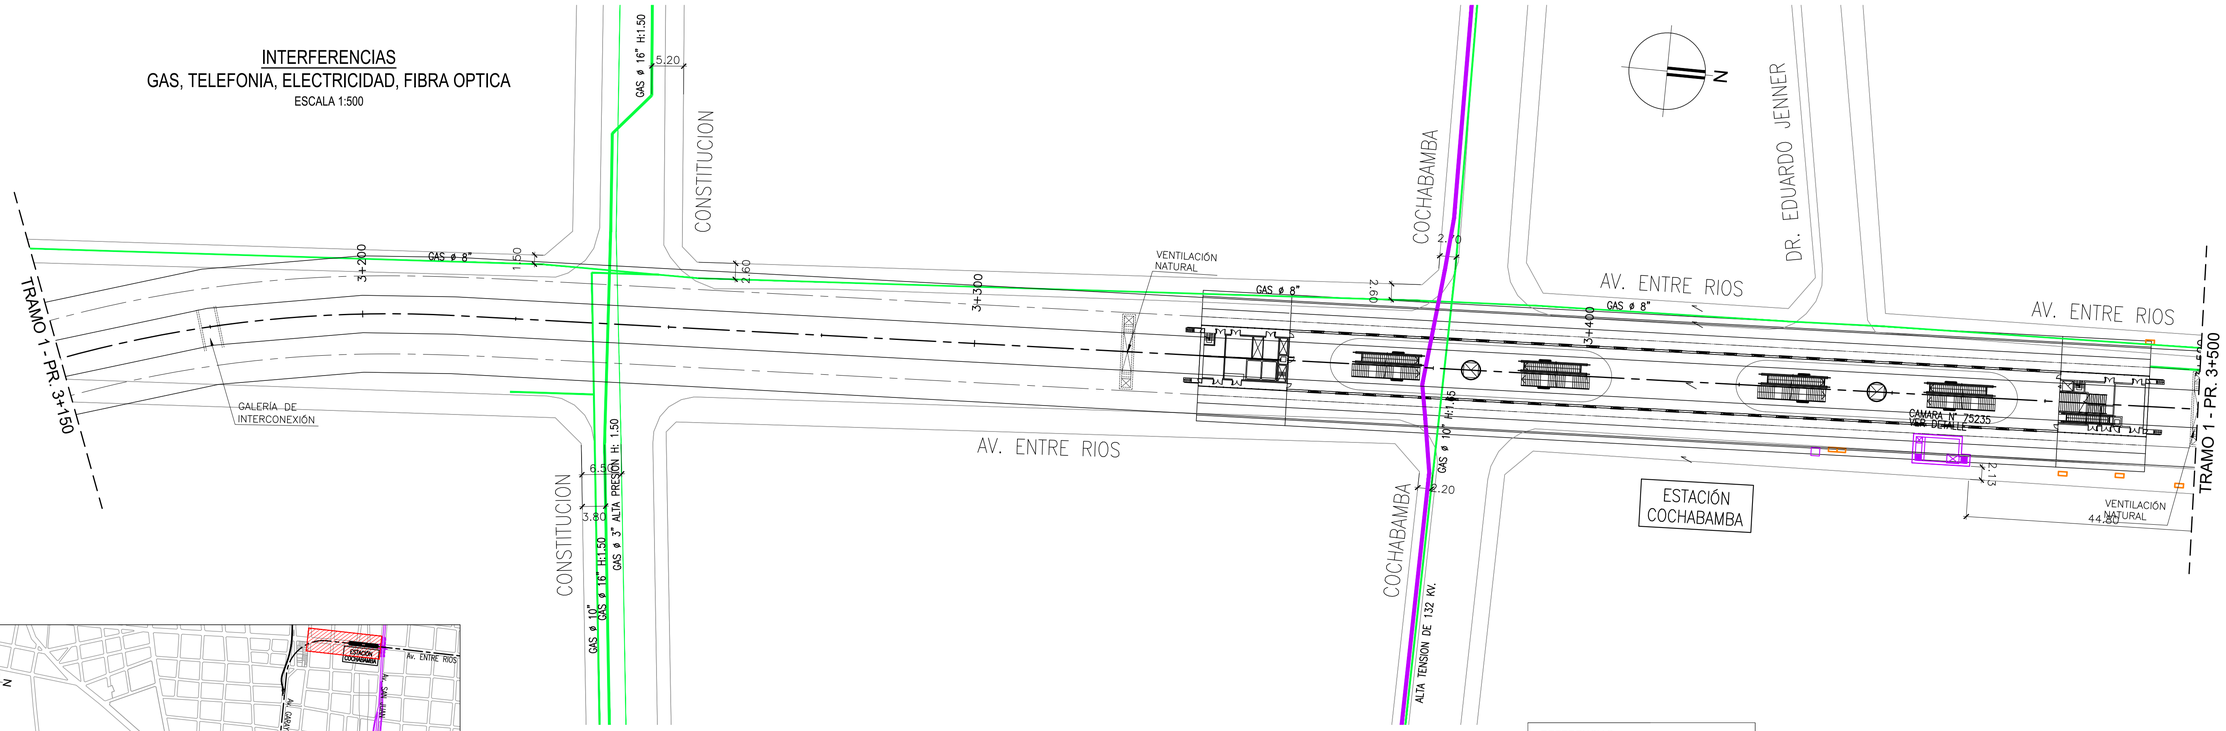

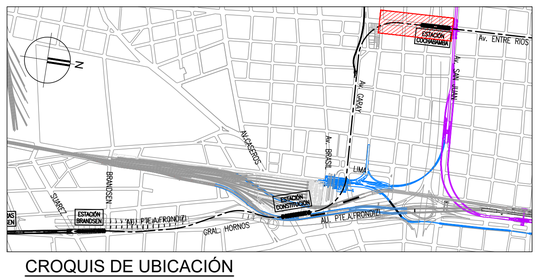

CROQUIS DE UBICACIÓN

REFERENCIAS
- RED CLOACAL
- RED PLUVIAL
- RED AGUA
- RED ELECTRICA
- RED GAS
- RED TELEFONICA
- RED FIBRA OPTICA MULTICANAL

0 10 20 30m
ESCALA 1:500

NOTAS:
EL PRESENTE PLANO ES INDICATIVO. LA CONTRATISTA CONFECCIONARA LOS PLANOS DE DETALLE DEFINITIVO, QUE DEBERAN SER APROBADOS POR LA D.G.O.S.INF.U Y LA INSPECCION DE OBRA. EL PLANO PRESENTADO POR LA CONTRATISTA ESTARA EN UN TODO DE ACUERDO CON LA NORMATIVA VIGENTE.
TODAS LAS MEDIDAS Y NIVELES SE VERIFICARAN EN OBRA POR EL CONTRATISTA.
TODOS LOS DETALLES CONSTRUCTIVOS SERAN COORDINADOS Y COMPATIBILIZADOS EN OBRA

PLANO NO APTO PARA CONSTRUCCION.

MODIFICACIONES:

REVISION	FECHA	DESCRIPCION
0	19/05/225	EMISION INICIAL
1	06/05/226	REVISION DE PROYECTO

Gobierno de la Ciudad de Buenos Aires

MINISTERIO DE INFRAESTRUCTURA
SUBSECRETARIA DE PROYECTOS Y OBRAS
DIRECCION GENERAL DE PROYECTOS

DGPRO

Obra: LÍNEA F
IF-2026-28525919-GCABA-DGPRO
Plano N° 010
Plano: INTERFERENCIAS TRAMO 1 - PLANIMETRÍA GENERAL - PROG. 3+150 A 3+500 | LF-GL-T01-INT-PL-010
Fecha: 06/05/2026 | Eq. de Proyecto: UPU-ATEC-IATASA | Dibujó: D.B. | Revisó: P.C. | Escala: 1:500

8/5/2026 14:51 p. m.
LF-GL-T01-INT-PL-001a019_1.dwg

INTERFERENCIAS
SERVICOS CLOACALES, PLUVIALES, AGUA CORRIENTE
ESCALA 1:500

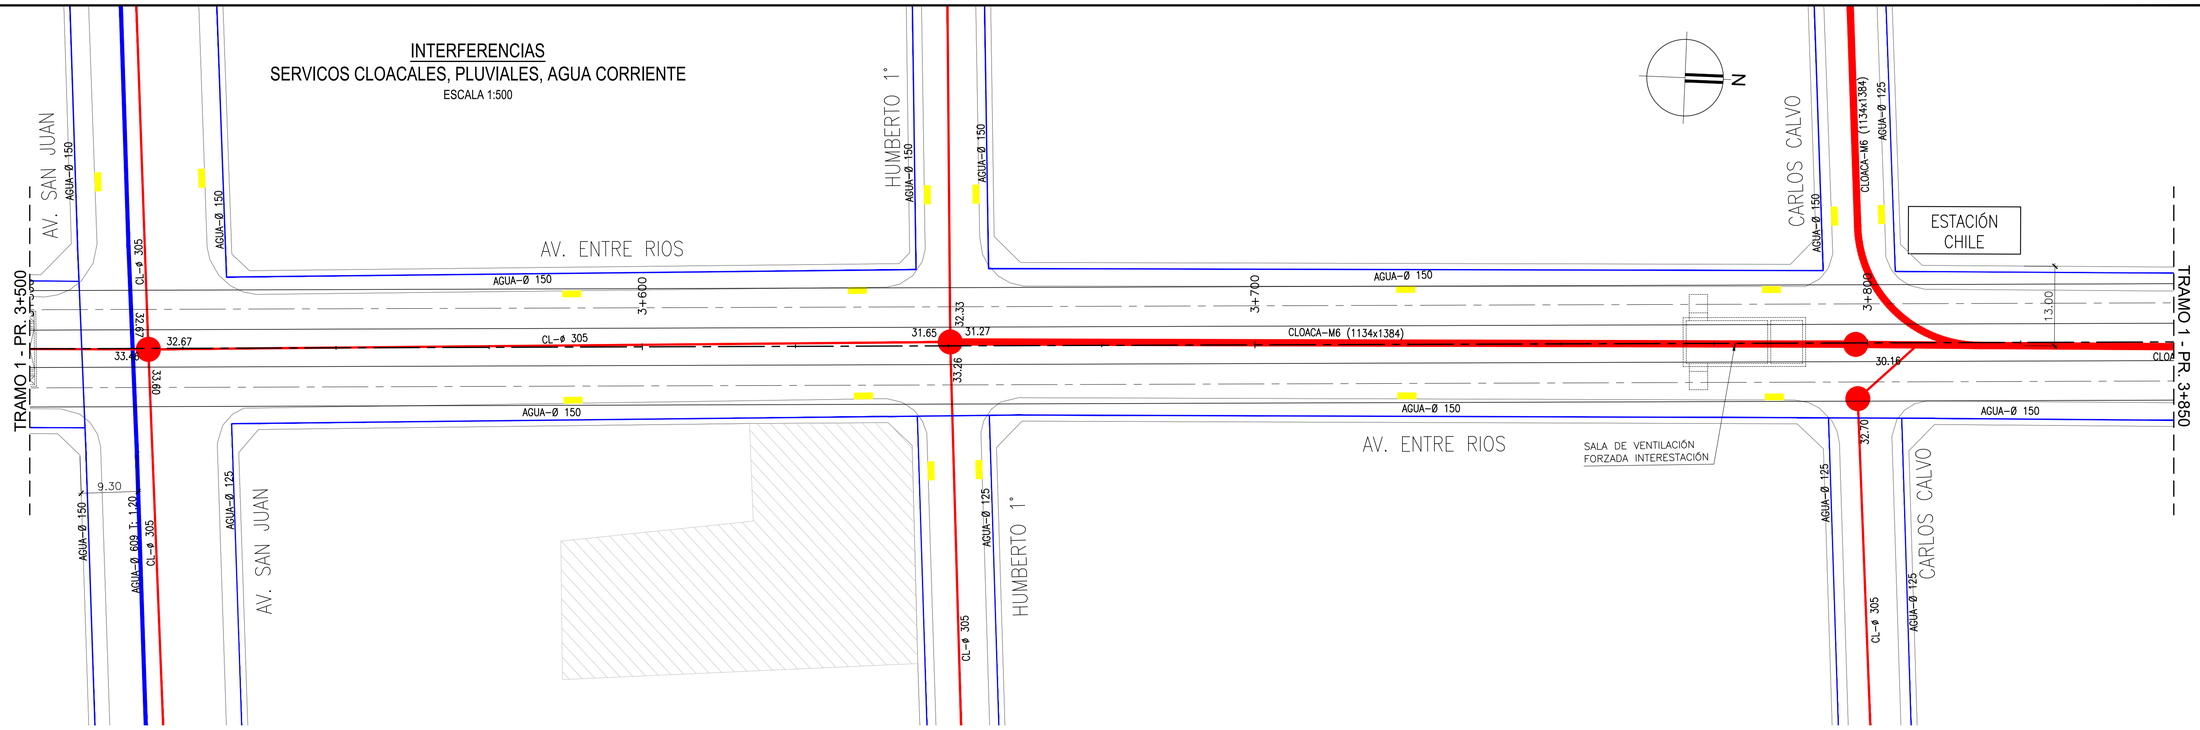

INTERFERENCIAS
GAS, TELEFONIA, ELECTRICIDAD, FIBRA OPTICA
ESCALA 1:500

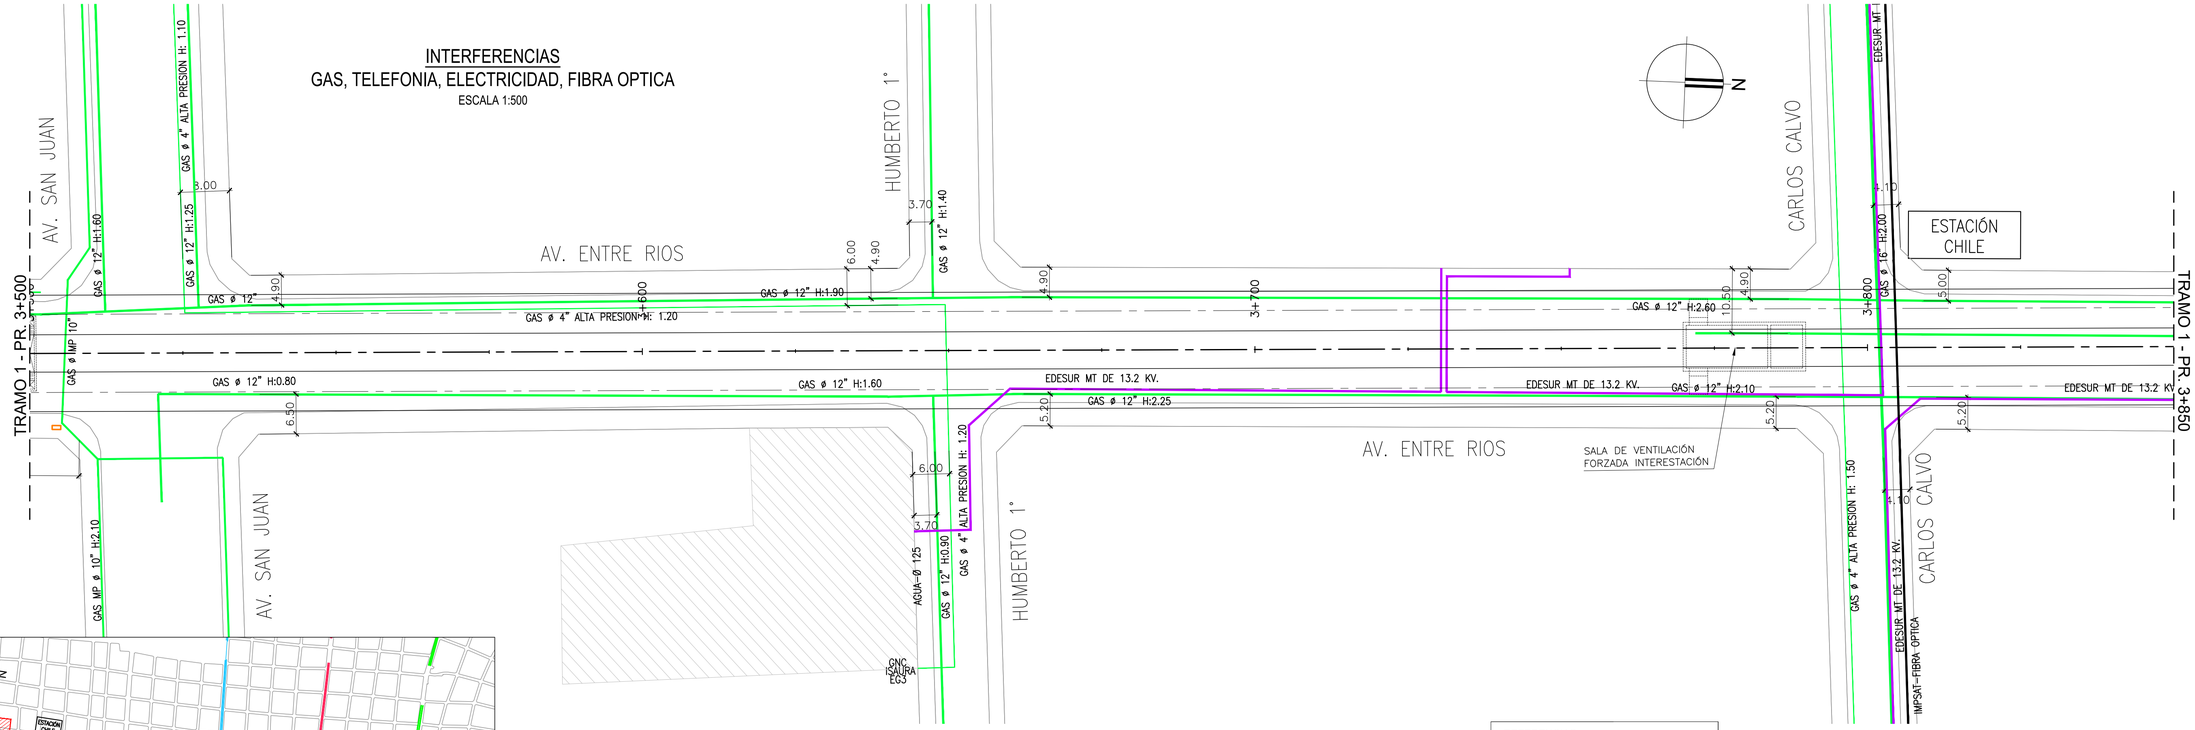

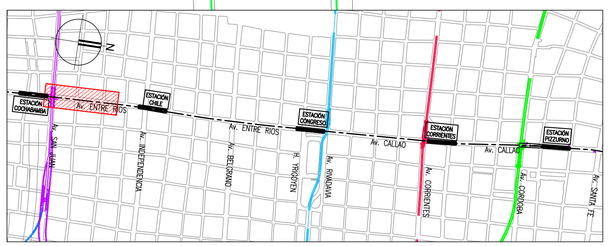

CROQUIS DE UBICACIÓN

REFERENCIAS
- RED CLOACAL
- RED PLUVIAL
- RED AGUA
- RED ELECTRICA
- RED GAS
- RED TELEFONICA
- RED FIBRA OPTICA MULTICANAL

0 10 20 30m
ESCALA 1:500

NOTAS:
EL PRESENTE PLANO ES INDICATIVO. LA CONTRATISTA CONFECCIONARA LOS PLANOS DE DETALLE DEFINITIVO, QUE DEBERAN SER APROBADOS POR LA D.G.D.IMF.I Y LA INSPECCION DE OBRA. EL PLANO PRESENTADO POR LA CONTRATISTA ESTARA EN LA DE TODO DE ACUERDO CON LA NORMATIVA VIGENTE.
TODAS LAS MEDIDAS Y NIVELES SE VERIFICARAN EN OBRA POR EL CONTRATISTA.
TODOS LOS DETALLES CONSTRUCTIVOS SERAN COORDINADOS Y COMPATIBILIZADOS EN OBRA

PLANO NO APTO PARA CONSTRUCCION.

MODIFICACIONES:

REVISION	FECHA	DESCRIPCION
0	19/09/2025	EMISION INICIAL
1	06/05/2026	REVISION DE PROYECTO

Gobierno de la Ciudad de Buenos Aires

MINISTERIO DE INFRAESTRUCTURA
SUBSECRETARIA DE PROYECTOS Y OBRAS
DIRECCION GENERAL DE PROYECTOS

DGPRO

Obra: LÍNEA F			IF-2026-28525919-GCABA-DGPRO
Plano: INTERFERENCIAS TRAMO 1 - PLANIMETRÍA GENERAL - PROG. 3+500 A 3+850			LF-GL-T01-INT-PL-011
Fecha: 06/05/2026	Eq. de Proyecto: UPU-ATEC-IATASA	Dibujó: D.B.	Revisó: P.C.	Escala: 1:500

Plano N° 011

8/5/2026 14:51 p. m.
LF-GL-T01-INT-PL-011p19_1.dwg

INTERFERENCIAS
SERVICOS CLOACALES, PLUVIALES, AGUA CORRIENTE
ESCALA 1:500

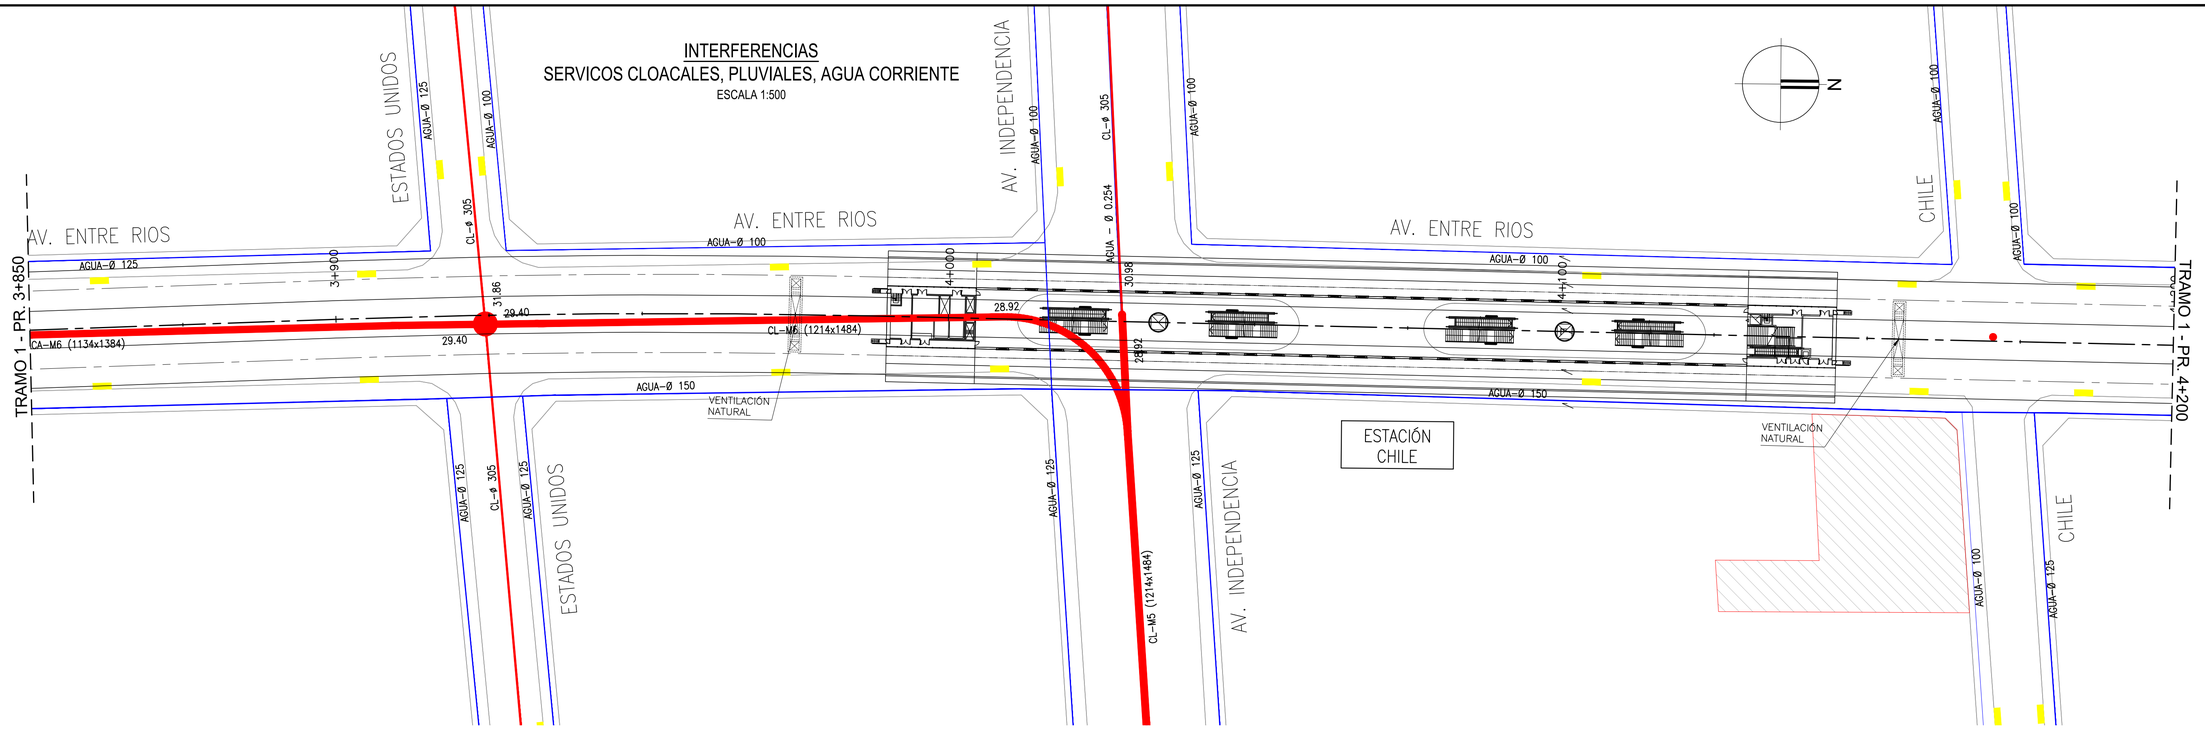

INTERFERENCIAS
GAS, TELEFONIA, ELECTRICIDAD, FIBRA OPTICA
ESCALA 1:500

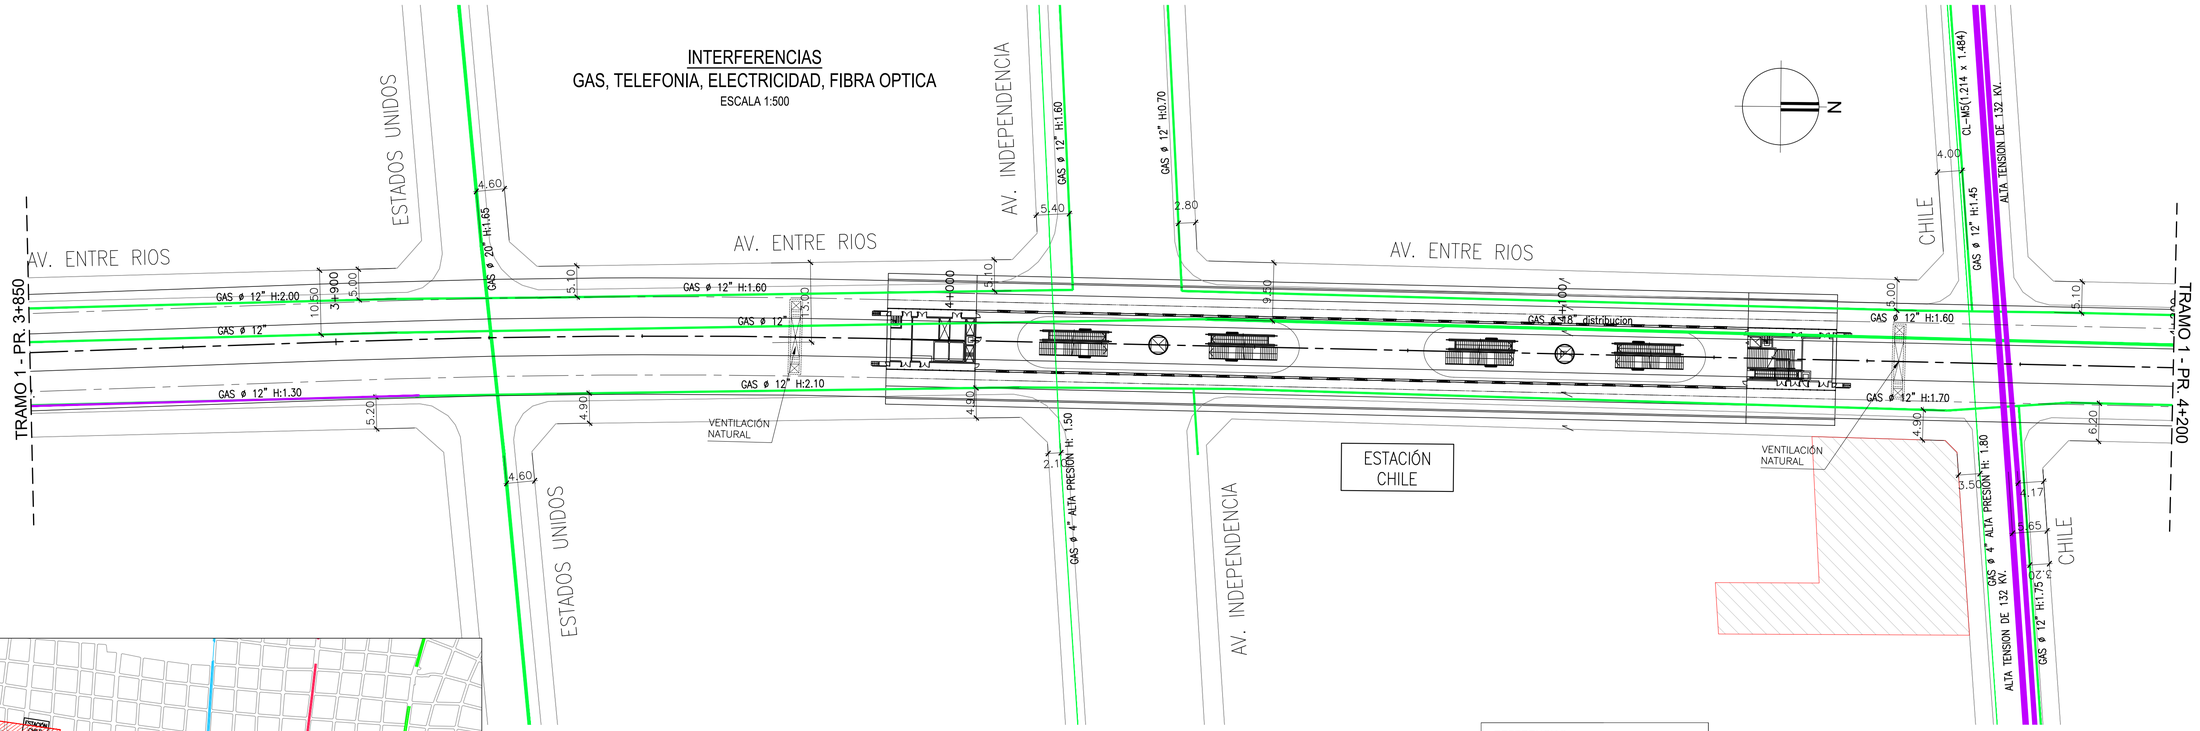

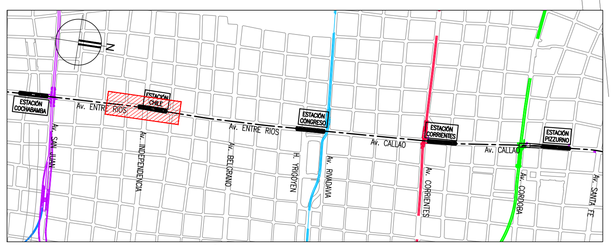

CROQUIS DE UBICACIÓN

REFERENCIAS
- RED CLOACAL
- RED PLUVIAL
- RED AGUA
- RED ELECTRICA
- RED GAS
- RED TELEFONICA
- RED FIBRA OPTICA MULTICANAL

0 10 20 30m
ESCALA 1:500

NOTAS:
EL PRESENTE PLANO ES INDICATIVO. LA CONTRATISTA CONFECCIONARA LOS PLANOS DE DETALLE DEFINITIVO, QUE DEBERAN SER APROBADOS POR LA D.G.O.INF.U Y LA INSPECCION DE OBRA. EL PLANO PRESENTADO POR LA CONTRATISTA ESTARA EN UN TODO DE ACUERDO CON LA NORMATIVA VIGENTE.
TODAS LAS MEDIDAS Y NIVELES SE VERIFICARAN EN OBRA POR EL CONTRATISTA.
TODOS LOS DETALLES CONSTRUCTIVOS SERAN COORDINADOS Y COMPATIBILIZADOS EN OBRA

PLANO NO APTO PARA CONSTRUCCION.

MODIFICACIONES:

REVISION	FECHA	DESCRIPCION
0	19/05/2025	EMISION INICIAL
1	06/05/2026	REVISION DE PROYECTO

Gobierno de la Ciudad de Buenos Aires

MINISTERIO DE INFRAESTRUCTURA
SUBSECRETARIA DE PROYECTOS Y OBRAS
DIRECCION GENERAL DE PROYECTOS

DGPRO

Obra: LÍNEA F
IF-2026-28525919-GCABA-DGPRO
Plano: INTERFERENCIAS TRAMO 1 - PLANIMETRÍA GENERAL - PROG. 3+850 A 4+200 | LF-GL-T01-INT-PL-012
Fecha: 06/05/2026 | Eq. de Proyecto: UPU-ATEC-IATASA | Dibujó: D.B. | Revisó: P.C. | Escala: 1:500
Plano N° 012

8/5/2026 14:51 p. m.
LF-GL-T01-INT-PL-001d19_1.dwg

INTERFERENCIAS
SERVICOS CLOACALES, PLUVIALES, AGUA CORRIENTE
ESCALA 1:500

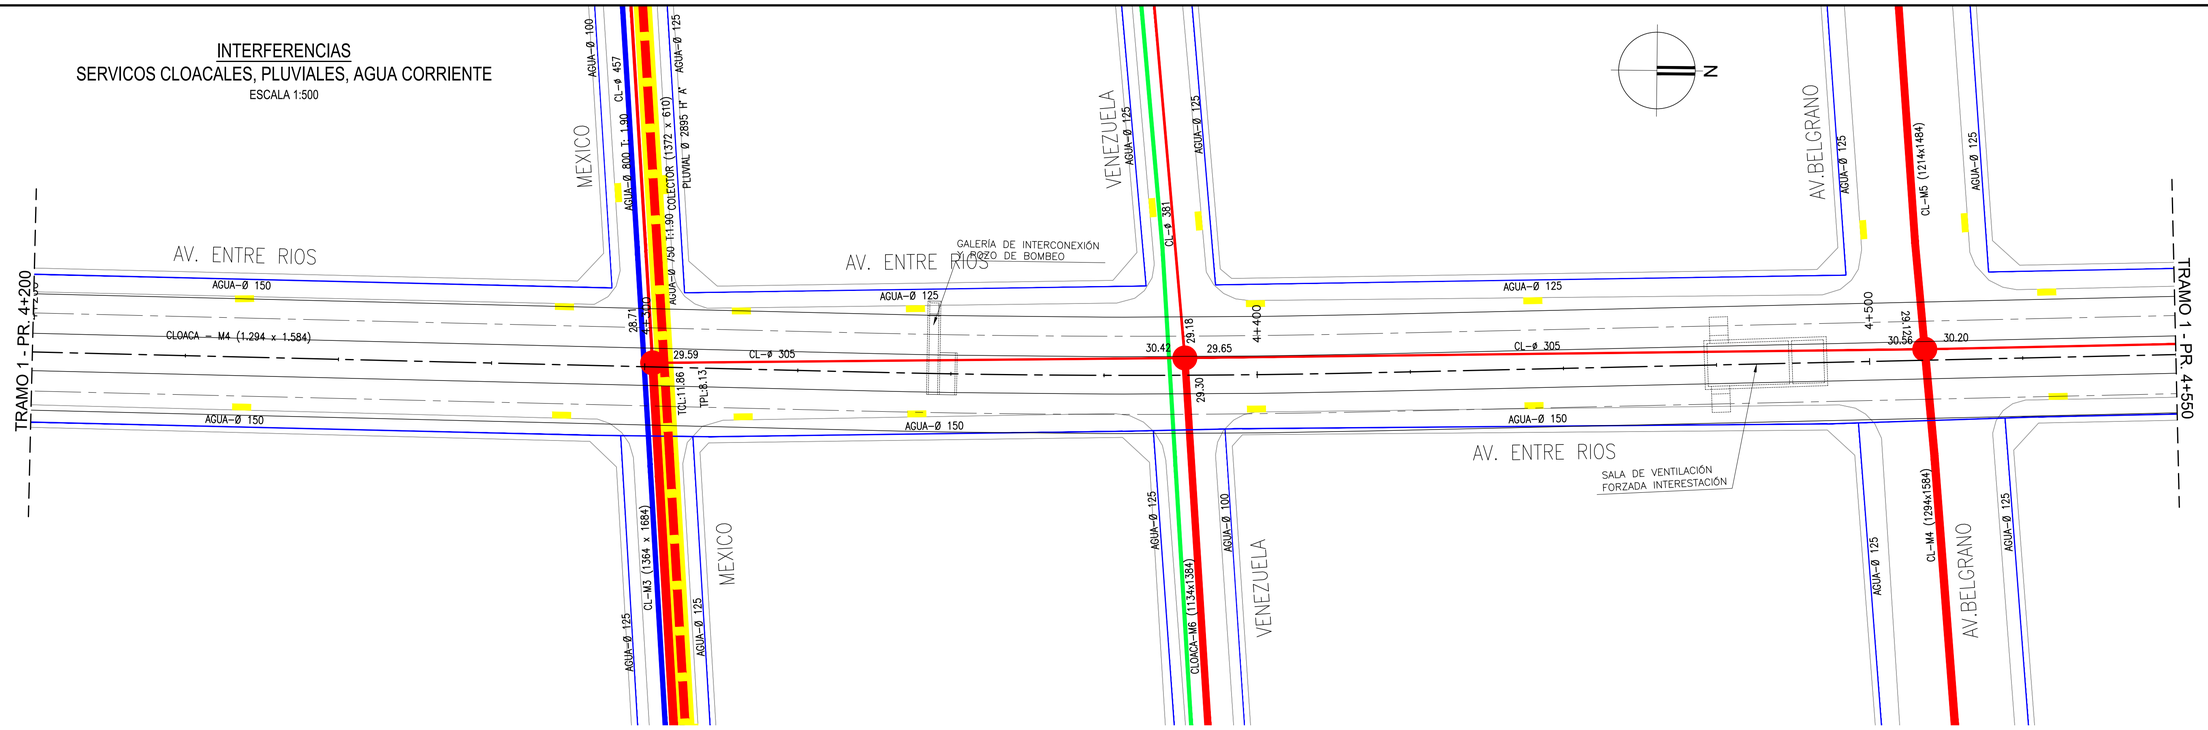

INTERFERENCIAS
GAS, TELEFONIA, ELECTRICIDAD, FIBRA OPTICA
ESCALA 1:500

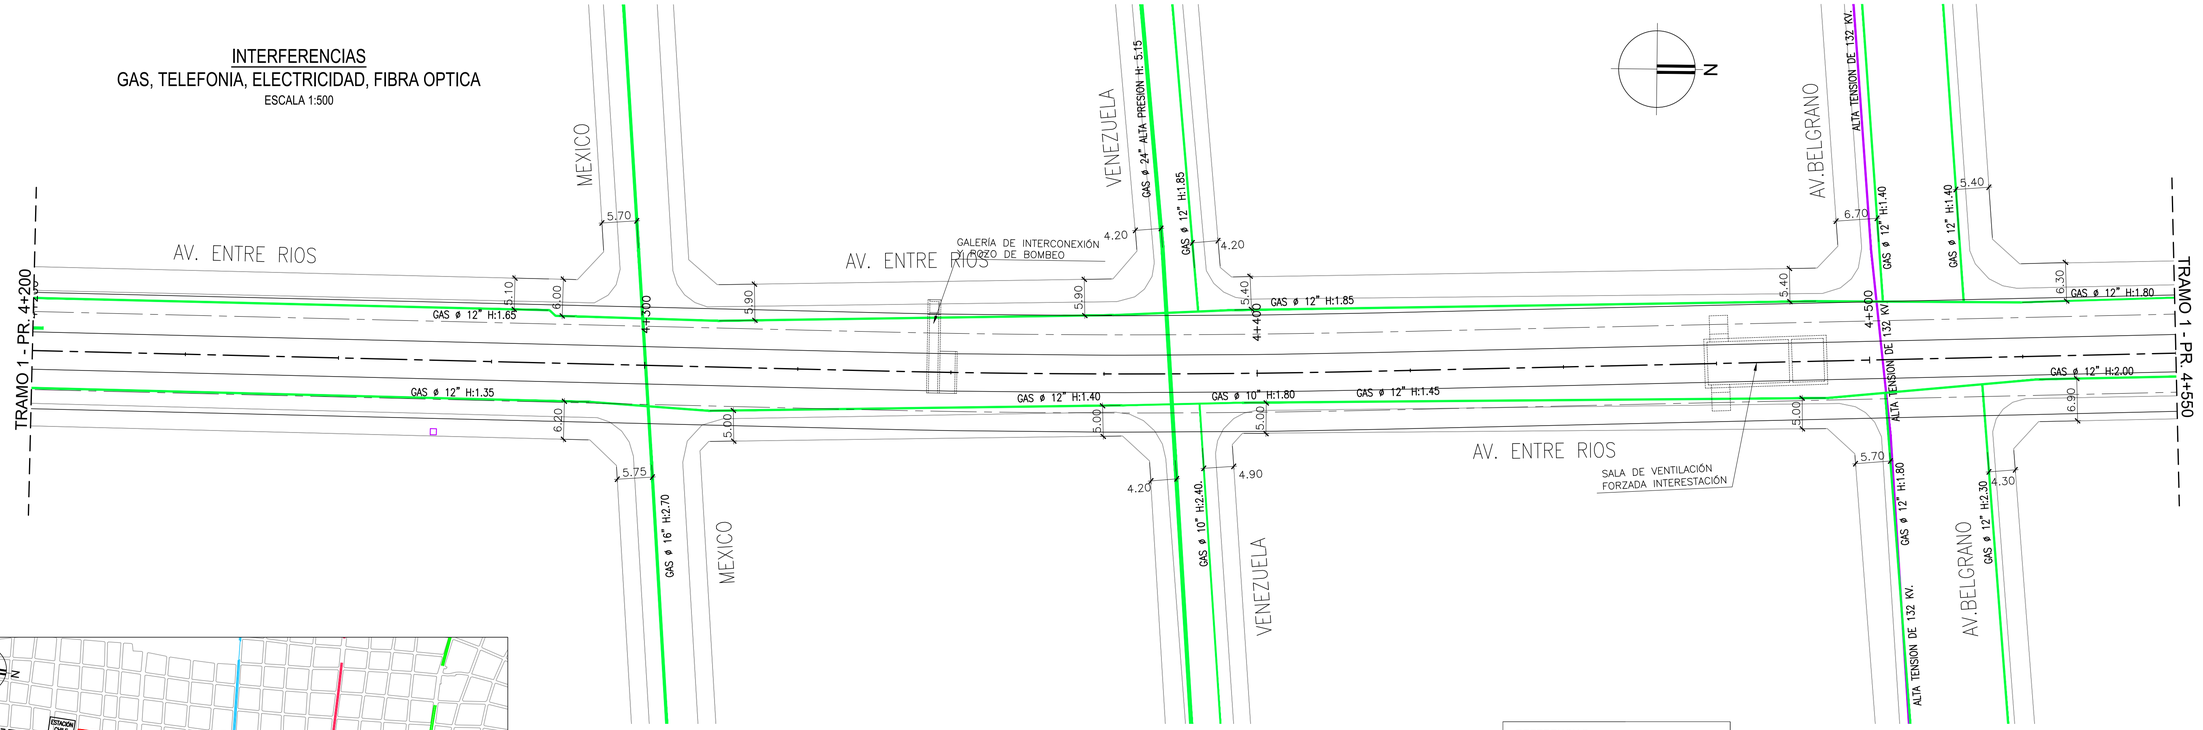

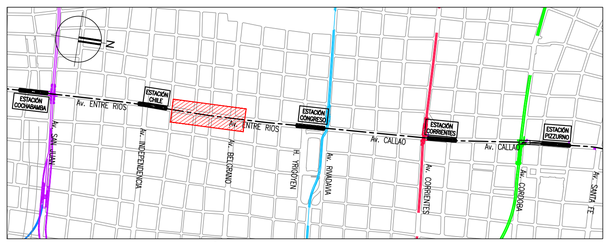

CROQUIS DE UBICACIÓN

REFERENCIAS
- RED CLOACAL
- RED PLUVIAL
- RED AGUA
- RED ELECTRICA
- RED GAS
- RED TELEFONICA
- RED FIBRA OPTICA MULTICANAL

0 10 20 30m
ESCALA 1:500

NOTAS:
EL PRESENTE PLANO ES INDICATIVO. LA CONTRATISTA CONFECCIONARA LOS PLANOS DE DETALLE DEFINITIVO, QUE DEBERAN SER APROBADOS POR LA D.G.D.INF.U Y LA INSPECCION DE OBRA. EL PLANO PRESENTADO POR LA CONTRATISTA ESTARA EN UN TODO DE ACUERDO CON LA NORMATIVA VIGENTE.
TODAS LAS MEDIDAS Y NIVELES SE VERIFICARAN EN OBRA POR EL CONTRATISTA.
TODOS LOS DETALLES CONSTRUCTIVOS SERAN COORDINADOS Y COMPATIBILIZADOS EN OBRA

PLANO NO APTO PARA CONSTRUCCION.

MODIFICACIONES:

REVISION	FECHA	DESCRIPCION
0	19/09/2025	EMISION INICIAL
1	06/05/2026	REVISION DE PROYECTO

Gobierno de la Ciudad de Buenos Aires

MINISTERIO DE INFRAESTRUCTURA
SUBSECRETARIA DE PROYECTOS Y OBRAS
DIRECCION GENERAL DE PROYECTOS

DGPRO

Obra: LÍNEA F					IF-2026-28525919-GCABA-DGPRO Plano N°
Plano: INTERFERENCIAS TRAMO 1 - PLANIMETRÍA GENERAL - PROG. 4+200 A 4+550					LF-GL-T01-INT-PL-013 013
Fecha: 06/05/2026	Eq. de Proyecto: UPU-ATEC-IATASA	Dibujó: D.B.	Revisó: P.C.	Escala: 1:500	

8/5/2026 14:51 p. m.
LF-GL-T01-INT-PL-0016019_1.dwg

INTERFERENCIAS
SERVICOS CLOACALES, PLUVIALES, AGUA CORRIENTE
ESCALA 1:500

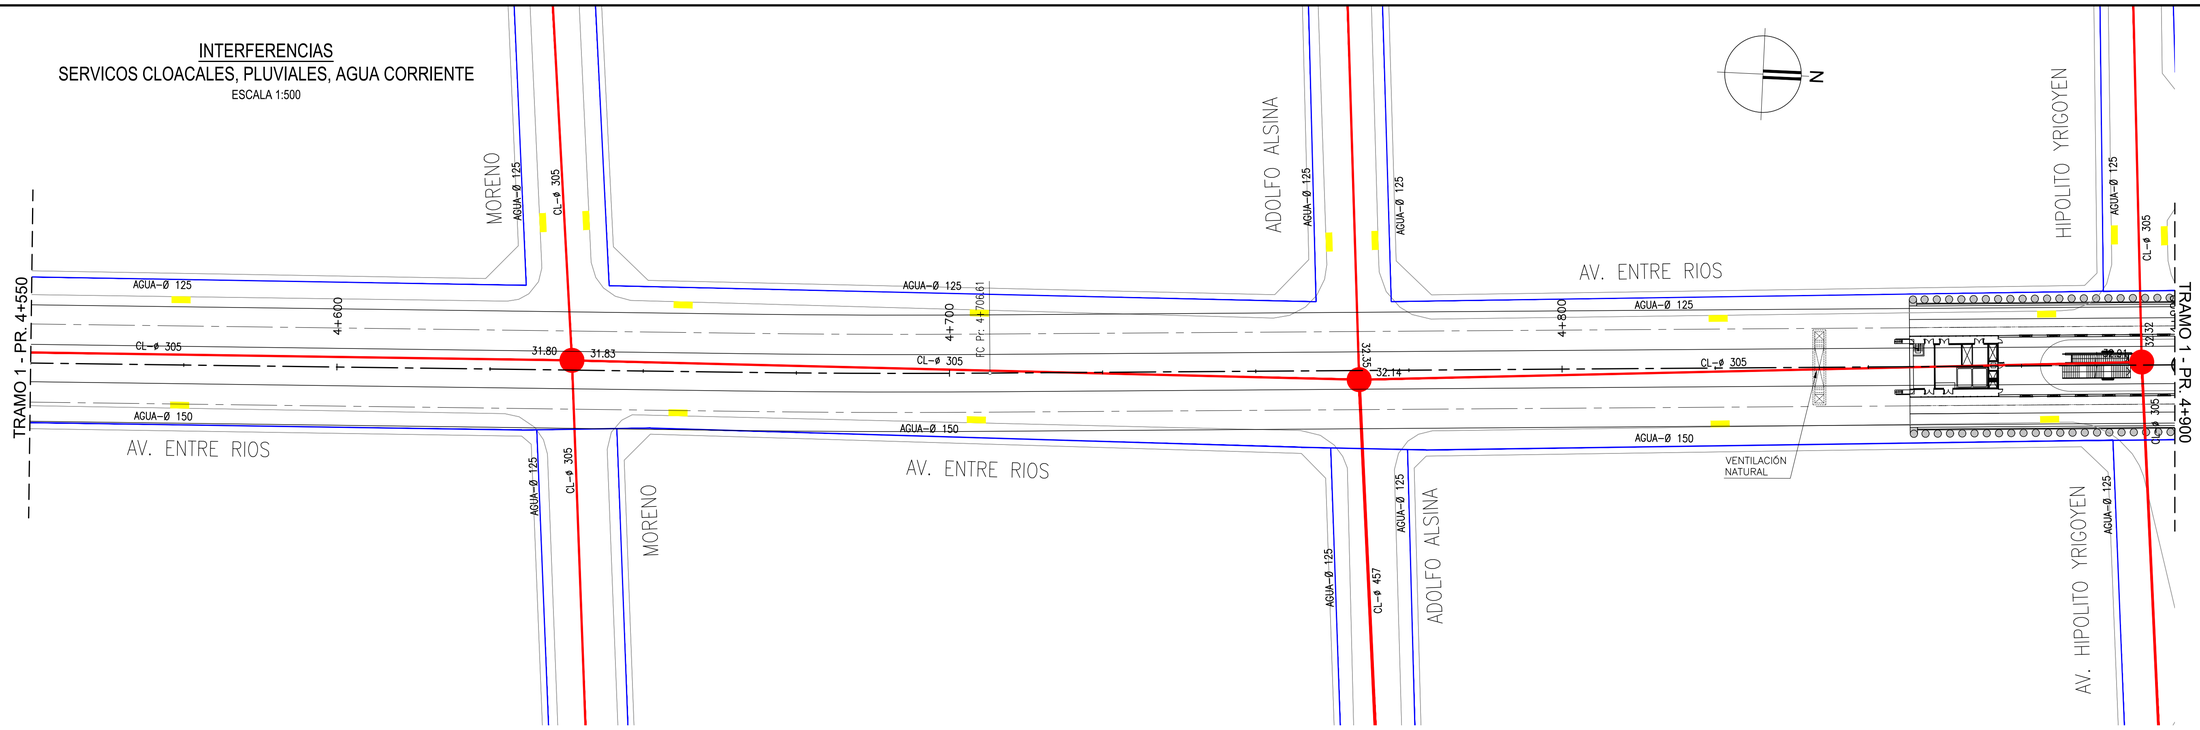

INTERFERENCIAS
GAS, TELEFONIA, ELECTRICIDAD, FIBRA OPTICA
ESCALA 1:500

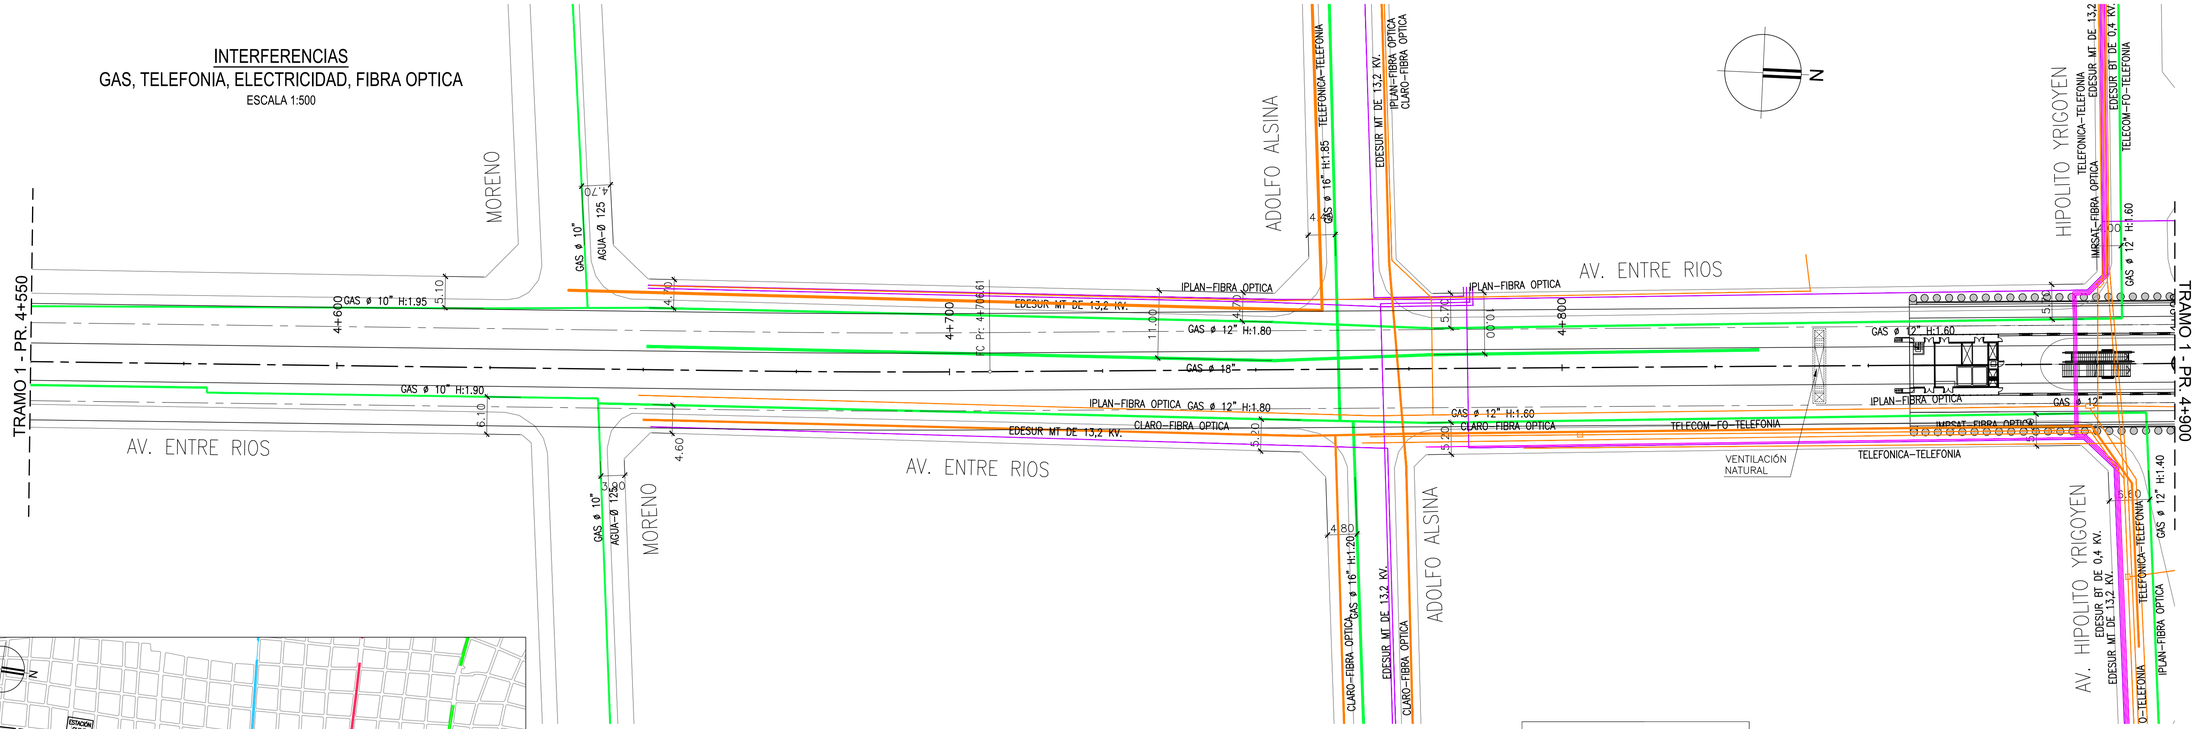

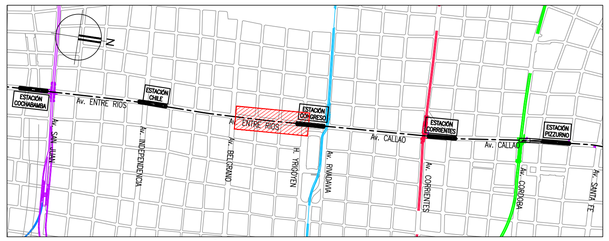

CROQUIS DE UBICACIÓN

REFERENCIAS
- RED CLOACAL
- RED PLUVIAL
- RED AGUA
- RED ELECTRICA
- RED GAS
- RED TELEFONICA
- RED FIBRA OPTICA MULTICANAL

0 10 20 30m
ESCALA 1:500

NOTAS:
1. EL PRESENTE PLANO ES INDICATIVO, LA CONTRATISTA CONFECCIONARA LOS PLANOS DE DETALLE DEFINITIVO, QUE DEBERAN SER APROBADOS POR LA D.G.O.IMF.U Y LA INSPECCION DE OBRA. EL PLANO PRESENTADO POR LA CONTRATISTA ESTARA EN UN TODO DE ACUERDO CON LA NORMATIVA VIGENTE.
2. TODAS LAS MEDIDAS Y NIVELES SE VERIFICARAN EN OBRA POR EL CONTRATISTA.
3. TODOS LOS DETALLES CONSTRUCTIVOS SERAN COORDINADOS Y COMPATIBILIZADOS EN OBRA

PLANO NO APTO PARA CONSTRUCCION.

MODIFICACIONES:

REVISION	FECHA	DESCRIPCION
0	19/05/225	EMISION INICIAL
1	06/05/226	REVISION DE PROYECTO

MINISTERIO DE INFRAESTRUCTURA
SUBSECRETARIA DE PROYECTOS Y OBRAS
DIRECCION GENERAL DE PROYECTOS

DGPRO

Obra: LÍNEA F				IF-2026-28525919-GCABA-DGPRO Plano N°
Plano: INTERFERENCIAS TRAMO 1 - PLANIMETRÍA GENERAL - PROG. 4+550 A 4+900				LF-GL-T01-INT-PL-014
Fecha: 06/05/2026	Eq. de Proyecto: UPU-ATEC-IATASA	Dibujó: D.B.	Revisó: P.C.	Escala: 1:500

014

8/5/2026 14:51 p. m.
LF-GL-T01-INT-PL-001o019_1.dwg

INTERFERENCIAS
SERVICOS CLOACALES, PLUVIALES, AGUA CORRIENTE
ESCALA 1:500

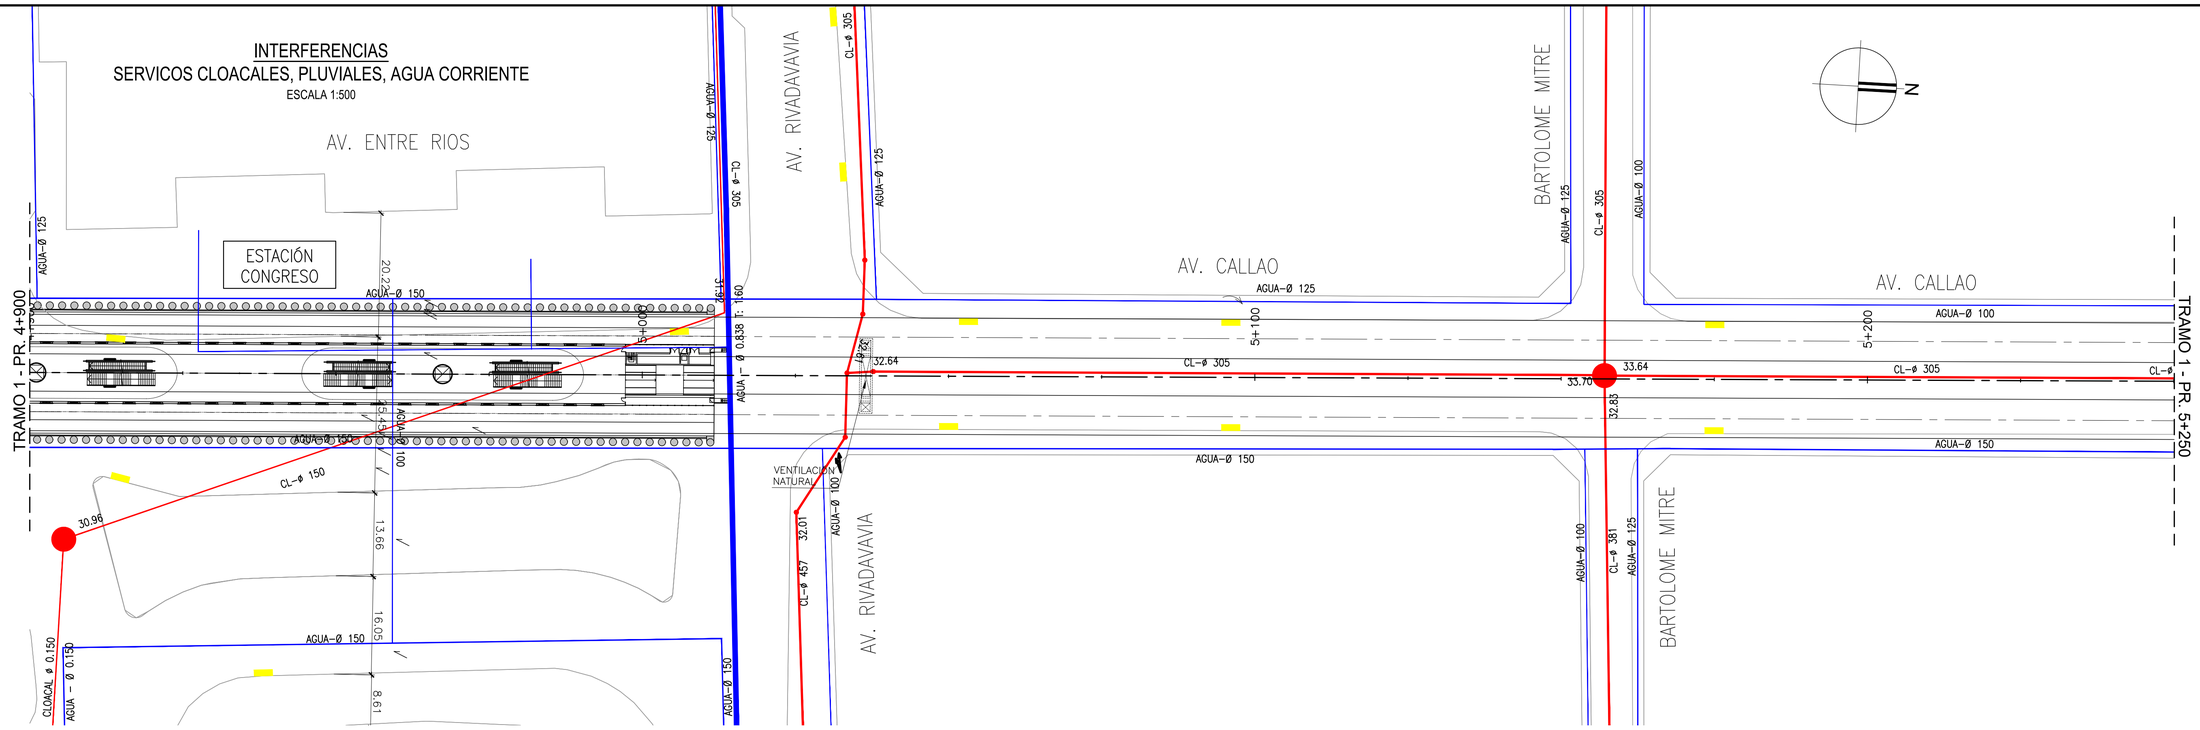

INTERFERENCIAS
GAS, TELEFONIA, ELECTRICIDAD, FIBRA OPTICA
ESCALA 1:500

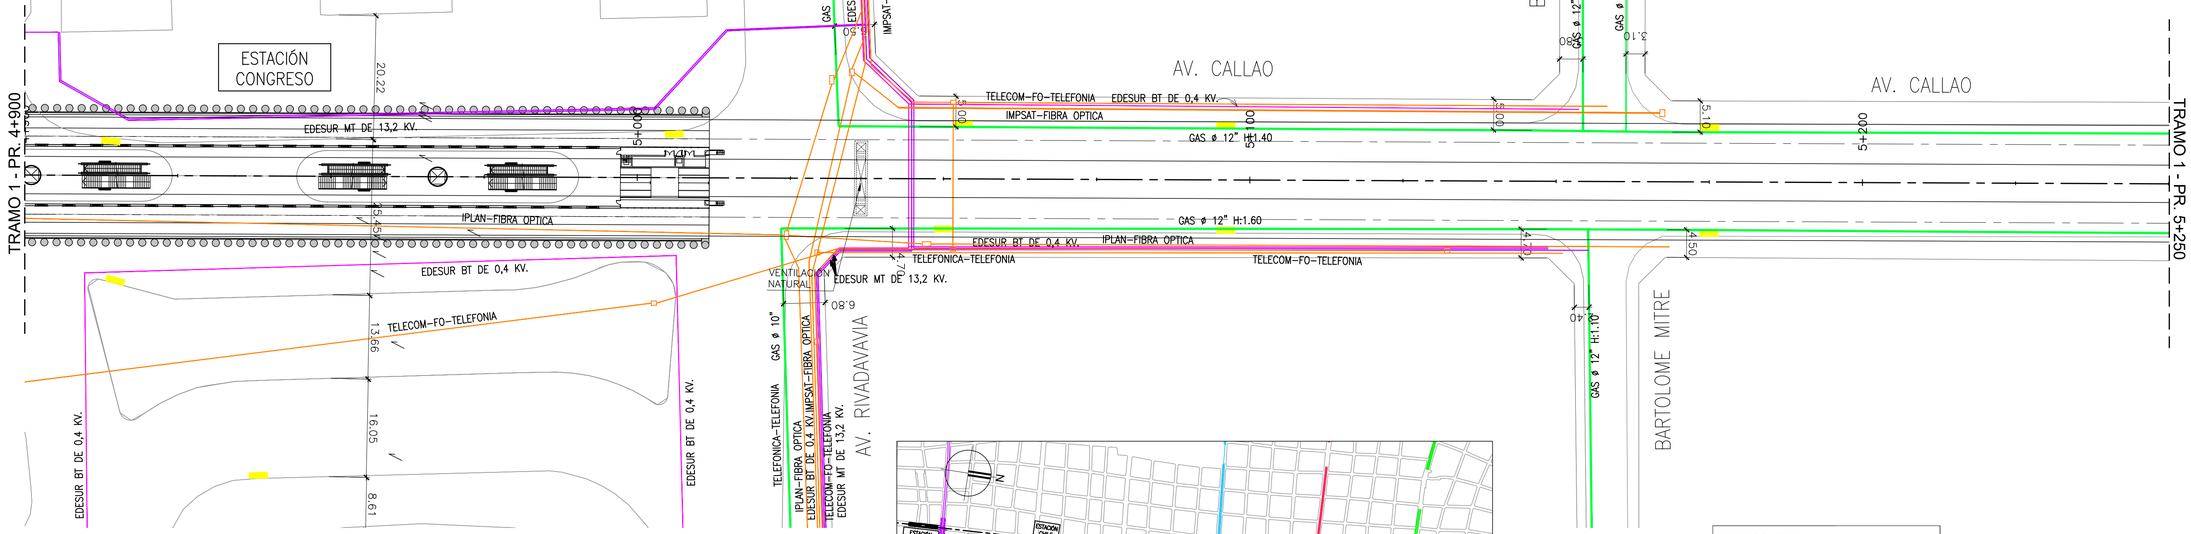

CROQUIS DE UBICACIÓN

REFERENCIAS
- RED CLOACAL
- RED PLUVIAL
- RED AGUA
- RED ELECTRICA
- RED GAS
- RED TELEFONICA
- RED FIBRA OPTICA MULTICANAL

0 10 20 30m
ESCALA 1:500

NOTAS:
1. EL PRESENTE PLANO ES INDICATIVO. LA CONTRATISTA CONFECCIONARA LOS PLANOS DE DETALLE DEFINITIVO, QUE DEBERAN SER APROBADOS POR LA D.G.D.MF.U Y LA INSPECCION DE OBRA. EL PLANO PRESENTADO POR LA CONTRATISTA ESTARA EN UN TODO DE ACUERDO CON LA NORMATIVA VIGENTE.
2. TODAS LAS MEDIDAS Y NIVELES SE VERIFICARAN EN OBRA POR EL CONTRATISTA.
3. TODOS LOS DETALLES CONSTRUCTIVOS SERAN COORDINADOS Y COMPATIBILIZADOS EN OBRA

PLANO NO APTO PARA CONSTRUCCION.

MODIFICACIONES:

REVISION	FECHA	DESCRIPCION
0	19/05/2025	EMISION INICIAL
1	06/05/2026	REVISION DE PROYECTO

Gobierno de la Ciudad de Buenos Aires

MINISTERIO DE INFRAESTRUCTURA
SUBSECRETARIA DE PROYECTOS Y OBRAS
DIRECCION GENERAL DE PROYECTOS

DGPRO

Obra: LÍNEA F					IF-2026-28525919-GCABA-DGPRO
Plano: INTERFERENCIAS TRAMO 1 - PLANIMETRÍA GENERAL - PROG. 4+900 A 5+250					LF-GL-T01-INT-PL-015
Fecha: 06/05/2026	Eq. de Proyecto: UPU-ATEC-IATASA	Dibujó: D.B.	Revisó: P.C.	Escala: 1:500	Plano N° 015

8/5/2026 14:51 p. m.
LF-GL-T01-INT-PL-001ed19_1.dwg

INTERFERENCIAS
SERVICOS CLOACALES, PLUVIALES, AGUA CORRIENTE
ESCALA 1:500

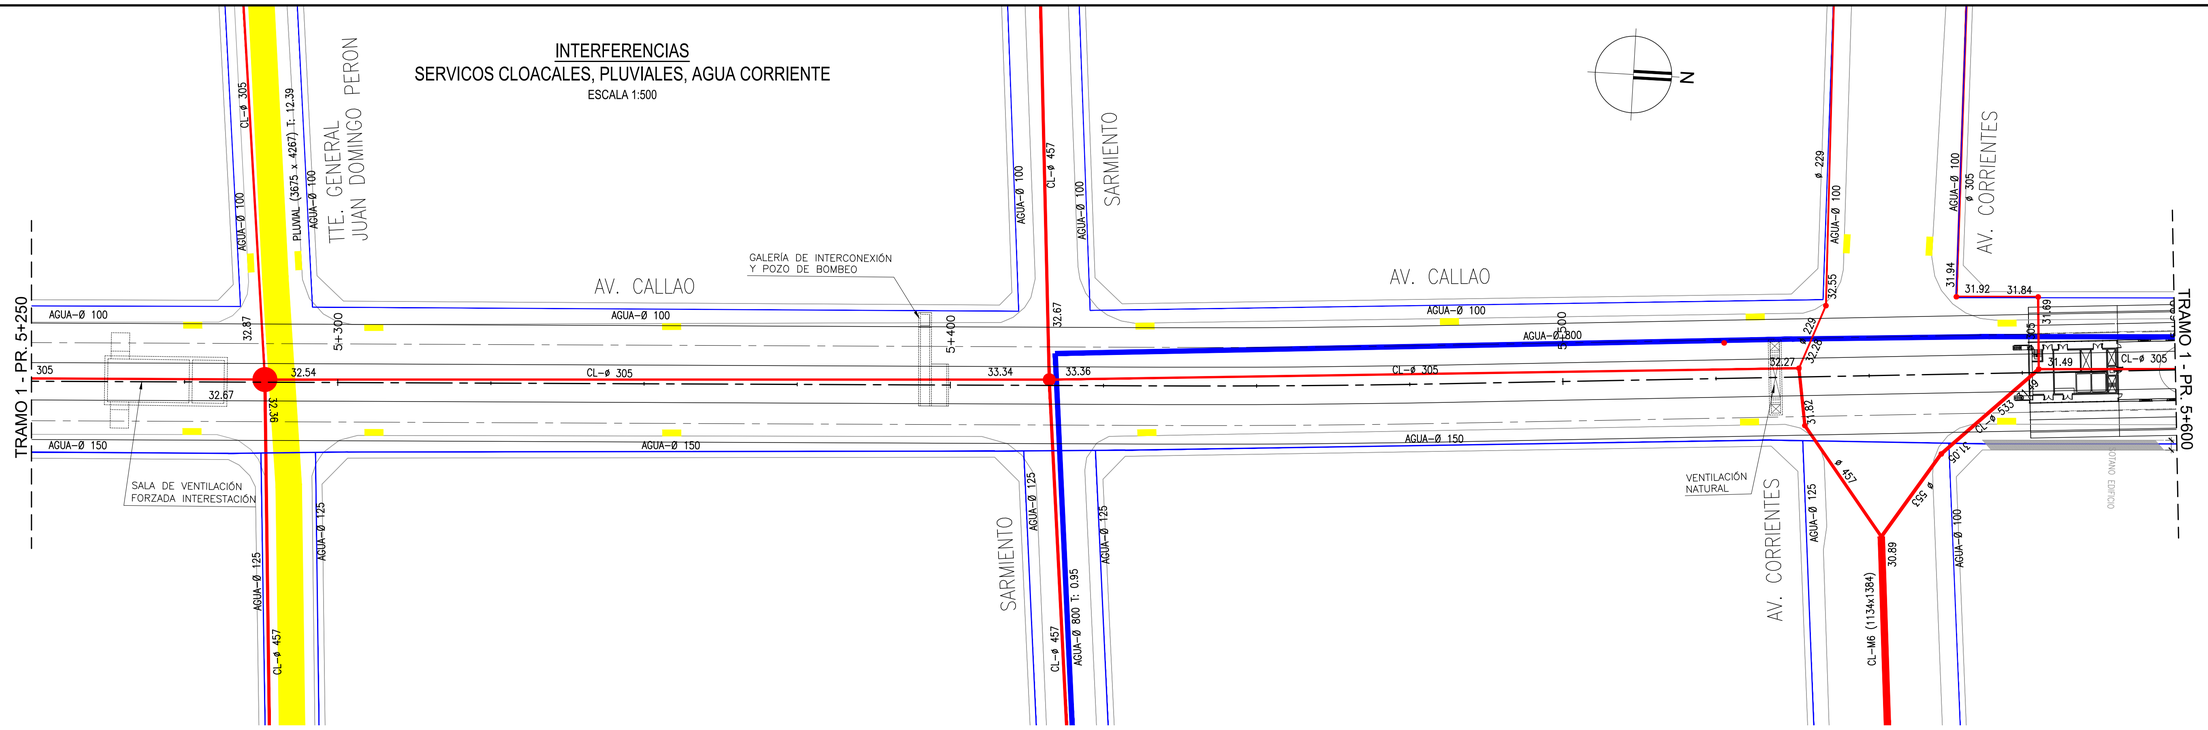

INTERFERENCIAS
GAS, TELEFONIA, ELECTRICIDAD, FIBRA OPTICA
ESCALA 1:500

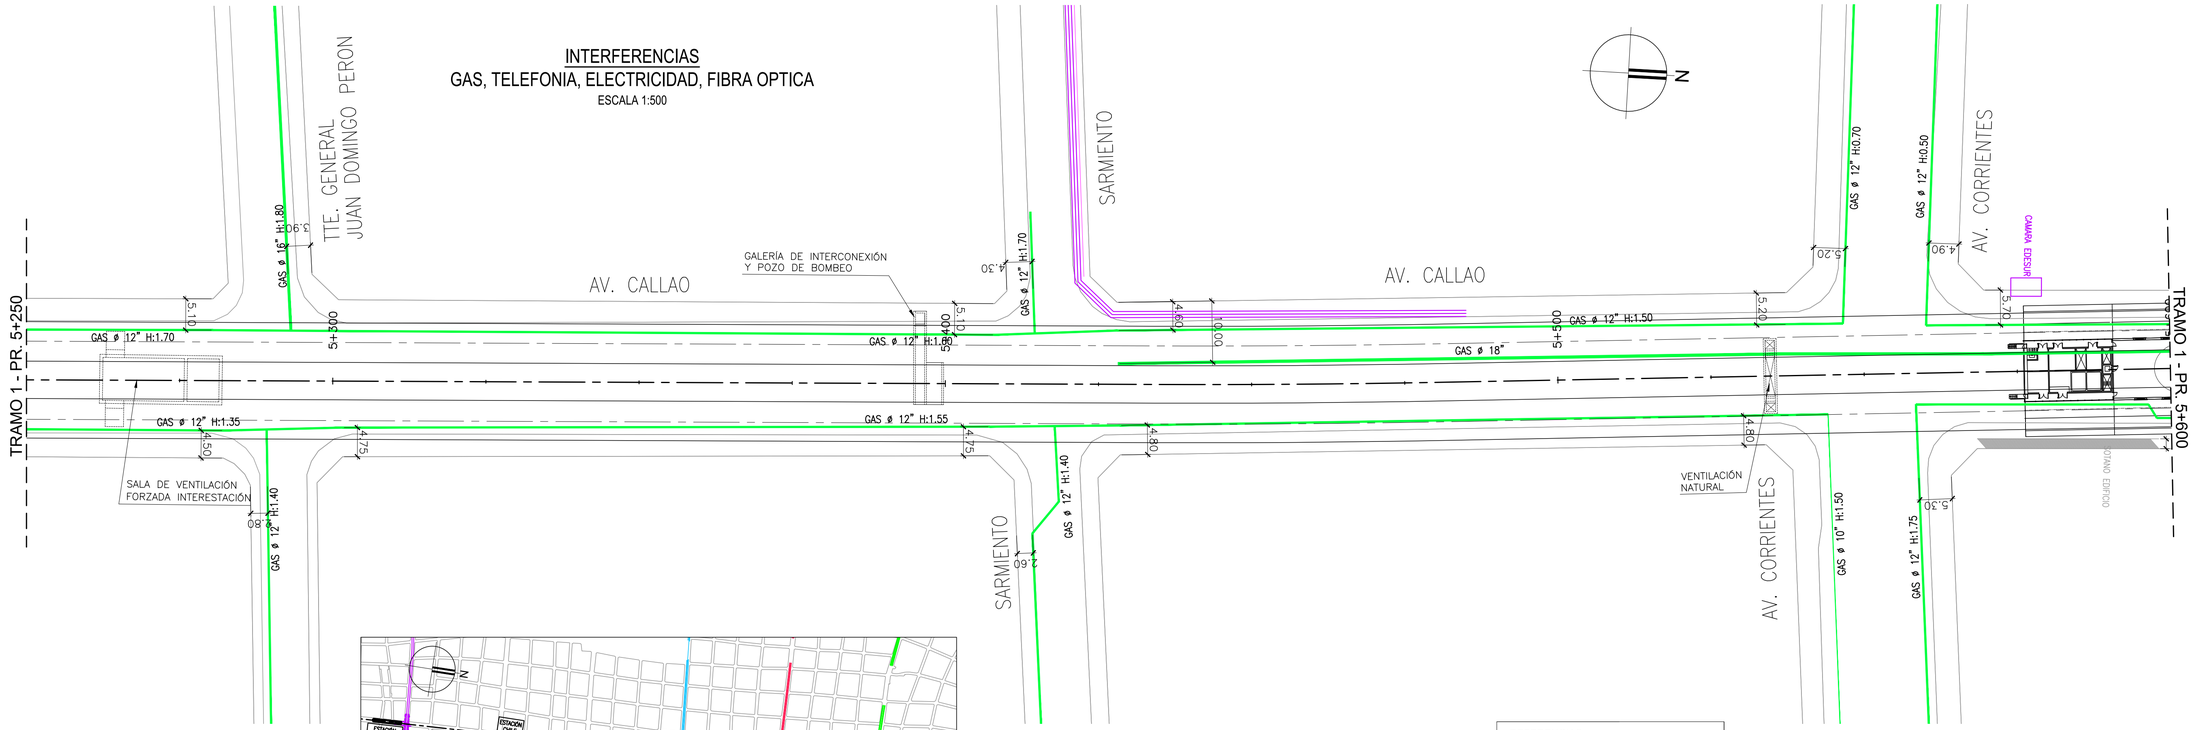

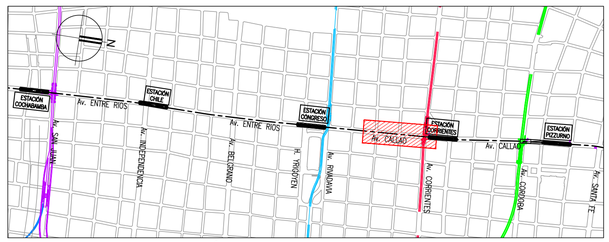

CROQUIS DE UBICACIÓN

REFERENCIAS
- RED CLOACAL
- RED PLUVIAL
- RED AGUA
- RED ELECTRICA
- RED GAS
- RED TELEFONICA
- RED FIBRA OPTICA MULTICANAL

0 10 20 30m
ESCALA 1:500

NOTAS:
EL PRESENTE PLANO ES INDICATIVO. LA CONTRATISTA CONFECCIONARA LOS PLANOS DE DETALLE DEFINITIVO, QUE DEBERAN SER APROBADOS POR LA D.G.O.INF.U Y LA INSPECCION DE OBRA. EL PLANO PRESENTADO POR LA CONTRATISTA ESTARA EN UN TODO DE ACUERDO CON LA NORMATIVA VIGENTE.
TODAS LAS MEDIDAS Y NIVELES SE VERIFICARAN EN OBRA POR EL CONTRATISTA.
TODOS LOS DETALLES CONSTRUCTIVOS SERAN COORDINADOS Y COMPATIBILIZADOS EN OBRA

PLANO NO APTO PARA CONSTRUCCION.

MODIFICACIONES:

REVISION	FECHA	DESCRIPCION
0	19/09/2025	EMISION INICIAL
1	06/05/2026	REVISION DE PROYECTO

MINISTERIO DE INFRAESTRUCTURA
SUBSECRETARIA DE PROYECTOS Y OBRAS
DIRECCION GENERAL DE PROYECTOS

DGPRO

Obra: LÍNEA F
IF-2026-28525919-GCABA-DGPRO
Plano: INTERFERENCIAS TRAMO 1 - PLANIMETRÍA GENERAL - PROG. 5+250 A 5+600 | LF-GL-T01-INT-PL-016
Fecha: 06/05/2026 | Eq. de Proyecto: UPU-ATEC-IATASA | Dibujó: D.B. | Revisó: P.C. | Escala: 1:500
Plano N° 016

8/5/2026 14:51 p. m.
LF-GL-T01-INT-PL-0016019_1.dwg

INTERFERENCIAS
SERVICOS CLOACALES, PLUVIALES, AGUA CORRIENTE
ESCALA 1:500

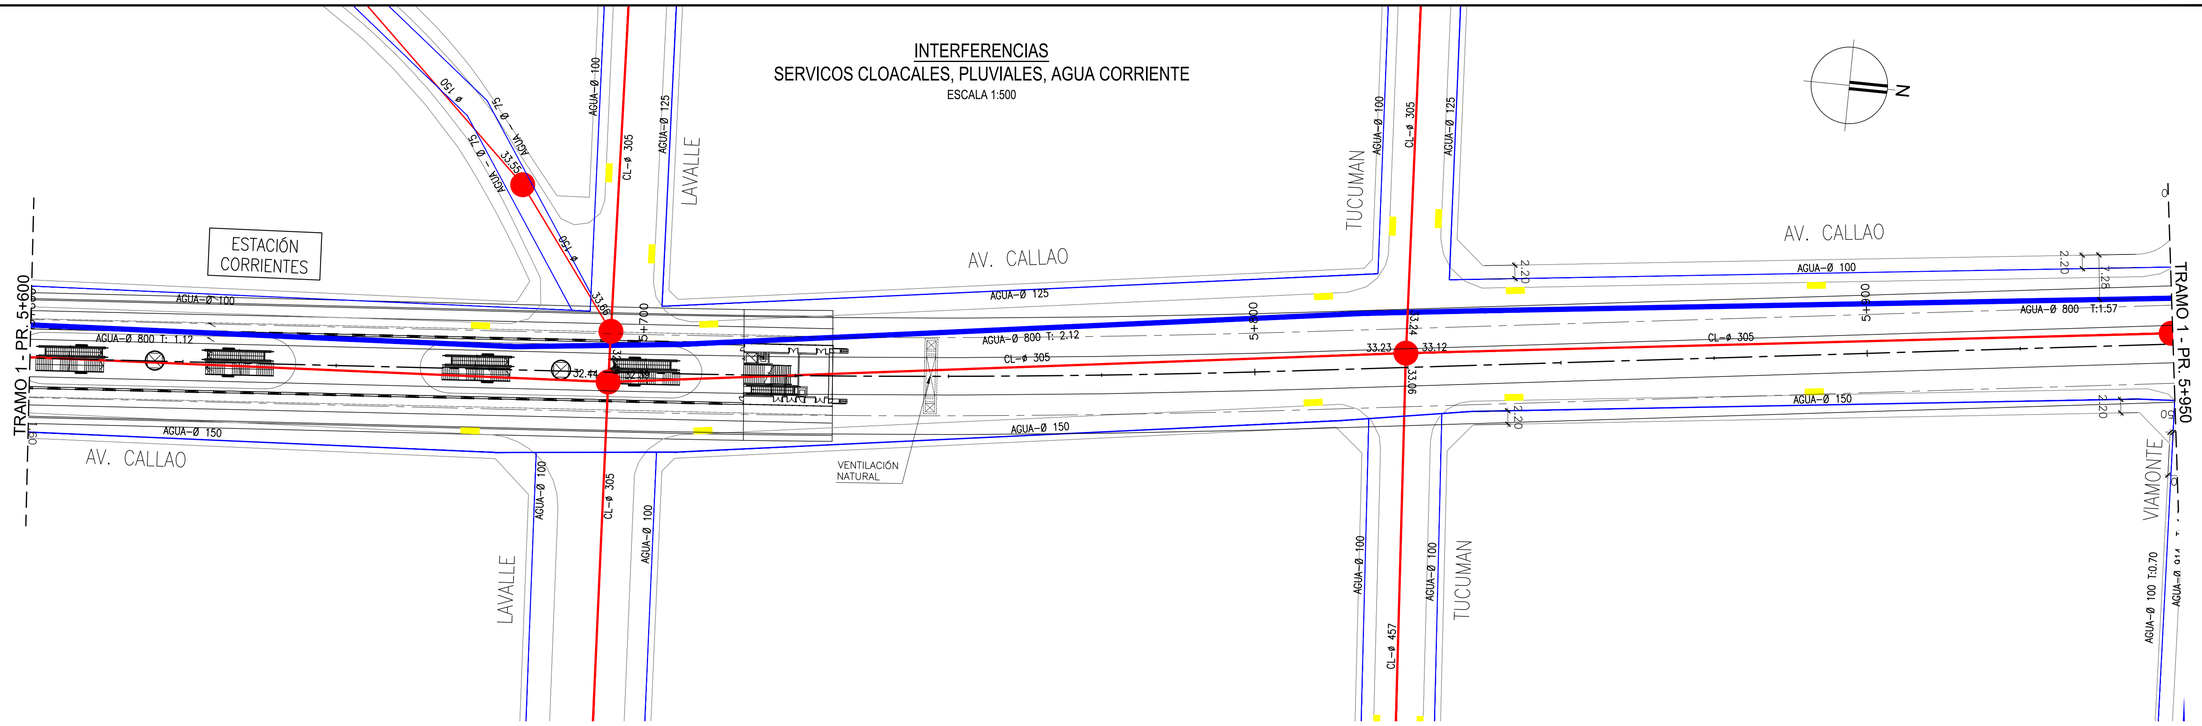

INTERFERENCIAS
GAS, TELEFONIA, ELECTRICIDAD, FIBRA OPTICA
ESCALA 1:500

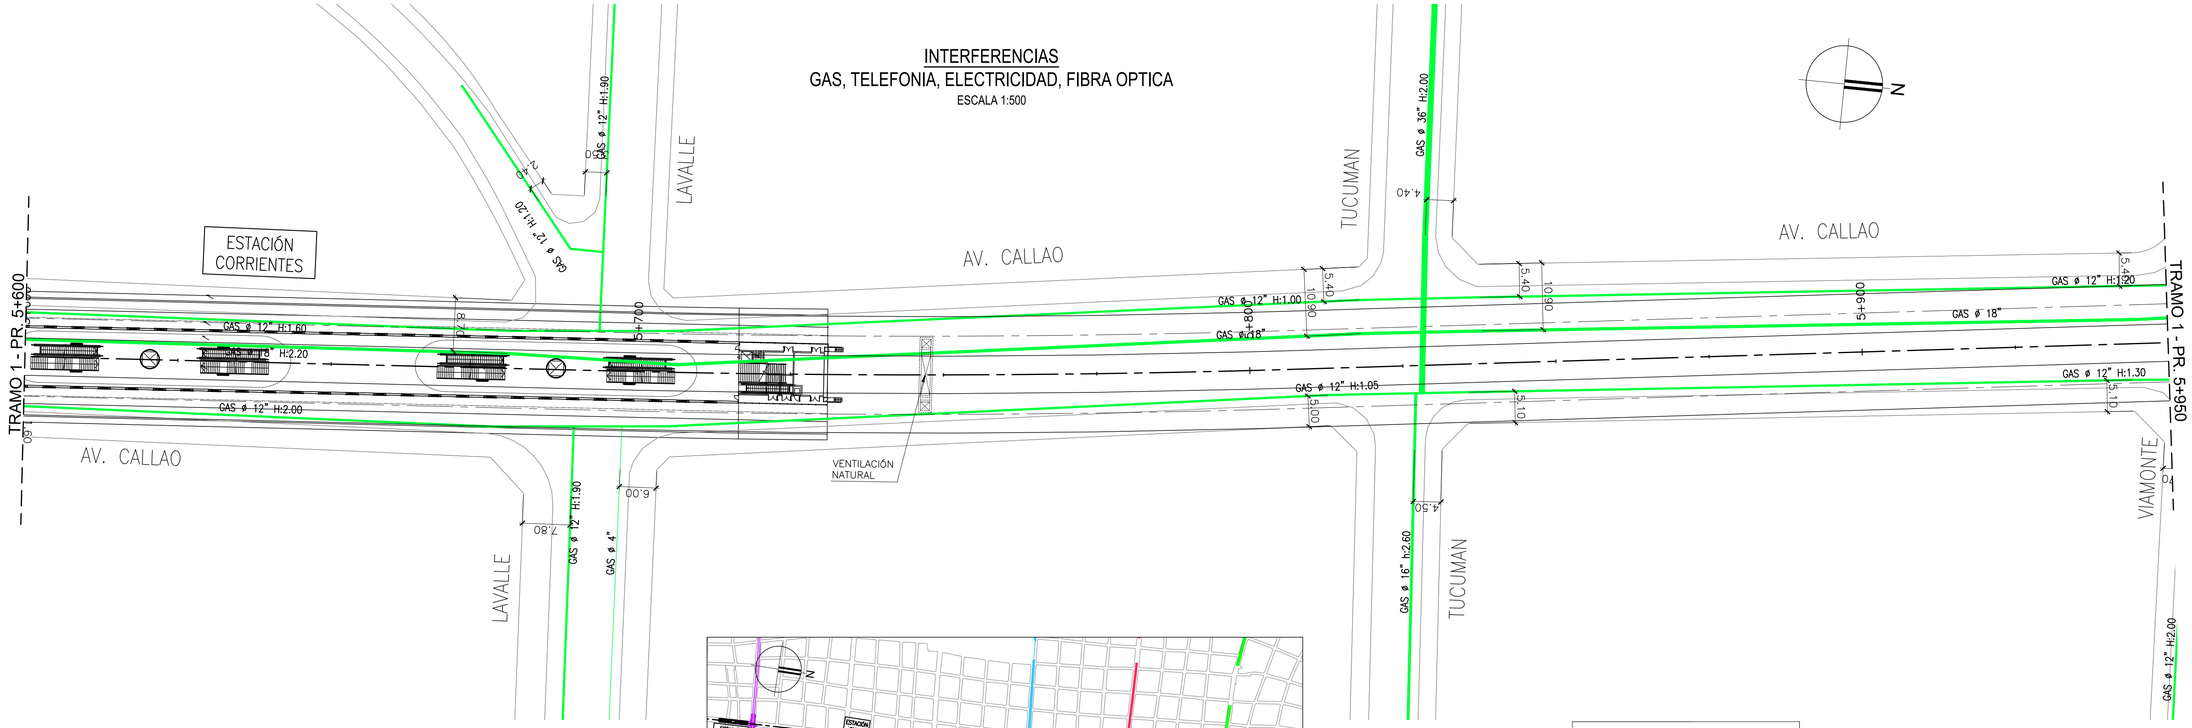

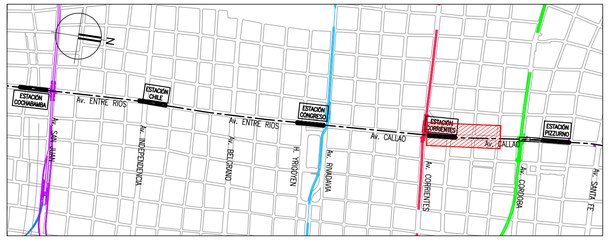

CROQUIS DE UBICACIÓN

REFERENCIAS
- RED CLOACAL
- RED PLUVIAL
- RED AGUA
- RED ELECTRICA
- RED GAS
- RED TELEFONICA
- RED FIBRA OPTICA MULTICANAL

0 10 20 30m
ESCALA 1:500

NOTAS:
EL PRESENTE PLANO ES INDICATIVO. LA CONTRATISTA CONFECCIONARA LOS PLANOS DE DETALLE DEFINITIVO, QUE DEBERAN SER APROBADOS POR LA D.G.O.INF.U Y LA INSPECCION DE OBRA. EL PLANO PRESENTADO POR LA CONTRATISTA ESTARA EN LA TODO DE ACUERDO CON LA NORMATIVA VIGENTE.
TODAS LAS MEDIDAS Y NIVELES SE VERIFICARAN EN OBRA POR EL CONTRATISTA.
TODOS LOS DETALLES CONSTRUCTIVOS SERAN COORDINADOS Y COMPATIBILIZADOS EN OBRA

PLANO NO APTO PARA CONSTRUCCION.

MODIFICACIONES:

REVISION	FECHA	DESCRIPCION
0	18/05/2025	EMISION INICIAL
1	06/05/2026	REVISIÓN DE PROYECTO

MINISTERIO DE INFRAESTRUCTURA
SUBSECRETARIA DE PROYECTOS Y OBRAS
DIRECCION GENERAL DE PROYECTOS

DGPRO

Obra: LÍNEA F				IF-2026-28525919-GCABA-DGPRO	Plano N°
Plano: INTERFERENCIAS TRAMO 1 - PLANIMETRÍA GENERAL - PROG. 5+600 A 5+950				LF-GL-T01-INT-PL-017	017
Fecha: 06/05/2026	Eq. de Proyecto: UPU-ATEC-IATASA	Dibujó: D.B.	Revisó: P.C.	Escala: 1:500	

8/5/2026 14:51 p. m.
LF-GL-T01-INT-PL_001a019_1.dwg

INTERFERENCIAS
SERVICOS CLOACALES, PLUVIALES, AGUA CORRIENTE
ESCALA 1:500

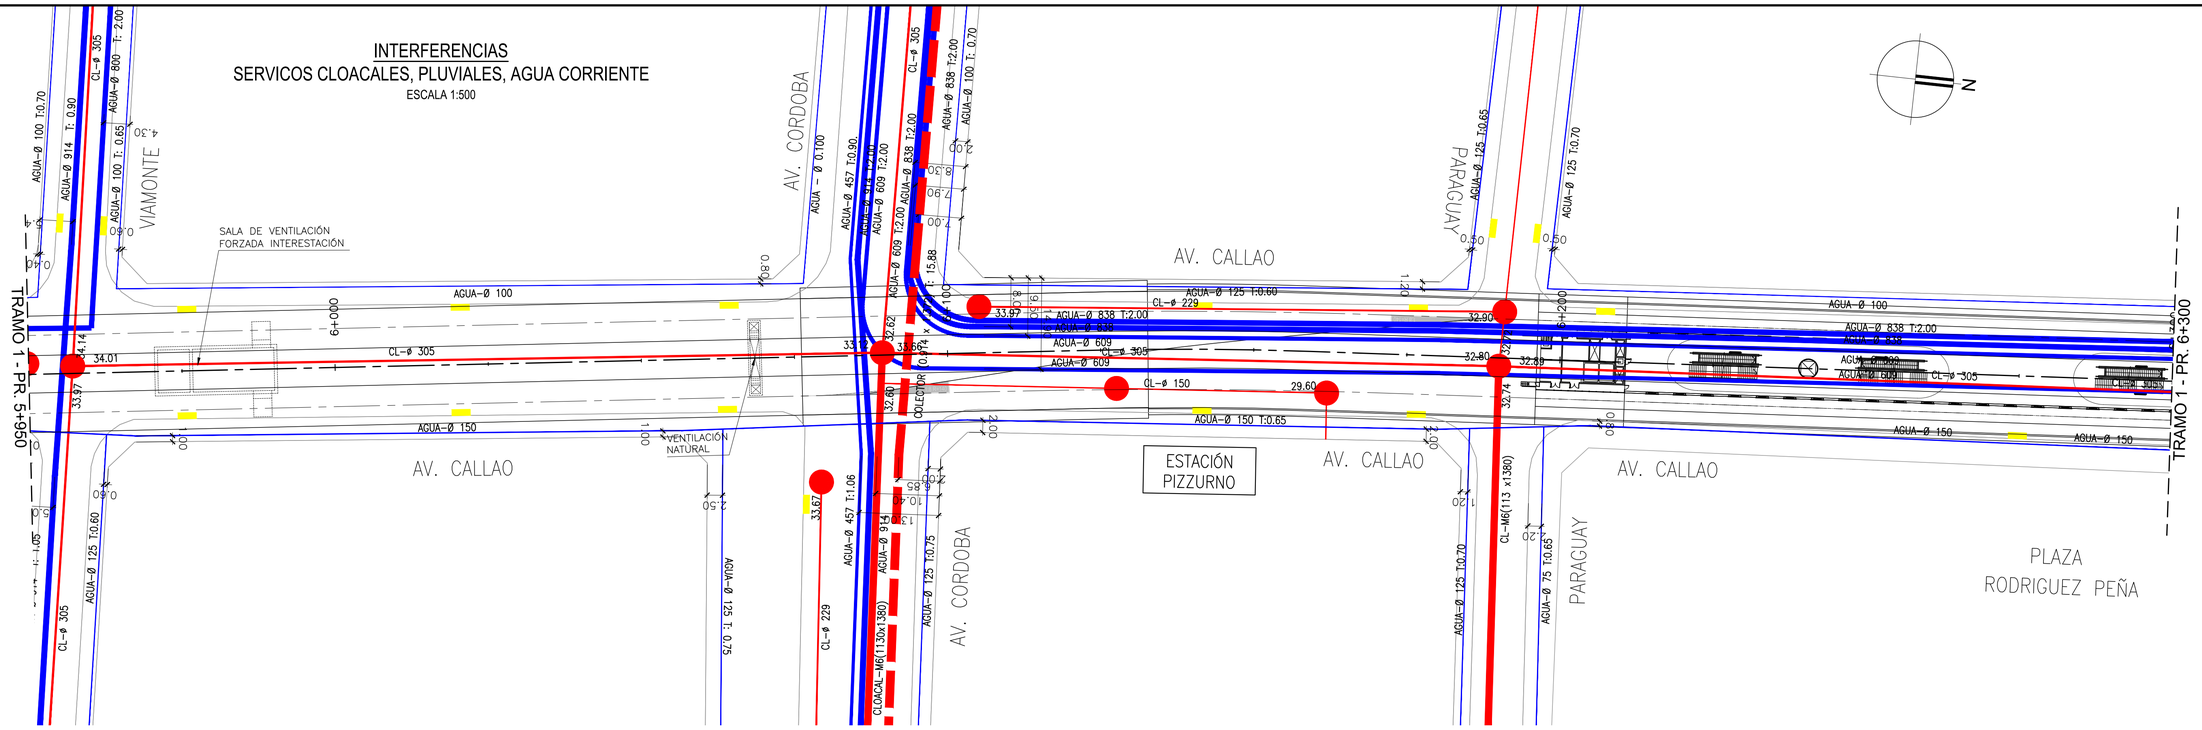

INTERFERENCIAS
GAS, TELEFONIA, ELECTRICIDAD, FIBRA OPTICA
ESCALA 1:500

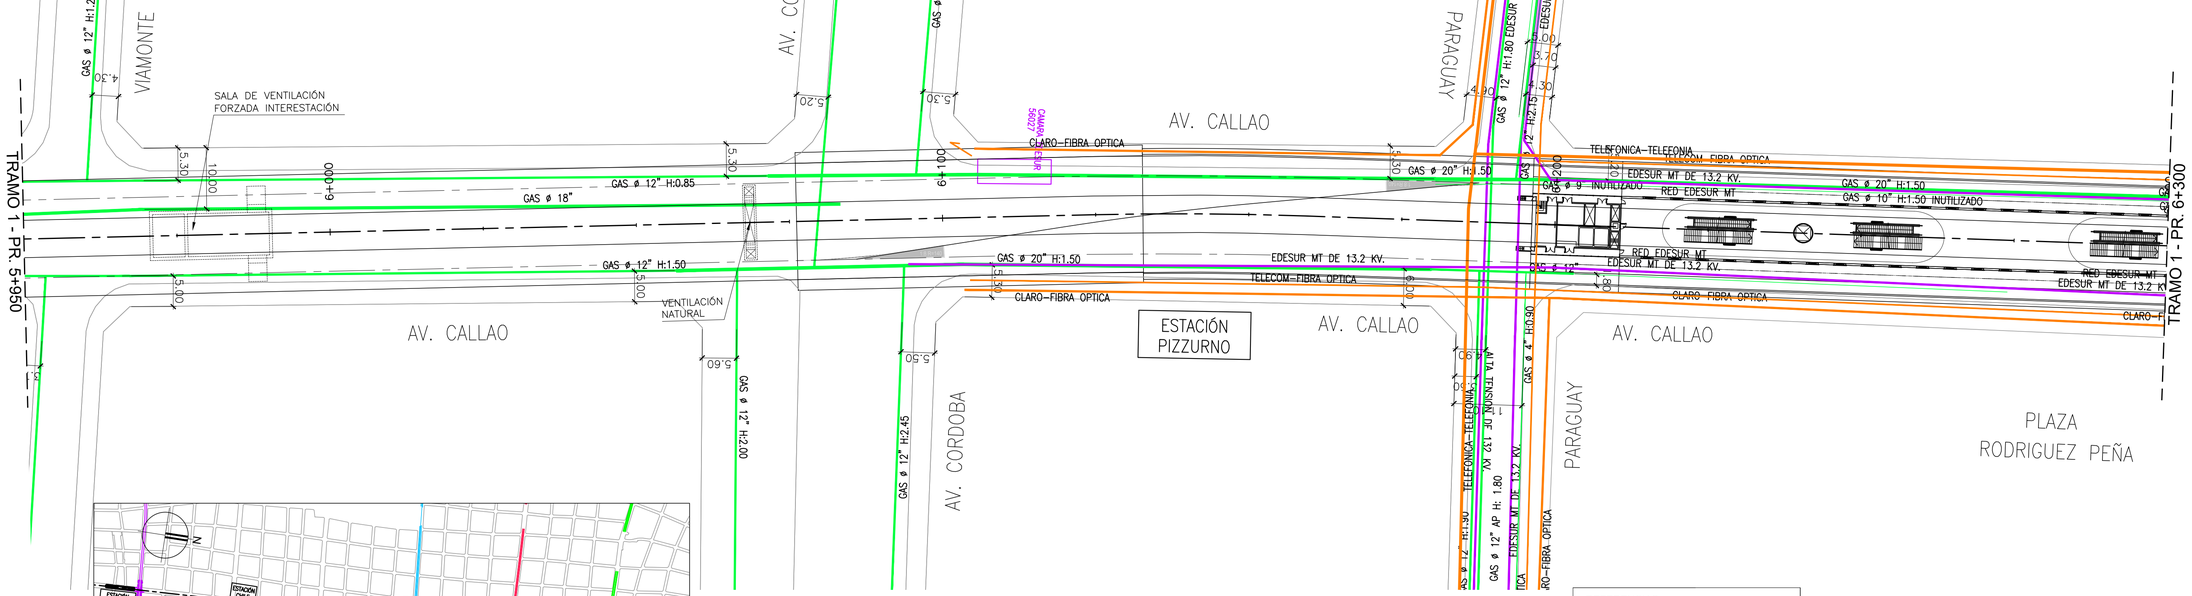

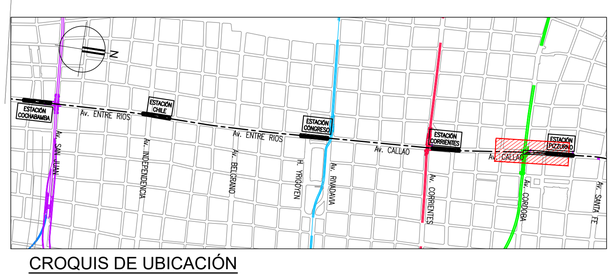

CROQUIS DE UBICACIÓN

REFERENCIAS
- RED CLOACAL
- RED PLUVIAL
- RED AGUA
- RED ELECTRICA
- RED GAS
- RED TELEFONICA
- RED FIBRA OPTICA MULTICANAL

0 10 20 30m
ESCALA 1:500

NOTAS:
1. EL PRESENTE PLANO ES INDICATIVO. LA CONTRATISTA CONFECCIONARA LOS PLANOS DE DETALLE DEFINITIVO, QUE DEBERAN SER APROBADOS POR LA D.G.D.GM.U Y LA INSPECCION DE OBRA. EL PLANO PRESENTADO POR LA CONTRATISTA ESTARA EN UN TODO DE ACUERDO CON LA NORMATIVA VIGENTE.
2. TODAS LAS MEDIDAS Y NIVELES SE VERIFICARAN EN OBRA POR EL CONTRATISTA.
3. TODOS LOS DETALLES CONSTRUCTIVOS SERAN COORDINADOS Y COMPATIBILIZADOS EN OBRA

PLANO NO APTO PARA CONSTRUCCION.

MODIFICACIONES:

REVISION	FECHA	DESCRIPCION
0	19/05/2025	EMISION INICIAL
1	06/05/2026	REVISION DE PROYECTO

Gobierno de la Ciudad de Buenos Aires

MINISTERIO DE INFRAESTRUCTURA
SUBSECRETARIA DE PROYECTOS Y OBRAS
DIRECCION GENERAL DE PROYECTOS

DGPRO

Obra: LÍNEA F					IF-2026-28525919-GCABA-DGPRO
Plano: INTERFERENCIAS TRAMO 1 - PLANIMETRÍA GENERAL - PROG. 5+950 A 6+300					LF-GL-T01-INT-PL-018
Fecha: 06/05/2026	Eq. de Proyecto: UPU-ATEC-IATASA		Dibujó: D.B.	Revisó: P.C.	Escala: 1:500

Plano N° 018

8/5/2026 14:51 p. m.
LF-GL-T01-INT-PL-001ed19_1.dwg

INTERFERENCIAS
SERVICOS CLOACALES, PLUVIALES, AGUA CORRIENTE
ESCALA 1:500

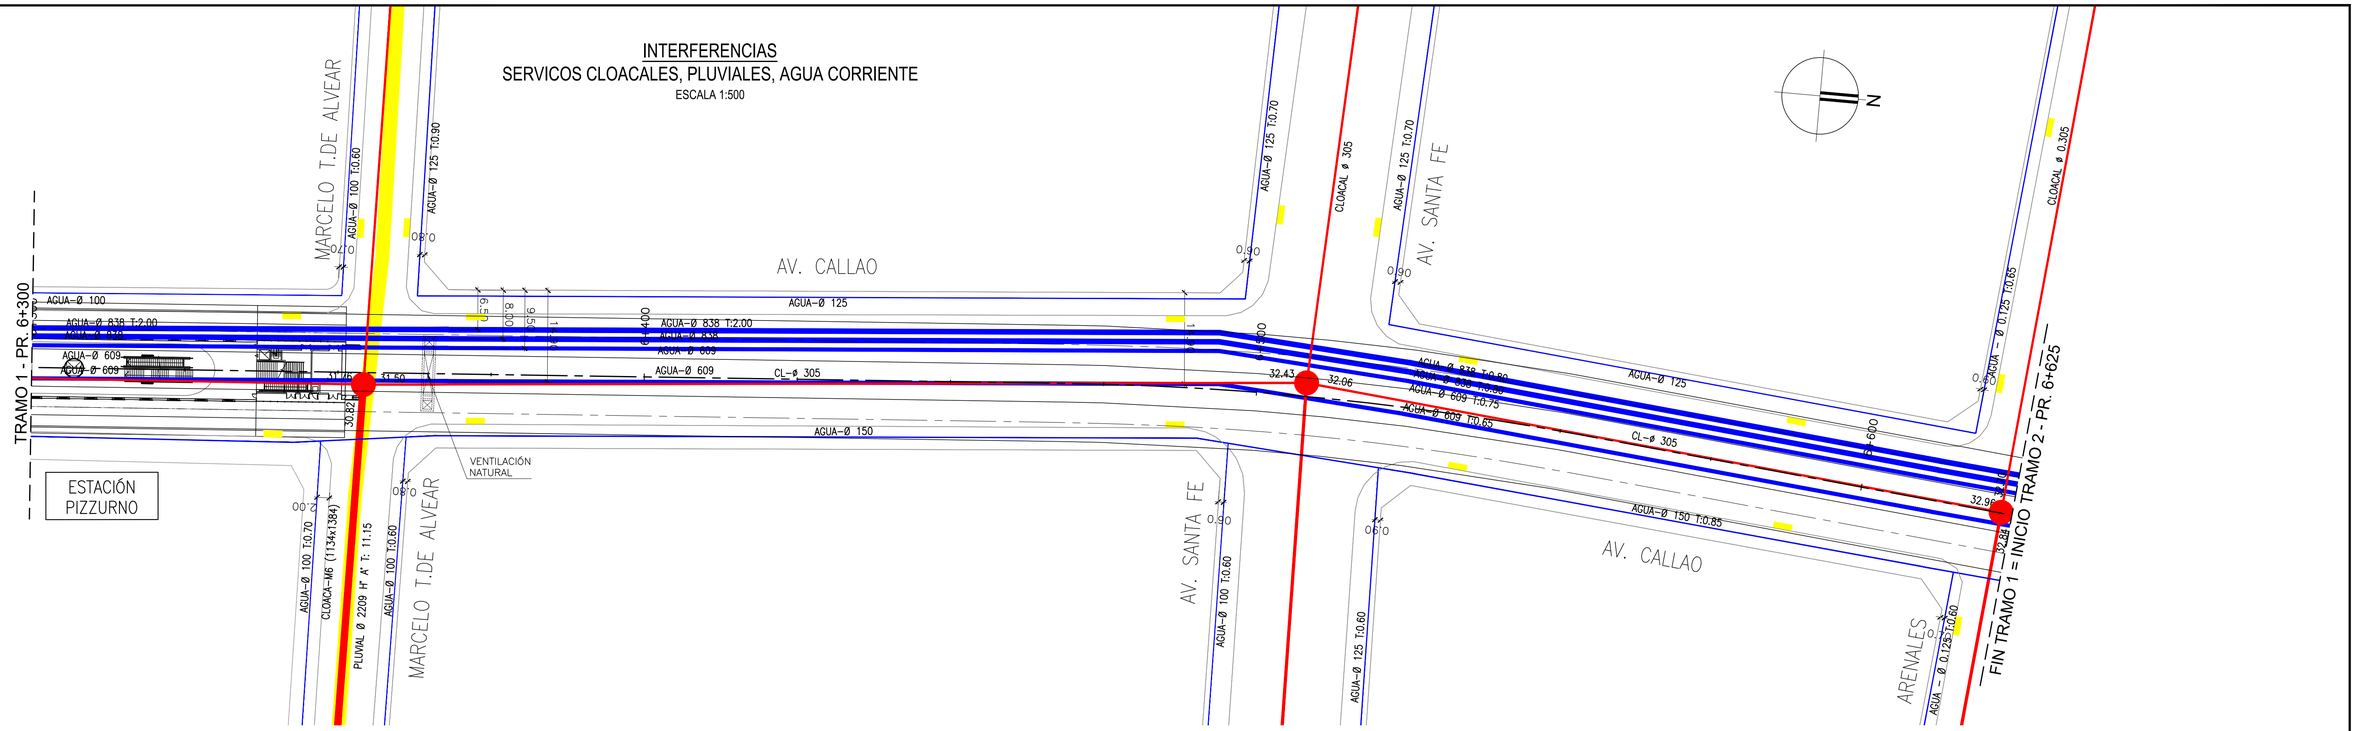

INTERFERENCIAS
GAS, TELEFONIA, ELECTRICIDAD, FIRA OPTICA
ESCALA 1:500

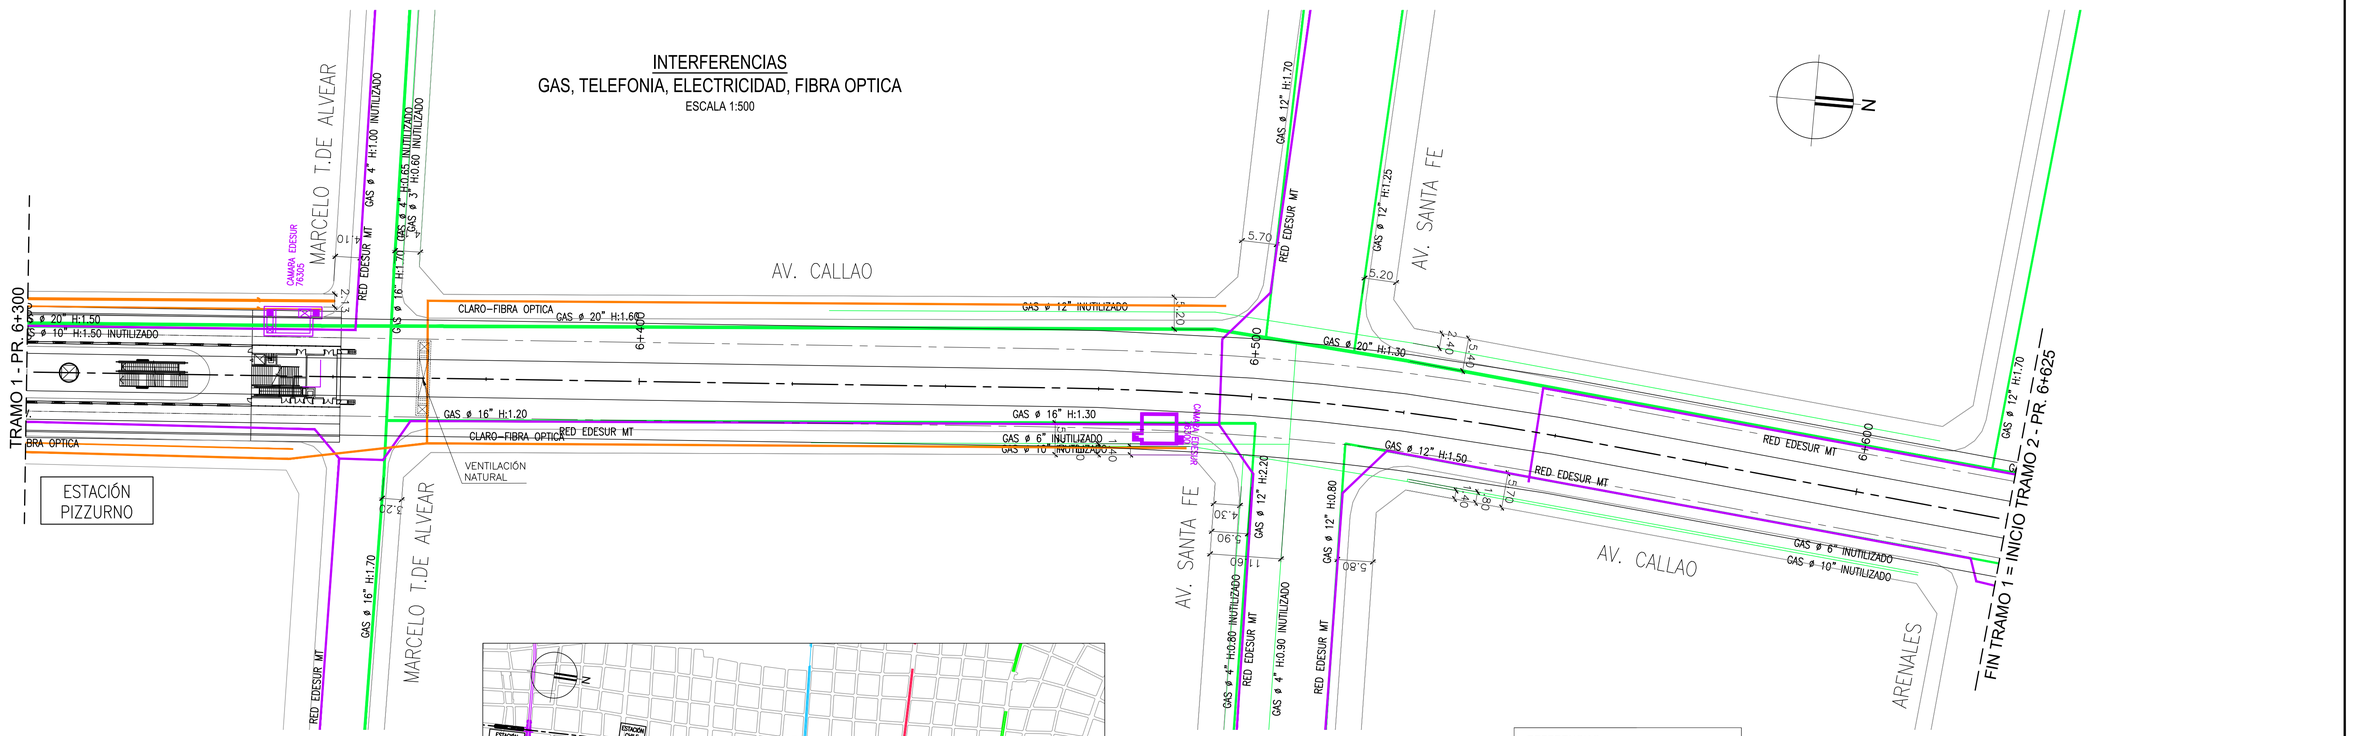

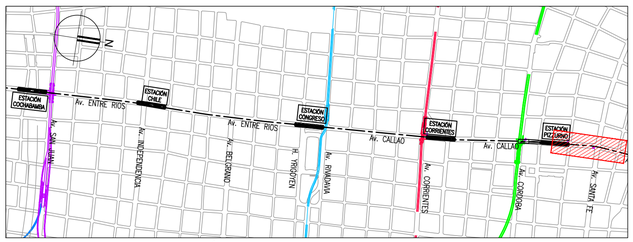

CROQUIS DE UBICACIÓN

REFERENCIAS
- RED CLOACAL
- RED PLUVIAL
- RED AGUA
- RED ELECTRICA
- RED GAS
- RED TELEFONICA
- RED FIBRA OPTICA MULTICANAL

0 10 20 30m
ESCALA 1:500

NOTAS:
1. EL PRESENTE PLANO ES INDICATIVO. LA CONTRATISTA CONFECCIONARA LOS PLANOS DE DETALLE DEFINITIVO, QUE DEBERAN SER APROBADOS POR LA D.G.O.INF.U Y LA INSPECCION DE OBRA. EL PLANO PRESENTADO POR LA CONTRATISTA ESTARA EN UN TODO DE ACUERDO CON LA NORMATIVA VIGENTE.
2. TODAS LAS MEDIDAS Y NIVELES SE VERIFICARAN EN OBRA POR EL CONTRATISTA.
3. TODOS LOS DETALLES CONSTRUCTIVOS SERAN COORDINADOS Y COMPATIBILIZADOS EN OBRA

PLANO NO APTO PARA CONSTRUCCION.

MODIFICACIONES:

REVISION	FECHA	DESCRIPCION
0	19/05/2025	EMISION INICIAL
1	06/05/2026	REVISION DE PROYECTO

Gobierno de la Ciudad de Buenos Aires

MINISTERIO DE INFRAESTRUCTURA
SUBSECRETARIA DE PROYECTOS Y OBRAS
DIRECCION GENERAL DE PROYECTOS

DGPRO

Obra: LÍNEA F					IF-2026-28525919-GCABA-DGPRO
Plano: INTERFERENCIAS TRAMO 1 - PLANIMETRÍA GENERAL - PROG. 6+300 A 6+625					LF-GL-T01-INT-PL-019
Fecha: 06/05/2026	Eq. de Proyecto: UPU-ATEC-IATASA	Dibujó: D.B.	Revisó: P.C.	Escala: 1:500	Plano N° 019

8/5/2026 14:51 p. m.
LF-GL-T01-INT-PL-001e019_1.dwg

INTERFERENCIAS
SERVICIOS CLOACALES, PLUVIALES, AGUA CORRIENTE
ESCALA 1:500

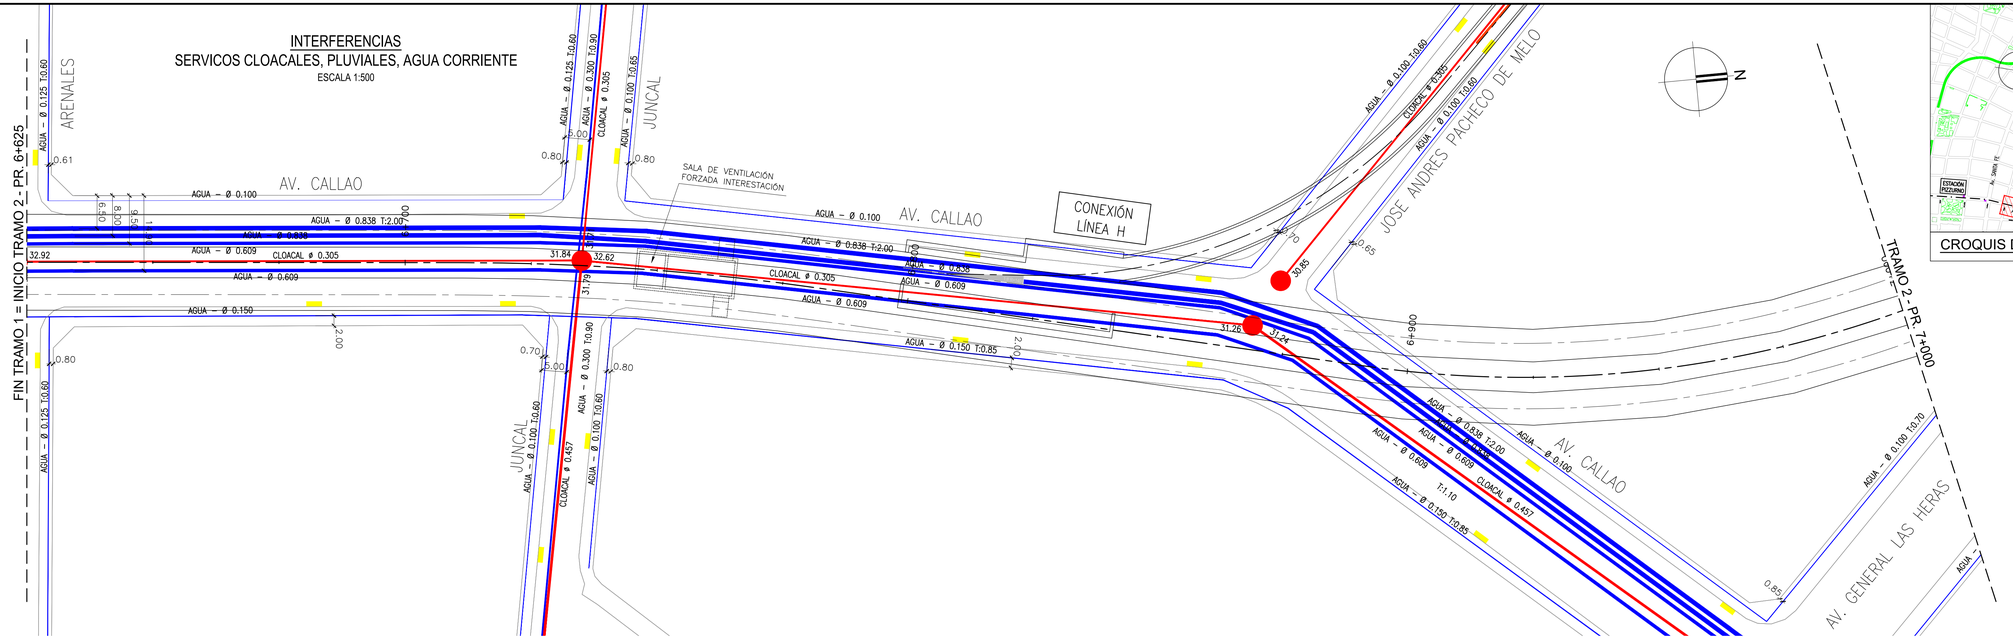

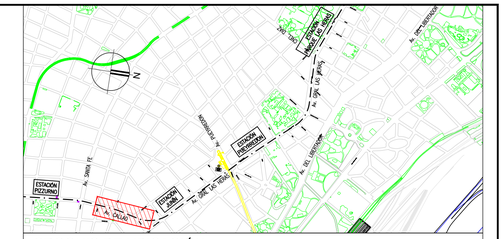

CROQUIS DE UBICACIÓN

INTERFERENCIAS
GAS, TELEFONIA, ELECTRICIDAD, FIBRA OPTICA
ESCALA 1:500

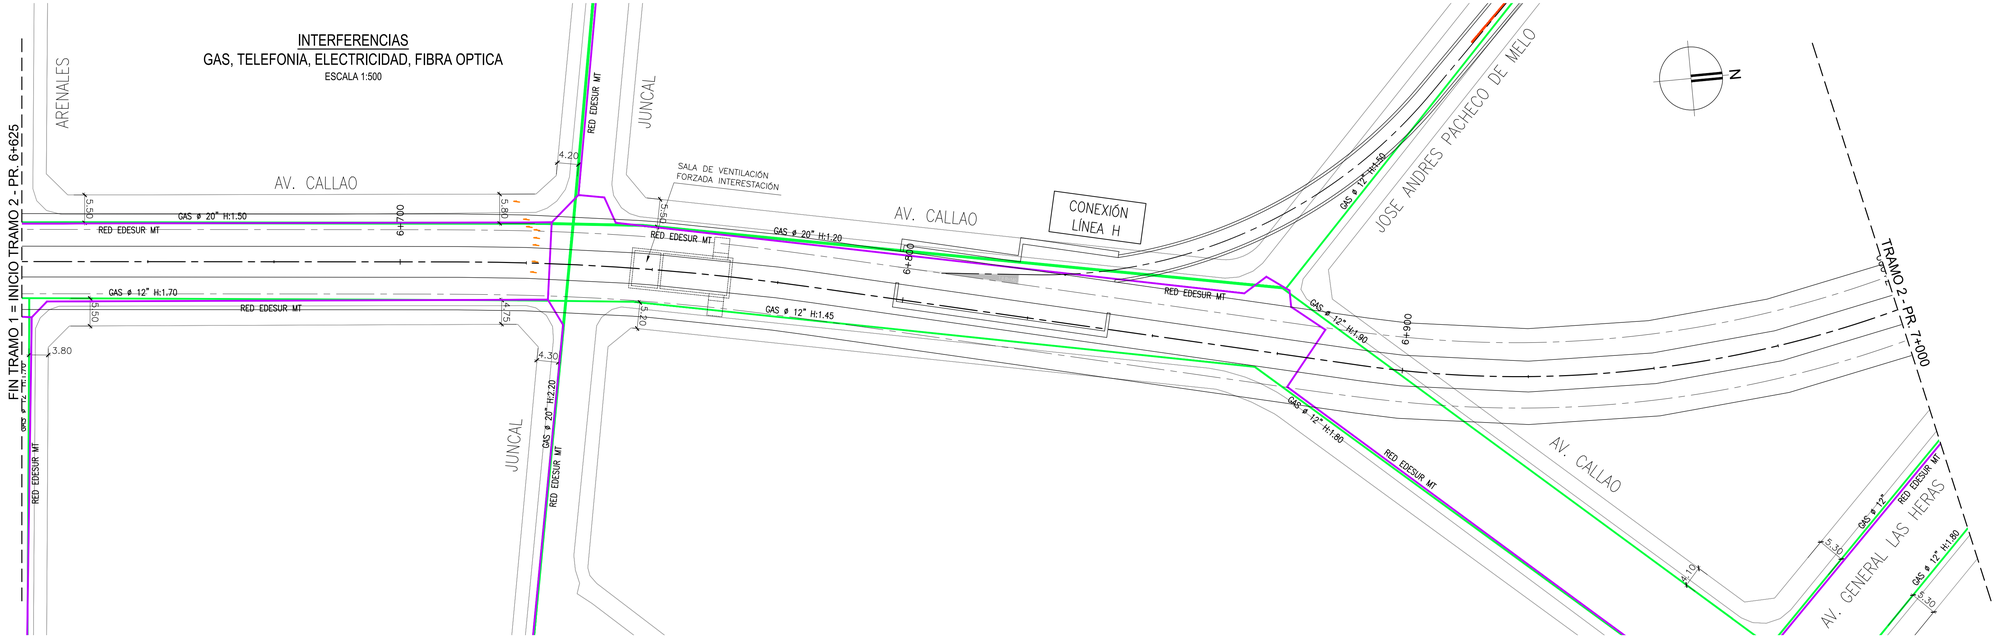

REFERENCIAS:
- RED CLOACAL
- RED PLUVIAL
- RED AGUA
- RED ELECTRICA
- RED GAS
- RED TELEFONICA
- RED FIBRA OPTICA MULTICANAL

NOTAS:
1- SISTEMA DE COORDENADAS DE LA CIUDAD DE BUENOS AIRES.
2- TODAS LAS MEDIDAS ESTÁN EXPRESADAS EN METROS, SALVO INDICACIÓN CONTRARIA

0 10 20 30m
ESCALA 1:500

NOTAS: EL PRESENTE PLANO ES INDICATIVO. LA CONTRATISTA CONFECCIONARA LOS PLANOS DE DETALLE DEFINITIVO QUE DEBERAN SER APROBADOS POR LA D.G.C.SIP.Q.Y LA INSPECCION DE OBRA. EL PLANO PRESENTADO POR LA CONTRATISTA DEBERA EN UN TODO DE ACUERDO CON LA NORMATIVA VIGENTE. TODAS LAS MEDIDAS Y NIVELES SE VERIFICARAN EN OBRA POR EL CONTRATISTA. TODOS LOS DETALLES CONSTRUCTIVOS SERAN COORDINADOS Y COMPATIBILIZADOS EN OBRA

PLANO NO APTO PARA CONSTRUCCION.

MODIFICACIONES:

REVISIÓN	FECHA	DESCRIPCIÓN
0	19/09/2025	EMISIÓN INICIAL
1	11/12/2025	AJUSTE DE PROYECTO
2	26/03/2026	AJUSTE DE PROYECTO

Gobierno de la Ciudad de Buenos Aires

MINISTERIO DE INFRAESTRUCTURA
SUBSECRETARIA DE PROYECTOS Y OBRAS
DIRECCION GENERAL DE PROYECTOS

DGPRO

Obra: LÍNEA F					IF-2026-28525919-GCABA-DGPRO
Plano: TRAZADO DE TÚNEL - INTERFERENCIAS - PROG. 6+625 A 7+000					LF-GL-T02-INT-PL-001
Fecha: 06/05/2026	Eq. de Proyecto: UPU-ATEC-IATASA	Dibujó: D.B.	Revisó: P.C.	Escala: 1:500	Plano N° 001

8/5/2026 11:03 a. m.
LF-GL-T02-INT-PL-001(12_2).dwg

INTERFERENCIAS
SERVICOS CLOACALES, PLUVIALES, AGUA CORRIENTE
ESCALA 1:500

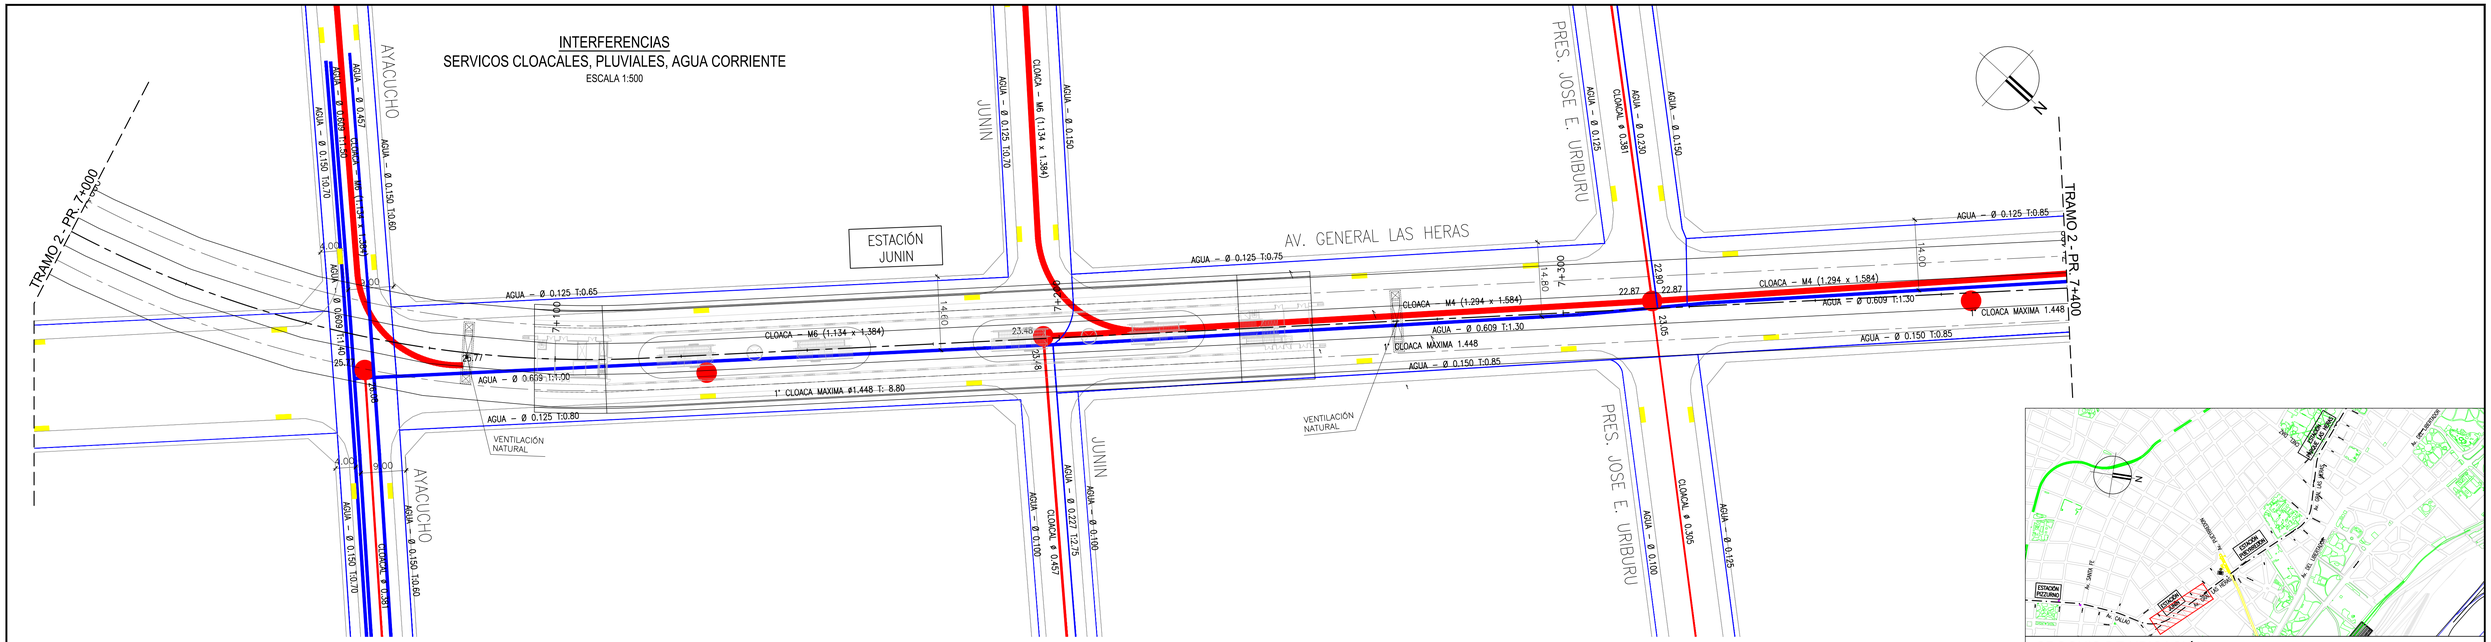

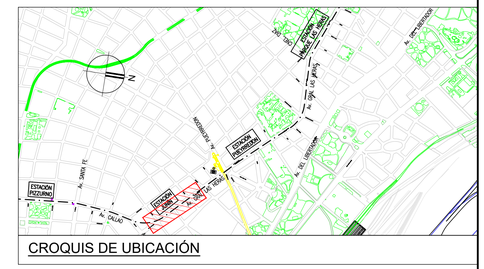
ESTACIÓN RETIRO
ESTACIÓN JUNIN
ESTACIÓN RETIRO
AV. GENERAL LAS HERAS
AV. DEL LIBERTADOR
AV. RAMOS MEJIA
AV. ORAN
AV. ALVEAR
AV. PRES. JOSE E. URIBURU
AV. DE MAYO
AV. CORRIENTES
AV. SANTA FE
AV. CORDOBA
AV. CALLAO
AV. PUEYRREDON
AV. 9 DE JULIO
AV. LEANDRO N. ALEM
AV. E. MADERO
AV. PTE. R. SAENZ PEÑA
AV. PTE. HIPOLITO YRIGOYEN
AV. PTE. JUAN D. PERON

INTERFERENCIAS
SERVICOS CLOACALES, PLUVIALES, AGUA CORRIENTE
ESCALA 1:500

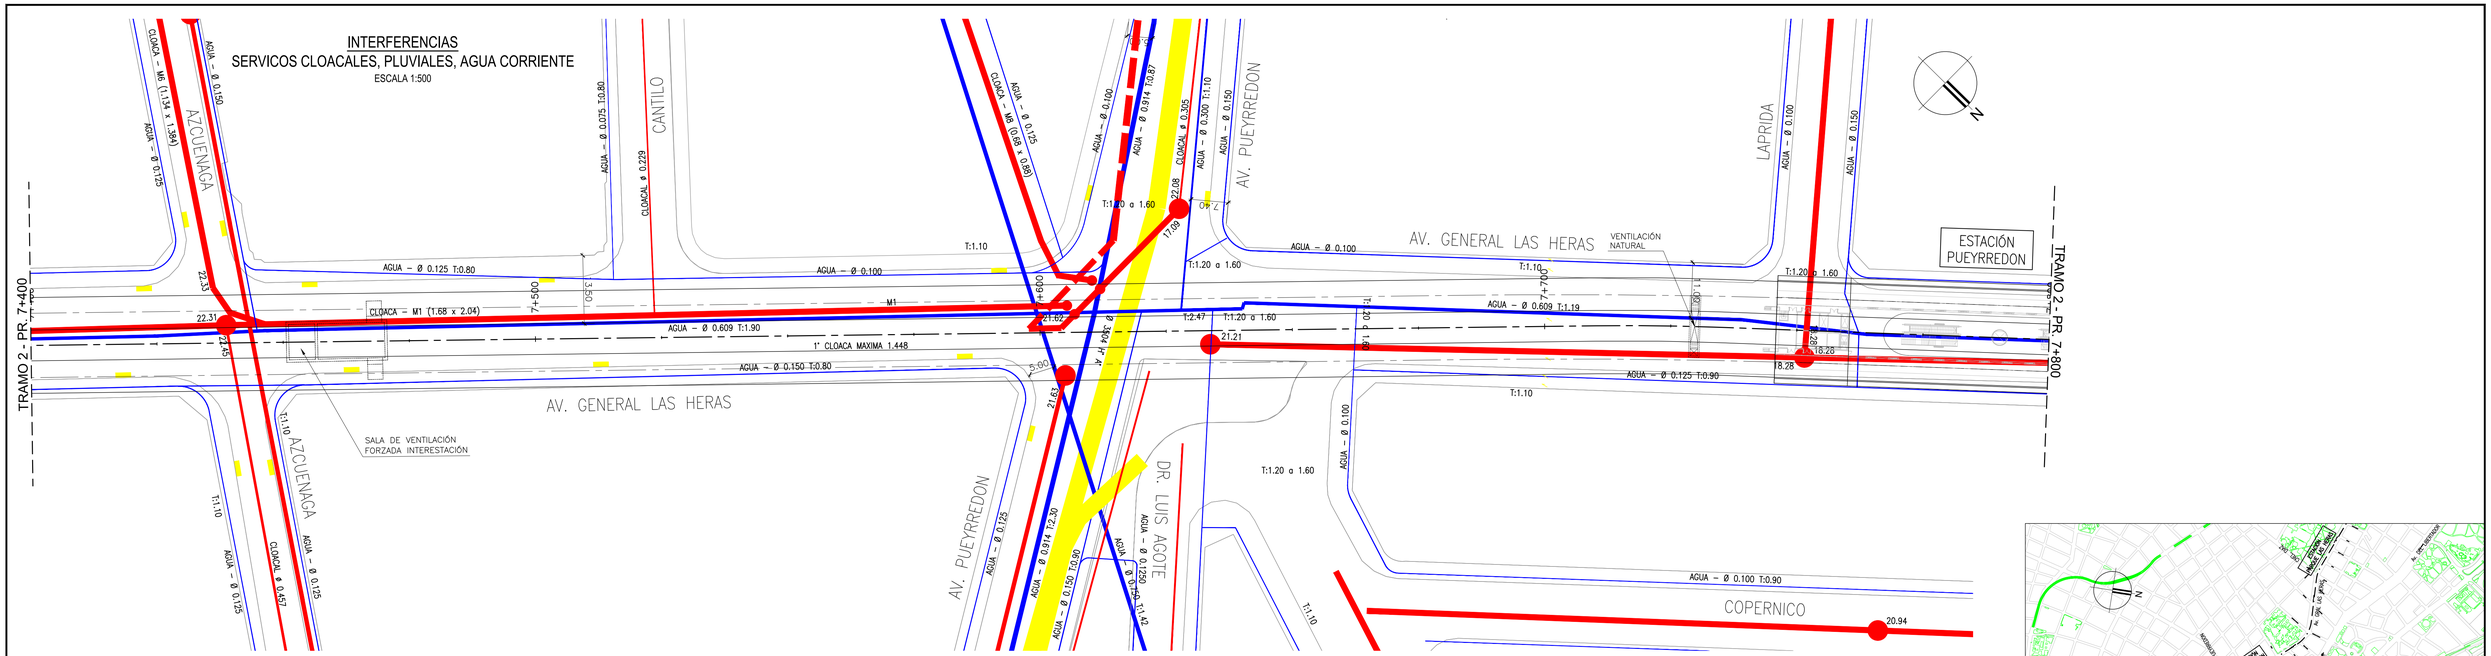

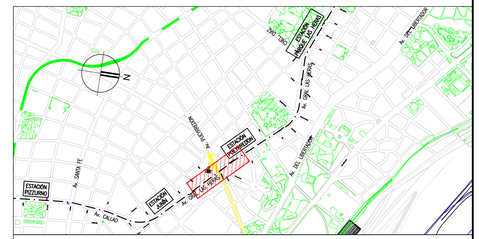

INTERFERENCIAS
GAS, TELEFONIA, ELECTRICIDAD, FIBRA OPTICA
ESCALA 1:500

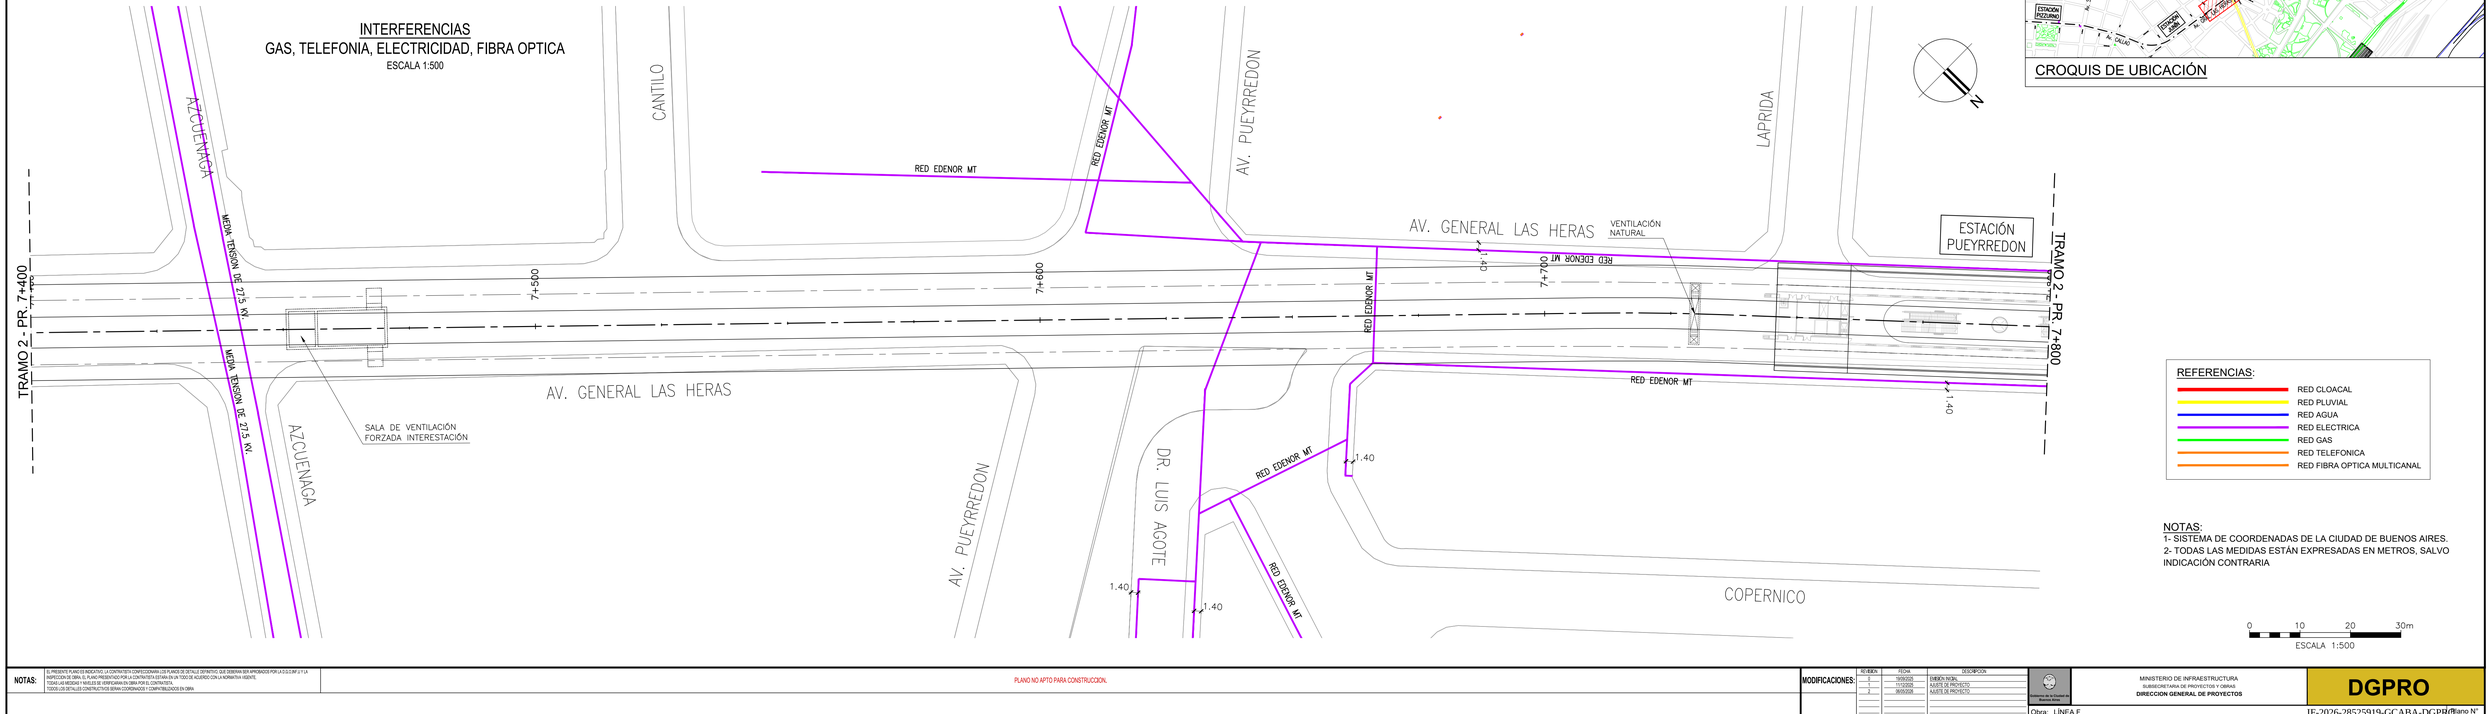

REFERENCIAS:
- RED CLOACAL
- RED PLUVIAL
- RED AGUA
- RED ELECTRICA
- RED GAS
- RED TELEFONICA
- RED FIBRA OPTICA MULTICANAL

NOTAS:
1- SISTEMA DE COORDENADAS DE LA CIUDAD DE BUENOS AIRES.
2- TODAS LAS MEDIDAS ESTÁN EXPRESADAS EN METROS, SALVO INDICACIÓN CONTRARIA

0 10 20 30m
ESCALA 1:500

NOTAS:
EL PRESENTE PLANO ES INDICATIVO. LA CONTRATISTA CONFECCIONARA LOS PLANOS DE DETALLE DEFINITIVO, QUE DEBERAN SER APROBADOS POR LA D.G.EMP. U OTRA INSPECCION DE OBRA, EL PLANO PRESENTADO POR LA CONTRATISTA ESTARA EN UN TODO DE ACUERDO CON LA NORMATIVA VIGENTE.
TODAS LAS MEDIDAS Y NIVELES SE VERIFICARAN EN OBRA POR EL CONTRATISTA.
TODOS LOS DETALLES CONSTRUCTIVOS SERAN CORROBORADOS Y CONFIRMADOS EN OBRA.

PLANO NO APTO PARA CONSTRUCCION.

MODIFICACIONES:

REVISIÓN	FECHA	DESCRIPCIÓN
0	19/09/2025	EMISIÓN INICIAL
1	11/12/2025	AJUSTE DE PROYECTO
2	30/05/2026	AJUSTE DE PROYECTO

Gobierno de la Ciudad de Buenos Aires

MINISTERIO DE INFRAESTRUCTURA
SUBSECRETARIA DE PROYECTOS Y OBRAS
DIRECCION GENERAL DE PROYECTOS

DGPRO

Obra: LINEA F		IF-2026-28525919-GCABA-DGPRO
Plano: TRAZADO DE TÚNEL - INTERFERENCIAS - PROG. 7+400 A 7+800		LF-GL-T02-INT-PL-003
Fecha: 06/05/2026	Eq. de Proyecto: UPU-ATEC-IATASA Dibujó: D.B.	Revisó: P.C. Escala: 1:500

Plano N° 003

8/5/2026 11:03 a. m.
LF-GL-T02-INT-PL-003 R0 2_2.dwg

INTERFERENCIAS
SERVICOS CLOACALES, PLUVIALES, AGUA CORRIENTE
ESCALA 1:500

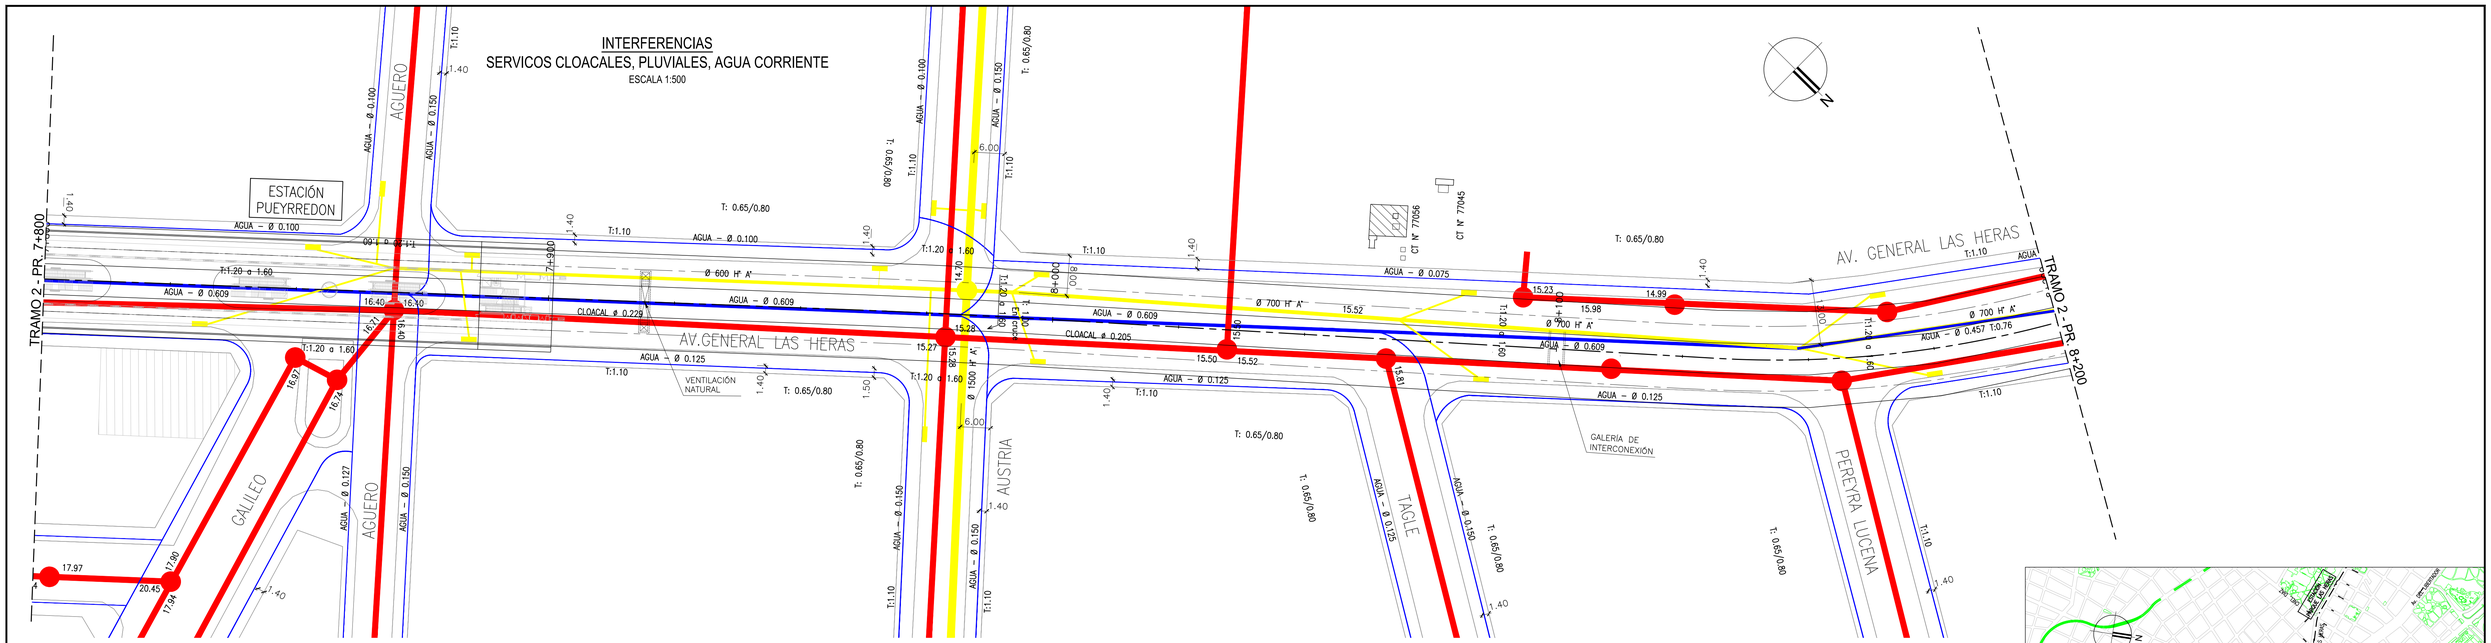

INTERFERENCIAS
GAS, TELEFONIA, ELECTRICIDAD, FIBRA OPTICA
ESCALA 1:500

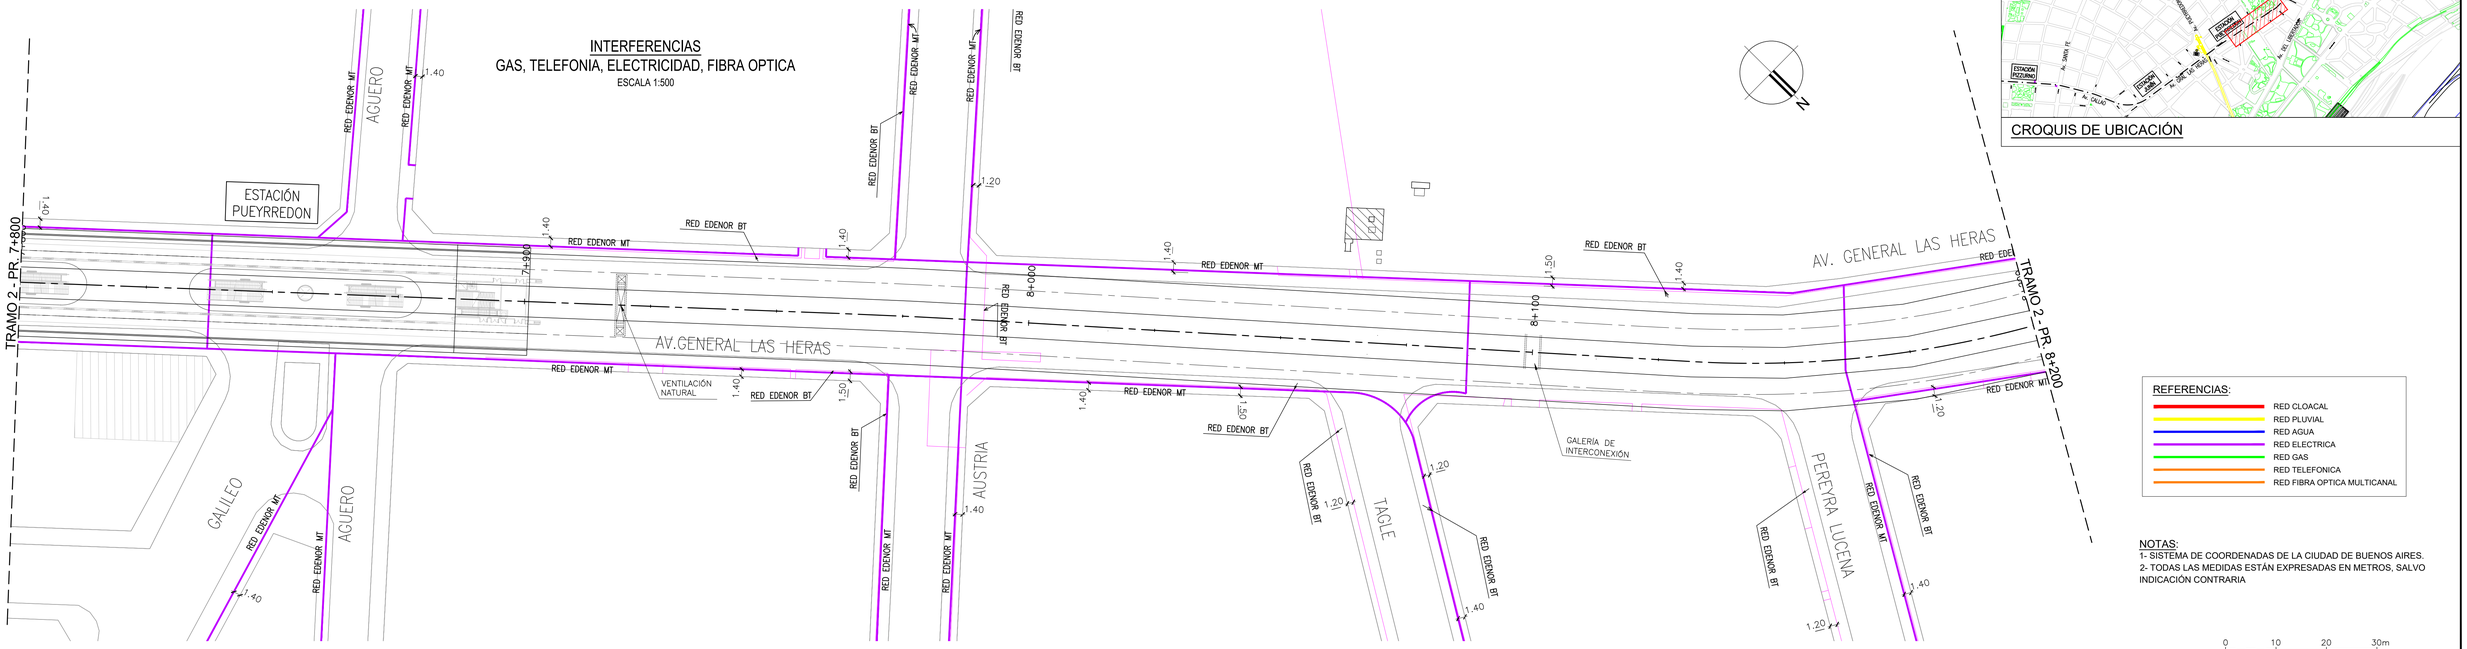

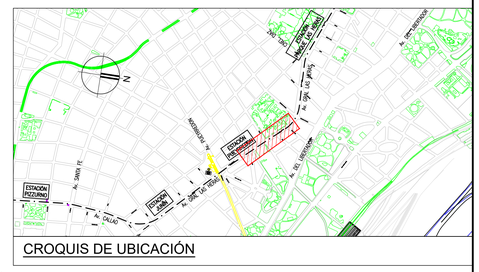

CROQUIS DE UBICACIÓN

REFERENCIAS:
- RED CLOACAL
- RED PLUVIAL
- RED AGUA
- RED ELECTRICA
- RED GAS
- RED TELEFONICA
- RED FIBRA OPTICA MULTICANAL

NOTAS:
1- SISTEMA DE COORDENADAS DE LA CIUDAD DE BUENOS AIRES.
2- TODAS LAS MEDIDAS ESTÁN EXPRESADAS EN METROS, SALVO INDICACIÓN CONTRARIA

0 10 20 30m
ESCALA 1:500

NOTAS:
EL PRESENTE PLANO ES INDICATIVO. LA CONTRATISTA CONFECCIONARA LOS PLANOS DE DETALLE DEFINITIVO, QUE DEBERAN SER APROBADOS POR LA D.G.O.SM° Y LA INSPECCION DE OBRA, EL PLANO PRESENTADO POR LA CONTRATISTA ESTARA EN UN TODO DE ACUERDO CON LA NORMATIVA VIGENTE.
TODAS LAS MEDIDAS Y NIVELES DE REFERENCIAS EN OBRA POR EL CONTRATISTA.
TODOS LOS DETALLES CONSTRUCTIVOS SERAN COORDINADOS Y CONFIRMTALIZADOS EN OBRA

PLANO NO APTO PARA CONSTRUCCION.

MODIFICACIONES:

N°/HOJA	FECHA	DESCRIPCION
0	19/09/2025	EMISION INICIAL
1	11/12/2025	AJUSTE DE PROYECTO
2	06/05/2026	AJUSTE DE PROYECTO

MINISTERIO DE INFRAESTRUCTURA
SUBSECRETARIA DE PROYECTOS Y OBRAS
DIRECCION GENERAL DE PROYECTOS

DGPRO

Obra: LINEA F
IF-2026-28525919-GCABA-DGPRO
Plano: TRAZADO DE TÚNEL - INTERFERENCIAS - PROG. 7+800 A 8+200
LF-GL-T02-INT-PL-004
Fecha: 06/05/2026 | Eq. de Proyecto: UPU-ATEC-IATASA | Dibujó: D.B. | Revisó: P.C. | Escala: 1:500
Plano N° 004

8/5/2026, 11:03 a. m.
LF-GL-T02-INT-PL-001of12_2.dwg

INTERFERENCIAS
SERVICOS CLOACALES, PLUVIALES, AGUA CORRIENTE
ESCALA 1:500

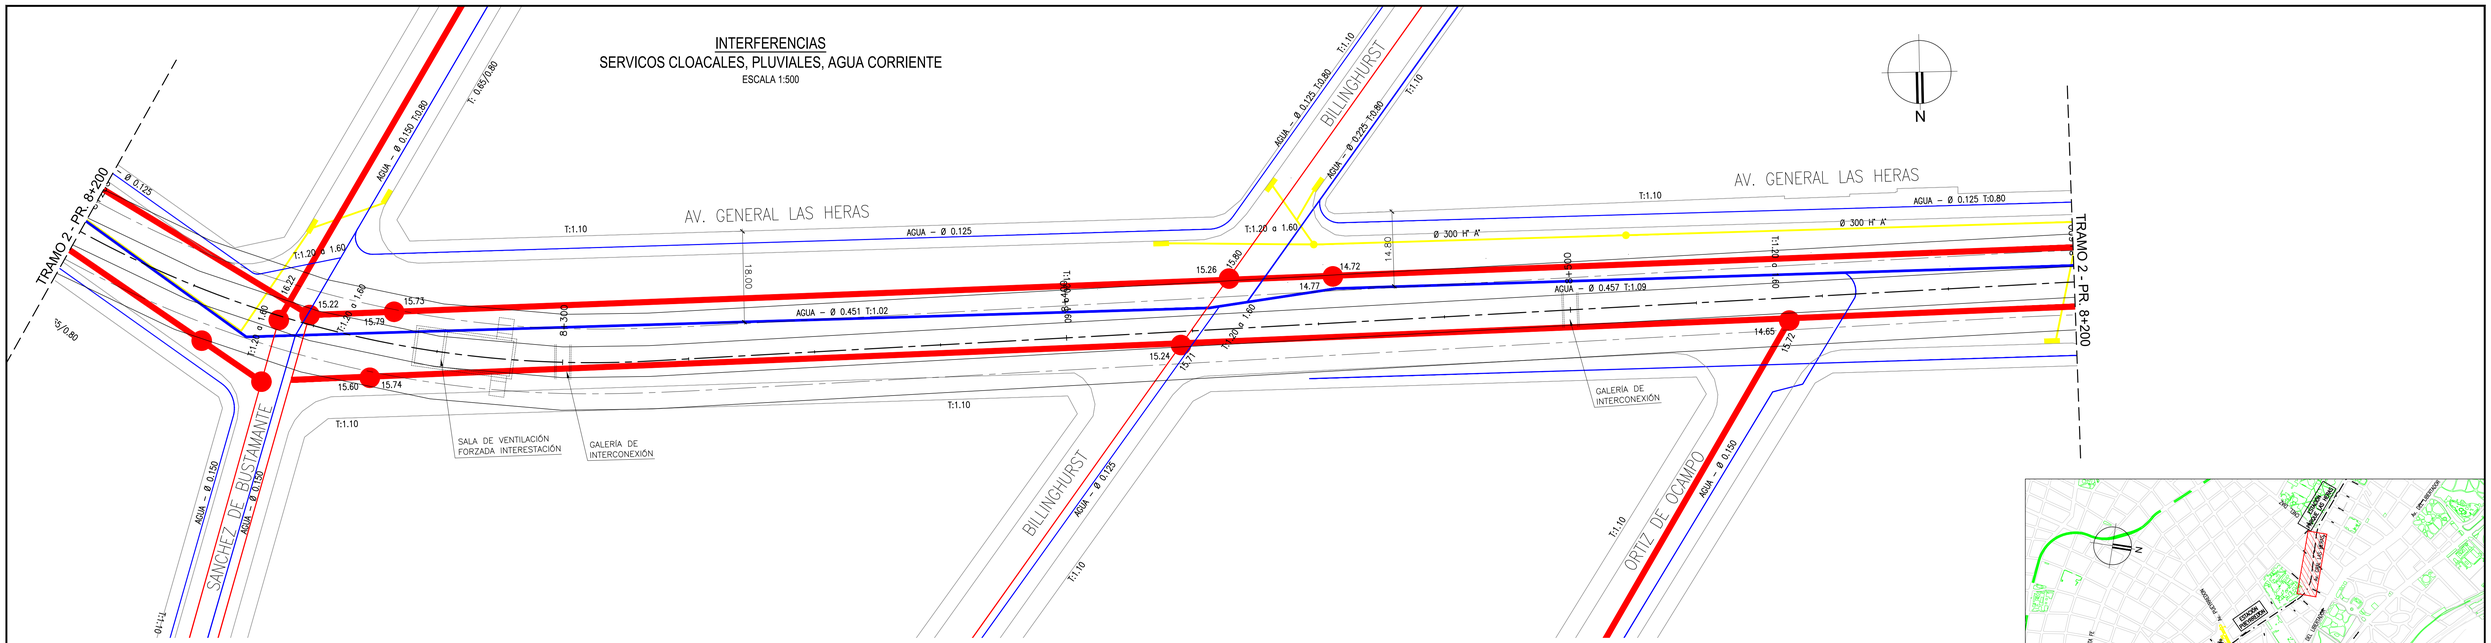

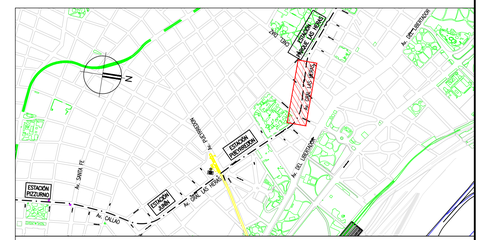

CROQUIS DE UBICACIÓN

INTERFERENCIAS
GAS, TELEFONIA, ELECTRICIDAD, FIBRA OPTICA
ESCALA 1:500

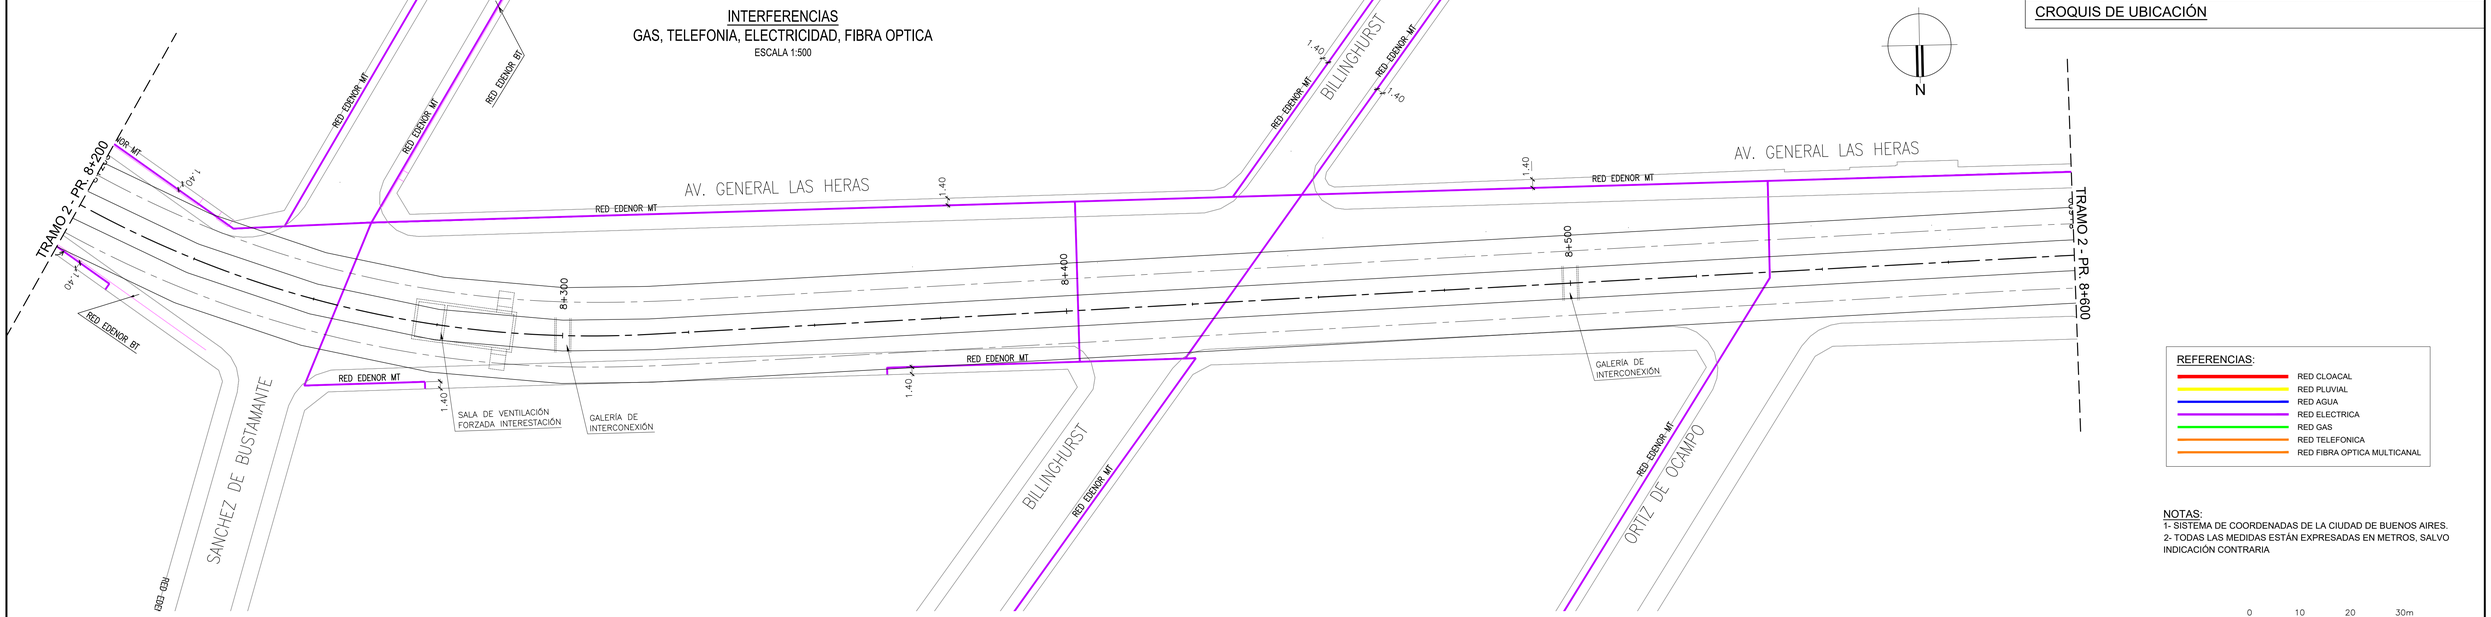

REFERENCIAS:
- RED CLOACAL
- RED PLUVIAL
- RED AGUA
- RED ELECTRICA
- RED GAS
- RED TELEFONICA
- RED FIBRA OPTICA MULTICANAL

NOTAS:
1- SISTEMA DE COORDENADAS DE LA CIUDAD DE BUENOS AIRES.
2- TODAS LAS MEDIDAS ESTÁN EXPRESADAS EN METROS, SALVO INDICACIÓN CONTRARIA

0 10 20 30m
ESCALA 1:500

NOTAS: EL PRESENTE PLANO ES INDICATIVO. LA CONTRATISTA CONFECCIONARA LOS PLANOS DE DETALLE CONSTRUCTIVO, QUE DEBERAN SER APROBADOS POR LA D.G.DAT.U Y LA INSPECCION DE OBRA, EL PLANO PRESENTADO POR LA CONTRATISTA ESTARA EN ALTOS DE ACUERDO CON LA NORMATIVA VIGENTE.
TODAS LAS MEDIDAS Y NIVELES SE VERIFICARAN EN OBRA POR EL CONTRATISTA.
TODOS LOS DETALLES CONSTRUCTIVOS SERAN COORDINADOS Y COMPATIBILIZADOS EN OBRA

PLANO NO APTO PARA CONSTRUCCION.

MODIFICACIONES:

REVISION	FECHA	DESCRIPCION
0	10/05/2023	EMISION INICIAL
1	11/12/2025	AJUSTE DE PROYECTO
2	26/05/2026	AJUSTE DE PROYECTO

MINISTERIO DE INFRAESTRUCTURA
SUBSECRETARIA DE PROYECTOS Y OBRAS
DIRECCION GENERAL DE PROYECTOS

DGPRO

Obra: LÍNEA F			IF-2026-28525919-GCABA-DGPRO Plano N°
Plano: TRAZADO DE TÚNEL - INTERFERENCIAS - PROG. 8+200 A 8+600			LF-GL-T02-INT-PL-005
Fecha: 06/05/2026	Eq. de Proyecto: UPU-ATEC-IATASA	Dibujó: D.B.	Revisó: P.C. Escala: 1:500

005

8/5/2026 11:03 a. m.
LF-GL-T02-INT-PL-005R02_2.dwg

INTERFERENCIAS
SERVICOS CLOACALES, PLUVIALES, AGUA CORRIENTE
ESCALA 1:500

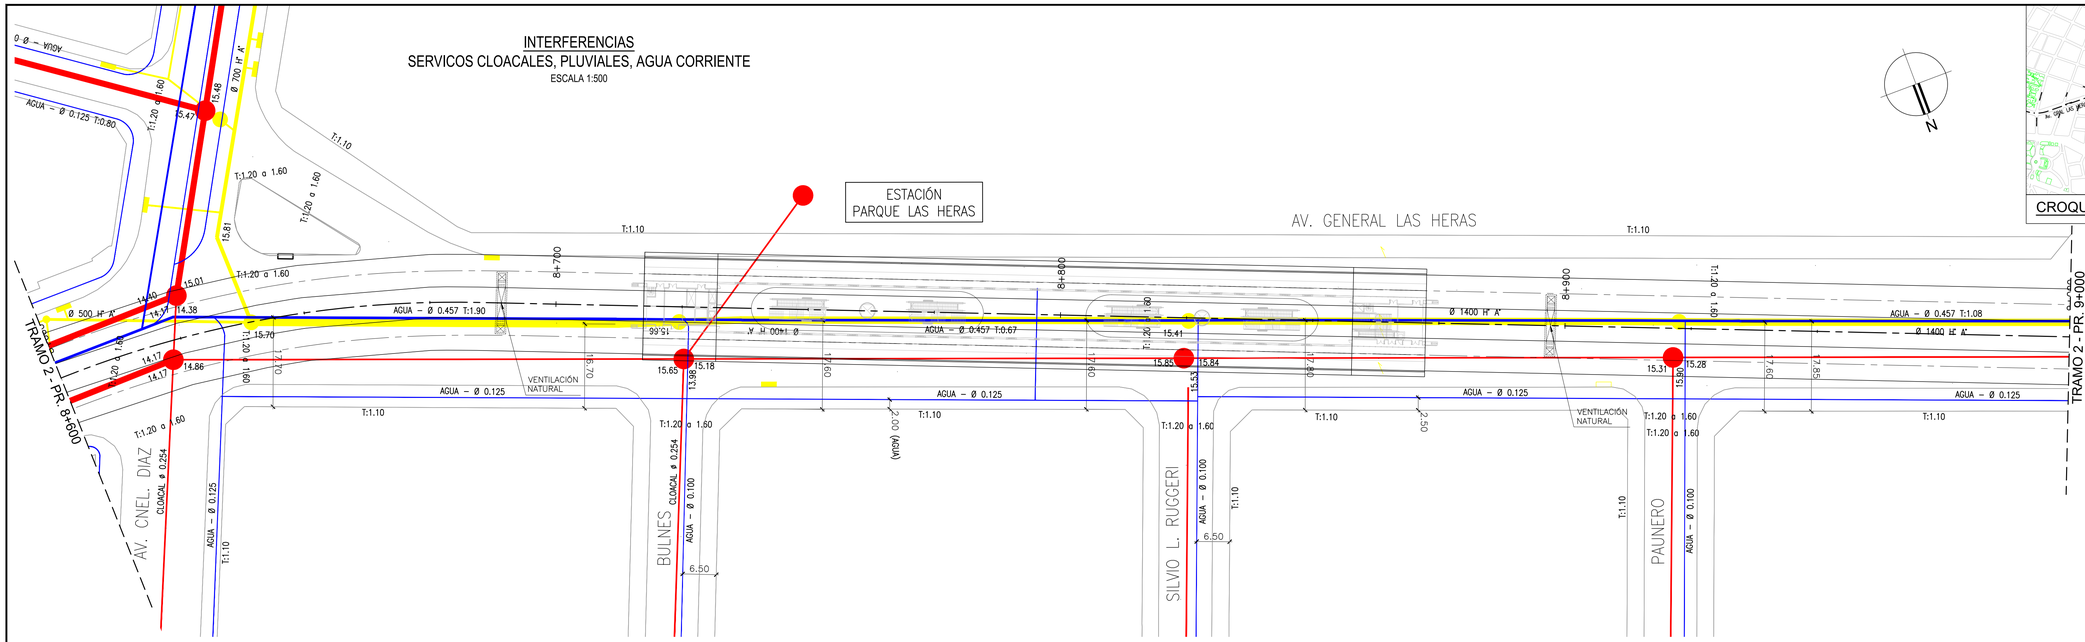

CROQUIS DE UBICACIÓN

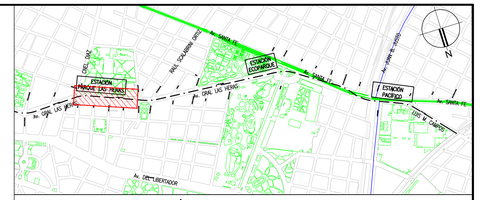

INTERFERENCIAS
GAS, TELEFONIA, ELECTRICIDAD, FIBRA OPTICA
ESCALA 1:500

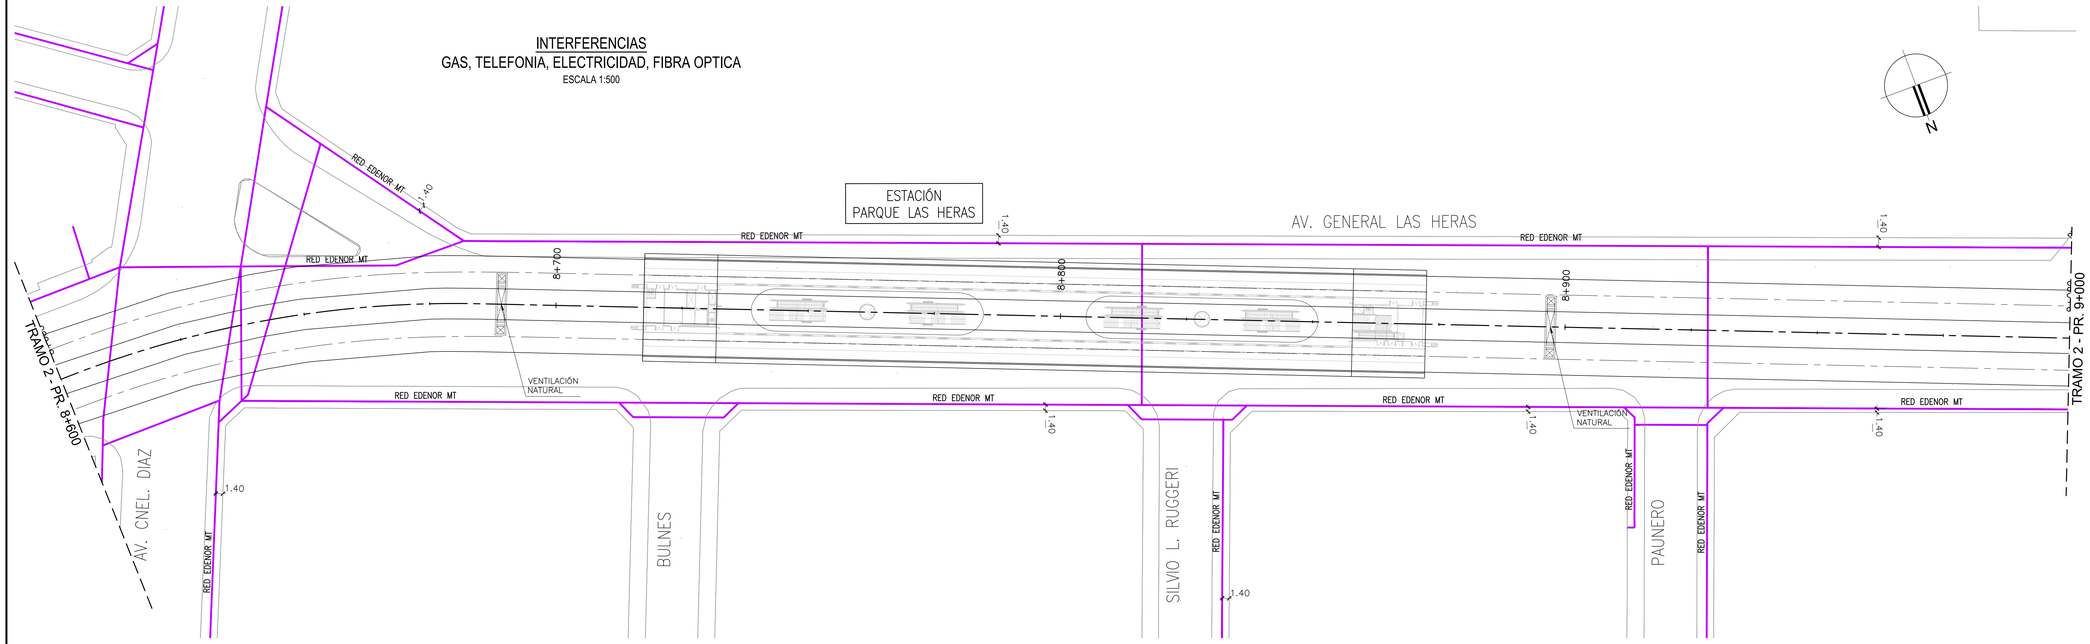

REFERENCIAS:

- RED CLOACAL
- RED PLUVIAL
- RED AGUA
- RED ELECTRICA
- RED GAS
- RED TELEFONICA
- RED FIBRA OPTICA MULTICANAL

NOTAS:

1- SISTEMA DE COORDENADAS DE LA CIUDAD DE BUENOS AIRES.
2- TODAS LAS MEDIDAS ESTÁN EXPRESADAS EN METROS, SALVO INDICACIÓN CONTRARIA

0 10 20 30m
ESCALA 1:500

NOTAS: EL PRESENTE PLANO ES INDICATIVO. LA CONTRATISTA CONFECCIONARA LOS PLANOS DE DETALLE DEFINITIVO QUE DEBERAN SER APROBADOS POR LA D.G.D.GP.U Y LA INSPECCION DE OBRA. EL PLANO PRESENTADO POR LA CONTRATISTA DEBERA EN UN TODO DE ACUERDO CON LA NORMATIVA VIGENTE. TODAS LAS MEDIDAS Y NIVELES SE VERIFICARAN EN OBRA POR EL CONTRATISTA. TODOS LOS DETALLES CONSTRUCTIVOS SERAN COORDINADOS Y COMPATIBILIZADOS EN OBRA

PLANO NO APTO PARA CONSTRUCCION.

MODIFICACIONES:

REVISION	FECHA	DESCRIPCION
0	19/05/2025	EMISION INICIAL
1	11/12/2025	AJUSTE DE PROYECTO
2	26/03/2026	AJUSTE DE PROYECTO

Gobierno de la Ciudad de Buenos Aires

MINISTERIO DE INFRAESTRUCTURA
SUBSECRETARIA DE PROYECTOS Y OBRAS
DIRECCION GENERAL DE PROYECTOS

DGPRO

Obra: LÍNEA F					IF-2026-28525919-GCABA-DGPRO
Plano: TRAZADO DE TÚNEL - INTERFERENCIAS - PROG. 8+600 A 9+000					LF-GL-T02-INT-PL-006
Fecha: 06/05/2026	Eq. de Proyecto: UPU-ATEC-IATASA	Dibujó: D.B.	Revisó: P.C.	Escala: 1:500	Plano N° 006

8/5/2026 11:03 a. m.
LF-GL-T02-INT-PL-001d12_2.dwg

INTERFERENCIAS
SERVICOS CLOACALES, PLUVIALES, AGUA CORRIENTE
ESCALA 1:500

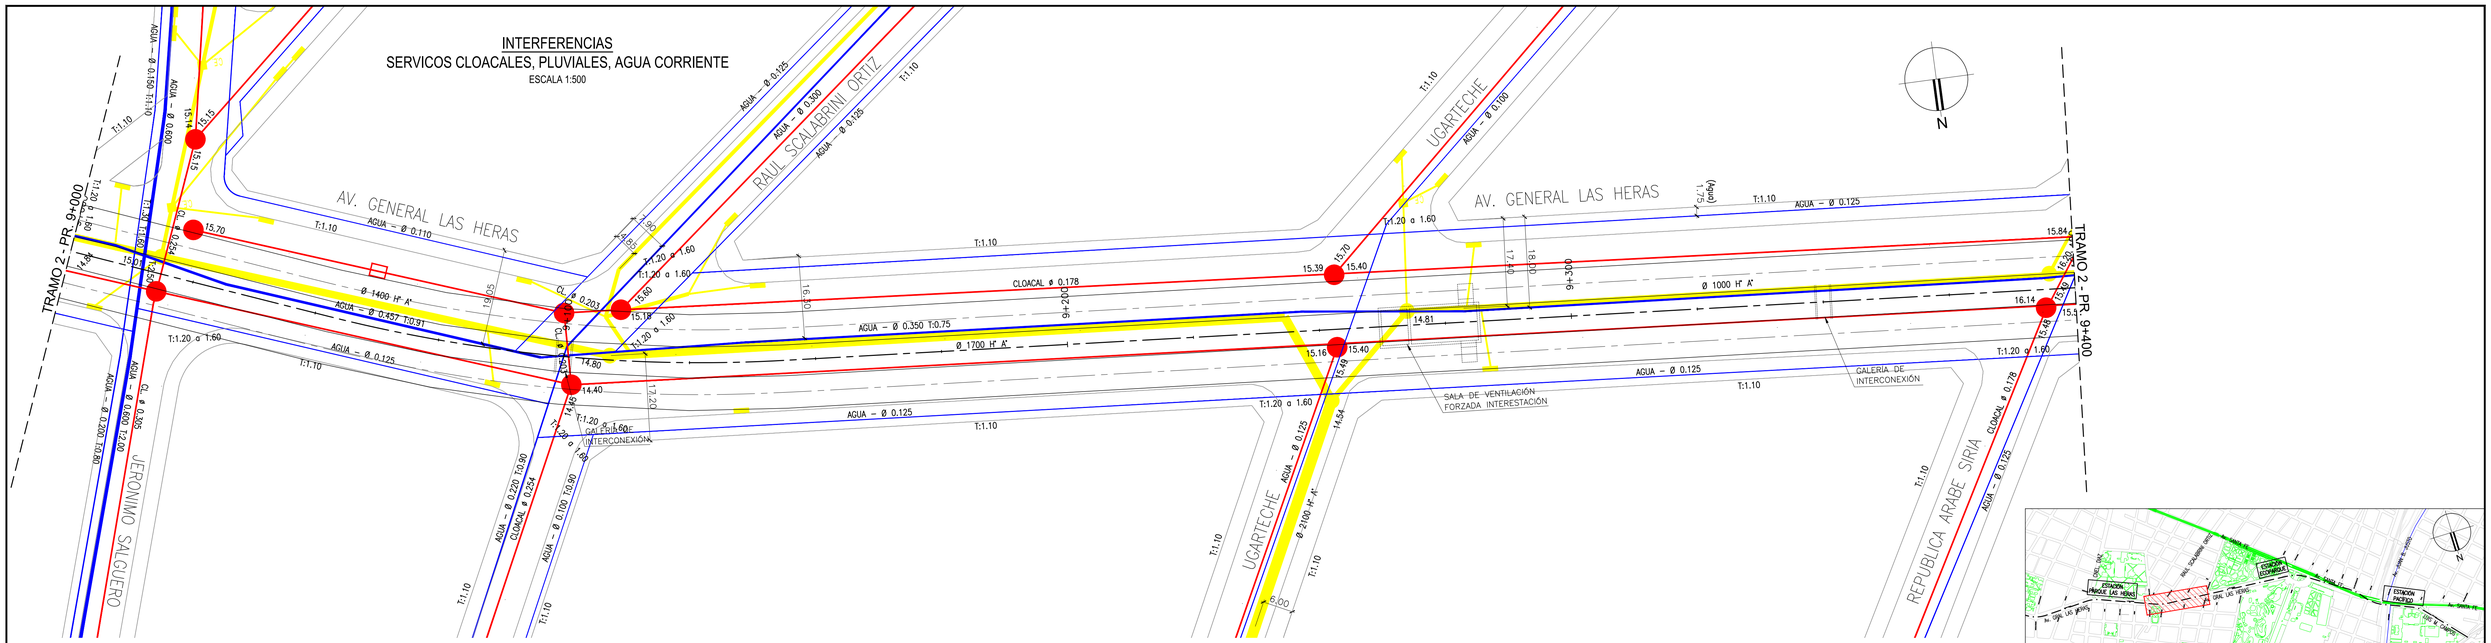

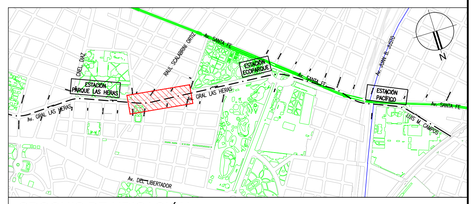

CROQUIS DE UBICACIÓN

INTERFERENCIAS
GAS, TELEFONIA, ELECTRICIDAD, FIBRA OPTICA
ESCALA 1:500

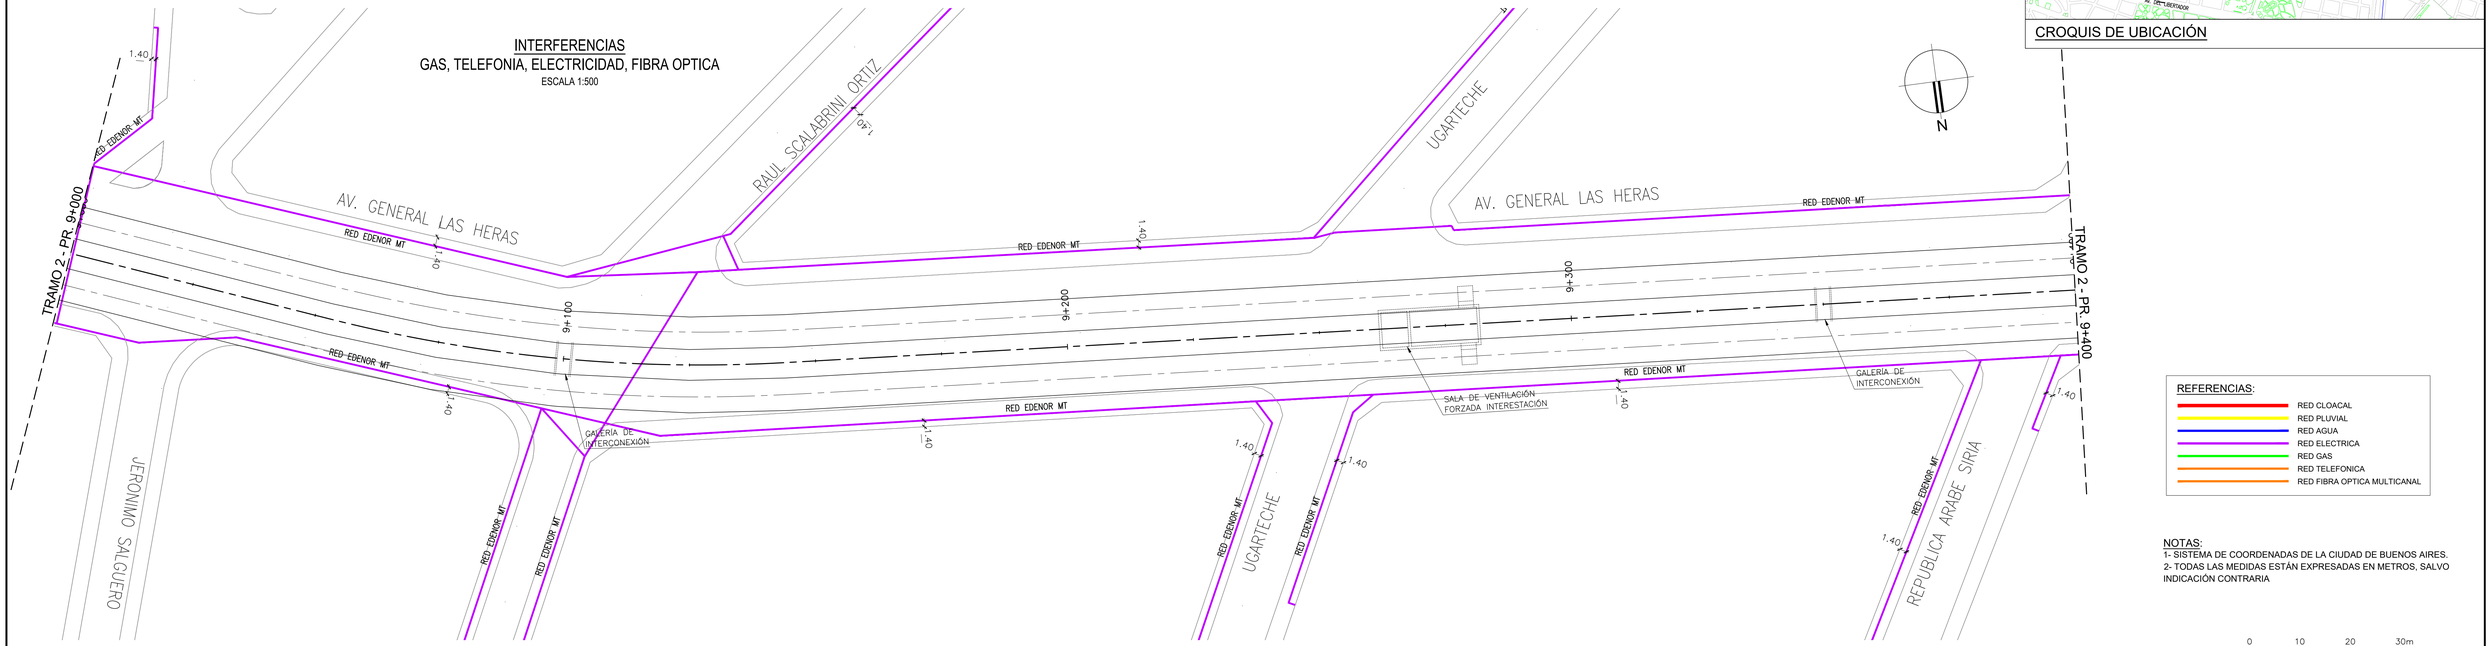

REFERENCIAS:
- RED CLOACAL
- RED PLUVIAL
- RED AGUA
- RED ELECTRICA
- RED GAS
- RED TELEFONICA
- RED FIBRA OPTICA MULTICANAL

NOTAS:
1- SISTEMA DE COORDENADAS DE LA CIUDAD DE BUENOS AIRES.
2- TODAS LAS MEDIDAS ESTÁN EXPRESADAS EN METROS, SALVO INDICACIÓN CONTRARIA

0 10 20 30m
ESCALA 1:500

NOTAS:
EL PRESENTE PLANO ES INDICATIVO. LA CONTRATISTA CONFECCIONARA LOS PLANOS DE DETALLE CORRECTIVO, QUE DEBERAN SER APROBADOS POR LA D.G.ESP. U.T.I.A. INSPECCION DE OBRA, EL PLANO PRESENTADO POR LA CONTRATISTA ESTARA EN UN TODO DE ACUERDO CON LA NORMATIVA VIGENTE.
TODAS LAS MEDIDAS Y NIVELES SE VERIFICARAN EN OBRA POR EL CONTRATISTA.
TODOS LOS DETALLES CONSTRUCTIVOS SERAN COORDINADOS Y CONVENCIONALIZADOS EN OBRA

PLANO NO APTO PARA CONSTRUCCION.

MODIFICACIONES:

REVISIÓN	FECHA	DESCRIPCIÓN
0	19/09/25	EMISIÓN INICIAL
1	11/12/25	AJUSTE DE PROYECTO
2	30/03/26	AJUSTE DE PROYECTO

MINISTERIO DE INFRAESTRUCTURA
SUBSECRETARIA DE PROYECTOS Y OBRAS
DIRECCION GENERAL DE PROYECTOS

DGPRO

Obra: LÍNEA F					IF-2026-28525919-GCABA-DGPRO Plano N°
Plano: TRAZADO DE TÚNEL - INTERFERENCIAS - PROG. 9+000 A 9+400					LF-GL-T02-INT-PL-007 007
Fecha: 06/05/2026	Eq. de Proyecto: UPU-ATEC-IATASA	Dibujó: D.B.	Revisó: P.C.	Escala: 1:500	

8/5/2026 11:03 a. m.
LF-GL-T02-INT-PL-007(R02_2.dwg

INTERFERENCIAS
SERVICOS CLOACALES, PLUVIALES, AGUA CORRIENTE
ESCALA 1:500

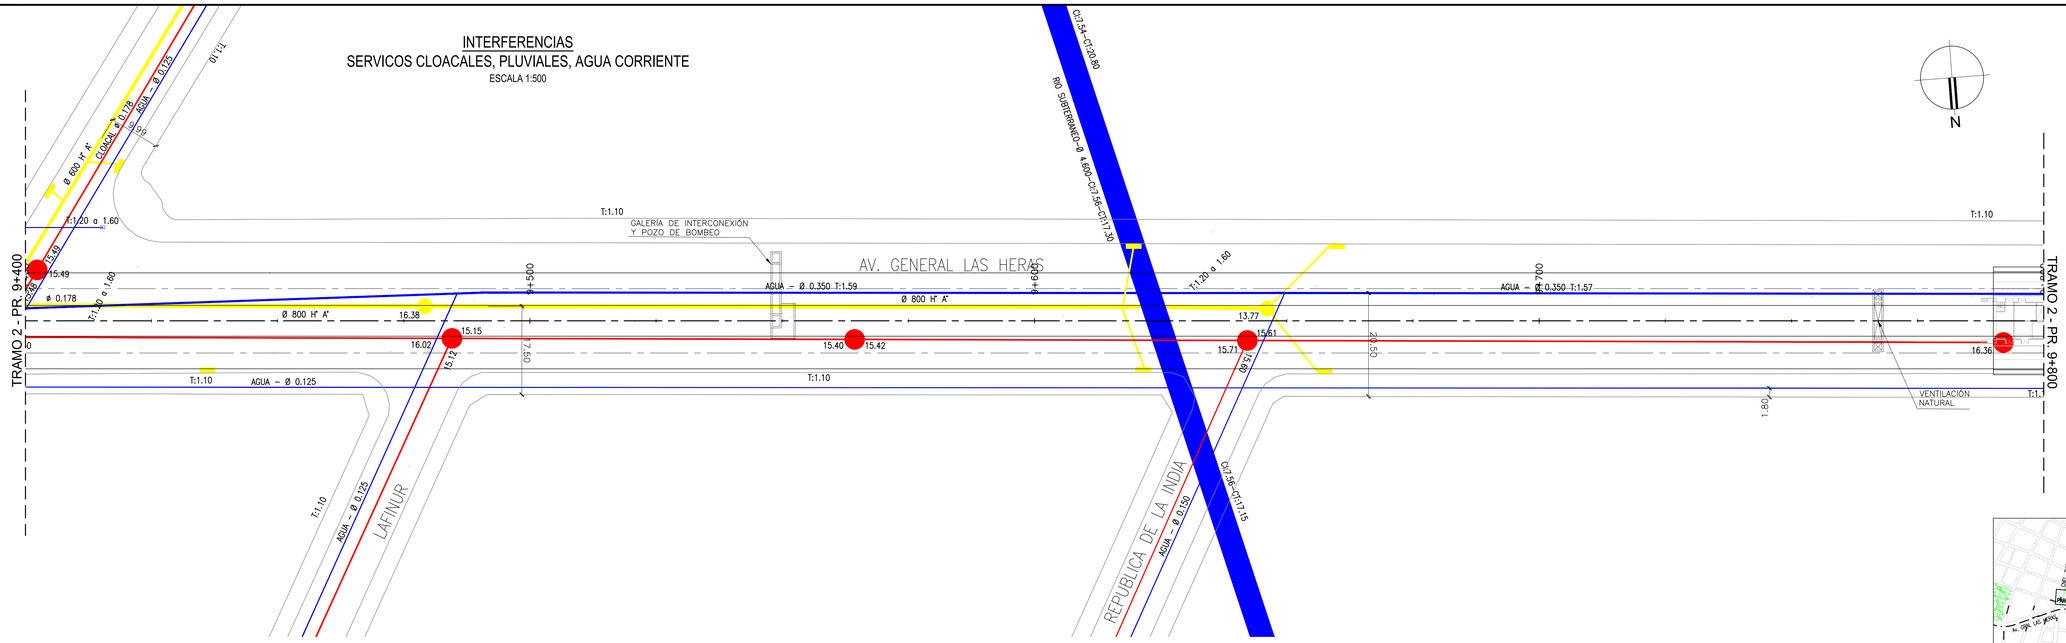

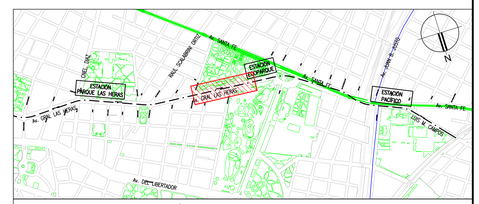

INTERFERENCIAS
GAS, TELEFONIA, ELECTRICIDAD, FIBRA OPTICA
ESCALA 1:500

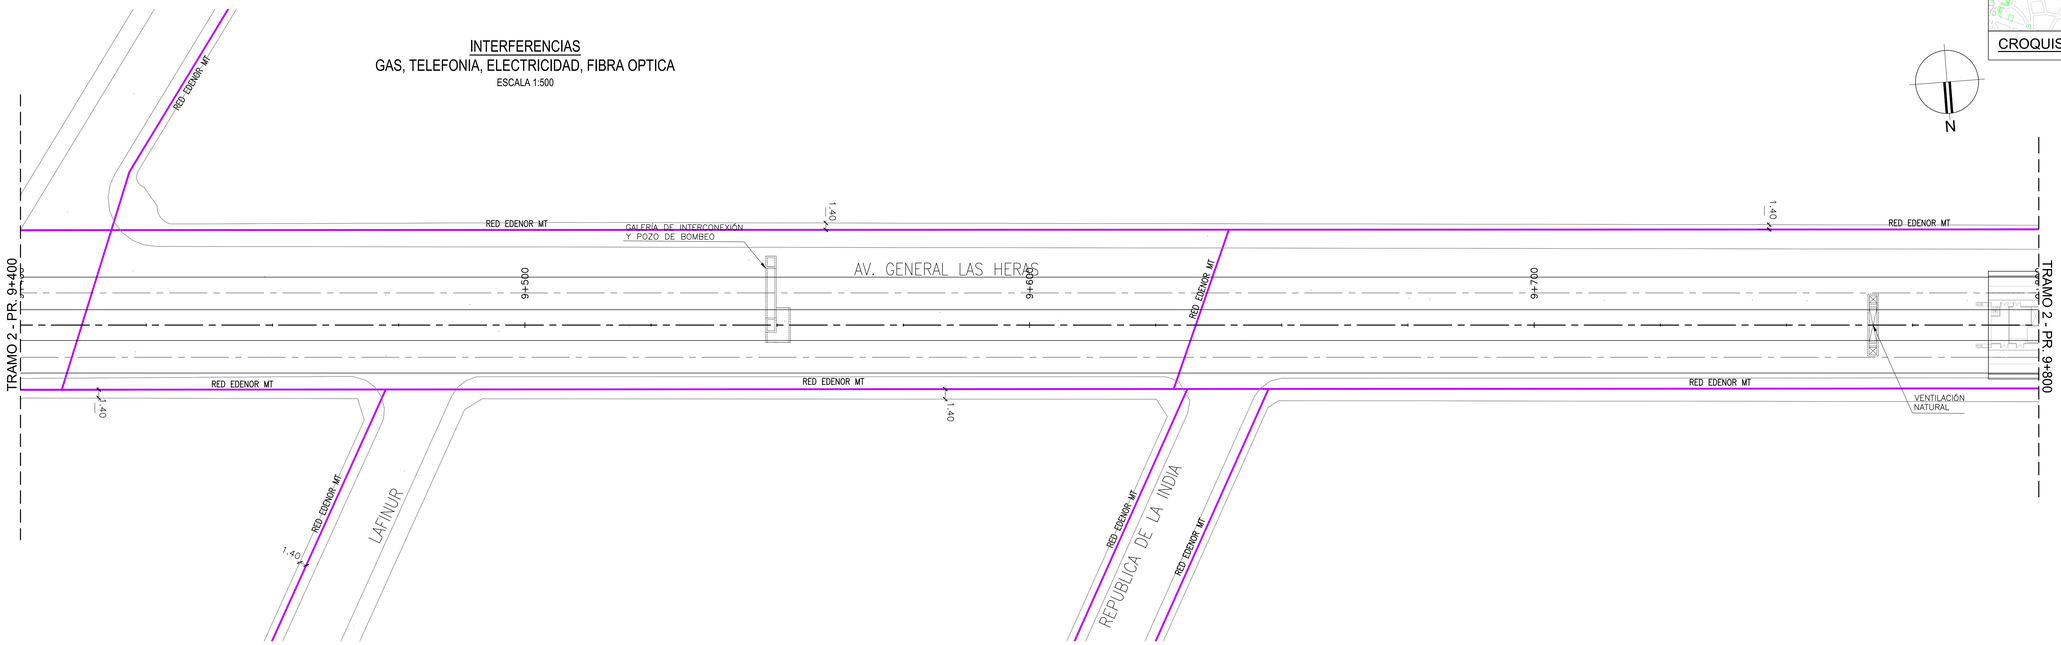

REFERENCIAS:
- RED CLOACAL
- RED PLUVIAL
- RED AGUA
- RED ELECTRICA
- RED GAS
- RED TELEFONICA
- RED FIBRA OPTICA MULTICANAL

NOTAS:
1- SISTEMA DE COORDENADAS DE LA CIUDAD DE BUENOS AIRES.
2- TODAS LAS MEDIDAS ESTÁN EXPRESADAS EN METROS, SALVO INDICACIÓN CONTRARIA

0 10 20 30m
ESCALA 1:500

NOTAS: EL PRESENTE PLANO ES INDICATIVO. LA CONTRATISTA CONFECCIONARÁ LOS PLANOS DE DETALLE DEFINITIVO, QUE DEBERÁN SER APROBADOS POR LA D.G.OBR. ó T.U.A. INSPECCIÓN DE OBRA, EL PLANO PRESENTADO POR LA CONTRATISTA ESTARÁ EN ATENCIÓN DE ACUERDO CON LA NORMATIVA VIGENTE.
TODAS LAS MEDIDAS Y NIVELES SE VERIFICARÁN EN OBRA POR EL CONTRATISTA.
TODOS LOS DETALLES CONSTRUCTIVOS SERÁN COORDINADOS Y CONFIRMADOS EN OBRA

PLANO NO APTO PARA CONSTRUCCION.

MODIFICACIONES:

REVISIÓN	FECHA	DESCRIPCIÓN
0	10/05/2026	DISEÑO INICIAL
1	11/12/2025	AJUSTE DE PROYECTO
2	26/05/2026	AJUSTE DE PROYECTO

MINISTERIO DE INFRAESTRUCTURA
SUBSECRETARIA DE PROYECTOS Y OBRAS
DIRECCION GENERAL DE PROYECTOS

DGPRO

Obra: LINEA F			IF-2026-28525919-GCABA-DGPRO
Plano: TRAZADO DE TÚNEL - INTERFERENCIAS - PROG. 9+400 A 9+800			LF-GL-T02-INT-PL-008
Fecha: 06/05/2026	Eq. de Proyecto: UPU-ATEC-IATASA	Dibujó: D.B.	Revisó: P.C.
			Escala: 1:500

Plano N° 008

8/5/2026 11:03 a. m.
LF-GL-T02-INT-PL-008(T2_2.dwg

INTERFERENCIAS
SERVICOS CLOACALES, PLUVIALES, AGUA CORRIENTE
ESCALA 1:500

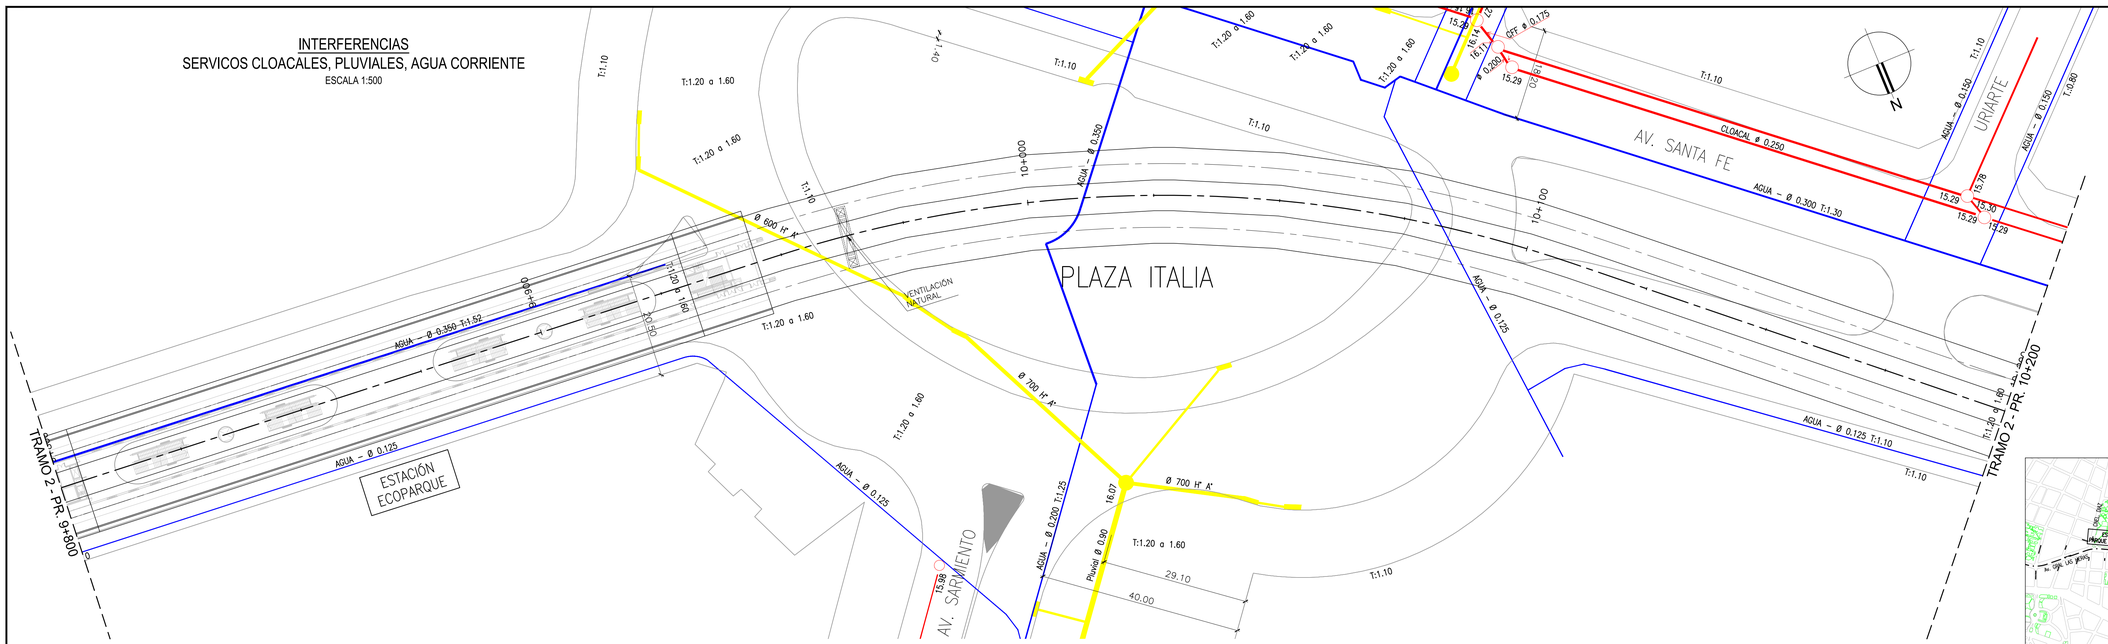

INTERFERENCIAS
GAS, TELEFONIA, ELECTRICIDAD, FIBRA OPTICA
ESCALA 1:500

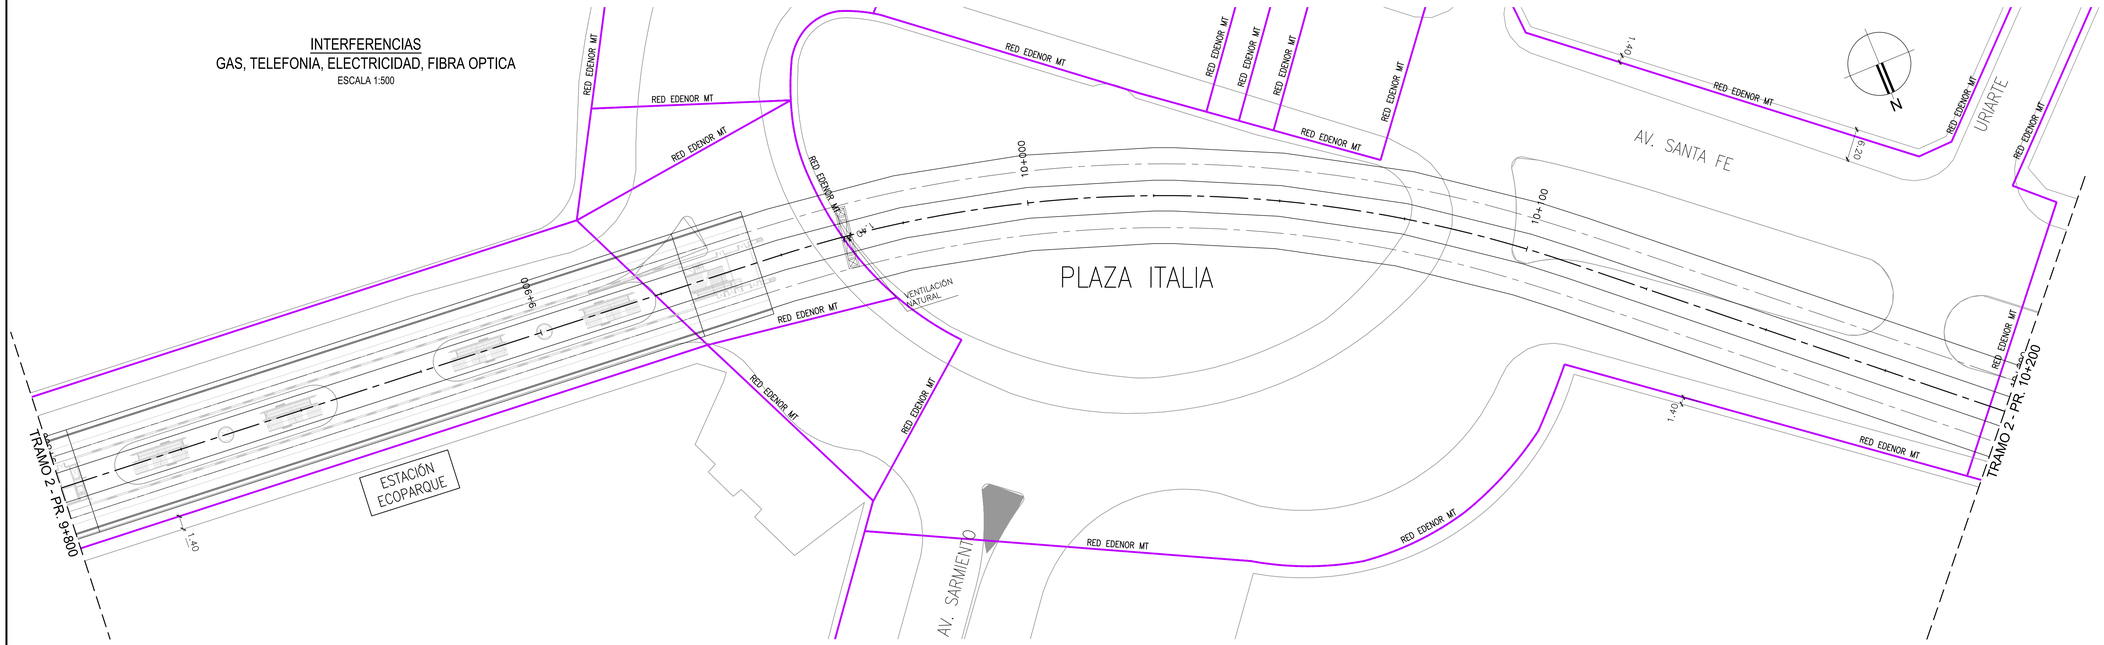

REFERENCIAS:
- RED CLOACAL
- RED PLUVIAL
- RED AGUA
- RED ELECTRICA
- RED GAS
- RED TELEFONICA
- RED FIBRA OPTICA MULTICANAL

NOTAS:
1- SISTEMA DE COORDENADAS DE LA CIUDAD DE BUENOS AIRES.
2- TODAS LAS MEDIDAS ESTÁN EXPRESADAS EN METROS, SALVO INDICACIÓN CONTRARIA

0 10 20 30m
ESCALA 1:500

NOTAS: EL PRESENTE PLANO ES INDICATIVO. LA CONTRATISTA CONFECCIONARA LOS PLANOS DE DETALLE DEFINITIVO QUE DEBERAN SER APROBADOS POR LA D.G.D.GIP.U Y LA INSPECCION DE OBRA. EL PLANO PRESENTADO POR LA CONTRATISTA DEBERA EN UN TODO DE ACUERDO CON LA NORMATIVA VIGENTE. TODAS LAS MEDIDAS Y NIVELES SE VERIFICARAN EN OBRA POR EL CONTRATISTA. TODOS LOS DETALLES CONSTRUCTIVOS SERAN COORDINADOS Y COMPATIBILIZADOS EN OBRA

PLANO NO APTO PARA CONSTRUCCION.

MODIFICACIONES:

REVISION	FECHA	DESCRIPCION
0	19/09/25	EMISION INICIAL
1	11/12/25	AJUSTE DE PROYECTO
2	26/03/26	AJUSTE DE PROYECTO

Gobierno de la Ciudad de Buenos Aires

MINISTERIO DE INFRAESTRUCTURA
SUBSECRETARIA DE PROYECTOS Y OBRAS
DIRECCION GENERAL DE PROYECTOS

DGPRO

Obra: LÍNEA F					IF-2026-28525919-GCABA-DGPRO
Plano: TRAZADO DE TÚNEL - INTERFERENCIAS - PROG. 9+800 A 10+200					LF-GL-T02-INT-PL-009
Fecha: 06/05/2026	Eq. de Proyecto: UPU-ATEC-IATASA	Dibujó: D.B.	Revisó: P.C.	Escala: 1:500	Plano N° 009

8/5/2026 11:03 a. m.
LF-GL-T02-INT-PL-001d12_2.dwg

INTERFERENCIAS
SERVICOS CLOACALES, PLUVIALES, AGUA CORRIENTE
ESCALA 1:500

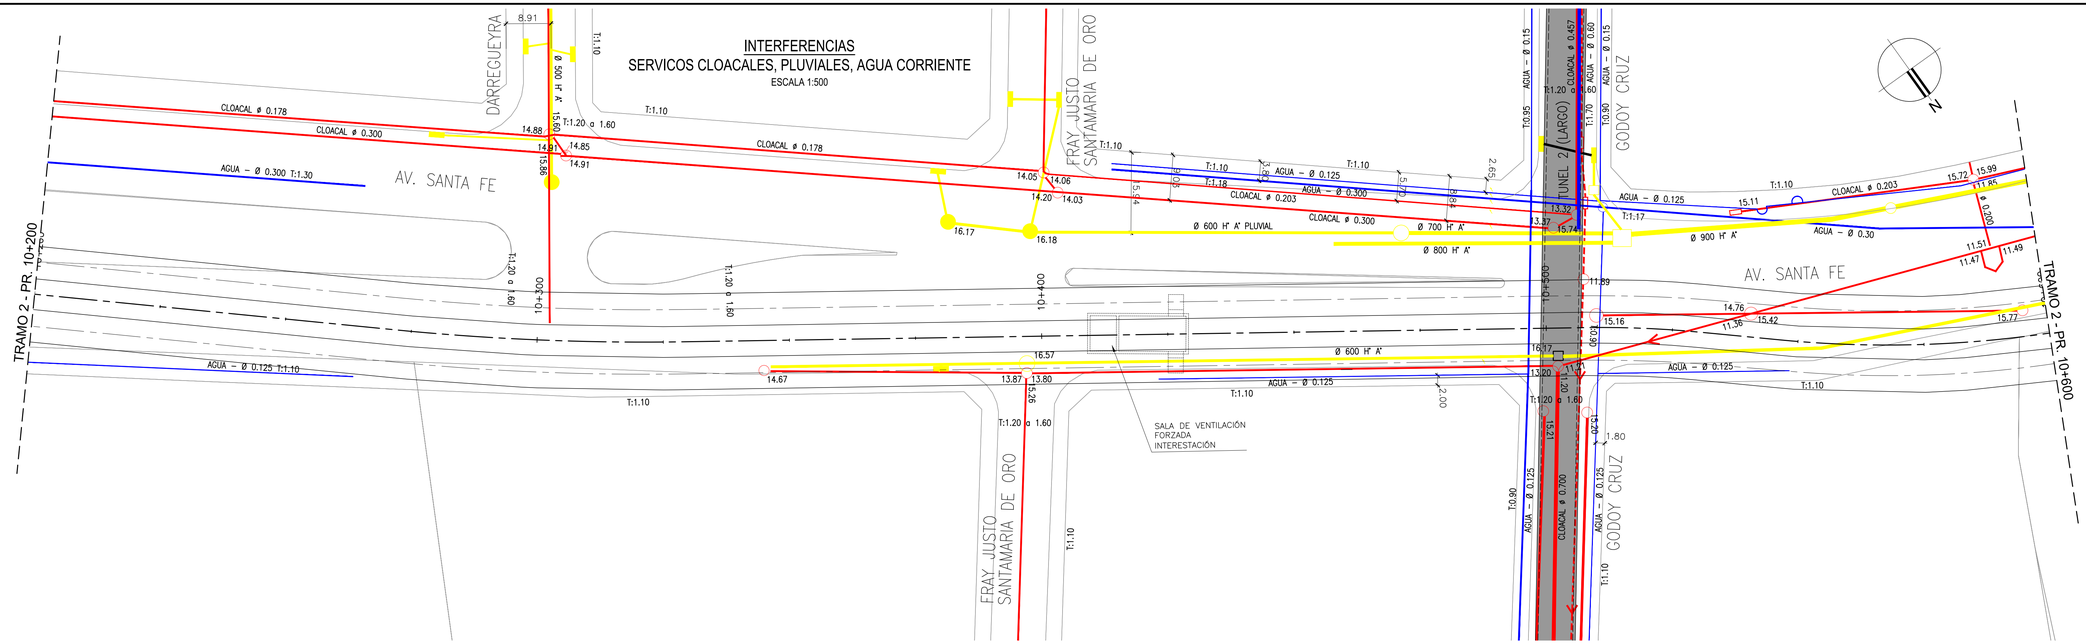

INTERFERENCIAS
GAS, TELEFONIA, ELECTRICIDAD, FIBRA OPTICA
ESCALA 1:500

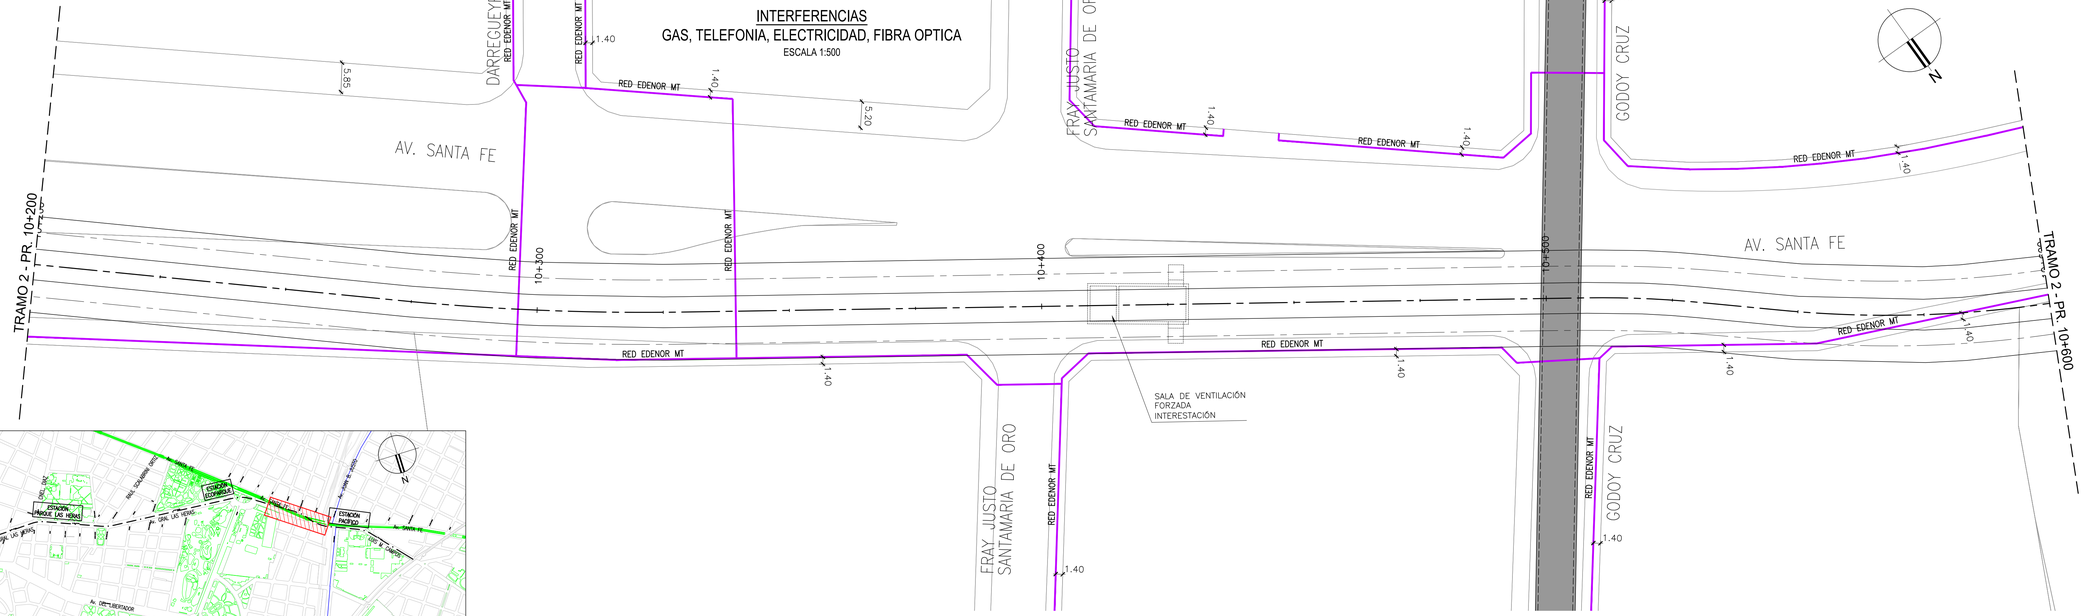

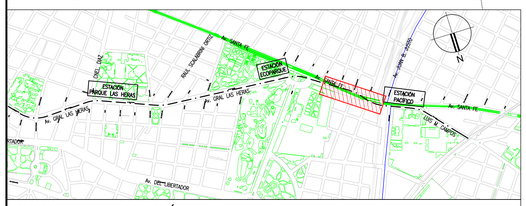

CROQUIS DE UBICACIÓN

REFERENCIAS:
- RED CLOACAL
- RED PLUVIAL
- RED AGUA
- RED ELECTRICA
- RED GAS
- RED TELEFONICA
- RED FIBRA OPTICA MULTICANAL

NOTAS:
1- SISTEMA DE COORDENADAS DE LA CIUDAD DE BUENOS AIRES.
2- TODAS LAS MEDIDAS ESTÁN EXPRESADAS EN METROS, SALVO INDICACIÓN CONTRARIA

0 10 20 30m
ESCALA 1:500

NOTAS: EL PRESENTE PLANO ES INDICATIVO, LA CONTRATISTA CONFECCIONARA LOS PLANOS DE DETALLE CORRECTIVO, QUE DEBERAN SER APROBADOS POR LA D.G.DGP. U.T.I.A. INSPECCION DE OBRA. EL PLANO PRESENTADO POR LA CONTRATISTA ESTARA EN UN TODO DE ACUERDO CON LA NORMATIVA VIGENTE. TODAS LAS MEDIDAS Y NIVELES SE VERIFICARAN EN OBRA POR EL CONTRATISTA. TODOS LOS DETALLES CONSTRUCTIVOS SERAN COORDINADOS Y CONVENCIONADOS EN OBRA

PLANO NO APTO PARA CONSTRUCCION.

MODIFICACIONES:	REVISIÓN	FECHA	DESCRIPCION
	0	19/09/25	EMISIÓN INICIAL
	1	11/12/25	AJUSTE DE PROYECTO
	2	30/03/26	AJUSTE DE PROYECTO

MINISTERIO DE INFRAESTRUCTURA
SUBSECRETARIA DE PROYECTOS Y OBRAS
DIRECCION GENERAL DE PROYECTOS

DGPRO

Obra: LÍNEA F			IF-2026-28525919-GCABA-DGPRO
Plano: TRAZADO DE TÚNEL - INTERFERENCIAS - PROG. 10+200 A 10+600			LF-GL-T02-INT-PL-010
Fecha: 06/05/2026	Eq. de Proyecto: UPU-ATEC-IATASA	Dibujó: D.B.	Revisó: P.C. Escala: 1:500

Plano N° 010

8/5/2026 11:03 a. m.
LF-GL-T02-INT-PL-010 R02_2.dwg

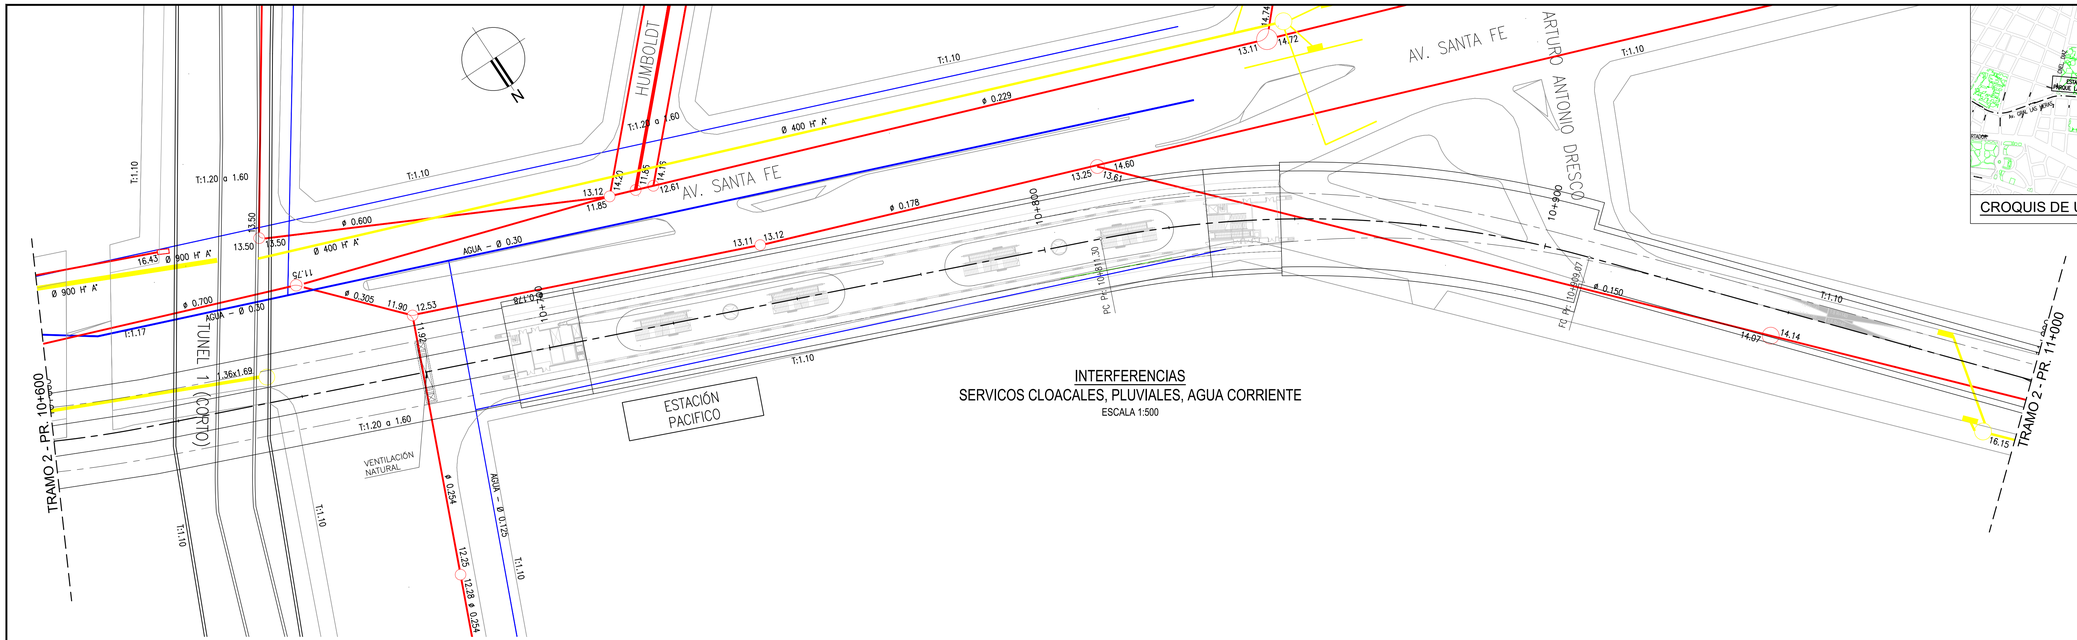

INTERFERENCIAS
SERVICIOS CLOACALES, PLUVIALES, AGUA CORRIENTE
ESCALA 1:500

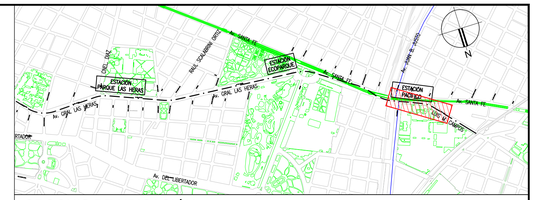

CROQUIS DE UBICACIÓN

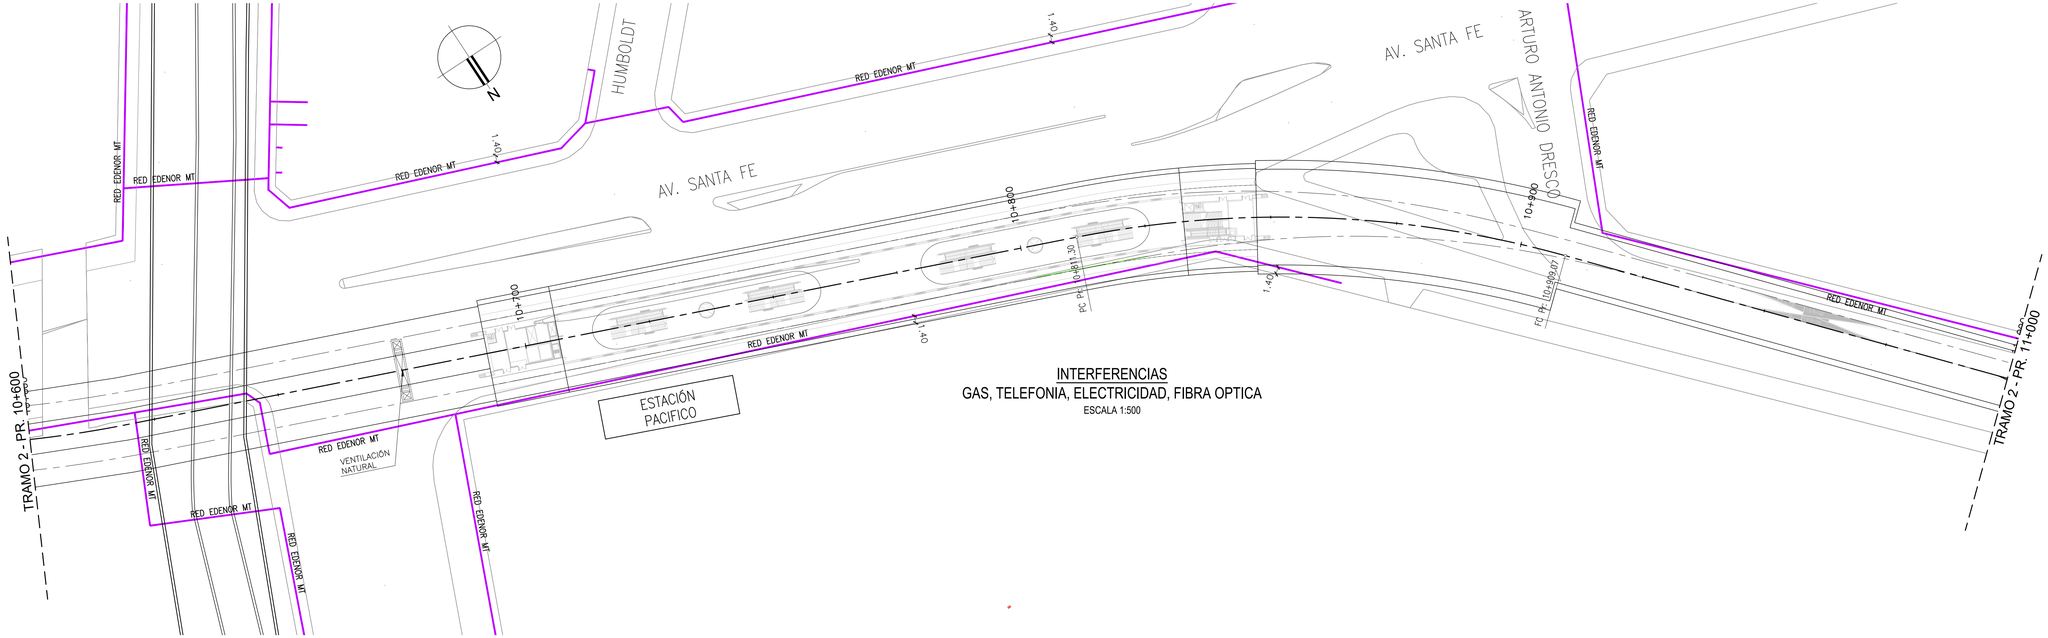

INTERFERENCIAS
GAS, TELEFONIA, ELECTRICIDAD, FIBRA OPTICA
ESCALA 1:500

REFERENCIAS:
- RED CLOACAL
- RED PLUVIAL
- RED AGUA
- RED ELECTRICA
- RED GAS
- RED TELEFONICA
- RED FIBRA OPTICA MULTICANAL

NOTAS:
1- SISTEMA DE COORDENADAS DE LA CIUDAD DE BUENOS AIRES.
2- TODAS LAS MEDIDAS ESTÁN EXPRESADAS EN METROS, SALVO INDICACIÓN CONTRARIA

0 10 20 30m
ESCALA 1:500

NOTAS: EL PRESENTE PLANO ES INDICATIVO. LA CONTRATISTA CONFECCIONARA LOS PLANOS DE DETALLE DEFINITIVO QUE DEBERAN SER APROBADOS POR LA D.G.D.GIP.U Y LA INSPECCION DE OBRA. EL PLANO PRESENTADO POR LA CONTRATISTA DEBERA EN UN TODO DE ACUERDO CON LA NORMATIVA VIGENTE. TODAS LAS MEDIDAS Y NIVELES SE VERIFICARAN EN OBRA POR EL CONTRATISTA. TODOS LOS DETALLES CONSTRUCTIVOS SERAN COORDINADOS Y COMPATIBILIZADOS EN OBRA

PLANO NO APTO PARA CONSTRUCCION.

MODIFICACIONES:

REVISION	FECHA	DESCRIPCION
0	19/05/2025	EMISION INICIAL
1	11/12/2025	AJUSTE DE PROYECTO
2	26/03/2026	AJUSTE DE PROYECTO

Gobierno de la Ciudad de Buenos Aires

MINISTERIO DE INFRAESTRUCTURA
SUBSECRETARIA DE PROYECTOS Y OBRAS
DIRECCION GENERAL DE PROYECTOS

DGPRO

Obra: LÍNEA F					IF-2026-28525919-GCABA-DGPRO
Plano: TRAZADO DE TÚNEL - INTERFERENCIAS - PROG. 10+600 A 11+000					LF-GL-T02-INT-PL-011
Fecha: 06/05/2026	Eq. de Proyecto: UPU-ATEC-IATASA	Dibujó: D.B.	Revisó: P.C.	Escala: 1:500	Plano N° 011

8/5/2026 11:03 a. m.
LF-GL-T02-INT-PL-001d12_2.dwg

INTERFERENCIAS
SERVICOS CLOACALES, PLUVIALES, AGUA CORRIENTE
ESCALA 1:500

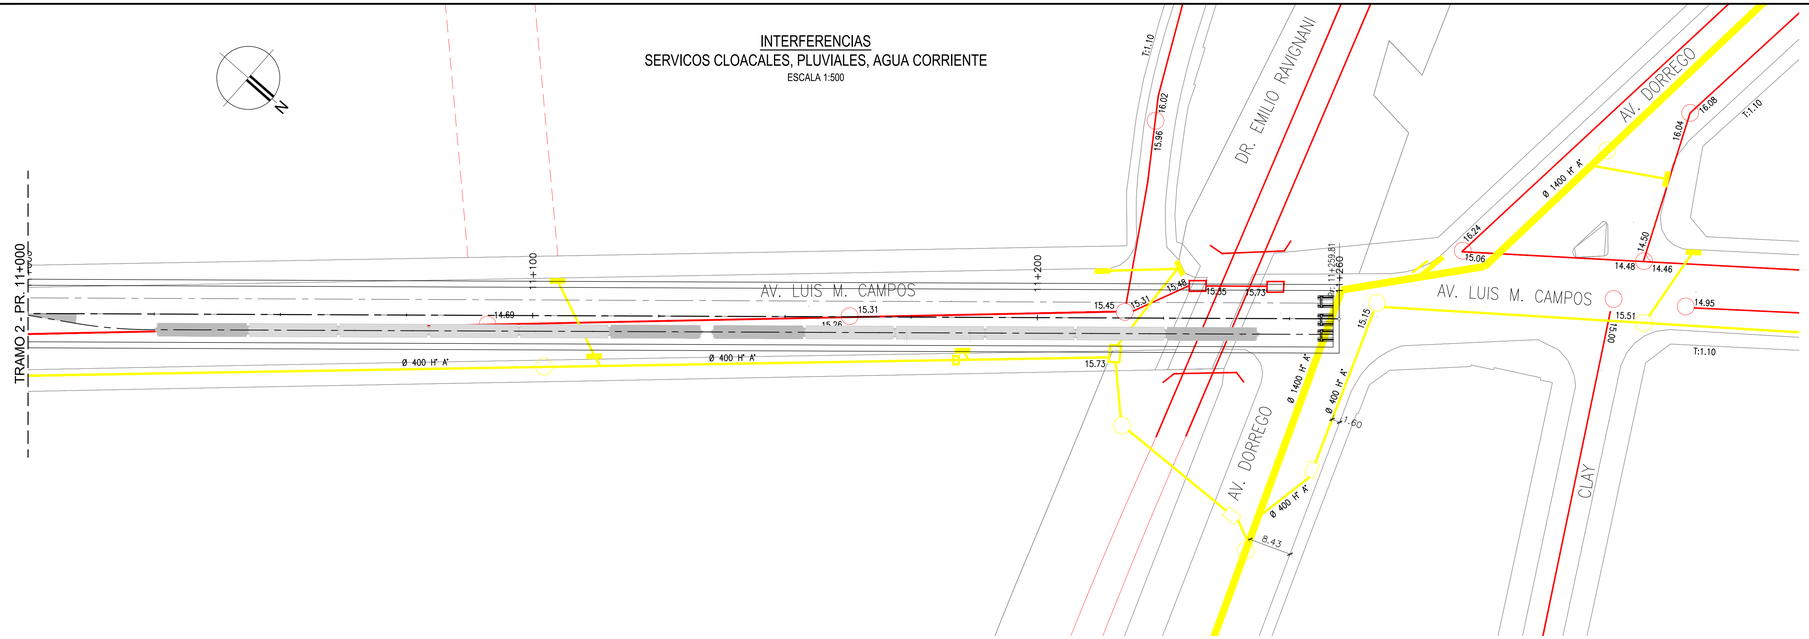

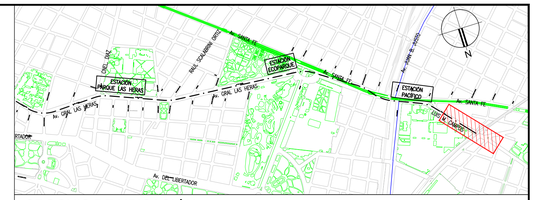
N
ESTACIÓN RETIRO (MITRE)
ESTACIÓN RETIRO (SAN MARTÍN)
ESTACIÓN RETIRO (BELGRANO)
ESTACIÓN MIGUEL LAS HERAS
ESTACIÓN RETIRO (GRAL. BELGRANO)
ESTACIÓN RETIRO (GRAL. SAN MARTÍN)
ESTACIÓN RETIRO (MITRE)
ESTACIÓN RETIRO (GRAL. LAS HERAS)
ESTACIÓN RETIRO (GRAL. LAS HERAS)
ESTACIÓN RETIRO (GRAL. LAS HERAS

G O B I E R N O DE LA C I U D A D DE B U E N O S A I R E S

"2026 - Año del 30° Aniversario de la sanción de la Constitución de la Ciudad Autónoma de Buenos Aires"

Hoja Adicional de Firmas
Informe gráfico

Número: IF-2026-28525919-GCABA-DGPRO

Buenos Aires, Jueves 18 de Junio de 2026

Referencia: Interferencias Linea F parte I y II

El documento fue importado por el sistema GEDO con un total de 31 pagina/s.

Digitally signed by Comunicaciones Oficiales
Date: 2026.06.18 12:57:45 -03:00

GEORGINA TUERO
Gerente Operativo
D. G. PROYECTOS
MINISTERIO DE MOVILIDAD E INFRAESTRUCTURA

Digitally signed by Comunicaciones Oficiales
Date: 2026.06.18 12:57:52 -03:00