


CONSTITUCION - PROYECTO_General

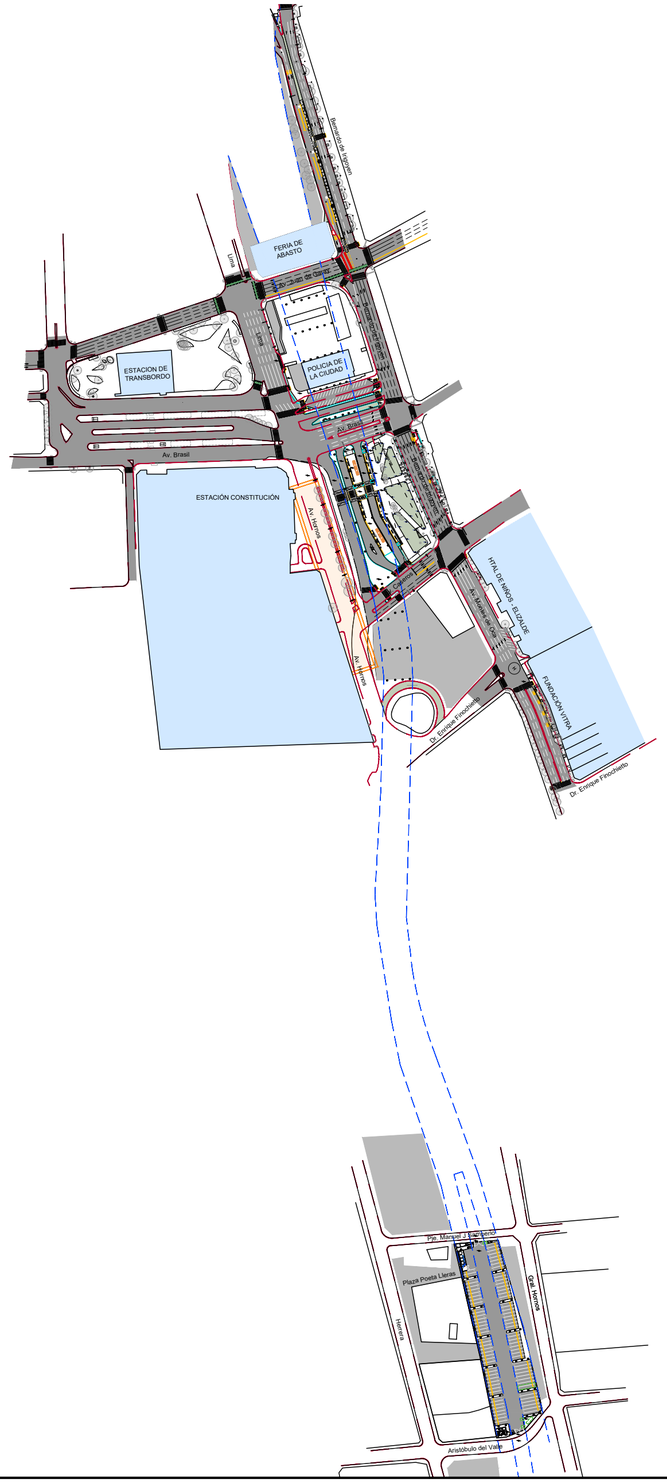

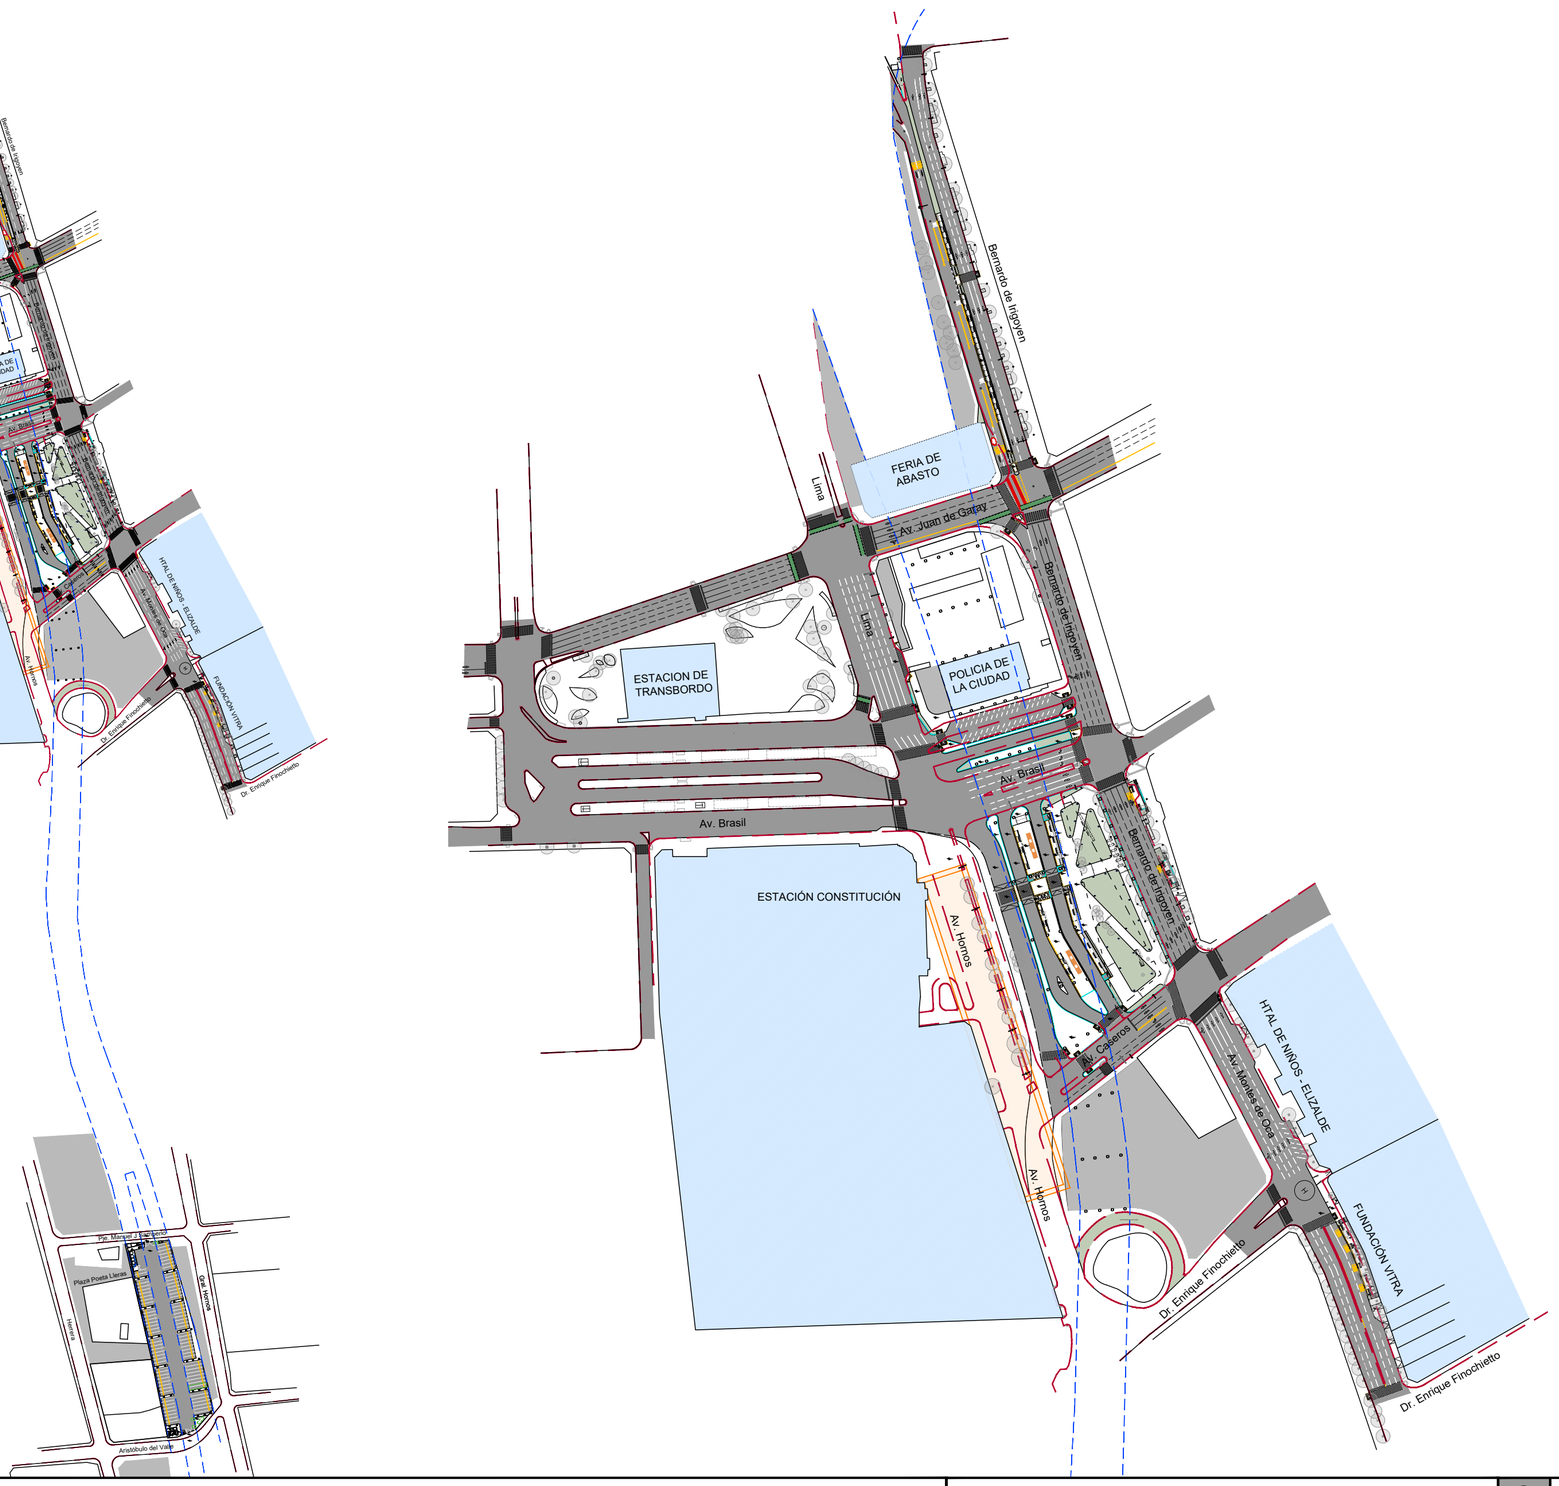


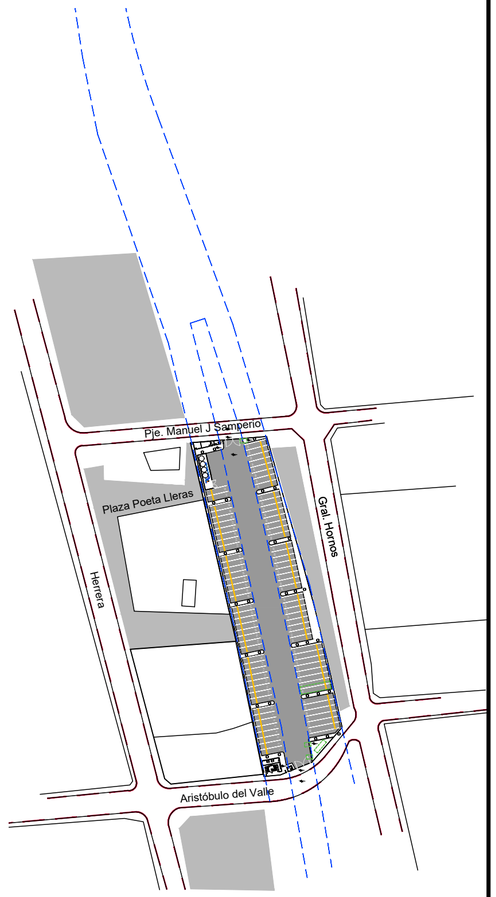

REFERENCIAS

- Edificios existentes importantes
- Áreas verdes existentes
- Árboles existentes
- Límite cordon existente
- Proyección de la Autopista
- Columnas Autopista
- Semáforos Existentes
- Demarcación Existente
- Vados Existentes
- Luminaria Existente
- Demarcador de carril "Tortuga" Existente
- Puesto Existente
- Paradores Existentes
- Accesos Vehiculares existentes
- Bicisenda Existente
- Bancos Existente
- Planteras Existentes
- Sumideros Existentes
- Áreas verdes nuevas
- Demarcación Nueva
- Reja o elemento a definir - impide el paso
- Barandas Paradores
- Cordón Simple montante nuevo
- Cordón Doble montante nuevo
- Baldosas Táctiles 40x40
- Baldosas Guias 40x40
- Juego TA-TE-TI
- Cazoleta Existente con cubre cazoleta nuevo
- Rayuela Pintada
- Calzada
- Luminarias Nuevas
- Obrador Linea F
- Vado Nuevo

ÁREA DE INTERVENCIÓN

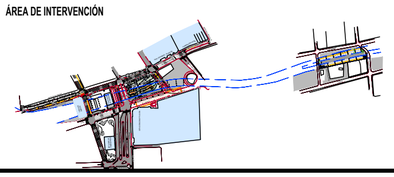

Gobierno de la Ciudad de Buenos Aires

MINISTERIO DE MOVILIDAD E INFRAESTRUCTURA
SUBSECRETARIA DE PROYECTOS Y OBRAS
DIRECCION GENERAL DE PROYECTOS

DGPRO

Obra: CT CONSTITUCION	Plano: CTC_ARQ_General	Plano N° A06
Rubro: ARQUITECTURA	Revisión: Rev.00	
Tramo: -	Fecha: 07/01/2026	Escala: -

MODIFICACIONES:


REVISION	FECHA	DESCRIPCION
-	-	-
-	-	-
-	-	-
-	-	-
-	-	-
-	-	-
-	-	-
-	-	-
-	-	-

NOTAS: EL PRESENTE PLANO ES INDICATIVO. LA CONTRATISTA CONFECCIONARA LOS PLANOS DE DETALLE DEFINITIVO, QUE DEBERAN SER APROBADOS POR LA D.G.CYM Y LA INSPECCION DE OBRA. EL PLANO PRESENTADO POR LA CONTRATISTA ESTARA EN UN TODO DE ACUERDO CON LA NORMATIVA VIGENTE.

PLANO-2026-06751823-GCABA-DGPRO

PLANO NO APTO PARA CONSTRUCCIÓN


CONSTITUCION - PROYECTO_Bernardo de Irigoyen

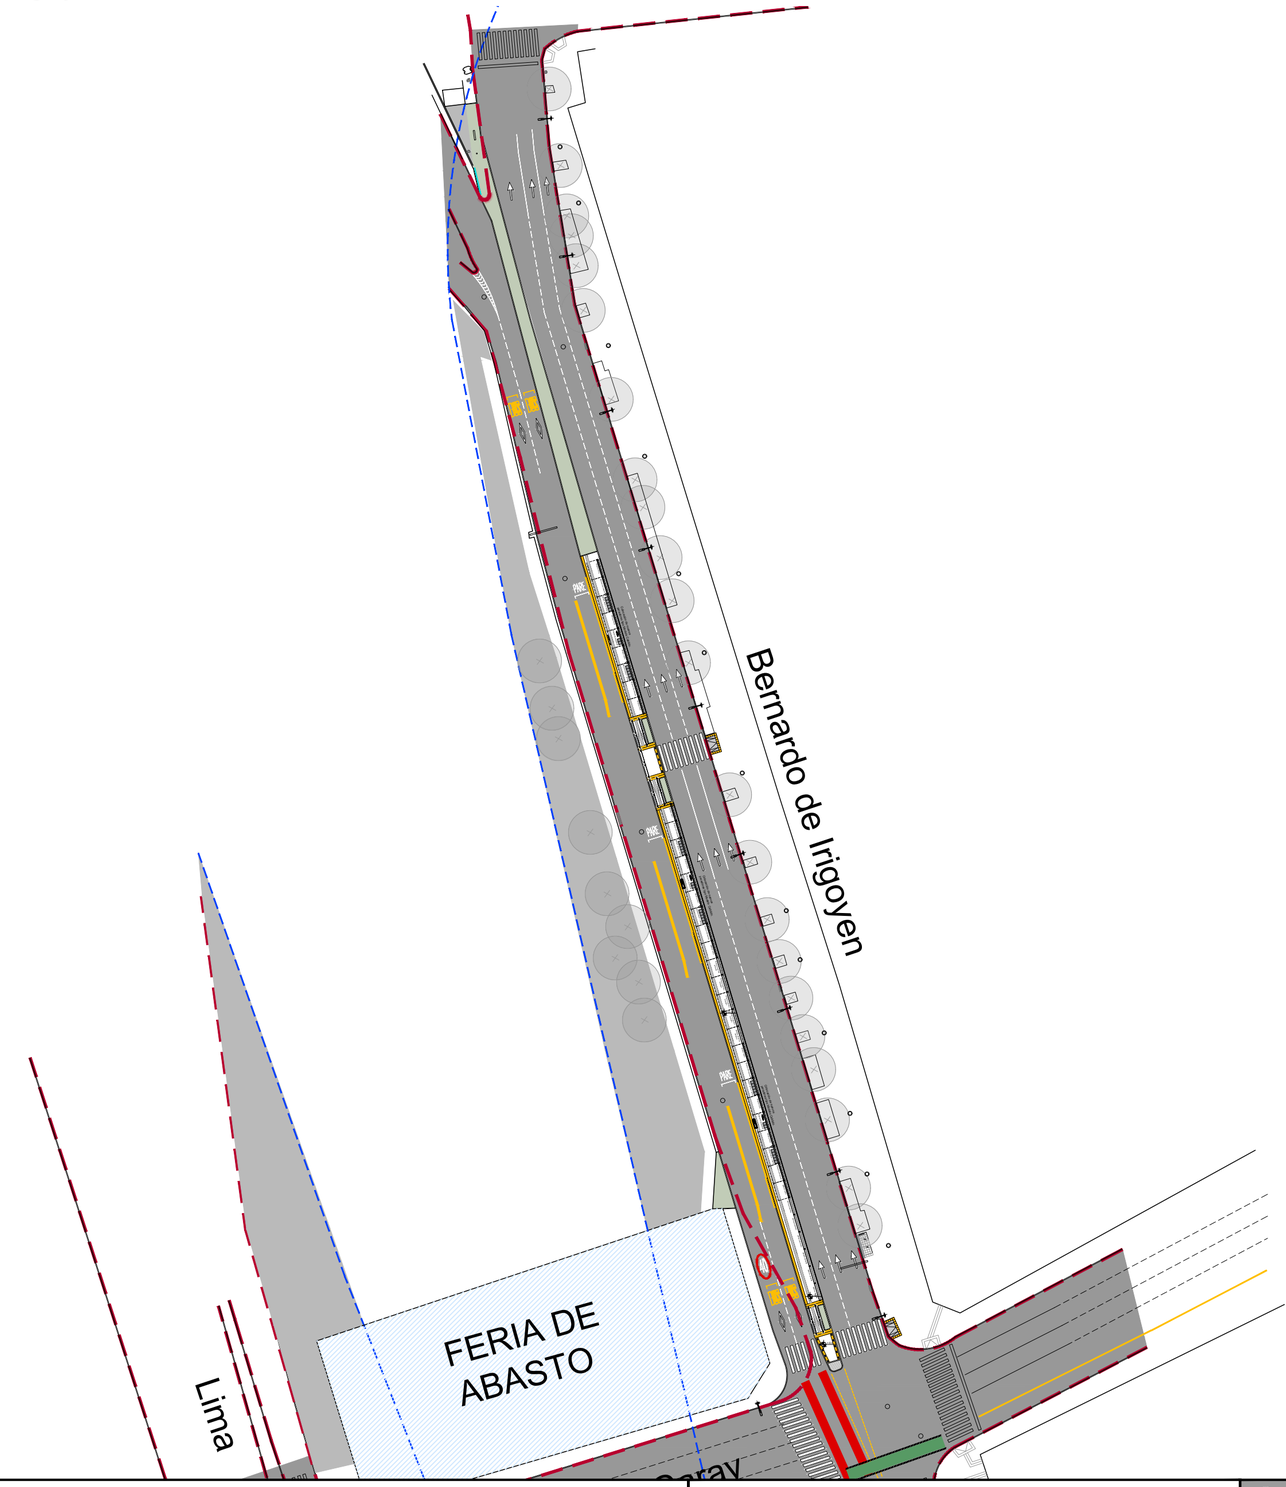

REFERENCIAS

- Edificios existentes importantes
- Áreas verdes existentes
- Árboles existentes
- Límite cordon existente
- Proyección de la Autopista
- Columnas Autopista
- Semáforos Existentes
- Demarcación Existente
- Vados Existentes
- Luminaria Existente
- Demarcador de carril "Tortuga" Existente
- Puesto Estiatoria
- Paradores Existentes
- Accesos Vehiculares existentes
- Bicisenda Existente
- Bancos Existente
- Planteras Existentes
- Sumideros Existentes
- Áreas verdes nuevas
- Demarcación Nueva
- Reja o elemento a definir - impide el paso
- Barandas Paradores
- Cordón Simple montante nuevo
- Cordón Doble montante nuevo
- Baldosas Táctiles 40x40
- Baldosas Guias 40x40
- Juego TA-TE-TI
- Cazoleta Existente con cubre cazoleta nuevo
- Rayuela Pintada
- Calzada
- Luminarias Nuevas
- Obrador Linea F
- Vado Nuevo

ÁREA DE INTERVENCIÓN

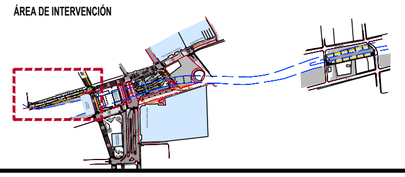

Gobierno de la Ciudad de Buenos Aires

MINISTERIO DE MOVILIDAD E INFRAESTRUCTURA
SUBSECRETARIA DE PROYECTOS Y OBRAS
DIRECCION GENERAL DE PROYECTOS

DGPRO

Obra: CT CONSTITUCION	Plano: CTC_ARQ_Bernardo de Irigoyen	Plano Nº A07
Rubro: ARQUITECTURA	Revisión: Rev.00	
Tramo: -	Fecha: 07/01/2026	Escala: -

MODIFICACIONES:

REVISION	FECHA	DESCRIPCION
-	-	-
-	-	-
-	-	-
-	-	-
-	-	-
-	-	-
-	-	-
-	-	-

NOTAS: EL PRESENTE PLANO ES INDICATIVO. LA CONTRATISTA CONFECCIONARÁ LOS PLANOS DE DETALLE DEFINITIVO, QUE DEBERÁN SER APROBADOS POR LA D.G.C.U.M.I.* Y LA INSPECCIÓN DE OBRA. EL PLANO PRESENTADO POR LA CONTRATISTA ESTARÁ EN UN TODO DE ACUERDO CON LA NORMATIVA VIGENTE.
*CONSULTAR CON EL ÁREA CORRESPONDIENTE EN CADA PROYECTO

PLANO NO APTO PARA CONSTRUCCIÓN

PLANO-2026-06751823-GCABA-DGPRO

CONSTITUCION - CORTES DE PROYECTO - BERNARDO DE IRIGOYEN



ÁREA DE INTERVENCIÓN

Gobierno de la Ciudad de Buenos Aires

MINISTERIO DE MOVILIDAD E INFRAESTRUCTURA
SUBSECRETARIA DE PROYECTOS Y OBRAS
DIRECCION GENERAL DE PROYECTOS

DGPRO

Obra: CT CONSTITUCION	Plano: CTC_COR_Bernardo de Irigoyen	Plano N° A12
Rubro: CORTES	Revisión: Rev.00	
Tramo:-	Fecha: 07/01/2026 Escala:1:250	

MODIFICACIONES:


REVISION	FECHA	DESCRIPCION
-	-	-
-	-	-
-	-	-
-	-	-
-	-	-
-	-	-
-	-	-
-	-	-
-	-	-
-	-	-

NOTAS: EL PRESENTE PLANO ES INDICATIVO. LA CONTRATISTA CONFECCIONARÁ LOS PLANOS DE DETALLE DEFINITIVO, QUE DEBERÁN SER APROBADOS POR LA D.G.D.IME Y Y LA INSPECCIÓN DE OBRA. EL PLANO PRESENTADO POR LA CONTRATISTA ESTARÁ EN UN TODO DE ACUERDO CON LA NORMATIVA VIGENTE
TODAS LAS MEDIDAS Y NIVELES DEBERÁN SER VERIFICADOS POR EL CONTRATISTA

PLANO NO APTO PARA CONSTRUCCIÓN

PLANO-2026-06751823-GCABA-DGPRO

CONSTITUCION - PROYECTO_Playa de regulación 1

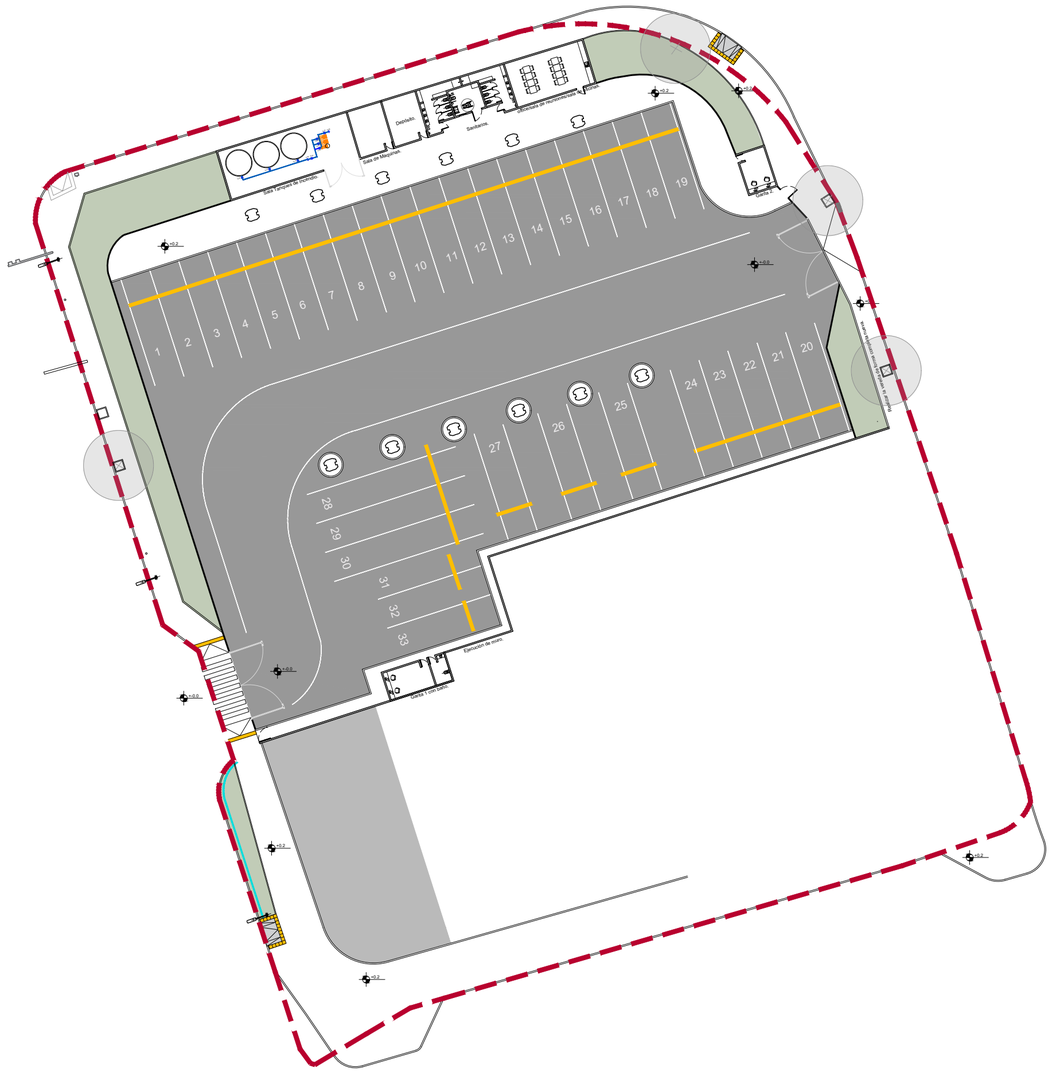

REFERENCIAS

- Edificios existentes importantes
- Áreas verdes existentes
- Árboles existentes
- Límite cordon existente
- Proyección de la Autopista
- Columnas Autopista
- Semáforos Existentes
- Demarcación Existente
- Vados Existentes
- Luminaria Existente
- Demarcador de carril "Tortuga" Existente
- Puntato Existente
- Paradores Existentes
- Accesos Vehiculares existentes
- Bicisenda Existente
- Bancos Existente
- Planteras Existentes
- Sumideros Existentes
- Áreas verdes nuevas
- Demarcación Nueva
- Reja o elemento a definir - impide el paso
- Barandas Paradores
- Cordón Simple montante nuevo
- Cordón Doble montante nuevo
- Baldosas Táctiles 40x40
- Baldosas Guias 40x40
- Juego TA-TE-TI
- Cazoleta Existente con cubre cazoleta nuevo
- Rayuela Pintada
- Calzada
- Luminarias Nuevas
- Obrador Linea F
- Vado Nuevo

ÁREA DE INTERVENCIÓN

Gobierno de la Ciudad de Buenos Aires

MINISTERIO DE MOVILIDAD E INFRAESTRUCTURA
SUBSECRETARIA DE PROYECTOS Y OBRAS
DIRECCION GENERAL DE PROYECTOS

DGPRO

Obra: CT CONSTITUCION	Plano: CTC_ARQ_Playa de regulación 1	Plano N° A08
Rubro: ARQUITECTURA	Revisión: Rev.00	
Tramo:-	Fecha: 07/01/2026	Escala: -

MODIFICACIONES:


REVISION	FECHA	DESCRIPCION
-	-	-
-	-	-
-	-	-
-	-	-
-	-	-
-	-	-
-	-	-
-	-	-

NOTAS: EL PRESENTE PLANO ES INDICATIVO. LA CONTRATISTA CONFECCIONARÁ LOS PLANOS DE DETALLE DEFINITIVO, QUE DEBERÁN SER APROBADOS POR LA D.G.CYM Y Y LA INSPECCIÓN DE OBRA. EL PLANO PRESENTADO POR LA CONTRATISTA ESTARÁ EN UN TODO DE ACUERDO CON LA NORMATIVA VIGENTE.
TODAS LAS MEDIDAS DEBEN SER VERIFICADAS EN OBRA POR EL CONTRATISTA

PLANO NO APTO PARA CONSTRUCCIÓN

PLANO-2026-06751823-GCABA-DGPRO


CONSTITUCION - PROYECTO_Av. Hornos

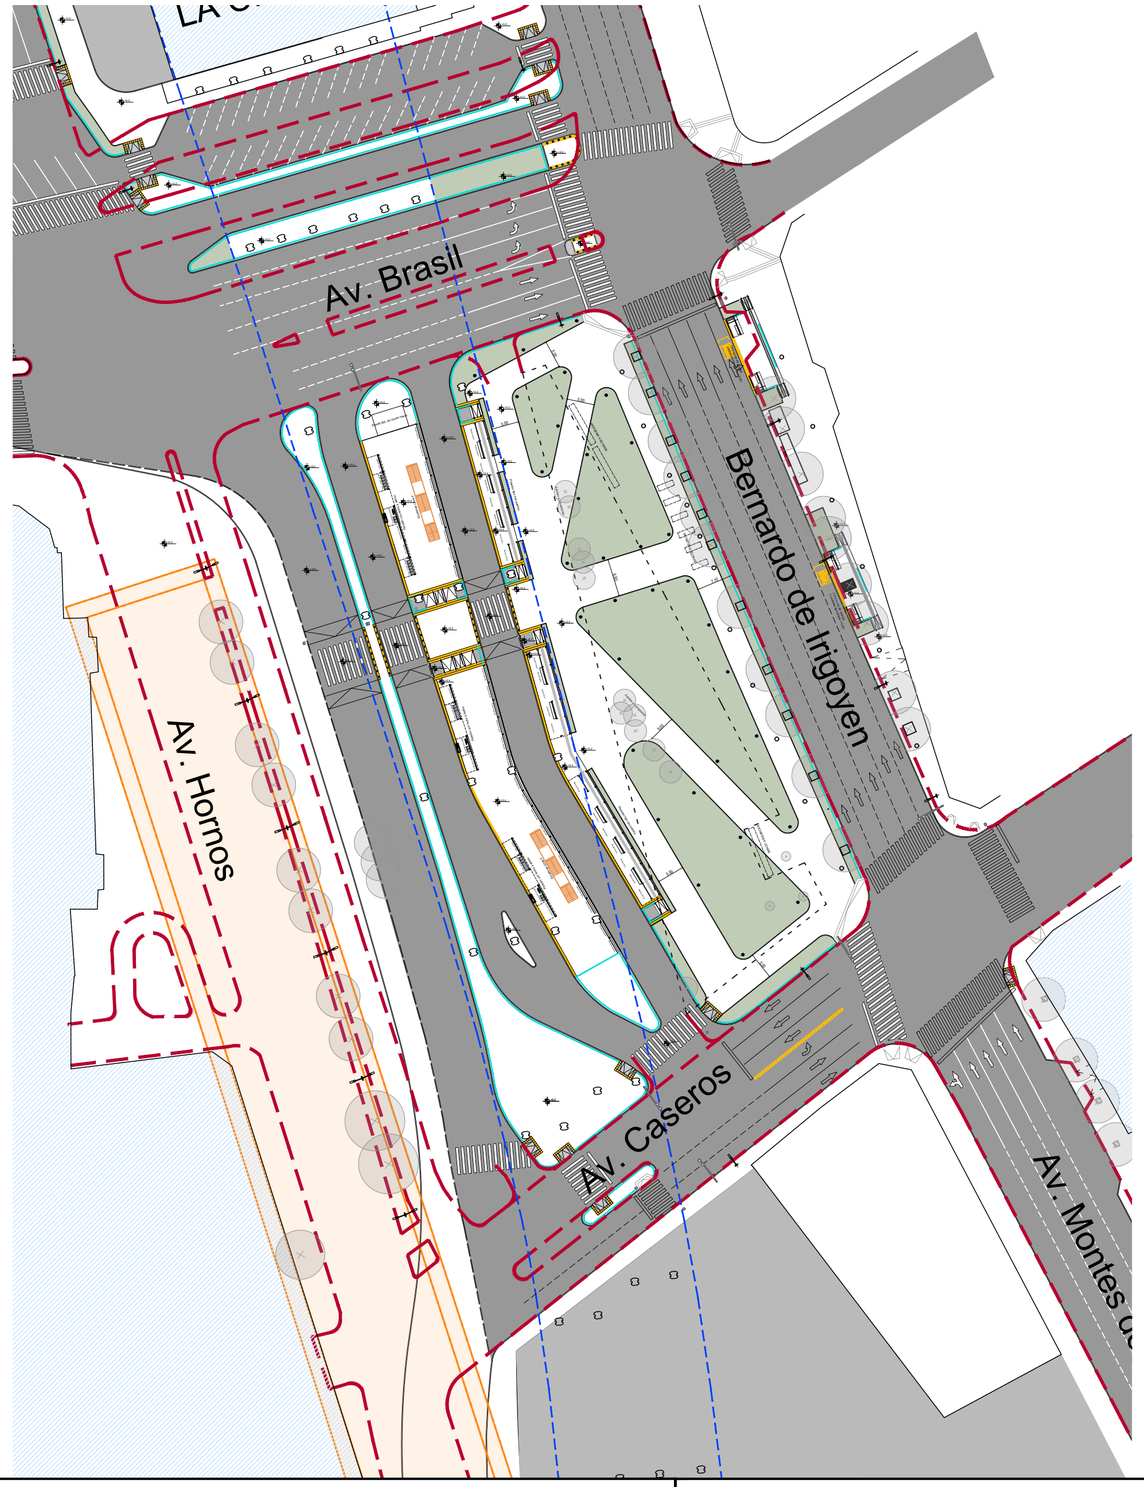

REFERENCIAS

- Edificios existentes importantes
- Áreas verdes existentes
- Árboles existentes
- Límite cordon existente
- Proyección de la Autopista
- Columnas Autopista
- Semáforos Existentes
- Demarcación Existente
- Vados Existentes
- Luminaria Existente
- Demarcador de carril "Tortuga" Existente
- Puesto Existente
- Paradores Existentes
- Accesos Vehiculares existentes
- Bicisenda Existente
- Bancos Existente
- Planteras Existentes
- Sumideros Existentes
- Áreas verdes nuevas
- Demarcación Nueva
- Reja o elemento a definir - impide el paso
- Barandas Paradores
- Cordón Simple montante nuevo
- Cordón Doble montante nuevo
- Baldosas Táctiles 40x40
- Baldosas Guias 40x40
- Juego TA-TE-TI
- Cazoleta Existente con cubre cazoleta nuevo
- Rayuela Pintada
- Calzada
- Luminarias Nuevas
- Obrador Linea F
- Vado Nuevo

ÁREA DE INTERVENCIÓN

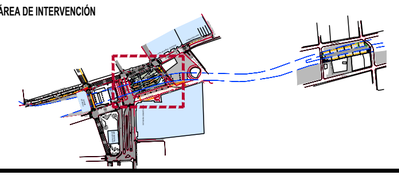

Gobierno de la Ciudad de Buenos Aires

MINISTERIO DE MOVILIDAD E INFRAESTRUCTURA
SUBSECRETARIA DE PROYECTOS Y OBRAS
DIRECCION GENERAL DE PROYECTOS

DGPRO

Obra: CT CONSTITUCION	Plano: CTC_ARQ_Av. Hornos	Plano N° A9
Rubro: ARQUITECTURA	Revisión: Rev.00	
Tramo:-	Fecha: 07/01/2026	Escala:-

MODIFICACIONES:


REVISION	FECHA	DESCRIPCION
-	-	-
-	-	-
-	-	-
-	-	-
-	-	-
-	-	-
-	-	-
-	-	-

NOTAS: EL PRESENTE PLANO ES INDICATIVO. LA CONTRATISTA CONFECCIONARA LOS PLANOS DE DETALLE DEFINITIVO, QUE DEBERAN SER APROBADOS POR LA D.G.O.INF.U Y LA INSPECCION DE OBRA. EL PLANO PRESENTADO POR LA CONTRATISTA ESTARA EN UN TODO DE ACUERDO CON LA NORMATIVA VIGENTE

PLANO-2026-06751823-GCABA-DGPRO

PLANO NO APTO PARA CONSTRUCCIÓN


CONSTITUCION - PROYECTO_Av. Montes de Oca

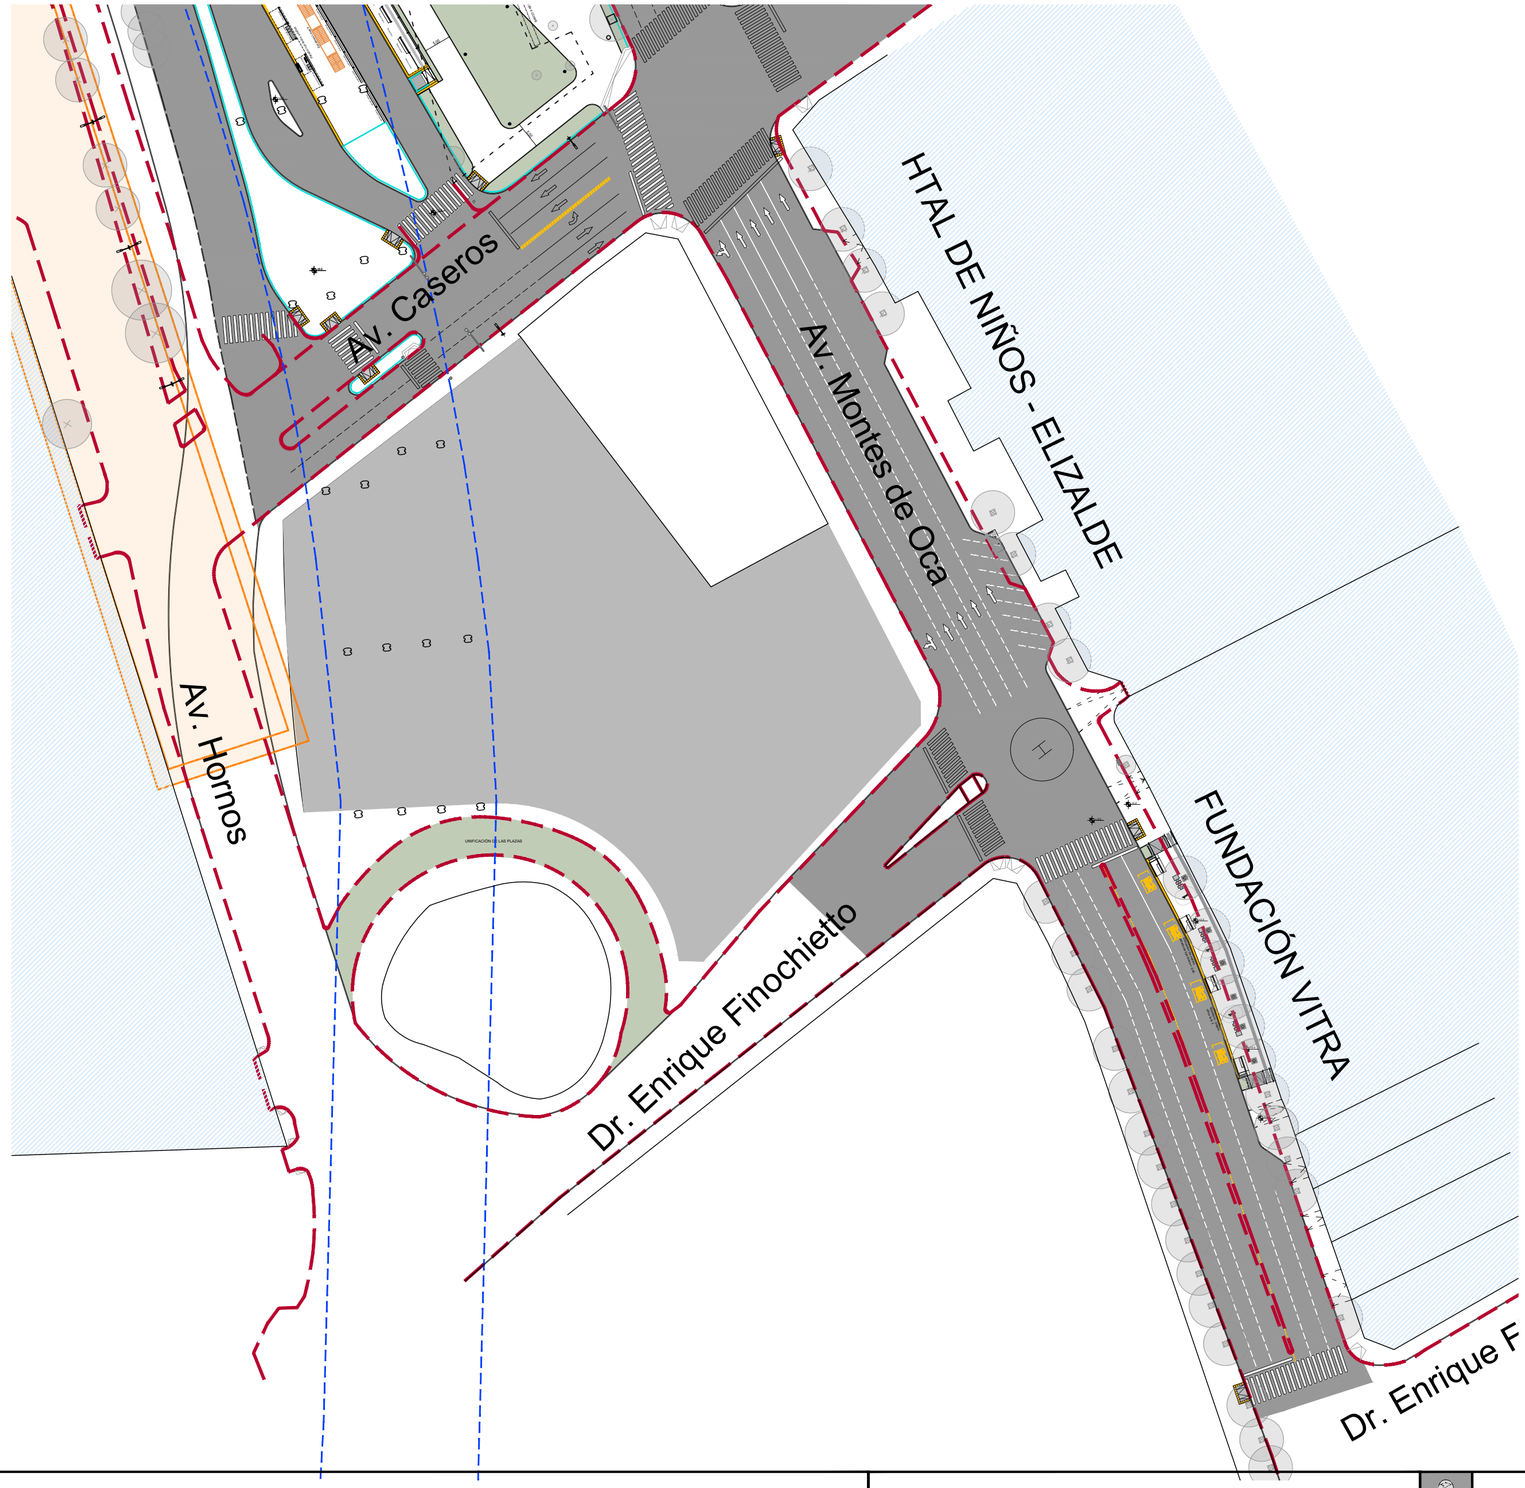

REFERENCIAS

- Edificios existentes importantes
- Áreas verdes existentes
- Árboles existentes
- Límite cordon existente
- Proyección de la Autopista
- Columnas Autopista
- Semáforos Existentes
- Demarcación Existente
- Vados Existentes
- Luminaria Existente
- Demarcador de carril "Tortuga" Existente
- Puesto Existente
- Paradores Existentes
- Accesos Vehiculares existentes
- Bicisenda Existente
- Bancos Existente
- Planteras Existentes
- Sumideros Existentes
- Áreas verdes nuevas
- Demarcación Nueva
- Reja o elemento a definir - impide el paso
- Barandas Paradores
- Cordón Simple montante nuevo
- Cordón Doble montante nuevo
- Baldosas Táctiles 40x40
- Baldosas Guias 40x40
- Juego TA-TE-TI
- Cazoleta Existente con cubre cazoleta nuevo
- Rayuela Pintada
- Calzada
- Luminarias Nuevas
- Obrador Linea F
- Vado Nuevo

ÁREA DE INTERVENCIÓN

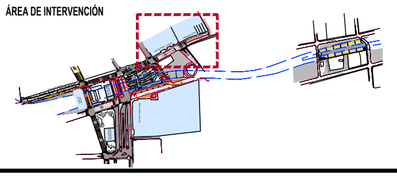

Gobierno de la Ciudad de Buenos Aires

MINISTERIO DE MOVILIDAD E INFRAESTRUCTURA
SUBSECRETARIA DE PROYECTOS Y OBRAS
DIRECCION GENERAL DE PROYECTOS

DGPRO

Obra: CT CONSTITUCION	Plano: CTC_ARQ_Av. Montes de Oca 1	Plano N° A10
Rubro: ARQUITECTURA	Revisión: Rev.00	
Tramo:-	Fecha: 07/01/2026 Escala:-	

MODIFICACIONES:


REVISION	FECHA	DESCRIPCION
-	-	-
-	-	-
-	-	-
-	-	-
-	-	-
-	-	-
-	-	-
-	-	-

NOTAS: EL PRESENTE PLANO ES INDICATIVO. LA CONTRATISTA CONFECCIONARA LOS PLANOS DE DETALLE DEFINITIVO, QUE DEBERAN SER APROBADOS POR LA D.G.C.U.M.I. Y LA INSPECCION DE OBRA. EL PLANO PRESENTADO POR LA CONTRATISTA ESTARA EN UN TODO DE ACUERDO CON LA NORMATIVA VIGENTE
TODAS LAS MEDIDAS DEBERAN SER VERIFICADAS EN OBRA POR EL CONTRATISTA

PLANO NO APTO PARA CONSTRUCCIÓN

PLANO-2026-06751823-GCABA-DGPRO


CONSTITUCION - PROYECTO__Playa de regulación 2

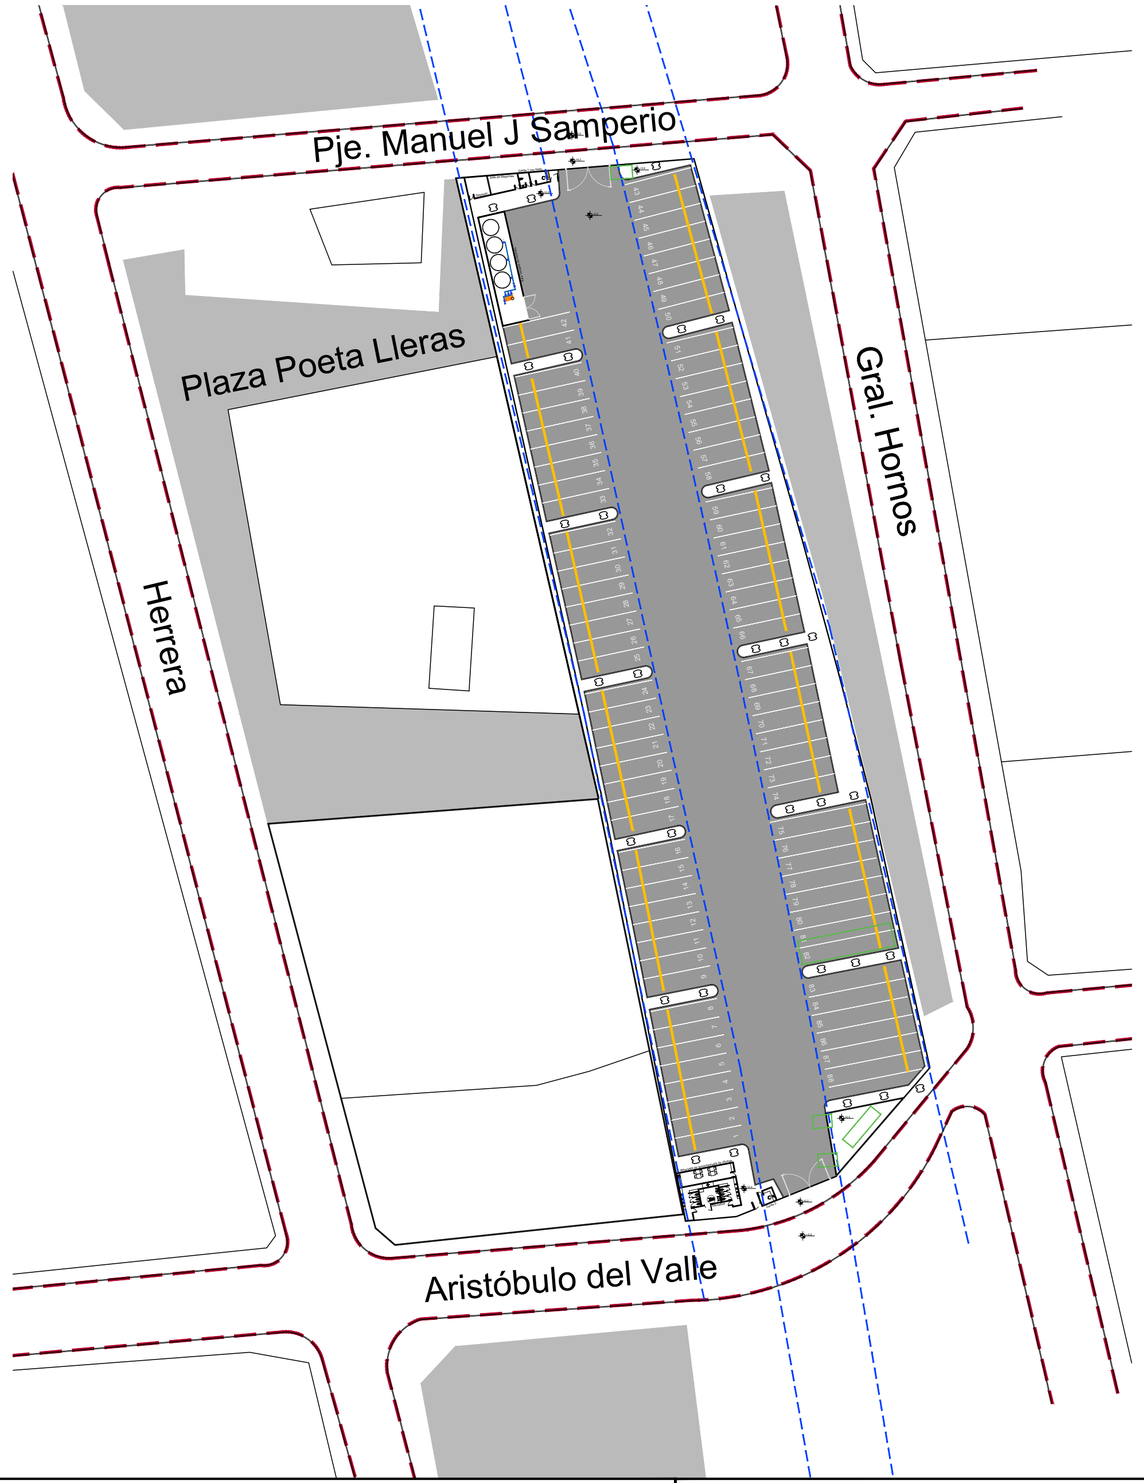

REFERENCIAS

- Edificios existentes importantes
- Áreas verdes existentes
- Árboles existentes
- Límite cordon existente
- Proyección de la Autopista
- Columnas Autopista
- Semáforos Existentes
- Demarcación Existente
- Vados Existentes
- Luminaria Existente
- Demarcador de carril "Tortuga" Existente
- Puesto Existente
- Paradores Existentes
- Accesos Vehiculares existentes
- Bicisenda Existente
- Bancos Existente
- Planteras Existentes
- Sumideros Existentes
- Áreas verdes existentes
- Demarcación Nueva
- Reja o elemento a definir - impide el paso
- Barandas Paradores
- Cordón Simple montante nuevo
- Cordón Doble montante nuevo
- Baldosas Táctiles 40x40
- Baldosas Guias 40x40
- Juego TA-TE-TI
- Cazoleta Existente con cubre cazoleta nuevo
- Rayuela Pintada
- Calzada
- Luminarias Nuevas
- Obrador Línea F
- Vado Nuevo

ÁREA DE INTERVENCIÓN

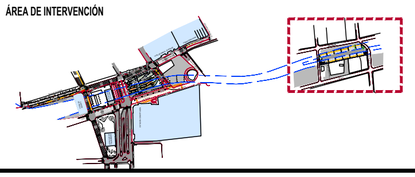

Gobierno de la Ciudad de Buenos Aires

MINISTERIO DE MOVILIDAD E INFRAESTRUCTURA
SUBSECRETARIA DE PROYECTOS Y OBRAS
DIRECCION GENERAL DE PROYECTOS

DGPRO

Obra: CT CONSTITUCION	Plano: CTC_ARQ_Playa de regulación 2	Plano N° A11
Rubro: ARQUITECTURA	Revisión: Rev.00	
Tramo:-	Fecha: 07/01/2026	Escala:-

MODIFICACIONES:

REVISION	FECHA	DESCRIPCION
-	-	-
-	-	-
-	-	-
-	-	-
-	-	-
-	-	-
-	-	-
-	-	-

NOTAS: EL PRESENTE PLANO ES INDICATIVO. LA CONTRATISTA CONFECCIONARÁ LOS PLANOS DE DETALLE DEFINITIVO, QUE DEBERÁN SER APROBADOS POR LA D.G.O.M.Y.U. LA INSPECCIÓN DE OBRA. EL PLANO PRESENTADO POR LA CONTRATISTA ESTARÁ EN UN TODO DE ACUERDO CON LA NORMATIVA VIGENTE.

PLANO-2026-06751823-GCABA-DGPRO

PLANO NO APTO PARA CONSTRUCCIÓN

G O B I E R N O DE LA C I U D A D DE B U E N O S A I R E S

"2026 - Año del 30° Aniversario de la sanción de la Constitución de la Ciudad Autónoma de Buenos Aires"

Hoja Adicional de Firmas
Plano

Número: PLANO-2026-06751823-GCABA-DGPRO

Buenos Aires, Viernes 30 de Enero de 2026

Referencia: ARQUITECTURA

El documento fue importado por el sistema GEDO con un total de 7 pagina/s.

Digitally signed by Comunicaciones Oficiales
Date: 2026.01.30 15:38:58 -03:00

GABRIEL EDUARDO ROSALES
Director General
D. G. PROYECTOS
MINISTERIO DE MOVILIDAD E INFRAESTRUCTURA

Digitally signed by Comunicaciones Oficiales
Date: 2026.01.30 15:39:01 -03:00