

CONSTITUCION - DETALLES_Paradores tipo "Cabildo"


Modulo reja

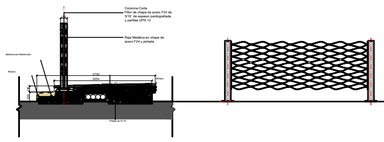


Modulo reja con techo

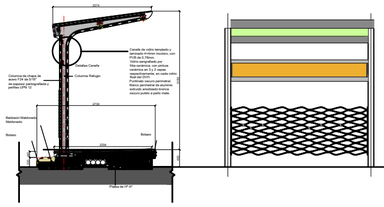


Modulo Infovial

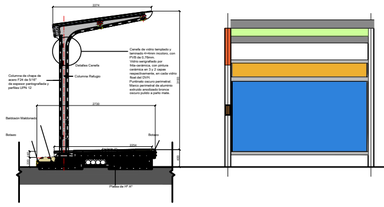

Modulo vidrio con baranda

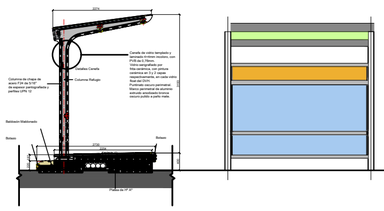

Modulo bancos

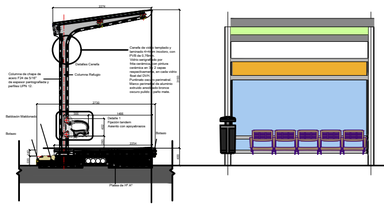


Modulo "Accesibilidad"

Calzada

Colocación de nuevos paradores tipo Modelo Cabildo.


+0.0

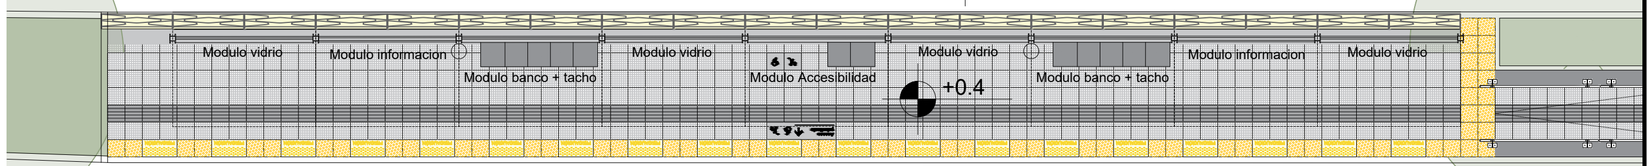


Calzada

+0.0


Colocación de nuevos paradores tipo Modelo Cabildo.

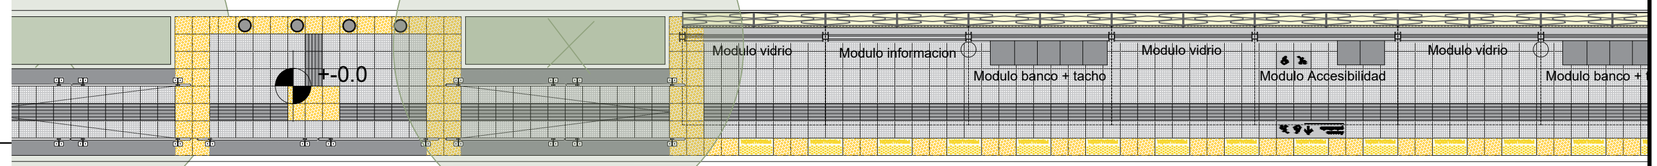

+0.0

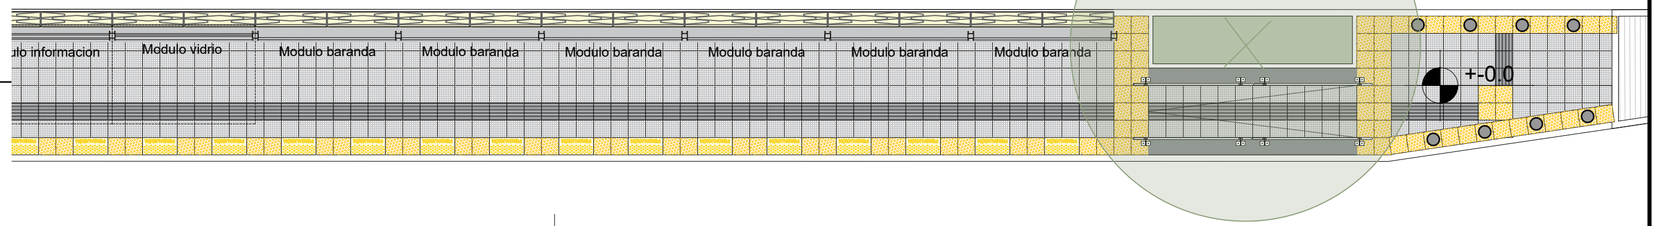

+0.0

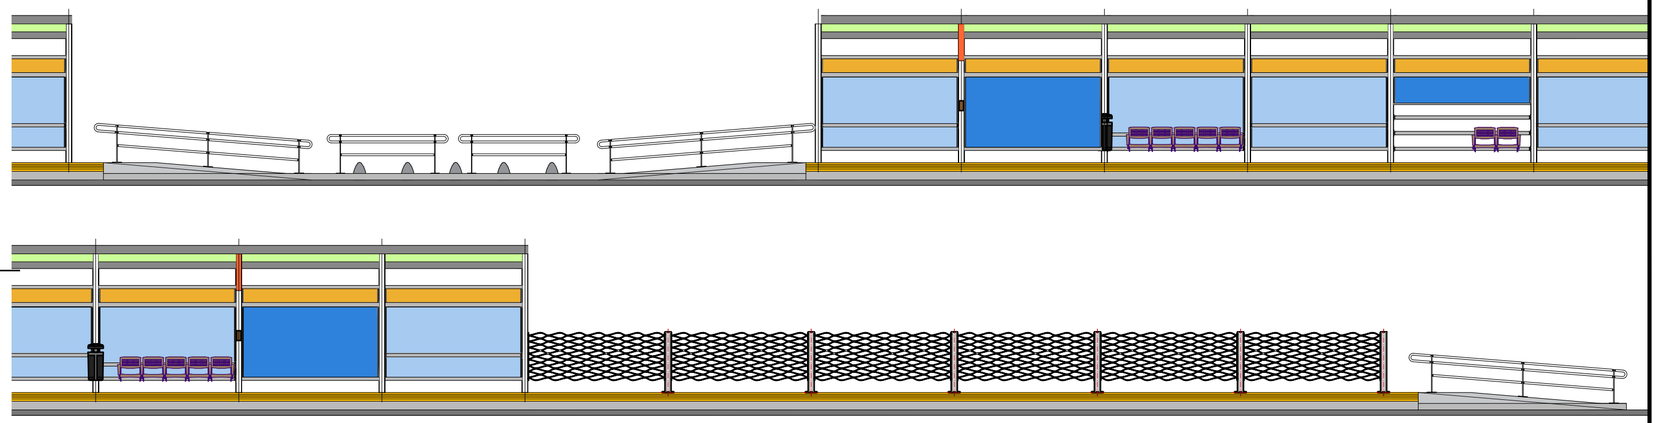

REFERENCIAS

ÁREA DE INTERVENCIÓN

Gobierno de la Ciudad de Buenos Aires	MINISTERIO DE MOVILIDAD E INFRAESTRUCTURA SUBSECRETARIA DE PROYECTOS Y OBRAS **DIRECCION GENERAL DE PROYECTOS**	**DGPRO**	
Obra: CT CONSTITUCION		Plano: CTC_DET_Tipologia A	Plano N° A13
Rubro: DETALLES		Revisión: Rev.00	
Tramo:-		Fecha: 07/01/2026	Escala:-

MODIFICACIONES:


REVISION	FECHA	DESCRIPCION
-	-	-
-	-	-
-	-	-
-	-	-
-	-	-
-	-	-
-	-	-
-	-	-
-	-	-
-	-	-


NOTAS: EL PRESENTE PLANO ES INDICATIVO. LA CONTRATISTA CONFECCIONARA LOS PLANOS DE DETALLE DEFINITIVO, QUE DEBERAN SER APROBADOS POR LA D.G.CINF.U Y LA INSPECCION DE OBRA. EL PLANO PRESENTADO POR LA CONTRATISTA ESTARA EN UN TODO DE ACUERDO CON LA NORMATIVA VIGENTE

PLANO NO APTO PARA CONSTRUCCIÓN


PLANO-2026-06753322-GCABA-DGPRO


Modulo reja

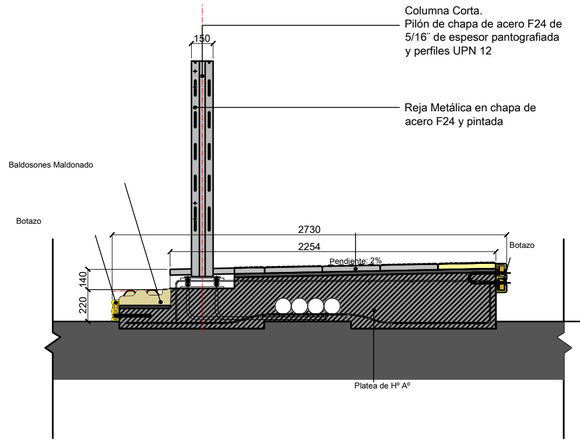

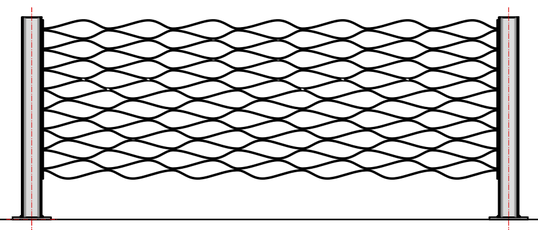

Modulo reja con techo

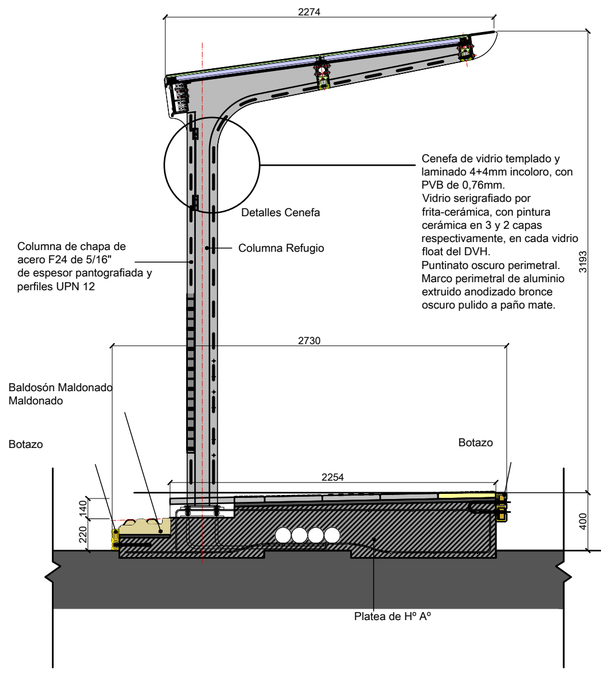

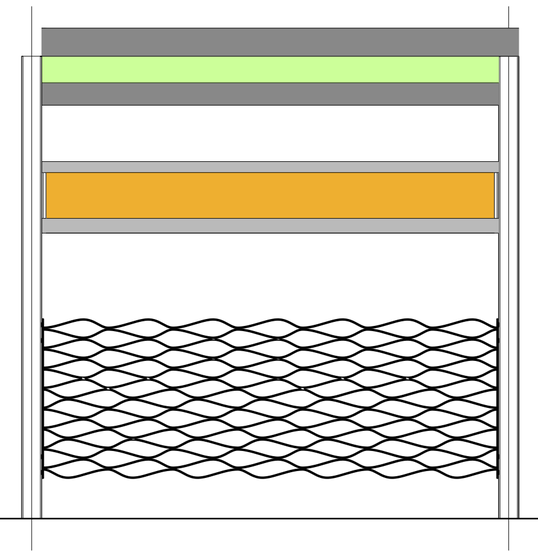

REFERENCIAS

ÁREA DE INTERVENCIÓN

MINISTERIO DE MOVILIDAD E INFRAESTRUCTURA
SUBSECRETARIA DE PROYECTOS Y OBRAS
DIRECCION GENERAL DE PROYECTOS

DGPRO

Obra: CT CONSTITUCION	Plano: CTC_DET_Tipologia A	Plano Nº 13a
Rubro: DETALLES	Revisión: Rev.00	
Tramo:-	Fecha: 07/01/2026 Escala:-	

MODIFICACIONES:


REVISION	FECHA	DESCRIPCION
-	-	
-	-	
-	-	
-	-	
-	-	
-	-	
-	-	
-	-	
-	-	
-	-	


NOTAS: EL PRESENTE PLANO ES INDICATIVO. LA CONTRATISTA CONFECCIONARA LOS PLANOS DE DETALLE DEFINITIVO, QUE DEBERAN SER APROBADOS POR LA D.G.O.INF.U Y LA INSPECCION DE OBRA. EL PLANO PRESENTADO POR LA CONTRATISTA ESTARA EN UN TODO DE ACUERDO CON LA NORMATIVA VIGENTE
TODAS LAS MEDIDAS Y NIVELES DEBERAN SER VERIFICADOS EN OBRA POR LA CONTRATISTA


PLANO NO APTO PARA CONSTRUCCIÓN

PLANO-2026-06753322-GCABA-DGPRO

Modulo bancos

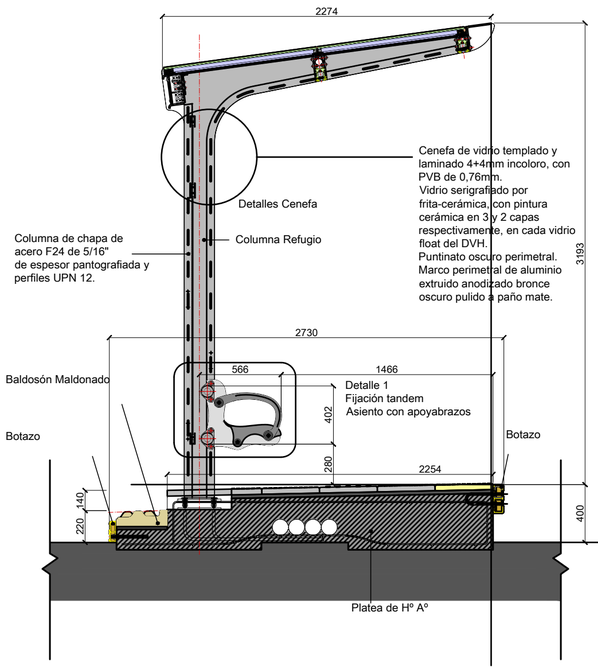

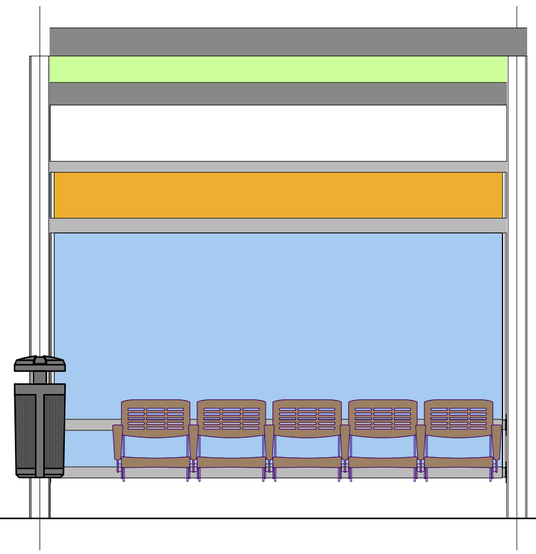

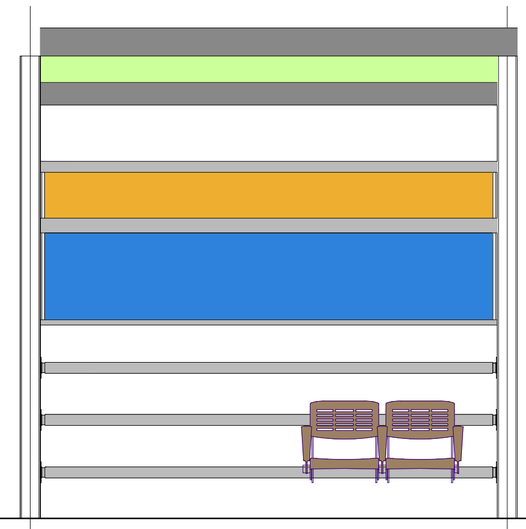

Modulo "Accesibilidad"

REFERENCIAS

ÁREA DE INTERVENCIÓN

MINISTERIO DE MOVILIDAD E INFRAESTRUCTURA
SUBSECRETARIA DE PROYECTOS Y OBRAS
DIRECCION GENERAL DE PROYECTOS

DGPRO

Obra: CT CONSTITUCION	Plano: CTC_DET_Tipologia A	Plano Nº 13b
Rubro: DETALLES	Revisión: Rev.00	
Tramo:-	Fecha: 07/01/2026 Escala: -	

MODIFICACIONES:


REVISION	FECHA	DESCRIPCION
-	-	-


NOTAS: EL PRESENTE PLANO ES INDICATIVO. LA CONTRATISTA CONFECCIONARA LOS PLANOS DE DETALLE DEFINITIVO, QUE DEBERAN SER APROBADOS POR LA D.G.O.INF.U Y LA INSPECCION DE OBRA. EL PLANO PRESENTADO POR LA CONTRATISTA ESTARA EN UN TODO DE ACUERDO CON LA NORMATIVA VIGENTE

PLANO-2026-06753322-GCABA-DGPRO


PLANO NO APTO PARA CONSTRUCCIÓN


Modulo Infovial

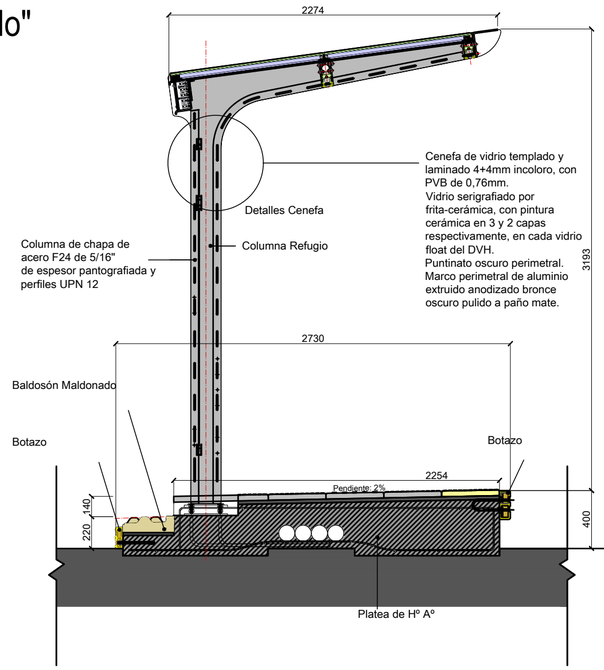

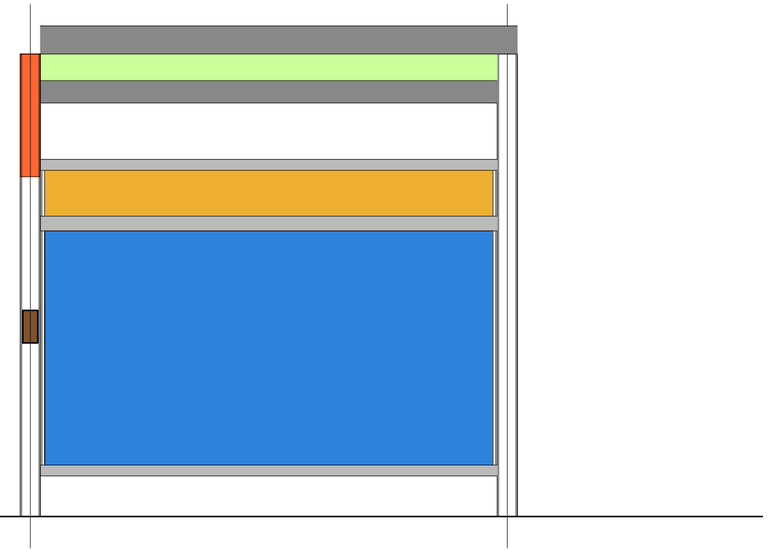

Modulo vidrio con baranda

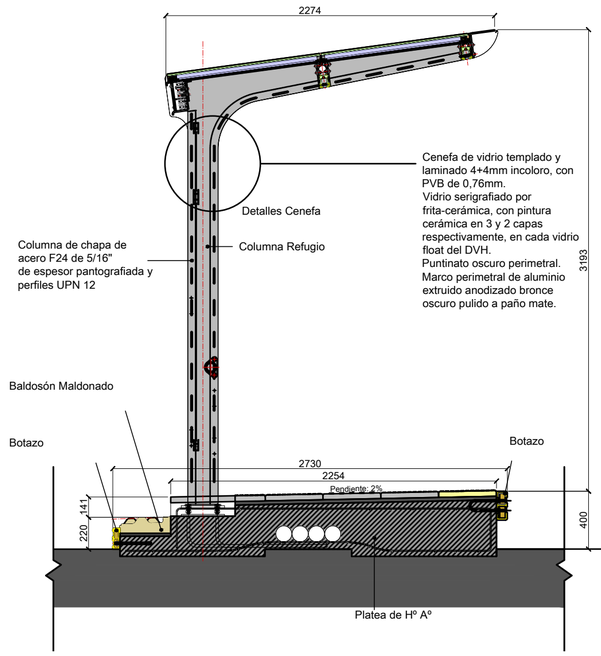

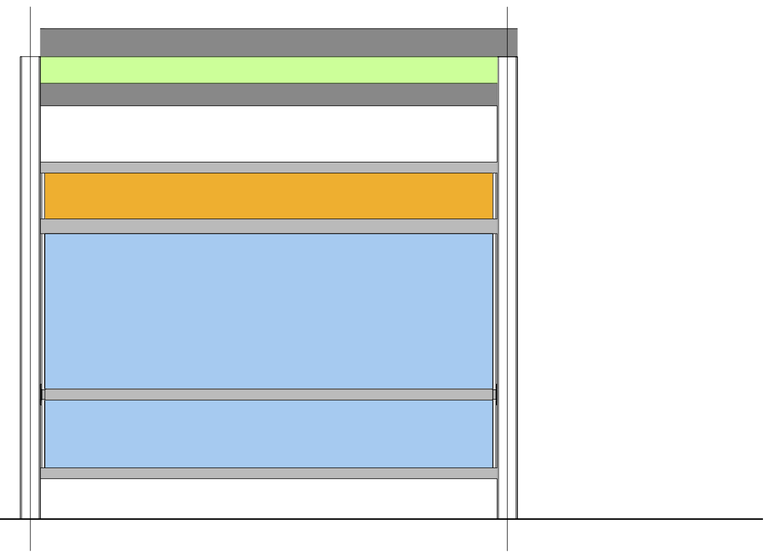

REFERENCIAS

ÁREA DE INTERVENCIÓN

Gobierno de la Ciudad de Buenos Aires

MINISTERIO DE MOVILIDAD E INFRAESTRUCTURA
SUBSECRETARIA DE PROYECTOS Y OBRAS
DIRECCION GENERAL DE PROYECTOS

DGPRO

Obra: CT CONSTITUCION	Plano: CTC_DET_Tipologia A	Plano Nº 13c
Rubro: DETALLES	Revisión: Rev.00	
Tramo:-	Fecha: 07/01/2026	Escala:-

MODIFICACIONES:

REVISION	FECHA	DESCRIPCION
-	-	-
-	-	-
-	-	-
-	-	-
-	-	-
-	-	-
-	-	-
-	-	-
-	-	-
-	-	-


NOTAS: EL PRESENTE PLANO ES INDICATIVO. LA CONTRATISTA CONFECCIONARA LOS PLANOS DE DETALLE DEFINITIVO, QUE DEBERAN SER APROBADOS POR LA D.G.O.M.P. Y LA INSPECCION DE OBRA. EL PLANO PRESENTADO POR LA CONTRATISTA ESTARA EN UN TODO DE ACUERDO CON LA NORMATIVA VIGENTE.

PLANO-2026-06753322-GCABA-DGPRO


PLANO NO APTO PARA CONSTRUCCIÓN

CONSTITUCION - DETALLES_Paradores Tipo "San Pedrito"


Modulo reja

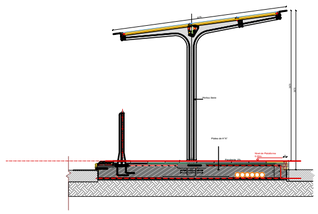


Modulo abierto sin baranda

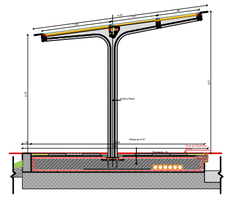


Modulo infovial

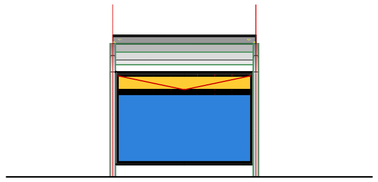

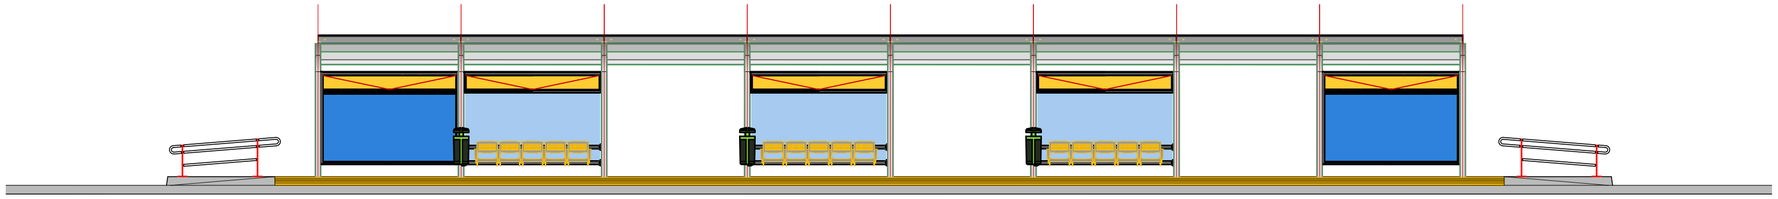

Modulo libre

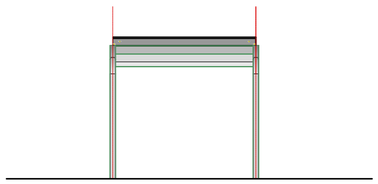

Vereda

+0.2

+0.2

+0.2

Parador tipo san pedrito +0,4

+0.2

+0.2

Modulo infovial | Modulo bancos | Modulo libre | Modulo bancos | Modulo libre | Modulo bancos | Modulo libre | Modulo infovial


+0.4

+0.4

+0.0

Calzada

Modulo bancos

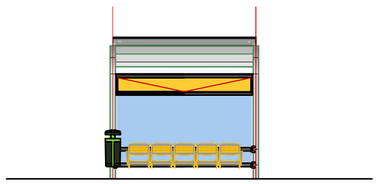

REFERENCIAS

ÁREA DE INTERVENCIÓN

Gobierno de la Ciudad de Buenos Aires

MINISTERIO DE MOVILIDAD E INFRAESTRUCTURA
SUBSECRETARIA DE PROYECTOS Y OBRAS
DIRECCION GENERAL DE PROYECTOS

DGPRO

Obra: CT CONSTITUCION	Plano: CTC_DET_Tipologia B	Plano N° A14
Rubro: DETALLES	Revisión: Rev.00	
Tramo:-	Fecha: 07/01/2026	Escala:-

MODIFICACIONES:


REVISION	FECHA	DESCRIPCION
-	-	-

NOTAS: EL PRESENTE PLANO ES INDICATIVO. LA CONTRATISTA CONFECCIONARA LOS PLANOS DE DETALLE DEFINITIVO, QUE DEBERAN SER APROBADOS POR LA D.G.DGPRO Y LA INSPECCION DE OBRA. EL PLANO PRESENTADO POR LA CONTRATISTA ESTARA EN UN TODO DE ACUERDO CON LA NORMATIVA VIGENTE.


PLANO-2026-06753322-GCABA-DGPRO

PLANO NO APTO PARA CONSTRUCCIÓN

Modulo reja

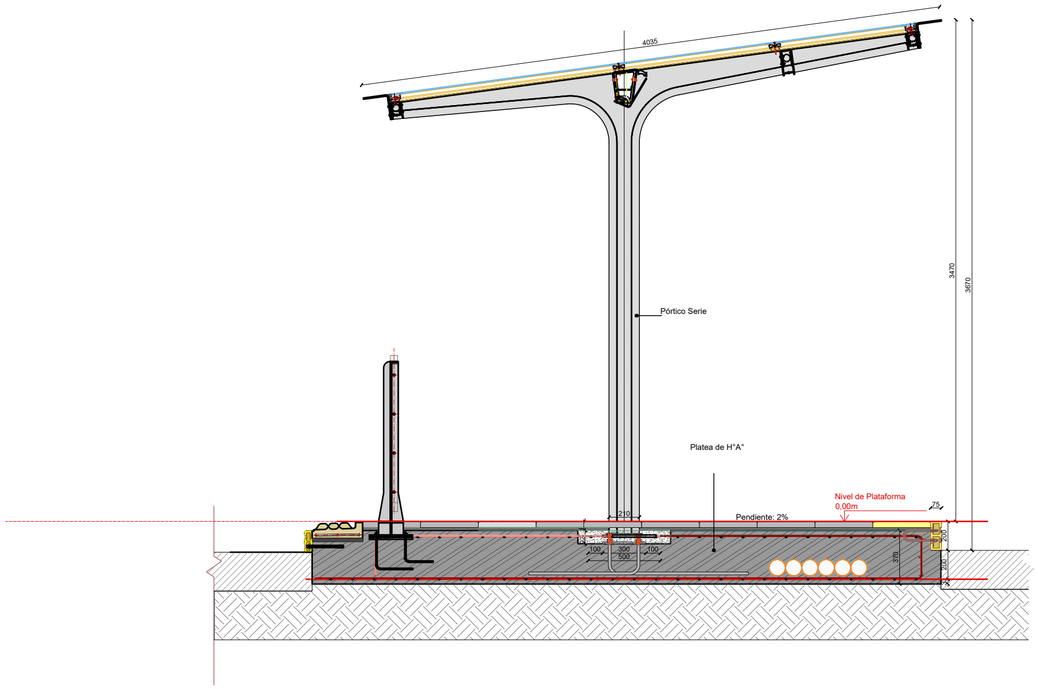

Modulo abierto sin baranda

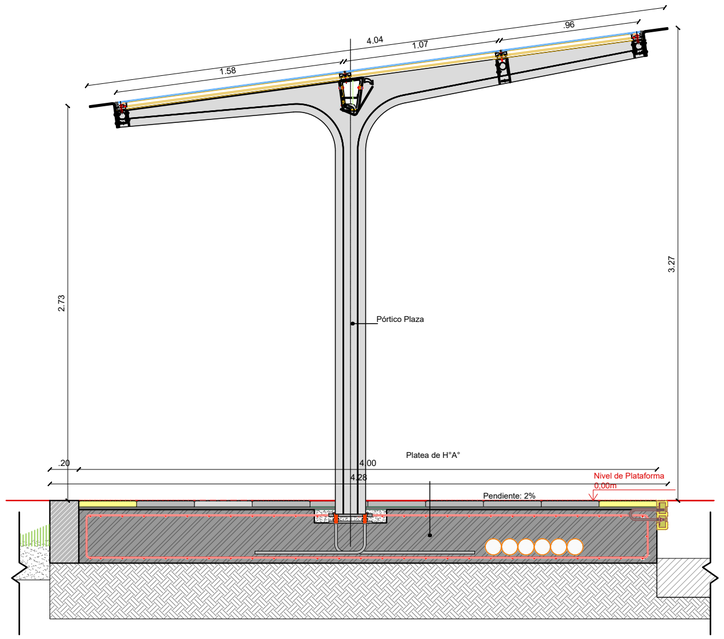

REFERENCIAS

ÁREA DE INTERVENCIÓN

Gobierno de la Ciudad de Buenos Aires

MINISTERIO DE MOVILIDAD E INFRAESTRUCTURA
SUBSECRETARIA DE PROYECTOS Y OBRAS
DIRECCION GENERAL DE PROYECTOS

DGPRO

Obra: CT CONSTITUCION	Plano: CTC_DET_Tipologia B	Plano N°: 14a
Rubro: DETALLES	Revisión: Rev.00	
Tramo:-	Fecha: 07/01/2026	Escala:-

MODIFICACIONES:


REVISION	FECHA	DESCRIPCION
-	-	-
-	-	-
-	-	-
-	-	-
-	-	-
-	-	-
-	-	-
-	-	-
-	-	-

NOTAS: EL PRESENTE PLANO ES INDICATIVO. LA CONTRATISTA CONFECCIONARA LOS PLANOS DE DETALLE DEFINITIVO, QUE DEBERAN SER APROBADOS POR LA D.G.O.INF.U Y LA INSPECCION DE OBRA. EL PLANO PRESENTADO POR LA CONTRATISTA ESTARA EN UN TODO DE ACUERDO CON LA NORMATIVA VIGENTE


PLANO NO APTO PARA CONSTRUCCIÓN

PLANO-2026-06753322-GCABA-DGPRO


Modulo infovial

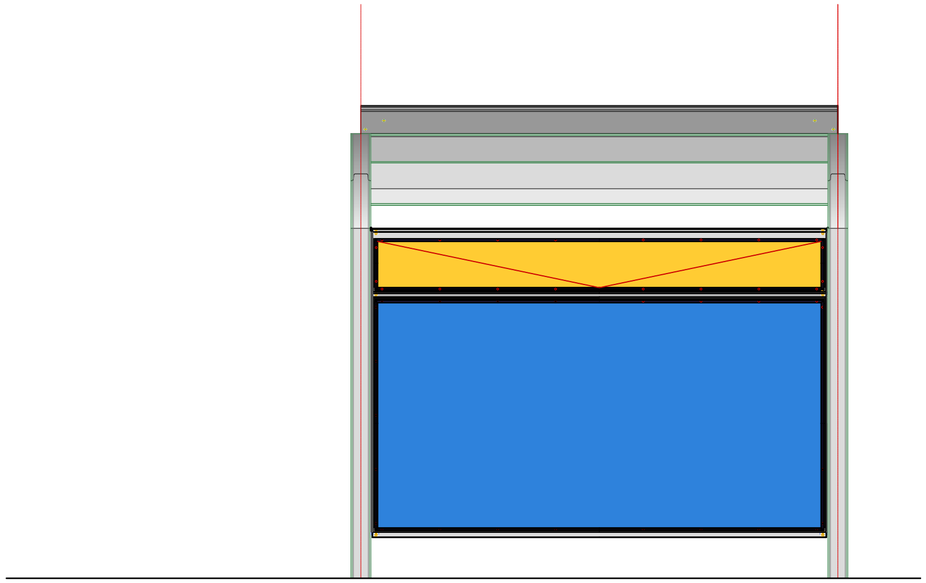

Modulo libre

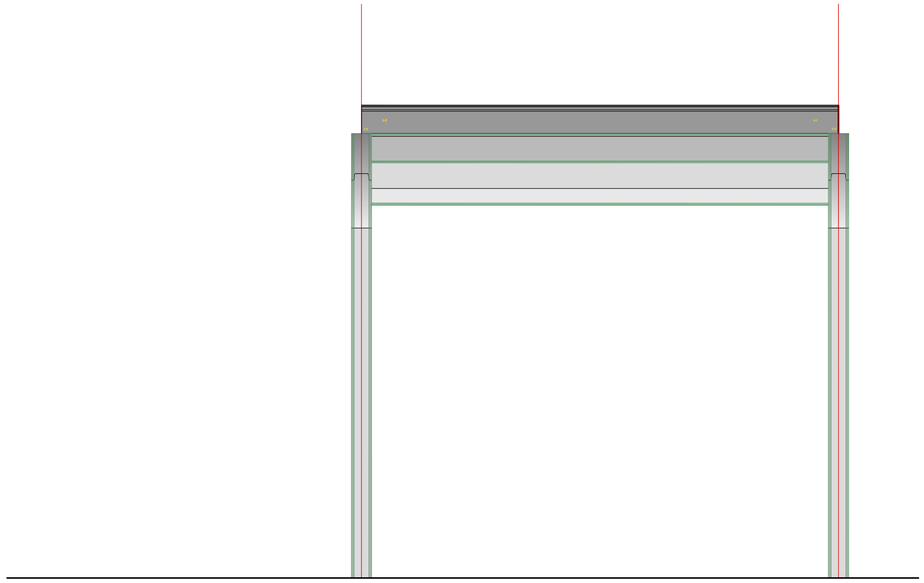

Modulo bancos

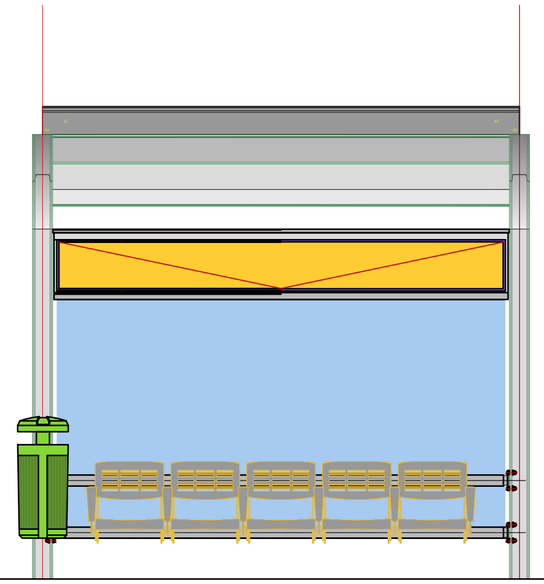

REFERENCIAS

ÁREA DE INTERVENCIÓN

Gobierno de la Ciudad de Buenos Aires

MINISTERIO DE MOVILIDAD E INFRAESTRUCTURA
SUBSECRETARIA DE PROYECTOS Y OBRAS
DIRECCION GENERAL DE PROYECTOS

DGPRO

Obra: CT CONSTITUCION	Plano: CTC_DET_Tipologia B	Plano Nº 14b
Rubro: DETALLES	Revisión: Rev.00	
Tramo: -	Fecha: 07/01/2026	Escala: -

MODIFICACIONES:


REVISION	FECHA	DESCRIPCION
-	-	-
-	-	-
-	-	-
-	-	-
-	-	-
-	-	-
-	-	-
-	-	-
-	-	-
-	-	-


NOTAS: EL PRESENTE PLANO ES INDICATIVO. LA CONTRATISTA CONFECCIONARÁ LOS PLANOS DE DETALLE DEFINITIVO, QUE DEBERÁN SER APROBADOS POR LA D.G.CIM Y LA INSPECCIÓN DE OBRA. EL PLANO PRESENTADO POR LA CONTRATISTA ESTARÁ EN UN TODO DE ACUERDO CON LA NORMATIVA VIGENTE.


PLANO-2026-06753322-GCABA-DGPRO


PLANO NO APTO PARA CONSTRUCCIÓN


CONSTITUCION - DETALLES_Paradores tipo "Liniers"

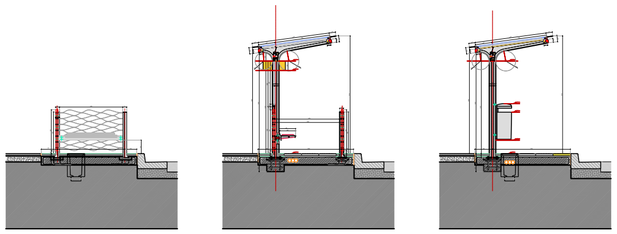

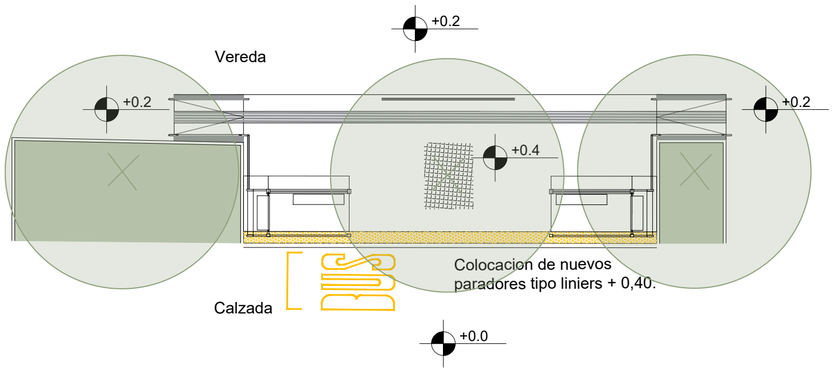

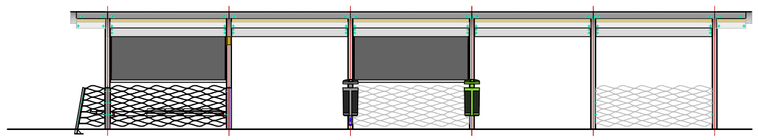

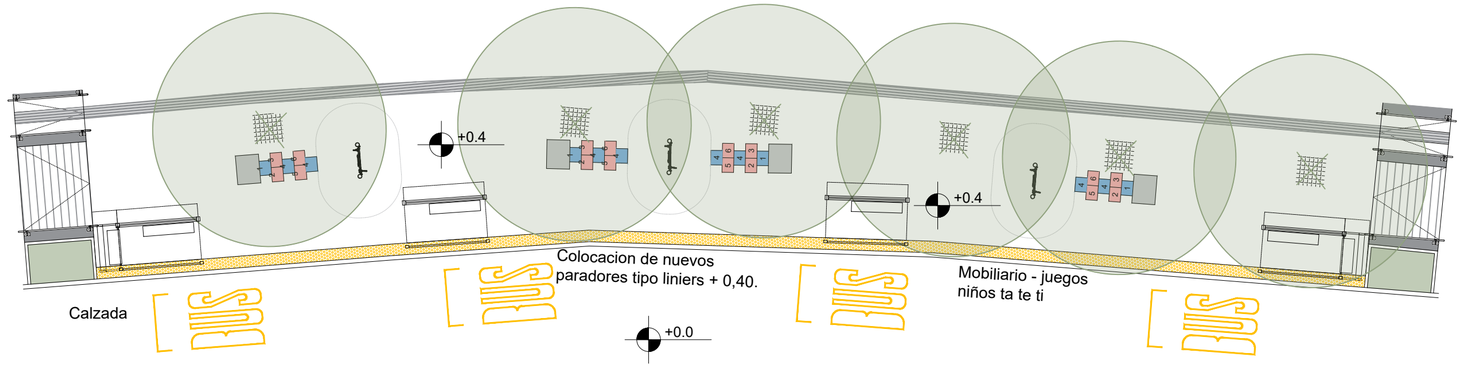

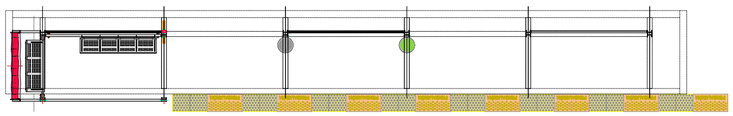

REFERENCIAS

ÁREA DE INTERVENCIÓN

Gobierno de la Ciudad de Buenos Aires

MINISTERIO DE MOVILIDAD E INFRAESTRUCTURA
SUBSECRETARIA DE PROYECTOS Y OBRAS
DIRECCION GENERAL DE PROYECTOS

DGPRO

Obra: CT CONSTITUCION	Plano: CTC_DET_Tipologia C	Plano N° A15
Rubro: DETALLES	Revisión: Rev.00	
Tramo:-	Fecha: 07/01/2026 Escala:-	

MODIFICACIONES:


REVISION	FECHA	DESCRIPCION
-	-	-
-	-	-
-	-	-
-	-	-
-	-	-
-	-	-
-	-	-
-	-	-
-	-	-
-	-	-


NOTAS: EL PRESENTE PLANO ES INDICATIVO. LA CONTRATISTA CONFECCIONARA LOS PLANOS DE DETALLE DEFINITIVO, QUE DEBERAN SER APROBADOS POR LA D.G.CMF Y LA INSPECCION DE OBRA. EL PLANO PRESENTADO POR LA CONTRATISTA ESTARA EN UN TODO DE ACUERDO CON LA NORMATIVA VIGENTE.


PLANO-2026-06753322-GCABA-DGPRO


PLANO NO APTO PARA CONSTRUCCIÓN

CONSTITUCION - DETALLES_Paradores tipo "Liniers"

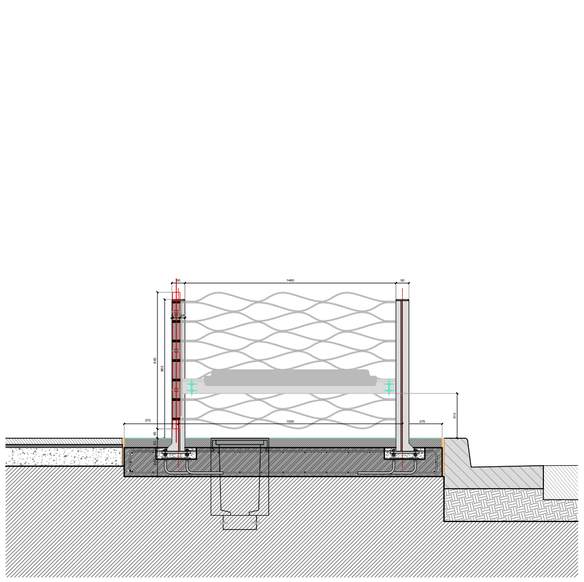

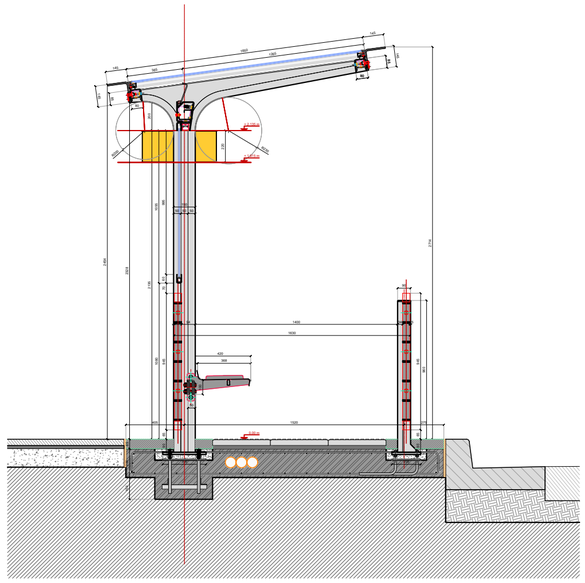

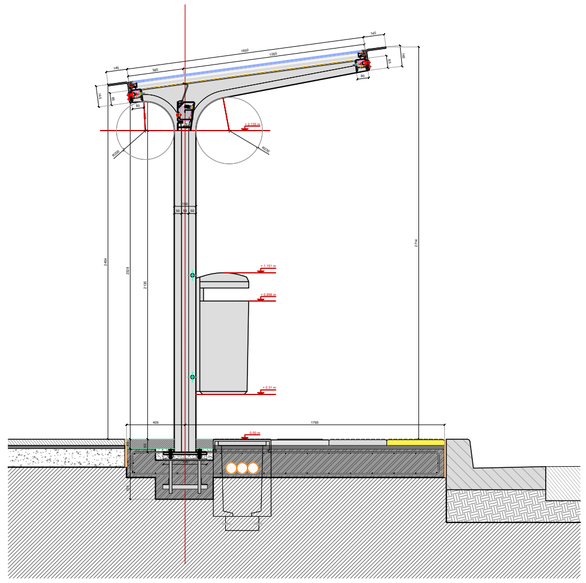

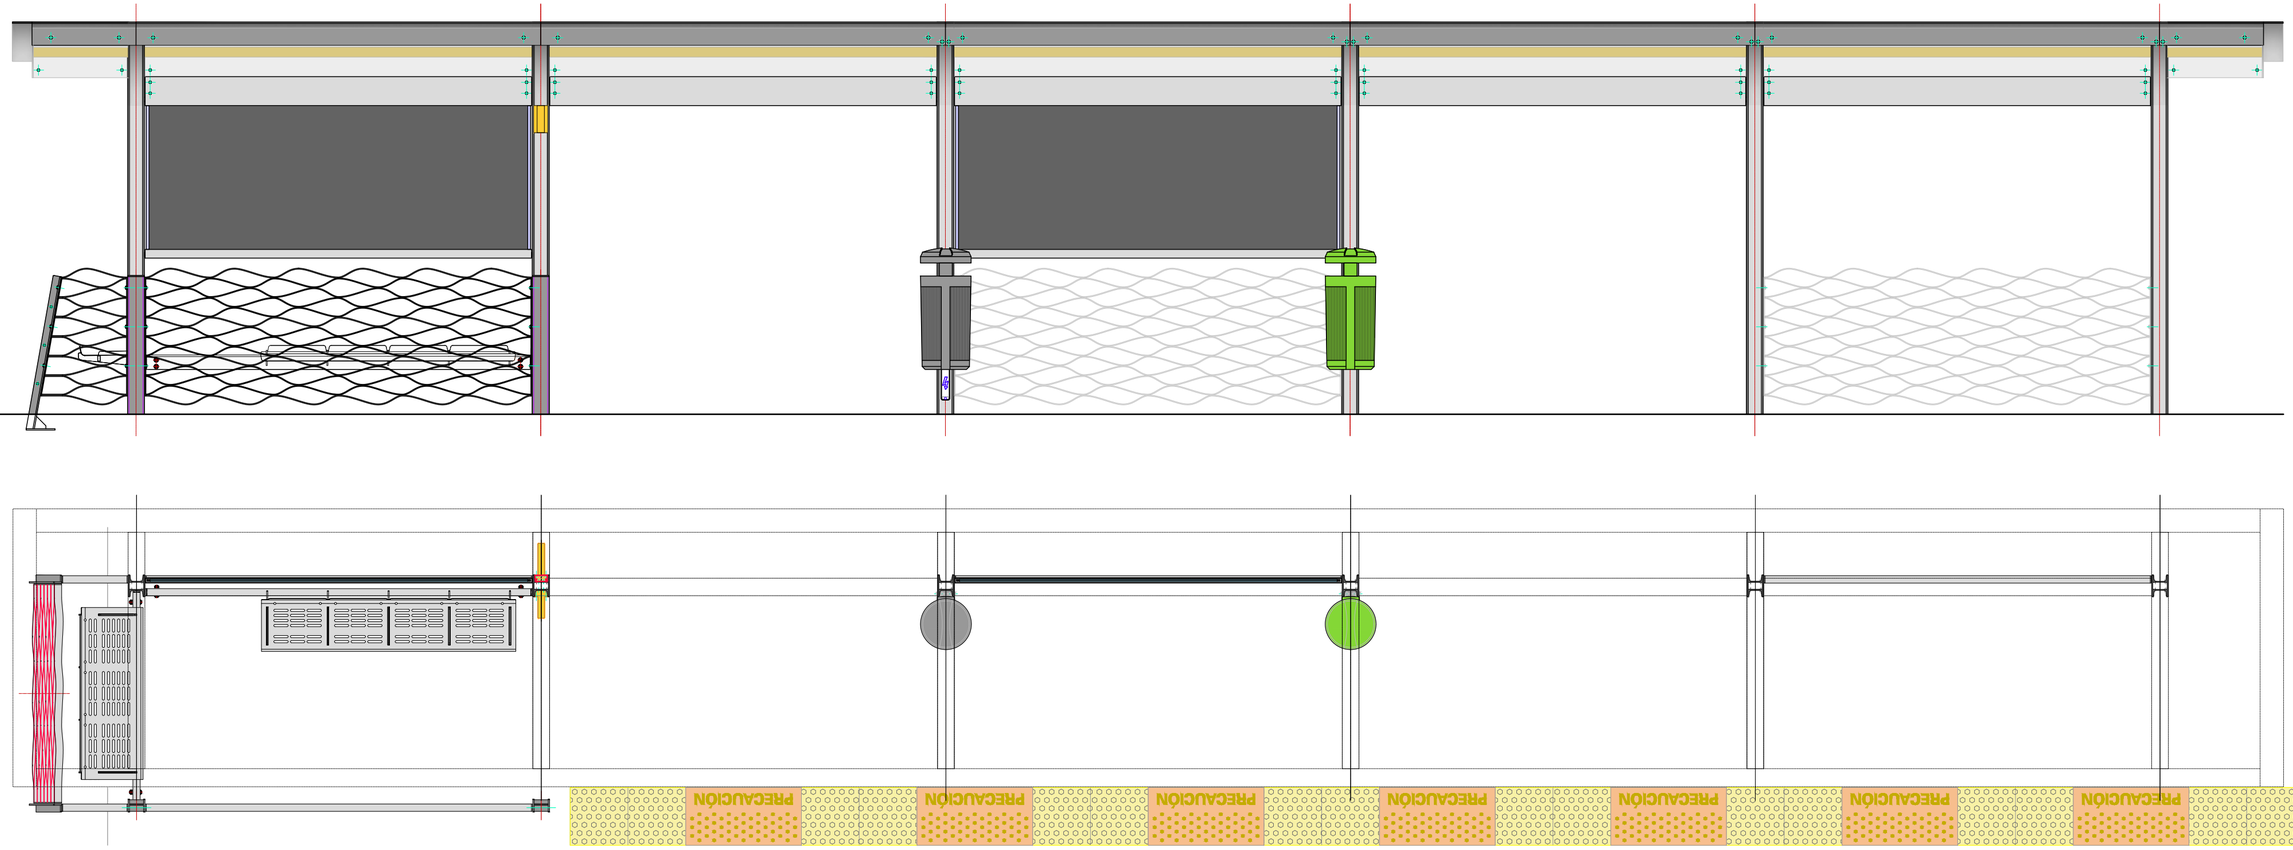

PRECAUCION PRECAUCION PRECAUCION PRECAUCION PRECAUCION PRECAUCION PRECAUCION PRECAUCION PRECAUCION PRECAUCION

REFERENCIAS

ÁREA DE INTERVENCIÓN

Gobierno de la Ciudad de Buenos Aires

MINISTERIO DE MOVILIDAD E INFRAESTRUCTURA
SUBSECRETARIA DE PROYECTOS Y OBRAS
DIRECCION GENERAL DE PROYECTOS

DGPRO

Obra: CT CONSTITUCION	Plano: CTC_DET_Tipologia C	Plano N° 15a
Rubro: DETALLES	Revisión: Rev.00	
Tramo: -	Fecha: 07/01/2026	Escala: -

MODIFICACIONES:

REVISION	FECHA	DESCRIPCION
-	-	-
-	-	-
-	-	-
-	-	-
-	-	-
-	-	-
-	-	-
-	-	-
-	-	-
-	-	-

NOTAS: EL PRESENTE PLANO ES INDICATIVO. LA CONTRATISTA CONFECCIONARA LOS PLANOS DE DETALLE DEFINITIVO, QUE DEBERAN SER APROBADOS POR LA D.G.C.U.M.I. Y / O LA INSPECCION DE OBRA. EL PLANO PRESENTADO POR LA CONTRATISTA ESTARA EN UN TODO DE ACUERDO CON LA NORMATIVA VIGENTE
TODAS LAS MEDIDAS A SER VERIFICADAS EN EL LUGAR POR EL CONTRATISTA

PLANO NO APTO PARA CONSTRUCCIÓN

PLANO-2026-06753322-GCABA-DGPRO

G O B I E R N O DE LA C I U D A D DE B U E N O S A I R E S

"2026 - Año del 30° Aniversario de la sanción de la Constitución de la Ciudad Autónoma de Buenos Aires"

Hoja Adicional de Firmas
Plano

Número: PLANO-2026-06753322-GCABA-DGPRO

Buenos Aires, Viernes 30 de Enero de 2026

Referencia: DETALLE DE PARADORES

El documento fue importado por el sistema GEDO con un total de 9 pagina/s.

Digitally signed by Comunicaciones Oficiales
Date: 2026.01.30 15:43:39 -03:00

GABRIEL EDUARDO ROSALES
Director General
D. G. PROYECTOS
MINISTERIO DE MOVILIDAD E INFRAESTRUCTURA

Digitally signed by Comunicaciones Oficiales
Date: 2026.01.30 15:43:41 -03:00