


CONSTITUCION - DETALLE DE BANCO

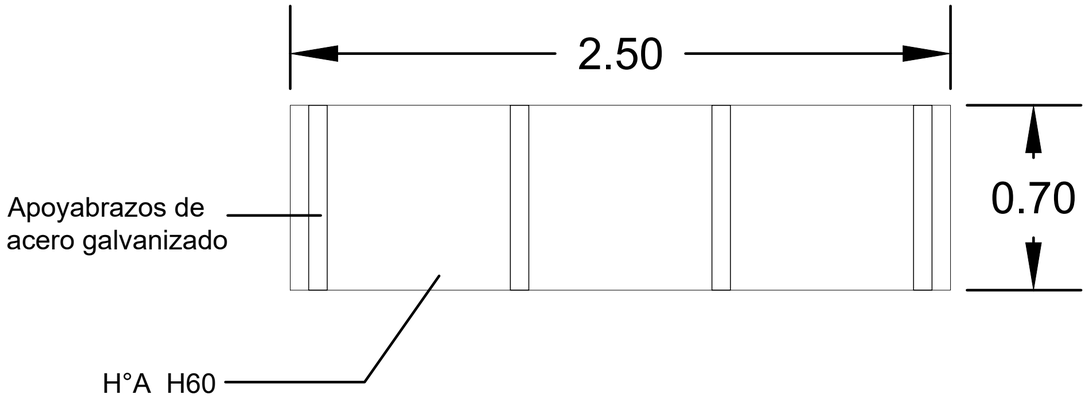

VISTA SUPERIOR

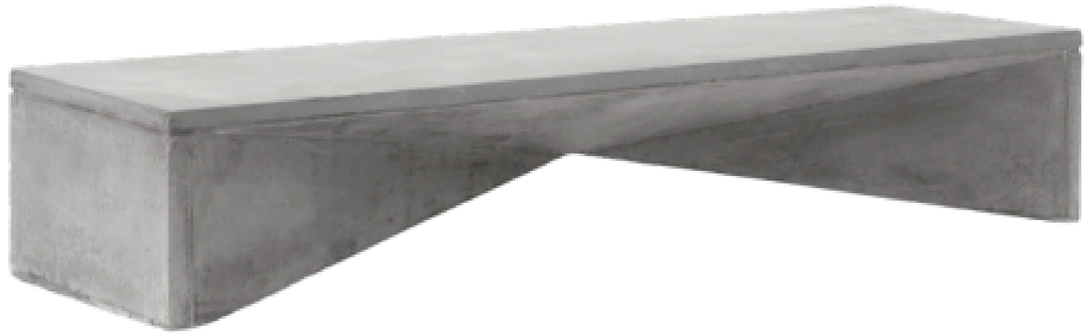

IMÁGEN ILUSTRATIVA - SUMAR APOYABRAZOS

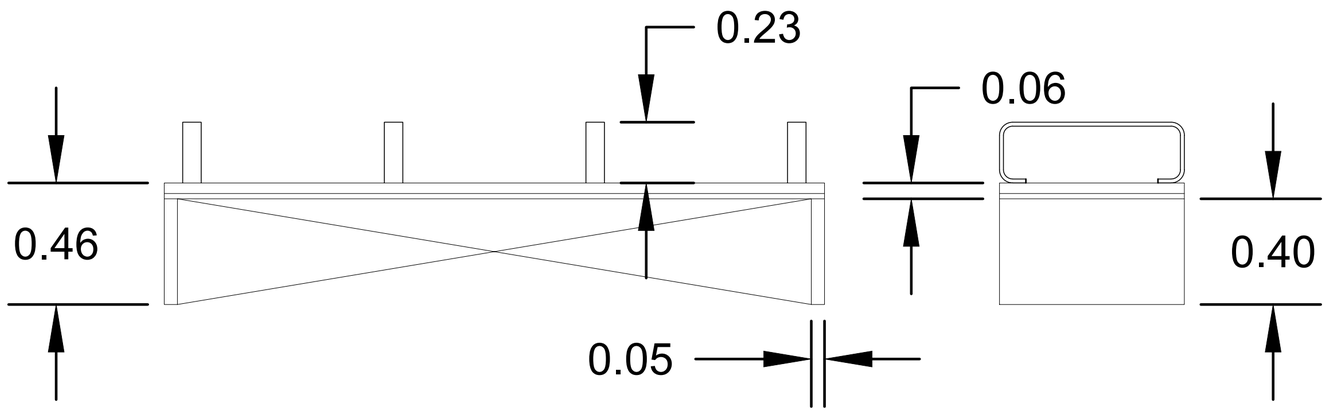

VISTA FRONTAL

VISTA LATERAL

ÁREA DE INTERVENCIÓN

MINISTERIO DE MOVILIDAD E INFRAESTRUCTURA
SUBSECRETARIA DE PROYECTOS Y OBRAS
DIRECCION GENERAL DE PROYECTOS

DGPRO

Obra: CT CONSTITUCION	Plano: CTC_EQP_Banco	Plano N° A17
Rubro: EQUIPAMIENTO	Revisión: Rev.00	
Tramo:-	Fecha: 07/01/2026 Escala:1:25	

MODIFICACIONES:


REVISION	FECHA	DESCRIPCION
-	-	-
-	-	-
-	-	-
-	-	-
-	-	-
-	-	-
-	-	-
-	-	-
-	-	-
-	-	-

NOTAS: EL PRESENTE PLANO ES INDICATIVO. LA CONTRATISTA CONFECCIONARÁ LOS PLANOS DE DETALLE DEFINITIVO, QUE DEBERÁN SER APROBADOS POR LA D.G.D.MI Y LA INSPECCION DE OBRA. EL PLANO PRESENTADO POR LA CONTRATISTA ESTARÁ EN UN TODO DE ACUERDO CON LA NORMATIVA VIGENTE
TODAS LAS MEDIDAS Y NIVELES DEBEN SER VERIFICADOS POR EL CONTRATISTA

PLANO-2026-06753690-GCABA-DGPRO

PLANO NO APTO PARA CONSTRUCCIÓN


CONSTITUCION - DETALLE DE JUEGO TA TE TI

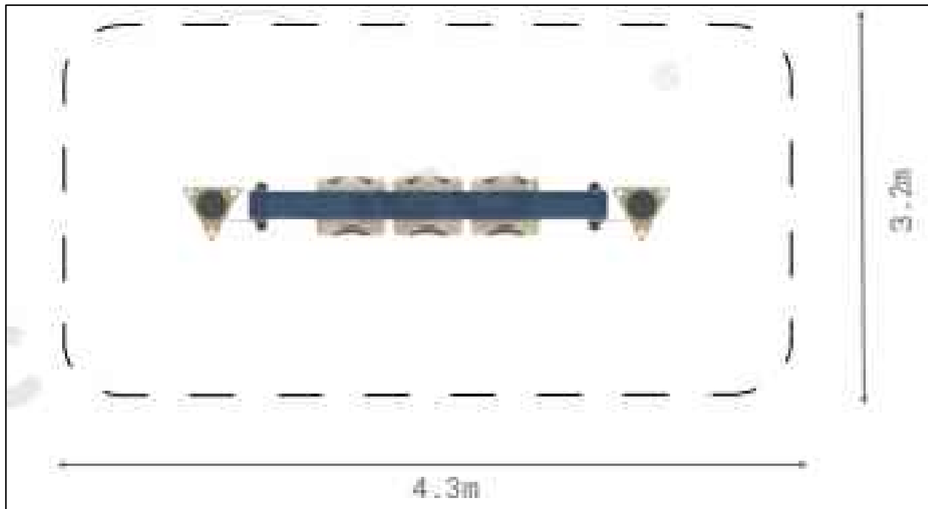

Medidas generales:

Vista frontal:



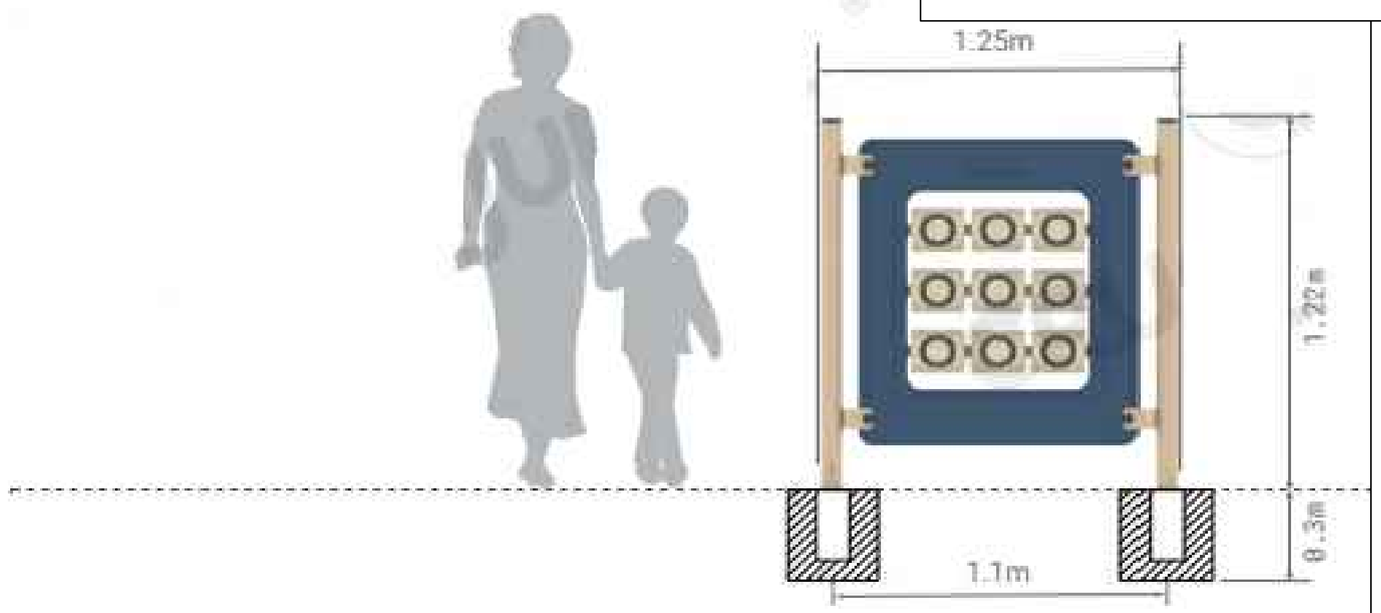

REFERENCIAS

ÁREA DE INTERVENCIÓN

MINISTERIO DE MOVILIDAD E INFRAESTRUCTURA
SUBSECRETARIA DE PROYECTOS Y OBRAS
DIRECCION GENERAL DE PROYECTOS

DGPRO

Obra: CT CONSTITUCION	Plano: CTC_EQP_Juegos	Plano N° A19
Rubro: EQUIPAMIENTO	Revisión: Rev.00	
Tramo: -	Fecha: 07/01/2026	Escala: 1:25

MODIFICACIONES:

REVISION	FECHA	DESCRIPCION
-	-	-

NOTAS: EL PRESENTE PLANO ES INDICATIVO. LA CONTRATISTA CONFECCIONARA LOS PLANOS DE DETALLE DEFINITIVO, QUE DEBERAN SER APROBADOS POR LA D.G.O.INF.U Y LA INSPECCION DE OBRA. EL PLANO PRESENTADO POR LA CONTRATISTA ESTARA EN UN TODO DE ACUERDO CON LA NORMATIVA VIGENTE


PLANO-2026-06753690-GCABA-DGPRO

PLANO NO APTO PARA CONSTRUCCIÓN

CONSTITUCION - DETALLE DE FAROLA PEATONAL 4.5M



ESQUEMA DE COLUMNA
Esc: 1:75

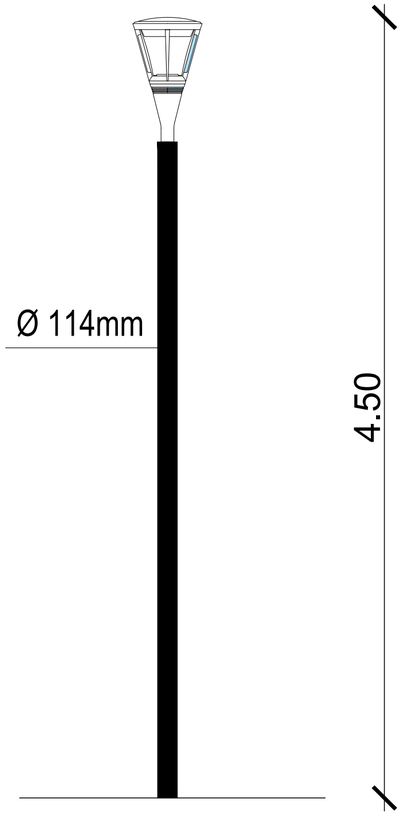

NOTAS :

- El Contratista confeccionará los Planos de
Detalle definitivos, que deberán ser aprobados por la Inspección de Obra.
- Asimismo, efectuará los cálculos y verificaciones estructurales correspondientes, para la aprobación por parte de la Inspección de Obra.
- El contratista proveerá las luminarias LEDs y columnas metálicas y deberá presentar muestra del artefacto, el detalle de columna y base; así como los dispositivos de unión entre partes para ser aprobados por la Inspección de Obra.
- Todas las piezas componentes serán galvanizadas por inmersión en caliente.
- Los artefactos de iluminación y sus instalaciones cumplirán en todos los casos con las normas de seguridad vigente para instalaciones electricas y artefactos en el espacio público. Contarán además con protección contra robo y vandalismo, que deberá ser presentada para su aprobación por la Inspección de Obra.
- Las instalaciones eléctricas, sus componenentes, así como el montaje de los mismos se regirán por las normas establecidas en el Pliego de Especificaciones Técnicas de Alumbrado Público de la Dirección General de Alumbrado Público (DGALUM)

REFERENCIAS

ÁREA DE INTERVENCIÓN

Gobierno de la Ciudad de Buenos Aires

MINISTERIO DE MOVILIDAD E INFRAESTRUCTURA
SUBSECRETARIA DE PROYECTOS Y OBRAS
DIRECCION GENERAL DE PROYECTOS

DGPRO

Obra: CT CONSTITUCION	Plano: CTC_EQP_Luminarias Peatonales	Plano N°: A18
Rubro: EQUIPAMIENTO	Revisión: Rev.00	
Tramo: -	Fecha: 07/01/2026	Escala: 1:25

MODIFICACIONES:

REVISION	FECHA	DESCRIPCIÓN
-	-	-
-	-	-
-	-	-
-	-	-
-	-	-
-	-	-
-	-	-
-	-	-
-	-	-
-	-	-


NOTAS: EL PRESENTE PLANO ES INDICATIVO. LA CONTRATISTA CONFECCIONARA LOS PLANOS DE DETALLE DEFINITIVO, QUE DEBERAN SER APROBADOS POR LA D.G.O.INF.U Y LA INSPECCION DE OBRA. EL PLANO PRESENTADO POR LA CONTRATISTA ESTARA EN UN TODO DE ACUERDO CON LA NORMATIVA VIGENTE

PLANO-2026-06753690-GCABA-DGPRO


PLANO NO APTO PARA CONSTRUCCIÓN

CONSTITUCION - DETALLE DE REJA


REJA SIMPLE

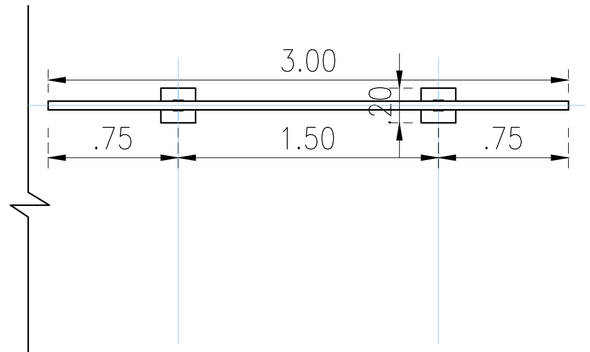


REJA COMPUESTA

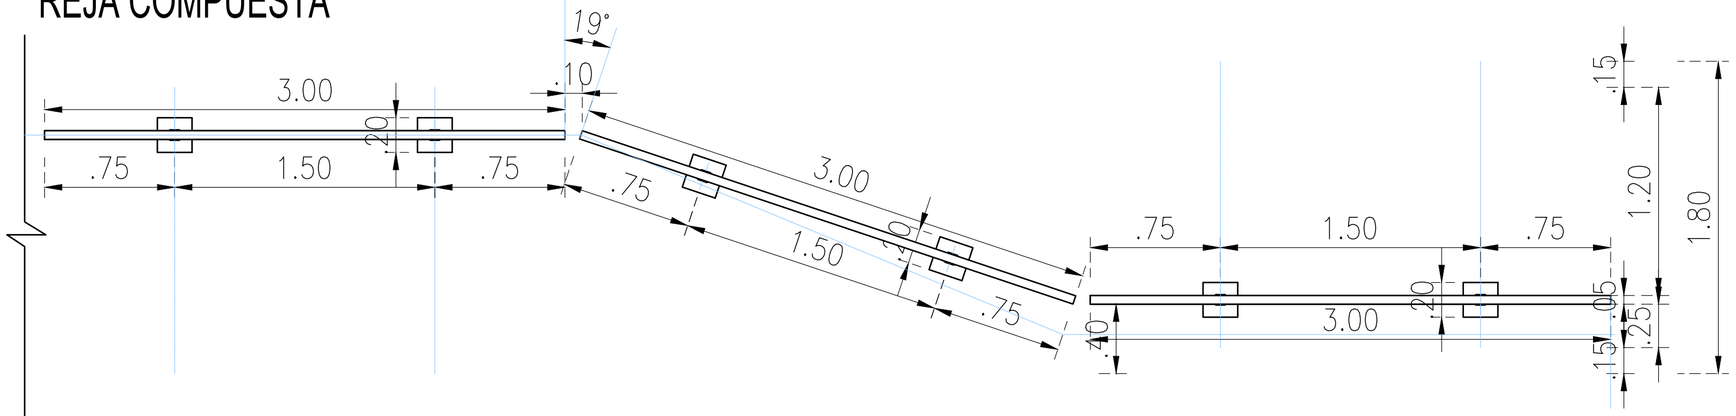

PLANTA

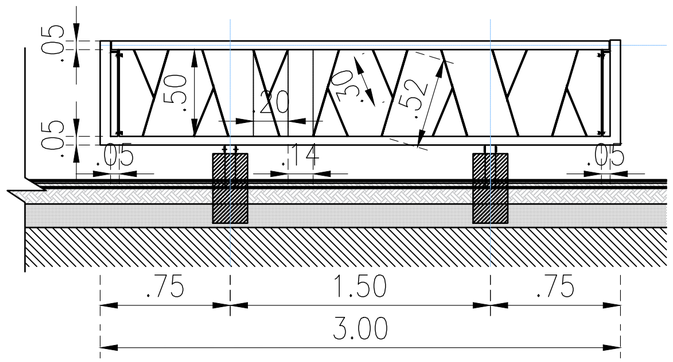


PLANTA

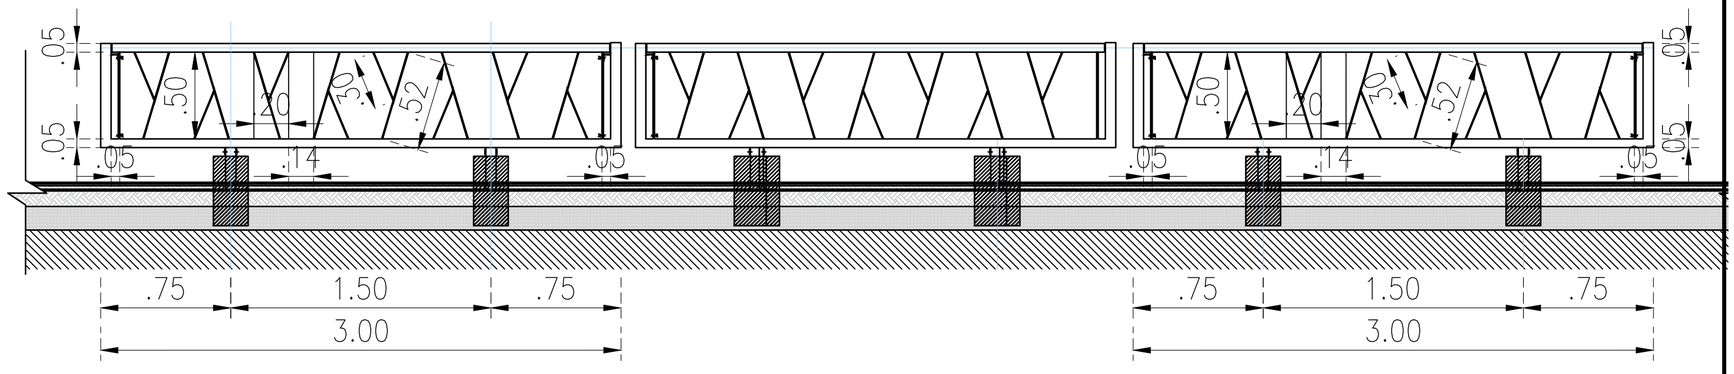


VISTA

VISTA


CORTE

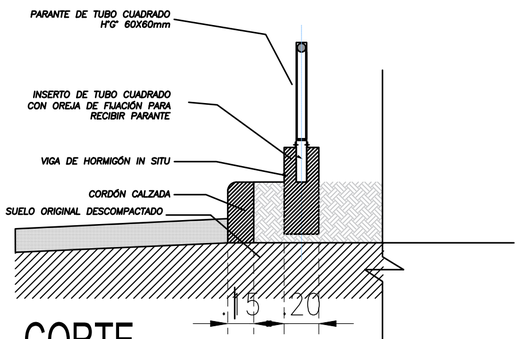

MÓDULOS

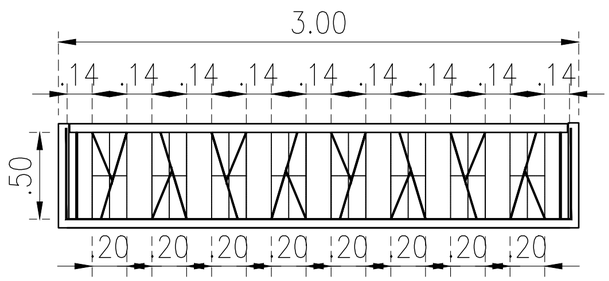

CORTE

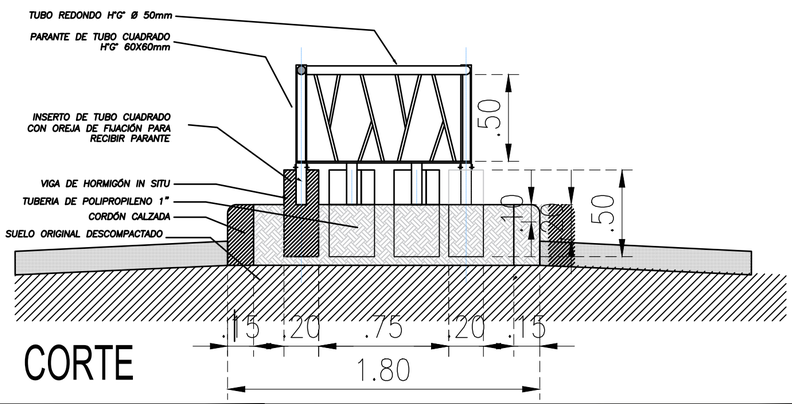

ÁREA DE INTERVENCIÓN

Gobierno de la Ciudad de Buenos Aires

MINISTERIO DE MOVILIDAD E INFRAESTRUCTURA
SUBSECRETARIA DE PROYECTOS Y OBRAS
DIRECCION GENERAL DE PROYECTOS

DGPRO

Obra: CT CONSTITUCION	Plano: CTC_EQP_Rejas	Plano N° A16
Rubro: EQUIPAMIENTO	Revisión: Rev.00	
Tramo:-	Fecha: 07/01/2026	Escala:1:25

MODIFICACIONES:

REVISION	FECHA	DESCRIPCION
-	-	-
-	-	-
-	-	-
-	-	-
-	-	-
-	-	-
-	-	-
-	-	-
-	-	-

NOTAS: EL PRESENTE PLANO ES INDICATIVO. LA CONTRATISTA CONFECCIONARÁ LOS PLANOS DE DETALLE DEFINITIVO, QUE DEBERÁN SER APROBADOS POR LA D.G.D.INF.U Y LA INSPECCION DE OBRA. EL PLANO PRESENTADO POR LA CONTRATISTA ESTARÁ EN UN TODO DE ACUERDO CON LA NORMATIVA VIGENTE
TODAS LAS MEDIDAS Y NIVELES DEBERÁN SER VERIFICADOS POR EL CONTRATISTA

PLANO NO APTO PARA CONSTRUCCIÓN

PLANO-2026-06753690-GCABA-DGPRO

G O B I E R N O DE LA C I U D A D DE B U E N O S A I R E S

"2026 - Año del 30° Aniversario de la sanción de la Constitución de la Ciudad Autónoma de Buenos Aires"

Hoja Adicional de Firmas
Plano

Número: PLANO-2026-06753690-GCABA-DGPRO

Buenos Aires, Viernes 30 de Enero de 2026

Referencia: EQUIPAMIENTO

El documento fue importado por el sistema GEDO con un total de 4 pagina/s.

Digitally signed by Comunicaciones Oficiales
Date: 2026.01.30 15:45:01 -03:00

GABRIEL EDUARDO ROSALES
Director General
D. G. PROYECTOS
MINISTERIO DE MOVILIDAD E INFRAESTRUCTURA

Digitally signed by Comunicaciones Oficiales
Date: 2026.01.30 15:45:03 -03:00