CONSTITUCION - PROYECTO__Av. Hornos

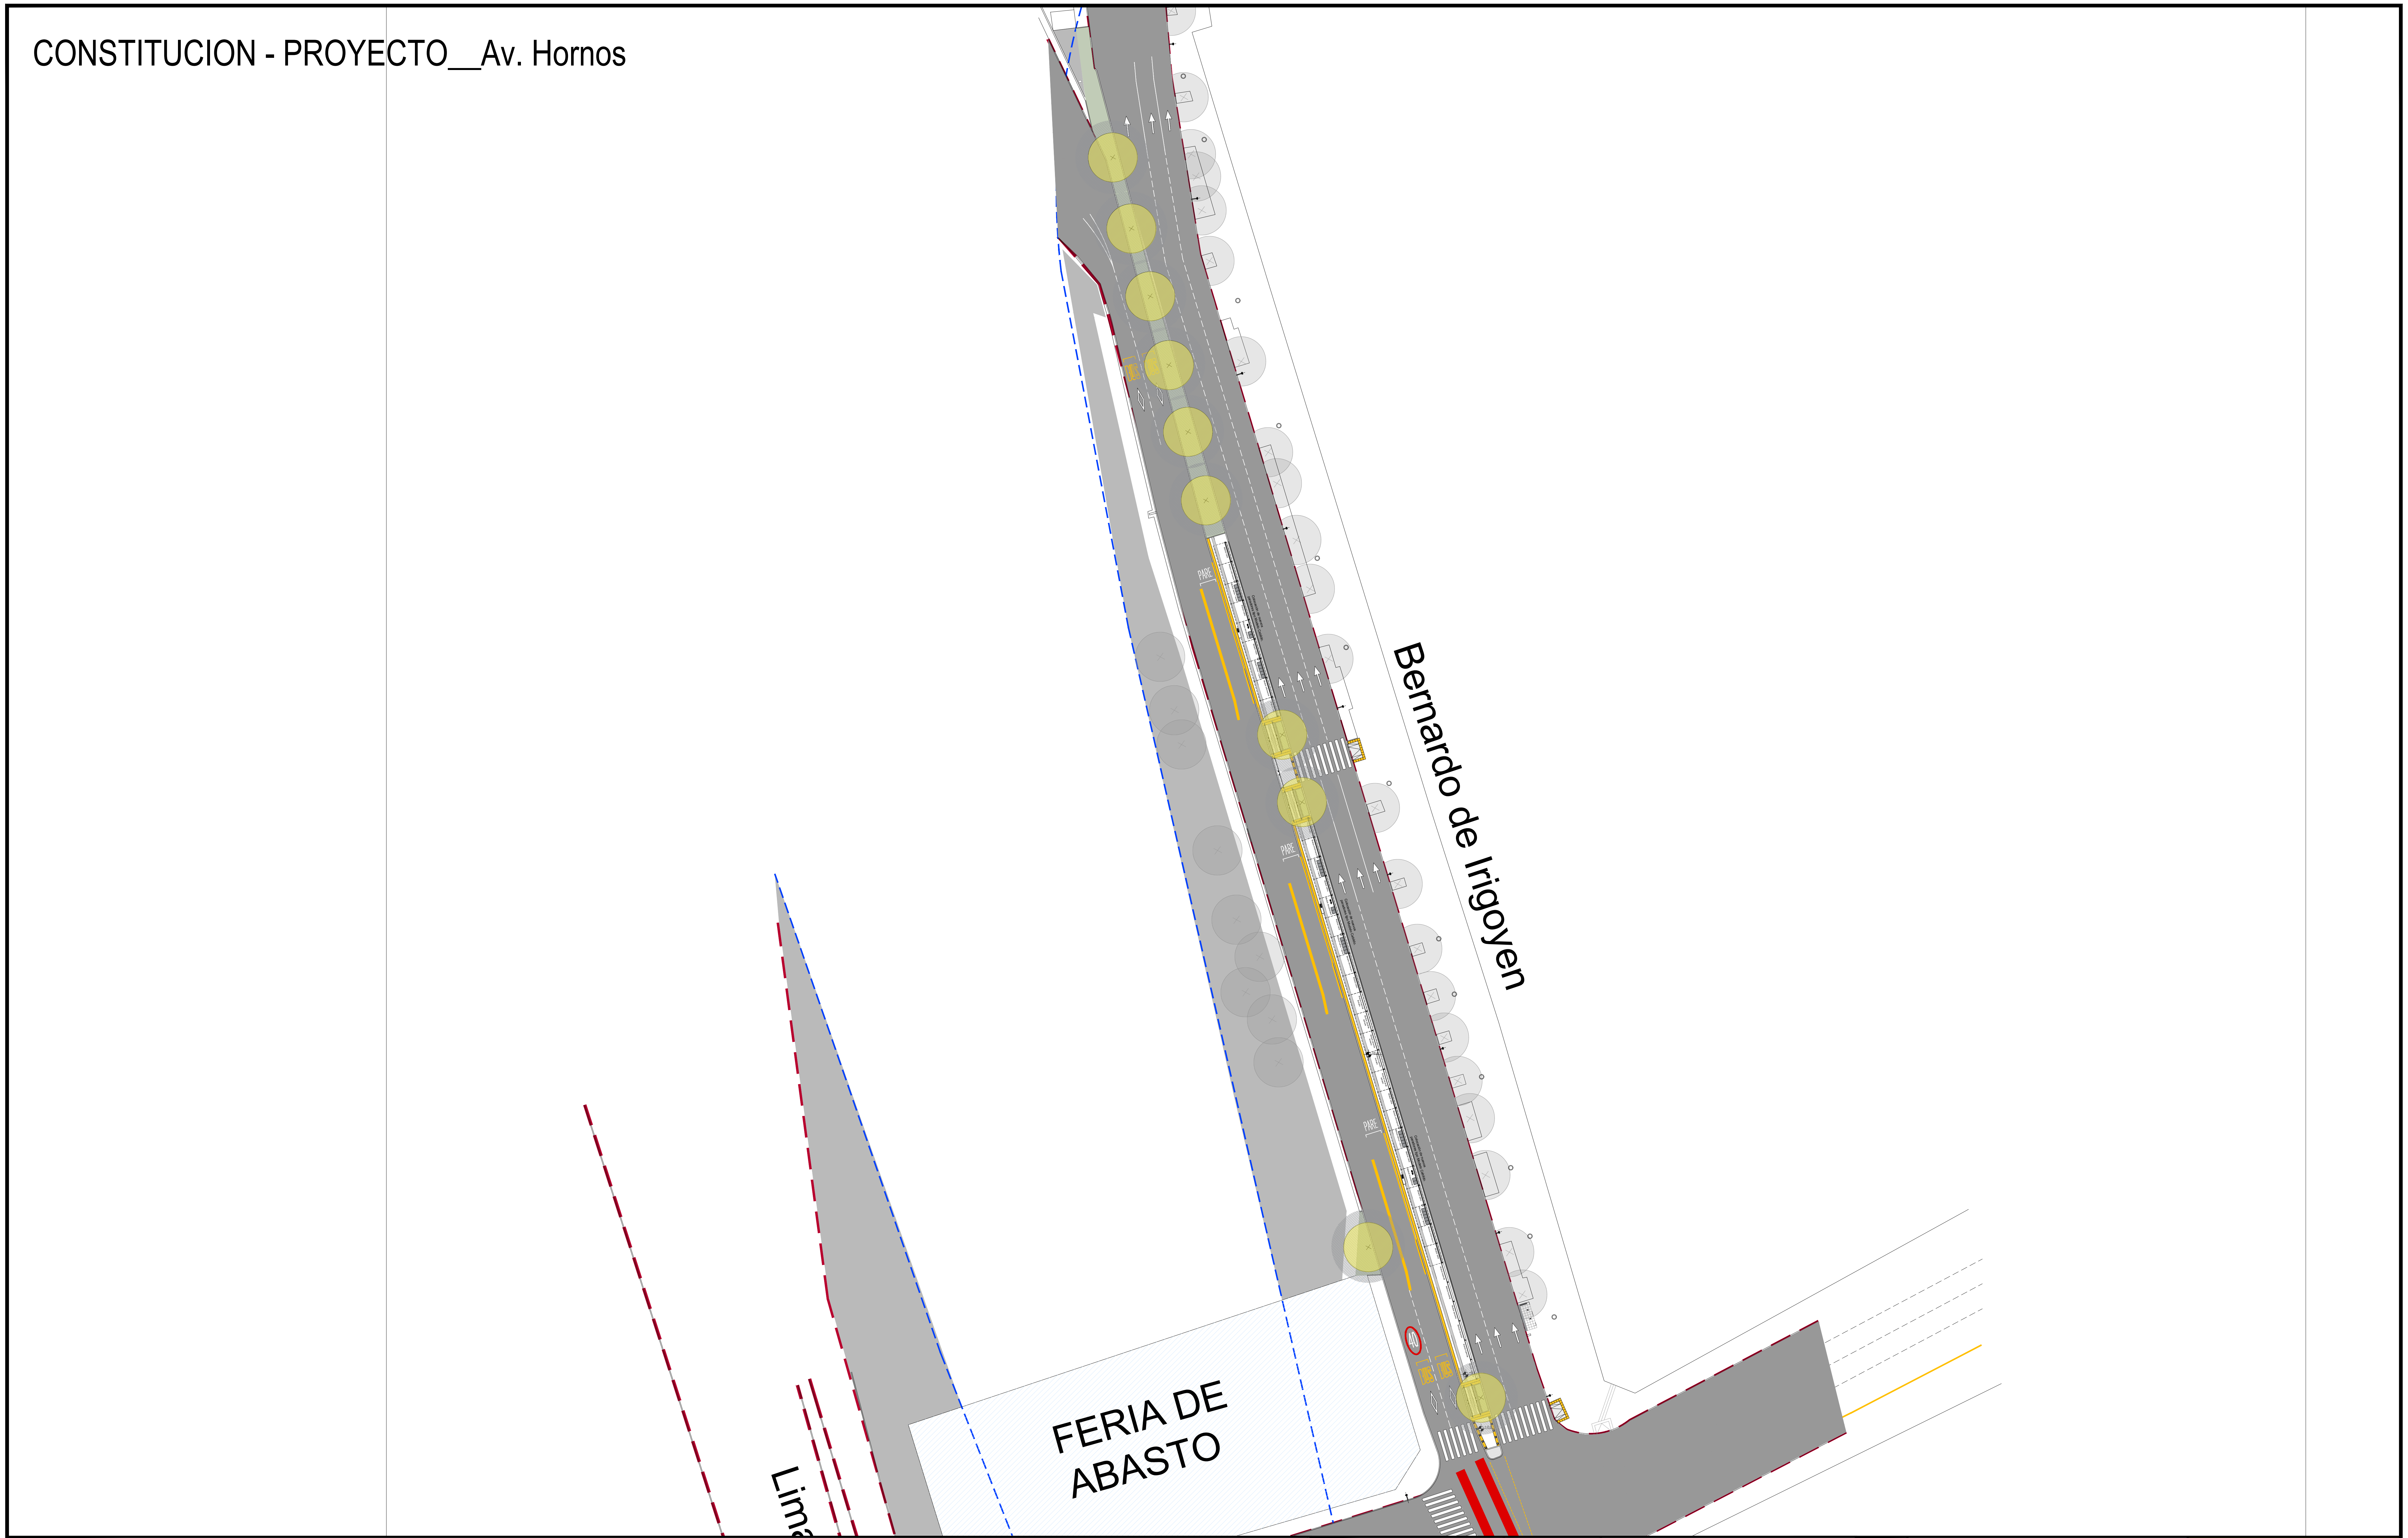

REFERENCIAS

ÁRBOLES

○	Ejemplares existentes a trasplantar
▨	Proyección del desarrollo máximo de la copa con su densidad de sombra
●	501-Jacaranda mimosifolia "Jacaranda" Envase 60L Cant. Total 4 unidades
●	502- Peltophroum dubium "Ibirá pita" Envase 60L Cant. Total 25 unidades
●	503-Enterolobium contortisiliquum "Timbó" Cant. Total 10 unidades Ejemplares trasplantados del boulevard Gral. Hornos

CÉSPED

🟩	Grama bahiana 1600m2

HERBÁCEAS

▨	201-Dietes grandiflora "Dietes" E3L 9 x m2 Cant. Total 1400 unidades

ARBUSTOS

▨	401- Salvia guaranitica "Salvia azul" E3L 7 x m2 Cant. Total 1400 unidades
▨	403- Euryops pecnitanus "Euryops" E3L 6 x m2 Cant. Total 800 unidades
▨	402-Salvia leucantha "Salvia leucanta" E3L 7 x m2 Cant. Total 260 unidades

ÁREA DE INTERVENCIÓN

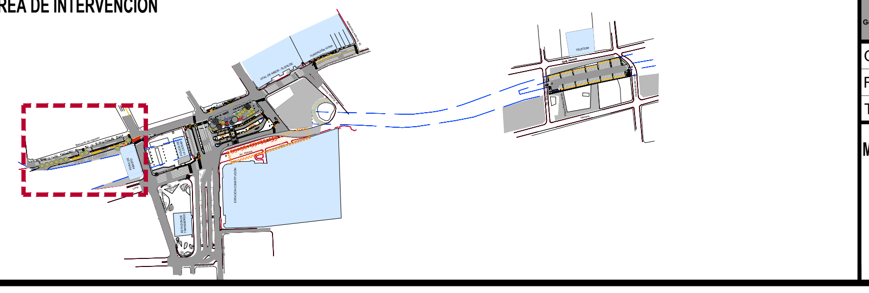

Gobierno de la Ciudad de Buenos Aires

MINISTERIO DE MOVILIDAD E INFRAESTRUCTURA
SUBSECRETARIA DE PROYECTOS Y OBRAS
DIRECCION GENERAL DE PROYECTOS

DGPRO

Obra: CT CONSTITUCION	Plano: CTC_ARQ_Playa de regulación 2	Plano N° A12
Rubro: PAISAJISMO	Revisión: Rev.00	
Tramo: Bernardo de Irigoyen	Fecha: 07/01/2026 Escala: -	

MODIFICACIONES:

REVISION	FECHA	DESCRIPCION
-	-	-
-	-	-
-	-	-
-	-	-
-	-	-
-	-	-
-	-	-
-	-	-
-	-	-
-	-	-

NOTAS: EL PRESENTE PLANO ES INDICATIVO. LA CONTRATISTA CONFECCIONARA LOS PLANOS DE DETALLE DEFINITIVO, QUE DEBERAN SER APROBADOS POR LA D.G.O.INF.U Y LA INSPECCION DE OBRA. EL PLANO PRESENTADO POR LA CONTRATISTA ESTARA EN UN TODO DE ACUERDO CON LA NORMATIVA VIGENTE
TODAS LAS MEDIDAS Y NIVELES SE VERIFICARAN EN OBRA POR EL CONTRATISTA.
TODOS LOS DETALLES CONSTRUCTIVOS SERÁN COORDINADOS Y COMPATIBILIZADOS EN OBRA

PLANO-2026-06754020-GCABA-DGPRO

PLANO NO APTO PARA CONSTRUCCIÓN

CONSTITUCION - PROYECTO_Playa de regulación 1_Canteros

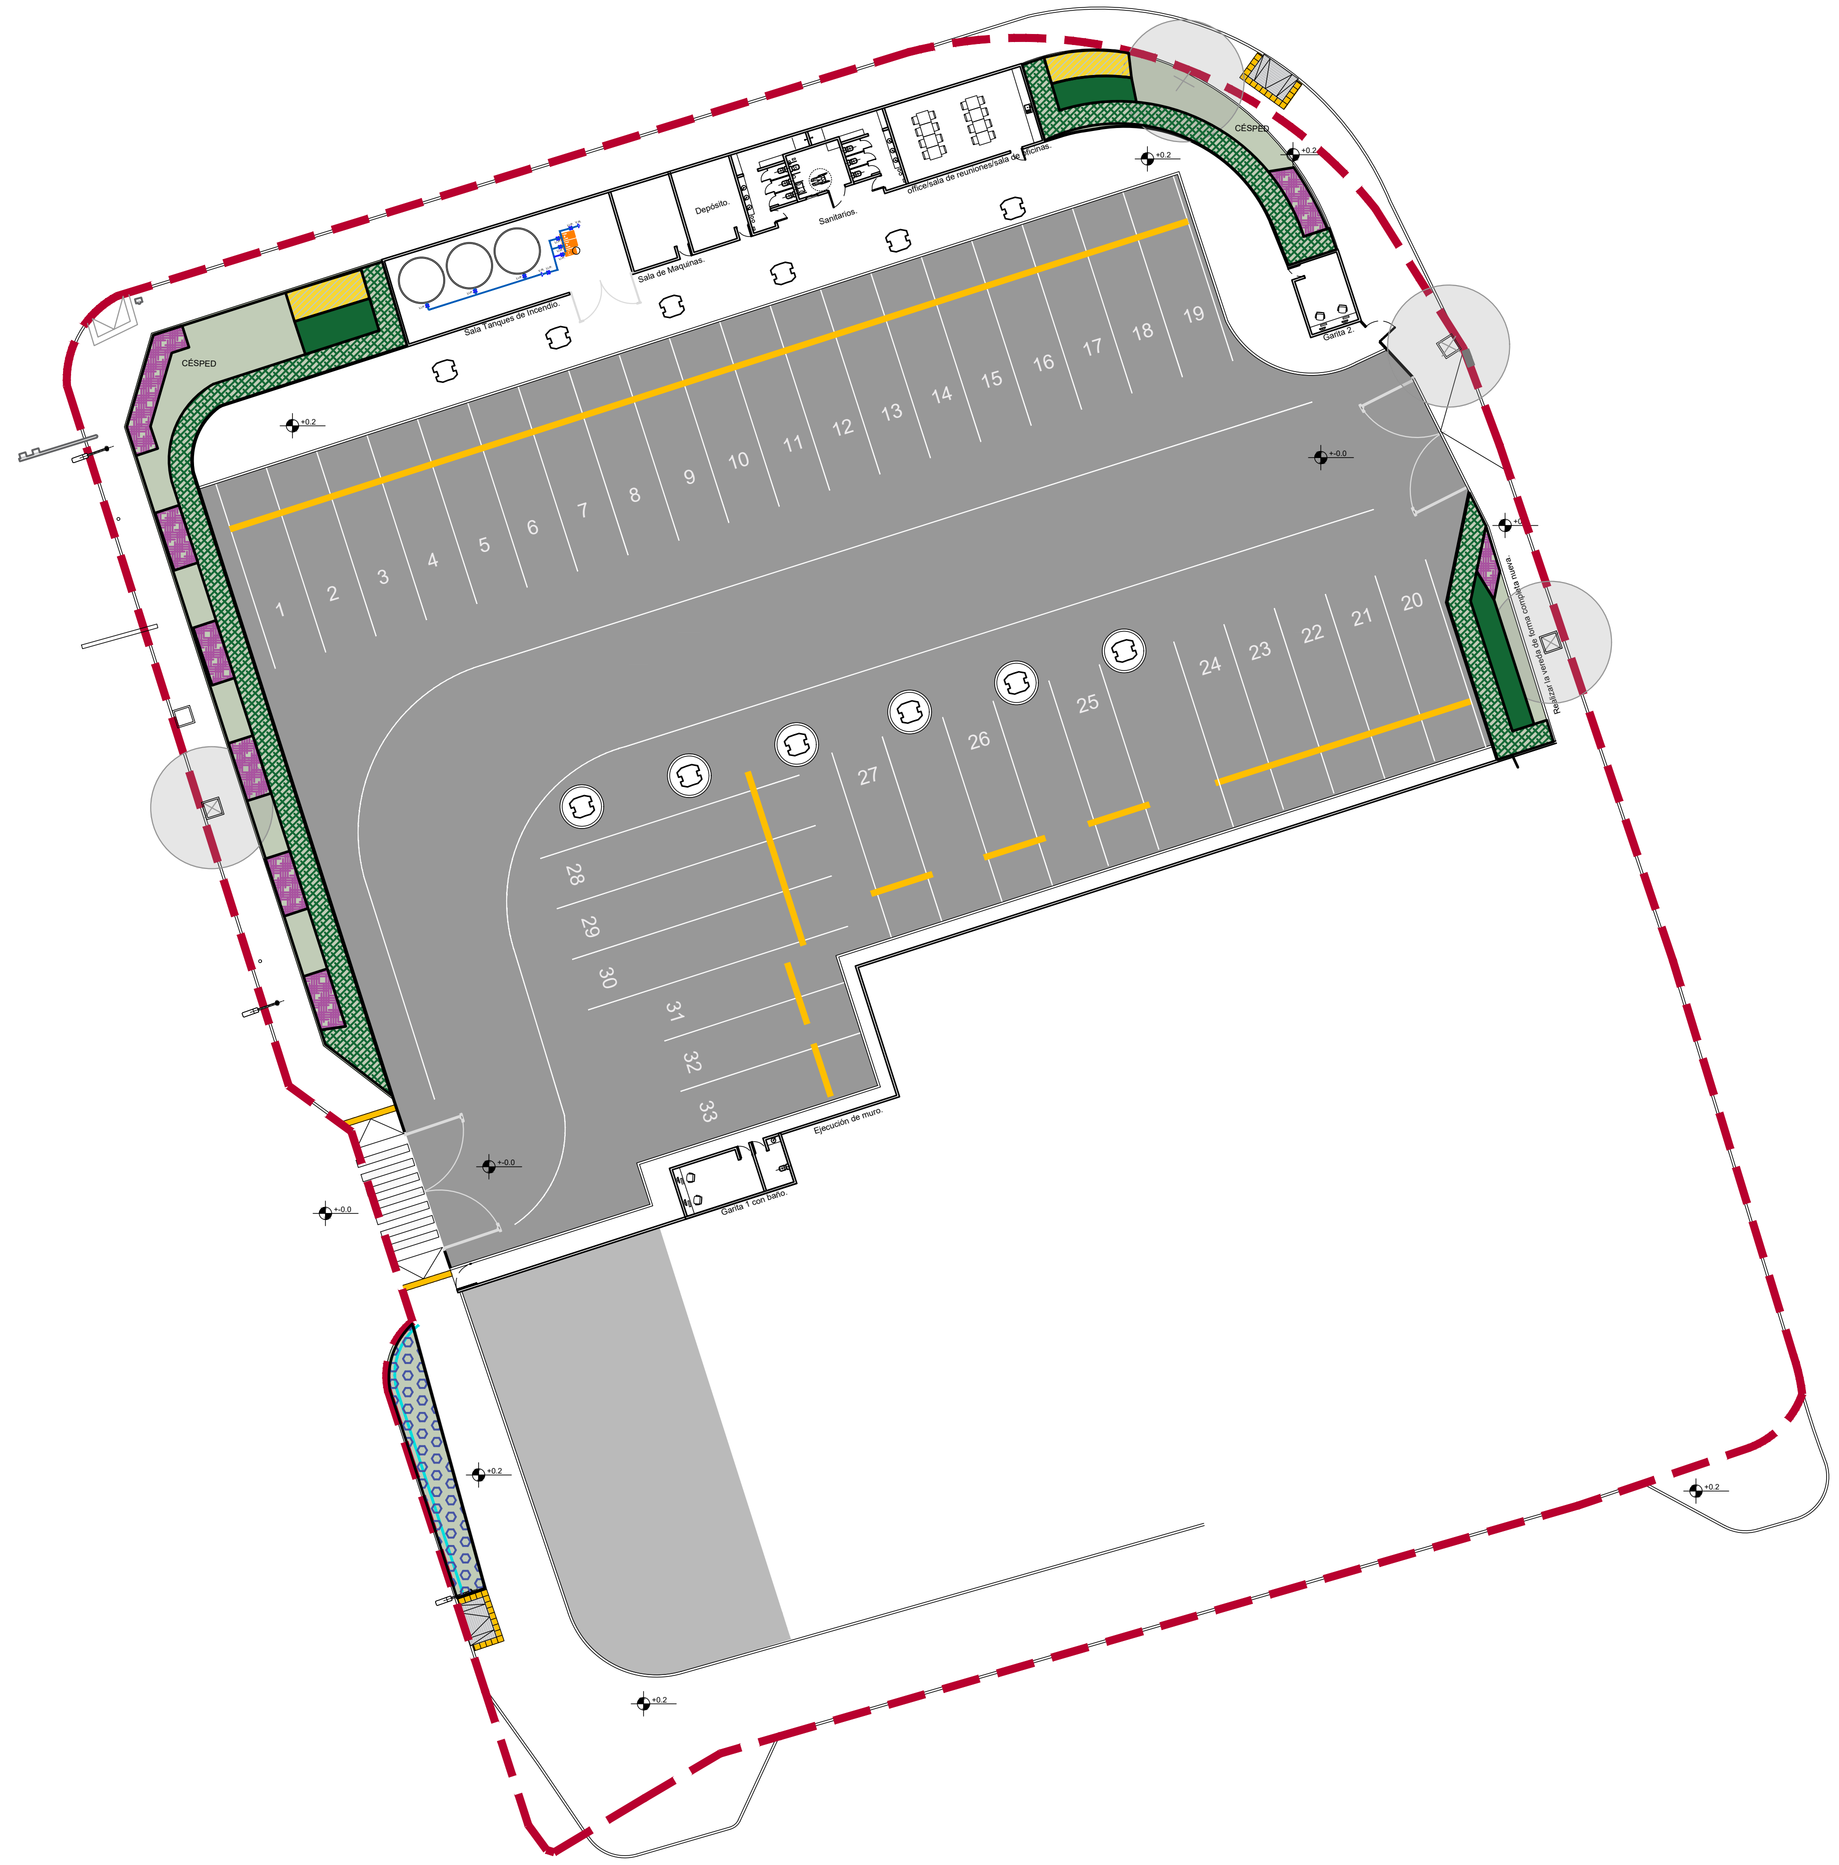

REFERENCIAS

CÉSPED

🟩 Grama bahiana
300m2

HERBÁCEAS

▨ 201-Dietes grandiflora
"Dietes"
E3L 9 x m2
Cant. Total 315 unidades

ARBUSTOS

▨ 401- Salvia guaranitica
"Salvia azul"
E3L 7 x m2
Cant. Total 270 unidades

▨ 402-Salvia leucantha
"Salvia leucanta"
E3L 7 x m2
Cant. Total 400 unidades

▨ 403- Euryops pecnitanus
"Euryops"
E3L 6 x m2
Cant. Total 120 unidades

▨ 404-Malaleuca armillaris
"Malaleuca"
E3L 4 x m2
Cant. Total 700 unidades

ÁREA DE INTERVENCIÓN

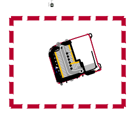

Gobierno de la Ciudad de Buenos Aires

MINISTERIO DE MOVILIDAD E INFRAESTRUCTURA
SUBSECRETARIA DE PROYECTOS Y OBRAS
DIRECCION GENERAL DE PROYECTOS

DGPRO

Obra: CT CONSTITUCION
Rubro: PAISAJISMO
Tramo: -
Plano: CTC_ARQ_Playa de regulación 1
Revisión: Rev.00
Fecha: 07/01/2026
Escala: -
Plano N° A08

MODIFICACIONES:

REVISION	FECHA	DESCRIPCION
-	-	-
-	-	-
-	-	-
-	-	-
-	-	-
-	-	-
-	-	-
-	-	-
-	-	-
-	-	-

NOTAS: EL PRESENTE PLANO ES INDICATIVO. LA CONTRATISTA CONFECCIONARA LOS PLANOS DE DETALLE DEFINITIVO, QUE DEBERAN SER APROBADOS POR LA D.G.O.INF.U Y LA INSPECCION DE OBRA. EL PLANO PRESENTADO POR LA CONTRATISTA ESTARA EN UN TODO DE ACUERDO CON LA NORMATIVA VIGENTE
TODAS LAS MEDIDAS Y NIVELES SE VERIFICARAN EN OBRA POR EL CONTRATISTA.
TODOS LOS DETALLES CONSTRUCTIVOS SERÁN COORDINADOS Y COMPATIBILIZADOS EN OBRA.

PLANO NO APTO PARA CONSTRUCCIÓN

CONSTITUCION - PROYECTO__Av. Hornos_ CANTEROS

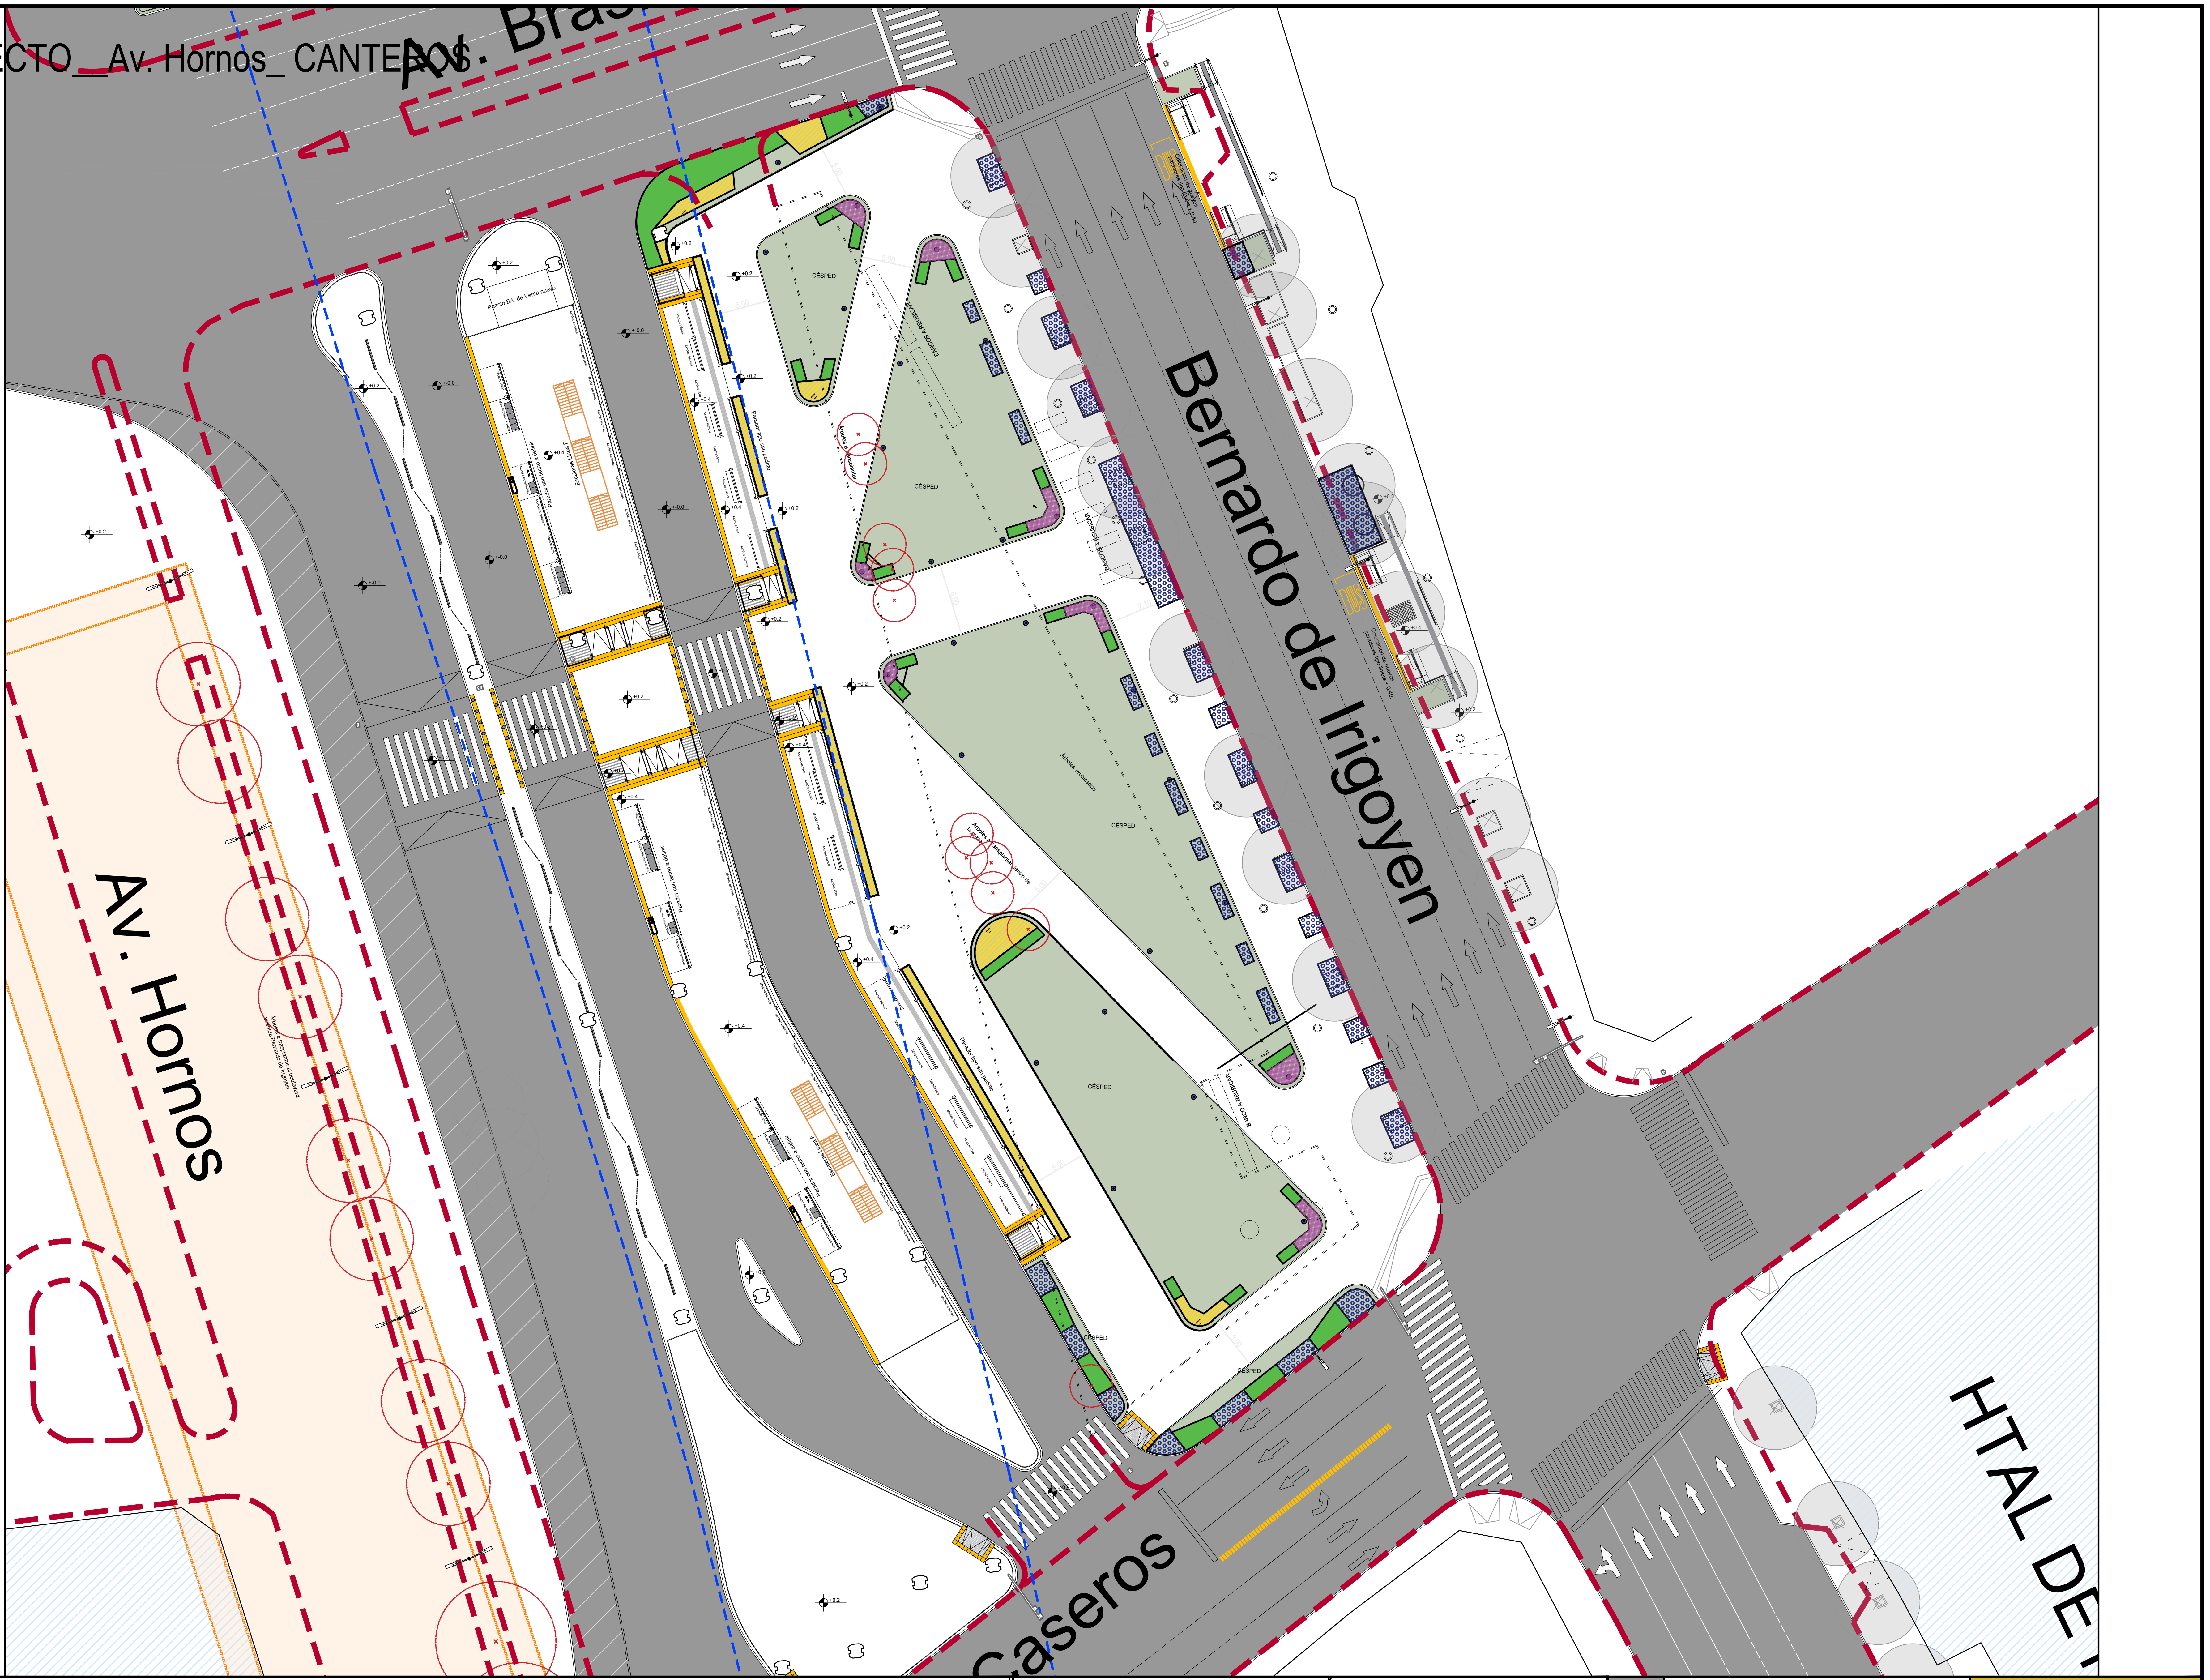

REFERENCIAS

ÁRBOLES

○ Ejemplares existentes a trasplantar

▨ Proyección del desarrollo máximo de la copa con su densidad de sombra

● 501-Jacaranda mimosifolia "Jacaranda" Envase 60L Cant. Total 4 unidades

● 502- Peltophroum dubium "Ibirá pita" Envase 60L Cant. Total 25 unidades

● 503-Enterolobium contortisiliquum "Timbó" Cant. Total 10 unidades Ejemplares trasplantados del boulevard Gral. Hornos

CÉSPED

🟩 Grama bahiana 1600m2

HERBÁCEAS

▨ 201-Dietes grandiflora "Dietes" E3L 9 x m2 Cant. Total 1400 unidades

ARBUSTOS

▨ 401- Salvia guaranitica "Salvia azul" E3L 7 x m2 Cant. Total 1400 unidades

▨ 403- Euryops pecnitanus "Euryops" E3L 6 x m2 Cant. Total 800 unidades

▨ 402-Salvia leucantha "Salvia leucanta" E3L 7 x m2 Cant. Total 260 unidades

ÁREA DE INTERVENCIÓN

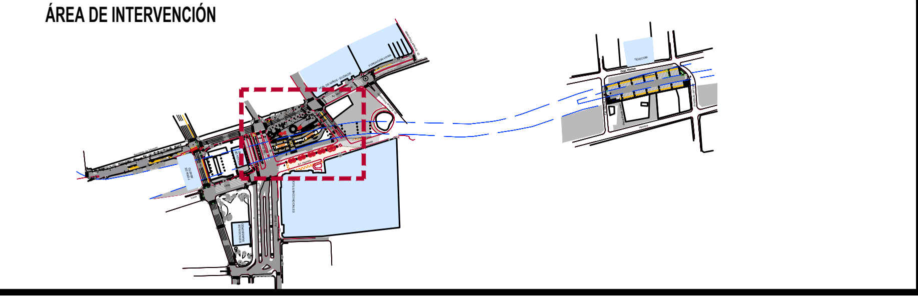

Gobierno de la Ciudad de Buenos Aires

MINISTERIO DE MOVILIDAD E INFRAESTRUCTURA
SUBSECRETARIA DE PROYECTOS Y OBRAS
DIRECCION GENERAL DE PROYECTOS

DGPRO

Obra: CT CONSTITUCION	Plano: CTC_ARQ_Playa de regulación 2	Plano N° A12
Rubro: PAISAJISMO	Revisión: Rev.00	
Tramo: -	Fecha: 07/01/2026 Escala: -	

MODIFICACIONES:

REVISION	FECHA	DESCRIPCION
-	-	-
-	-	-
-	-	-
-	-	-
-	-	-
-	-	-
-	-	-
-	-	-
-	-	-
-	-	-

NOTAS: EL PRESENTE PLANO ES INDICATIVO. LA CONTRATISTA CONFECCIONARA LOS PLANOS DE DETALLE DEFINITIVO, QUE DEBERAN SER APROBADOS POR LA D.G.O.INF.U Y LA INSPECCION DE OBRA. EL PLANO PRESENTADO POR LA CONTRATISTA ESTARA EN UN TODO DE ACUERDO CON LA NORMATIVA VIGENTE
TODAS LAS MEDIDAS Y NIVELES SE VERIFICARAN EN OBRA POR EL CONTRATISTA.
TODOS LOS DETALLES CONSTRUCTIVOS SERÁN COORDINADOS Y COMPATIBILIZADOS EN OBRA.

PLANO NO APTO PARA CONSTRUCCIÓN

CONSTITUCION - PROYECTO__Av. Hornos_Árbolado

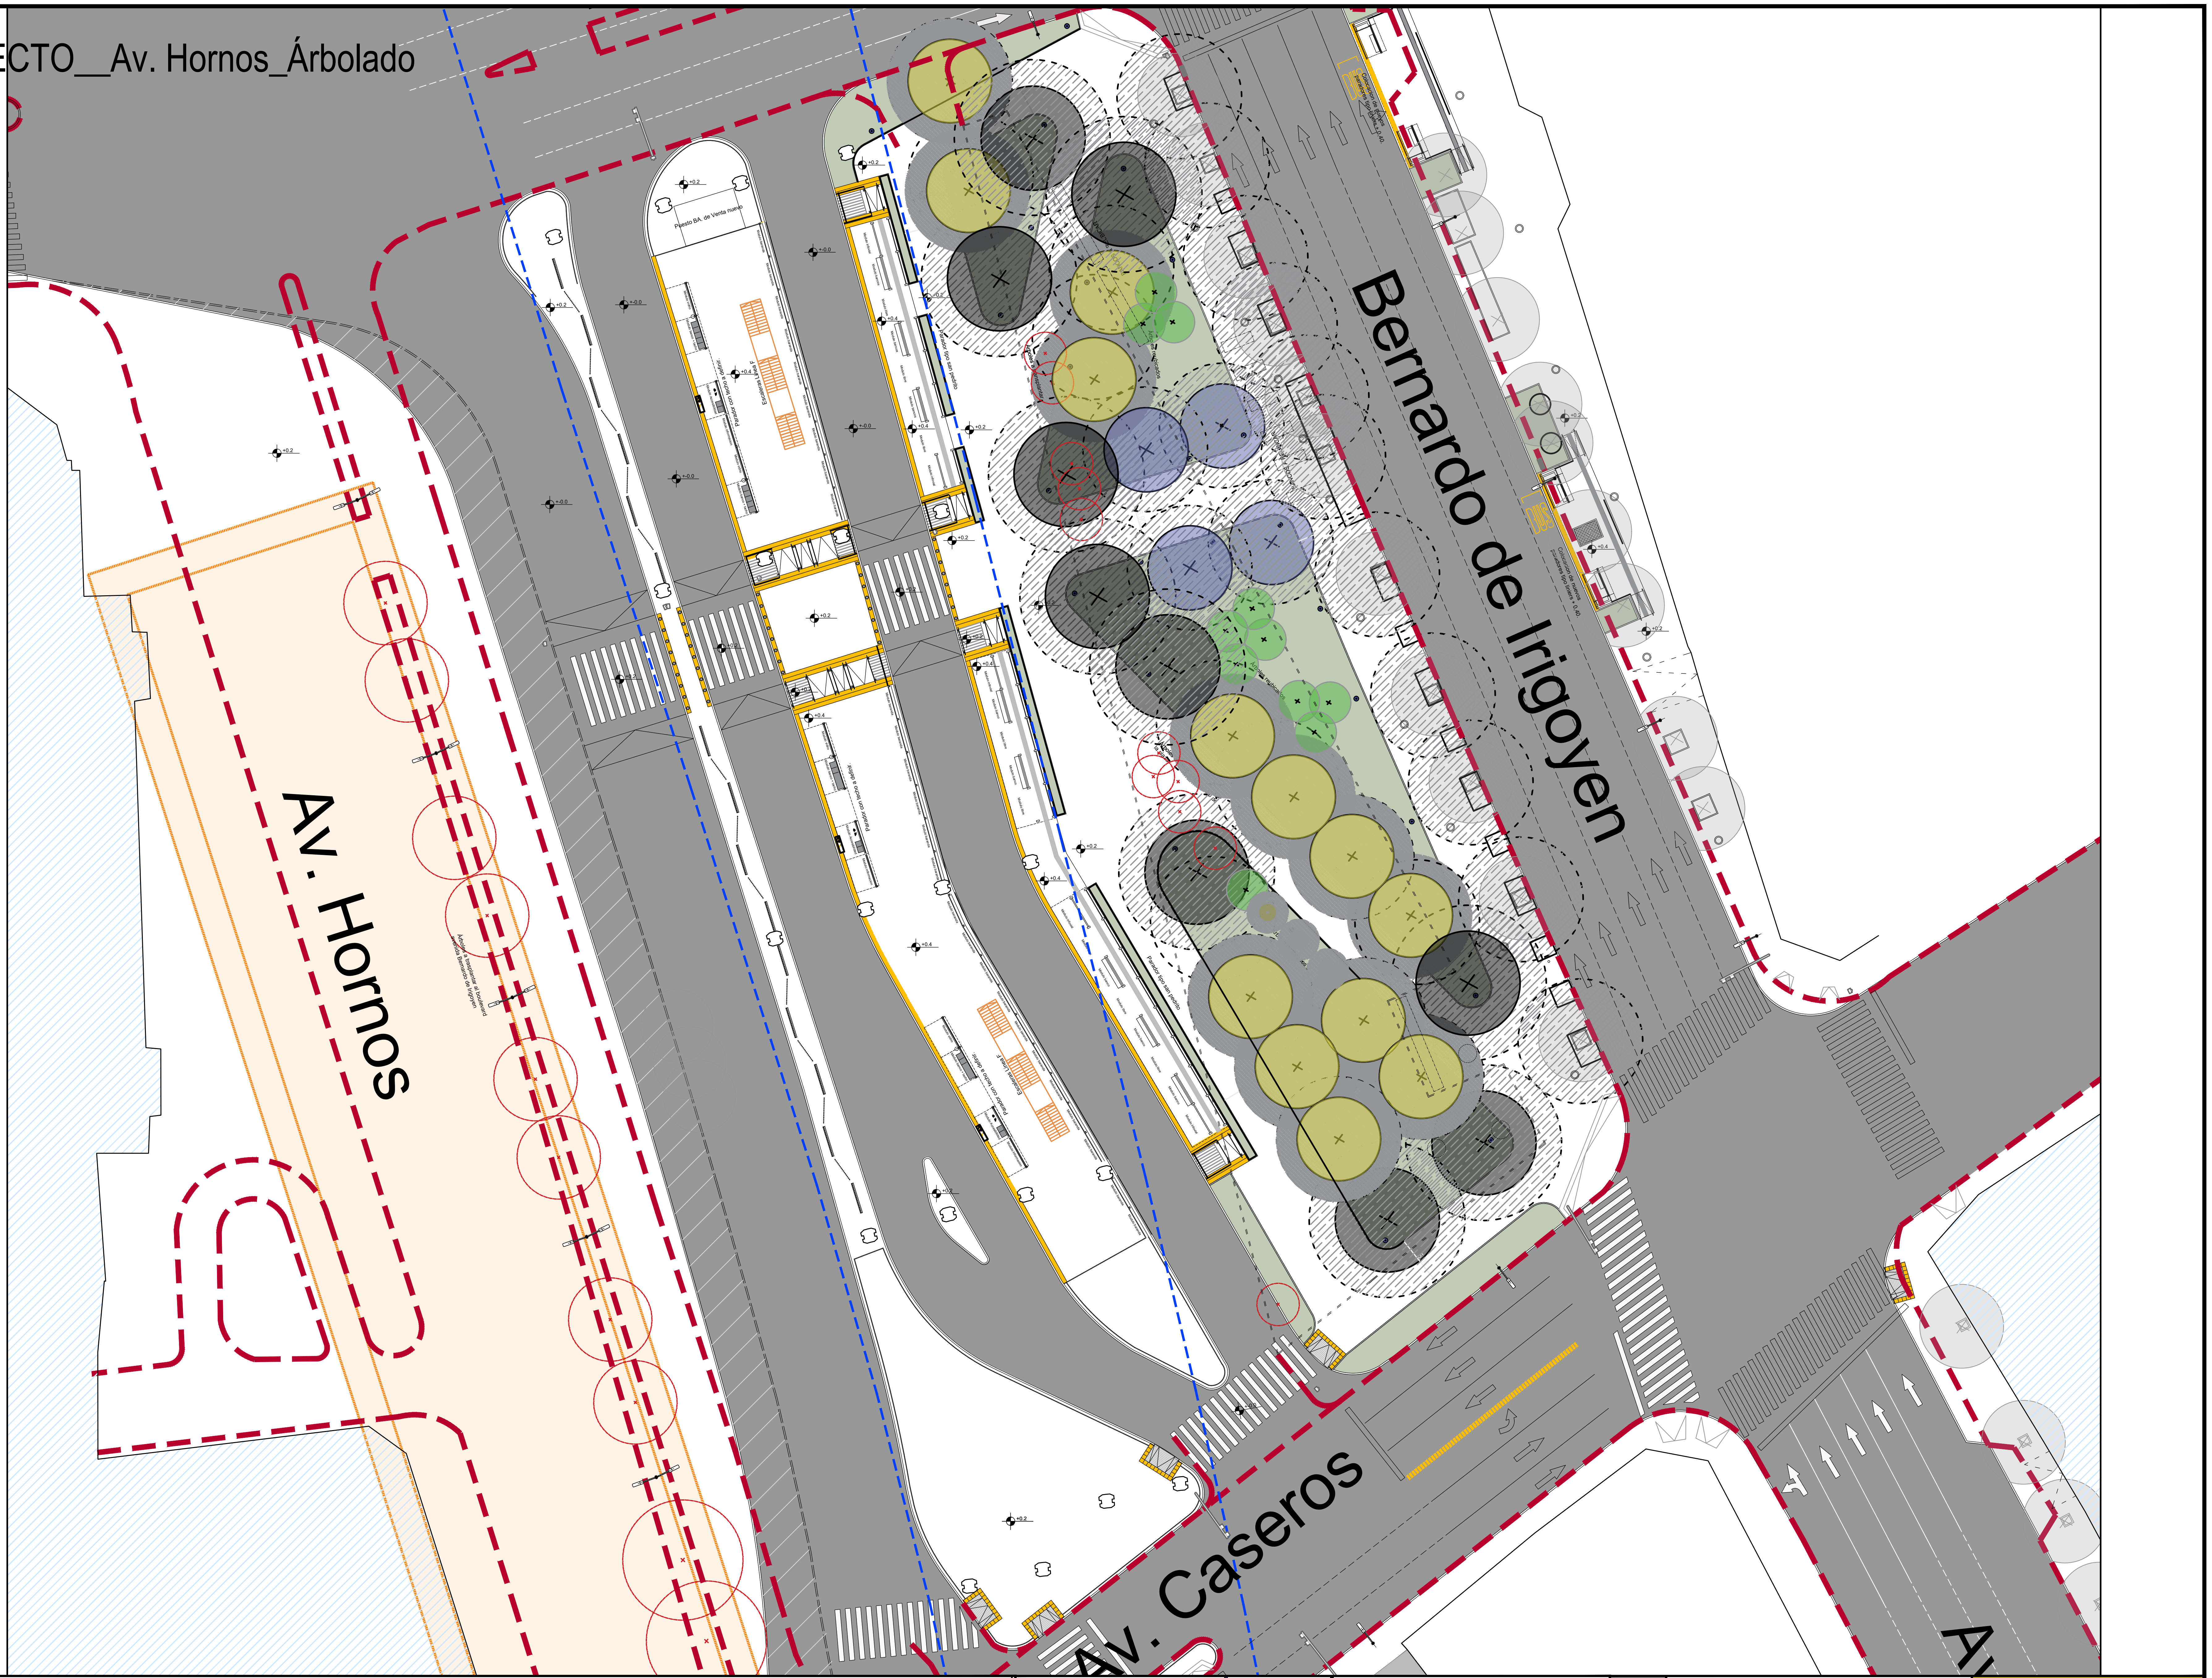

REFERENCIAS

ÁRBOLES

- ⊙ Ejemplares existentes a trasplantar
- ▨ Proyección del desarrollo máximo de la copa con su densidad de sombra
- ● 501-Jacaranda mimosifolia "Jacaranda" Envase 60L Cant. Total 4 unidades
- ● 502- Peltophroum dubium "Ibirá pita" Envase 60L Cant. Total 25 unidades
- ● 503-Enterolobium contortisiliquum "Timbó" Cant. Total 10 unidades Ejemplares trasplantados del boulevard Gral. Hornos

CÉSPED

- 🟩 Grama bahiana 1600m2

HERBÁCEAS

- ▨ 201-Dietes grandiflora "Dietes" E3L 9 x m2 Cant. Total 1400 unidades

ARBUSTOS

- ▨ 401- Salvia guaranitica "Salvia azul" E3L 7 x m2 Cant. Total 1400 unidades
- ▨ 402-Salvia leucantha "Salvia leucanta" E3L 7 x m2 Cant. Total 260 unidades
- ▨ 403- Euryops pecnitanus "Euryops" E3L 6 x m2 Cant. Total 800 unidades

ÁREA DE INTERVENCIÓN

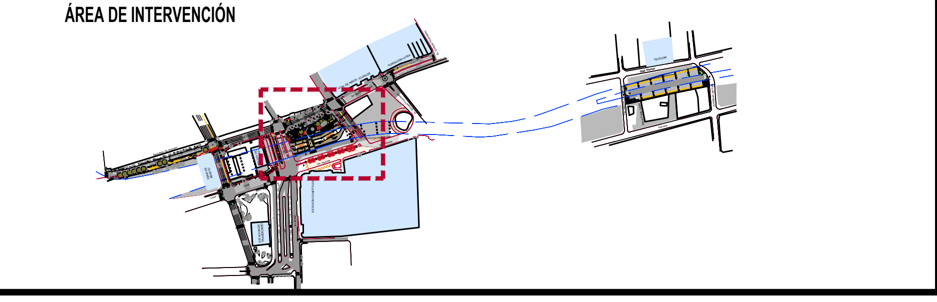

Gobierno de la Ciudad de Buenos Aires

MINISTERIO DE MOVILIDAD E INFRAESTRUCTURA
SUBSECRETARIA DE PROYECTOS Y OBRAS
DIRECCION GENERAL DE PROYECTOS

DGPRO

Obra: CT CONSTITUCION
Rubro: PAISAJISMO
Tramo: -
Plano: CTC_ARQ_Playa de regulación 2
Revisión: Rev.00
Fecha: 07/01/2026
Escala: -
Plano N° A12

MODIFICACIONES:

REVISION	FECHA	DESCRIPCION
-	-	-
-	-	-
-	-	-
-	-	-
-	-	-
-	-	-
-	-	-
-	-	-
-	-	-
-	-	-

NOTAS: EL PRESENTE PLANO ES INDICATIVO. LA CONTRATISTA CONFECCIONARA LOS PLANOS DE DETALLE DEFINITIVO, QUE DEBERAN SER APROBADOS POR LA D.G.O.INF.U Y LA INSPECCION DE OBRA. EL PLANO PRESENTADO POR LA CONTRATISTA ESTARA EN UN TODO DE ACUERDO CON LA NORMATIVA VIGENTE
TODAS LAS MEDIDAS Y NIVELES SE VERIFICARAN EN OBRA POR EL CONTRATISTA.
TODOS LOS DETALLES CONSTRUCTIVOS SERÁN COORDINADOS Y COMPATIBILIZADOS EN OBRA

PLANO NO APTO PARA CONSTRUCCIÓN

GOBIERNO DE LA CIUDAD DE BUENOS AIRES
"2026 - Año del 30° Aniversario de la sanción de la Constitución de la Ciudad Autónoma de Buenos Aires"

Hoja Adicional de Firmas
Plano

Número: PLANO-2026-06754020-GCABA-DGPRO

Buenos Aires, Viernes 30 de Enero de 2026

Referencia: PAISAJE

El documento fue importado por el sistema GEDO con un total de 4 pagina/s.

Digitally signed by Comunicaciones Oficiales
Date: 2026.01.30 15:46:15 -03:00

GABRIEL EDUARDO ROSALES
Director General
D. G. PROYECTOS
MINISTERIO DE MOVILIDAD E INFRAESTRUCTURA

Digitally signed by Comunicaciones Oficiales
Date: 2026.01.30 15:46:17 -03:00