

CONSTITUCION - SITUACIÓN EXISTENTE_General

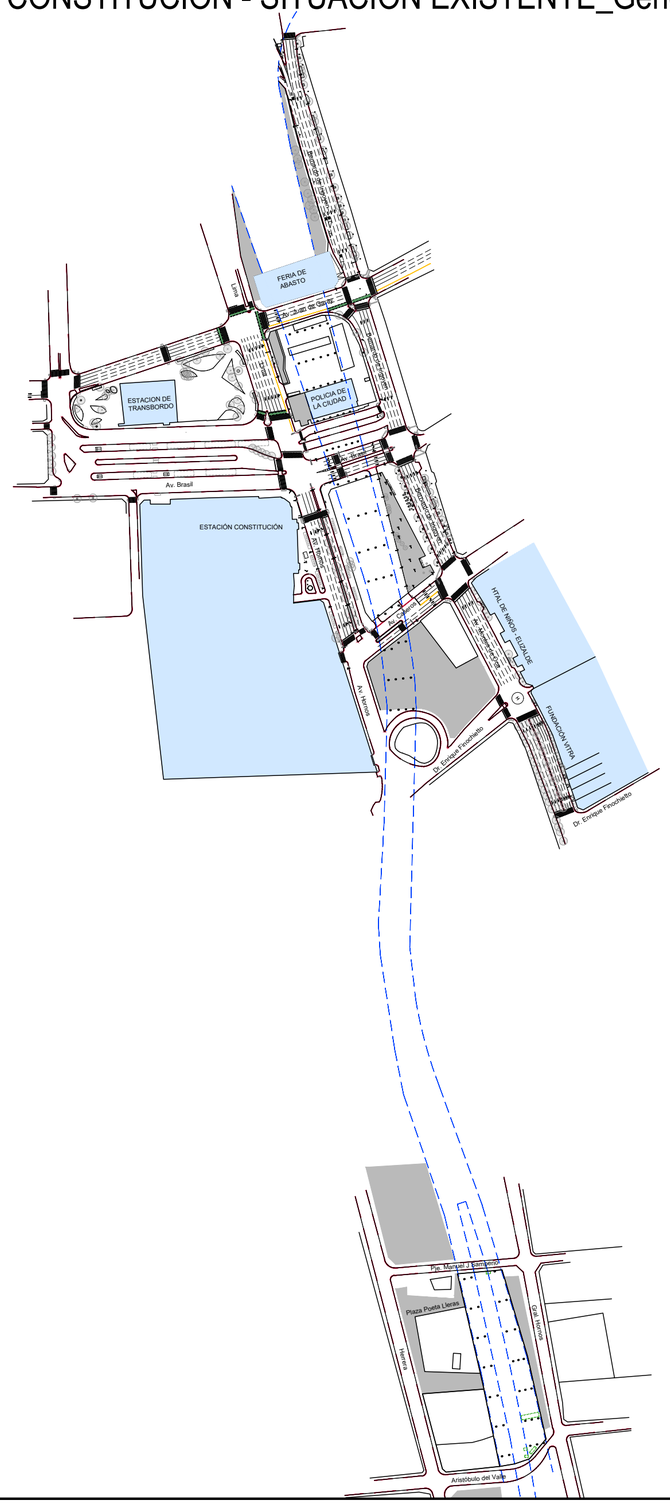


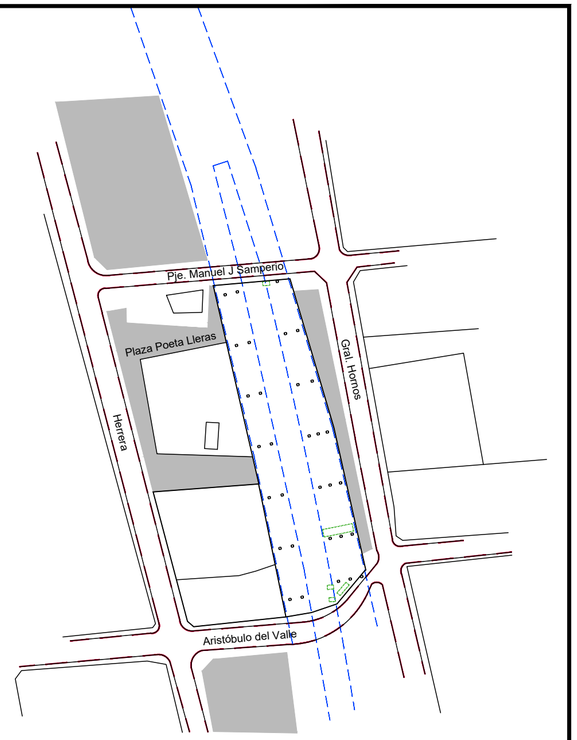

REFERENCIAS

- Edificios existentes importantes
- Áreas verdes existentes
- Árboles existentes
- Límite cordon existente
- Proyección de la Autopista
- Columnas Autopista
- Semáforos Existentes
- Demarcación Existente
- Vados Existentes
- Luminaria Existente
- Demarcador de carril "Tortuga" Existente
- Puesto Existente
- Paradores Existentes
- Accesos Vehiculares existentes
- Bicisenda Existente
- Bancos Existente
- Planteras Existentes
- Sumideros Existentes

ÁREA DE INTERVENCIÓN

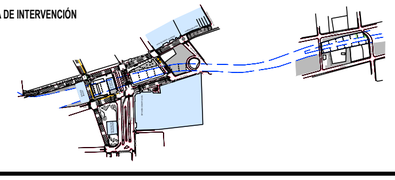

MINISTERIO DE MOVILIDAD E INFRAESTRUCTURA
SUBSECRETARIA DE PROYECTOS Y OBRAS
DIRECCION GENERAL DE PROYECTOS

DGPRO

Obra: CT CONSTITUCION	Plano: CTC_SA_General	Plano N° A01
Rubro: SITUACIÓN EXISTENTE	Revisión: Rev.00	
Tramo:-	Fecha: 07/01/2026	Escala:-

MODIFICACIONES:


REVISION	FECHA	DESCRIPCIÓN
-	-	-
-	-	-
-	-	-
-	-	-
-	-	-
-	-	-
-	-	-
-	-	-
-	-	-

NOTAS: EL PRESENTE PLANO ES INDICATIVO. LA CONTRATISTA CONFECCIONARA LOS PLANOS DE DETALLE DEFINITIVO, QUE DEBERAN SER APROBADOS POR LA D.G.O.M.P. Y LA INSPECCION DE OBRA. EL PLANO PRESENTADO POR LA CONTRATISTA ESTARA EN UN TODO DE ACUERDO CON LA NORMATIVA VIGENTE

PLANO NO APTO PARA CONSTRUCCIÓN

PLANO-2026-06754424-GCABA-DGPRO

CONSTITUCION - SITUACIÓN EXISTENTE_Bernardo de Irigoyen

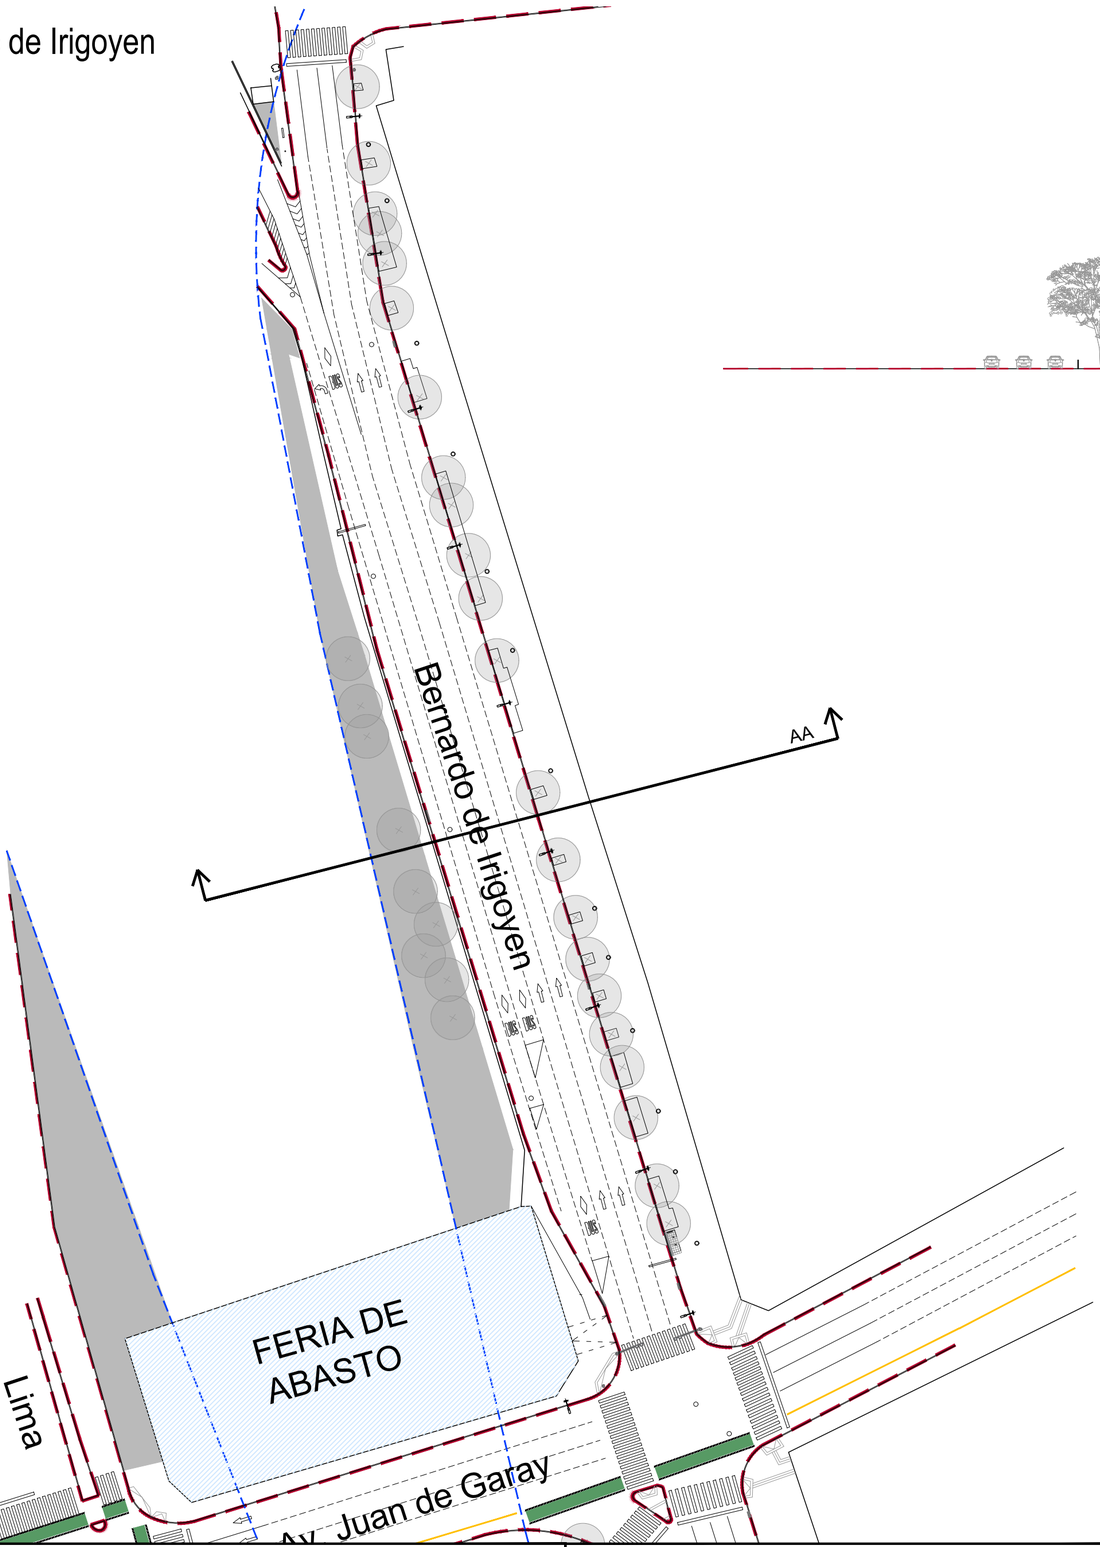




AA - Esc. 1:500

REFERENCIAS

- Edificios existentes importantes
- Áreas verdes existentes
- Árboles existentes
- Límite cordon existente
- Proyección de la Autopista
- Columnas Autopista
- Semáforos Existentes
- Demarcación Existente
- Vados Existentes
- Luminaria Existente
- Demarcador de carril "Tortuga" Existente
- Puesto Existente
- Paradores Existentes
- Accesos Vehiculares existentes
- Bicisenda Existente
- Bancos Existente
- Planteras Existentes
- Sumideros Existentes

ÁREA DE INTERVENCIÓN

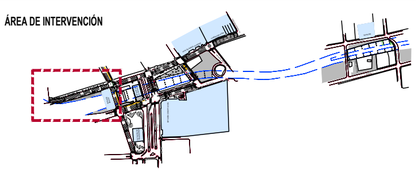

Gobierno de la Ciudad de Buenos Aires

MINISTERIO DE MOVILIDAD E INFRAESTRUCTURA
SUBSECRETARIA DE PROYECTOS Y OBRAS
DIRECCION GENERAL DE PROYECTOS

DGPRO

Obra: CT CONSTITUCION	Plano: CTC_SA_Bernardo de Irigoyen	Plano N° A02
Rubro: SITUACIÓN EXISTENTE	Revisión: Rev.00	
Tramo:-	Fecha: 07/01/2026 Escala:-	

MODIFICACIONES:


REVISION	FECHA	DESCRIPCION
-	-	-
-	-	-
-	-	-
-	-	-
-	-	-
-	-	-
-	-	-
-	-	-
-	-	-

NOTAS: EL PRESENTE PLANO ES INDICATIVO. LA CONTRATISTA CONFECCIONARÁ LOS PLANOS DE DETALLE DEFINITIVO, QUE DEBERÁN SER APROBADOS POR LA D.G.I.M.E Y LA INSPECCIÓN DE OBRA. EL PLANO PRESENTADO POR LA CONTRATISTA ESTARÁ EN UN TODO DE ACUERDO CON LA NORMATIVA VIGENTE.
TODA DISCREPANCIA ENTRE LO EXISTENTE Y LO REPRESENTADO EN EL PRESENTE PLANO DEBERÁ SER COMUNICADA A LA INSPECCIÓN DE OBRA.


PLANO NO APTO PARA CONSTRUCCIÓN

PLANO-2026-06754424-GCABA-DGPRO

CONSTITUCION - SITUACIÓN EXISTENTE_Av. Hornos

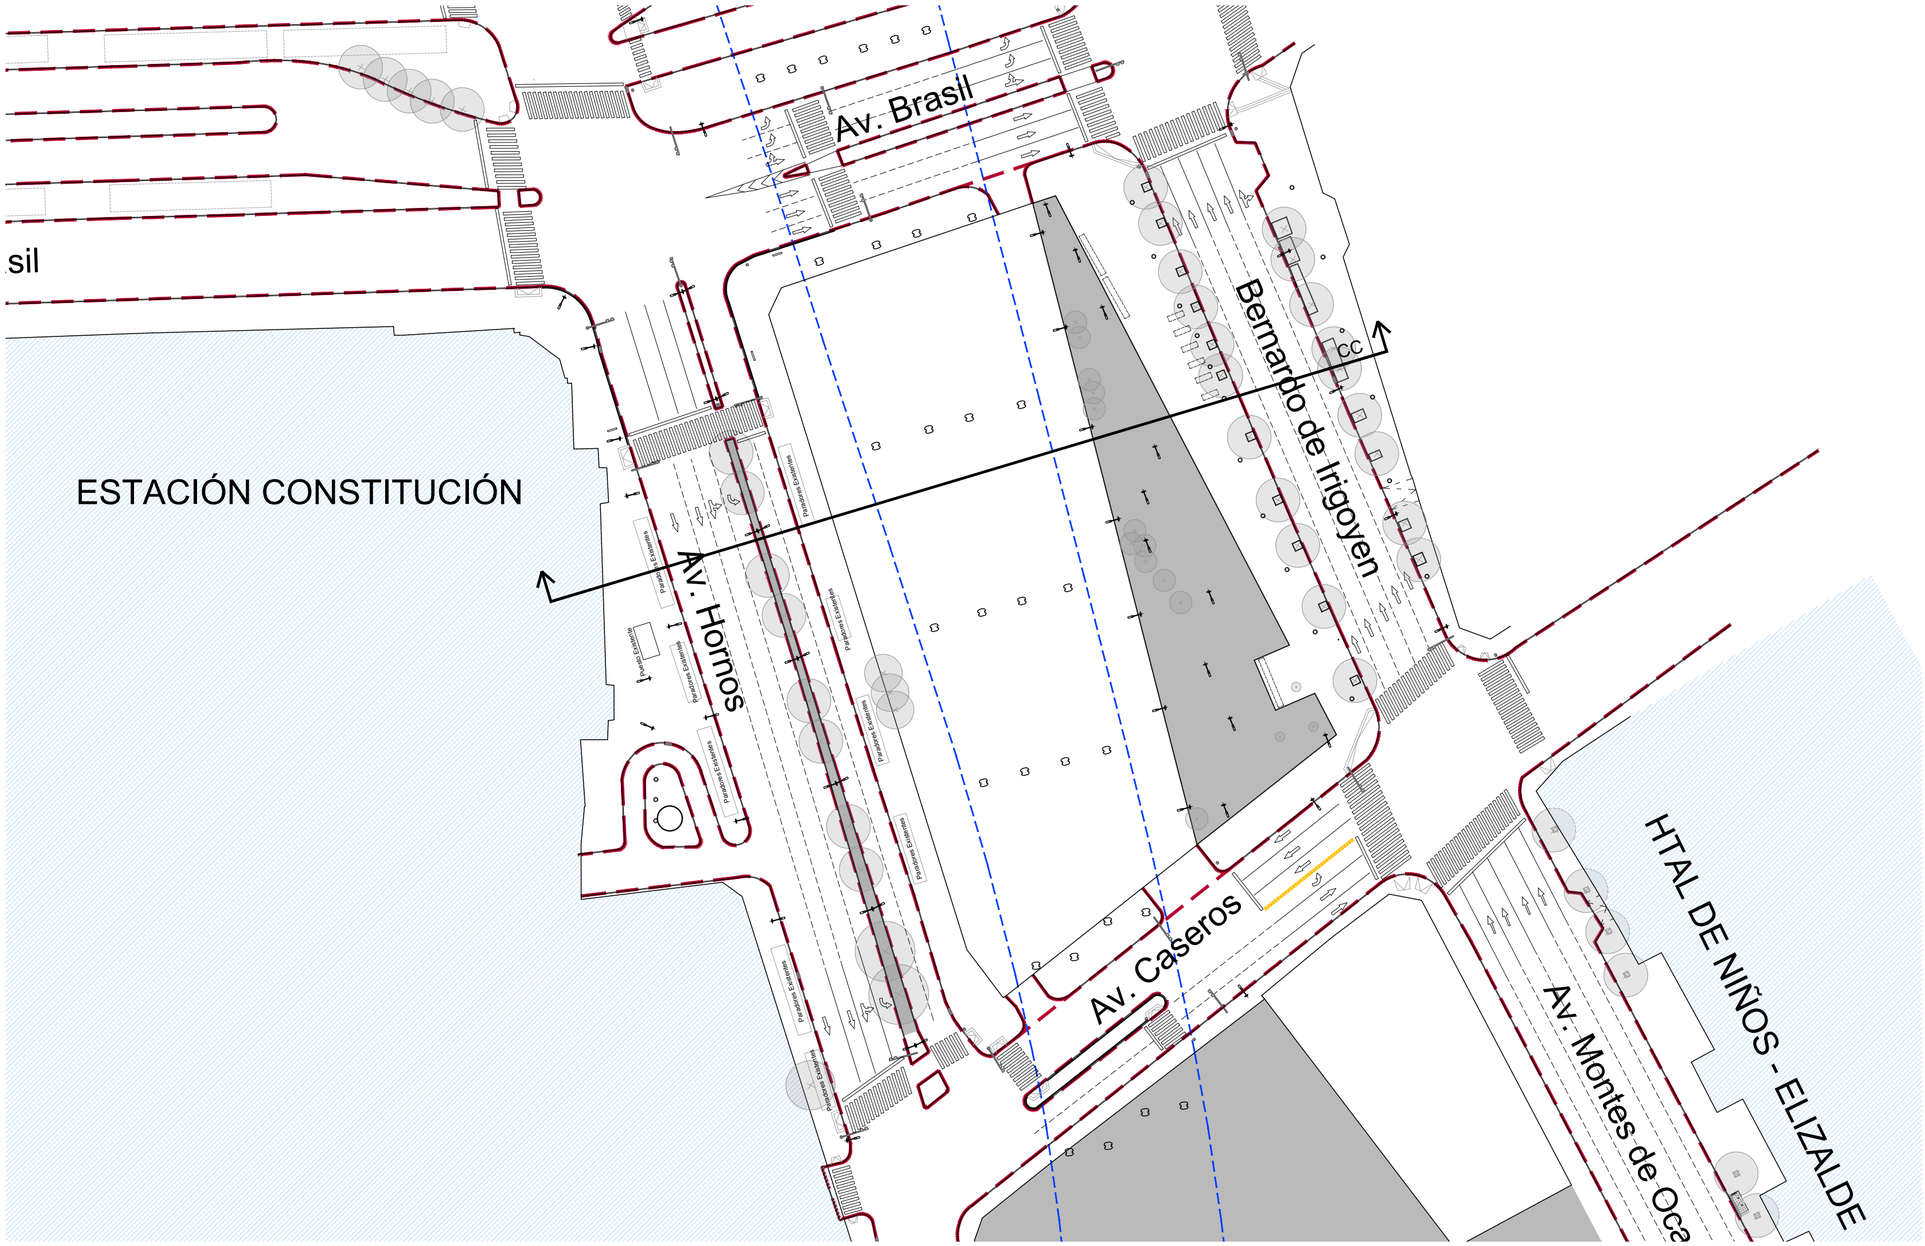

Perfil existente Bajo Autopista

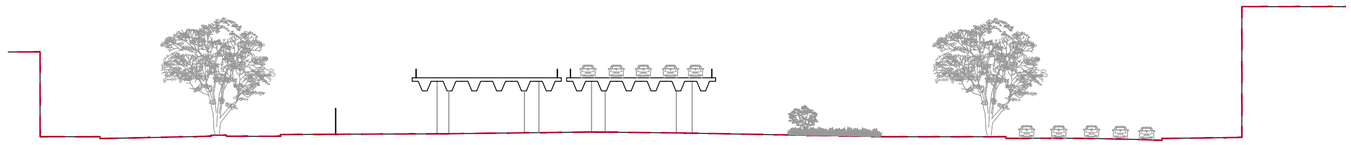


CC - Esc. 1:500

REFERENCIAS

- Edificios existentes importantes
- Áreas verdes existentes
- Árboles existentes
- Límite cordon existente
- Proyección de la Autopista
- Columnas Autopista
- Semáforos Existentes
- Demarcación Existente
- Vados Existentes
- Luminaria Existente
- Demarcador de carril "Tortuga" Existente
- Puesto Existente / Paradores Existentes
- Accesos Vehiculares existentes
- Bicisenda Existente
- Bancos Existente
- Planteras Existentes
- Sumideros Existentes

ÁREA DE INTERVENCIÓN

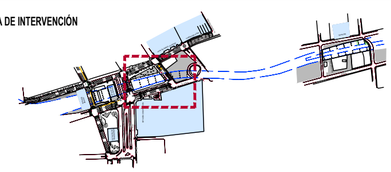

Gobierno de la Ciudad de Buenos Aires

MINISTERIO DE MOVILIDAD E INFRAESTRUCTURA
SUBSECRETARIA DE PROYECTOS Y OBRAS
DIRECCION GENERAL DE PROYECTOS

DGPRO

Obra: CT CONSTITUCION	Plano: CTC_SA_Av. Hornos	Plano N° A03
Rubro: SITUACIÓN EXISTENTE	Revisión: Rev.00	
Tramo:-	Fecha: 07/01/2026 Escala:-	

MODIFICACIONES:


REVISION	FECHA	DESCRIPCION
-	-	-
-	-	-
-	-	-
-	-	-
-	-	-
-	-	-
-	-	-
-	-	-


NOTAS: EL PRESENTE PLANO ES INDICATIVO. LA CONTRATISTA CONFECCIONARÁ LOS PLANOS DE DETALLE DEFINITIVO, QUE DEBERÁN SER APROBADOS POR LA D.G.IM.P. Y LA INSPECCIÓN DE OBRA. EL PLANO PRESENTADO POR LA CONTRATISTA ESTARÁ EN UN TODO DE ACUERDO CON LA NORMATIVA VIGENTE

PLANO NO APTO PARA CONSTRUCCIÓN

PLANO-2026-06754424-GCABA-DGPRO

CONSTITUCION - SITUACIÓN EXISTENTE_Av. Montes de Oca.

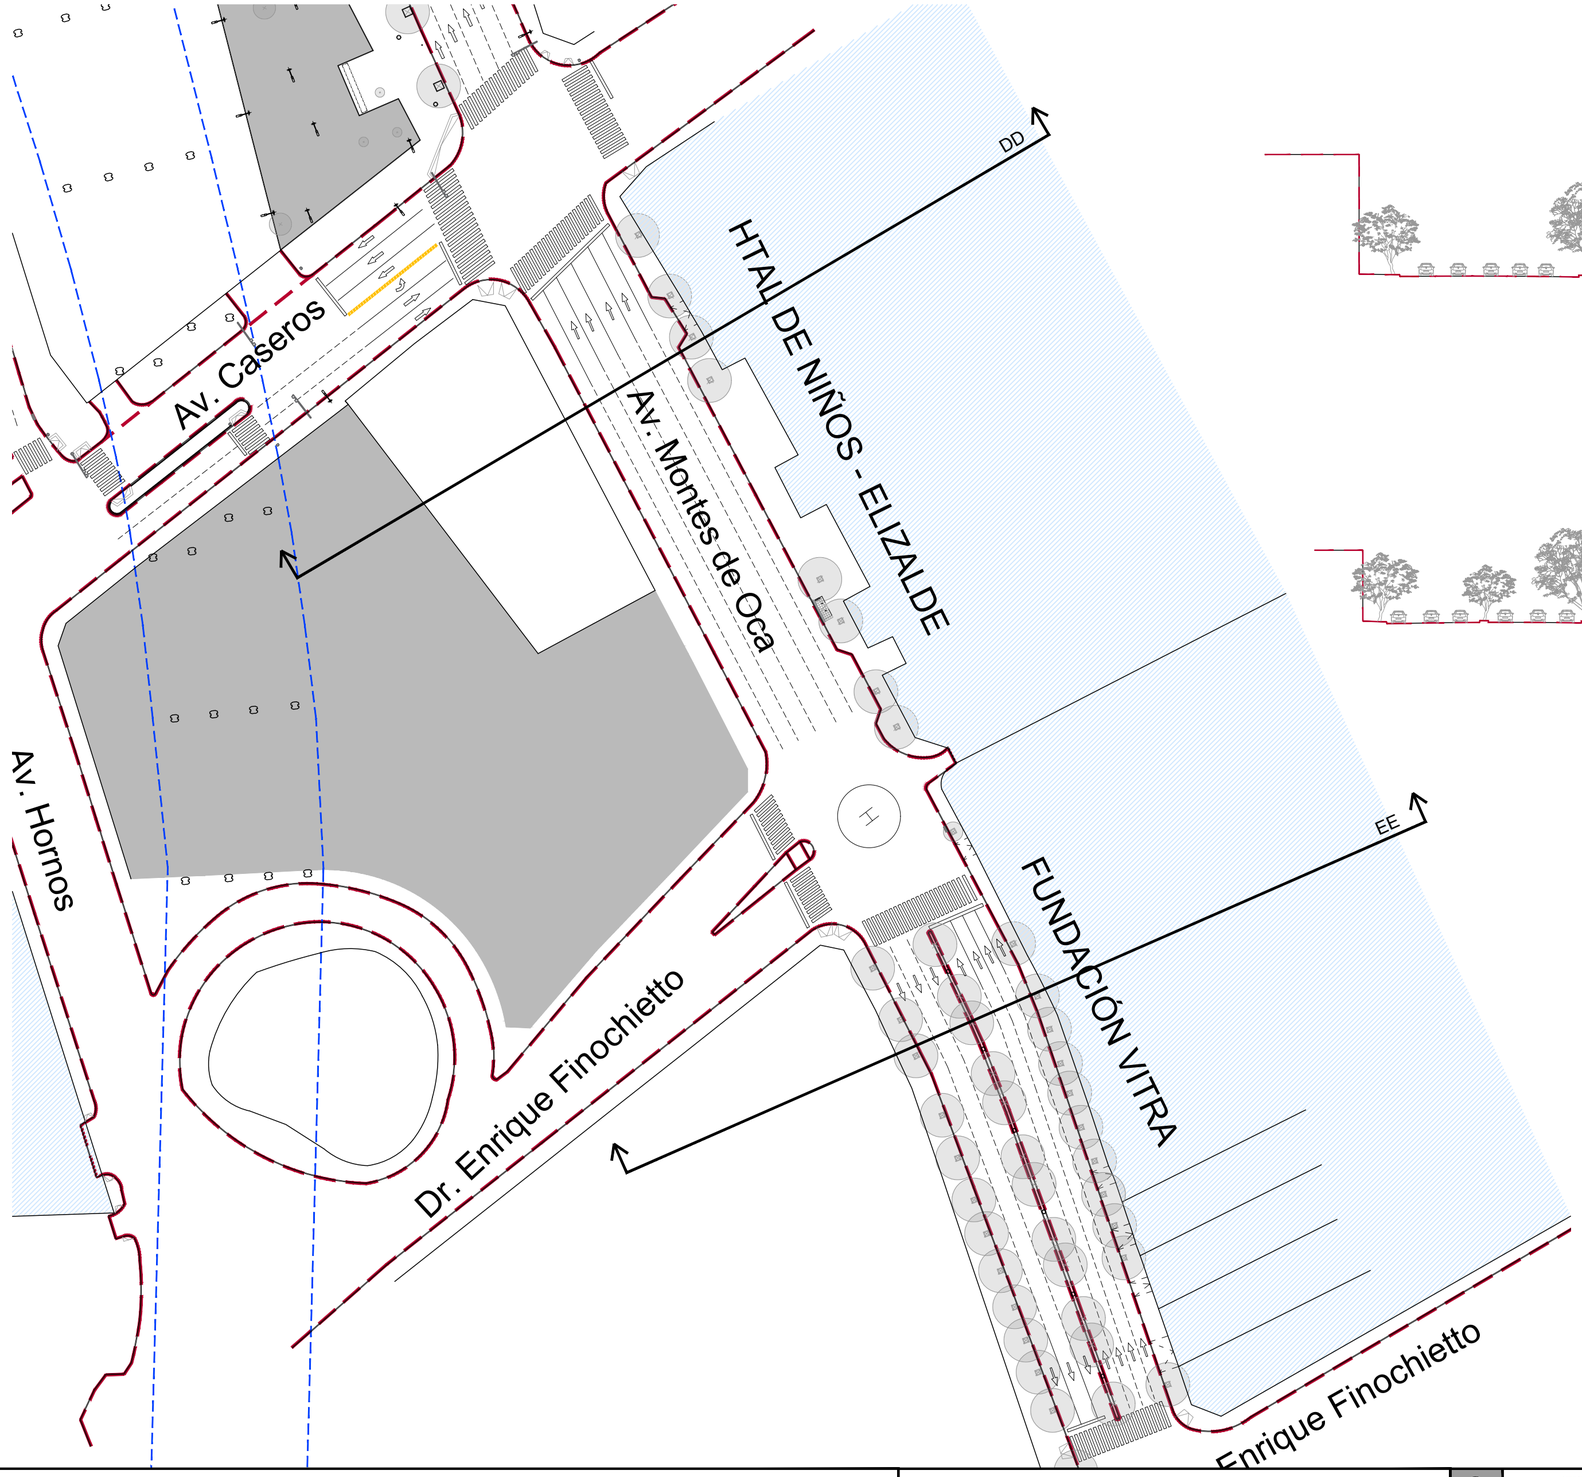

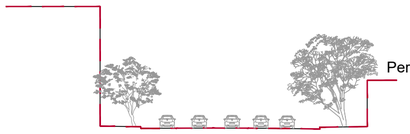

Perfil existente Av. Montes de Oca 1

DD - Esc. 1:500




Perfil existente Av. Montes de Oca 2

EE - Esc. 1:500

REFERENCIAS

- Edificios existentes importantes
- Áreas verdes existentes
- Árboles existentes
- Límite cordon existente
- Proyección de la Autopista
- Columnas Autopista
- Semáforos Existentes
- Demarcación Existente
- Vados Existentes
- Luminaria Existente
- Demarcador de carril "Tortuga" Existente
- Puesto Existente
- Paradores Existentes
- Accesos Vehiculares existentes
- Bicisenda Existente
- Bancos Existente
- Planteras Existentes
- Sumideros Existentes

ÁREA DE INTERVENCIÓN

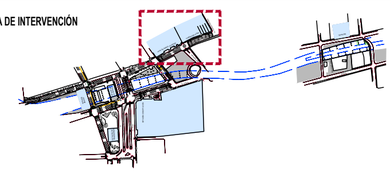

Gobierno de la Ciudad de Buenos Aires

MINISTERIO DE MOVILIDAD E INFRAESTRUCTURA
SUBSECRETARIA DE PROYECTOS Y OBRAS
DIRECCION GENERAL DE PROYECTOS

DGPRO

Obra: CT CONSTITUCION	Plano: CTC_SA_Av. Montes de Oca	Plano N° A04
Rubro: SITUACIÓN EXISTENTE	Revisión: Rev.00	
Tramo:-	Fecha: 07/01/2026 Escala:-	

MODIFICACIONES:


REVISION	FECHA	DESCRIPCION
-	-	-
-	-	-
-	-	-
-	-	-
-	-	-
-	-	-
-	-	-
-	-	-
-	-	-

NOTAS: EL PRESENTE PLANO ES INDICATIVO. LA CONTRATISTA CONFECCIONARÁ LOS PLANOS DE DETALLE DEFINITIVO, QUE DEBERÁN SER APROBADOS POR LA D.G.M.E Y LA INSPECCIÓN DE OBRA. EL PLANO PRESENTADO POR LA CONTRATISTA ESTARÁ EN UN TODO DE ACUERDO CON LA NORMATIVA VIGENTE.
TODA DISCREPANCIA ENTRE EL PRESENTE PLANO Y LA REALIDAD DEBERÁ SER COMUNICADA


PLANO NO APTO PARA CONSTRUCCIÓN

PLANO-2026-06754424-GCABA-DGPRO

CONSTITUCION - SITUACIÓN EXISTENTE_Playa de regulación 2

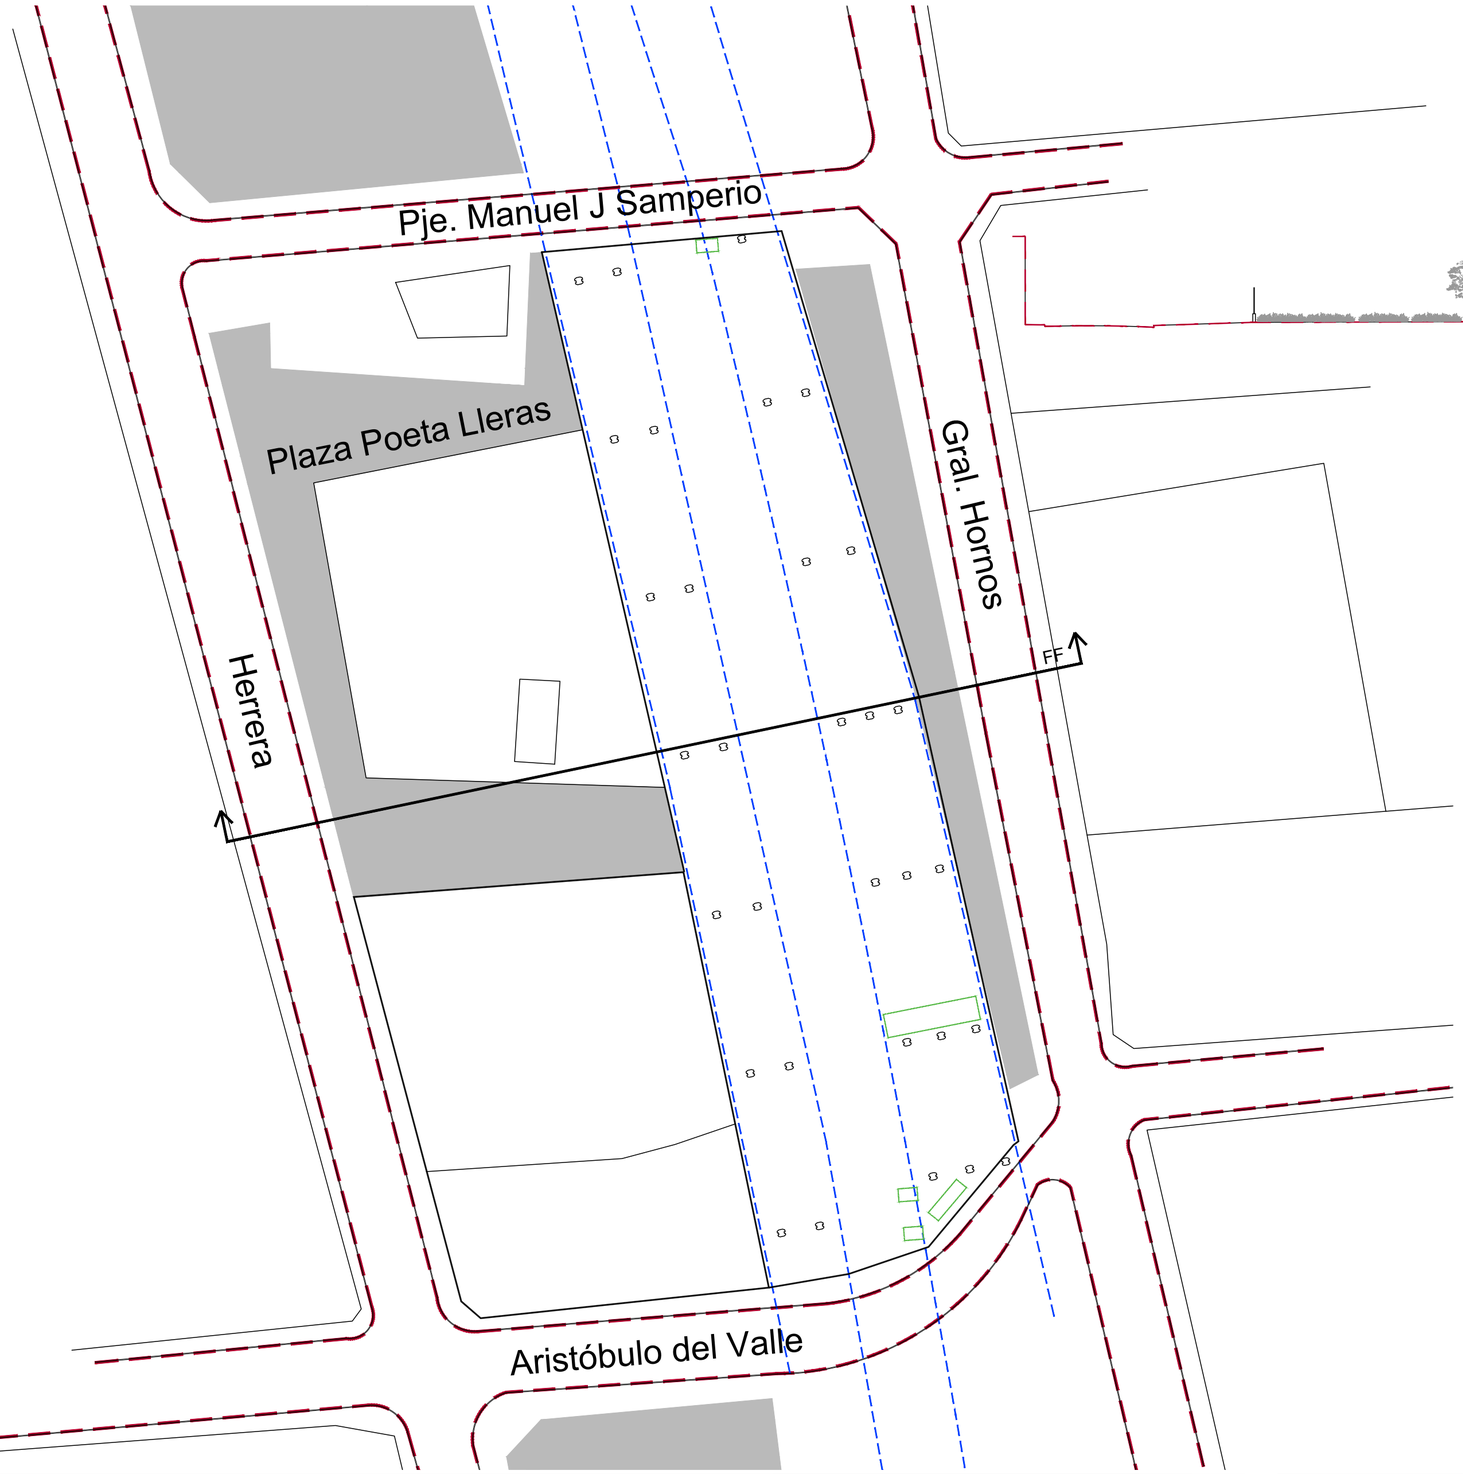

Perfil existente Playa de regulacion 2

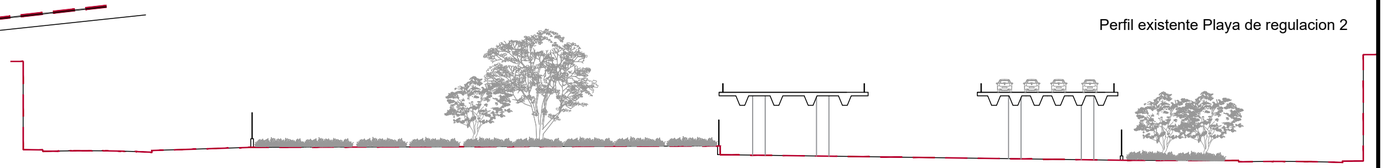


FF - Esc. 1:500

REFERENCIAS

- Edificios existentes importantes
- Áreas verdes existentes
- Árboles existentes
- Límite cordon existente
- Proyección de la Autopista
- Columnas Autopista
- Semáforos Existentes
- Demarcación Existente
- Vados Existentes
- Luminaria Existente
- Demarcador de carril "Tortuga" Existente
- Puesto Existente
- Paradores Existentes
- Accesos Vehiculares existentes
- Bicisenda Existente
- Bancos Existente
- Planteras Existentes
- Sumideros Existentes

ÁREA DE INTERVENCIÓN

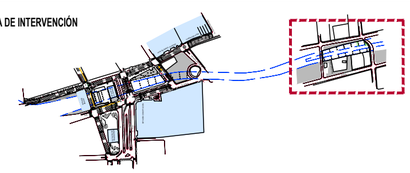

Gobierno de la Ciudad de Buenos Aires

MINISTERIO DE MOVILIDAD E INFRAESTRUCTURA
SUBSECRETARIA DE PROYECTOS Y OBRAS
DIRECCION GENERAL DE PROYECTOS

DGPRO

Obra: CT CONSTITUCION	Plano: CTC_SA_Playa de regulación 2	Plano N° A05
Rubro: SITUACIÓN EXISTENTE	Revisión: Rev.00	
Tramo:-	Fecha: 07/01/2026 Escala:-	

MODIFICACIONES:

REVISION	FECHA	DESCRIPCION
-	-	-
-	-	-
-	-	-
-	-	-
-	-	-
-	-	-
-	-	-
-	-	-
-	-	-
-	-	-

NOTAS: EL PRESENTE PLANO ES INDICATIVO. LA CONTRATISTA CONFECCIONARA LOS PLANOS DE DETALLE DEFINITIVO, QUE DEBERAN SER APROBADOS POR LA D.G.D.M.F.V Y LA INSPECCION DE OBRA. EL PLANO PRESENTADO POR LA CONTRATISTA ESTARA EN UN TODO DE ACUERDO CON LA NORMATIVA VIGENTE

PLANO NO APTO PARA CONSTRUCCIÓN

PLANO-2026-06754424-GCABA-DGPRO

G O B I E R N O DE LA C I U D A D DE B U E N O S A I R E S

"2026 - Año del 30° Aniversario de la sanción de la Constitución de la Ciudad Autónoma de Buenos Aires"

Hoja Adicional de Firmas
Plano

Número: PLANO-2026-06754424-GCABA-DGPRO

Buenos Aires, Viernes 30 de Enero de 2026

Referencia: SITUACION ACTUAL

El documento fue importado por el sistema GEDO con un total de 5 pagina/s.

Digitally signed by Comunicaciones Oficiales
Date: 2026.01.30 15:47:54 -03:00

GABRIEL EDUARDO ROSALES
Director General
D. G. PROYECTOS
MINISTERIO DE MOVILIDAD E INFRAESTRUCTURA

Digitally signed by Comunicaciones Oficiales
Date: 2026.01.30 15:47:54 -03:00