CONSTITUCION - PROYECTO_Av. Hornos

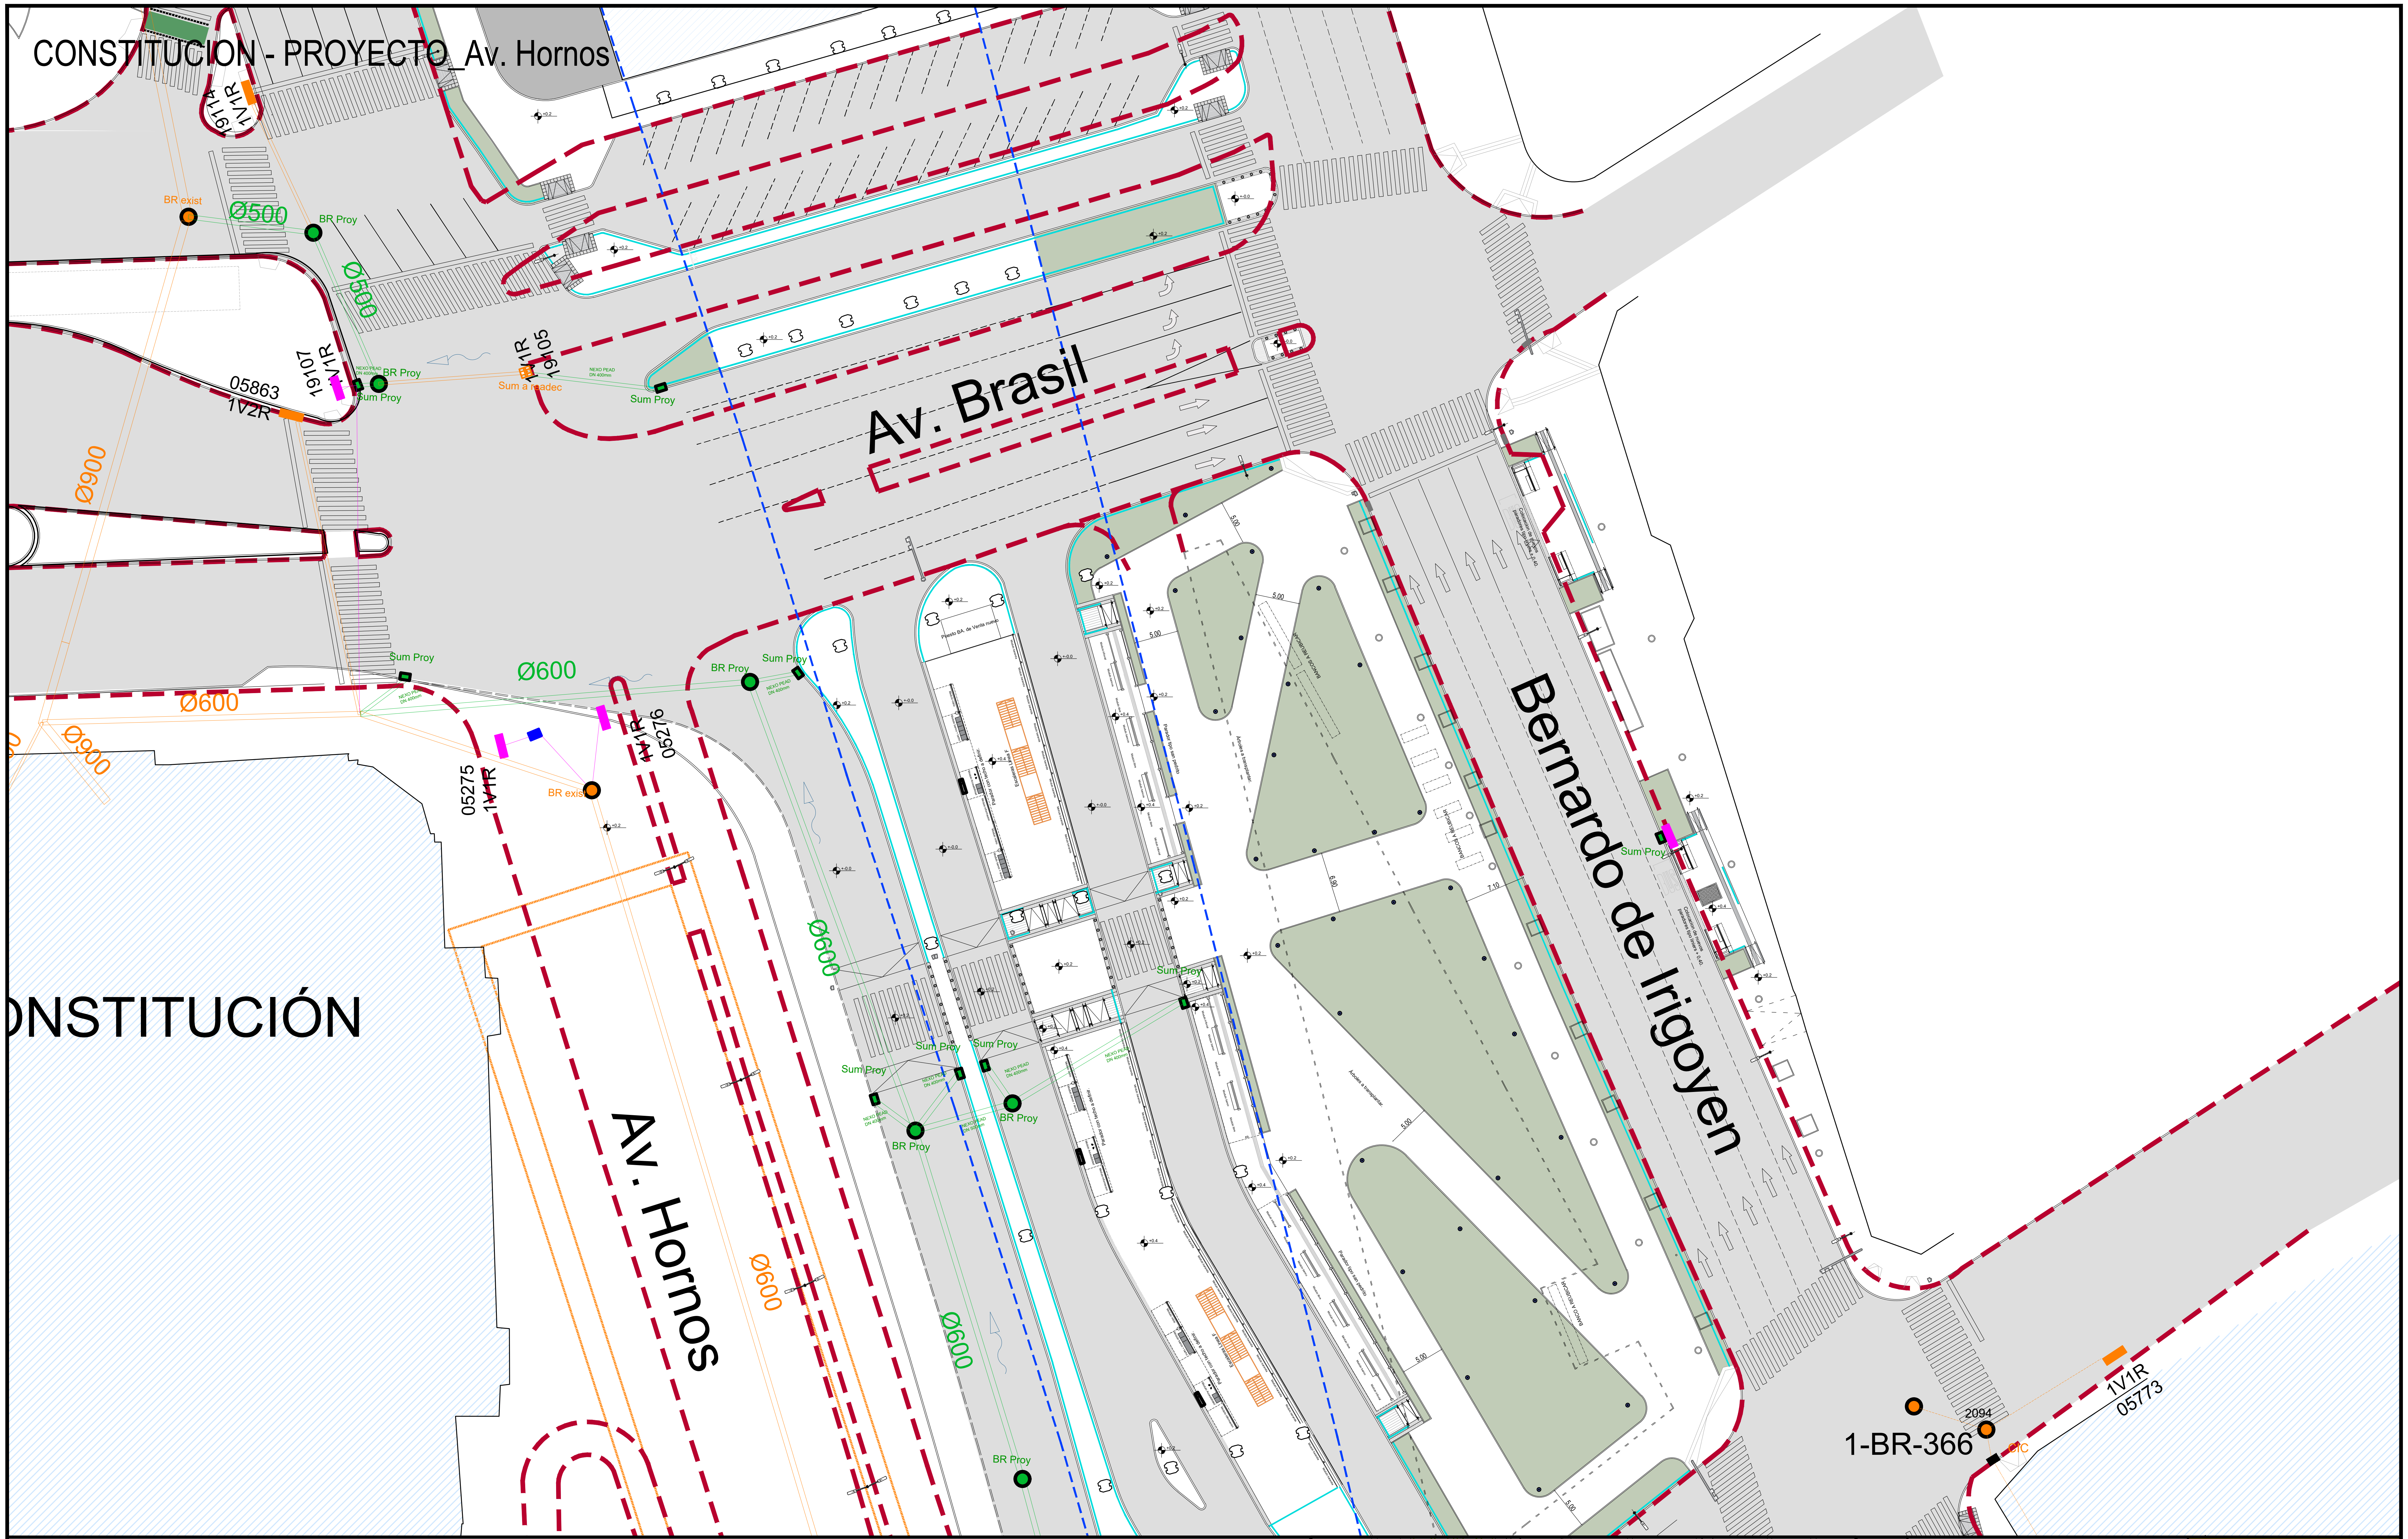
Av. Brasil
Bernardo de Irigoyen
Av. Hornos
CONSTITUCIÓN
BR exist
BR Proy
Sum Proy
Sum a readec
Ø500
Ø600
Ø900
Ø600
1V1R
19114
19107
1V1R
05863
1V2R
1V1R
19105
05275
1V1R
1V1R
05276
1-BR-366
2094
CIC
1V1R
05773

REFERENCIAS

Nexo existente a anular	Sumidero existente a readecuar	Conducto pluvial PEAD (NEXO PEAD DN 400mm)	Cámara de inspección 0,6 x 0,6
Conducto existente (Ø800; HºAº)	Boca de registro existente	Sumidero mixto de 100 x 50	Sumidero existente a anular
Albañal existente	Boca de registro a ejecutar	Canaleta de hormigón con rejilla galvanizada	

ÁREA DE INTERVENCIÓN

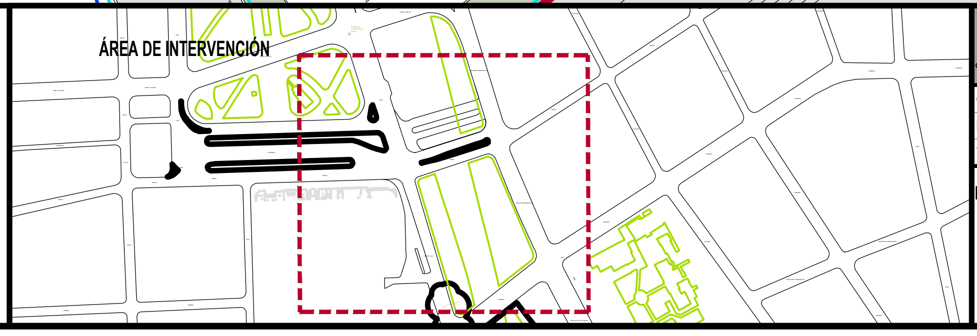

Gobierno de la Ciudad de Buenos Aires

MINISTERIO DE MOVILIDAD E INFRAESTRUCTURA
SUBSECRETARIA DE PROYECTOS Y OBRAS
DIRECCION GENERAL DE PROYECTOS

DGPRO

Obra: CT CONSTITUCION	Plano: CTC_HID_Av. Hornos-1	Plano N° 01
Rubro: HIDRAULICA	Revisión: Rev.00	
Tramo: -	Fecha: 30/01/2026 Escala: -	

MODIFICACIONES:

REVISION	FECHA	DESCRIPCION
-	-	-
-	-	-
-	-	-
-	-	-
-	-	-
-	-	-
-	-	-
-	-	-
-	-	-
-	-	-

NOTAS: EL PRESENTE PLANO ES INDICATIVO. LA CONTRATISTA CONFECCIONARA LOS PLANOS DE DETALLE DEFINITIVO, QUE DEBERAN SER APROBADOS POR LA D.G.O.INF.U Y LA INSPECCION DE OBRA. EL PLANO PRESENTADO POR LA CONTRATISTA ESTARA EN UN TODO DE ACUERDO CON LA NORMATIVA VIGENTE
TODAS LAS MEDIDAS Y NIVELES SE VERIFICARAN EN OBRA POR EL CONTRATISTA.
TODOS LOS DETALLES CONSTRUCTIVOS SERAN COORDINADOS Y COMPATIBILIZADOS EN OBRA.

PLANO NO APTO PARA CONSTRUCCIÓN

CONSTITUCION - PROYECTO_Av. Hornos

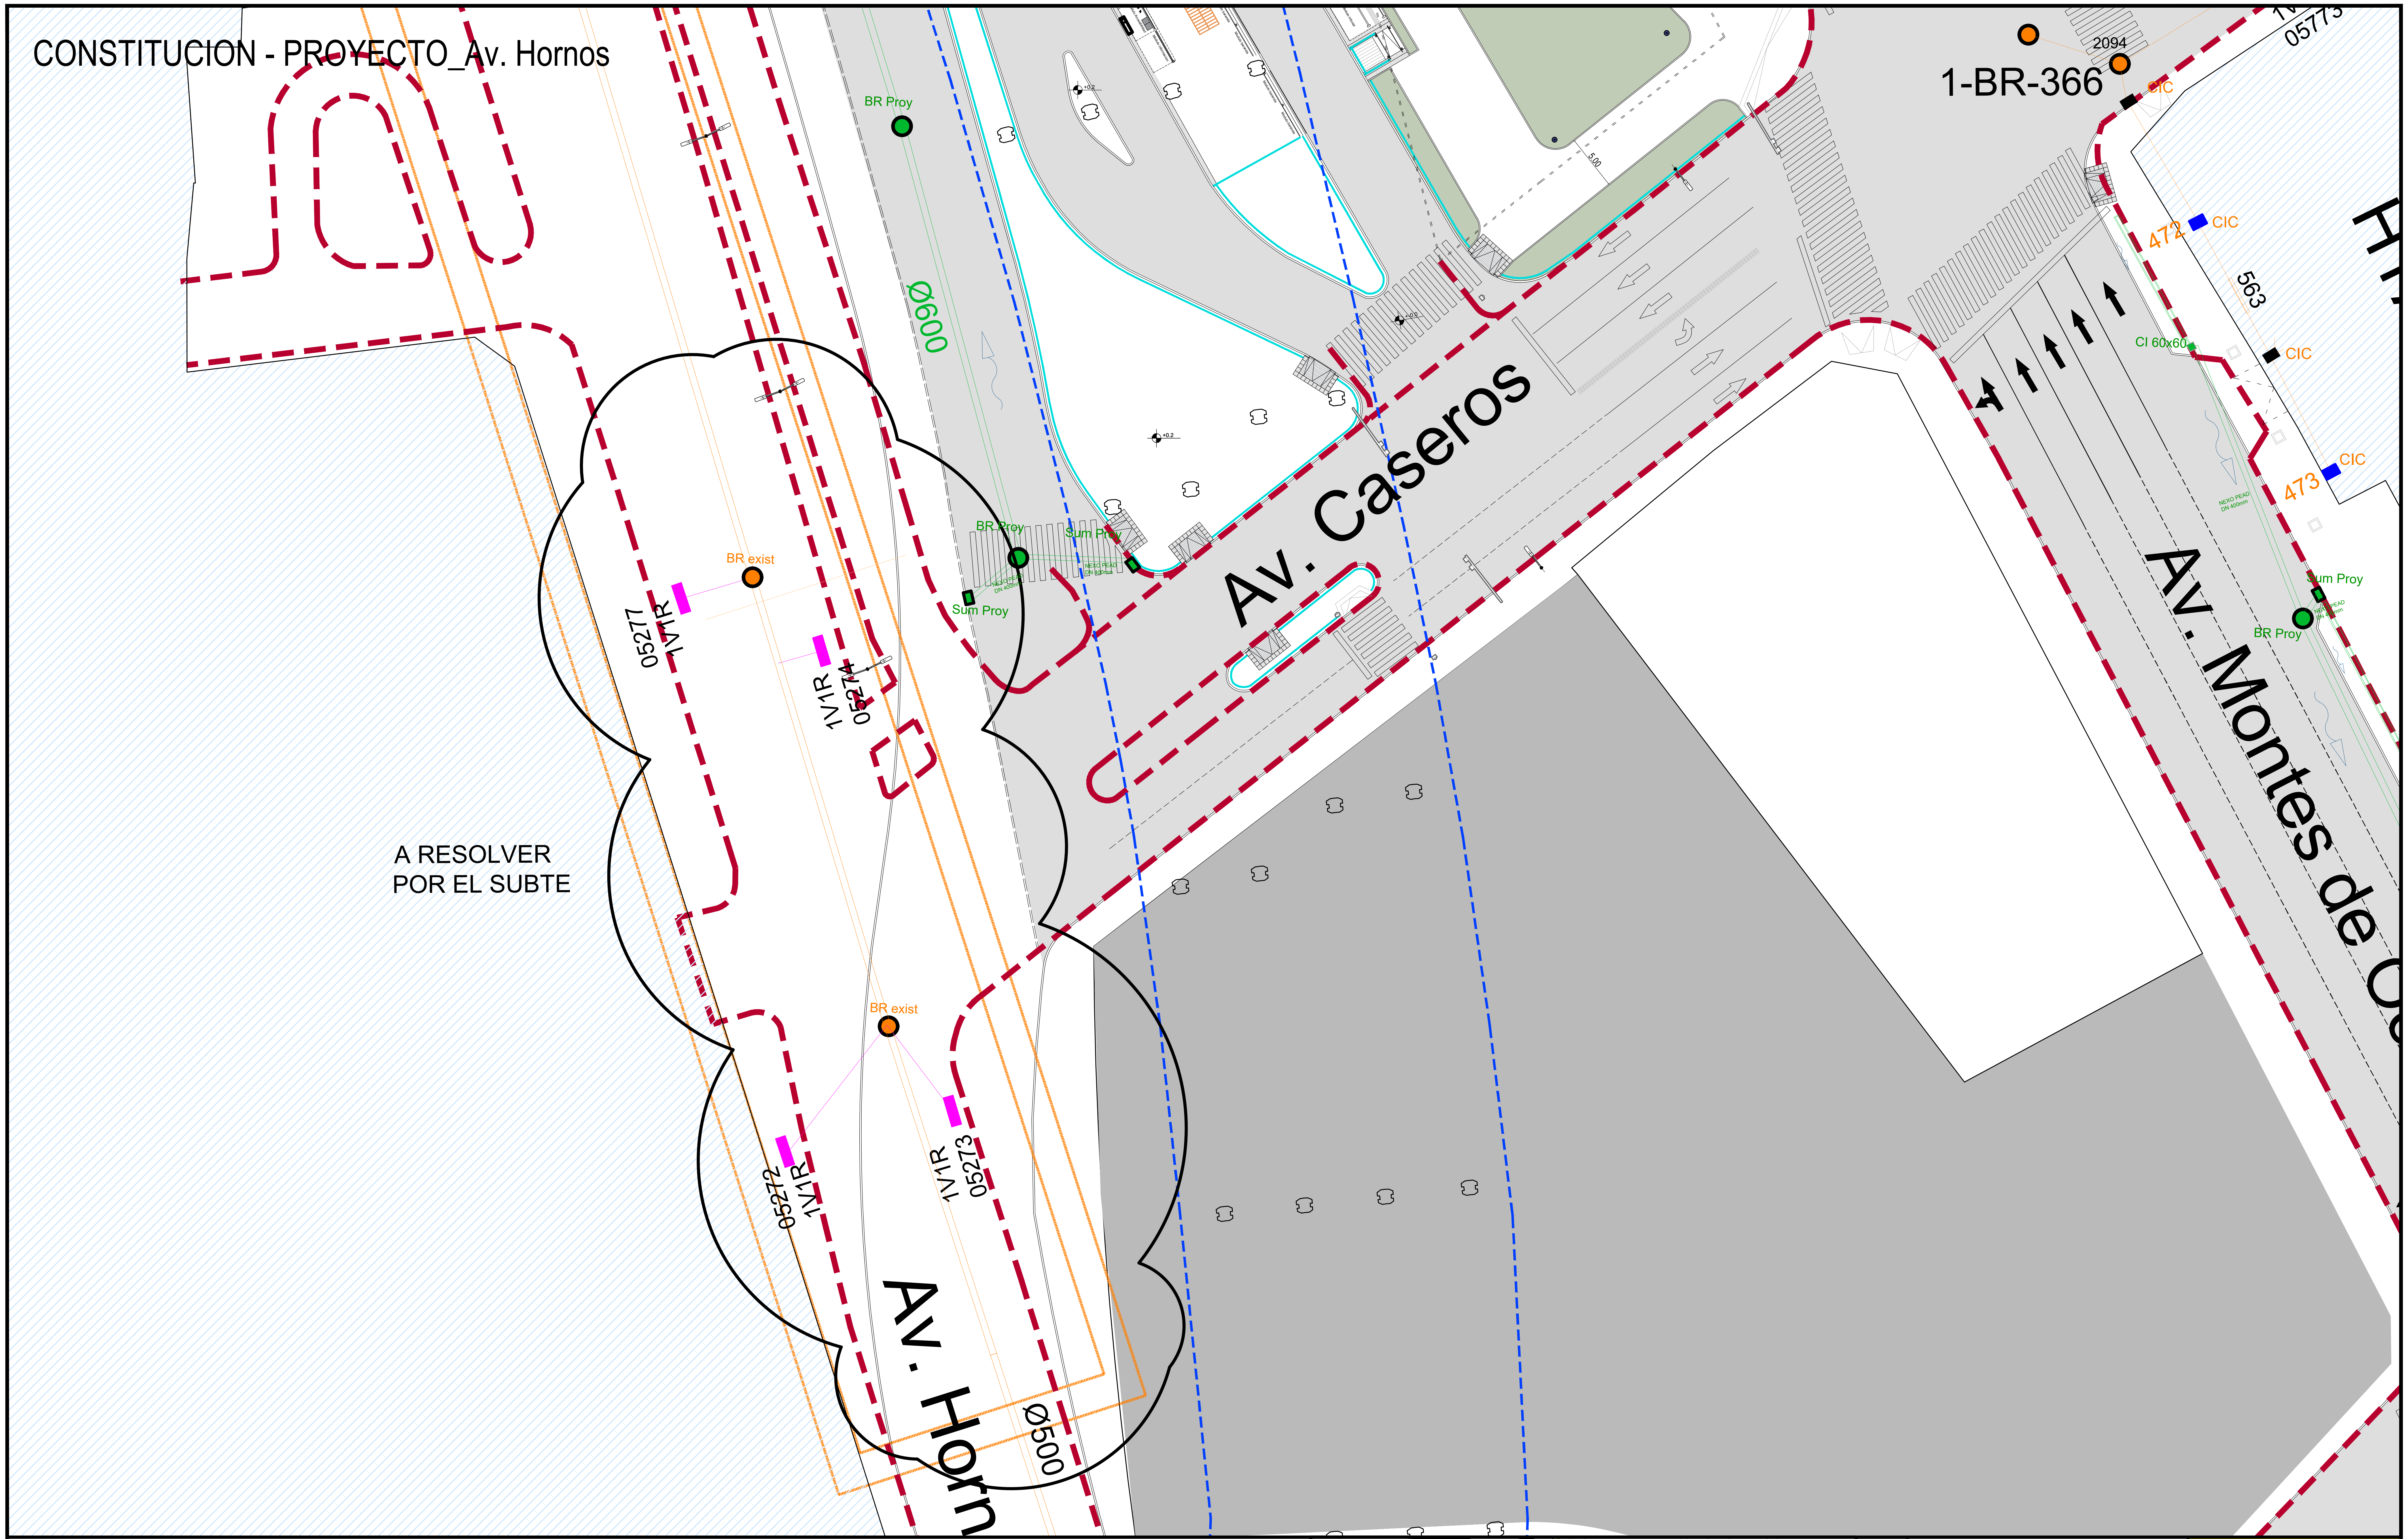
BR Proy
Ø600
1-BR-366
2094
CIC
05773
472
CIC
563
CIC
CI 60x60
CIC
473
5.00
Av. Caseros
Av. Montes de O
BR Proy
Sum Proy
Sum Proy
Sum Proy
BR Proy
BR exist
05277
1V1R
1V1R
05274
A RESOLVER
POR EL SUBTE
BR exist
05272
1V1R
1V1R
05273
Av. Horn
Ø500

REFERENCIAS

╪╪╪	Nexo existente a anular	▦	Sumidero existente a readecuar	NEXO PEAD DN 400mm ▬	Conducto pluvial PEAD	🟩	Cámara de inspección 0,6 x 0,6
Ø800; HºAº ▪▪▪	Conducto existente	●	Boca de registro existente	🟩	Sumidero mixto de 100 x 50	▬	Sumidero existente a anular
▪▪▪	Albañal existente	●	Boca de registro a ejecutar	▭	Canaleta de hormigón con rejilla galvanizada		

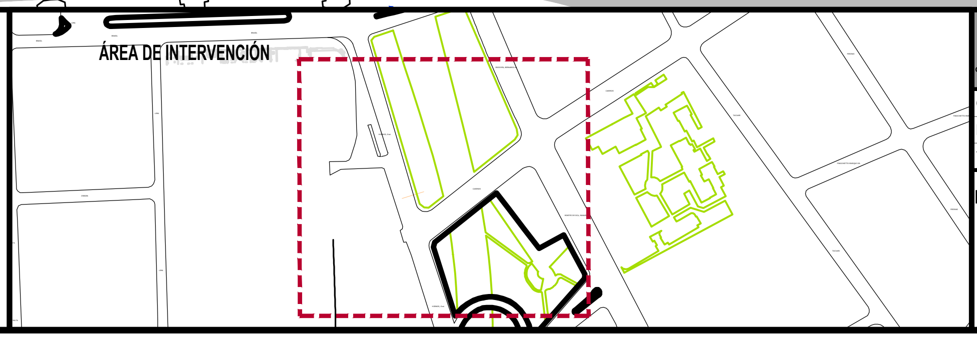
ÁREA DE INTERVENCIÓN

Gobierno de la Ciudad de Buenos Aires

MINISTERIO DE MOVILIDAD E INFRAESTRUCTURA
SUBSECRETARIA DE PROYECTOS Y OBRAS
DIRECCION GENERAL DE PROYECTOS

DGPRO

Obra: CT CONSTITUCION	Plano: CTC_HID_Av. Hornos-2	Plano N° 02
Rubro: HIDRAULICA	Revisión: Rev.00	
Tramo: -	Fecha: 30/01/2026 Escala: -	

MODIFICACIONES:

REVISION	FECHA	DESCRIPCION
-	-	-
-	-	-
-	-	-
-	-	-
-	-	-
-	-	-
-	-	-
-	-	-
-	-	-
-	-	-

NOTAS: EL PRESENTE PLANO ES INDICATIVO. LA CONTRATISTA CONFECCIONARA LOS PLANOS DE DETALLE DEFINITIVO, QUE DEBERAN SER APROBADOS POR LA D.G.O.INF.U Y LA INSPECCION DE OBRA. EL PLANO PRESENTADO POR LA CONTRATISTA ESTARA EN UN TODO DE ACUERDO CON LA NORMATIVA VIGENTE
TODAS LAS MEDIDAS Y NIVELES SE VERIFICARAN EN OBRA POR EL CONTRATISTA.
TODOS LOS DETALLES CONSTRUCTIVOS SERAN COORDINADOS Y COMPATIBILIZADOS EN OBRA.

PLANO NO APTO PARA CONSTRUCCIÓN

CONSTITUCION - PROYECTO_Av. Irigoyen

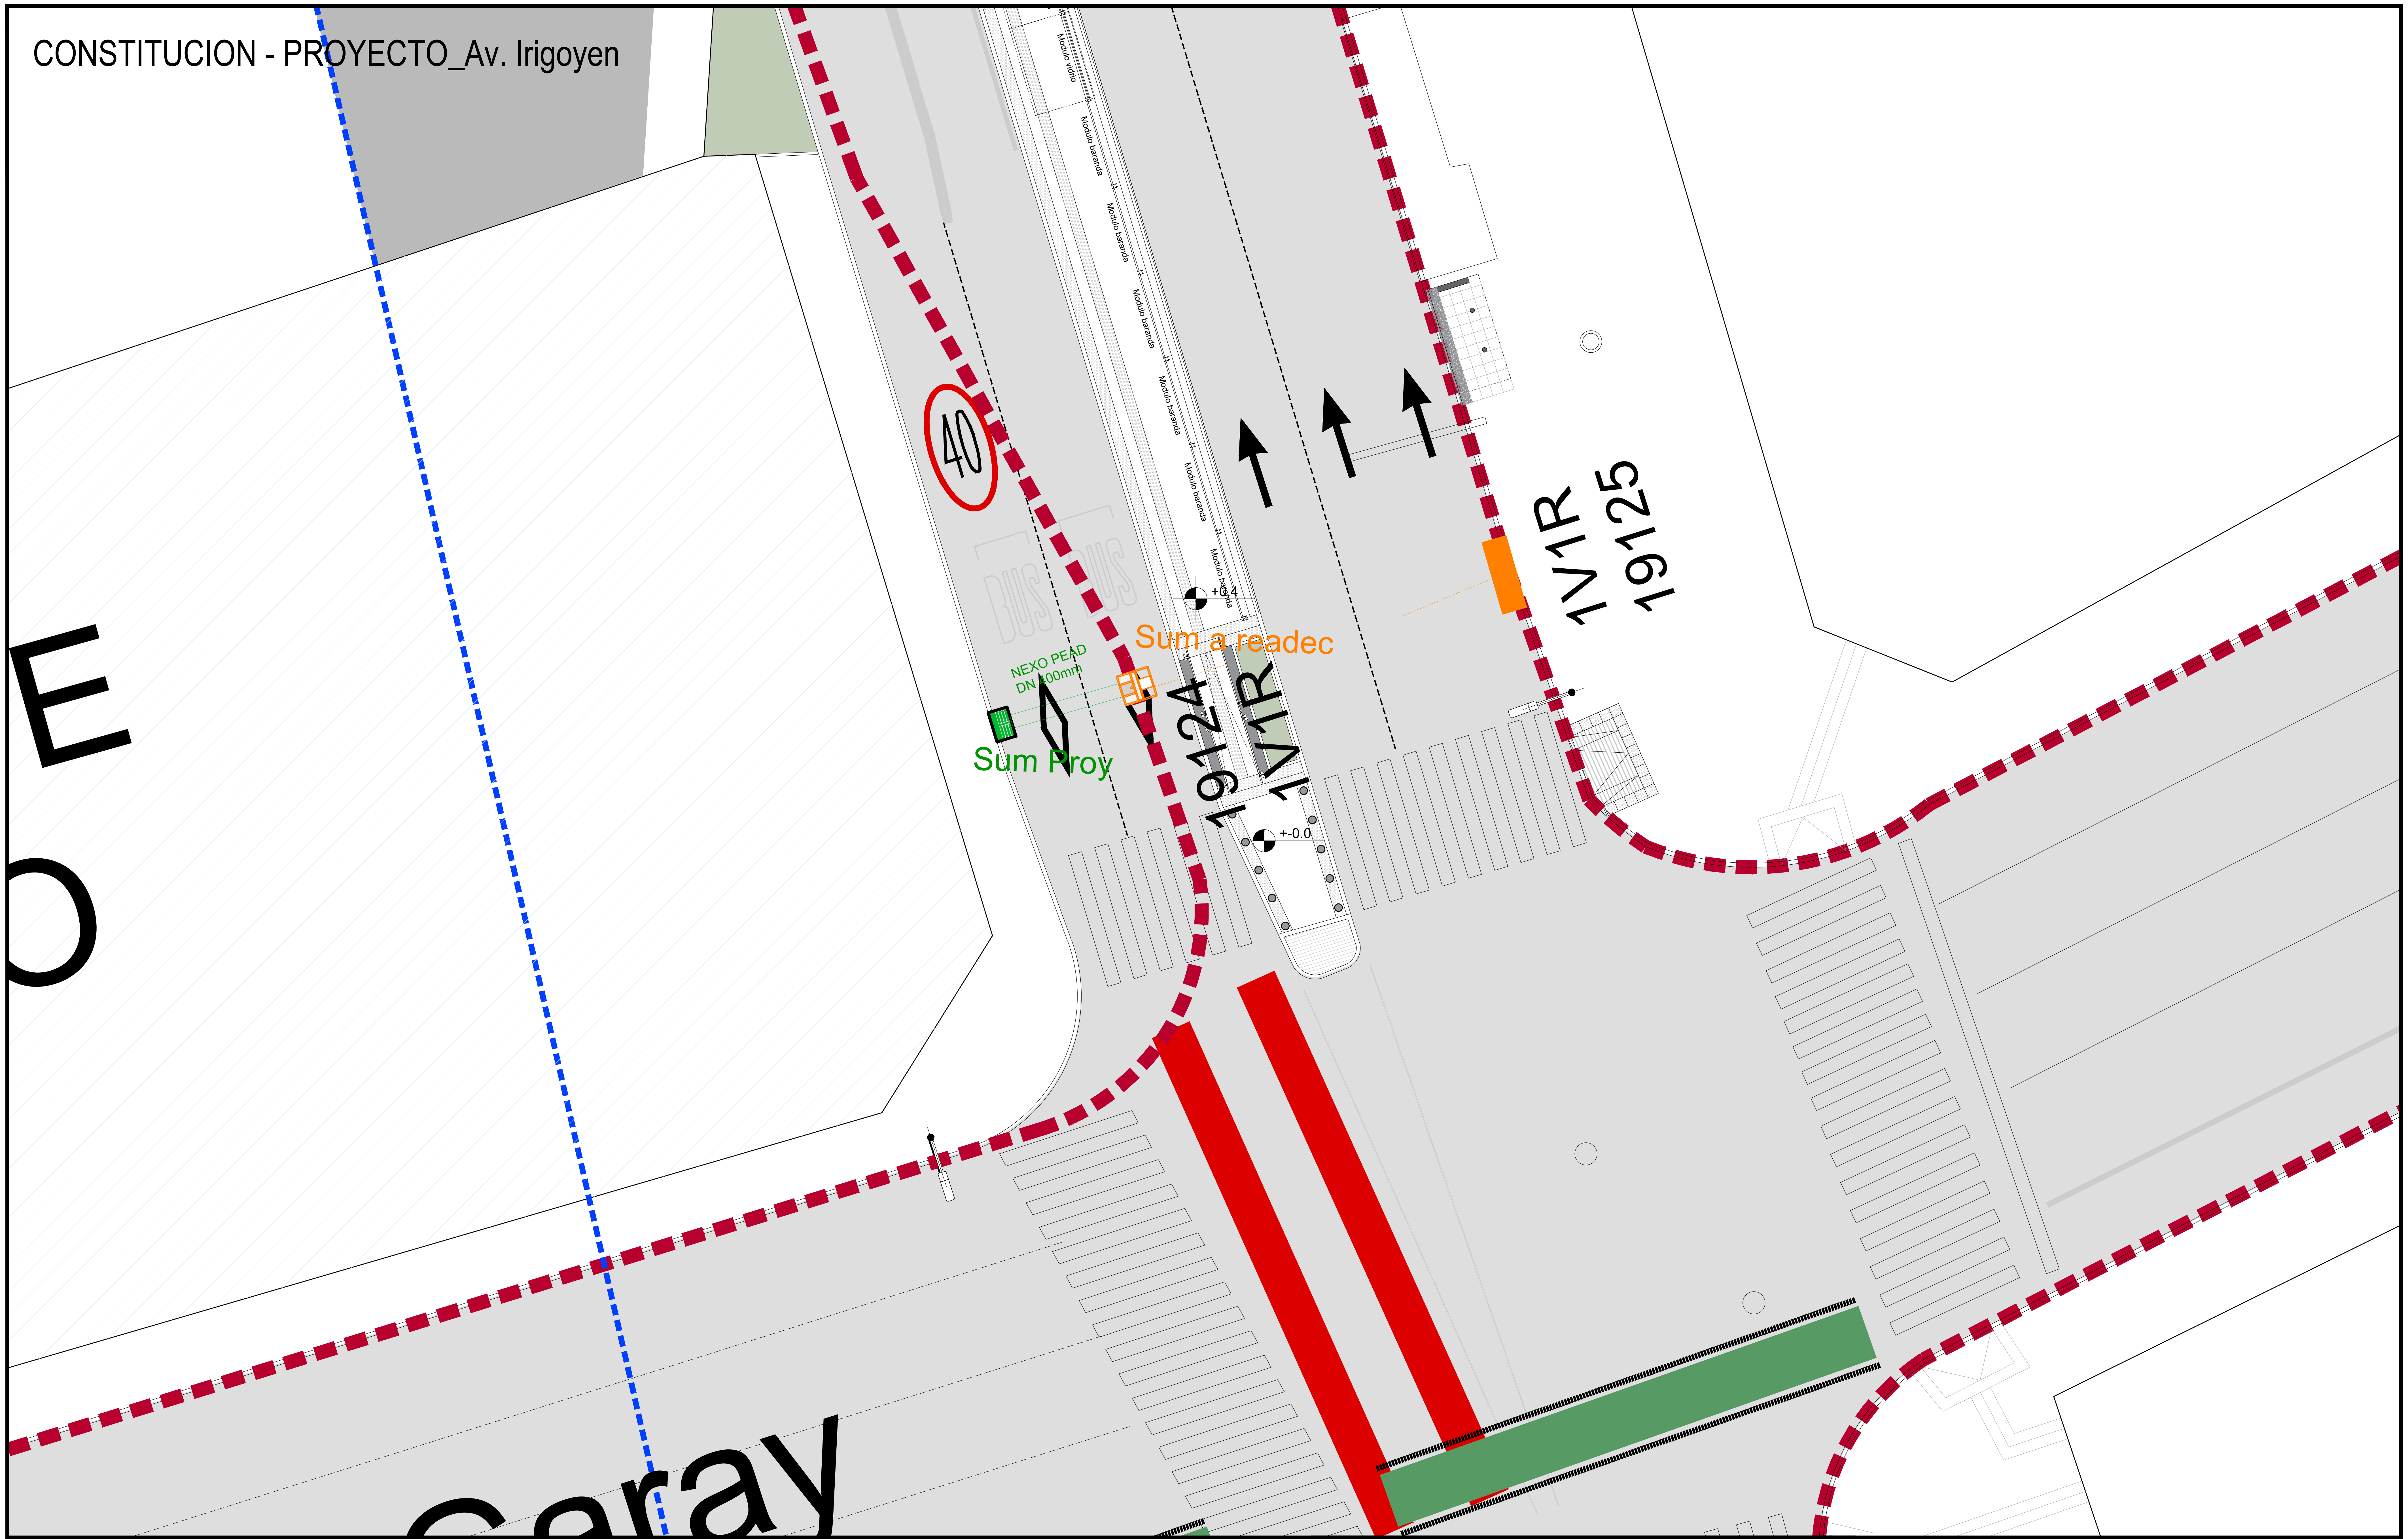
40
Modulo vidrio
Modulo baranda
Modulo baranda
Modulo baranda
Modulo baranda
Modulo baranda
BUS
+0.4
+-0.0
Sum a readec
NEXO PEAD DN 400mm
Sum Proy
19124
1V1R
1V1R
19125
E
O
Garay

REFERENCIAS

┼┼┼┼	Nexo existente a anular	▦	Sumidero existente a readecuar	NEXO PEAD DN 400mm	Conducto pluvial PEAD	🟩	Cámara de inspección 0,6 x 0,6
Ø800; HºAº	Conducto existente	●	Boca de registro existente	🟩	Sumidero mixto de 100 x 50	▬	Sumidero existente a anular
■■■■■	Albañal existente	●	Boca de registro a ejecutar	▭	Canaleta de hormigón con rejilla galvanizada		

ÁREA DE INTERVENCIÓN

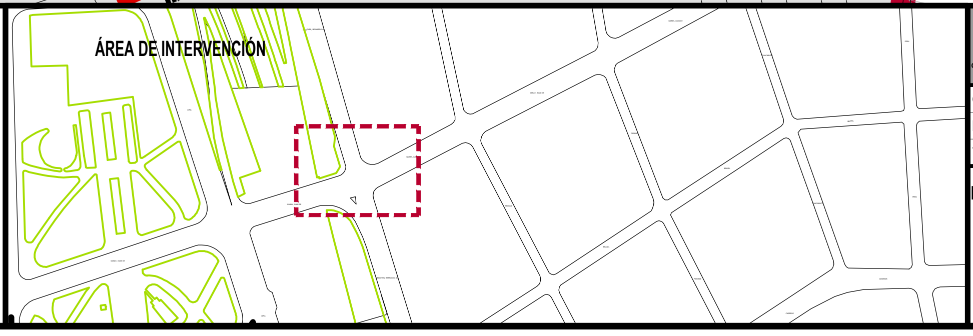

Gobierno de la Ciudad de Buenos Aires

MINISTERIO DE MOVILIDAD E INFRAESTRUCTURA
SUBSECRETARIA DE PROYECTOS Y OBRAS
DIRECCION GENERAL DE PROYECTOS

DGPRO

Obra: CT CONSTITUCION
Rubro: HIDRAULICA
Tramo: -
Plano: CTC_HID_Av. Irigoyen-1
Revisión: Rev.00
Fecha: 30/01/2026
Escala: -
Plano N° 03

MODIFICACIONES:

REVISION	FECHA	DESCRIPCION
-	-	-
-	-	-
-	-	-
-	-	-
-	-	-
-	-	-
-	-	-
-	-	-
-	-	-
-	-	-

NOTAS: EL PRESENTE PLANO ES INDICATIVO. LA CONTRATISTA CONFECCIONARA LOS PLANOS DE DETALLE DEFINITIVO, QUE DEBERAN SER APROBADOS POR LA D.G.O.INF.U Y LA INSPECCION DE OBRA. EL PLANO PRESENTADO POR LA CONTRATISTA ESTARA EN UN TODO DE ACUERDO CON LA NORMATIVA VIGENTE
TODAS LAS MEDIDAS Y NIVELES SE VERIFICARAN EN OBRA POR EL CONTRATISTA.
TODOS LOS DETALLES CONSTRUCTIVOS SERAN COORDINADOS Y COMPATIBILIZADOS EN OBRA.

PLANO NO APTO PARA CONSTRUCCIÓN

CONSTITUCION - PROYECTO_Av. Irigoyen

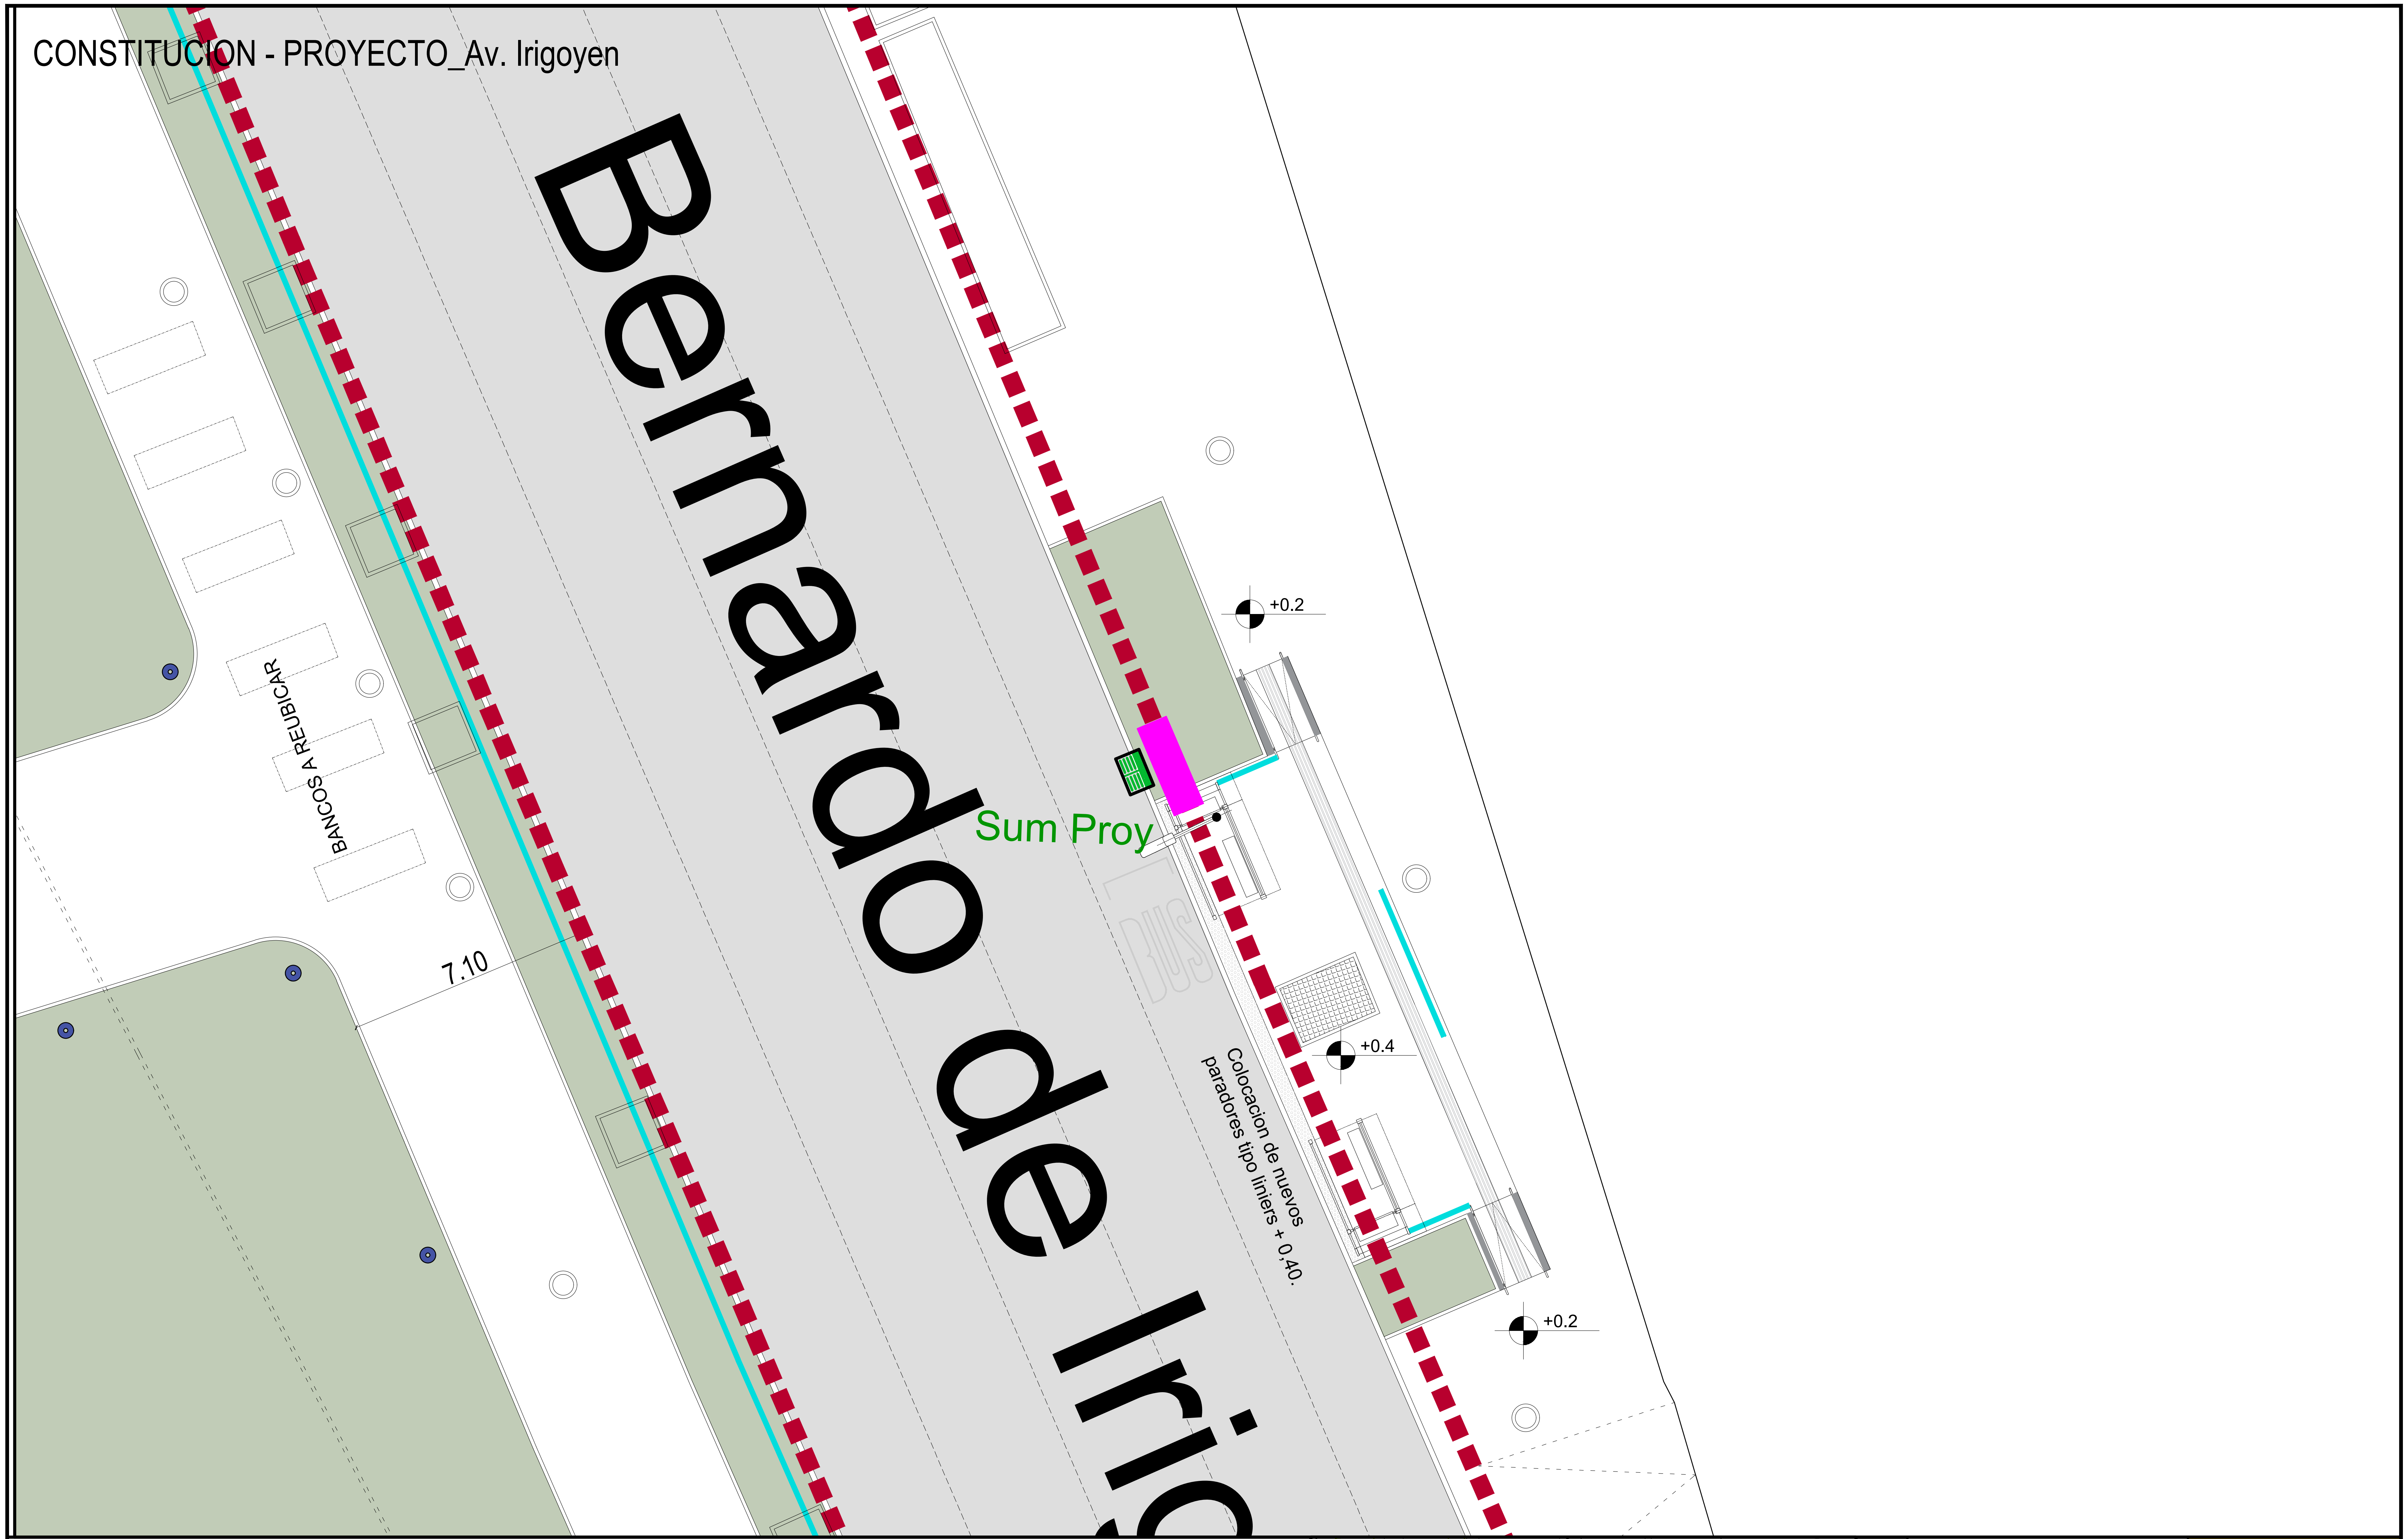

REFERENCIAS

Nexo existente a anular	Sumidero existente a readecuar	NEXO PEAD DN 400mm Conducto pluvial PEAD	Cámara de inspección 0,6 x 0,6
Ø800; HºAº Conducto existente	Boca de registro existente	Sumidero mixto de 100 x 50	Sumidero existente a anular
Albañal existente	Boca de registro a ejecutar	Canaleta de hormigón con rejilla galvanizada	

AREA DE INTERVENCIÓN

Gobierno de la Ciudad de Buenos Aires

MINISTERIO DE MOVILIDAD E INFRAESTRUCTURA
SUBSECRETARIA DE PROYECTOS Y OBRAS
DIRECCION GENERAL DE PROYECTOS

DGPRO

Obra: CT CONSTITUCION
Rubro: HIDRAULICA
Tramo: -
Plano: CTC_HID_Av. Irigoyen-2
Revisión: Rev.00
Fecha: 30/01/2026
Escala: -
Plano N° 04

MODIFICACIONES:

REVISION	FECHA	DESCRIPCION
-	-	-
-	-	-
-	-	-
-	-	-
-	-	-
-	-	-
-	-	-
-	-	-
-	-	-
-	-	-

NOTAS: EL PRESENTE PLANO ES INDICATIVO. LA CONTRATISTA CONFECCIONARA LOS PLANOS DE DETALLE DEFINITIVO, QUE DEBERAN SER APROBADOS POR LA D.G.O.INF.U Y LA INSPECCION DE OBRA. EL PLANO PRESENTADO POR LA CONTRATISTA ESTARA EN UN TODO DE ACUERDO CON LA NORMATIVA VIGENTE
TODAS LAS MEDIDAS Y NIVELES SE VERIFICARAN EN OBRA POR EL CONTRATISTA.
TODOS LOS DETALLES CONSTRUCTIVOS SERAN COORDINADOS Y COMPATIBILIZADOS EN OBRA.

PLANO NO APTO PARA CONSTRUCCIÓN

CONSTITUCION - PROYECTO_Av. Montes de Oca

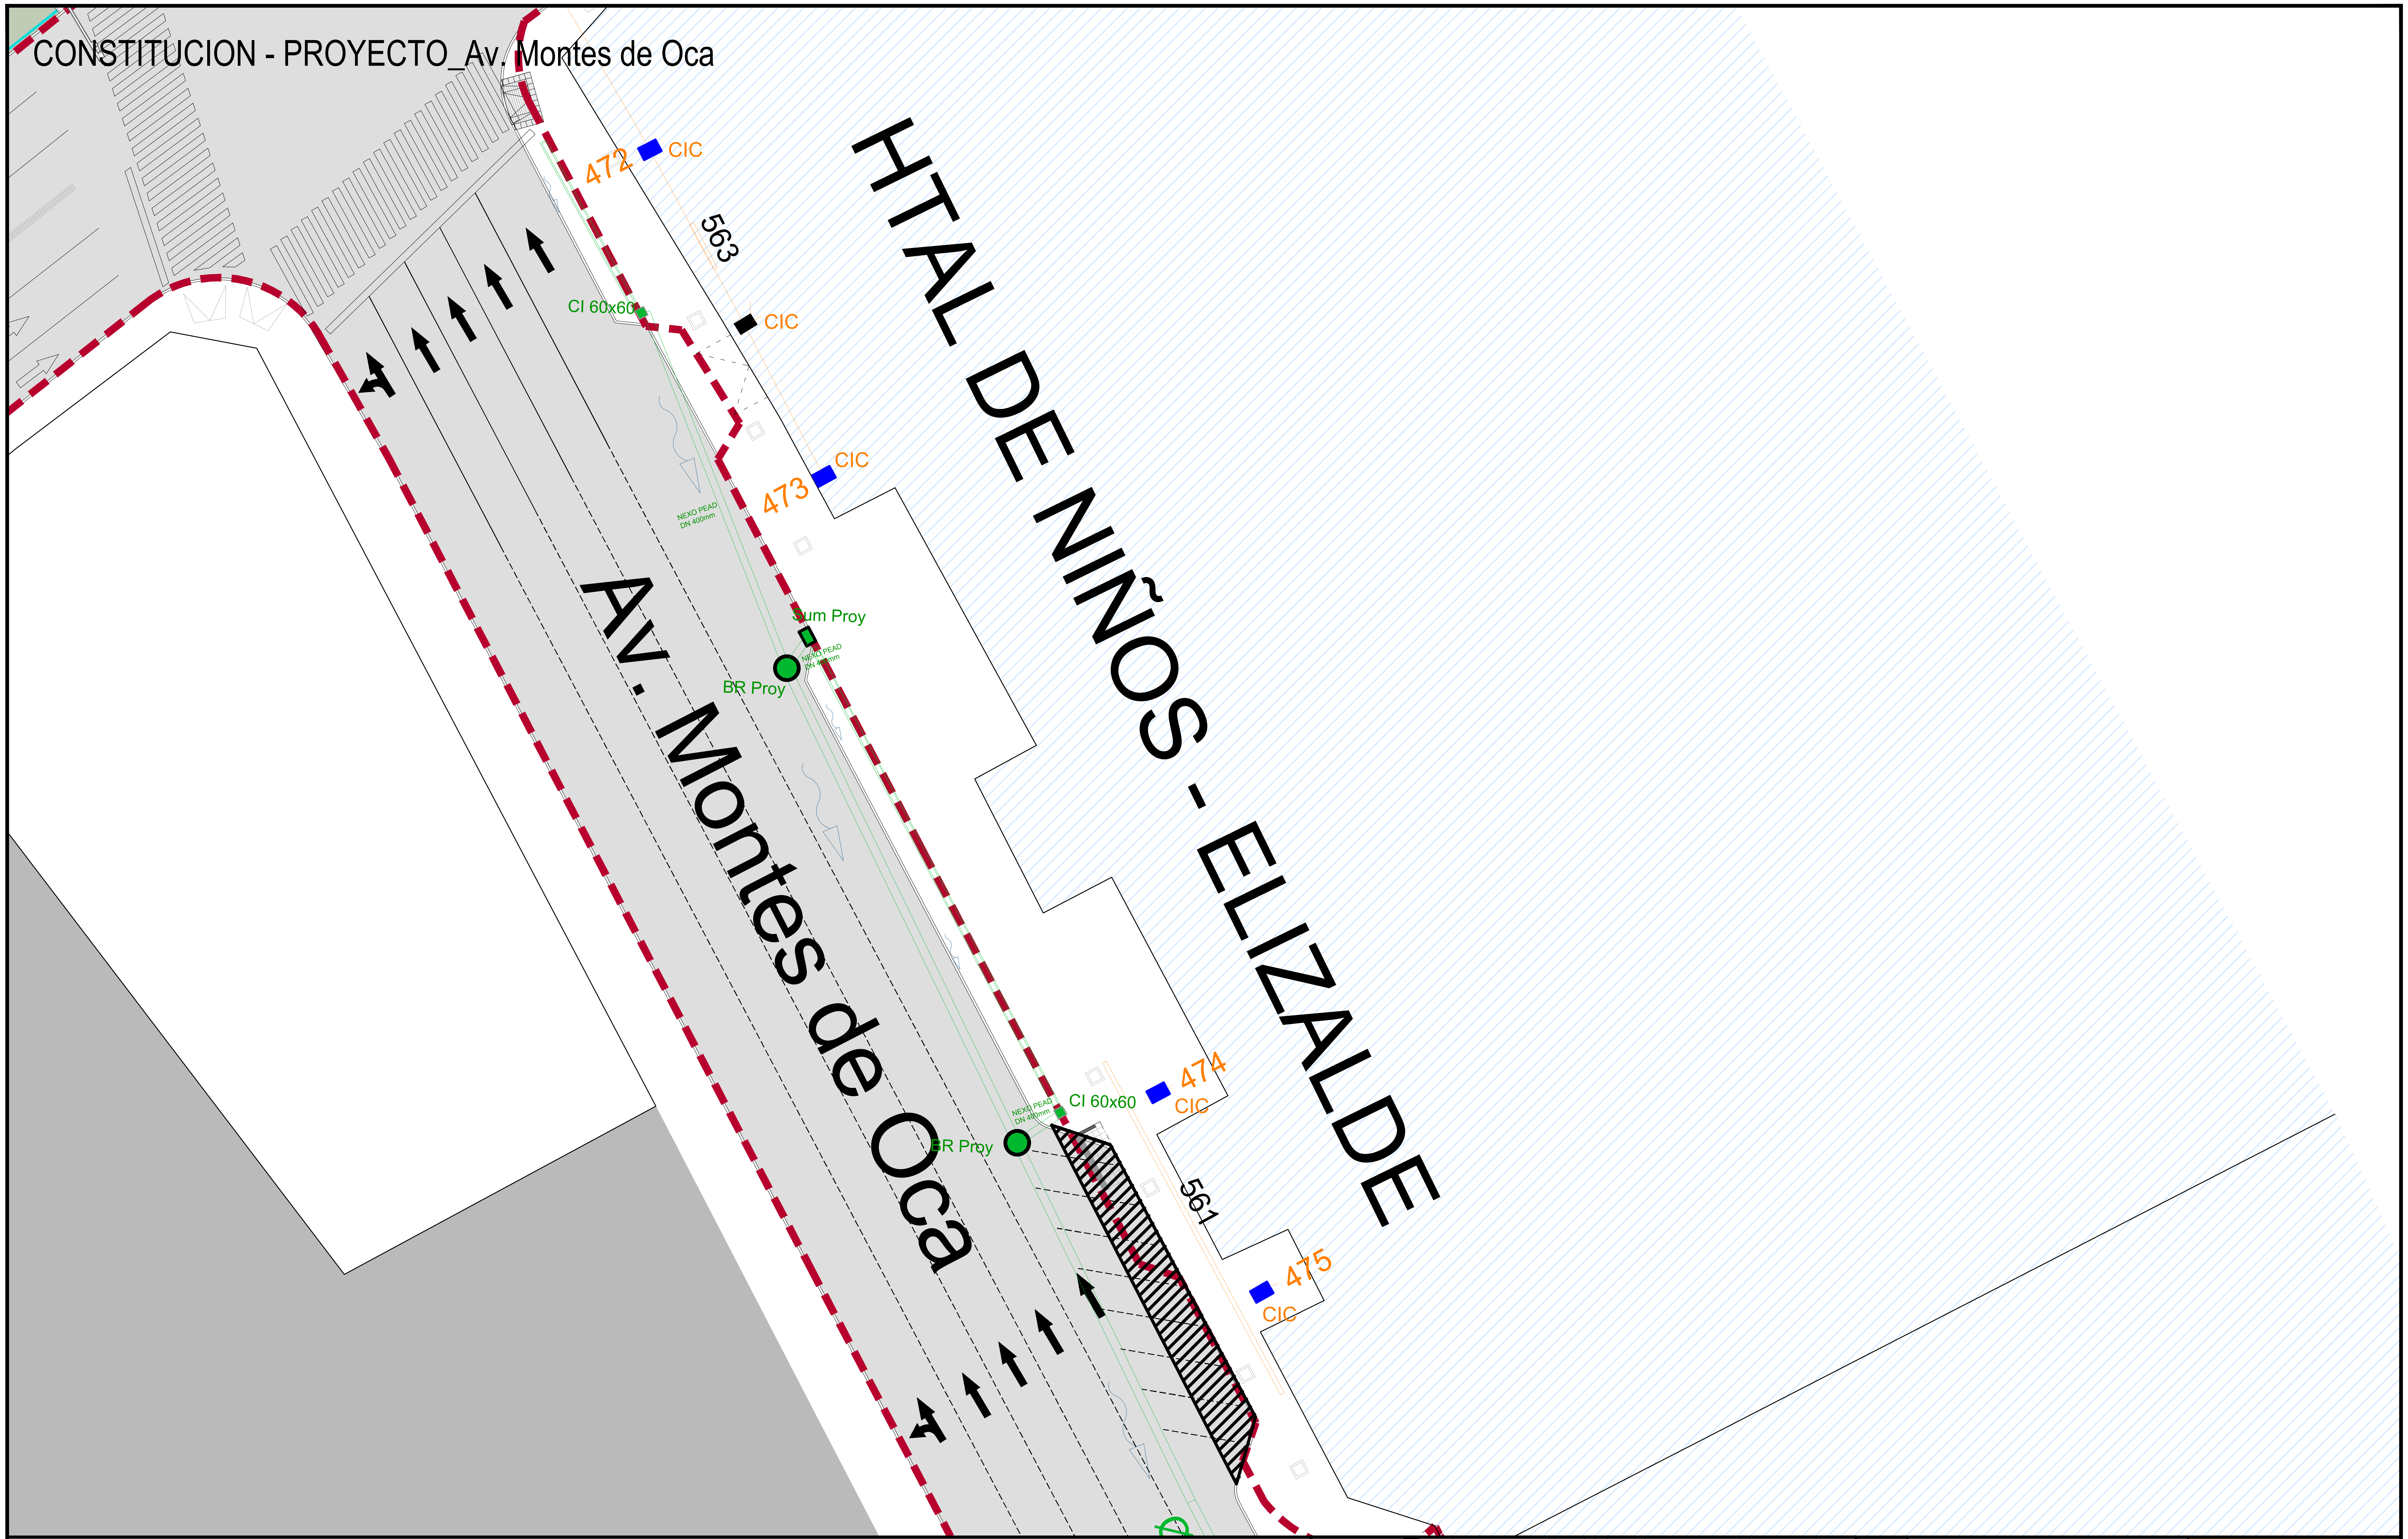
HTAL DE NIÑOS - ELIZALDE
Av. Montes de Oca
472
CIC
563
CIC
CI 60x60
473
CIC
NEXO PEAD DN 400mm
Sum Proy
NEXO PEAD DN 400mm
BR Proy
474
CIC
CI 60x60
NEXO PEAD DN 400mm
BR Proy
561
475
CIC

REFERENCIAS

┼┼┼┼	Nexo existente a anular	▦	Sumidero existente a readecuar	NEXO PEAD DN 400mm ▬	Conducto pluvial PEAD	🟩	Cámara de inspección 0,6 x 0,6
Ø800; HºAº ▪▪▪▪	Conducto existente	●	Boca de registro existente	🟩	Sumidero mixto de 100 x 50	▬	Sumidero existente a anular
▪▪▪▪▪	Albañal existente	●	Boca de registro a ejecutar	▭	Canaleta de hormigón con rejilla galvanizada	▨	Dársena de estacionamiento a readecuar

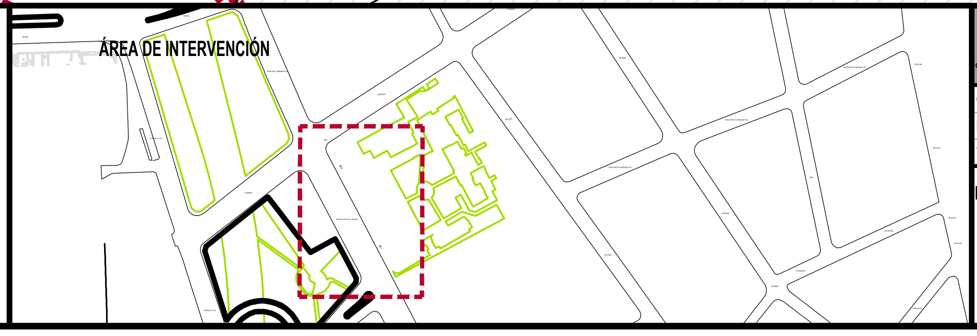
ÁREA DE INTERVENCIÓN

Gobierno de la Ciudad de Buenos Aires

MINISTERIO DE MOVILIDAD E INFRAESTRUCTURA
SUBSECRETARIA DE PROYECTOS Y OBRAS
DIRECCION GENERAL DE PROYECTOS

DGPRO

Obra: CT CONSTITUCION
Rubro: HIDRAULICA
Tramo: -
Plano: CTC_HID_Av. Montes de Oca-1
Revisión: Rev.00
Fecha: 30/01/2026
Escala: -
Plano N° 05

MODIFICACIONES:

REVISION	FECHA	DESCRIPCION
-	-	-
-	-	-
-	-	-
-	-	-
-	-	-
-	-	-
-	-	-
-	-	-
-	-	-
-	-	-

NOTAS: EL PRESENTE PLANO ES INDICATIVO. LA CONTRATISTA CONFECCIONARA LOS PLANOS DE DETALLE DEFINITIVO, QUE DEBERAN SER APROBADOS POR LA D.G.O.INF.U Y LA INSPECCION DE OBRA. EL PLANO PRESENTADO POR LA CONTRATISTA ESTARA EN UN TODO DE ACUERDO CON LA NORMATIVA VIGENTE
TODAS LAS MEDIDAS Y NIVELES SE VERIFICARAN EN OBRA POR EL CONTRATISTA.
TODOS LOS DETALLES CONSTRUCTIVOS SERAN COORDINADOS Y COMPATIBILIZADOS EN OBRA.

PLANO NO APTO PARA CONSTRUCCIÓN

CONSTITUCION - PROYECTO_Av. Montes de Oca

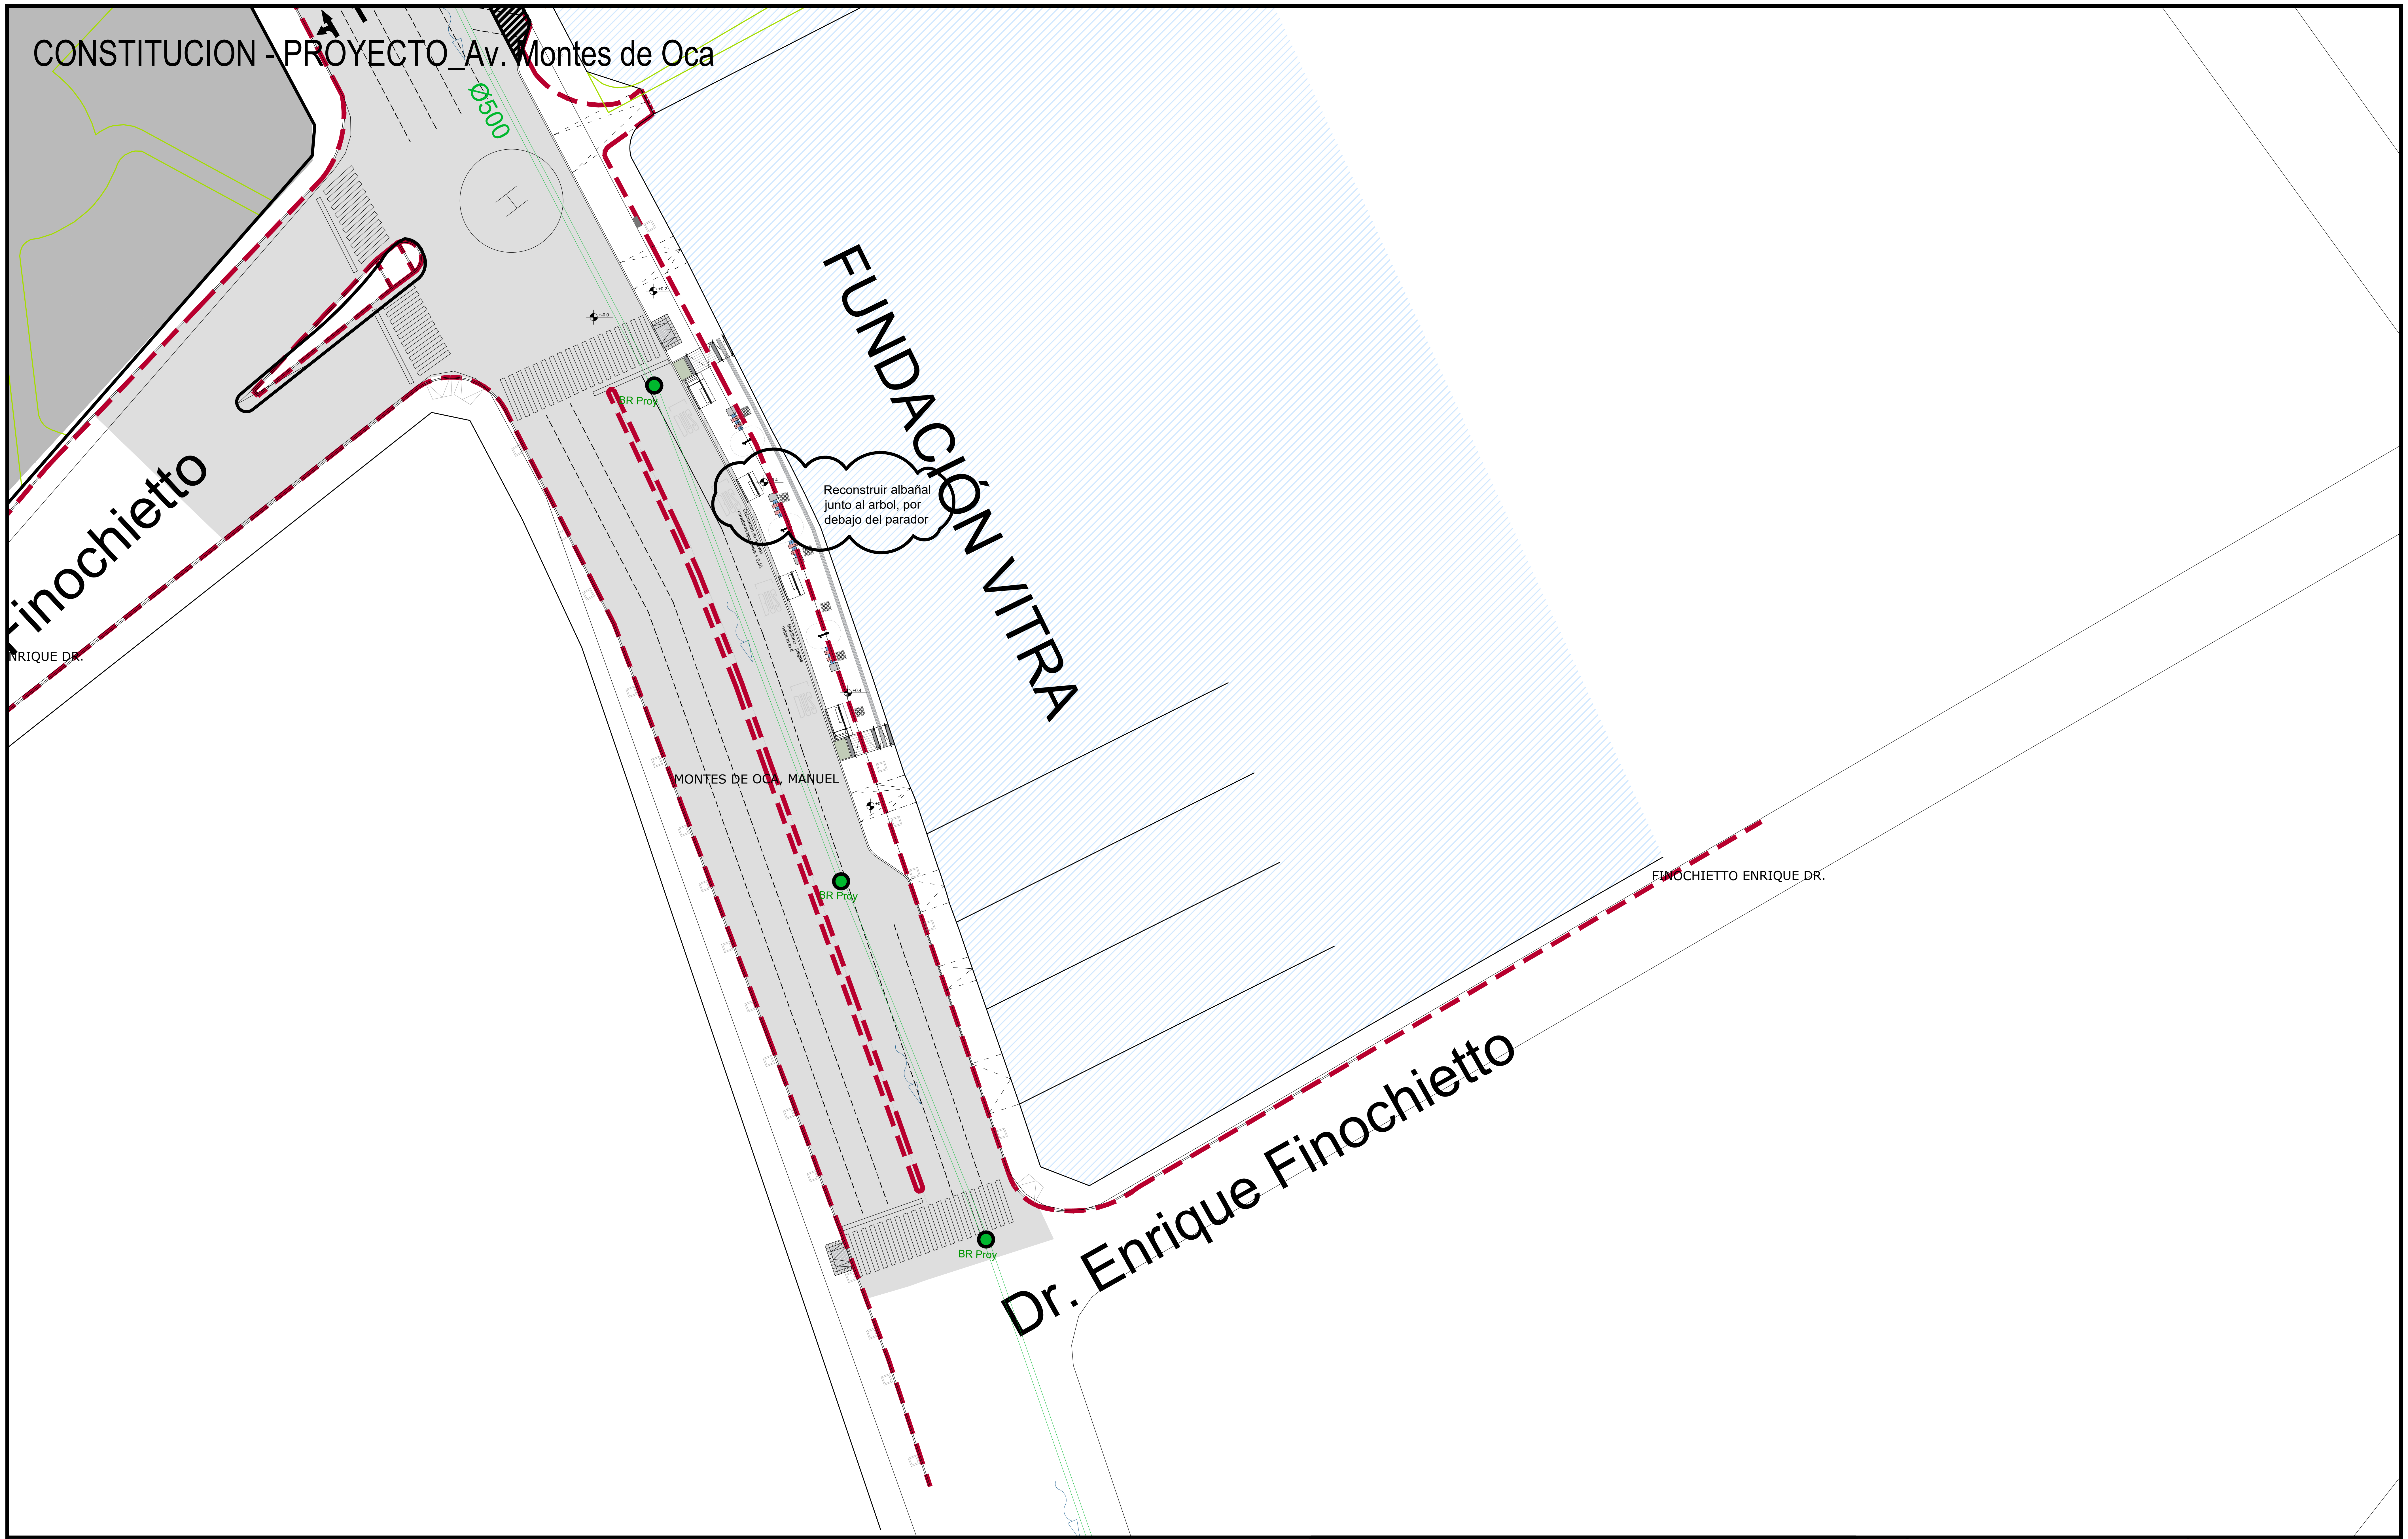
Ø500
FUNDACIÓN VITRA
Reconstruir albañal junto al arbol, por debajo del parador
BR Proy
BR Proy
BR Proy
Finochietto
NRIQUE DR.
MONTES DE OCA, MANUEL
FINOCHIETTO ENRIQUE DR.
Dr. Enrique Finochietto

REFERENCIAS

┼┼┼┼	Nexo existente a anular	▦	Sumidero existente a readecuar	NEXO PEAD DN 400mm ▬	Conducto pluvial PEAD	🟩	Cámara de inspección 0,6 x 0,6
Ø800; HºAº ▪▪▪▪	Conducto existente	●	Boca de registro existente	🟩	Sumidero mixto de 100 x 50	▬	Sumidero existente a anular
▪▪▪▪	Albañal existente	●	Boca de registro a ejecutar	▭	Canaleta de hormigón con rejilla galvanizada		

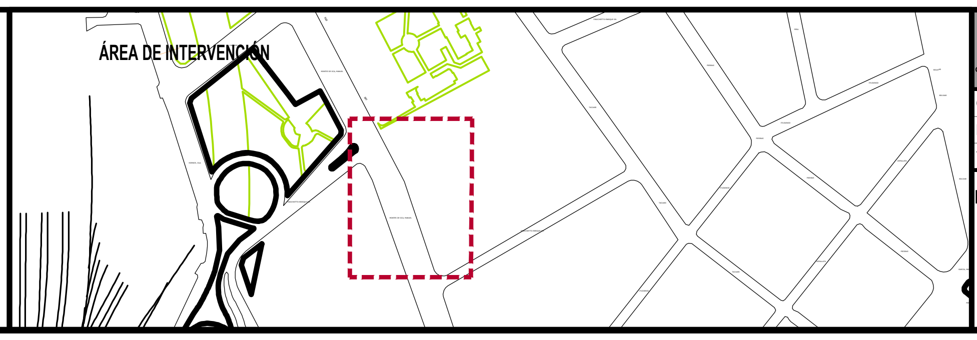
ÁREA DE INTERVENCIÓN

Gobierno de la Ciudad de Buenos Aires

MINISTERIO DE MOVILIDAD E INFRAESTRUCTURA
SUBSECRETARIA DE PROYECTOS Y OBRAS
DIRECCION GENERAL DE PROYECTOS

DGPRO

Obra: CT CONSTITUCION
Rubro: HIDRAULICA
Tramo: -
Plano: CTC_HID_Av. Montes de Oca-2
Revisión: Rev.00
Fecha: 30/01/2026 Escala: -
Plano N° 06

MODIFICACIONES:

REVISION	FECHA	DESCRIPCION
-	-	-
-	-	-
-	-	-
-	-	-
-	-	-
-	-	-
-	-	-
-	-	-
-	-	-
-	-	-

NOTAS: EL PRESENTE PLANO ES INDICATIVO. LA CONTRATISTA CONFECCIONARA LOS PLANOS DE DETALLE DEFINITIVO, QUE DEBERAN SER APROBADOS POR LA D.G.O.INF.U Y LA INSPECCION DE OBRA. EL PLANO PRESENTADO POR LA CONTRATISTA ESTARA EN UN TODO DE ACUERDO CON LA NORMATIVA VIGENTE
TODAS LAS MEDIDAS Y NIVELES SE VERIFICARAN EN OBRA POR EL CONTRATISTA.
TODOS LOS DETALLES CONSTRUCTIVOS SERAN COORDINADOS Y COMPATIBILIZADOS EN OBRA.

PLANO NO APTO PARA CONSTRUCCIÓN

CONSTITUCION - PROYECTO_Av. Montes de Oca

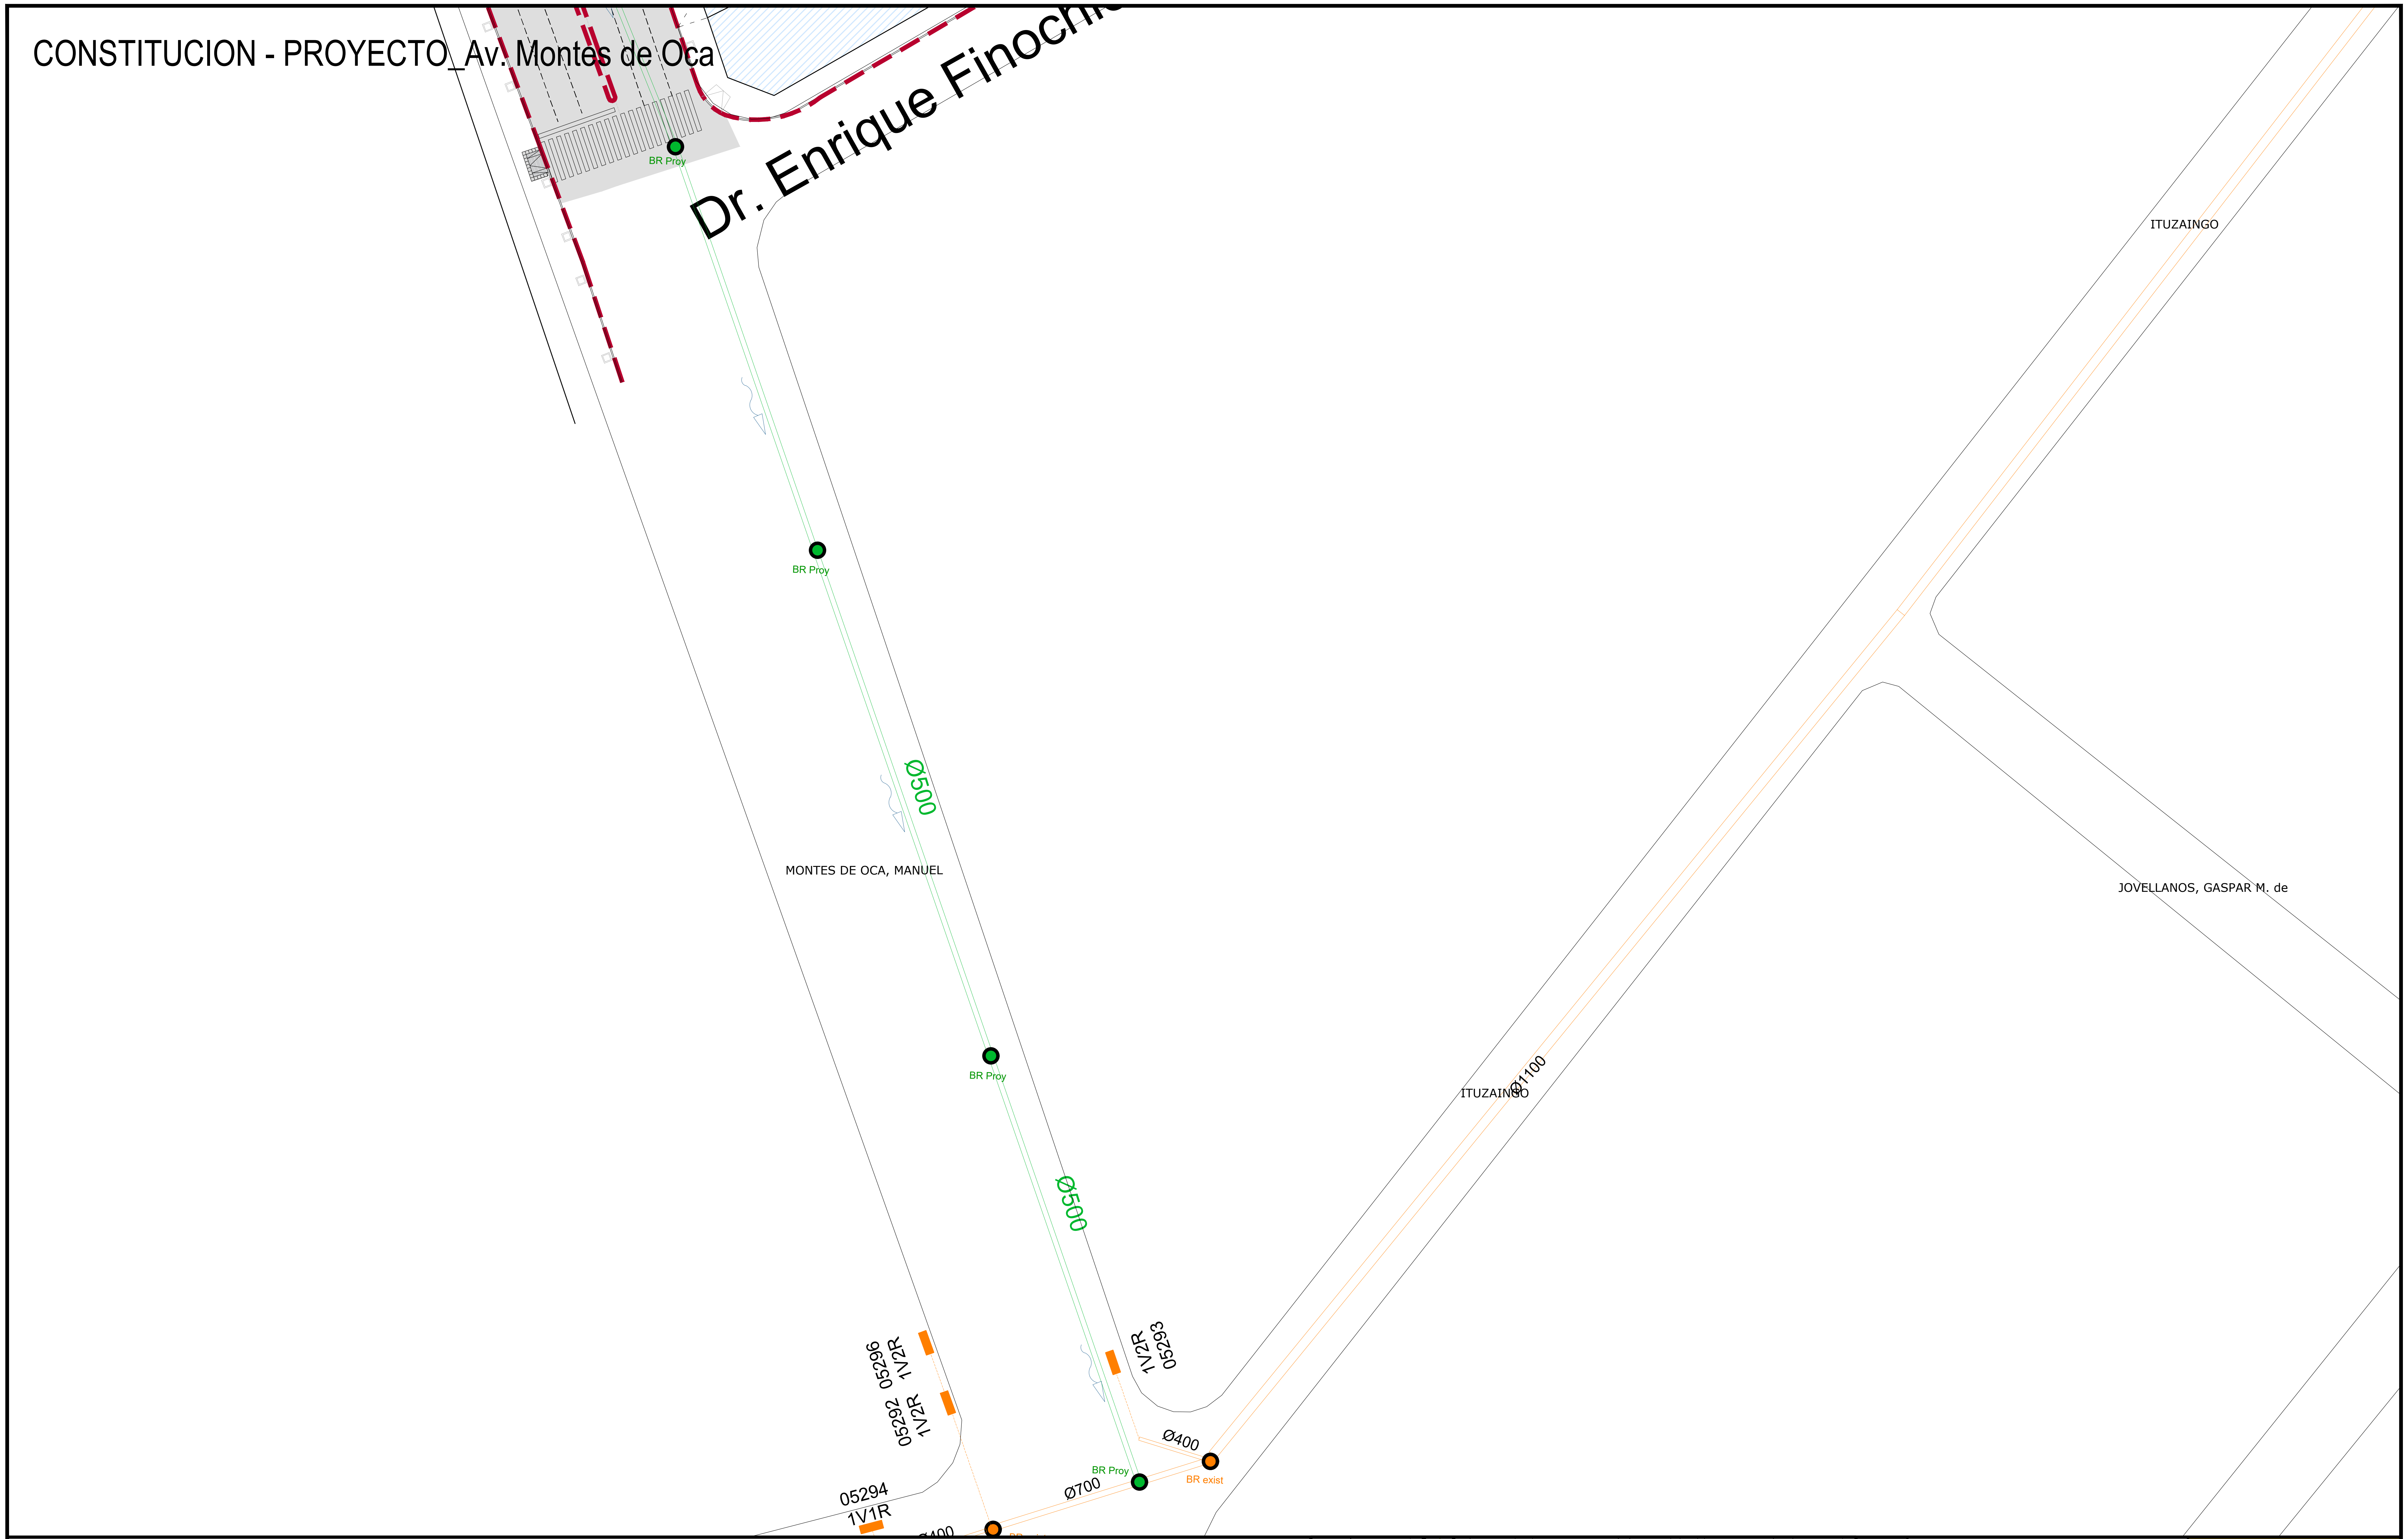
Dr. Enrique Finochi
BR Proy
BR Proy
BR Proy
Ø500
Ø500
MONTES DE OCA, MANUEL
ITUZAINGO
ITUZAINGO
Ø1100
JOVELLANOS, GASPAR M. de
05296
1V2R
05292
1V2R
1V2R
05293
Ø400
BR Proy
Ø700
BR exist
05294
1V1R

REFERENCIAS

┿┿┿┿	Nexo existente a anular	▦	Sumidero existente a readecuar	NEXO PEAD DN 400mm	Conducto pluvial PEAD	🟩	Cámara de inspección 0,6 x 0,6
Ø800; HºAº	Conducto existente	●	Boca de registro existente	🟩	Sumidero mixto de 100 x 50	▬	Sumidero existente a anular
▪▪▪▪▪	Albañal existente	●	Boca de registro a ejecutar	▭	Canaleta de hormigón con rejilla galvanizada		

ÁREA DE INTERVENCIÓN

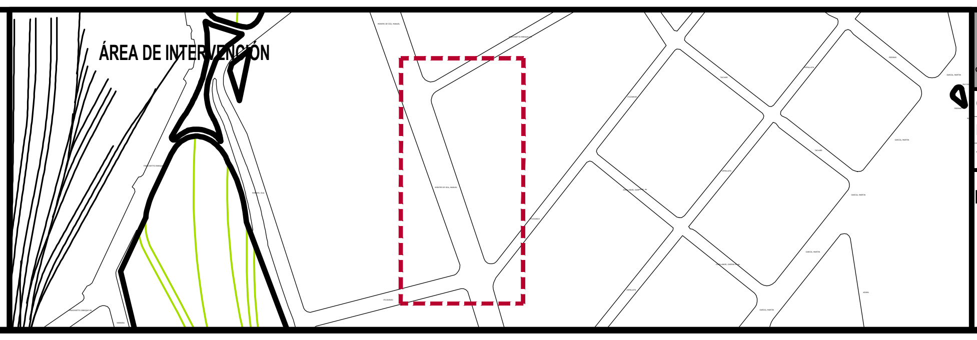

Gobierno de la Ciudad de Buenos Aires

MINISTERIO DE MOVILIDAD E INFRAESTRUCTURA
SUBSECRETARIA DE PROYECTOS Y OBRAS
DIRECCION GENERAL DE PROYECTOS

DGPRO

Obra: CT CONSTITUCION
Rubro: HIDRAULICA
Tramo: -
Plano: CTC_HID_Av. Montes de Oca-3
Revisión: Rev.00
Fecha: 30/01/2026
Escala: -
Plano N° 07

MODIFICACIONES:

REVISION	FECHA	DESCRIPCION
-	-	-
-	-	-
-	-	-
-	-	-
-	-	-
-	-	-
-	-	-
-	-	-
-	-	-
-	-	-

NOTAS: EL PRESENTE PLANO ES INDICATIVO. LA CONTRATISTA CONFECCIONARA LOS PLANOS DE DETALLE DEFINITIVO, QUE DEBERAN SER APROBADOS POR LA D.G.O.INF.U Y LA INSPECCION DE OBRA. EL PLANO PRESENTADO POR LA CONTRATISTA ESTARA EN UN TODO DE ACUERDO CON LA NORMATIVA VIGENTE
TODAS LAS MEDIDAS Y NIVELES SE VERIFICARAN EN OBRA POR EL CONTRATISTA.
TODOS LOS DETALLES CONSTRUCTIVOS SERAN COORDINADOS Y COMPATIBILIZADOS EN OBRA.

PLANO-2026-06728892-GCABA-DGPRO

PLANO NO APTO PARA CONSTRUCCIÓN

G O B I E R N O DE LA C I U D A D DE B U E N O S A I R E S

"2026 - Año del 30° Aniversario de la sanción de la Constitución de la Ciudad Autónoma de Buenos Aires"

Hoja Adicional de Firmas
Plano

Número: PLANO-2026-06728892-GCABA-DGPRO

Buenos Aires, Viernes 30 de Enero de 2026

Referencia: CTC_HID

El documento fue importado por el sistema GEDO con un total de 7 pagina/s.

Digitally signed by Comunicaciones Oficiales
Date: 2026.01.30 14:29:00 -03:00

GABRIEL EDUARDO ROSALES
Director General
D. G. PROYECTOS
MINISTERIO DE MOVILIDAD E INFRAESTRUCTURA

Digitally signed by Comunicaciones Oficiales
Date: 2026.01.30 14:29:02 -03:00