

ACCESO SECUNDARIO


VISTA 4-4 1:25

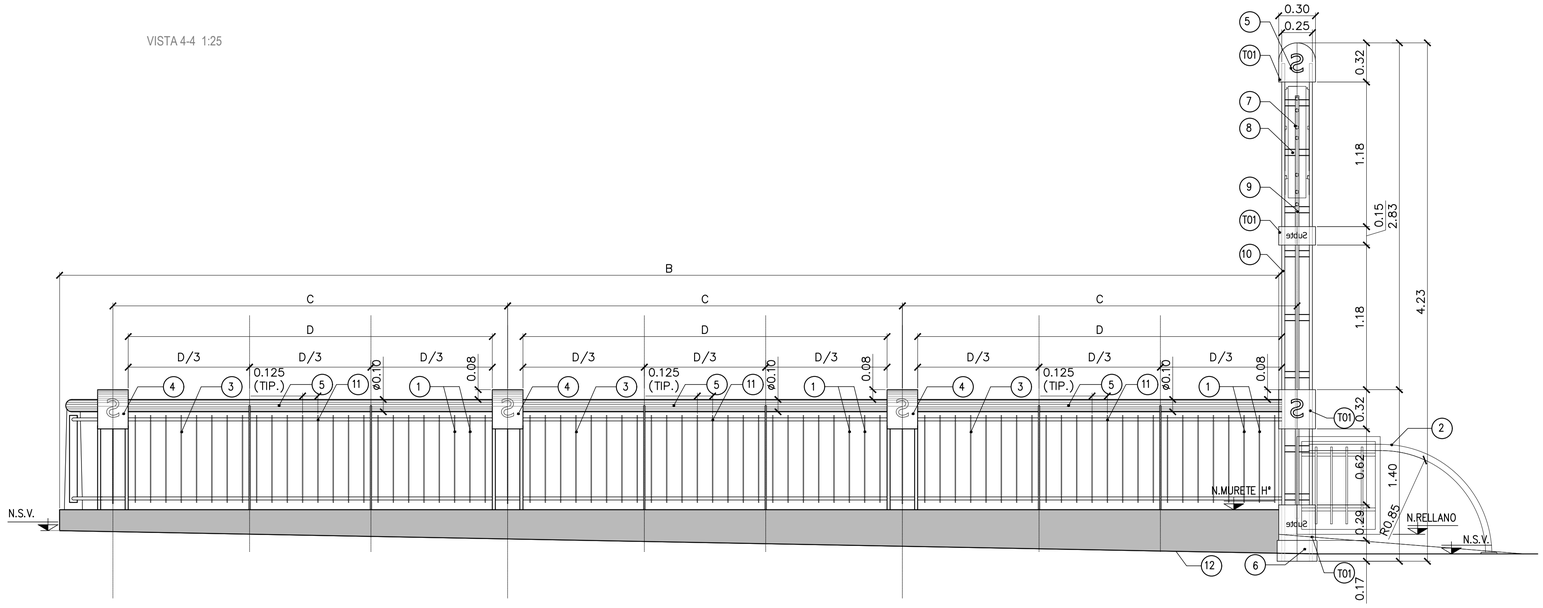


VISTA FRONTAL 1-1 1:25

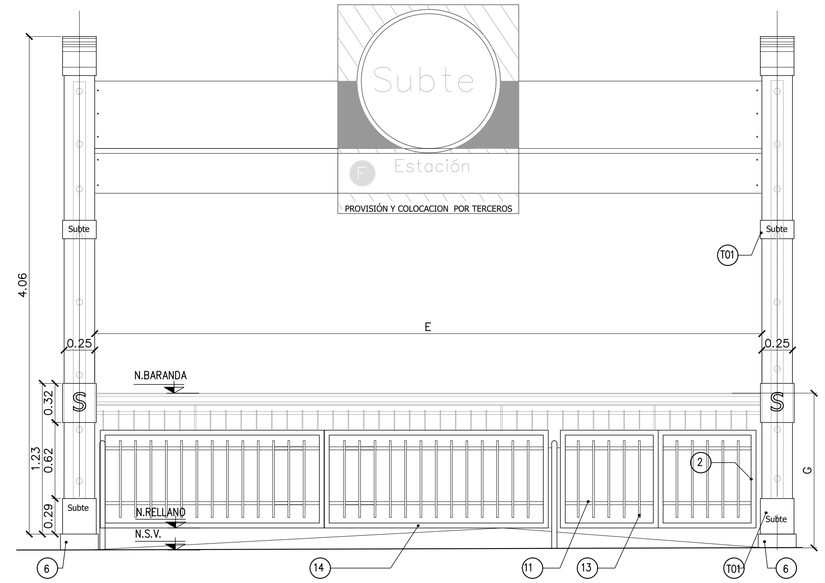

PLANTA DETALLE 1:25

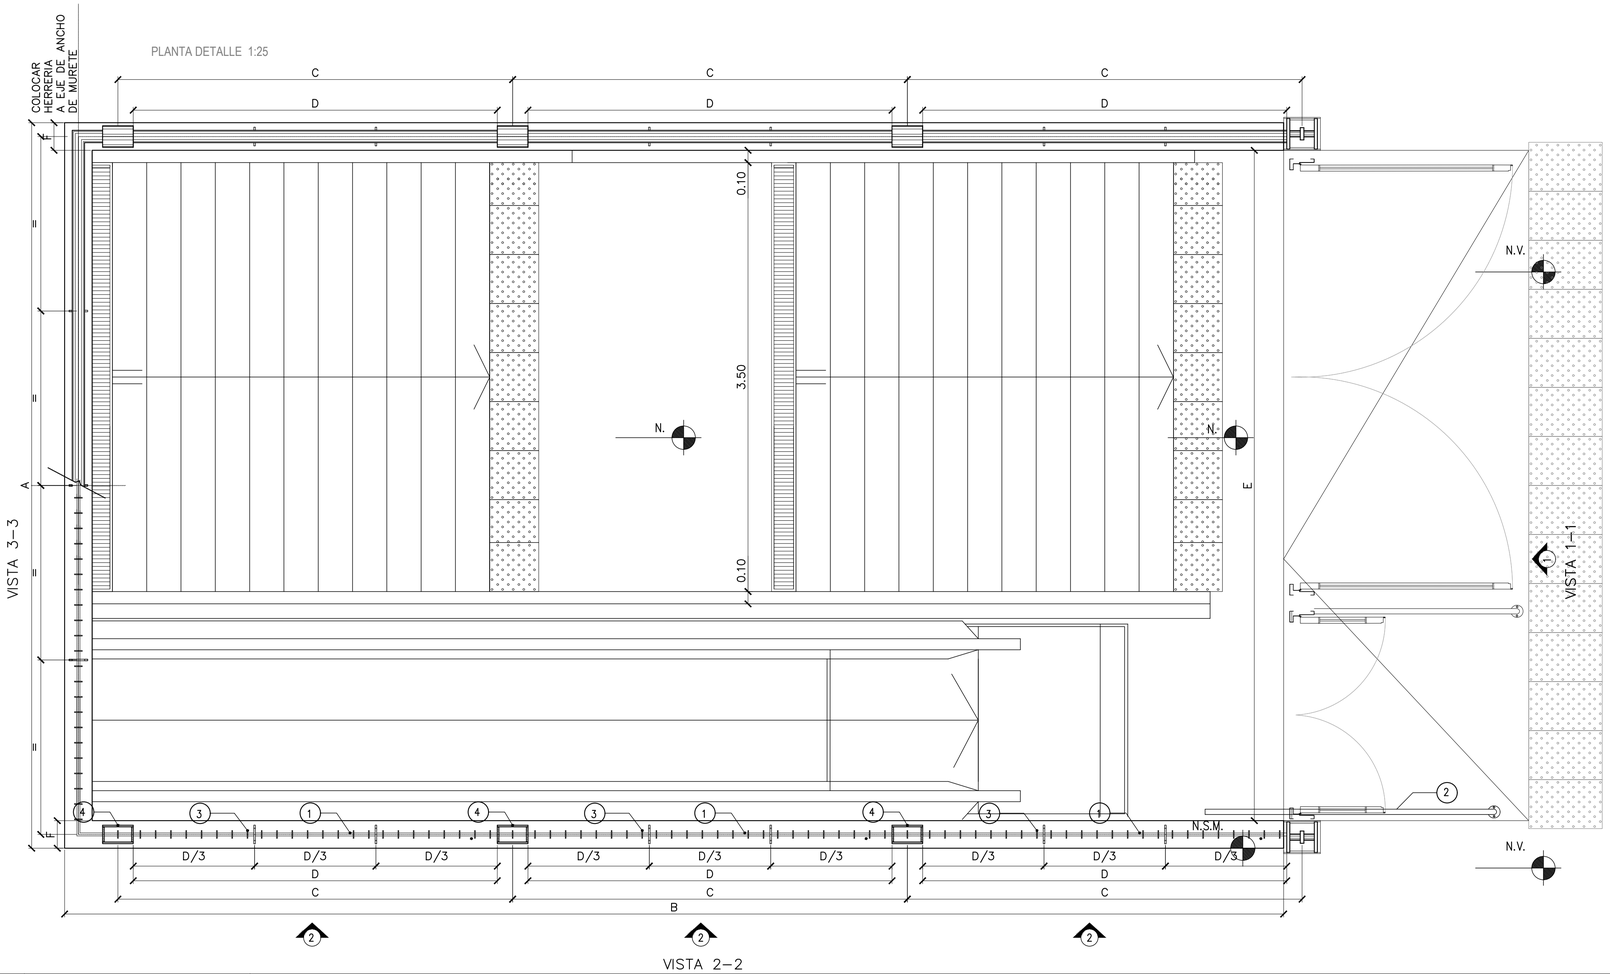

VISTA POSTERIOR 3-3 1:25

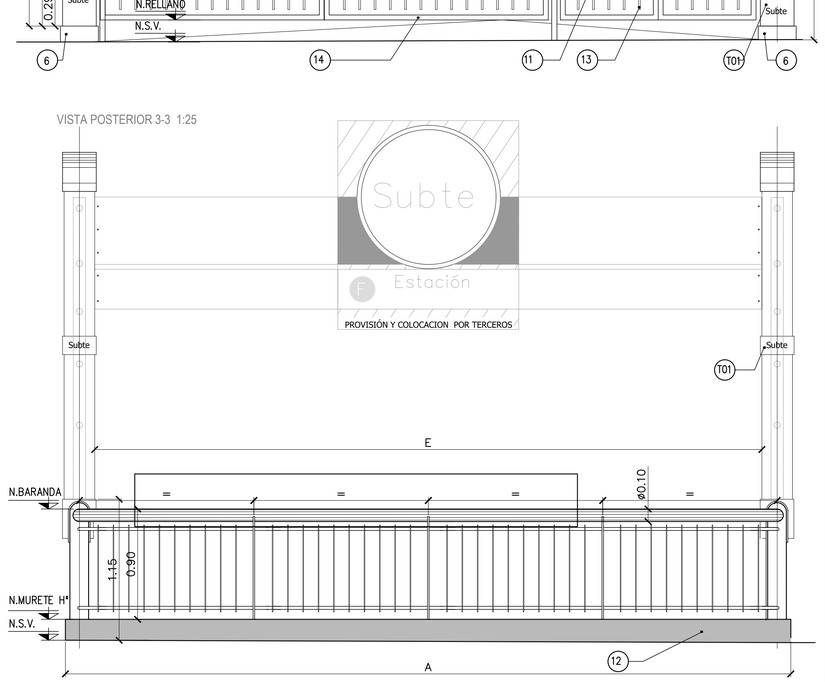

REFERENCIAS:

1 – PLANCHUELAS DE HIERRO 2 1/2" ANCHO X 1/4" esp.
TERMINACION: 2 MANOS DE ANTIOXIDO + 3 MANOS DE ESMALTE SINTETICO COLOR GRIS

2 – PASAMANOS – IDEM. INTERIOR DE ESTACION

3 – PARANTES VERTICALES 4" ARR / 6" AB DE ANCHO X 1/2" esp. AMURADOS CON GRAMPAS A HORMIGON ARMADO.
TERMINACION: 2 MANOS DE ANTIOXIDO + 3 MANOS DE ESMALTE SINTETICO COLOR GRIS

4 – COLUMNATA DE FE.
PARANTES VERTICALES 6" x ½" DE ESPESOR.
SOMBRERETE CURVO 250x12.5mm C/LETRA "S" CALADA ½" ESP.
BASE ¾" ESPESOR CON GRAMPAS A H° A° Y/O ANCLAJES.
TERMINACION: 2 MANOS DE ANTIOXIDO + 3 MANOS DE ESMALTE SINTETICO COLOR GRIS

5 – CAÑO DE FE 101.6 mm. (ø 4") 5 mm ESPESOR.
TERMINACION: 2 MANOS DE ANTIOXIDO + 3 MANOS DE ESMALTE SINTETICO COLOR GRIS

6 – BASE HORMIGON. CEMENTO ALISADO. ALTURA VARIABLE, MIN. 30 mm. esp. DIMENCIONES: 323 x 300 mm.

7 – PROYECCION SEÑALETICA

8 – CAÑO DE FE 50.8mm. (ø 2") 3mm. esp. LONGITUD: 86mm.
TERMINACION: 2 MANOS DE ANTIOXIDO + 3 MANOS DE ESMALTE SINTETICO COLOR GRIS

9 – TUBO ESTRUCTURAL 30 X 100 X 2.5mm. (CANALIZA INST. ELECTRICA DE SEÑALETICA PORTICO ACCESO) ALTURA: 3460mm.
TERMINACION: 2 MANOS DE ANTIOXIDO + 3 MANOS DE ESMALTE SINTETICO COLOR GRIS

10 –PLANCHUELA DE HIERRO 10" X 1/2" esp.
TERMINACION: 2 MANOS DE ANTIOXIDO + 3 MANOS DE ESMALTE SINTETICO COLOR GRIS.

11 – CAÑO DE FE ø1" x 3 mm. esp.
TERMINACION: 2 MANOS DE ANTIOXIDO + 3 MANOS DE ESMALTE SINTETICO COLOR GRIS.

12 – MURETE DE HORMIGON ARMADO CON ANTEPECHO DE GRANITO PULIDO NEGRO.

13 – PLANCHUELAS DE HIERRO 2" ANCHO X1/8" esp.
TERMINACION: 2 MANOS DE ANTIOXIDO + 3 MANOS DE ESMALTE SINTETICO COLOR GRIS

14 – TUBO ESTRUCTURAL 40X40mm.
TERMINACION: 2 MANOS DE ANTIOXIDO + 3 MANOS DE ESMALTE SINTETICO COLOR GRIS

REFERENCIAS – TERMINACIONES:

T01 – TERM.: 2 MANOS DE ANTIOXIDO + 3 MANOS DE ESMALTE SINTETICO COLOR GRIS. LETRA LOGOTIPO "S"– "SUBTE" EN RELIEVE O CALADO (10 mm) COLOR: GRIS OSCURO

NOTAS: EL PRESENTE PLANO ES INDICATIVO. LA CONTRATISTA CONSTATARÁ LOS PLANOS DE DETALLE DEFINITIVO, QUE DEBERÁN SER APROBADOS POR LA D.G.DPRO. Y LA INSPECCIÓN DE OBRA. EL PLANO PRESENTADO POR LA CONTRATISTA ESTARÁ EN UN TODO DE ACUERDO CON LA NORMATIVA VIGENTE.
TODAS LAS MEDIDAS Y NIVELES SE VERIFICARÁN EN OBRA POR EL CONTRATISTA.
TODOS LOS DETALLES CONSTRUCTIVOS SERÁN COORDINADOS Y COMPATIBILIZADOS EN OBRA.

PLANO NO APTO PARA CONSTRUCCIÓN

MODIFICACIONES:

REVISION	FECHA	DESCRIPCION
00	20-11-2025	EMISIÓN PARA LICITACIÓN
01	10-04-2026	EMISIÓN PARA LICITACIÓN

Gobierno de la Ciudad de Buenos Aires

MINISTERIO DE INFRAESTRUCTURA
SUBSECRETARIA DE PROYECTOS Y OBRAS
DIRECCION GENERAL DE PROYECTOS

DGPRO

Obra: LÍNEA F				PLANO-2026-23204372-GCABA-SSPO	
Plano Estacion Constitución- Detalle Acceso secundario - Dársena				LF-ES-CON-ARQ-PL-027-R01	
Fecha :10/04/2026	Eq. de Proyecto: UPU - ATEC - IATASA	Dibujó: JS	Revisó: GV	Escala: 1:25	Nº: A027

G O B I E R N O DE LA C I U D A D DE B U E N O S A I R E S

"2026 - Año del 30° Aniversario de la sanción de la Constitución de la Ciudad Autónoma de Buenos Aires"

Hoja Adicional de Firmas
Plano

Número: PLANO-2026-23204372-GCABA-SSPO

Buenos Aires, Domingo 17 de Mayo de 2026

Referencia: LF-ES-CON-ARQ-PL-027_1

El documento fue importado por el sistema GEDO con un total de 1 pagina/s.

Digitally signed by Comunicaciones Oficiales
Date: 2026.05.17 16:38:10 -03:00

Facundo Lombardo
Subsecretario
SUBSECRETARIA PROYECTOS Y OBRAS
MINISTERIO DE MOVILIDAD E INFRAESTRUCTURA

Digitally signed by Comunicaciones Oficiales
Date: 2026.05.17 16:38:08 -03:00