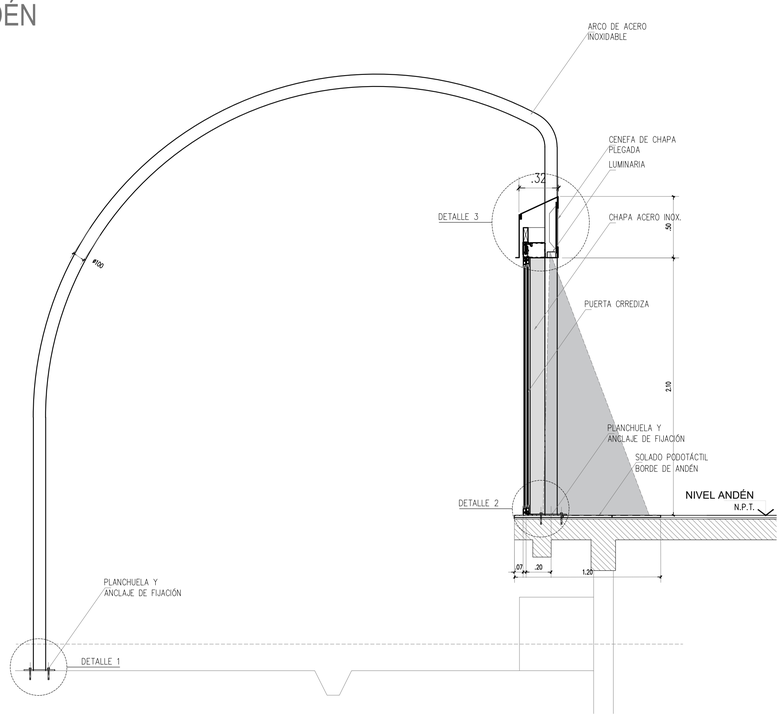
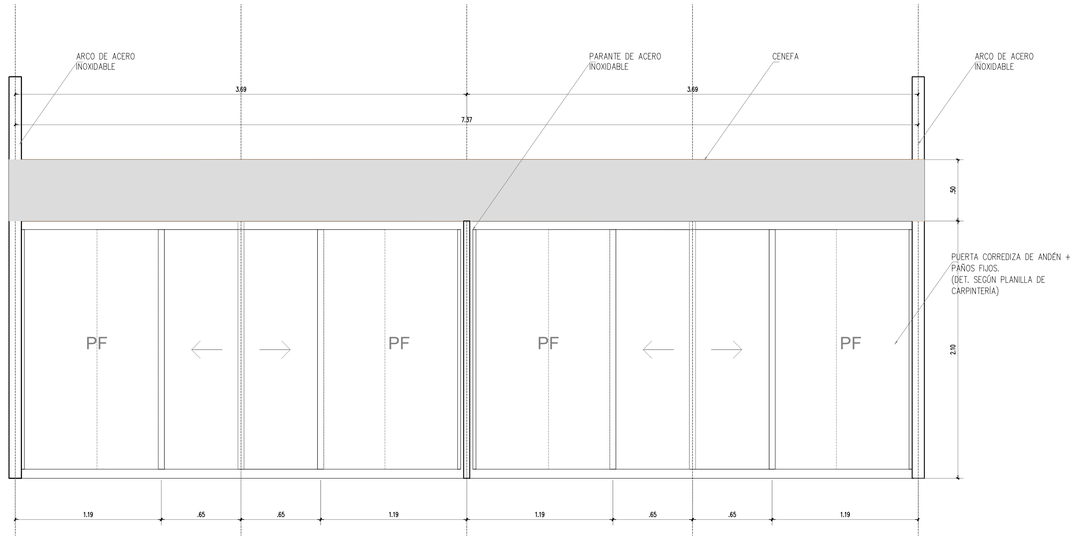
# PUERTA ANDÉN


CORTE 1:25





VISTA 1:25



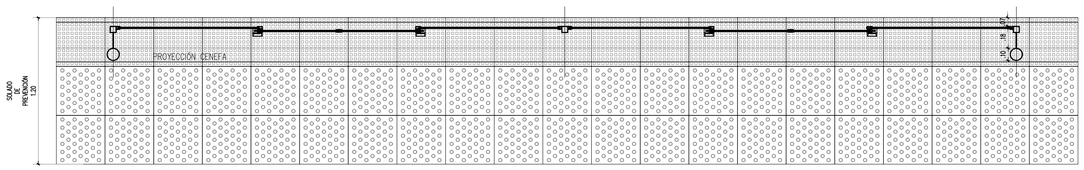

PLANTA 1:25





DETALLE 1 1:5
FIJACIÓN PERFIL

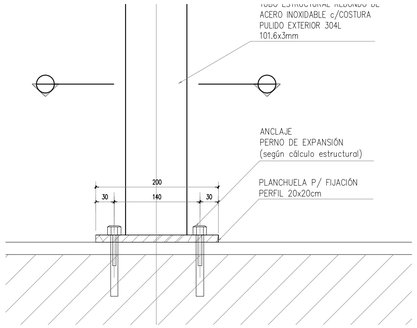



DETALLE 2 1:5
FIJACIÓN PERFIL

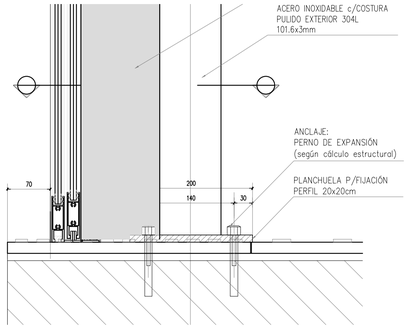



DETALLE 3 1:5
CENEFA

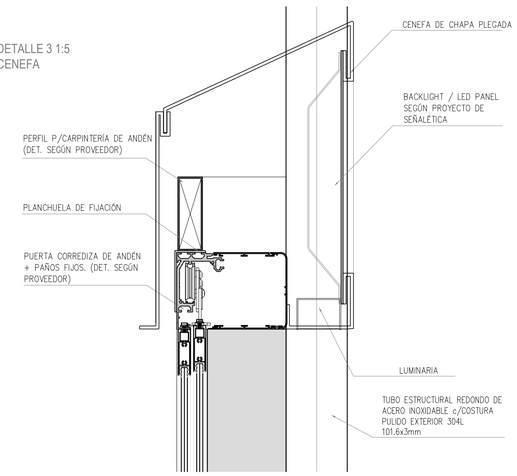


PLANTA 1 1:5
FIJACIÓN PERFIL

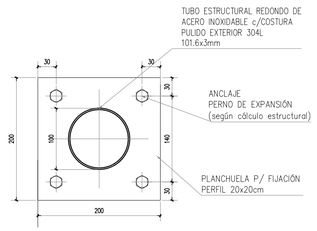


PLANTA 2 1:5
FIJACIÓN PERFIL

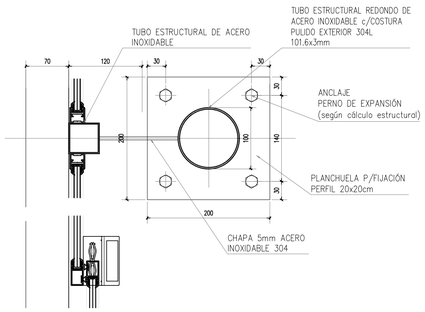


**NOTAS:** EL PRESENTE PLANO ES INDICATIVO. LA CONTRATISTA CONFECCIONARÁ LOS PLANOS DE DETALLE DEFINITIVOS, QUE DEBERÁN SER APROBADOS POR LA D.G.U.OBY LA INSPECCIÓN DE OBRA. EL PLANO PRESENTADO POR LA CONTRATISTA ESTARÁ EN UN TODO DE ACUERDO CON LA NORMATIVA VIGENTE. LA CONTRATISTA DEBERÁ VERIFICAR TODAS LAS MEDIDAS EN OBRA ANTES DE EJECUTAR LOS TRABAJOS. TODOS LOS DETALLES CONSTRUCTIVOS SERÁN COORDINADOS Y CONVENCIONADOS EN OBRA.

PLANO NO APTO PARA CONSTRUCCIÓN

**MODIFICACIONES:**

| REVISION | FECHA | DESCRIPCION |
|---|---|---|
| 00 | 20-11-2025 | EMISIÓN PARA LICITACIÓN |
| 01 | 10-04-2026 | EMISIÓN PARA LICITACIÓN |

MINISTERIO DE INFRAESTRUCTURA
SUBSECRETARIA DE PROYECTOS Y OBRAS
**DIRECCION GENERAL DE PROYECTOS**

**DGPRO**

Obra: LÍNEA F

Plano Estacion Constitución- Detalle Puerta de Andén

Fecha :10/04/2026 | Eq. de Proyecto: UPU - ATEC - IATASA | Dibujó: JS | Revisó: GV | Escala: 1:25/ 1:5

PLANO-2026-23204517-GCABA-SSP

LF-ES-CON-ARQ-PL-023-R01

Hoja N°: A023

G O B I E R N O DE LA C I U D A D DE B U E N O S A I R E S

"2026 - Año del 30° Aniversario de la sanción de la Constitución de la Ciudad Autónoma de Buenos Aires"

**Hoja Adicional de Firmas**
**Plano**

**Número:** PLANO-2026-23204517-GCABA-SSPO

Buenos Aires, Domingo 17 de Mayo de 2026

**Referencia:** LF-ES-CON-ARQ-PL-023_1

---

El documento fue importado por el sistema GEDO con un total de 1 pagina/s.

Digitally signed by Comunicaciones Oficiales
Date: 2026.05.17 16:42:24 -03:00

Facundo Lombardo
Subsecretario
SUBSECRETARIA PROYECTOS Y OBRAS
MINISTERIO DE MOVILIDAD E INFRAESTRUCTURA

Digitally signed by Comunicaciones Oficiales
Date: 2026.05.17 16:42:25 -03:00