ALZADO 01
1 : 25

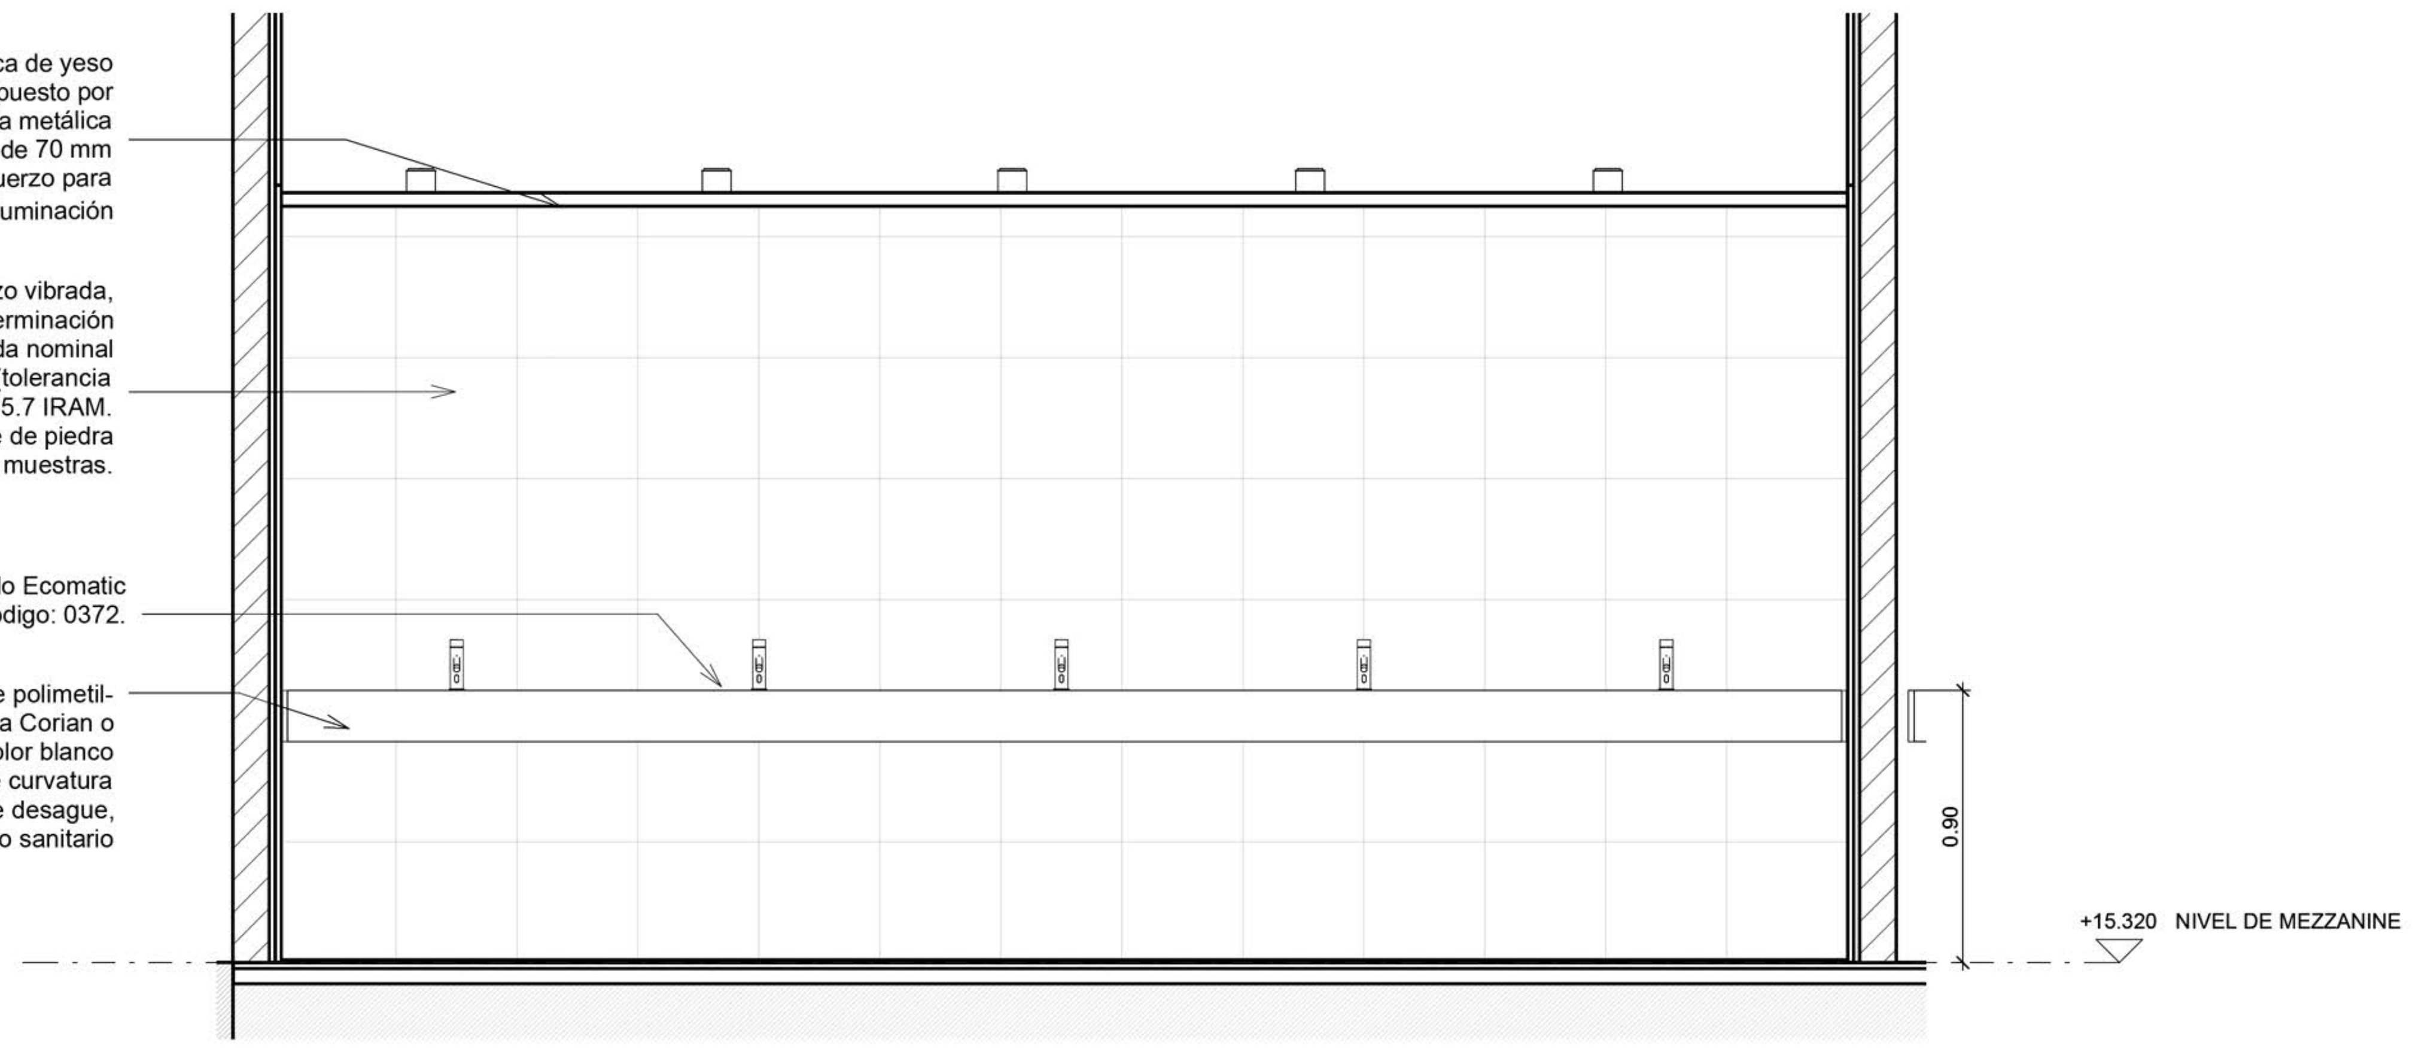
C1 Cielorraso suspendido de placas de roca de yeso resistente a la humedad junta tomada compuesto por placa de roca de yeso de 12,5 mm + estructura metálica de chaoa galvanizada n| 24 compuesta por soleras de 70 mm y montantes de 69 mm seoarados cada 40 cm, c/refuerzo para Artefacto de iluminación
R1: Piso y pared. Placa granítica tipo Terrazo vibrada, prensada y pulida para terminación e impermeabilización en obra. Medida nominal 397mmx397mmx18mm (tolerancia +/. 1 mm). Canto Rectificado. Absorción de agua 5.7 IRAM. Color de masa, color, granulometría y porcentaje de piedra a definir sobre muestras.
Gr-01: canilla automática modelo Ecomatic para lavatorio, marca FV. Código: 0372.
Sa-04: Lavatorio y mesada de polimetil-metacrilato de Dupont línea Corian o similar color blanco en una sola pieza con leve curvatura para generar pendiente de desague, largo variable según núcleo sanitario
0.90
+15.320 NIVEL DE MEZZANINE

ALZADO 02
1 : 25

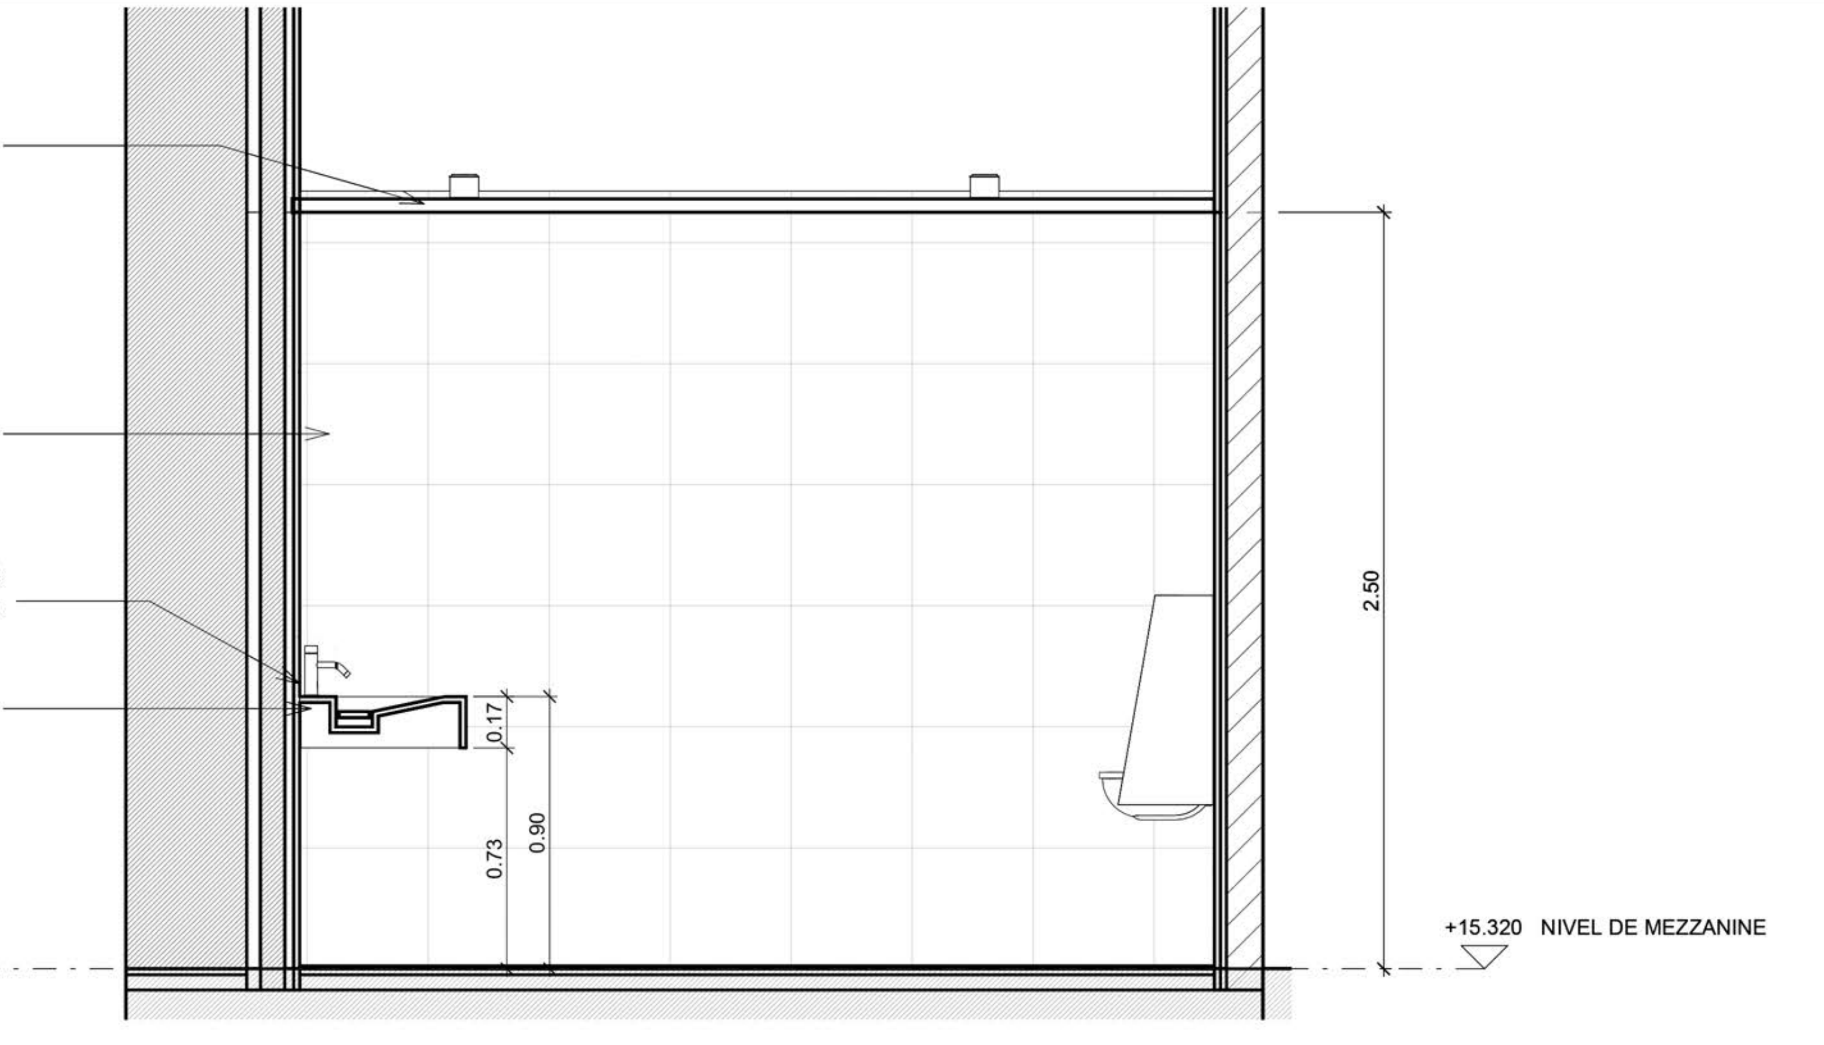
C1 Cielorraso suspendido de placas de roca de yeso resistente a la humedad junta tomada compuesto por placa de roca de yeso de 12,5 mm + estructura metálica de chaoa galvanizada n| 24 compuesta por soleras de 70 mm y montantes de 69 mm seoarados cada 40 cm, c/refuerzo para Artefacto de iluminación
Espejo sobre bastidor metálico con garganta superior para luminaria lineal a definir por la D.O.
Gr-01: canilla automática modelo Ecomatic para lavatorio, marca FV. Código: 0372.
Sa-04: Lavatorio y mesada de polimetil-metacrilato de Dupont línea Corian o similar color blanco en una sola pieza con leve curvatura para generar pendiente de desague, largo variable según núcleo sanitario
2.50
0.17
0.73
0.90
+15.320 NIVEL DE MEZZANINE

ALZADO 03
1 : 25

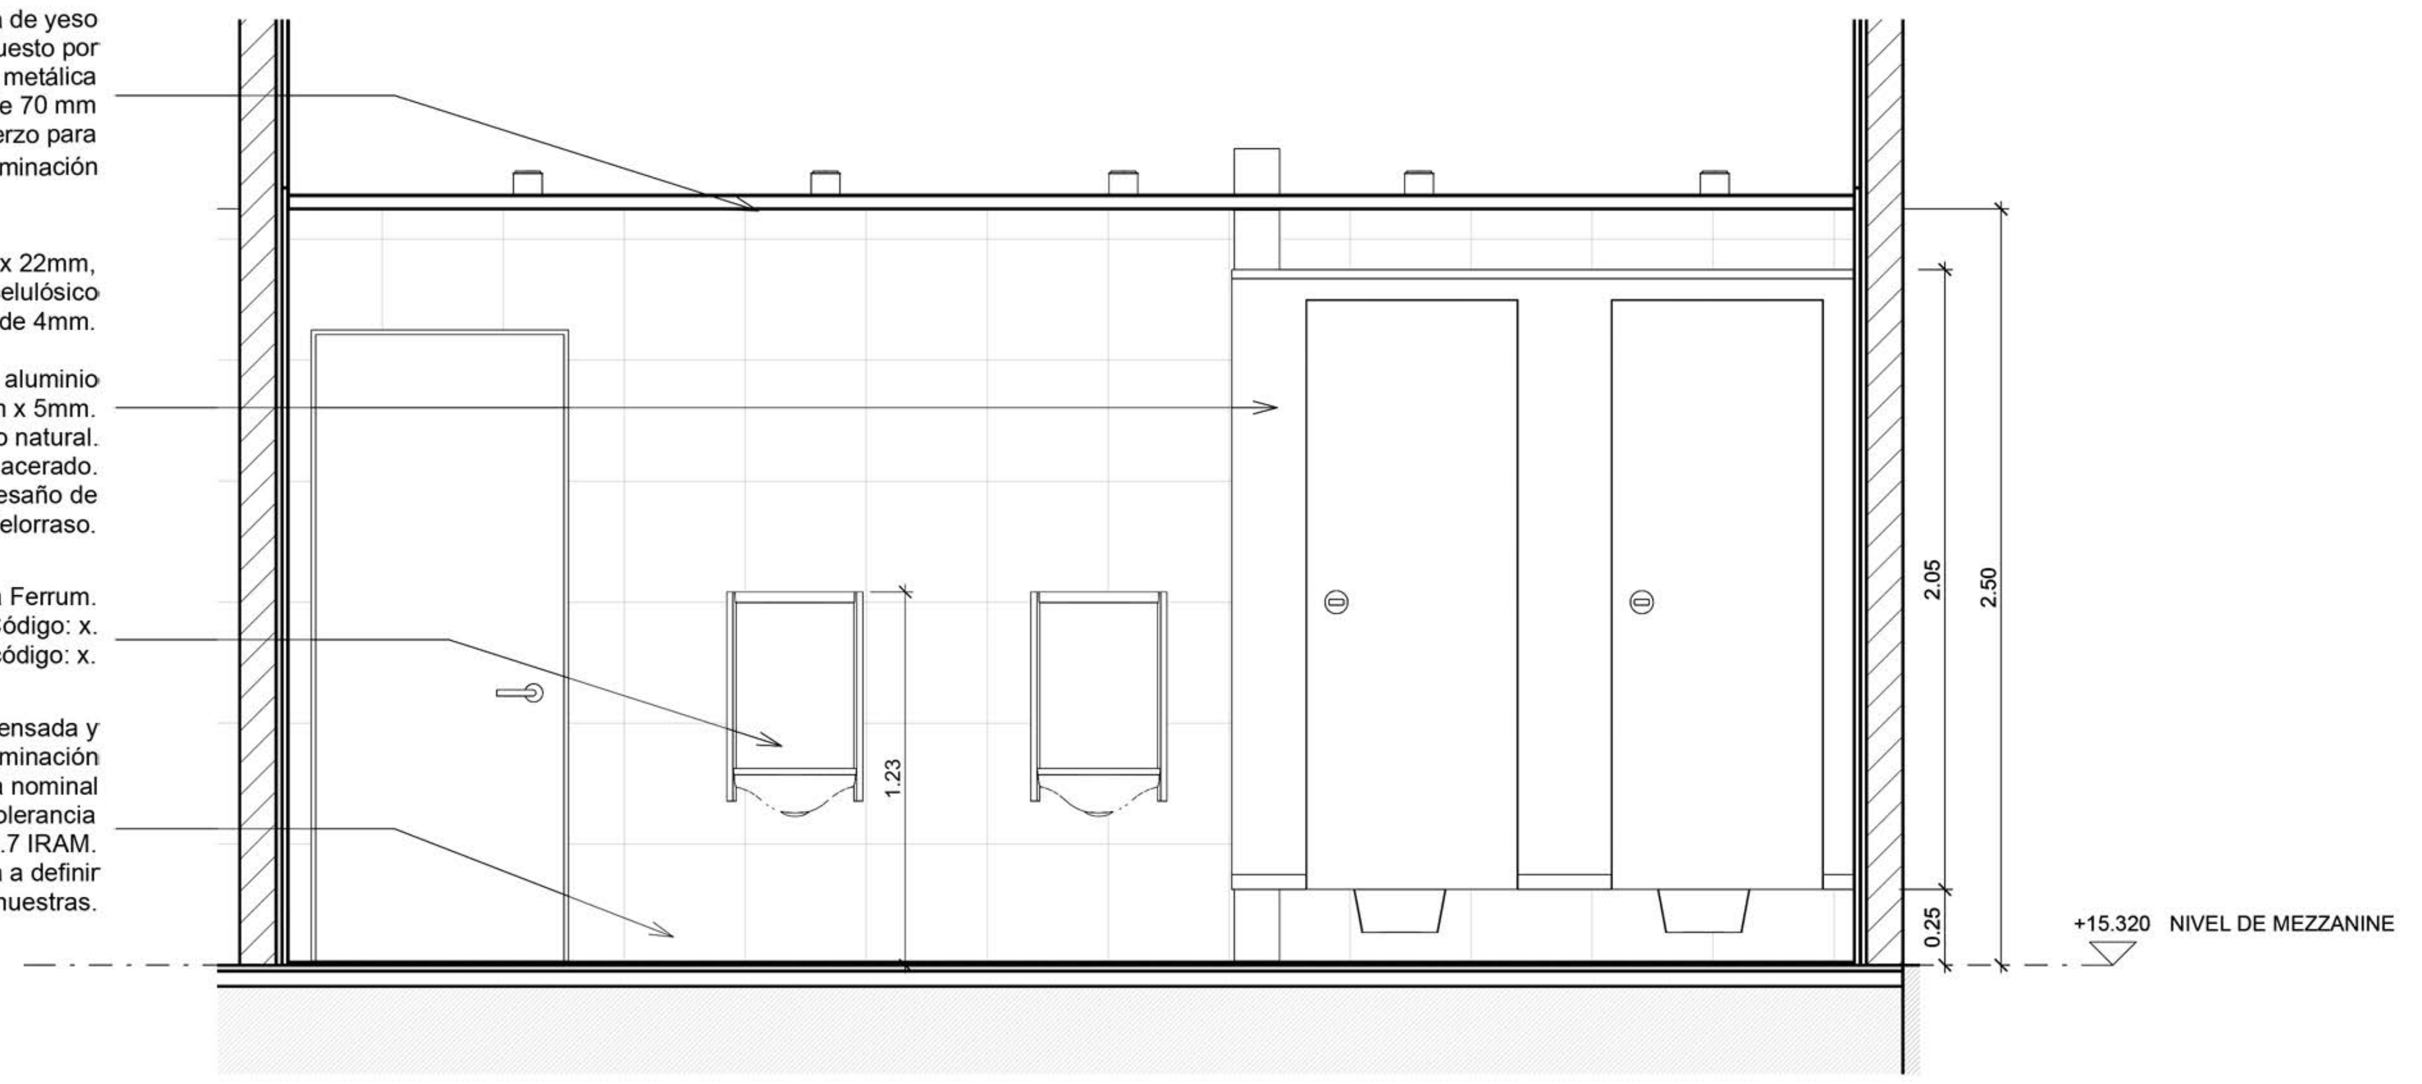
C1 Cielorraso suspendido de placas de roca de yeso resistente a la humedad junta tomada compuesto por placa de roca de yeso de 12,5 mm + estructura metálica de chaoa galvanizada n| 24 compuesta por soleras de 70 mm y montantes de 69 mm seoarados cada 40 cm, c/refuerzo para Artefacto de iluminación
Placas con bastidor de MDF de 45 x 22mm, rellenas con nido de abeja celulósico impermeable, con tapas de MDF de 4mm.
Tapacantos con perfil de aluminio anodizadoMVT194® de 45mm x 5mm. Bisagras de aluminio anodizado natural. Herraje de cierre tipo libre-ocupado acerado. Zócalos de acero inoxidable y travesaño de aluminio con o sin vinculación a cielorraso.
Sa-XX: Mingitorio mural, color blanco, marca Ferrum. Código: x. Con refuerzo y ménsula marca Ferrum, código: x.
R1: Piso y pared. Placa granítica tipo Terrazo vibrada, prensada y pulida para terminación e impermeabilización en obra. Medida nominal 397mmx397mmx18mm (tolerancia +/. 1 mm). Canto Rectificado. Absorción de agua 5.7 IRAM. Color de masa, color, granulometría y porcentaje de piedra a definir sobre muestras.
1.23
2.05
2.50
0.25
+15.320 NIVEL DE MEZZANINE

ALZADO 04
1 : 25

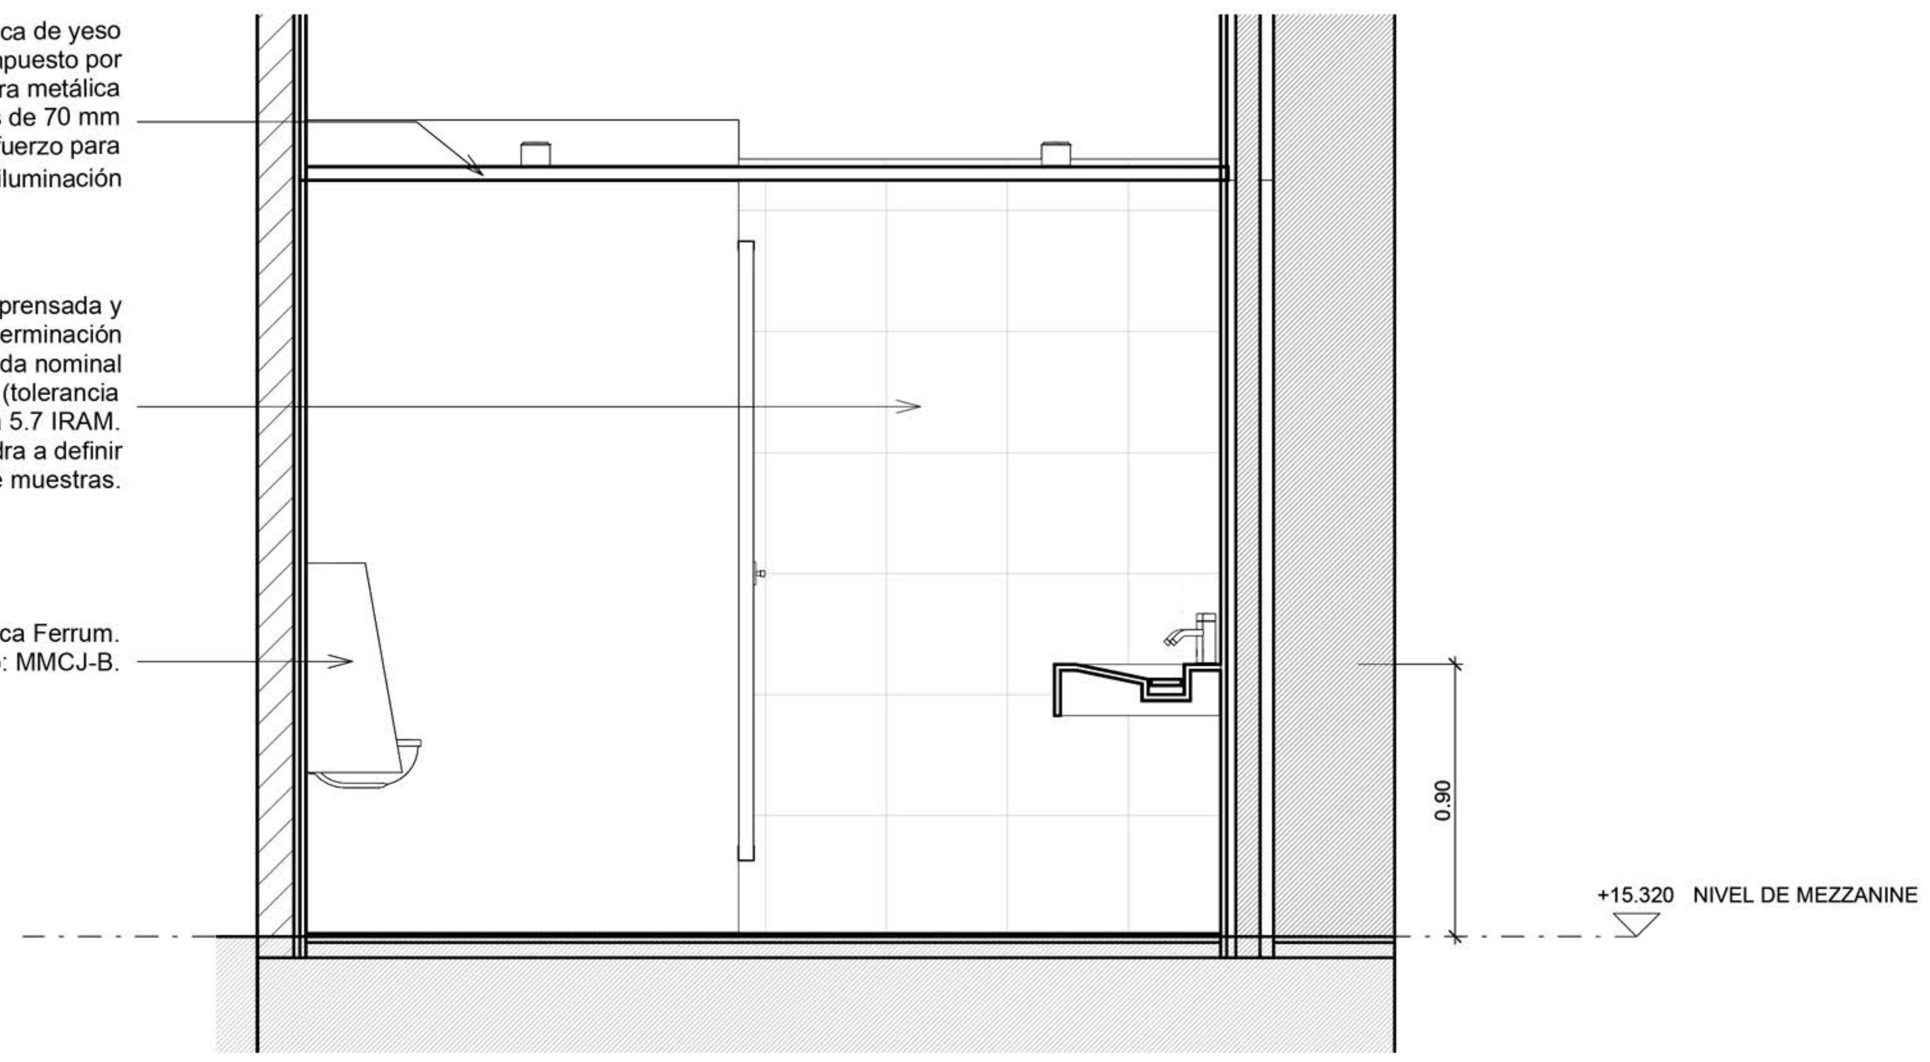
C1 Cielorraso suspendido de placas de roca de yeso resistente a la humedad junta tomada compuesto por placa de roca de yeso de 12,5 mm + estructura metálica de chaoa galvanizada n| 24 compuesta por soleras de 70 mm y montantes de 69 mm seoarados cada 40 cm, c/refuerzo para Artefacto de iluminación
R1: Piso y pared. Placa granítica tipo Terrazo vibrada, prensada y pulida para terminación e impermeabilización en obra. Medida nominal 397mmx397mmx18mm (tolerancia +/. 1 mm). Canto Rectificado. Absorción de agua 5.7 IRAM. Color de masa, color, granulometría y porcentaje de piedra a definir sobre muestras.
Sa-03: Mingitorio mural corto, color blanco, marca Ferrum. Código: MMCJ-B.
0.90
+15.320 NIVEL DE MEZZANINE

ALZADO 05
1 : 25

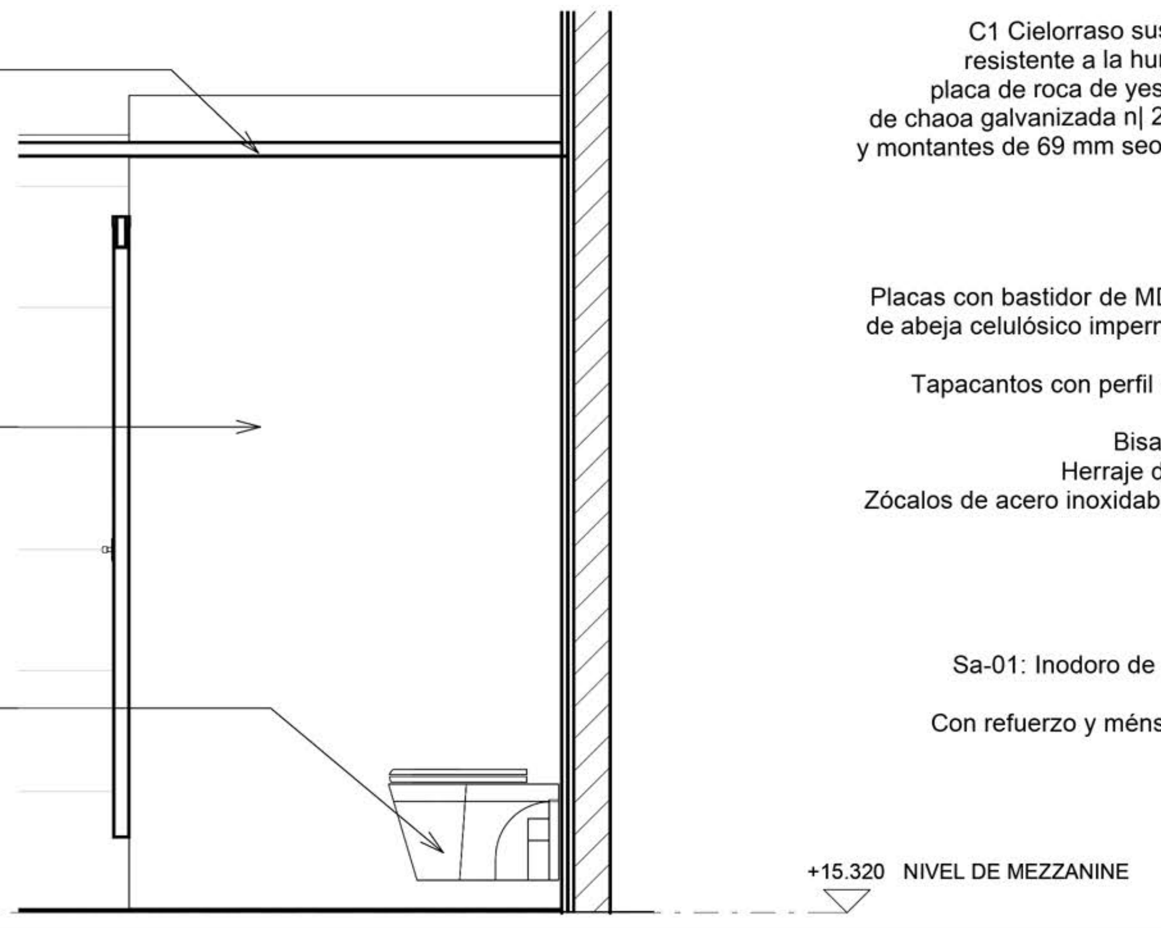
C1 Cielorraso suspendido de placas de roca de yeso resistente a la humedad junta tomada compuesto por placa de roca de yeso de 12,5 mm + estructura metálica de chaoa galvanizada n| 24 compuesta por soleras de 70 mm y montantes de 69 mm seoarados cada 40 cm, c/refuerzo para Artefacto de iluminación
Placas con bastidor de MDF de 45 x 22mm, rellenas con nido de abeja celulósico impermeable, con tapas de MDF de 4mm.
Tapacantos con perfil de aluminio anodizadoMVT194® de 45mm x 5mm. Bisagras de aluminio anodizado natural. Herraje de cierre tipo libre-ocupado acerado. Zócalos de acero inoxidable y travesaño de aluminio con o sin vinculación a cielorraso.
Sa-01: Inodoro de colgar modelo Marina, color blanco, marca Ferrum. Código: IHPJ-B. Con refuerzo y ménsula marca Ferrum, código: VPSAC.
+15.320 NIVEL DE MEZZANINE

ALZADO 06
1 : 25

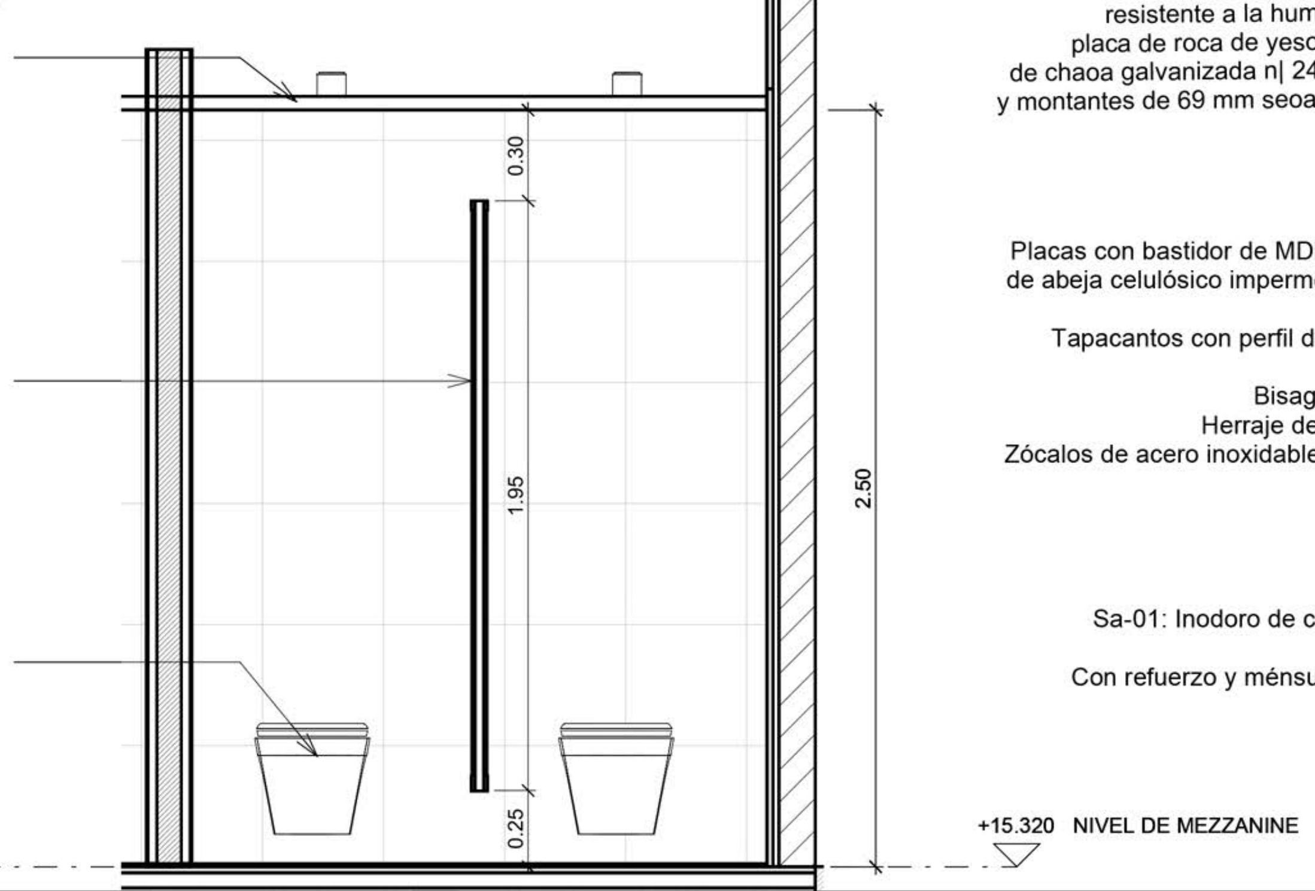
C1 Cielorraso suspendido de placas de roca de yeso resistente a la humedad junta tomada compuesto por placa de roca de yeso de 12,5 mm + estructura metálica de chaoa galvanizada n| 24 compuesta por soleras de 70 mm y montantes de 69 mm seoarados cada 40 cm, c/refuerzo para Artefacto de iluminación
Placas con bastidor de MDF de 45 x 22mm, rellenas con nido de abeja celulósico impermeable, con tapas de MDF de 4mm.
Tapacantos con perfil de aluminio anodizadoMVT194® de 45mm x 5mm. Bisagras de aluminio anodizado natural. Herraje de cierre tipo libre-ocupado acerado. Zócalos de acero inoxidable y travesaño de aluminio con o sin vinculación a cielorraso.
Sa-01: Inodoro de colgar modelo Marina, color blanco, marca Ferrum. Código: IHPJ-B. Con refuerzo y ménsula marca Ferrum, código: VPSAC.
0.30
1.95
0.25
2.50
+15.320 NIVEL DE MEZZANINE

ALZADO 07
1 : 25

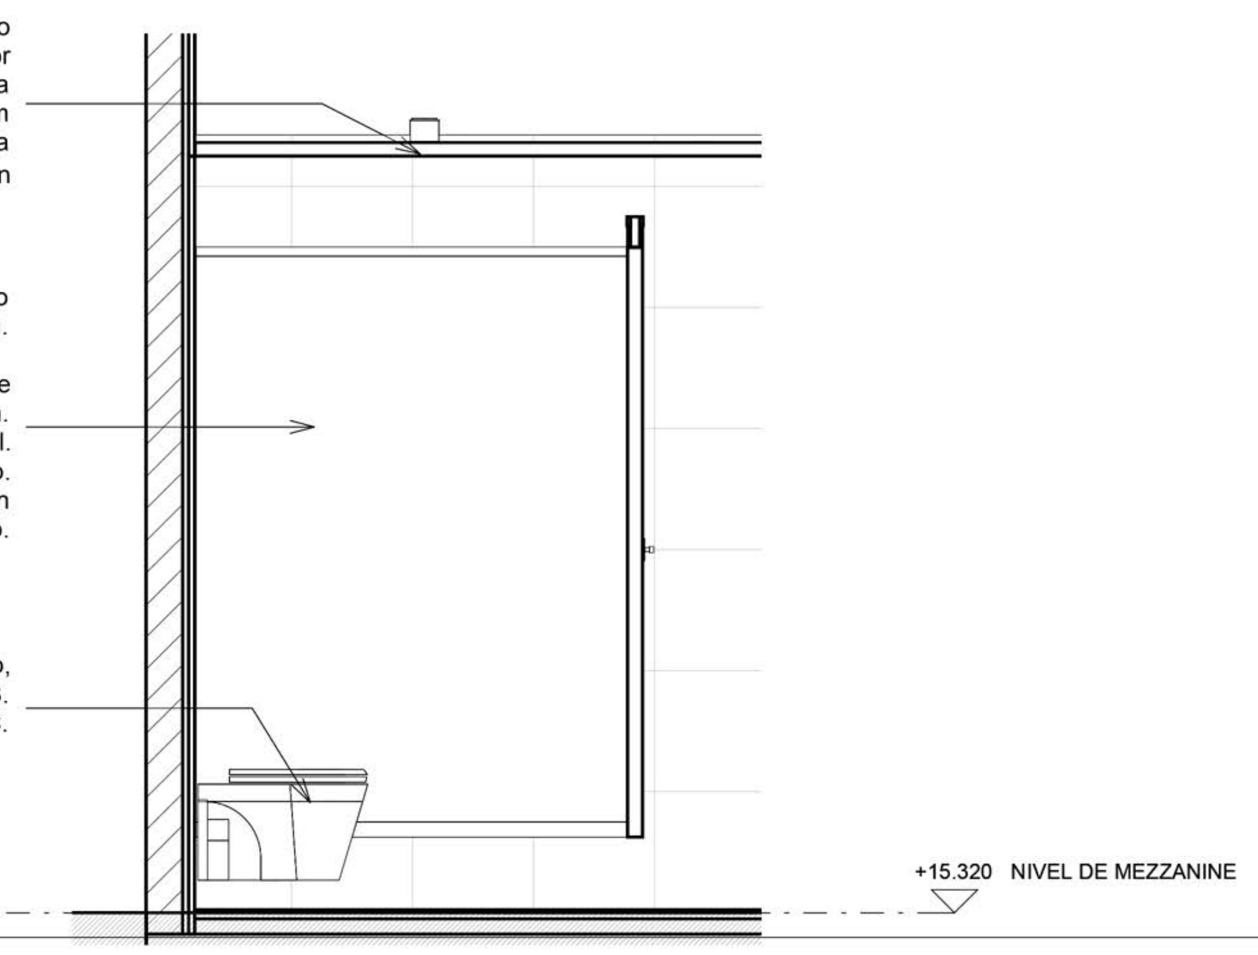
C1 Cielorraso suspendido de placas de roca de yeso resistente a la humedad junta tomada compuesto por placa de roca de yeso de 12,5 mm + estructura metálica de chaoa galvanizada n| 24 compuesta por soleras de 70 mm y montantes de 69 mm seoarados cada 40 cm, c/refuerzo para Artefacto de iluminación
Placas con bastidor de MDF de 45 x 22mm, rellenas con nido de abeja celulósico impermeable, con tapas de MDF de 4mm.
Tapacantos con perfil de aluminio anodizadoMVT194® de 45mm x 5mm. Bisagras de aluminio anodizado natural. Herraje de cierre tipo libre-ocupado acerado. Zócalos de acero inoxidable y travesaño de aluminio con o sin vinculación a cielorraso.
Sa-01: Inodoro de colgar modelo Marina, color blanco, marca Ferrum. Código: IHPJ-B. Con refuerzo y ménsula marca Ferrum, código: VPSAC.
+15.320 NIVEL DE MEZZANINE

PODOTÁCTIL

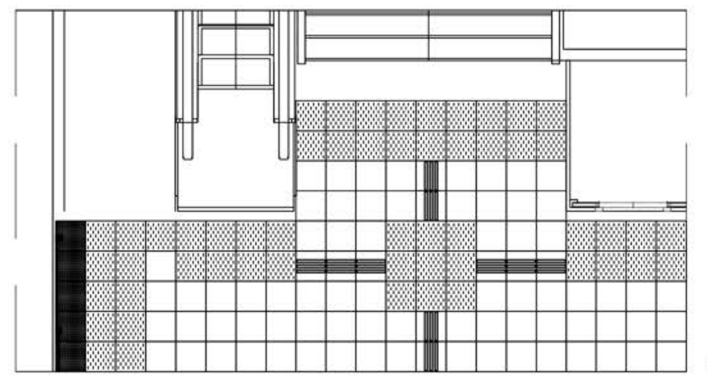
DETALLE ESQUEMA 01

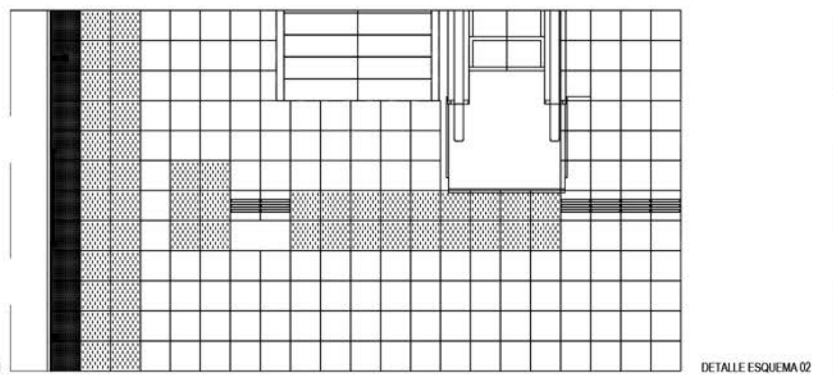
DETALLE ESQUEMA 02

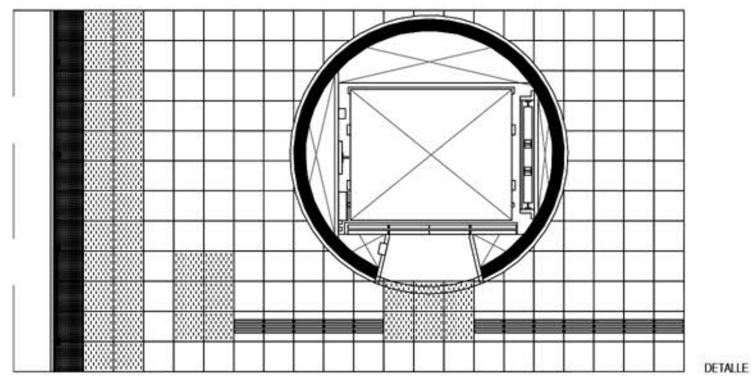
DETALLE ESQUEMA 03

SOLADO TIPO S3
LOS SOLADOS DE PREVENCIÓN SON SEÑALIZACIONES EN PISOS QUE SE UTILIZAN PARA:
-INDICAR COMIENZO Y FINALIZACIÓN DE UNA FRANJA GUÍA.
-SEÑALAR BIFURCACIONES EN UNA FRANJA GUÍA.
-ANUNCIAR LA PRESENCIA DE ESCALERAS O RAMPAS.
-INFORMAR SOBRE LA EXISTENCIA DE OBSTÁCULOS Y ELEMENTOS DE INFORMACIÓN.
EL SOLADO DE PREVENCIÓN SE COLOCARÁ, SOBRE TODO EL ANCHO, FRENTE DE ESCALERAS Y RAMPAS, EN UNA FRANJA DE 600mm DE LADO COMO MÍNIMO.
TAMBIÉN E COLOCARÁ EN EL PERÍMETRO DE TODOS LOS BAJO ESCALERAS PERO EN UNA FRANJA DE 300mm.

SOLADO TIPO S4
LAS FRANJAS DE GUÍA PARA DISCAPACITADOS VISUALES SON SEÑALIZACIONES EN SOLADOS QUE INDICAN LA DIRECCIÓN DE RECORRIDO, CUYAS ACANALADURAS SIEMPRE DEBEN ESTAR ORIENTADAS EN LA DIRECCIÓN DE LA MARCHA.
4.2.3 SE DEBEN COLOCAR DENTRO DEL VOLUMEN LIBRE DE RIESGO, SEGÚN IRAM 111100, A UNA DISTANCIA MÍNIMA DE 600mm DE LOS ELEMENTOS FIJOS, EN GRANDES ESPACIOS SIN PAUTAS DE REFERENCIA PRÓXIMAS.

SOLADO TIPO S5
LOS SOLADOS DE PELIGRO SON SEÑALIZACIONES EN PISOS QUE SE UITLIZAN PARA:
-ALERTAR SOBRE SITUACIONES DE RIESGO DE CAÍDAS POR LA PRESENCIA DE DESNIVELES INFRANQUEABLES, BORDES DE ANDENES, ESCALERAS DESCENDENTES Y EN EL LÍMITE DE ÁREAS RESTRINGIDAS POR SEGURIDAD.
SE DEBEN DISPONER SOLADOS DE PELIGRO EN:
-LOS BORDES DE ANDENES.
EN EL BORDE DE ANDÉN EL SOLADO DE PELIGRO SE COMBINARÁ CON DOS PIEZAS DEL SOLADO DE PREVENCIÓN COMO LO INDICA LA FIGURA

NOTACIÓN

LOCAL — INDICA NOMBRE DE LOCAL
N-XX — NUMERO DE LOCAL
— NIVEL DE PLANTA
CX 0.00 — CIELORRASO Y ALTURA DEL LOCAL
SX ZX — SOLADO Y ZÓCALO
PXX 0.00 — INDICA NUMERO DE CARPINTERIA / INDICA ANCHO DE VANO
INDICA DETALLE DE SECTOR O LOCAL — DETALLE 01 VER PLANO A1001
MXX — INDICA TIPO DE MURO SEGUN PLANILLA
RXX — INDICA TERMINACION MURO SEGUN PLANILLA

MUROS

M1 TABIQUE DE HORMIGÓN ARMADO S/ CÁLCULO.

M2 TABIQUE DE HORMIGÓN BLANCO A LA VISTA UNA SOLA CARA, ENCOFRADO FENÓLICO TIPO "GRANDIS" SELECCIÓN DE PRIMERA CALIDAD CON SEPARADORES A 30 MM, PASADORES MODULADOS S/ PLANO DE ENCOFRADO.

M3 TABIQUE COMPUESTO: TABIQUE DE HORMIGÓN ARMADO SEGUN CALCULO ESPESOR VARIABLE + CAMARA DE AIRE 3CM + TABIQUE DE LADRILLO COMÚN DE 12X25X5 APAREJO DE 15 CM.

M4 TABIQUE DE LADRILLO CERÁMICO HUECO DE 12X18X33.

M5 TABIQUE DE LADRILLO CERÁMICO HUECO DE 18X18X33.

M6 TABIQUE DE LADRILLO COMÚN 12X25X5 CM REVOCADO + ESTRUCTURA METÁLICA DE CHAPA GALVANIZADA DE 70MM +FIBRA DE VIDRIO (70 MM 35 KG/M3) +SEPARACIÓN DE 3 CM + FIBRA DE VIDRIO (50 MM 35 KG/M3)+ 2 PLACAS CEMENTICIAS DE 15 MM + ESTRUCTURA GALVANIZADA DE 54 MM + FIBRA DE VIDRIO (50 MM 50KG/M3) + CHAPA PERFORADA SEGÚN CÁLCULO SOBRE BASTIDOR DE ALUMINIO.

M7 TABIQUE COMPUESTO: TABIQUE DE HORMIGÓN ARMADO SEGÚN CALCULO ESPESOR VARIABLE + CAMARA DE AIRE 3CM + TABIQUE DE LADRILLO CERÁMICO HUECO DE 8X18X33.

M8 TABIQUE COMPUESTO: TABIQUE DE HORMIGÓN ARMADO SEGÚN CALCULO ESPESOR VARIABLE + TABIQUE DE LADRILLO CERÁMICO HUECO DE 8X18X33.

M9 TABIQUE DE LADRILLO COMÚN DE 12X25X5, APAREJO DE 15CM

M10 TABIQUE DE HORMIGÓN ARMADO SEG. CÁLCULO + ESTRUCTURA METÁLICA DE CHAPA GALVANIZADA DE 70MM +FIBRA DE VIDRIO (70 MM 35 KG/M3) +SEPARACIÓN DE 3 CM + FIBRA DE VIDRIO (50 MM 35 KG/M3)+ 2 PLACAS CEMENTICIAS DE 15 MM + ESTRUCTURA GALVANIZADA DE 54 MM + FIBRA DE VIDRIO (50 MM 50KG/M3) + CHAPA PERFORADA SEGÚN CÁLCULO SOBRE BASTIDOR DE ALUMINIO.

TERMINACIONES Y REVESTIMIENTOS

R1 PLACA GRANÍTICA TIPO TERRAZZO VIBRADA, PRENSADA Y PULIDA PARA TERMINACIÓN E IMPERMEABILIZACIÓN EN OBRA. TERMINACIÓN SATINADA. MEDIDA NOMINAL 397MMX397MMX18MM (TOLERANCIA +/-1MM). CANTO RECTIFICADO. ABSORCIÓN DE AGUA 5.7 IRAM ≤10%. COLOR DE MASA, COLOR, GRANULOMETRÍA Y PORCENTAJE DE PIEDRA A DEFINIR SOBRE MUESTRAS.

R2 PINTURA SILICONADA HIDRÓFUGA INCOLORA EN BASE ACUOSA "SILEQUIM A" O SIMILAR EQUIVALENTE.

R3 G.R.C. (GLASS FIBER REINFORCED CONCRETE) COMPUESTO DE UNA MATRIZ DE MORTERO ARMADO CON FIBRA DE VIDRIO RESISTENTE A LOS ÁLCALIS. SISTEMA TIPO STUD-FRAME FORMADO POR UNA CÁSCARA DE G.R.C. DE 10 MM A LA QUE SE LE INCORPORA UN BASTIDOR TUBULAR METÁLICO ZINCADO FIJADO MEDIANTE CONECTORES METÁLICOS A DICHA CÁSCARA.TIPO PICAST O SIMILAR EQUIVALENTE.

R4 G.R.C. CON AISLACIÓN ACÚSTICA: (GLASS FIBER REINFORCED CONCRETE) COMPUESTO DE UNA MATRIZ DE MORTERO ARMADO CON FIBRA DE VIDRIO RESISTENTE A LOS ÁLCALIS. SISTEMA TIPO STUD-FRAME FORMADO POR UNA CÁSCARA PERFORADA DE G.R.C. DE 10 MM A LA QUE SE LE INCORPORA UN BASTIDOR TUBULAR METÁLICO ZINCADO FIJADO MEDIANTE CONECTORES METÁLICOS A DICHA CÁSCARA CON AISLACIÓN DE LANA DE ROCA 50MM 74 KG/M3 + VELO DE VIDRIO NEGRO. TIPO PICAST O SIMILAR EQUIVALENTE.

R5 PINTURA AL LÁTEX ACRÍLICO. COLOR A DEFINIR.

R6 ESMALTE SINTÉTICO AL AGUA. COLOR A DEFINIR.

R7 BANDEJAS DE ACERO INNOXIDABLE AISI 300 E=2.5MM CON RESPALDO DE LAMINADO FENOLICO E:15MM COLGADO CON SISITEMA DE PERCHAS DE ALUMINIO. TERMINACION PULIDO SATINADO.

R8 REVESTIMIENTO CON LIGANTE ACRÍLICO PIEDRA PLAST, DE MOLINOS TARQUINI O SIMILAR EQUIVALENTE.
COLOR: FINISTERRE BALVANERA.

R9 REVESTIMIENTO ACRÍLICO Y MINERAL GRANALLADO TEXTURA DE BAJA DENSIDAD. DE MOLINOS TARQUINI O SIMILAR EQUIVALENTE. COLOR: A DEFINIR.

CIELORRASOS

C1 CIELORRASO SUSPENDIDO DE PLACAS DE ROCA DE YESO RESISTENTE A LA HUMEDAD JUNTA TOMADA COMPUESTO POR PLACA DE ROCA DE YESO DE 12,5MM + ESTRUCTURA METÁLICA DE CHAPA GALVANIZADA N° 24 COMPUESTA POR SOLERAS DE 70 MM Y MONTANTES DE 69 MM SEPARADOS CADA 40 CM. C/ REFUERZO PARA ARTEF. DE ILUMINACIÓN.

C2 CIELORRASO SUSPENDIDO DE PLACAS DE ROCA DE YESO JUNTA TOMADA COMPUESTO POR PLACA DE ROCA DE YESO RESISTENTE RF60 DE 12,5MM + ESTRUCTURA METÁLICA DE CHAPA GALVANIZADA N° 24 COMPUESTA POR SOLERAS DE 70 MM Y MONTANTES DE 69 MM SEPARADOS CADA 40 CM. C/ REFUERZO PARA ARTEF. DE ILUMINACIÓN.

C3 GRC (GLASS FIBER REINFORCED CONCRETE) COMPUESTO DE MORTERO Y VIDRIO. ESPESOR 10MM SOBRE BASTIDOR METÁLICO ZINCADO SEGÚN CÁLCULO. TIPO PICAST O SIMILAR EQUIVALENTE.

C4 PINTURA SILICONADA HIDRÓFUGA INCOLORA EN BASE ACUOSA "SILEQUIM A" O SIMILAR EQUIVALENTE, SOBRE HORMIGON A LA VISTA TAPONADO PARA PINTAR.

C5 PINTURA AL LÁTEX ACRÍLICO SOBRE HORMIGÓN A LA VISTA TAPONADO PARA PINTAR. COLOR A DEFINIR.

C6 CIELORRASO MODULAR METALICO PERFORADO ACUSTICO SUSPENDIDO.
COLOR A DEFINIR.

C7 LAMAS DE GRC (GLASS FIBER REINFORCED CONCRETE) COMPUESTO DE MORTERO Y VIDRIO. ESPESOR 10CM, ALTURA 100CM , SOBRE BASTIDOR METÁLICO ZINCADO SEGÚN CÁLCULO. TIPO PICAST O SIMILAR EQUIVALENTE.

ZÓCALOS Y SOLIAS

Z1 ZÓCALO SANITARIO H:100MM, RADIO DE CURVATURA 25MM, LARGO 397MM, ANCHO: 50MM, ESPESOR 18MM. IDEM S1.

Z2 ZÓCALO DE ALISADO DE CEMENTO CON COLOR INCORPORADO H:125MM ESPESOR 10MM.

SO1 SOLIA VARILLA ACERO INOXIDABLE *35 MM MARCA ATRIM O SIMILAR EQUIVALENTE.

SOLADOS

S1 PLACA GRANÍTICA TIPO TERRAZZO VIBRADA, PRENSADA Y PULIDA PARA TERMINACIÓN E IMPERMEABILIZACIÓN EN OBRA. TERMINACIÓN SATINADA. MEDIDA NOMINAL 397MMX397MMX18MM (TOLERANCIA +/-1MM). CANTO RECTIFICADO. ABSORCIÓN DE AGUA: 5.7% (IRAM ≤10%). RESISTENCIA AL DESGASTE:133(IRAM ≤15MM). PRUEBA DE IMPACTO: 180 (IRAM≥70CM ALTURA). RESISTENCIA A LA FLEXIÓN: 596KG/CM2(IRAM≥35KG/CM2). COLOR DE MASA, COLOR, GRANULOMETRÍA Y PORCENTAJE DE PIEDRA A DEFINIR SOBRE MUESTRAS.

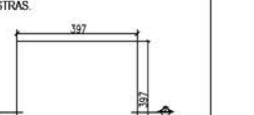

S2 ESCALÓN GRANÍTICO CONTINUO EJECUTADO IN SITU CON AGREGADO DE FIBRAS DE NYLON SOBRE CARPETA DE CONCRETO PARA TERMINACIÓN E IMPERMEABILIZACIÓN EN OBRA. TERMINACIÓN SATINADA. COLOR DE MASA, COLOR, GRANULOMETRÍA Y PORCENTAJE DE PIEDRA A DEFINIR SOBRE MUESTRAS. ESPESOR COLADO 12MM CON MALLA DE 10X10MM X150GRS.

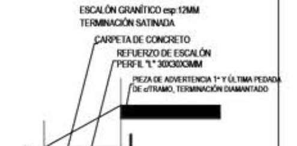
ESCALÓN GRANÍTICO esp:12MM TERMINACIÓN SATINADA
CARPETA DE CONCRETO
REFUERZO DE ESCALÓN PERFIL "L" 30X30X3MM
PIEZA DE ADVERTENCIA 1° Y ÚLTIMA PEDADA DE c/TRAMO, TERMINACIÓN DIAMANTADO
290
162
319
330

S3 SOLADO DE PREVENCIÓN. PLACA GRANÍTICA TIPO TERRAZZO VIBRADA, PRENSADA Y PULIDA PARA TERMINACIÓN E IMPERMEABILIZACIÓN EN OBRA, ÍDEM S1. SUPERFICIE TEXTURADA EN FORMA DE BOTONES EN RELIEVE DE 5MM +/- 1MM DE ALTURA, CON DIÁMETRO DE BASE 25MM +/- 5MM, COLOCADOS EN TRESBOLILLO CON UNA DISTANCIA AL CENTRO DE LOS RELIEVES DE 60MM +/- 5MM. COLOR DE MASA, COLOR, GRANULOMETRÍA Y PORCENTAJE DE PIEDRA A DEFINIR SOBRE MUESTRAS.

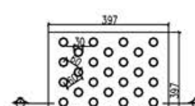

S4 SOLADO GUÍA PARA DISCAPACITADOS VISUALES. PLACA GRANÍTICA TIPO TERRAZZO VIBRADA, PRENSADA Y PULIDA PARA TERMINACIÓN E IMPERMEABILIZACIÓN EN OBRA, ÍDEM S1. SUPERFICIE TEXTURADA EN FORMA DE TRES BARRAS EN RELIEVE DE SECCIÓN PIRAMIDAL TRUNCA SIN ARISTAS VIVAS DE 4MM DE ALTURA POR 30MM MÁS 4MM DE BASE SEPARADAS 37MM +/-1MM. LA LONGITUD DE LAS BARRAS SERÁ DE 38MM. COLOR DE MASA, COLOR, GRANULOMETRÍA Y PORCENTAJE DE PIEDRA A DEFINIR SOBRE MUESTRAS.

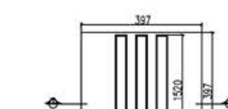

S5 PLACA GRANÍTICA TIPO TERRAZZO VIBRADA, PRENSADA Y PULIDA PARA TERMINACIÓN E IMPERMEABILIZACIÓN EN OBRA, ÍDEM S1. SUPERFICIE ANTIDESLIZANTE CONSTITUIDA POR UNA RELIEVE DE CUADRADOS DE 2MM. COLOR DE MASA, COLOR, GRANULOMETRÍA Y PORCENTAJE DE PIEDRA A DEFINIR SOBRE MUESTRAS.

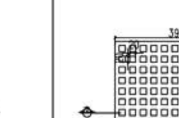

S6 ALISADO DE CEMENTO CON COLOR INCORPORADO Y CON ENDURECEDOR CUARCITICO. TERMINACIÓN RODILLADO. COLOR A DEFINIR CON TRATAMIENTO ANTI-POLVO, CURADOR Y SELLADOR TRANSPARENTE SIKAFLOOR CURE HARD 24.

S7 VIDRIO LAMINADO TRIPLE CAPA 10+10 +10 CON PVB DE SEGURIDAD SEGÚN CÁLCULO. TERMINACIÓN SUPERFICIAL ANTIDESLIZANTE EN BANDAS EJECUTADO MECÁNICAMENTE POR DESVASTADO EN LA TOTALIDAD DE LA SUPERFICIE DE LA PIEZA.

S8 MOSAICO RANURADO. LOSETA GRANÍTICA PREFABRICADA Y PRENSADA 40CMX40CM E: 3CM. MODELO 64 PANES. COLOR A DEFINIR.

S9 MOSAICO PODOTÁCTIL. BALDOSA DE PREVENCIÓN. PIEZA PREFABRICADA CEMENTICIA DE 40CMX40CM E:3CM. SUPERFICIE TEXTURADA EN FORMA DE BOTONES EN RELIEVE DE 5MM +/- 1MM DE ALTURA, CON DIÁMETRO DE BASE 25MM +/- 5MM, COLOCADOS EN TRESBOLILLO CON UNA DISTANCIA AL CENTRO DE LOS RELIEVES DE 60MM +/- 5MM. COLOR AMARILLO.

S10 MOSAICO PODOTACTIL. BALDOSA GUÍA. PIEZA PREFABRICADA CEMENTICIA DE 40CMX40CM E:3CM. SUPERFICIE TEXTURADA EN FORMA DE CINCO BARRAS EN RELIEVE DE SECCIÓN PIRAMIDAL TRUNCA SIN ARISTAS VIVAS DE 4MM DE ALTURA POR 30MM MÁS 4MM DE BASE SEPARADAS 37MM +/-1MM. LA LONGITUD DE LAS BARRAS SERÁ DE 38MM. COLOR A DEFINIR.

S11 PAVIMENTO CONTINUO ASFALTICO IDEM EXISTENTE

S12 PAVIMENTO PEATONAL DE HORMIGÓN ESTRIADO (PEINADO)

S13 SOLADO EXISTENTE. (NIC).

S14 PORFIDO PATAGONICO COLOR GRIS 10CMX10CM E: 4 A 6CM

S15 BALDOSA DE PÓRFIDO CORTE A DISCO GRIS, ANCHO 40CM Y LARGO VARIABLE E: 2 A 5CM.

NOTAS: EL PRESENTE PLANO ES INDICATIVO. LA CONTRATISTA CONFECCIONARÁ LOS PLANOS DE DETALLE DEFINITIVO, QUE DEBERÁN SER APROBADOS POR LA D.G.O.INF.U Y LA INSPECCIÓN DE OBRA. EL PLANO PRESENTADO POR LA CONTRATISTA ESTARA EN UN TODO DE ACUERDO CON LA NORMATIVA VIGENTE.
TODAS LAS MEDIDAS Y NIVELES SE VERIFICARÁN EN OBRA POR EL CONTRATISTA.
TODOS LOS DETALLES CONSTRUCTIVOS SERAN COORDINADOS Y COMPATIBILIZADOS EN OBRA.

PLANO NO APTO PARA CONSTRUCCIÓN

MODIFICACIONES:

REVISION	FECHA	DESCRIPCION
00	20/11/2025	Emision para Licitacion
01	10/04/2026	Emision para Licitacion

Gobierno de la Ciudad de Buenos Aires

MINISTERIO DE INFRAESTRUCTURA
SUBSECRETARIA DE PROYECTOS Y OBRAS
DIRECCION GENERAL DE PROYECTOS

DGPRO

Obra: LÍNEA F
Plano ESTACION CONSTITUCION- DETALLE DE SANITARIOS 02 de 02
Fecha :10/04/2026
Eq. de Proyecto: UPU - ATEC -IATASA
Dibujó: JG
PLANO-2026-23204710-GCABA-SSPO
LF-ES-CON-ARQ-PL-017-02-R01
Revisó: GV
Escala:
Plano N°: 017-02

GOBIERNO DE LA CIUDAD DE BUENOS AIRES

"2026 - Año del 30° Aniversario de la sanción de la Constitución de la Ciudad Autónoma de Buenos Aires"

Hoja Adicional de Firmas
Plano

Número: PLANO-2026-23204710-GCABA-SSPO

Buenos Aires, Domingo 17 de Mayo de 2026

Referencia: LF-ES-CON-ARQ-PL-017-02_1

El documento fue importado por el sistema GEDO con un total de 1 pagina/s.

Digitally signed by Comunicaciones Oficiales
Date: 2026.05.17 16:46:53 -03:00

Facundo Lombardo
Subsecretario
SUBSECRETARIA PROYECTOS Y OBRAS
MINISTERIO DE MOVILIDAD E INFRAESTRUCTURA

Digitally signed by Comunicaciones Oficiales
Date: 2026.05.17 16:46:54 -03:00