
SANITARIOS HOMBRES NIVEL +15.32

1 : 25

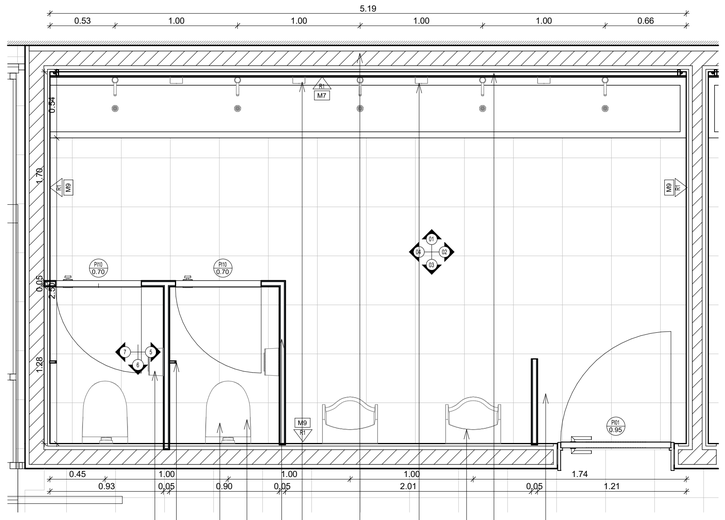

Ac-12: Dispenser de papel higienico de acero inoxidable marca Inelec.

Ac-08: Percha Arizona, marca FV.

Sa-02: Asiento y tapa para inodoro Marina, color blanco, marca Ferrum. Código: THXUS-B.

Sa-01: Inodoro de colgar modelo Marina, color blanco, marca Ferrum. Código: IHPJ-B.
Con refuerzo y ménsula marca Ferrum, código: VPSAC.

Placas con bastidor de MDF de 45 x 22mm, rellenas con nido de abeja celulósico impermeable, con tapas de MDF de 4mm.

Tapacantos con perfil de aluminio anodizadoMVT194® de 45mm x 5mm.
Bisagras de aluminio anodizado natural.
Herraje de cierre tipo libre-ocupado acerado.
Zócalos de acero inoxidable y travesaño de aluminio con o sin vinculación a cielorraso.

R1: Piso y pared. Placa granítica tipo Terrazo vibrada, prensada y pulida para terminación e impermeabilización en obra. Medida nominal 397mmx397mmx18mm (tolerancia +/. 1 mm). Canto Rectificado. Absorción de agua 5.7 IRAM. Color de masa, color, granulometría y porcentaje de piedra a definir sobre muestras.

Sa-04: Lavatorio y mesada de polimetil-metacrilato de Dupont linea Corian o similar color blanco en una sola pieza con leve curvatura para generar pendiente de desague, largo variable según núcleo sanitario

Sa-03: Mingitorio mural corto, color blanco, marca Ferrum. Código: MMCJ-B.


Ac-13: Espejo sobre bastidor metálico con garganta superior para luminaria lineal a definir por la D.O.

Gr-01: Canilla automática modelo Ecomatic para lavatorio, marca FV.

Ac- 09: Dispenser de jabon de acero inox marca Inelec.

SANITARIOS HOMBRES CIELORRASO - NIVEL +15.32

1 : 25

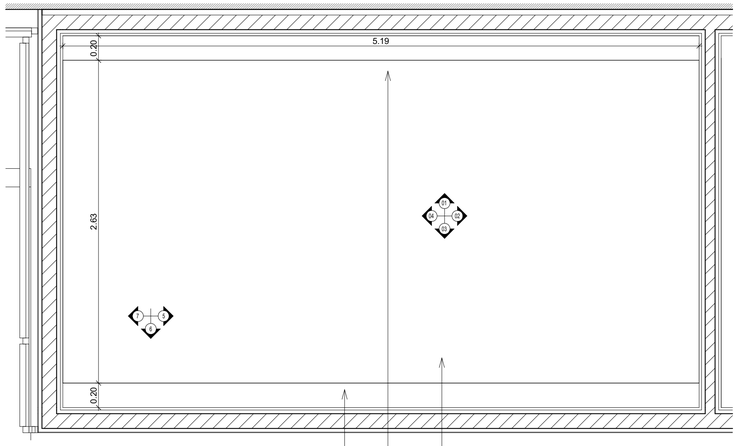


Garganta con artefacto de iluminación led lineal en cielorraso suspendido según plano de iluminación.

Artefacto de iluminación led lineal embutido en cielorraso suspendido.

C1. Cielorraso suspendido de placas de rocas de yeso resistente a la humedad junta tomada compuesto por placa de roca de yeso de 12.5 mm + estructura metálica de chapa galvanizada N24 compuesta por soleras de 70 mm y montantes de 69 mm separados cada 40 cm, con resfuerzo para artefacto de iluminación..

Detalle Lavatorio

1 : 10

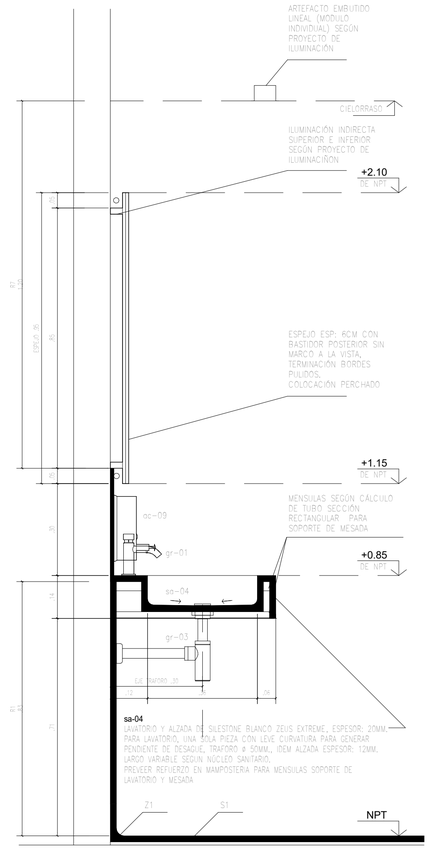

REFERENCIAS PARA DETALLES DE BAÑOS Y VESTUARIOS

SANITARIOS


Sa-01: Inodoro de colgar modelo Marina, color blanco, marca Ferrum. Código: IHPJ-B. Con refuerzo y ménsula marca Ferrum, código: VPSAC.
Sa-02: Asiento y tapa para inodoro Marina, color blanco, marca Ferrum. Código: THXUS-B.
Sa-03: Mingitorio mural corto, color blanco, marca Ferrum. Código: MMCJ-B.
Sa-04: Lavatorio y mesada de polimetil-metacrilato de Dupont línea Corian o similar color blanco en una sola pieza con leve curvatura para generar pendiente de desague. largo variable según núcleo sanitario ver detalle.
Sa-05: Lavatorio con sistema de soporte fijo, modelo Bari, marca Ferrum línea espacio. Código: LET1F-B.

GRIFERÍAS

Gr-01: Canilla automática modelo Ecomatic para lavatorio, marca FV. Código: 0372.
Gr-02: Desagüe "soft touch" para lavatorio marca FV, código: 0248.01
Gr-03: Descarga con sifón para lavatorio minimalista, marca FV código: 0242.01
Gr-04: Canilla automática para mesada para personas con movilidad reducida, marca FV. Código: 0361.03A
Gr-05: Llaves de paso tipo esférica, de paso total, con esfera de acero inoxidable y asientos de teflón, con volante modelo Oregon incorporado marca FV.
Gr-06: Válvula automática Ecomatic para mingitorio marca FV. Código: 0362.01
Gr-07: Tapa tecla para válvula de descarga, marca FV Código: 0368.04 y válvula para descarga de inodoros, marca FV Código 0368.01.
Gr-08: Juego para ducha, modelo Arizona Plus marca FV. Código: 0109/B1P.

ACCESORIOS :

Ac-01: Barral rebatible y portarollo Espacio, marca Ferrum. Código:
Ac-02: Barral fijo espacio Bari 65cm, marca Ferrum. Código: VEFR6-B.
Ac-03: Barral rebatible Espacio Bari 60 cm, marca Ferrum. Código: VTEB-B
Ac-08: Percha Arizona, marca FV. Código: 0166/B1
Ac-09: Dispenser de jabon de acero inox marca Inelec. Código: 15016562.
Ac-10: Dispenser de toallas intercaladas y cesto 5l de acero inoxidable de empotrar marca Inelec código: 2601229-10.
Ac-11: Cesto de residuos de acero inoxidable de colgar marca Inelec capacidad 5.7lt. Código: 1501359.
Ac-12: Dispenser de papel higienico de acero inoxidable marca Inelec. Código: 1501AR-800
Ac-13: Espejo sobre bastidor metálico con garganta superior para luminaria lineal a definir por la D.O.

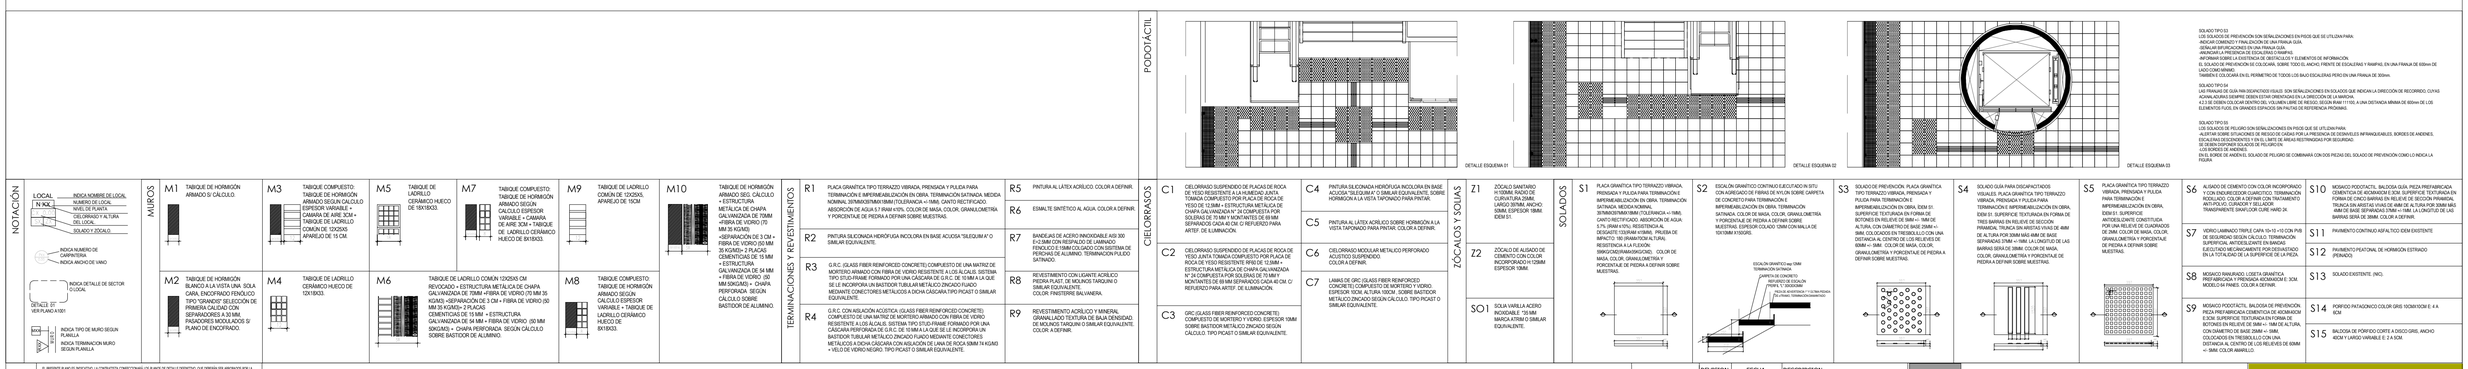

NOTAS:

EL PRESENTE PLANO ES INDICATIVO. LA CONTRATISTA CONFECCIONARÁ LOS PLANOS DE DETALLE DEFINITIVO, QUE DEBERÁN SER APROBADOS POR LA D.O.(M.O.) Y LA DIRECCIÓN DE OBRA. EL PLANO PRESENTADO POR LA CONTRATISTA DEBERÁ SER DE TODO DE ACUERDO CON LA NORMATIVA VIGENTE. TODAS LAS MEDIDAS Y NIVELES SE VERIFICARÁN EN OBRA POR EL CONTRATISTA.
TODOS LOS DETALLES CONSTRUCTIVOS DEBERÁN COORDINARSE Y COMPATIBILIZARSE EN OBRA.

PLANO NO APTO PARA CONSTRUCCIÓN

MODIFICACIONES:

REVISION	FECHA	DESCRIPCION
00	20/11/2025	Emision para Licitacion
01	10/04/2026	Emision para Licitacion

Gobierno de la Ciudad de Buenos Aires

MINISTERIO DE INFRAESTRUCTURA
SUBSECRETARIA DE PROYECTOS Y OBRAS
DIRECCION GENERAL DE PROYECTOS

DGPRO

Obra: LÍNEA F
Plano ESTACION CONSTITUCION- DETALLE DE SANITARIOS 01 de 02
Fecha :10/04/2026 | Eq. de Proyecto: UPU - ATEC - IATASA | Dibujó: JS | Revisó: GV | Escala: Como se indica

PLANO-2026-23204737-GCABA-DGPRO
LF-ES-CON-ARQ-PL-017-01-R01
Nº: 017-01

G O B I E R N O DE LA C I U D A D DE B U E N O S A I R E S

"2026 - Año del 30° Aniversario de la sanción de la Constitución de la Ciudad Autónoma de Buenos Aires"

Hoja Adicional de Firmas
Plano

Número: PLANO-2026-23204737-GCABA-SSPO

Buenos Aires, Domingo 17 de Mayo de 2026

Referencia: LF-ES-CON-ARQ-PL-017-01

El documento fue importado por el sistema GEDO con un total de 1 pagina/s.

Digitally signed by Comunicaciones Oficiales
Date: 2026.05.17 16:47:44 -03:00

Facundo Lombardo
Subsecretario
SUBSECRETARIA PROYECTOS Y OBRAS
MINISTERIO DE MOVILIDAD E INFRAESTRUCTURA

Digitally signed by Comunicaciones Oficiales
Date: 2026.05.17 16:47:46 -03:00