


CORTE A01
1 : 500

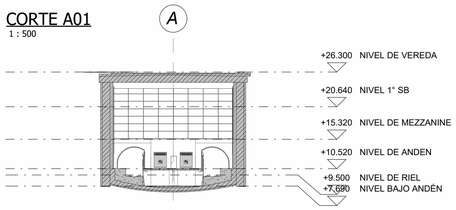


CORTE A02
1 : 500

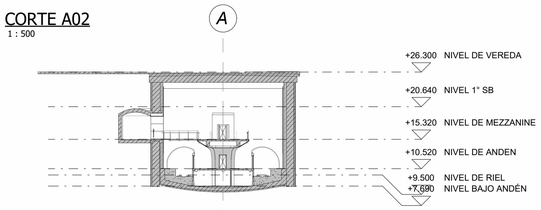


CORTE A03
1 : 500

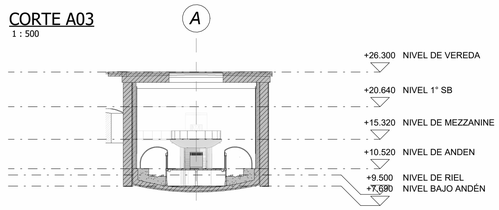


CORTE A04
1 : 500

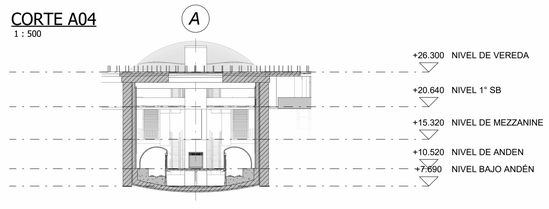


CORTE A05
1 : 500

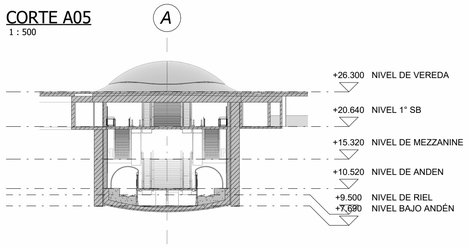


CORTE A06
1 : 500

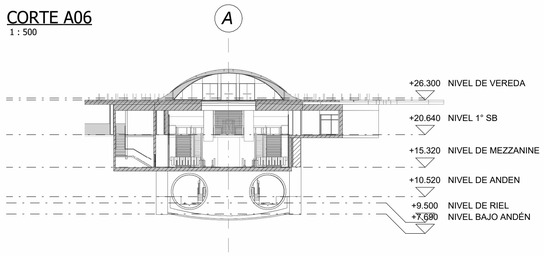


CORTE A07
1 : 500

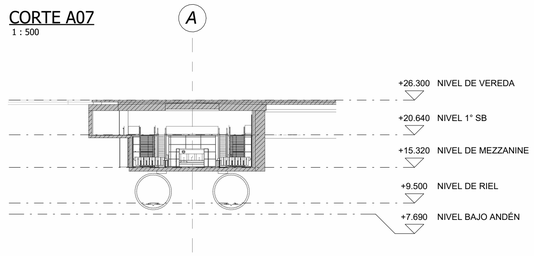


CORTE A08
1 : 500

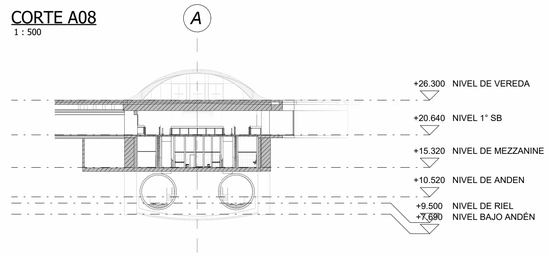


CORTE A09
1 : 500

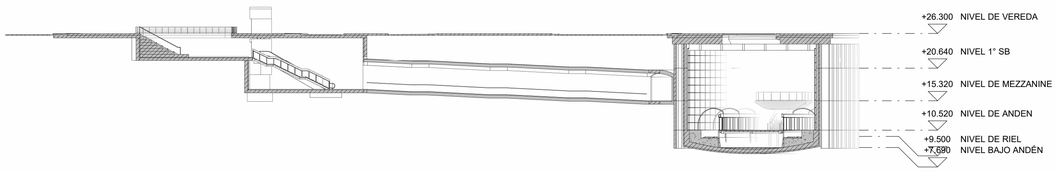


CORTE A10 1/500
1 : 500

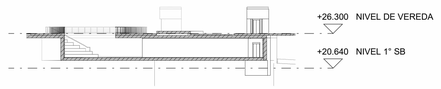


CORTE B01 1/500
1 : 500

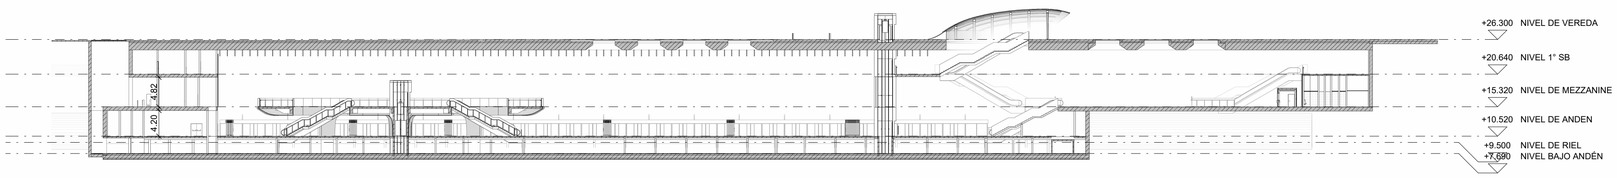


CORTE B02 1/500
1 : 500

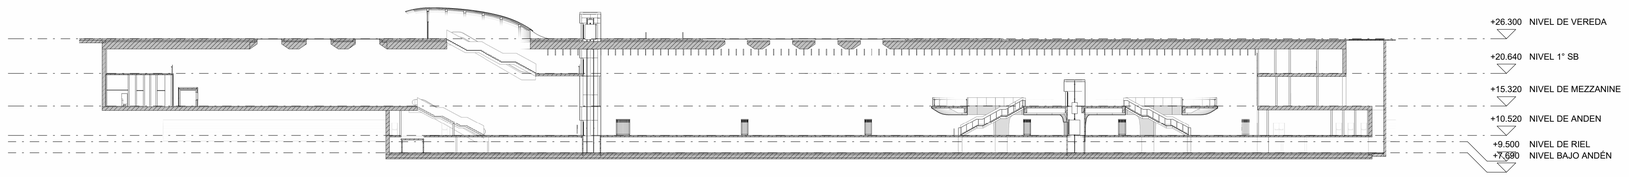

CORTE B03 1/500
1 : 500

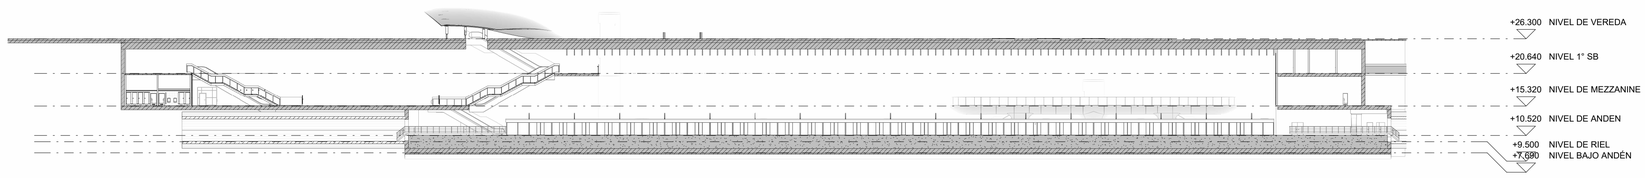

CORTE B04 1/500
1 : 500

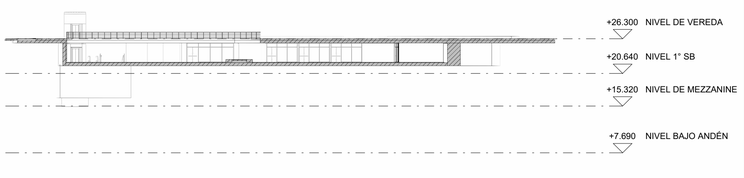

NOTAS: EL PRESENTE PLANO ES INDICATIVO. LA CONTRATISTA CONFECCIONARÁ LOS PLANOS DE DETALLE CORRECTIVOS, QUE DEBERÁN SER APROBADOS POR LA D.G.DGPRO Y LA INSPECCIÓN DE OBRA. EL PLANO PRESENTADO POR LA CONTRATISTA ESTARÁ EN BASE AL TODO EL ACUERDO CON LA AGENCIA DE ACENTO. TODAS LAS MEDIDAS Y NIVELES SE VERIFICARÁN EN OBRA POR EL CONTRATISTA.
TODOS LOS DETALLES CONSTRUCTIVOS SERÁN COORDINADOS Y CONFIRMADOS EN OBRA.

PLANO NO APTO PARA CONSTRUCCIÓN

MODIFICACIONES:	REVISION	FECHA	DESCRIPCION
	00	20/11/2025	Emision para Licitacion
	01	10/04/2026	Emision para Licitacion

Gobierno de la Ciudad de Buenos Aires

MINISTERIO DE INFRAESTRUCTURA
SUBSECRETARIA DE PROYECTOS Y OBRAS
DIRECCION GENERAL DE PROYECTOS

DGPRO

Obra: LÍNEA F					Plano Nº: A007
Plano ESTACION CONSTITUCION- CORTES GENERALES				LF-ES-CON-ARQ-PL-007-R01	
Fecha :10/04/2026	Eq. de Proyecto: UPU - ATEC - IATASA	Dibujó: J.S.	Revisó: G.V.	Escala: 1 : 500	

G O B I E R N O DE LA C I U D A D DE B U E N O S A I R E S

"2026 - Año del 30° Aniversario de la sanción de la Constitución de la Ciudad Autónoma de Buenos Aires"

Hoja Adicional de Firmas
Plano

Número: PLANO-2026-23246556-GCABA-SSPO

Buenos Aires, Lunes 18 de Mayo de 2026

Referencia: LF-ES-CON-ARQ-PL-007_1

El documento fue importado por el sistema GEDO con un total de 1 pagina/s.

Digitally signed by Comunicaciones Oficiales
Date: 2026.05.18 09:31:23 -03:00

Facundo Lombardo
Subsecretario
SUBSECRETARIA PROYECTOS Y OBRAS
MINISTERIO DE MOVILIDAD E INFRAESTRUCTURA

Digitally signed by Comunicaciones Oficiales
Date: 2026.05.18 09:31:22 -03:00