


CORTE TRANSVERSAL A01
1 : 500

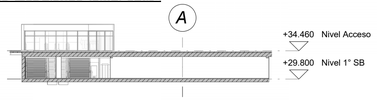


CORTE TRANSVERSAL A02
1 : 500

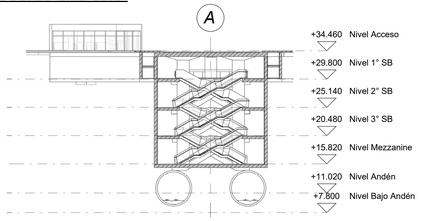


CORTE TRANSVERSAL A03
1 : 500

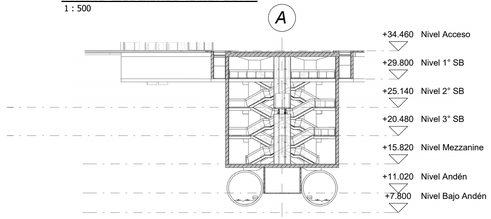


CORTE TRANSVERSAL A04
1 : 500

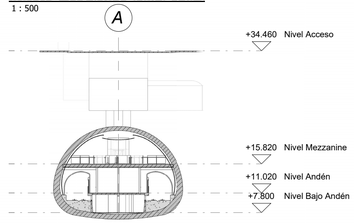


CORTE TRANSVERSAL A05
1 : 500

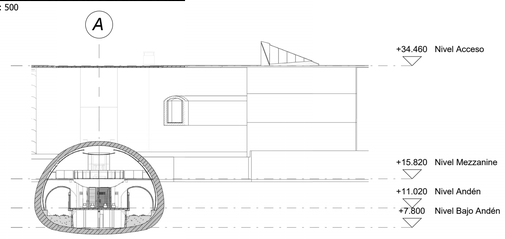


CORTE TRANSVERSAL A06
1 : 500

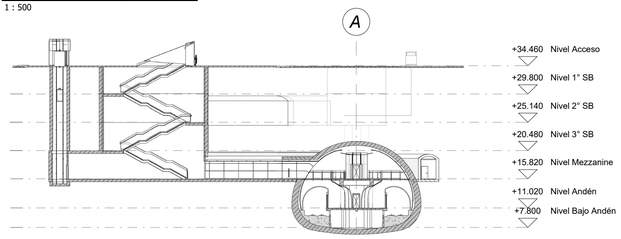


CORTE TRANSVERSAL A07
1 : 500

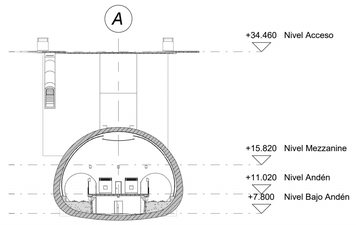


CORTE LONGITUDINAL B01
1 : 500

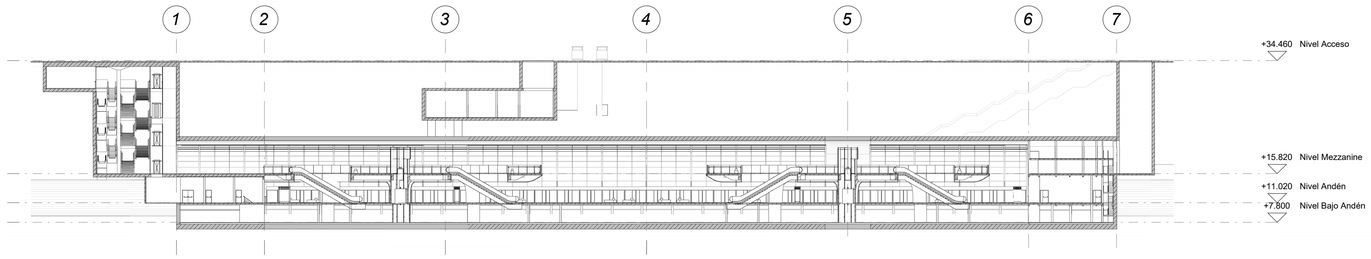


CORTE LONGITUDINAL B04
1 : 500

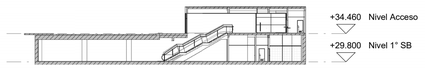


CORTE LONGITUDINAL B02
1 : 500

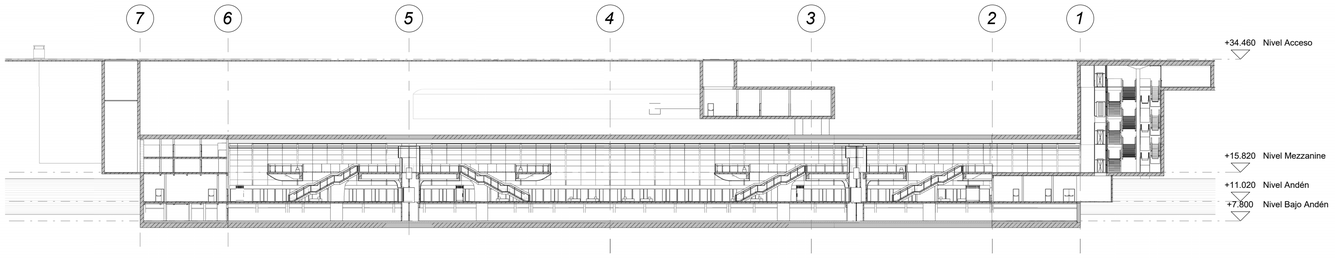

CORTE LONGITUDINAL B05
1 : 500

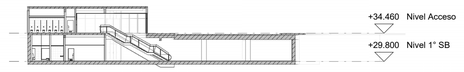

CORTE LONGITUDINAL B03
1 : 500

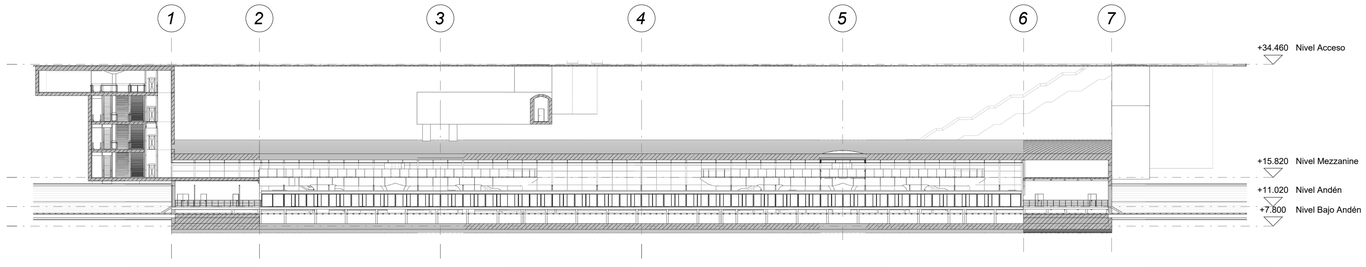

NOTAS:

EL PRESENTE PLANO ES INDICATIVO. LA CONTRATISTA CORROBORARÁ LOS PLANOS DE DETALLE DEFINITIVO, QUE DEBERÁN SER APROBADOS POR LA D.G.U.PRO Y LA DIRECCIÓN DE OBRA. EL PLANO PRESENTADO POR LA CONTRATISTA DEBERÁ EN TODO SE AJUSTARSE CON LA NORMATIVA VIGENTE. TODAS LAS MEDIDAS Y NIVELES SE VERIFICARÁN EN OBRA POR EL CONTRATISTA.
TODOS LOS DETALLES CONSTRUCTIVOS SERÁN CONSENSUADOS Y COMPATIBILIZADOS EN OBRA.

PLANO NO APTO PARA CONSTRUCCIÓN

MODIFICACIONES:	REVISION	FECHA	DESCRIPCION
	00	30/01/2026	EMISION PARA LICITACION
	01	10/04/2026	EMISION PARA LICITACION

Gobierno de la Ciudad de Buenos Aires

MINISTERIO DE INFRAESTRUCTURA
SUBSECRETARIA DE PROYECTOS Y OBRAS
DIRECCION GENERAL DE PROYECTOS

DGPRO

Obra: LÍNEA F

Plano ESTACION CORRIENTES - CORTES GENERALES | LF-ES-CRR-ARQ-PL-007-R01

Fecha :10/04/2026 | Eq. de Proyecto: UPU - ATEC - IATASA | Dibujó: X | Revisó: G.V. | Escala: 1 : 500

Plano A007

PLANO-2026-18218757-GCABA-SSPO

G O B I E R N O DE LA C I U D A D DE B U E N O S A I R E S

"2026 - Año del 30° Aniversario de la sanción de la Constitución de la Ciudad Autónoma de Buenos Aires"

Hoja Adicional de Firmas
Plano

Número: PLANO-2026-18218757-GCABA-SSPO

Buenos Aires, Viernes 17 de Abril de 2026

Referencia: LF-ES-CRR-ARQ-PL-007_1

El documento fue importado por el sistema GEDO con un total de 1 pagina/s.

Digitally signed by Comunicaciones Oficiales
Date: 2026.04.17 12:19:02 -03:00

Facundo Lombardo
Subsecretario
SUBSECRETARIA PROYECTOS Y OBRAS
MINISTERIO DE MOVILIDAD E INFRAESTRUCTURA

Digitally signed by Comunicaciones Oficiales
Date: 2026.04.17 12:19:02 -03:00