


F60

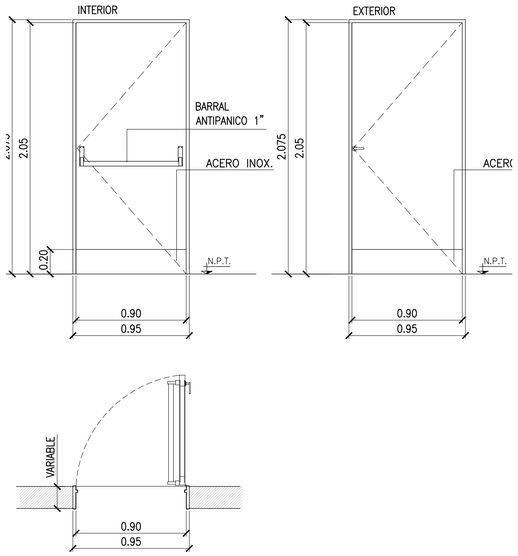


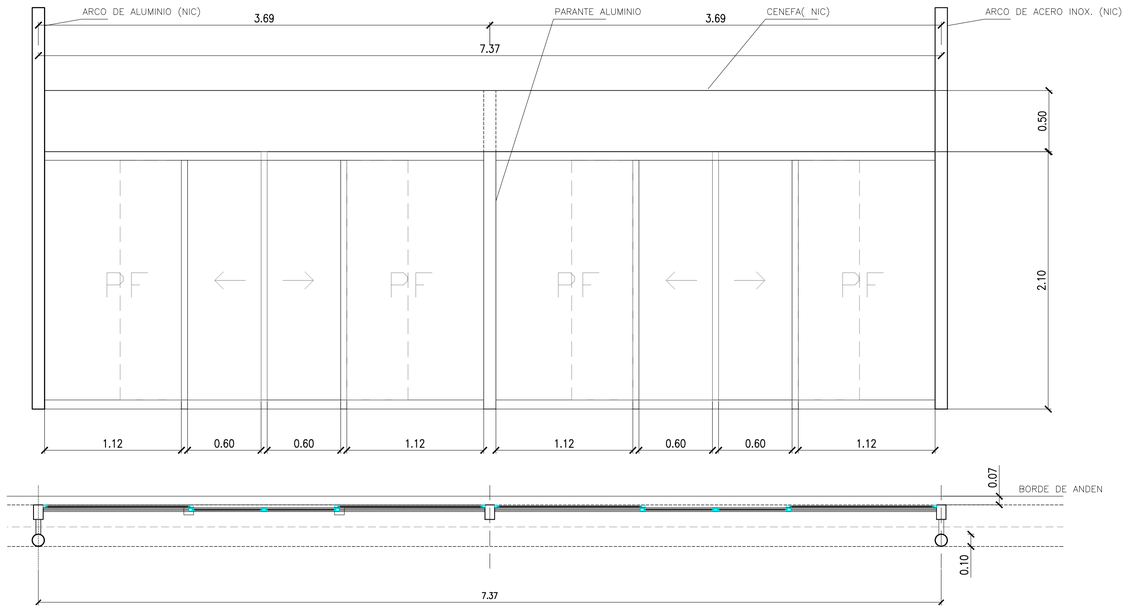


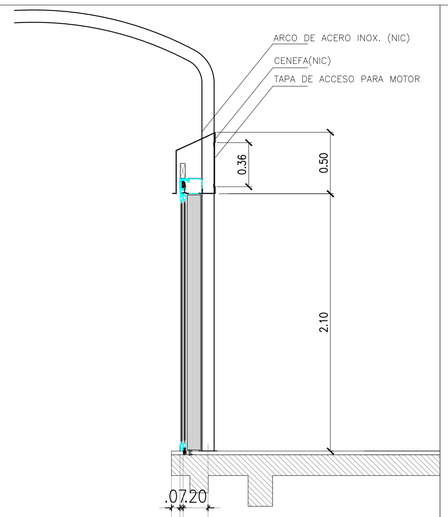

UBICACION	SALAS Y LOCALES TECNICOS/ ESCALERAS	P9	0.95
TIPO	CANT. S/COMPUTO | DER. VER PLANTAS | IZQ. VER PLANTAS		
MARCO	CHAPA DOBLADA BWG N°18 PINTURA 2 MANOS DE ANTIOXIDO+2 MANOS DE SINT.COLOR A DEF.		
HOJAS	DOBLE CHAPA ESP. 45mm BWG 18 CON REFUERZOS INTERNOS –LANA MINERAL 60KG/M3 O MATERIAL APROBADO – PINT. 2 MANOS ANTIOXIDO+ 2 MANOS ESMALTE SINTETICO A DEFINIR		
HERRAJES	BISAGRAS REFORZADAS A MUNICION ,CERRADURA DE EMBUTIR DE SEGURIDAD ACYTRA CON FRENTE DE BRONCE PLATIL. BARRAL ANTIPANICO 1" CIERRE DOBLE CONTACTO CON BURLETE INTUMECENTE CIERRE PUERTA AEREO		
OBSERVACIONES	ZOCALO AC° INOX° H:20cm.		

UBICACION	NIVEL ANDEN	P9	7.37
TIPO	CANT. S/COMPUTO | DER. VER PLANTAS | IZQ. VER PLANTAS		
MARCO			
HOJAS	Hoja de carpinteria Estanqueidad E20 Movil y Fija / Cristal laminado incoloro 4+4 mm con bordes estancos / Alto libre: 2100 mm / Ancho HM: 640 mm / Ancho HF: 1120 mm Acabado de perfileria anodizado natural		
HERRAJES	Cerrojo automatico / Fotocelulas de seguridad / Guia de seguridad embutida en piso		
MOTOR	Sistema de apertura central de serie pesada Visio 125 Manusa / Doble motor Inverter, velocidad maxima 2 m/s. /Largo motor: 3440 mm / Paso libre: 1200 mm / Ancho: 180 mm / Alto: 125 mm		
OBSERVACIONES			

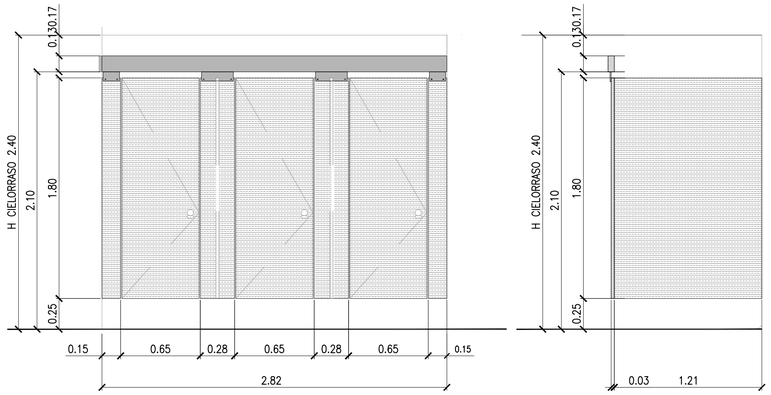

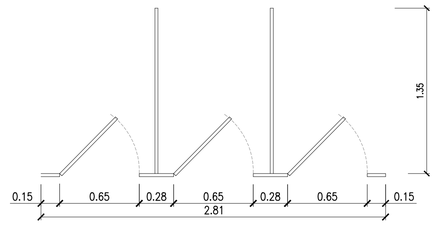

UBICACION	EN RETRETES	P10	2.82
TIPO	CANT. S/COMPUTO | DER. VER PLANTAS | IZQ. VER PLANTAS		
MARCO	DIVISORES, PUERTAS Y FRENTE REALIZADO EN PLACA SIMPLE DE MELAMINA SOBRE MDF 25MM CON CANTOS DE ABS 2MM		
HOJAS	PUERTAS MONTADAS EN LINA DE FRENTE SUSPENDIDOS DE UNA VIGA ESTRUCTURAL EN PLACA SIMPLE DE MELAMINA SOBRE MDF 25MM CON CANTOS ABS 2MM		
HERRAJES	VIGA DE REFUERZO SUPERIOR COLOCADO A LA VISTA REVESTIDO EN ACERO INOXIDABLE. PASADOR CON INDICADOR LIBRE/OCUPADO DE A. I. Y FUNCION DE ACCESO EN CASO DE EMERGENCIA		
OBSERVACIONES			

NOTAS: EL PRESENTE PLANO ES INDICATIVO. LA CONTRATISTA CORROBORARÁ LOS PLANOS DE DETALLE DISPONIBLES, QUE DEBERÁN SER APROBADOS POR LA D.G.LIM.Y P. Y LA SUPERVISIÓN DE OBRA. EL PLANO PRESENTADO POR LA CONTRATISTA DEBERÁ EN SU TODO AL ACORDE CON LA NORMATIVA VIGENTE. TODAS LAS MEDIDAS Y NIVELES SE VERIFICARÁN EN OBRA POR EL CONTRATISTA. TODOS LOS DETALLES CONSTRUCTIVOS SERÁN COORDINADOS Y COMPATIBILIZADOS EN OBRA.

PLANO NO APTO PARA CONSTRUCCIÓN

MODIFICACIONES:

REVISION	FECHA	DESCRIPCION
00	30-01-2026	EMISIÓN PARA LICITACIÓN
01	10-04-2026	EMISIÓN PARA LICITACIÓN

Gobierno de la Ciudad Buenos Aires

MINISTERIO DE INFRAESTRUCTURA
SUBSECRETARIA DE PROYECTOS Y OBRAS
DIRECCION GENERAL DE PROYECTOS

DGPRO

Obra: LÍNEA F
PLANO-2026-18236819-GCABA-SSPO
Plano Estación Corrientes- Planilla de Carpinterías 02 de 02
LF-ES-CRR-ARQ-PL-026-02-R01
Fecha :10/04/2026 | Eq. de Proyecto: UPU - ATEC - IATASA | Dibujó: JS | Revisó: GV | Escala: 1:25

Nº: A026-02

G O B I E R N O DE LA C I U D A D DE B U E N O S A I R E S

"2026 - Año del 30° Aniversario de la sanción de la Constitución de la Ciudad Autónoma de Buenos Aires"

Hoja Adicional de Firmas
Plano

Número: PLANO-2026-18236819-GCABA-SSPO

Buenos Aires, Viernes 17 de Abril de 2026

Referencia: LF-ES-CRR-ARQ-PL-026-02_1

El documento fue importado por el sistema GEDO con un total de 1 pagina/s.

Digitally signed by Comunicaciones Oficiales
Date: 2026.04.17 13:03:32 -03:00

Facundo Lombardo
Subsecretario
SUBSECRETARIA PROYECTOS Y OBRAS
MINISTERIO DE MOVILIDAD E INFRAESTRUCTURA

Digitally signed by Comunicaciones Oficiales
Date: 2026.04.17 13:03:34 -03:00