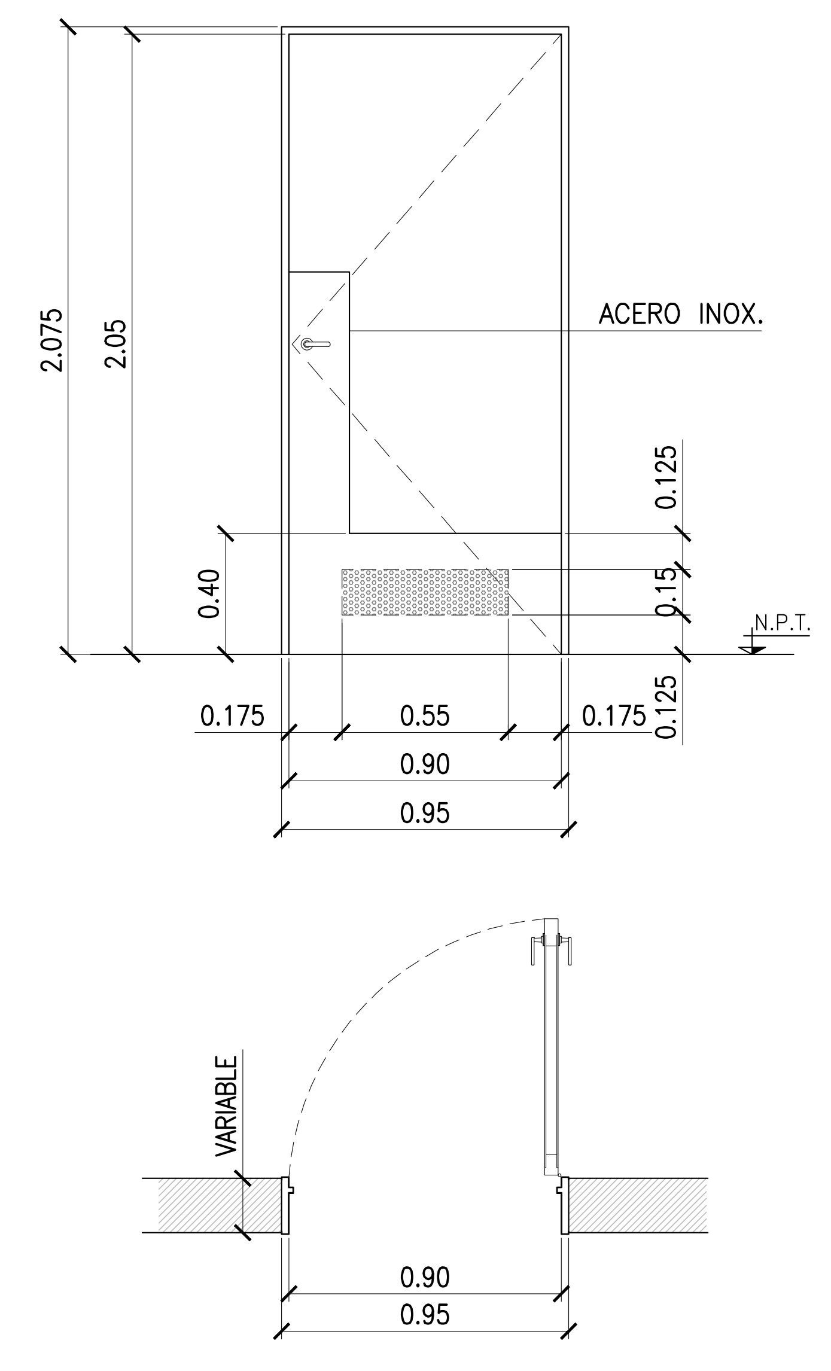

UBICACION	VESTUARIOS, SALAS DE DESCANSO, BOLETERIAS				**P1**
TIPO	CANT. S/COMPUTO	DER. VER PLANTAS	IZQ. VER PLANTAS		
MARCO	CHAPA DOBLADA BWG N°18 PINTURA 2 MANOS DE ANTIOXIDO+2 MANOS DE SINT.COLOR A DEF.				
HOJAS	DOBLE CHAPA ESP. 45mm BWG 18 CON REFUERZOS INTERNOS – LANA MINERAL 60kg/m3 O MATERIAL APROB. – PINT. 2 MANOS ANTIOXIDO+ 2 MANOS ESMALTE SINTETICO A DEFINIR				
HERRAJES	BISAGRAS TIPO POMELA BRONCE PLATIL . PICAPORTE DOBLE BALANCIN BRONCE PLATIL CON PLACA AC° INOX° S/DIBUJO MODELO SANATORIO PESADO. CERRADURA DE SEGURIDAD. CIERRAPUERTA AEREO				**0.95**
OBSERVACIONES	ZOCALO Y GUARDAMANOS A° INOX° h:40cm AMBAS CARAS c/PERFORACION VENTILACION s/DISEÑO				

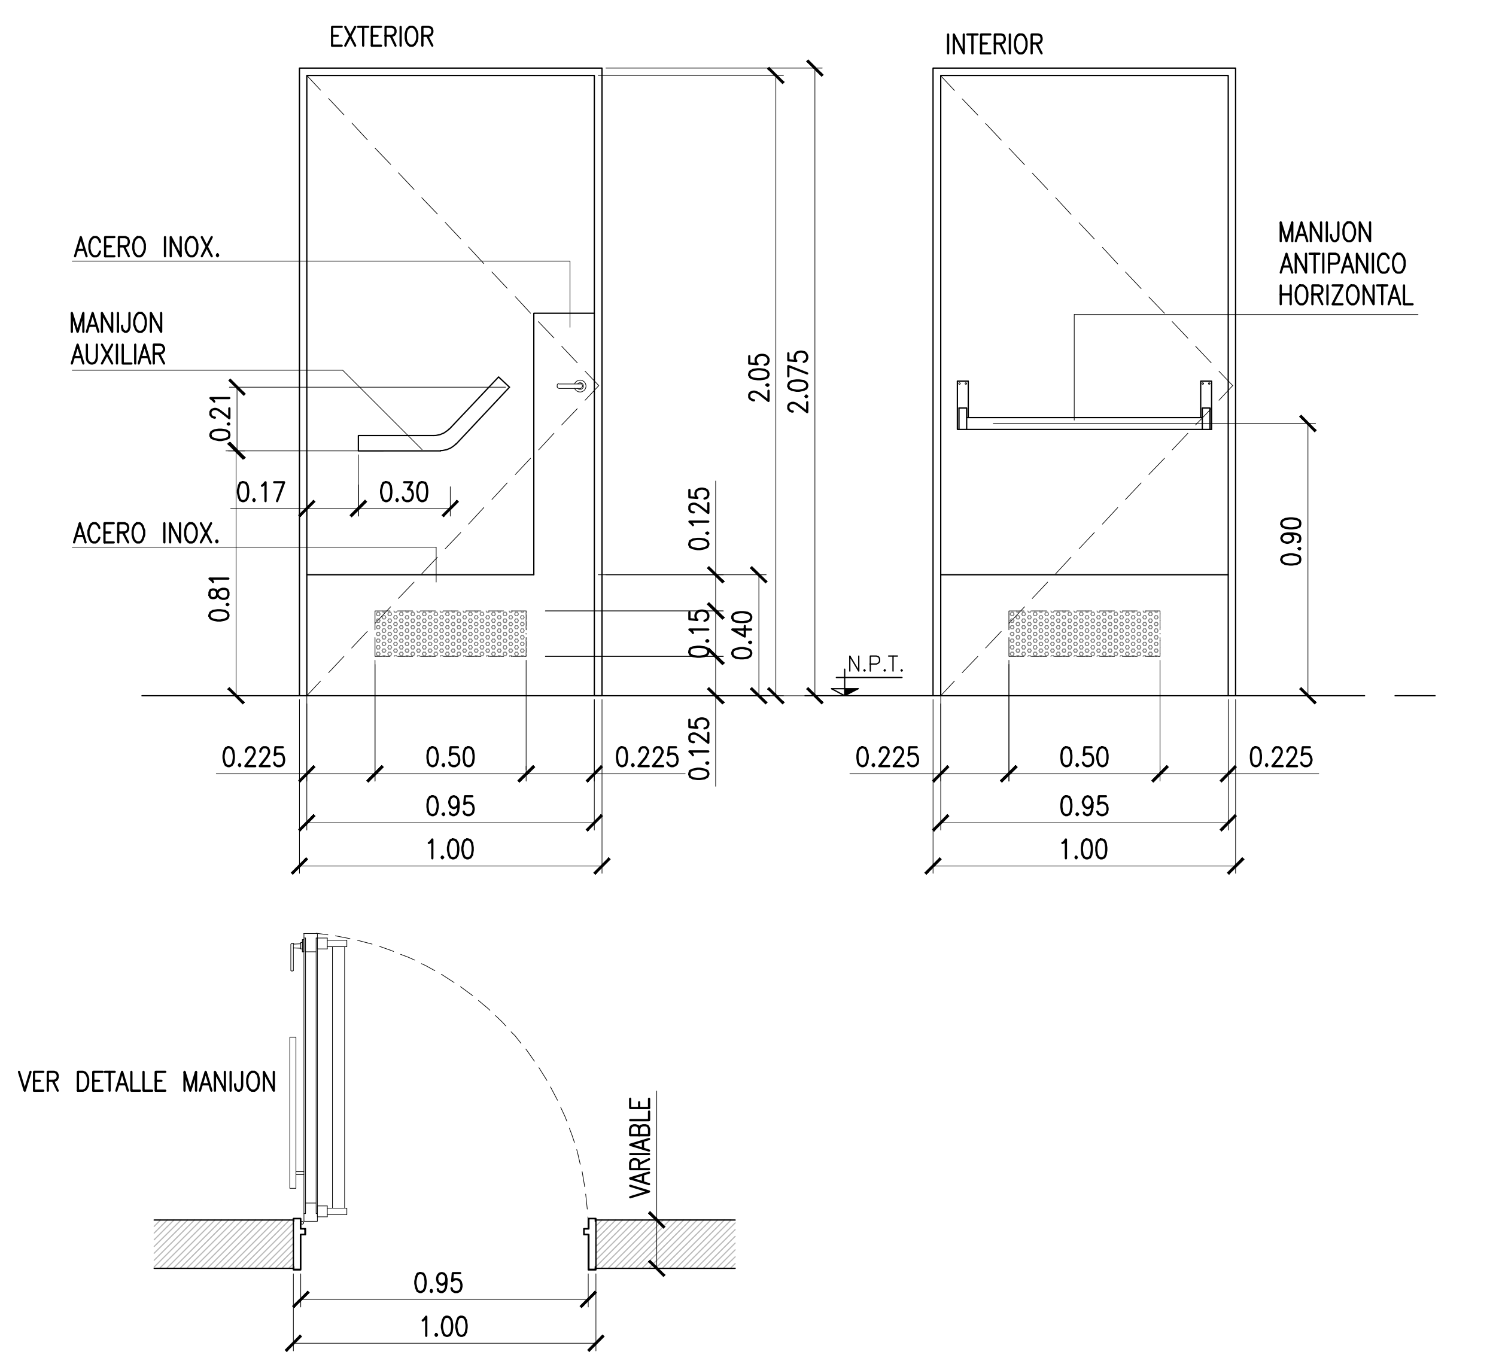

UBICACION	SANITARIOS DISCAPACITADOS				**P2**
TIPO	CANT. S/COMPUTO	DER. VER PLANTAS	IZQ. VER PLANTAS		
MARCO	CHAPA DOBLADA BWG N°18 PINTURA 2 MANOS DE ANTIOXIDO+2 MANOS DE SINT.COLOR A DEF.				
HOJAS	DOBLE CHAPA ESP. 45mm BWG 18 CON REFUERZOS INTERNOS – LANA MINERAL 60kg/m3 O MATERIAL APROB. – PINT. 2 MANOS ANTIOXIDO+ 2 MANOS ESMALTE SINTETICO A DEFINIR				
HERRAJES	BISAGRAS TIPO POMELA BRONCE PLATIL. BARRAL ANTIPANICO ACERO INOX.(DIAMETRO 1") CON ACCESO EXTERIOR CON MANIJA Y LLAVE MARCA JAQUE QUE PERMITE APERTURA AUNQUE ESTE CERRADA CON LLAVE. CIERRAPUERTA AEREO				**1.00**
OBSERVACIONES	ZOCALO Y GUARDAMANOS A° INOX° h:40cm AMBAS CARAS c/PERFORACION VENTILACION s/DISEÑO				

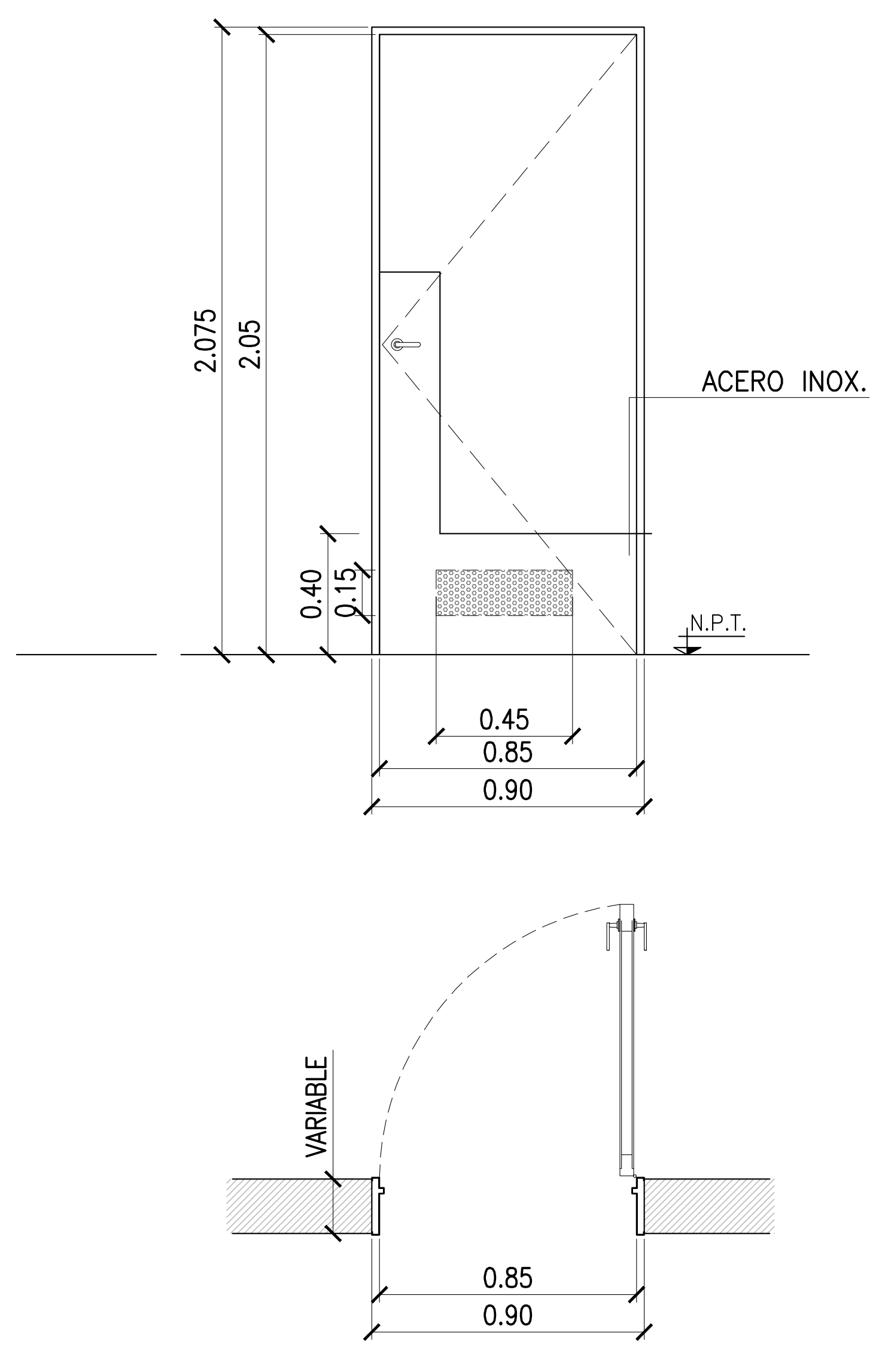

UBICACION	SANITARIOS HOMBRES / MUJERES				**P3**
TIPO	CANT. S/COMPUTO	DER. VER PLANTAS	IZQ. VER PLANTAS		
MARCO	CHAPA DOBLADA BWG N°18 PINTURA 2 MANOS DE ANTIOXIDO+2 MANOS DE SINT.COLOR A DEF.				
HOJAS	DOBLE CHAPA ESP. 45mm BWG 18 CON REFUERZOS INTERNOS INYECTADA CON POLIURETANO PINT. 2 MANOS ANTIOXIDO+ 2 MANOS ESMALTE SINTETICO A DEFINIR				
HERRAJES	BISAGRAS REFORZADAS A MUNICION ,CERRADURA DE EMBUTIR DE SEGURIDAD ACYTRA CON FRENTE DE BRONCE PLATIL. PICAPORTE DOBLE BALANCIN BRONCE PLATIL.				**0.90**
OBSERVACIONES	ZOCALO Y GUARDAMANOS A° INOX° h:40cm AMBAS CARAS c/PERFORACION VENTILACION s/DISEÑO				

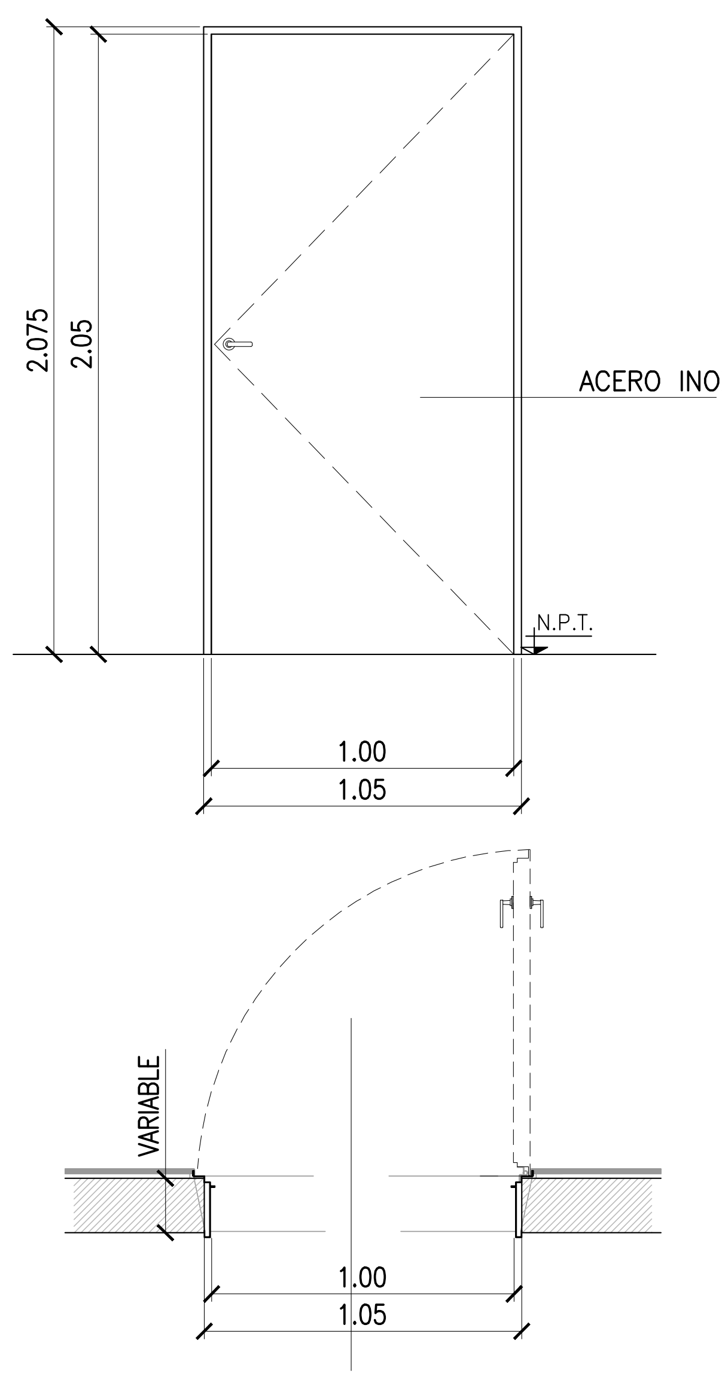

UBICACION	ACCESO SECTORPERSONAL				**P4**
TIPO	CANT. S/COMPUTO	DER. VER PLANTAS	IZQ. VER PLANTAS		
MARCO	CHAPA DOBLADA BWG N°18. EL PLEGADO PERMITIRÁ ALOJAMIENTO OCULTO DE las BISAGRAS.				
HOJAS	DOBLE CHAPA ESP. 45mm BWG 18 CON REFUERZOS INTERNOS – LANA MINERAL 60kg/m3 O MATERIAL APROB. – REVESTIMIENTO DE CHAPA PLEGADA DE ACERO INOXIDABLE AISI 300 ESP. 2.5MM LADO EXTERIOR DE LA HOJA. – 2 MANOS ANTIOXIDO+ 2 MANOS ESMALTE SINTETICO A DEFINIR LADO INTERIOR DE LA HOJA				
HERRAJES	BISAGRAS REFORZADAS A MUNICION ,CERRADURA DE EMBUTIR DE SEGURIDAD ACYTRA CON FRENTE DE BRONCE PLATIL. PICAPORTE DOBLE BALANCIN ACERO INOX. CON BURLETE INTUMECENTE. CIERRA PUERTA AEREO.				**1.05**
OBSERVACIONES	LA HOJA DEBE QUEDAR COPLANAR CON EL REVESTIMIENTO DE ACERO INOXIDABLE DEL HALL.				

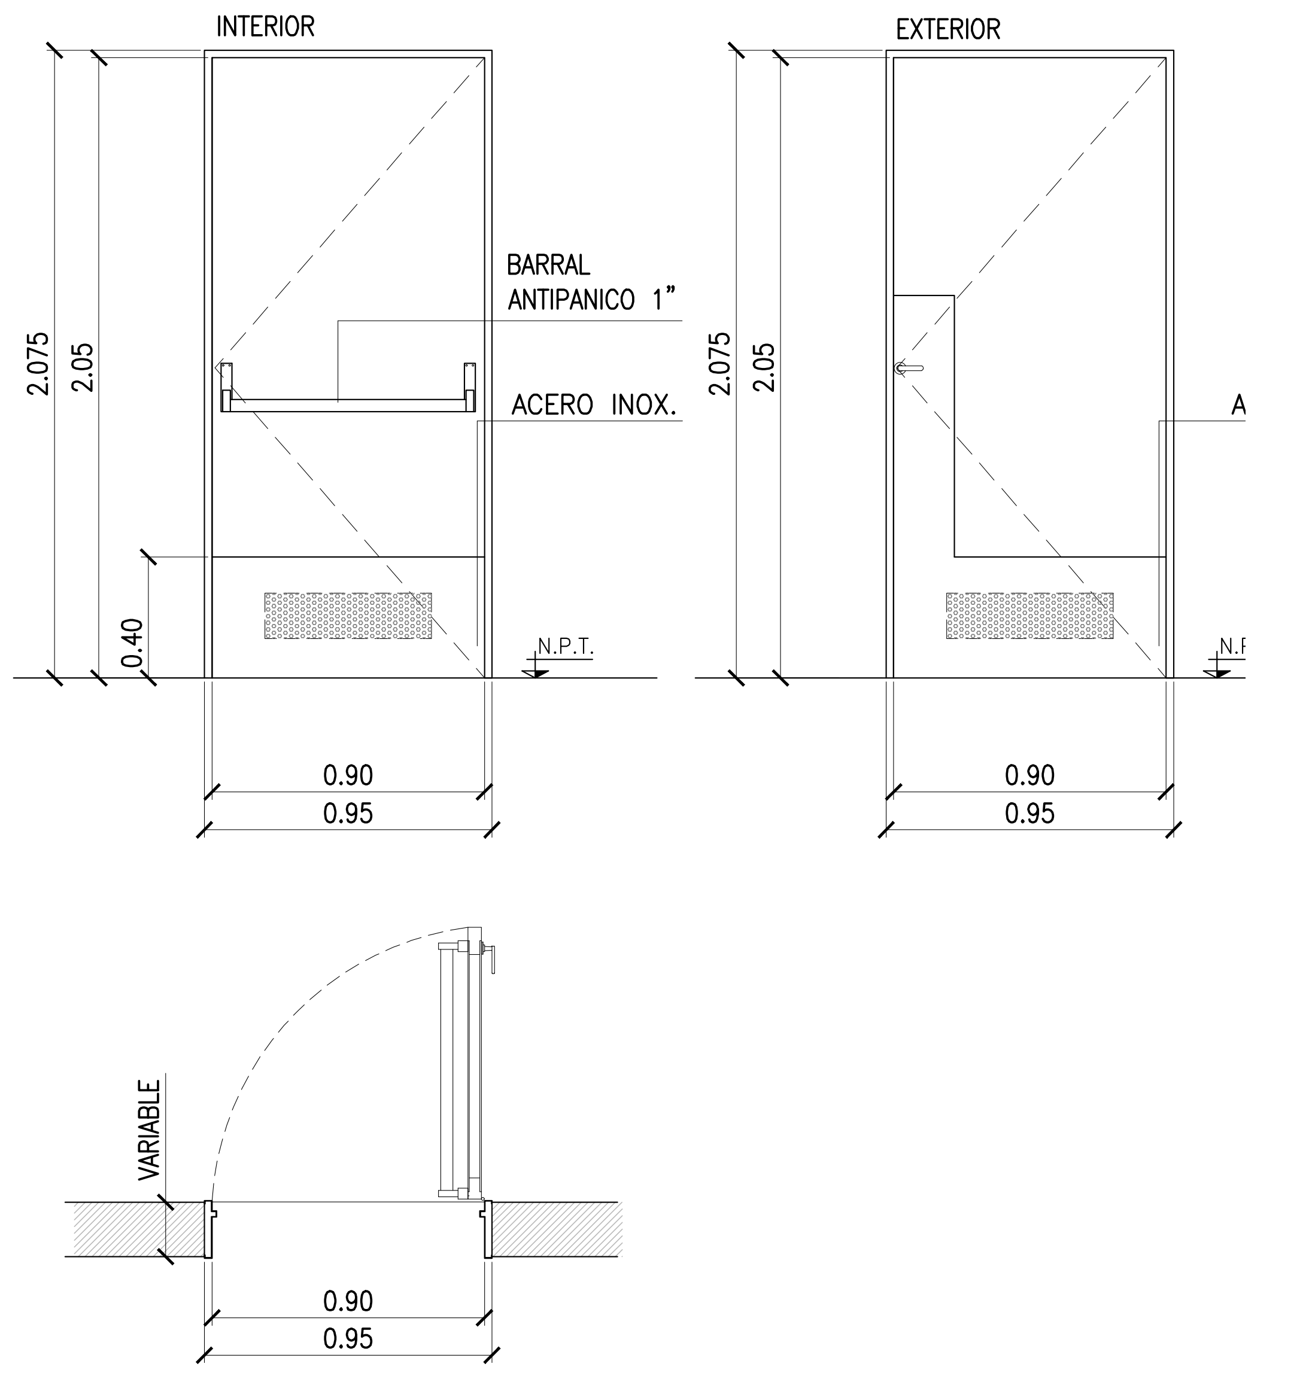

UBICACION	DEPOSITO				**P5**
TIPO	CANT. S/COMPUTO	DER. VER PLANTAS	IZQ. VER PLANTAS		
MARCO	CHAPA DOBLADA BWG N°18 PINTURA 2 MANOS DE ANTIOXIDO+2 MANOS DE SINT.COLOR A DEF.				
HOJAS	DOBLE CHAPA ESP. 45mm BWG 18 CON REFUERZOS INTERNOS –LANA MINERAL 60KG/M3 O MATERIAL APROBADO – PINT. 2 MANOS ANTIOXIDO+ 2 MANOS ESMALTE SINTETICO A DEFINIR				
HERRAJES	BISAGRAS REFORZADAS A MUNICION ,CERRADURA DE EMBUTIR DE SEGURIDAD ACYTRA CON FRENTE DE BRONCE PLATIL. BARRAL ANTIPANICO 1" CIERRE DOBLE CONTACTO CON BURLETE INTUMECENTE CIERRE PUERTA AEREO				**0.95**
OBSERVACIONES	ZOCALO AC° INOX° H:20cm.				

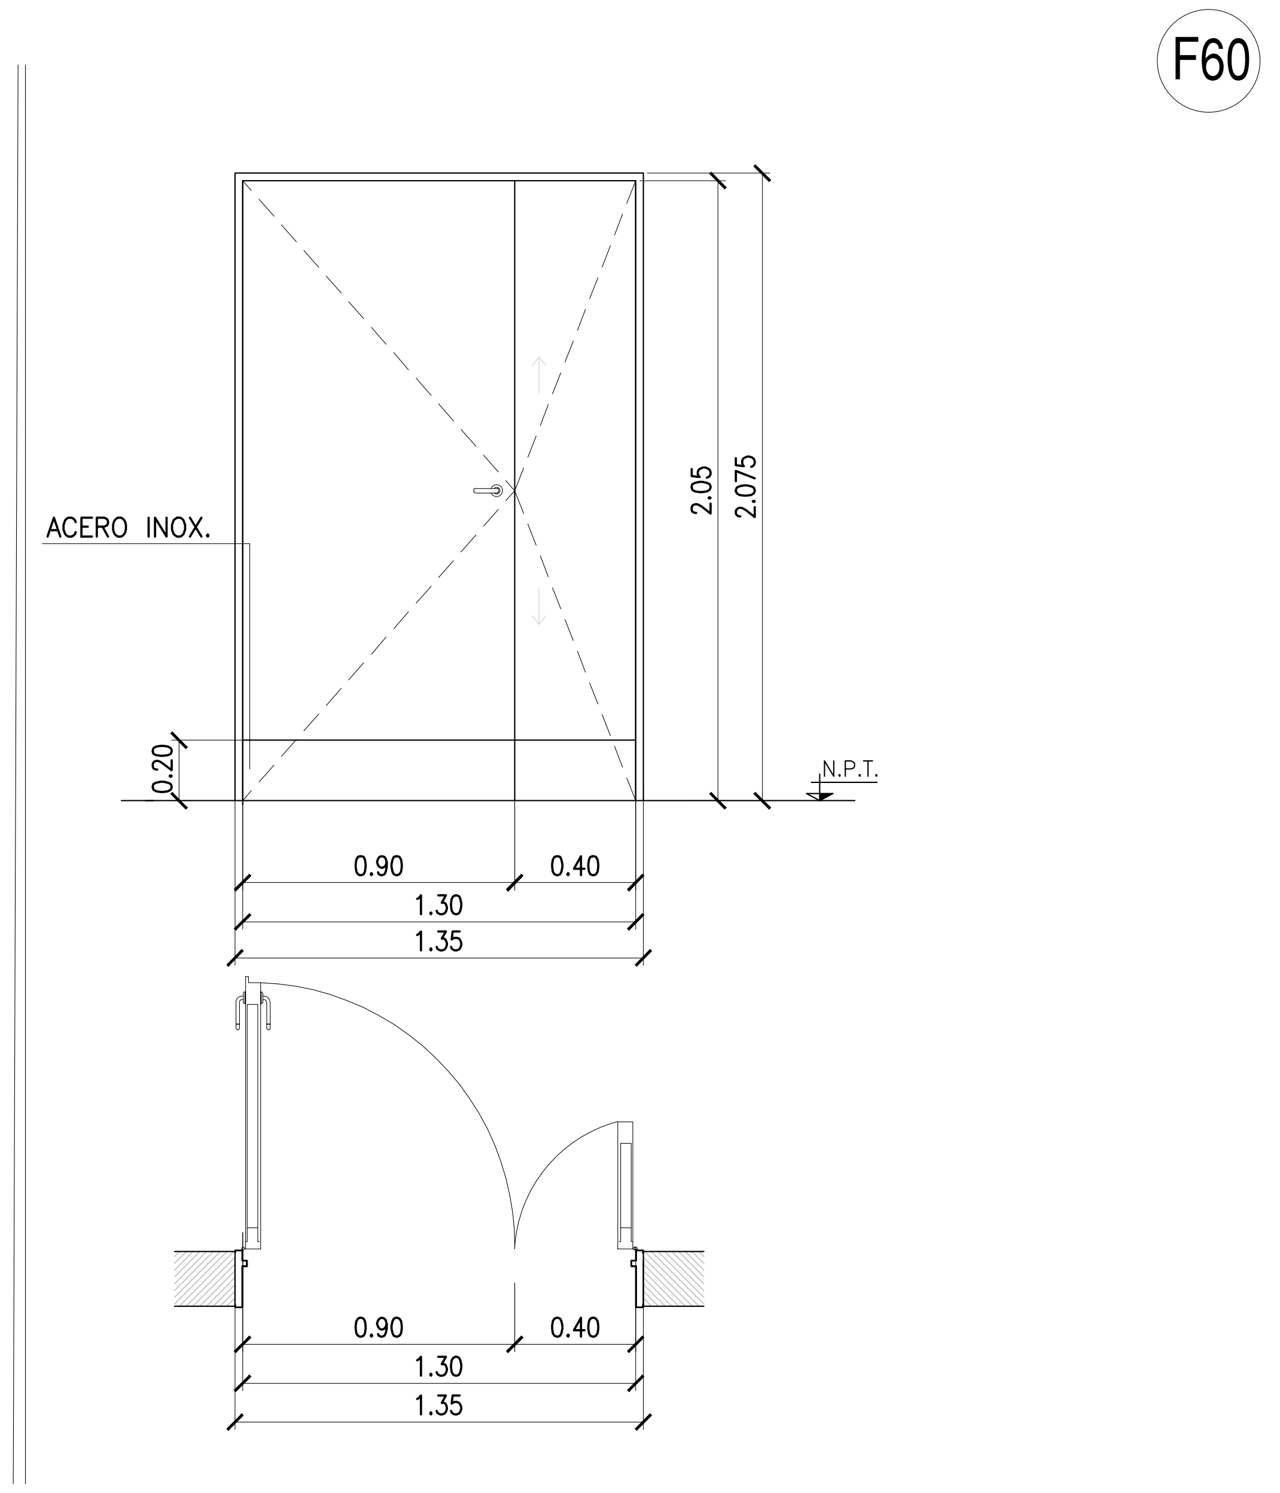

UBICACION	ACCESO A PLENO				**P6**
TIPO	CANT. S/COMPUTO	DER. VER PLANTAS	IZQ. VER PLANTAS		
MARCO	CHAPA DOBLADA BWG N°18 PINTURA 2 MANOS DE ANTIOXIDO+2 MANOS DE SINT.COLOR A DEF.				
HOJAS	DOBLE CHAPA ESP. 45mm BWG 18 CON REFUERZOS INTERNOS – LANA MINERAL 60KG/M3 O MATERIAL APROB – PINT. 2 MANOS ANTIOXIDO+ 2 MANOS ESMALTE SINTETICO A DEFINIR				
HERRAJES	BISAGRAS REFORZADAS A MUNICION ,CERRADURA DE EMBUTIR DE SEGURIDAD ACYTRA CON FRENTE DE BRONCE PLATIL. PICAPORTE DOBLE BALANCIN BRONCE PLATIL. PASADORES DE HIERRO DE APLICAR. CIERRE DOBLE CONTACTO CON BURLETE INTUMECENTE – CIERRE PUERTA AEREO				**1.35**
OBSERVACIONES	ZOCALO AC° INOX° H:20cm.				

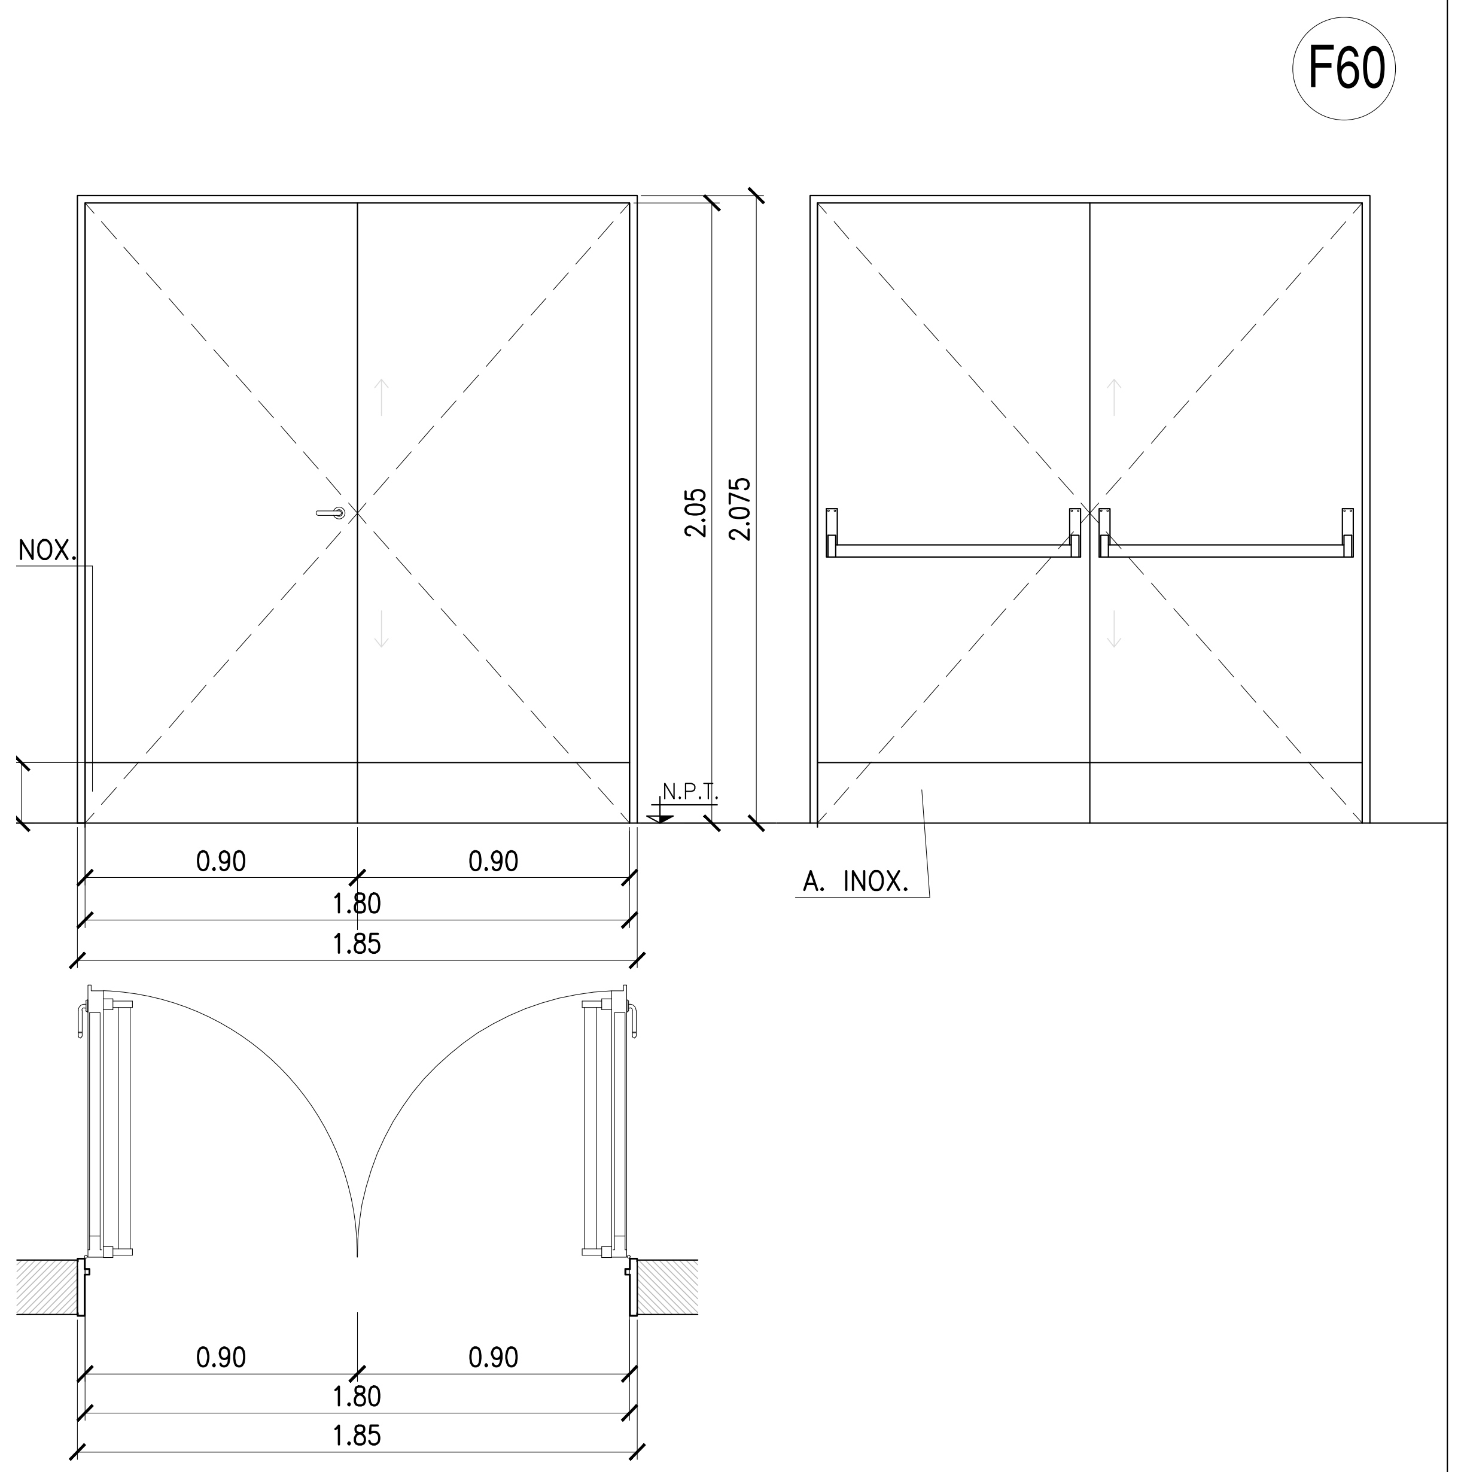

UBICACION	CENTRO DE POTENCIA, SALA DE SEÑALES				**P7**
TIPO	CANT. S/COMPUTO	DER. VER PLANTAS	IZQ. VER PLANTAS		
MARCO	CHAPA DOBLADA BWG N°18 PINTURA 2 MANOS DE ANTIOXIDO+2 MANOS DE SINT.COLOR A DEF.				
HOJAS	DOBLE CHAPA ESP. 45mm BWG 18 CON REFUERZOS INTERNOS – LANA MINERAL 60KG/M3 O MATERIAL APROB. – PINT. 2 MANOS ANTIOXIDO+ 2 MANOS ESMALTE SINTETICO A DEFINIR				
HERRAJES	BISAGRAS REFORZADAS A MUNICION ,CERRADURA DE EMBUTIR DE SEGURIDAD ACYTRA CON FRENTE DE BRONCE PLATIL. BARRAL ANTIPANICO 1" PLATIL. PASADORES DE HIERRO DE APLICAR. CIERRE DOBLE CONTACTO C/ BURLETE INTUMECENTE – CIERRE PUERTA AEREO				**1.85**
OBSERVACIONES	ZOCALO AC° INOX° H:20cm.				

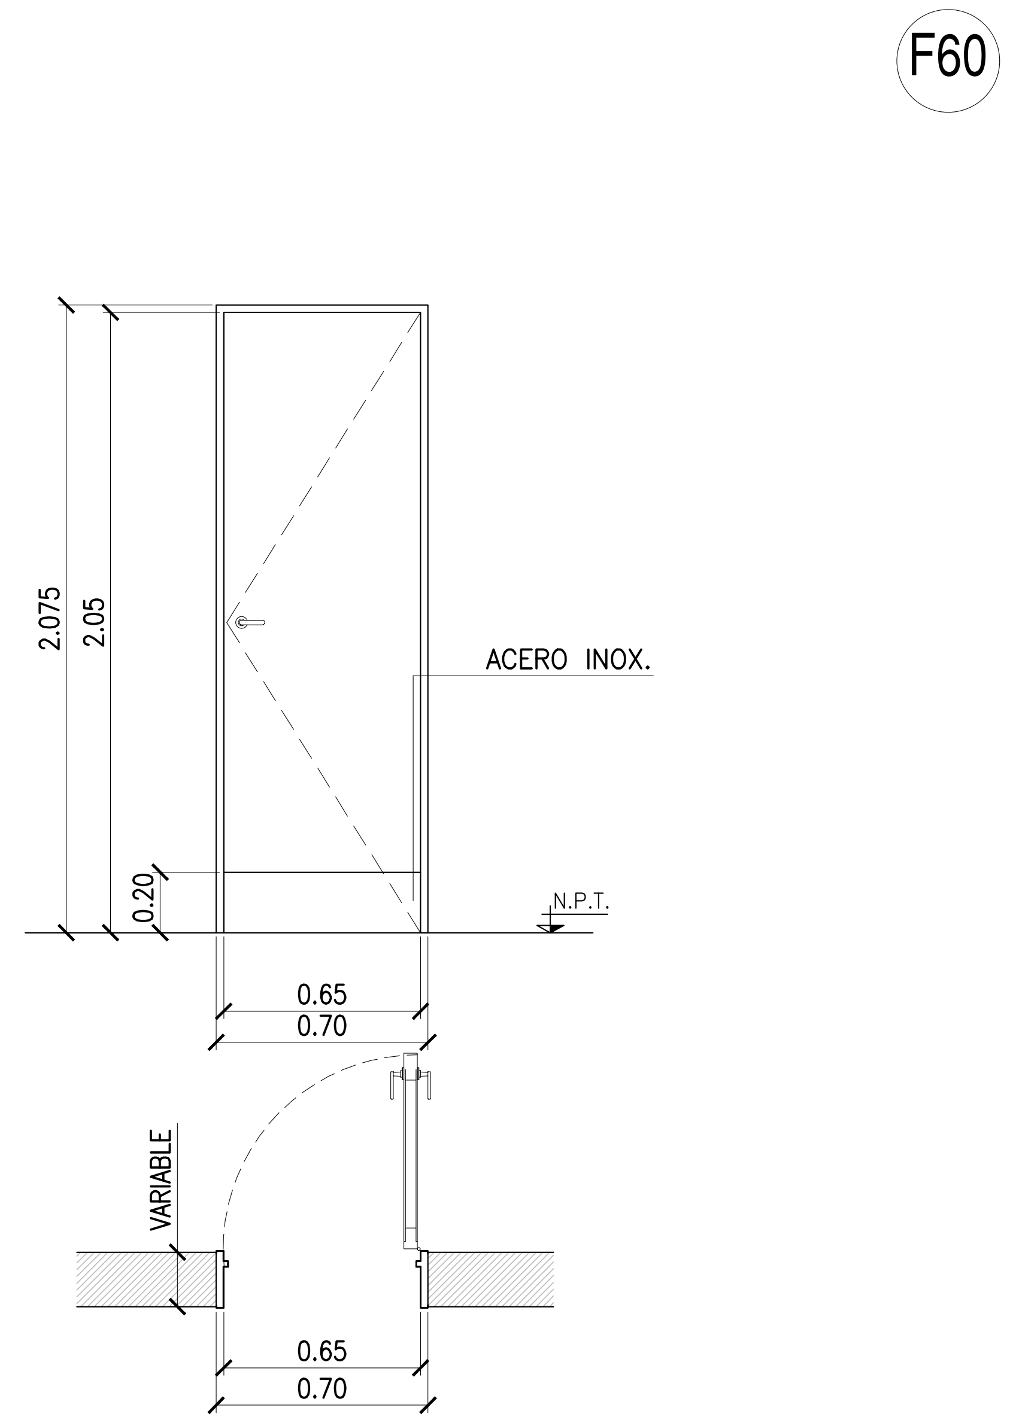

UBICACION	EN ACCESO A PLENO INSTALACIONES				**P8**
TIPO	CANT. S/COMPUTO	DER. VER PLANTAS	IZQ. VER PLANTAS		
MARCO	CHAPA DOBLADA BWG N°18 PINTURA 2 MANOS DE ANTIOXIDO+2 MANOS DE SINT.COLOR A DEF.				
HOJAS	DOBLE CHAPA ESP. 45mm BWG 18 CON REFUERZOS INTERNOS – LANA MINERAL 60KG/M3 O MATERIAL APROB. – PINT. 2 MANOS ANTIOXIDO+ 2 MANOS ESMALTE SINTETICO A DEFINIR				
HERRAJES	BISAGRAS REFORZADAS A MUNICION ,CERRADURA DE EMBUTIR DE SEGURIDAD ACYTRA CON FRENTE DE BRONCE PLATIL. PICAPORTE DOBLE BALANCIN BRONCE PLASTIL. CIERRE DOBLE CONTACTO C/ BURLETE INTUMECENTE – CIERRE PUERTA AEREO				**0.70**
OBSERVACIONES	ZOCALO AC° INOX° H:20cm.				

NOTAS:
EL PRESENTE PLANO ES INDICATIVO. LA CONTRATISTA CONFECCIONARÁ LOS PLANOS DE DETALLE DEFINITIVO, QUE DEBERÁN SER APROBADOS POR LA D.G.O.INF.U Y LA INSPECCIÓN DE OBRA. EL PLANO PRESENTADO POR LA CONTRATISTA ESTARA EN UN TODO DE ACUERDO CON LA NORMATIVA VIGENTE.
TODAS LAS MEDIDAS Y NIVELES SE VERIFICARÁN EN OBRA POR EL CONTRATISTA.
TODOS LOS DETALLES CONSTRUCTIVOS SERAN COORDINADOS Y COMPATIBILIZADOS EN OBRA.

PLANO NO APTO PARA CONSTRUCCIÓN

MODIFICACIONES:

REVISION	FECHA	DESCRIPCION
00	30-01-2026	EMISIÓN PARA LICITACIÓN
01	10-04-2026	EMISIÓN PARA LICITACIÓN

Gobierno de la Ciudad de Buenos Aires

MINISTERIO DE INFRAESTRUCTURA
SUBSECRETARIA DE PROYECTOS Y OBRAS
DIRECCION GENERAL DE PROYECTOS

DGPRO

Obra: LÍNEA F
Plano Estación Corrientes- Planilla de Carpinterías 01 de 02
Fecha :10/04/2026
Eq. de Proyecto: UPU - ATEC - IATASA
Dibujó: JS
PLANO-2026-18237204-GCABA-SSPO
LF-ES-CRR-ARQ-PL-026-01-R01
Revisó: GV
Escala: 1:25
Plano N°: A026-01
Página 1 de 1

GOBIERNO DE LA CIUDAD DE BUENOS AIRES
"2026 - Año del 30° Aniversario de la sanción de la Constitución de la Ciudad Autónoma de Buenos Aires"

Hoja Adicional de Firmas
Plano

Número: PLANO-2026-18237204-GCABA-SSPO

Buenos Aires, Viernes 17 de Abril de 2026

Referencia: LF-ES-CRR-ARQ-PL-026-01_1

El documento fue importado por el sistema GEDO con un total de 1 pagina/s.

Digitally signed by Comunicaciones Oficiales
Date: 2026.04.17 13:04:26 -03:00

Facundo Lombardo
Subsecretario
SUBSECRETARIA PROYECTOS Y OBRAS
MINISTERIO DE MOVILIDAD E INFRAESTRUCTURA

Digitally signed by Comunicaciones Oficiales
Date: 2026.04.17 13:04:27 -03:00