

PUERTA ANDÉN


CORTE 1:25

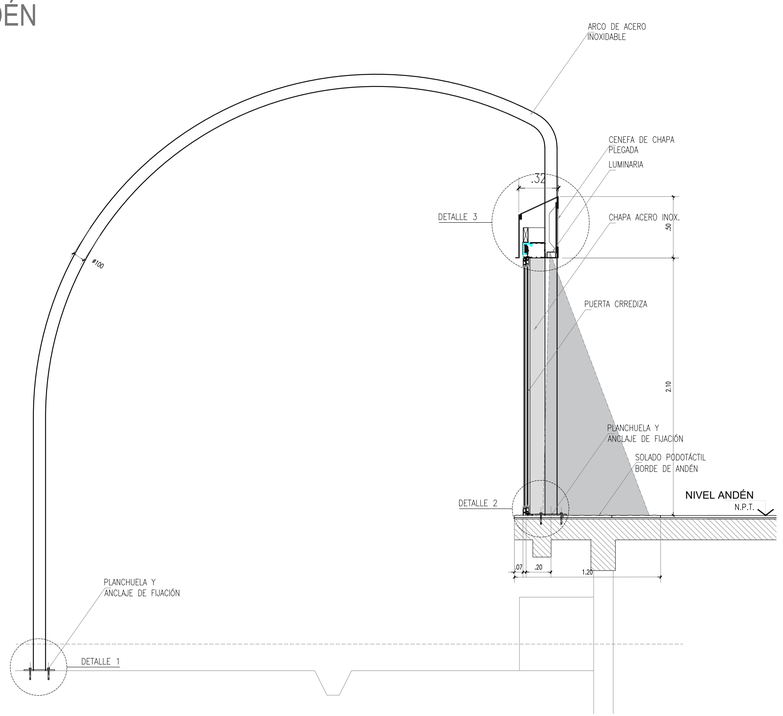


VISTA 1:25

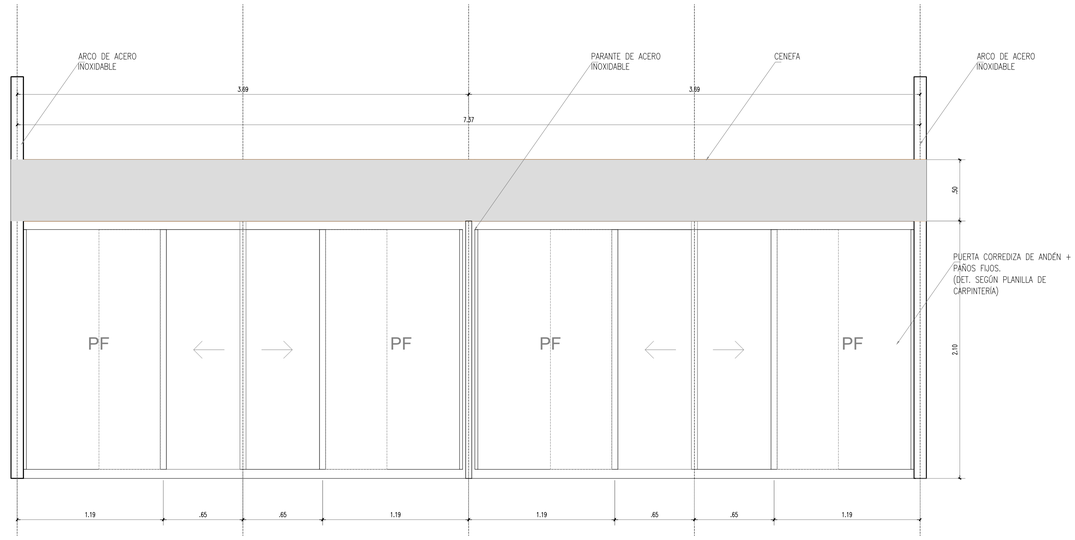


PLANTA 1:25

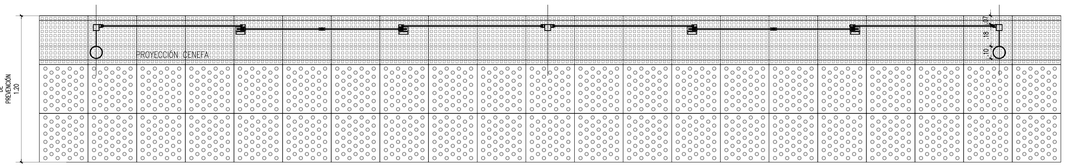


DETALLE 1 1:5
FIJACIÓN PERFIL

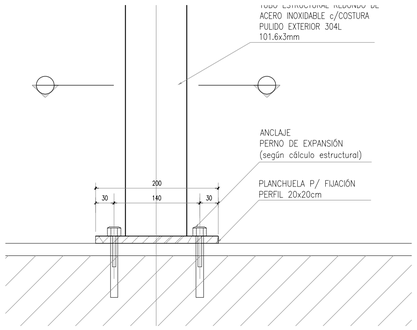


DETALLE 2 1:5
FIJACIÓN PERFIL

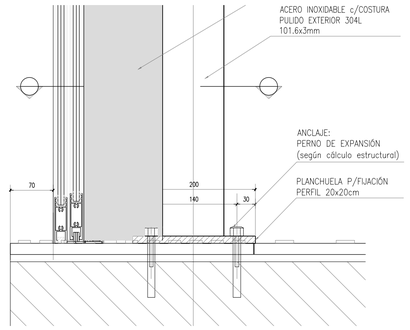


DETALLE 3 1:5
CENEFA

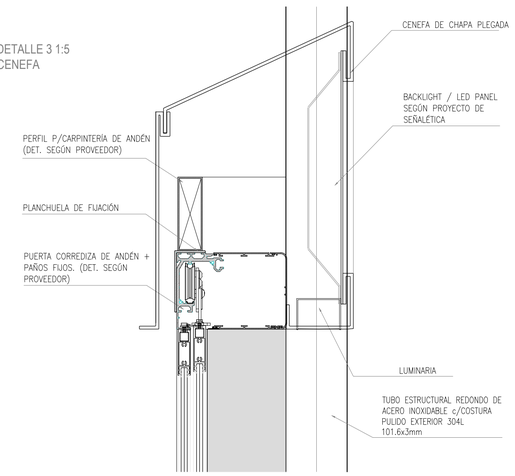

PLANTA 1 1:5
FIJACIÓN PERFIL

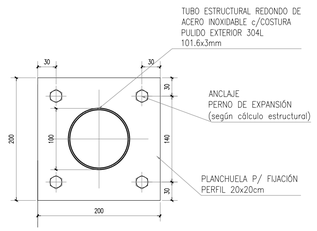

PLANTA 2 1:5
FIJACIÓN PERFIL

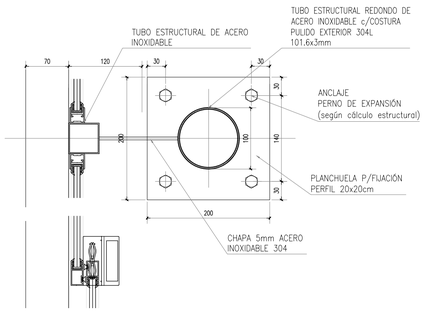

NOTAS: EL PRESENTE PLANO ES INDICATIVO. LA CONTRATISTA CONFECCIONARÁ LOS PLANOS DE DETALLE DEFINITIVOS, QUE DEBERÁN SER APROBADOS POR LA S.U.G.SIP. Y LA DIRECCIÓN DE OBRA. EL PLANO PRESENTADO POR LA CONTRATISTA ESTARÁ EN UN TODO DE ACUERDO CON LA NORMATIVA VIGENTE. TODAS LAS MEDIDAS Y NIVELES SE VERIFICARÁN EN OBRA POR EL CONTRATISTA. TODOS LOS DETALLES CONSTRUCTIVOS SERÁN CONSENSUADOS Y COMPATIBILIZADOS EN OBRA.

PLANO NO APTO PARA CONSTRUCCIÓN

MODIFICACIONES:

REVISION	FECHA	DESCRIPCION
00	30-01-2026	EMISIÓN PARA LICITACIÓN
01	10-04-2026	EMISIÓN PARA LICITACIÓN

Gobierno de la Ciudad Buenos Aires

MINISTERIO DE INFRAESTRUCTURA
SUBSECRETARIA DE PROYECTOS Y OBRAS
DIRECCION GENERAL DE PROYECTOS

DGPRO

Obra: LÍNEA F			PLANO-2026-18237683-GCABA-SSPO
Plano Estación Corrientes - Detalle Puerta de Andén			LF-ES-CRR-ARQ-PL-022-R01
Fecha :10/04/2026	Eq. de Proyecto: UPU - ATEC - IATASA	Dibujó: JS	Revisó: GV / Escala: 1:25/ 1:5

Nº: A022

G O B I E R N O DE LA C I U D A D DE B U E N O S A I R E S

"2026 - Año del 30° Aniversario de la sanción de la Constitución de la Ciudad Autónoma de Buenos Aires"

Hoja Adicional de Firmas
Plano

Número: PLANO-2026-18237683-GCABA-SSPO

Buenos Aires, Viernes 17 de Abril de 2026

Referencia: LF-ES-CRR-ARQ-PL-022_1

El documento fue importado por el sistema GEDO con un total de 1 pagina/s.

Digitally signed by Comunicaciones Oficiales
Date: 2026.04.17 13:05:32 -03:00

Facundo Lombardo
Subsecretario
SUBSECRETARIA PROYECTOS Y OBRAS
MINISTERIO DE MOVILIDAD E INFRAESTRUCTURA

Digitally signed by Comunicaciones Oficiales
Date: 2026.04.17 13:05:33 -03:00