


PLANIMETRÍA GENERAL - INST. ELÉCTRICA/TOMACORRIENTES
PLANTA NIVEL ACCESO/VEREDA
ESCALA 1:100

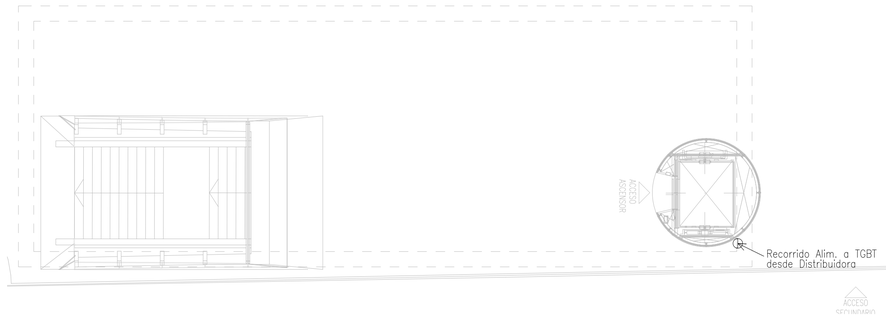

PLANIMETRÍA GENERAL - INST. ELÉCTRICA/TOMACORRIENTES
PLANTA NIVEL VENTILACIÓN
ESCALA 1:100

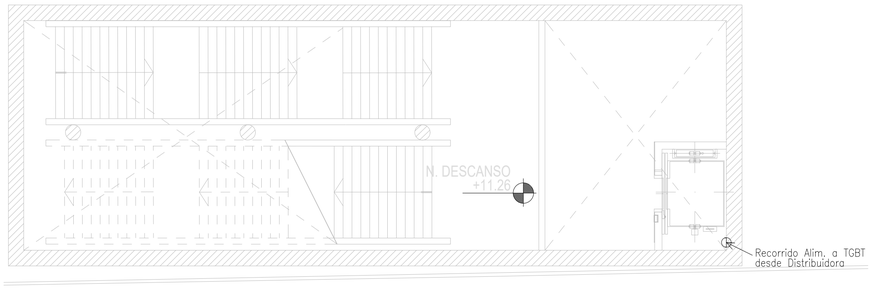

PLANIMETRÍA GENERAL
INST. ELÉCTRICA/TOMACORRIENTES
PLANTA NIVEL VENTILACIÓN
ESCALA 1:100

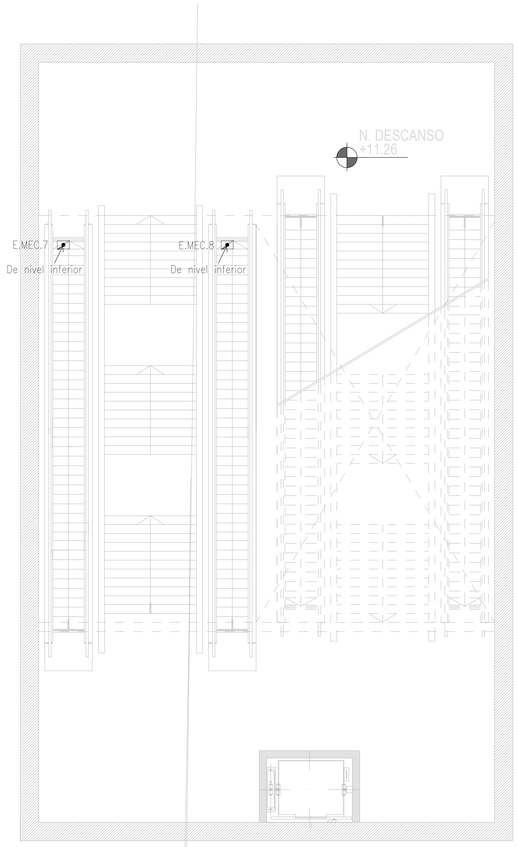

ALIMENTADORES A TABLEROS, BARRA NO ESENCIAL

Tablero	Ubicación	Cable Sección (mm²)	Longitud (m)
TSASC.1	Sala Máquinas. Ascensor 1	4x16	50
TSASC.2	Sala Máquinas. Ascensor 2	3x25+1x16	120
TSASC.3	Sala Máquinas. Ascensor 3	3x50+1x25	70
TSASC.4	Sala Máquinas. Ascensor 4	3x50+1x25	230
TSA1.N	Andén	3x25+1x16	30
TSVIE	Sala de Ventilación Inyección y Extracción	3x95+1x50	25
TSVENT	Sala de Ventilación	3x185+1x95	270
TSTUN1.N	Túnel	4x16	25
TSTUN2.N	Túnel	4x16	25
TSTUN3.N	Túnel	3x35+1x16	170
TSTUN4.N	Túnel	3x35+1x16	170
TSPPC	Pozo de bombeo pluviocloacal	3x50+1x25	185
E.MEC.1	Esc. Mecánica	4x16	40
E.MEC.2	Esc. Mecánica	4x16	75
E.MEC.3	Esc. Mecánica	3x25+1x16	110
E.MEC.4	Esc. Mecánica	3x25+1x16	145
E.MEC.5	Esc. Mecánica	3x25+1x16	220
E.MEC.6	Esc. Mecánica	3x50+1x25	230
E.MEC.7	Esc. Mecánica	3x50+1x25	250
E.MEC.8	Esc. Mecánica	3x50+1x25	260


ALIMENTADORES A TABLEROS, BARRA ESENCIAL

Tablero	Ubicación	Cable Sección (mm²)	Longitud (m)
TSB 1.E	Boleteria 1	4x16	230
TSM1.E	Mezzanine	4x6	70
TSM2.E	Mezzanine	4x10	140
TSA1.E	Andén	3x25+1x16	30
TSTUN1.E	Túnel	3x25+1x16	25
TSTUN2.E	Túnel	3x25+1x16	25
TSTUN3.E	Túnel	3x35+1x16	170
TSTUN4.E	Túnel	3x35+1x16	170
TSEN.E	Sala de enclavamiento	4x16	160
TSTEL.E	Sala telefonía	4x6	20
TSSEÑ.E	Sala de señales	4x10	25
TSCOM.E	Sala de comunicaciones	4x10	25
TSFAS.E	Fire Alarm System	4x10	175
TSCIS.E	Bombas de Incendio (Sala Cisterna)	3x150+1x70	175
TSB1	Centro de potencia	4x6	15

ALIMENTADORES A TABLEROS, BARRA ESENCIAL – UPS

Tablero	Ubicación	Cable Sección (mm²)	Longitud (m)
TSU1	Boleteria 1	4x16	230
TSU2	Mezzanine	4x6	70
TSU3	Mezzanine	4x10	140
TSU4	Andén	4x6	25

ESQUEMA DE ALIMENTACIÓN ELÉCTRICA

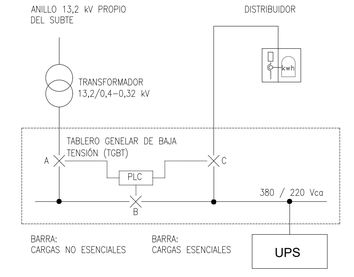

OPERACIÓN NORMAL:
INTERRUPTO A Y B CERRADOS, C ABIERTO

OPERACIÓN DE RESERVA (FALLA ALIMENTACIÓN PRINCIPAL)
INTERRUPTO C CERRADO, A Y B ABIERTO

EVACUACIÓN (FALLAN AMBAS ALIMENTACIONES)
UPS ALIMENTA ILUMINACIÓN DE EVACUACIÓN

SÍMBOLOS:

- INSTALACION A LA VISTA CON CAÑO H°G°
- INSTALACION EMBUTIDA CON CAÑO Y ACCESORIOS SEGUN IRAM-IAS U500-2005 Y CAJAS METALICAS SEGUN IRAM 62005
- CAJAS DE PASO
- BANDEJAS TIPO ESCALERA. BANDEJAS TIPO PERFORADAS.
- ARTEFACTO 90W LED, TIPO TUBO INDUSTRIAL, APLICADO, IP65
- CAJA OCTOGONAL CHICA SEGÚN IRAM 62005, EMBUTIDA EN LOSA. SALIDA PARA ARTEFACTO DE ILUMINACIÓN.
- CAJA REDONDA A°F° SEGÚN IRAM 2005, APLICDA EN LOSA O SOBRE CIELORRASO, SEGÚN CORRESPONDA. SALIDA PARA ARTEFACTO DE ILUMINACIÓN.
- LLAVE DE EFECTO EN CAJA 100x50x50mm, SEGÚN IRAM 62005, EMBUTIDA. SALVO OTRA INDICACIÓN, h=1,10m SOBRE N.P.T.
- LLAVE DE EFECTO EN CAJA 100x50mm, F°A° SEGÚN IRAM 2005. SALVO OTRA INDICACIÓN, h=1,10m SOBRE N.P.T.
- B CAJA DE PASO, CON BORNERAS EN SU INTERIOR
- TOMACORRIENTES MONOFASICO 2x10A+T, EN CAJA 100x50x50mm EMBUTIDA EN FORMA HORIZONTAL
- CAJA CUADRADA DE PVC

PLANIMETRÍA GENERAL - INST. ELÉCTRICA/TOMACORRIENTES
PLANTA NIVEL VENTILACIÓN
ESCALA 1:100



NOTA PUESTA A TIERRA

TOMA DE TIERRA DE LA ESTACIÓN

LAS ESTACIONES TENDRÁN 2 TOMAS DE TIERRA INDEPENDIENTES. LAS MISMAS ESTARÁN VINCULADAS ENTRE SÍ PARA GARANTIZAR EQUIPOTENCIALIZACIÓN ENTRE ELLAS.


UNA TOMA SERÁ DE SERVICIO Y SEGURIDAD DE LAS INSTALACIONES DE POTENCIA (BAJA TENSIÓN). LA OTRA SERÁ PARA EL SISTEMA DE CORRIENTES DÉBILES Y SEÑALES.

PARA ESTAS TOMAS DE TIERRA SE DEBERÁN UTILIZAR 6 JABALINAS DE 3 MTS. COMO MÍNIMO. SALVO QUE PUEDA ASEGURARSE LA IMPERMEABILIDAD ABSOLUTA, NO PODRÁN ESTAR UBICADAS EN LA PARTE INFERIOR DE LAS ESTACIONES (BAJO ANDÉN). EN TAL SENTIDO PODRÁN PREVERSE EN LA ZONA MÁS ALTA POSIBLE CON LA PRESIÓN DEL AGUA MÁS BAJA Y TOMADO TODO LOS RECAUDAOS PARA EVITAR FILTRACIONES.


NOTAS:

1. LAS SECCIONES DE CABLES SE INDICAN EN mm²
2. TODOS LOS CABLES EN BANDEJAS Y/O TETRAPOLARES SON SEGUN IRAM 2178
3. TODAS LAS CAJAS DE PASO A LA VISTA SERÁN DE FUNDICIÓN DE ALUMINIO
4. TODAS LAS CAJAS DE PASO EMBUTIDAS SERÁN CAJAS METALICAS SEGUN IRAM 62005
5. LAS CAJAS DE PASO PODRÁN SER COMPARTIDAS CON CIRCUITOS DE DISTRIBUCIÓN, DE ILUMINACIÓN Y/O TOMACORRIENTES
6. LAS BANDEJAS HORIZONTALES SON SOPORTADAS C/ 1,5m
7. LOS CAÑOS NO INDICADOS SON RS19 O H°G° 3/4"
8. TODOS LOS CIRCUITOS SON CABLES SEGUN IRAM NM 247-3
9. LOS RECORRIDOS TRONCALES Y SUS CAJAS DE PASO SON COMPARTIDOS CON CIRCUITOS PARA TOMACORRIENTES.
10. LA CONEXIÓN A LLAVES DE EFECTO ES CON CABLE DE 1,5 SEGUN IRAM 247-3
11. PARA CABLES DE SECCIONES DE 6mm O MAYORES, LAS DERIVACIONES SERÁN POR MEDIO DE BORNERAS COMPONIBLES.

N. ACCESO

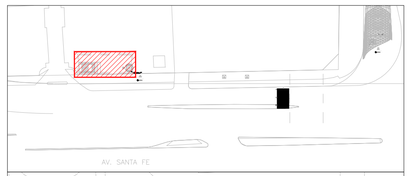

N. VENTILACIÓN

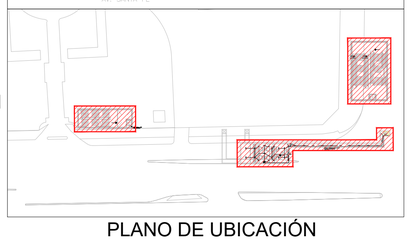

PLANO DE UBICACIÓN

NOTAS:
EL PRESENTE PLANO ES INDICATIVO. LA CONTRATISTA CONFECCIONARA LOS PLANOS DE DETALLE DEFINITIVO, QUE DEBERAN SER APROBADOS POR LA D.G.INF.U Y LA INSPECCION DE OBRA. EL PLANO PRESENTADO POR LA CONTRATISTA ESTARA EN UN TODO DE ACUERDO CON LA NORMATIVA VIGENTE.
TODAS LAS MEDIDAS Y NIVELES SE VERIFICARAN EN OBRA POR EL CONTRATISTA.
TODOS LOS DETALLES CONSTRUCTIVOS SERAN COORDINADOS Y COMPATIBILIZADOS EN OBRA

PLANO NO APTO PARA CONSTRUCCION.

NOTA

MODIFICACIONES:

REVISION	FECHA	DESCRIPCION
0	25/03/2026	EMISIÓN PARA LICITACIÓN


MINISTERIO DE INFRAESTRUCTURA
SUBSECRETARIA DE PROYECTOS Y OBRAS
DIRECCION GENERAL DE PROYECTOS

DGPRO


Obra: LINEA F			PLANO-2026-18239568-GCABA-SSPO#MI	
Plano: Estación Pacifico - Accesos - Inst. Eléctrica - Tomacorrientes			LF-ES-PAC-ELE-PL-006-01	
Fecha: 25/03/2026	Eq. de Proyecto: UPU-ATEC-IATASA	Dibujó: M.B.	Revisó: A.L.	Escala: 1:100

1/2


PLANIMETRÍA GENERAL - CORRIENTES DÉBILES
PLANTA NIVEL ACCESO/VEREDA
ESCALA 1:100

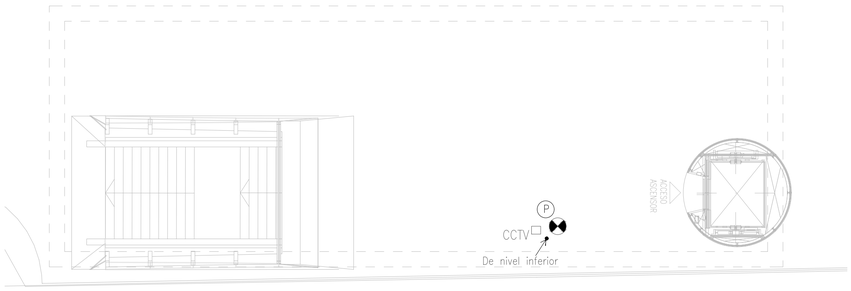

PLANIMETRÍA GENERAL - CORRIENTES DÉBILES
PLANTA NIVEL VENTILACIÓN
ESCALA 1:100

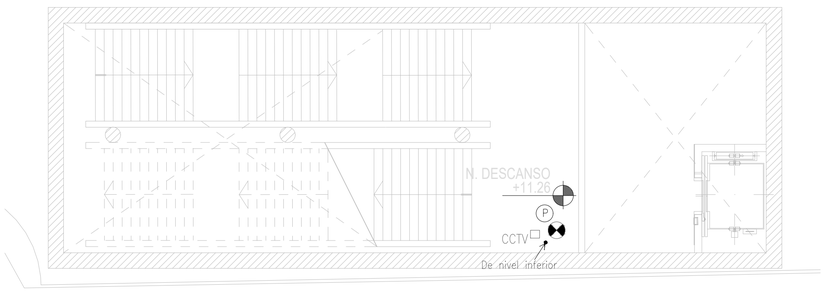

PLANIMETRÍA GENERAL - CORRIENTES DÉBILES
PLANTA NIVEL VENTILACIÓN
ESCALA 1:100

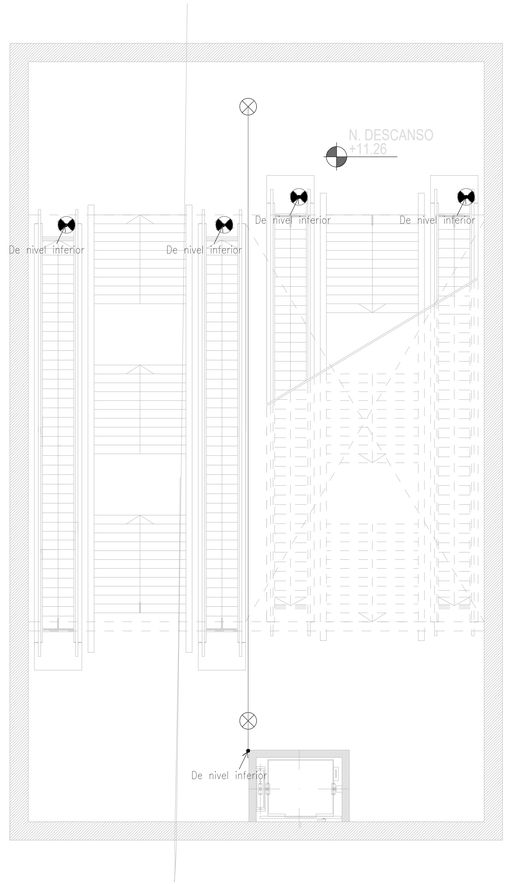

PLANIMETRÍA GENERAL - CORRIENTES DÉBILES
PLANTA NIVEL VENTILACIÓN
ESCALA 1:100



NOTAS:


1. LOS CAÑOS NO INDICADOS SON RS19 O H°G° 3/4"
2. LAS CAÑERIAS VACIAS SERÁN RECORRIDAS EN SU TOTALIDAD POR ALAMBRES GUIA GALVANIZADO.

SÍMBOLOS:

- INSTALACION A LA VISTA CON CAÑO H°G°
- INSTALACION EMBUTIDA CON CAÑO Y ACCESORIOS SEGUN IRAM-IAS U500-2005 Y CAJAS METALICAS SEGUN IRAM 62005
- CAJAS DE PASO
- BANDEJAS TIPO PERFORADAS.
- CAJA CUADRADA DE PVC
- P — CAJA REDONDA DE FUNDICION DE ALUMINIO SEGUN IRAM 2005, SALIDA PARA PARLANTE.
- CCTV — CAJA PARA SALIDA DE CAMARA CIRCUITO CERRADO DE TV
- TI — BOCA PARA TELEFONIA INTERNA EN CAJA METALICA 100x50x50 mm, EMBUTIDA
- TI — BOCA PARA TELEFONIA INTERNA EN CAJA F°A° 100x50 mm, APLICADA
- CAJA REDONDA DE FUNDICION DE ALUMINIO SEGUN IRAM 2005, SALIDA PARA DETECTOR DE INCENDIO, APLICADA.
- CAJA OCTOGONAL CHICA SEGUN IRAM 62005, SALIDA PARA DETECTOR DE INCENDIO, EMBUTIDA.
- D — BOCA PARA DATOS EN CAJA METALICA SEGUN NORMA IRAM 62005 A UNA ALTURA DE 0.55m SOBRE N.P.T.
- AMI — AVISADOR MANUAL DE INCEDIO, h=1,20m SOBRE N.P.T.

N. ACCESO

N. VENTILACIÓN

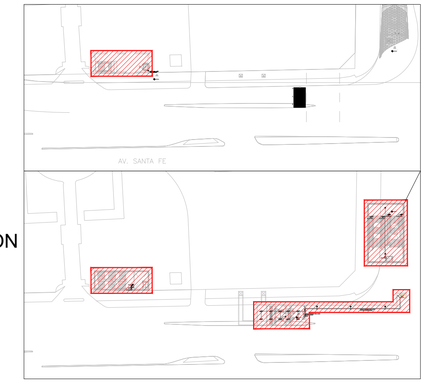

PLANO DE UBICACIÓN

NOTAS:
EL PRESENTE PLANO ES INDICATIVO. LA CONTRATISTA CONFECCIONARA LOS PLANOS DE DETALLE DEFINITIVO, QUE DEBERAN SER APROBADOS POR LA D.G.INF.U Y LA INSPECCION DE OBRA. EL PLANO PRESENTADO POR LA CONTRATISTA ESTARA EN UN TODO DE ACUERDO CON LA NORMATIVA VIGENTE.
TODAS LAS MEDIDAS Y NIVELES SE VERIFICARAN EN OBRA POR EL CONTRATISTA.
TODOS LOS DETALLES CONSTRUCTIVOS SERAN COORDINADOS Y COMPATIBILIZADOS EN OBRA

PLANO NO APTO PARA CONSTRUCCION.

NOTA

MODIFICACIONES:

REVISION	FECHA	DESCRIPCION
0	25/03/2026	EMISIÓN PARA LICITACIÓN

MINISTERIO DE INFRAESTRUCTURA
SUBSECRETARIA DE PROYECTOS Y OBRAS
DIRECCION GENERAL DE PROYECTOS

DGPRO

Obra: LINEA F

PLANO-2026-18239568-GCABA-SSPO N°

Plano: Estación Pacífico - Accesos - Inst. Eléctrica - Corrientes Débiles | LF-ES-PAC-ELE-PL-006-03 | 2/2

Fecha: 25/03/2026 | Eq. de Proyecto: UPU-ATEC-IATASA | Dibujó: M.B. | Revisó: A.L. | Escala: 1:100

G O B I E R N O DE LA C I U D A D DE B U E N O S A I R E S

"2026 - Año del 30° Aniversario de la sanción de la Constitución de la Ciudad Autónoma de Buenos Aires"

Hoja Adicional de Firmas
Plano

Número: PLANO-2026-18239568-GCABA-SSPO

Buenos Aires, Viernes 17 de Abril de 2026

Referencia: LF-ES-PAC-ELE-PL-006-01/02_0

El documento fue importado por el sistema GEDO con un total de 2 pagina/s.

Digitally signed by Comunicaciones Oficiales
Date: 2026.04.17 13:10:43 -03:00

Facundo Lombardo
Subsecretario
SUBSECRETARIA PROYECTOS Y OBRAS
MINISTERIO DE MOVILIDAD E INFRAESTRUCTURA

Digitally signed by Comunicaciones Oficiales
Date: 2026.04.17 13:10:43 -03:00