
PLANIMETRÍA GENERAL
CORTE LONGITUDINAL

ESCALA 1:125

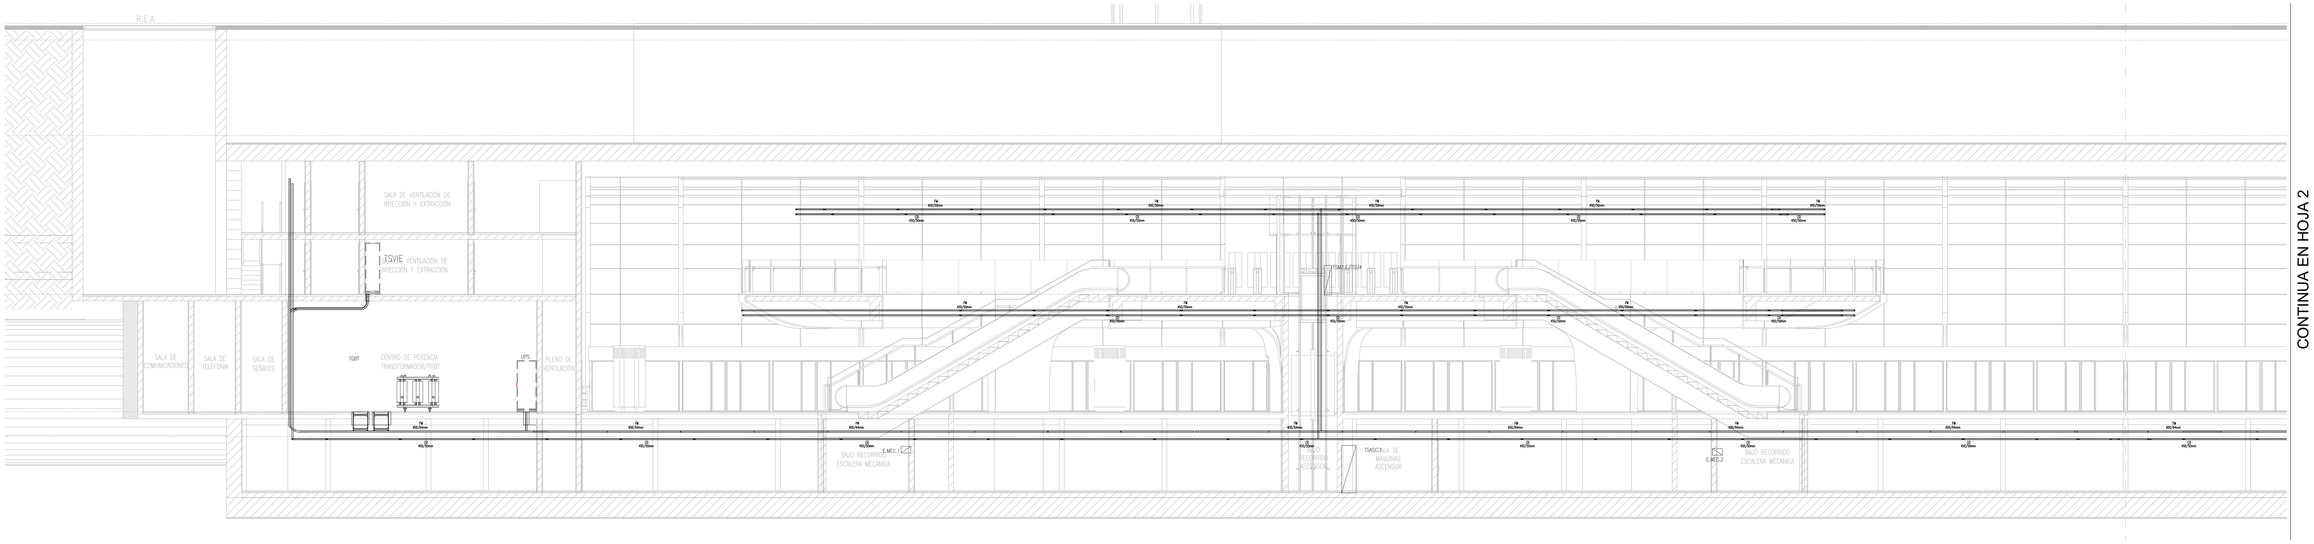

ALIMENTADORES A TABLEROS, BARRA NO ESENCIAL


Tablero	Ubicación	Cable Sección (mm²)	Longitud (m)
TSASC.1	Sala Máquinas. Ascensor 1	4x16	50
TSASC.2	Sala Máquinas. Ascensor 2	3x25+1x16	120
TSASC.3	Sala Máquinas. Ascensor 3	3x50+1x25	70
TSASC.4	Sala Máquinas. Ascensor 4	3x50+1x25	230
TSA1.N	Andén	3x25+1x16	30
TSVIE	Sala de Ventilación Inyección y Extracción	3x95+1x50	25
TSVENT	Sala de Ventilación	3x185+1x95	270
TSTUN1.N	Túnel	4x16	25
TSTUN2.N	Túnel	4x16	25
TSTUN3.N	Túnel	3x35+1x16	170
TSTUN4.N	Túnel	3x35+1x16	170
TSPPC	Pozo de bombeo pluviocloacal	3x50+1x25	185
E.MEC.1	Esc. Mecánica	4x16	40
E.MEC.2	Esc. Mecánica	4x16	75
E.MEC.3	Esc. Mecánica	3x25+1x16	110
E.MEC.4	Esc. Mecánica	3x25+1x16	145
E.MEC.5	Esc. Mecánica	3x25+1x16	220
E.MEC.6	Esc. Mecánica	3x50+1x25	230
E.MEC.7	Esc. Mecánica	3x50+1x25	250
E.MEC.8	Esc. Mecánica	3x50+1x25	260

ALIMENTADORES A TABLEROS, BARRA ESENCIAL

Tablero	Ubicación	Cable Sección (mm²)	Longitud (m)
TSB 1.E	Boletería 1	4x16	230
TSM1.E	Mezzanine	4x6	70
TSM2.E	Mezzanine	4x10	140
TSA1.E	Andén	3x25+1x16	30
TSTUN1.E	Túnel	3x25+1x16	25
TSTUN2.E	Túnel	3x25+1x16	25
TSTUN3.E	Túnel	3x35+1x16	170
TSTUN4.E	Túnel	3x35+1x16	170
TSEN.E	Sala de enclavamiento	4x16	160
TSTEL.E	Sala telefonía	4x6	20
TSSEÑ.E	Sala de señales	4x10	25
TSCOM.E	Sala de comunicaciones	4x10	25
TSFAS.E	Fire Alarm System	4x10	175
TSCIS.E	Bombas de Incendio (Sala Cisterna)	3x150+1x70	175
TSB1	Centro de potencia	4x6	15

ALIMENTADORES A TABLEROS, BARRA ESENCIAL – UPS

Tablero	Ubicación	Cable Sección (mm²)	Longitud (m)
TSU1	Boletería 1	4x16	230
TSU2	Mezzanine	4x6	70
TSU3	Mezzanine	4x10	140
TSU4	Andén	4x6	25

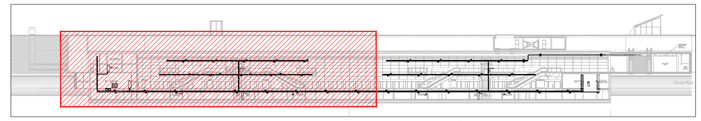

PLANO DE UBICACIÓN

NOTAS:

EL PRESENTE PLANO ES INDICATIVO. LA CONTRATISTA CONFECCIONARA LOS PLANOS DE DETALLE DEFINITIVO, QUE DEBERAN SER APROBADOS POR LA D.G.O. INF U Y LA INSPECCION DE OBRA. EL PLANO PRESENTADO POR LA CONTRATISTA ESTARA EN UN TODO DE ACUERDO CON LA NORMATIVA VIGENTE.
TODAS LAS MEDIDAS Y NIVELES SE VERIFICARAN EN OBRA POR EL CONTRATISTA.
TODOS LOS DETALLES CONSTRUCTIVOS SERAN COORDINADOS Y COMPATIBILIZADOS EN OBRA

PLANO NO APTO PARA CONSTRUCCION.

NOTA

MODIFICACIONES:

REVISION	FECHA	DESCRIPCION
0	25/03/2026	EMISIÓN PARA LICITACIÓN

Gobierno de la Ciudad de Buenos Aires

MINISTERIO DE INFRAESTRUCTURA
SUBSECRETARIA DE PROYECTOS Y OBRAS
DIRECCION GENERAL DE PROYECTOS

DGPRO


Obra: LINEA F			PLANO-2026-18239806-GCABA-SSPRO
Plano: Estación Pacífico - Corte Longitudinal - Ins. Eléctrica y Corrientes Débiles			LF-ES-PAC-ELE-PL-004-1
Fecha: 25/03/2026	Eq. de Proyecto: UPU-ATEC-IATASA	Dibujó: M.B.	Revisó: A.L.	Escala: 1:125

HOJA N° 1/2

PLANIMETRÍA GENERAL
CORTE LONGITUDINAL

ESCALA 1:125

CONTINUA EN HOJA 1

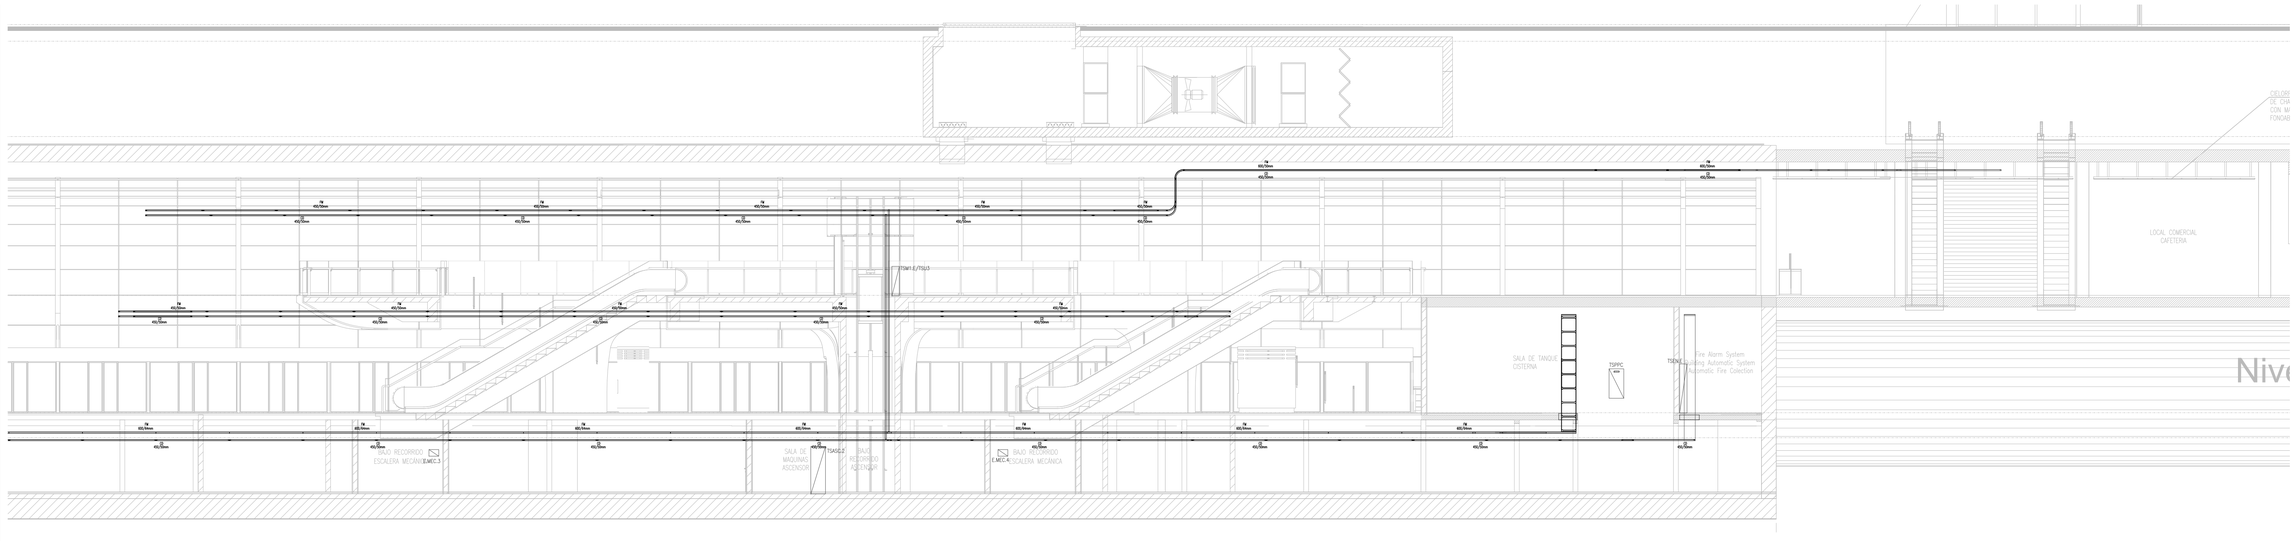

ALIMENTADORES A TABLEROS, BARRA NO ESENCIAL


Tablero	Ubicación	Cable Sección (mm²)	Longitud (m)
TSASC.1	Sala Máquinas. Ascensor 1	4x16	50
TSASC.2	Sala Máquinas. Ascensor 2	3x25+1x16	120
TSASC.3	Sala Máquinas. Ascensor 3	3x50+1x25	70
TSASC.4	Sala Máquinas. Ascensor 4	3x50+1x25	230
TSA1.N	Andén	3x25+1x16	30
TSVIE	Sala de Ventilación Inyección y Extracción	3x95+1x50	25
TSVENT	Sala de Ventilación	3x185+1x95	270
TSTUN1.N	Túnel	4x16	25
TSTUN2.N	Túnel	4x16	25
TSTUN3.N	Túnel	3x35+1x16	170
TSTUN4.N	Túnel	3x35+1x16	170
TSPPC	Pozo de bombeo pluviocloacal	3x50+1x25	185
E.MEC.1	Esc. Mecánica	4x16	40
E.MEC.2	Esc. Mecánica	4x16	75
E.MEC.3	Esc. Mecánica	3x25+1x16	110
E.MEC.4	Esc. Mecánica	3x25+1x16	145
E.MEC.5	Esc. Mecánica	3x25+1x16	220
E.MEC.6	Esc. Mecánica	3x50+1x25	230
E.MEC.7	Esc. Mecánica	3x50+1x25	250
E.MEC.8	Esc. Mecánica	3x50+1x25	260

ALIMENTADORES A TABLEROS, BARRA ESENCIAL

Tablero	Ubicación	Cable Sección (mm²)	Longitud (m)
TSB 1.E	Boletería 1	4x16	230
TSM1.E	Mezzanine	4x6	70
TSM2.E	Mezzanine	4x10	140
TSA1.E	Andén	3x25+1x16	30
TSTUN1.E	Túnel	3x25+1x16	25
TSTUN2.E	Túnel	3x25+1x16	25
TSTUN3.E	Túnel	3x35+1x16	170
TSTUN4.E	Túnel	3x35+1x16	170
TSEN.E	Sala de enclavamiento	4x16	160
TSTEL.E	Sala telefonía	4x6	20
TSSEÑ.E	Sala de señales	4x10	25
TSCOM.E	Sala de comunicaciones	4x10	25
TSFAS.E	Fire Alarm System	4x10	175
TSCIS.E	Bombas de Incendio (Sala Cisterna)	3x150+1x70	175
TSB1	Centro de potencia	4x6	15

ALIMENTADORES A TABLEROS, BARRA ESENCIAL – UPS

Tablero	Ubicación	Cable Sección (mm²)	Longitud (m)
TSU1	Boletería 1	4x16	230
TSU2	Mezzanine	4x6	70
TSU3	Mezzanine	4x10	140
TSU4	Andén	4x6	25

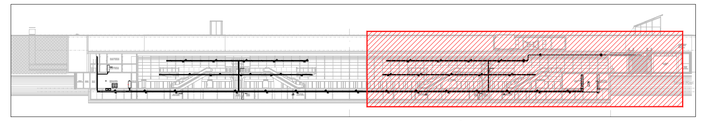

PLANO DE UBICACIÓN

NOTAS:
EL PRESENTE PLANO ES INDICATIVO. LA CONTRATISTA CONFECCIONARA LOS PLANOS DE DETALLE DEFINITIVO, QUE DEBERAN SER APROBADOS POR LA D.G.O. INF U Y LA INSPECCION DE OBRA. EL PLANO PRESENTADO POR LA CONTRATISTA ESTARA EN UN TODO DE ACUERDO CON LA NORMATIVA VIGENTE.
TODAS LAS MEDIDAS Y NIVELES SE VERIFICARAN EN OBRA POR EL CONTRATISTA.
TODOS LOS DETALLES CONSTRUCTIVOS SERAN COORDINADOS Y COMPATIBILIZADOS EN OBRA

PLANO NO APTO PARA CONSTRUCCION.

NOTA

MODIFICACIONES:

REVISION	FECHA	DESCRIPCION
0	25/03/2026	-EMISIÓN PARA LICITACIÓN

Gobierno de la Ciudad de Buenos Aires

MINISTERIO DE INFRAESTRUCTURA
SUBSECRETARIA DE PROYECTOS Y OBRAS
DIRECCION GENERAL DE PROYECTOS

DGPRO

Obra: LINEA F			PLANO-2026-18239806-GCABA-SSPO
Plano: Estación Pacífico - Corte Longitudinal - Ins. Eléctrica y Corrientes Débiles			LF-ES-PAC-ELE-PL-004-2
Fecha: 25/03/2026	Eq. de Proyecto: UPU-ATEC-IATASA	Dibujó: M.B.	Revisó: A.L. Escala: 1:125

HOJA N° 2/2

G O B I E R N O DE LA C I U D A D DE B U E N O S A I R E S

"2026 - Año del 30° Aniversario de la sanción de la Constitución de la Ciudad Autónoma de Buenos Aires"

Hoja Adicional de Firmas
Plano

Número: PLANO-2026-18239806-GCABA-SSPO

Buenos Aires, Viernes 17 de Abril de 2026

Referencia: LF-ES-PAC-ELE-PL-004-01/02_0

El documento fue importado por el sistema GEDO con un total de 2 pagina/s.

Digitally signed by Comunicaciones Oficiales
Date: 2026.04.17 13:11:14 -03:00

Facundo Lombardo
Subsecretario
SUBSECRETARIA PROYECTOS Y OBRAS
MINISTERIO DE MOVILIDAD E INFRAESTRUCTURA

Digitally signed by Comunicaciones Oficiales
Date: 2026.04.17 13:11:14 -03:00