REJA EXTRACCIÓN DE AIRE EN CALZADA

PLANTA 1:25

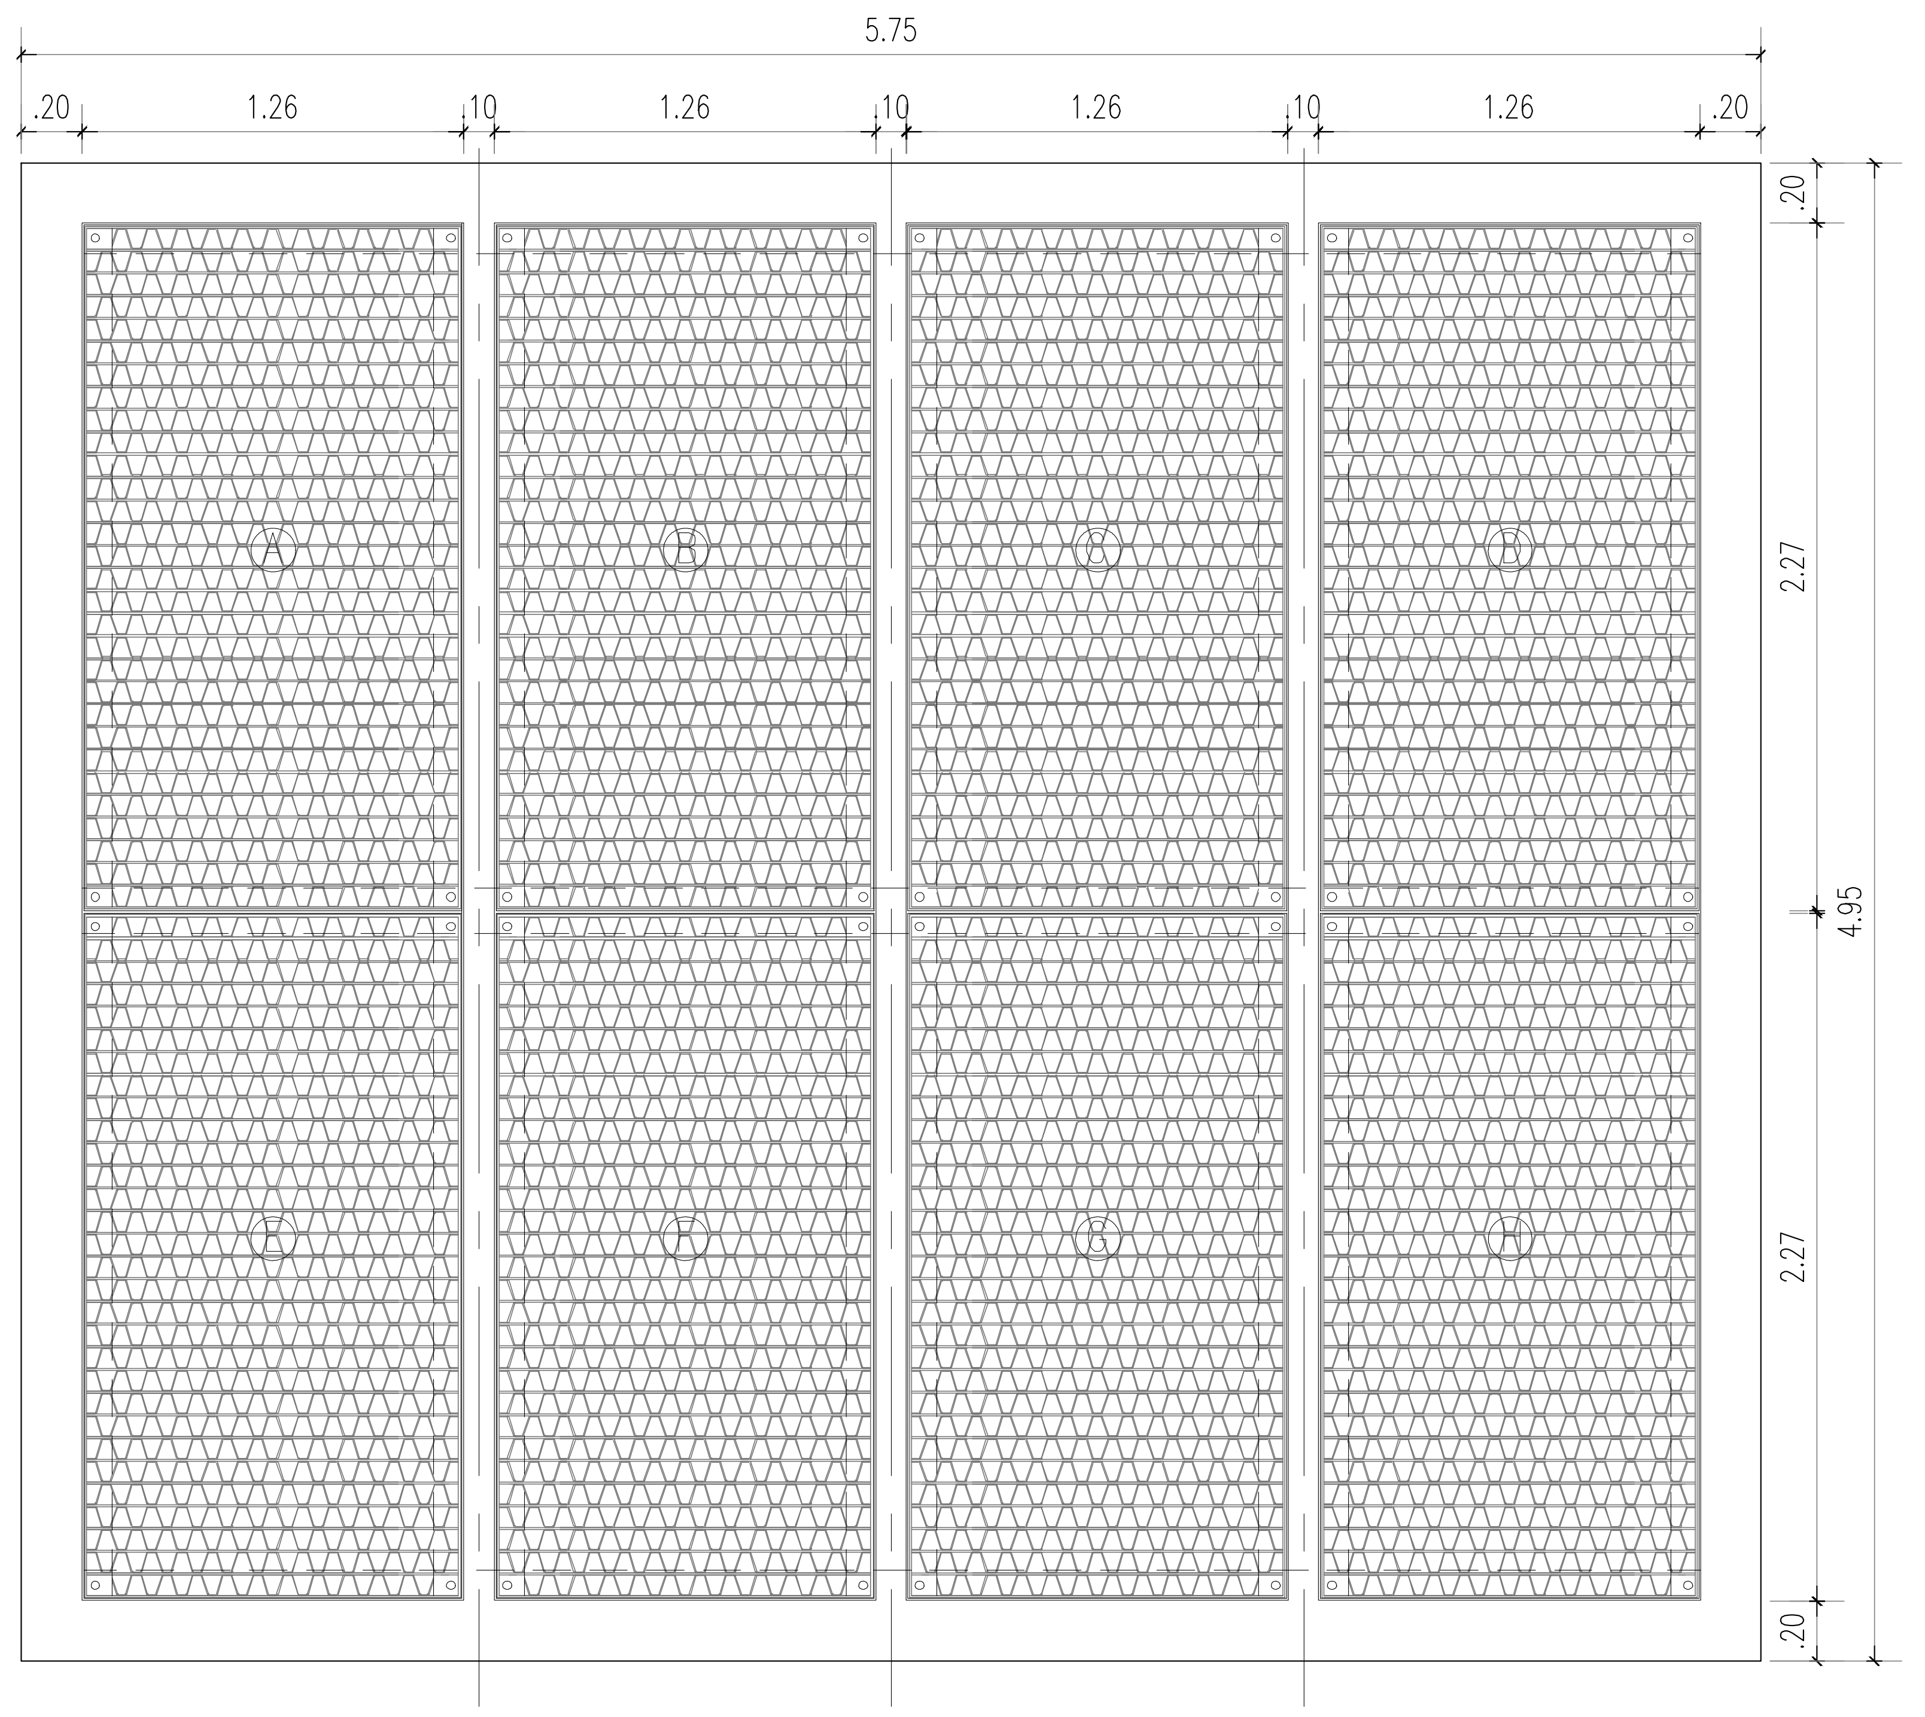

PLANTA 1:10

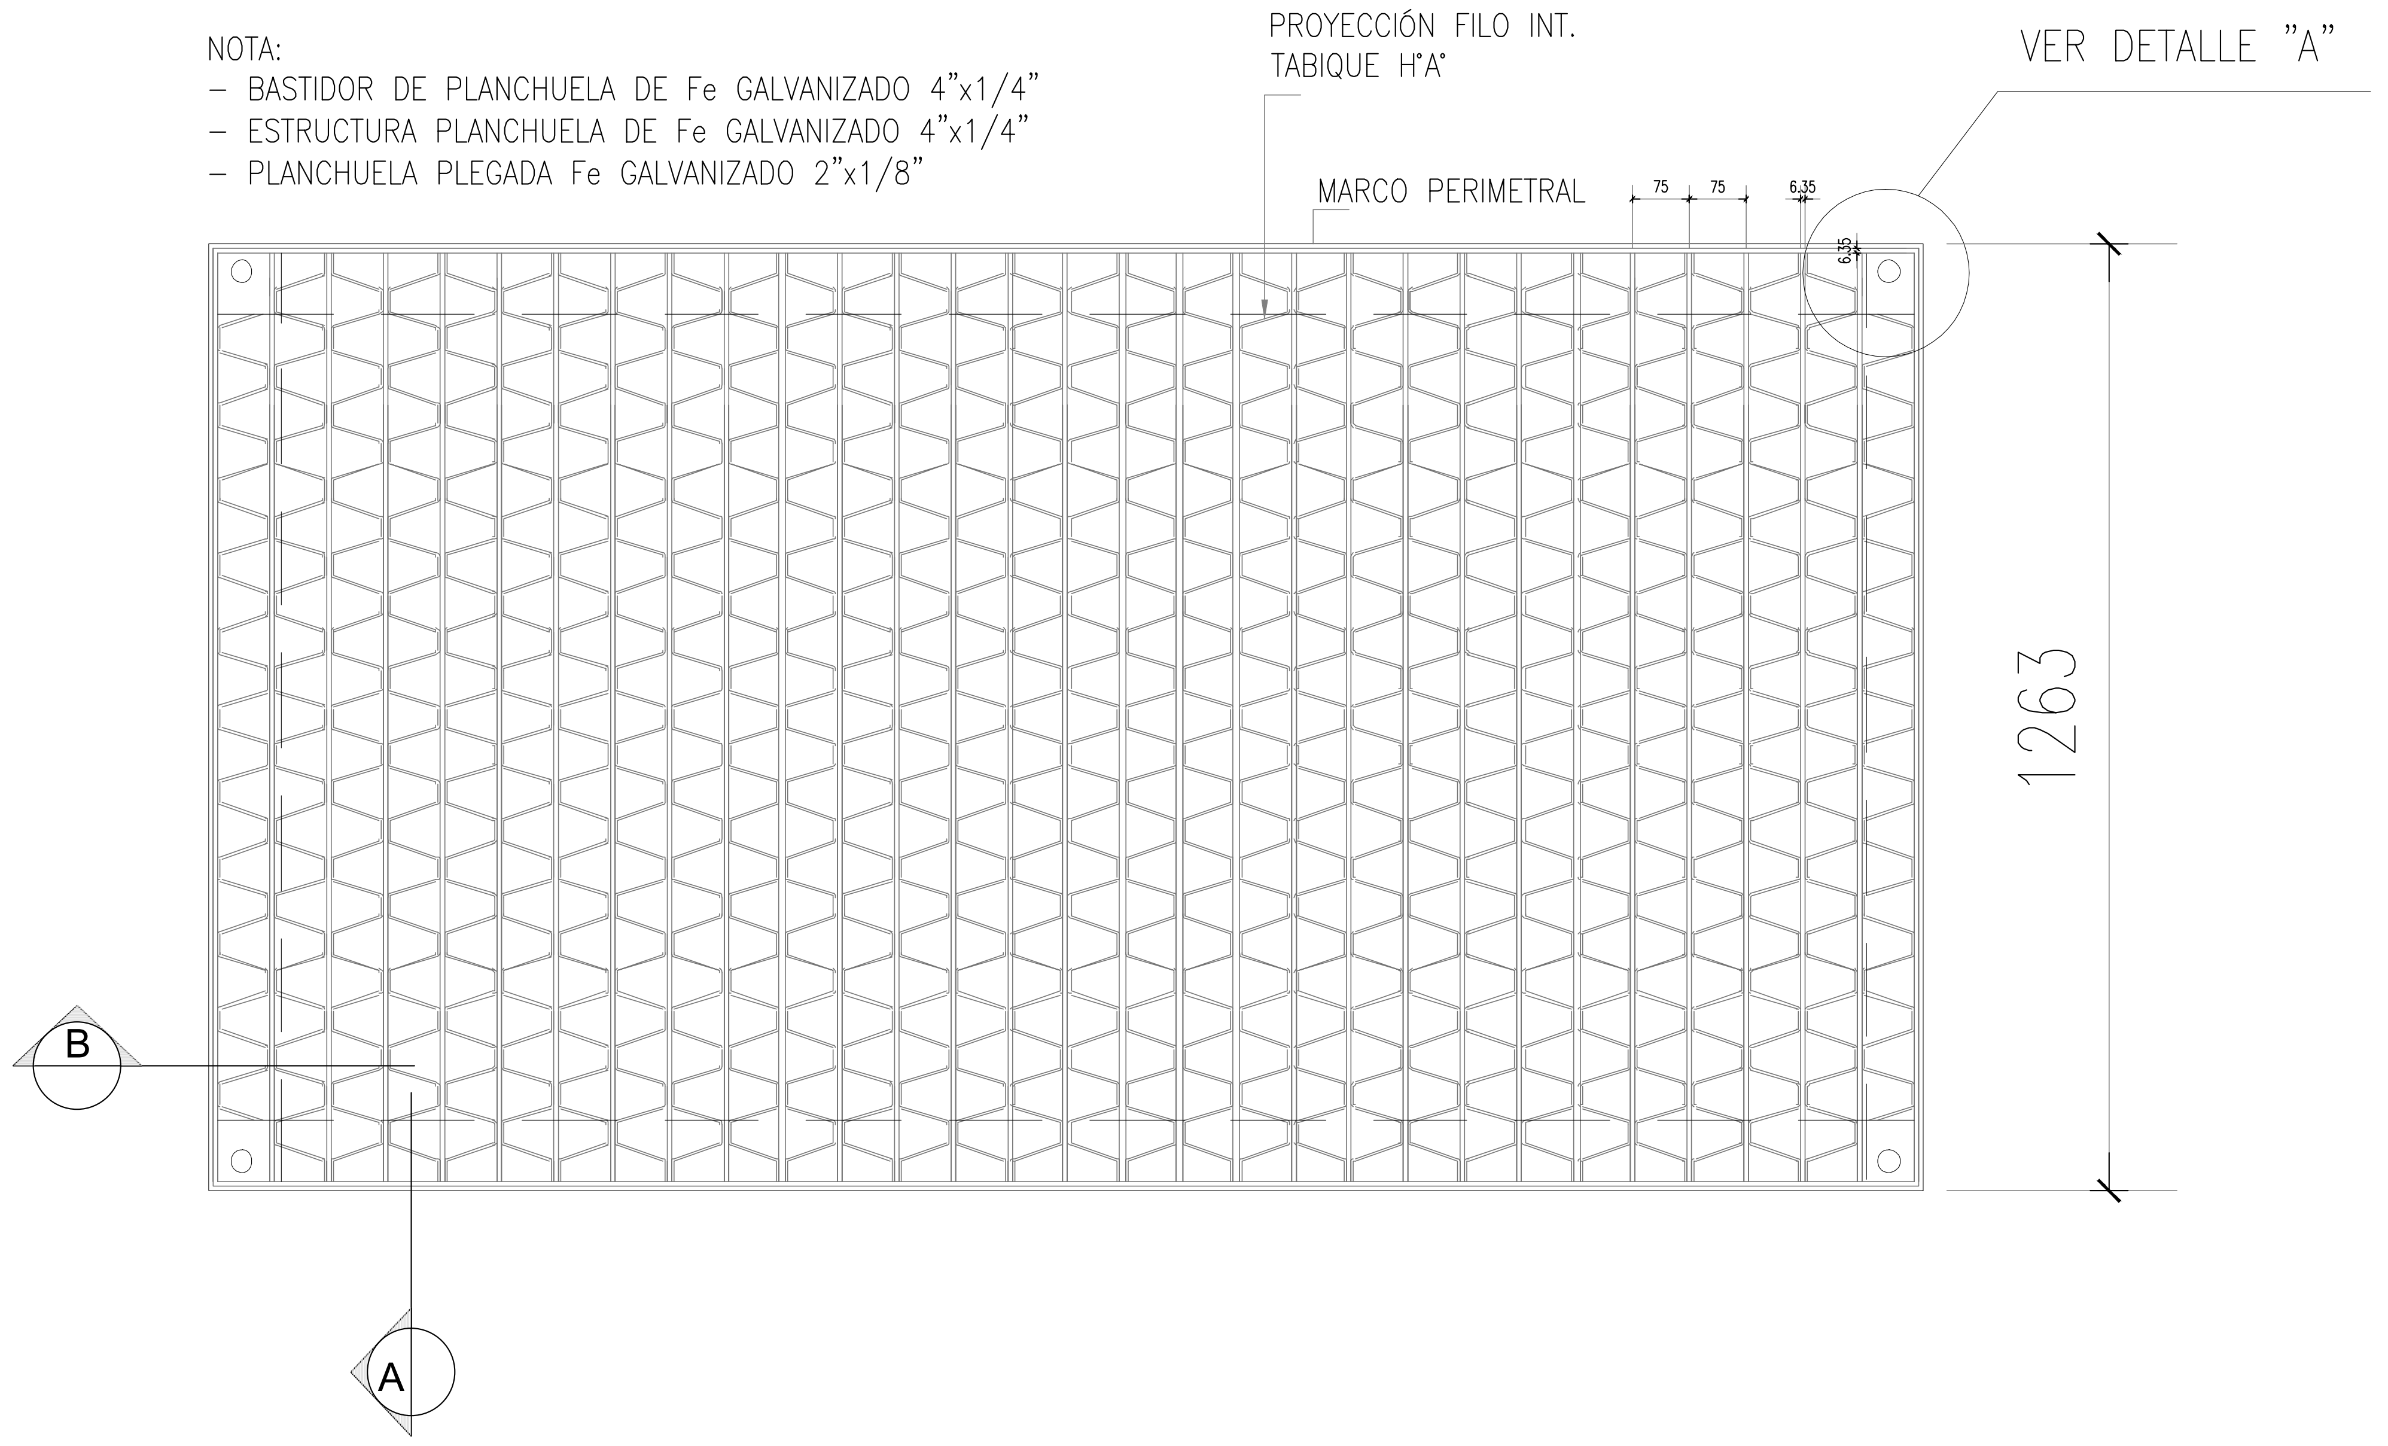

NOTA:
- BASTIDOR DE PLANCHUELA DE Fe GALVANIZADO 4"x1/4"
- ESTRUCTURA PLANCHUELA DE Fe GALVANIZADO 4"x1/4"
- PLANCHUELA PLEGADA Fe GALVANIZADO 2"x1/8"

DETALLE A 1:7.5
ANCLAJE PLANCHUELA

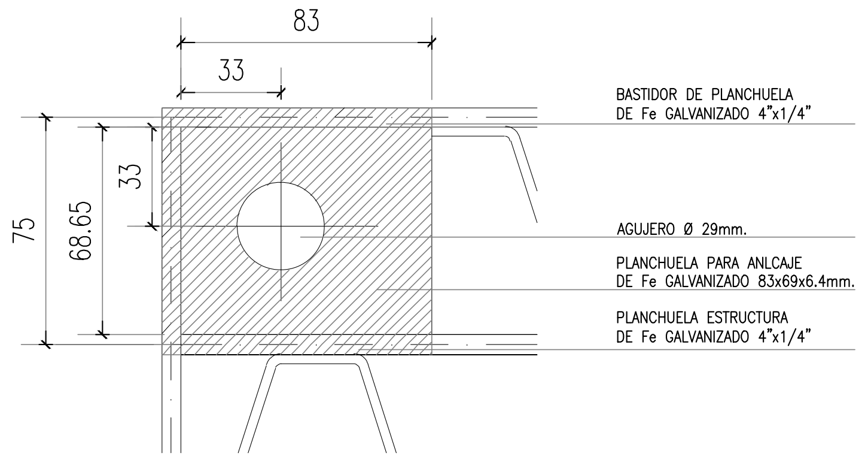

DETALLE 1:7.5
PLEGADO EXTREMOS

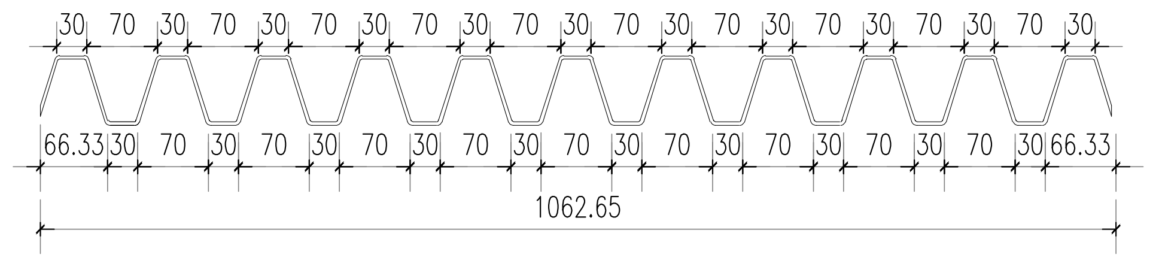

DETALLE 1:7.5
PLEGADO INTERMEDIOS

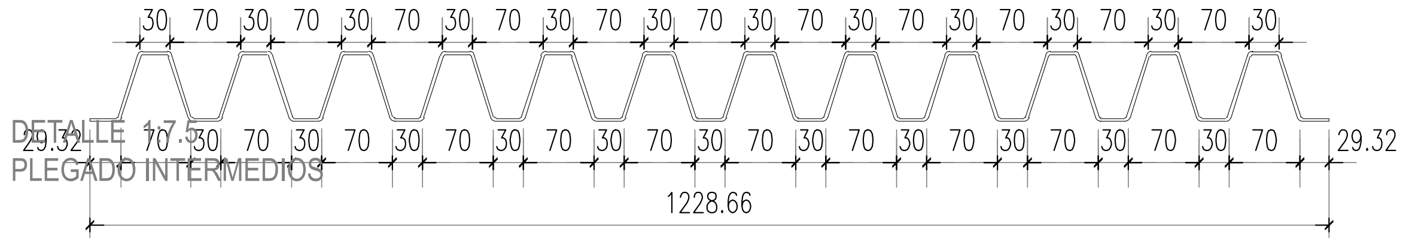

CORTE A-A 1:2.5
APOYO ANCLAJE

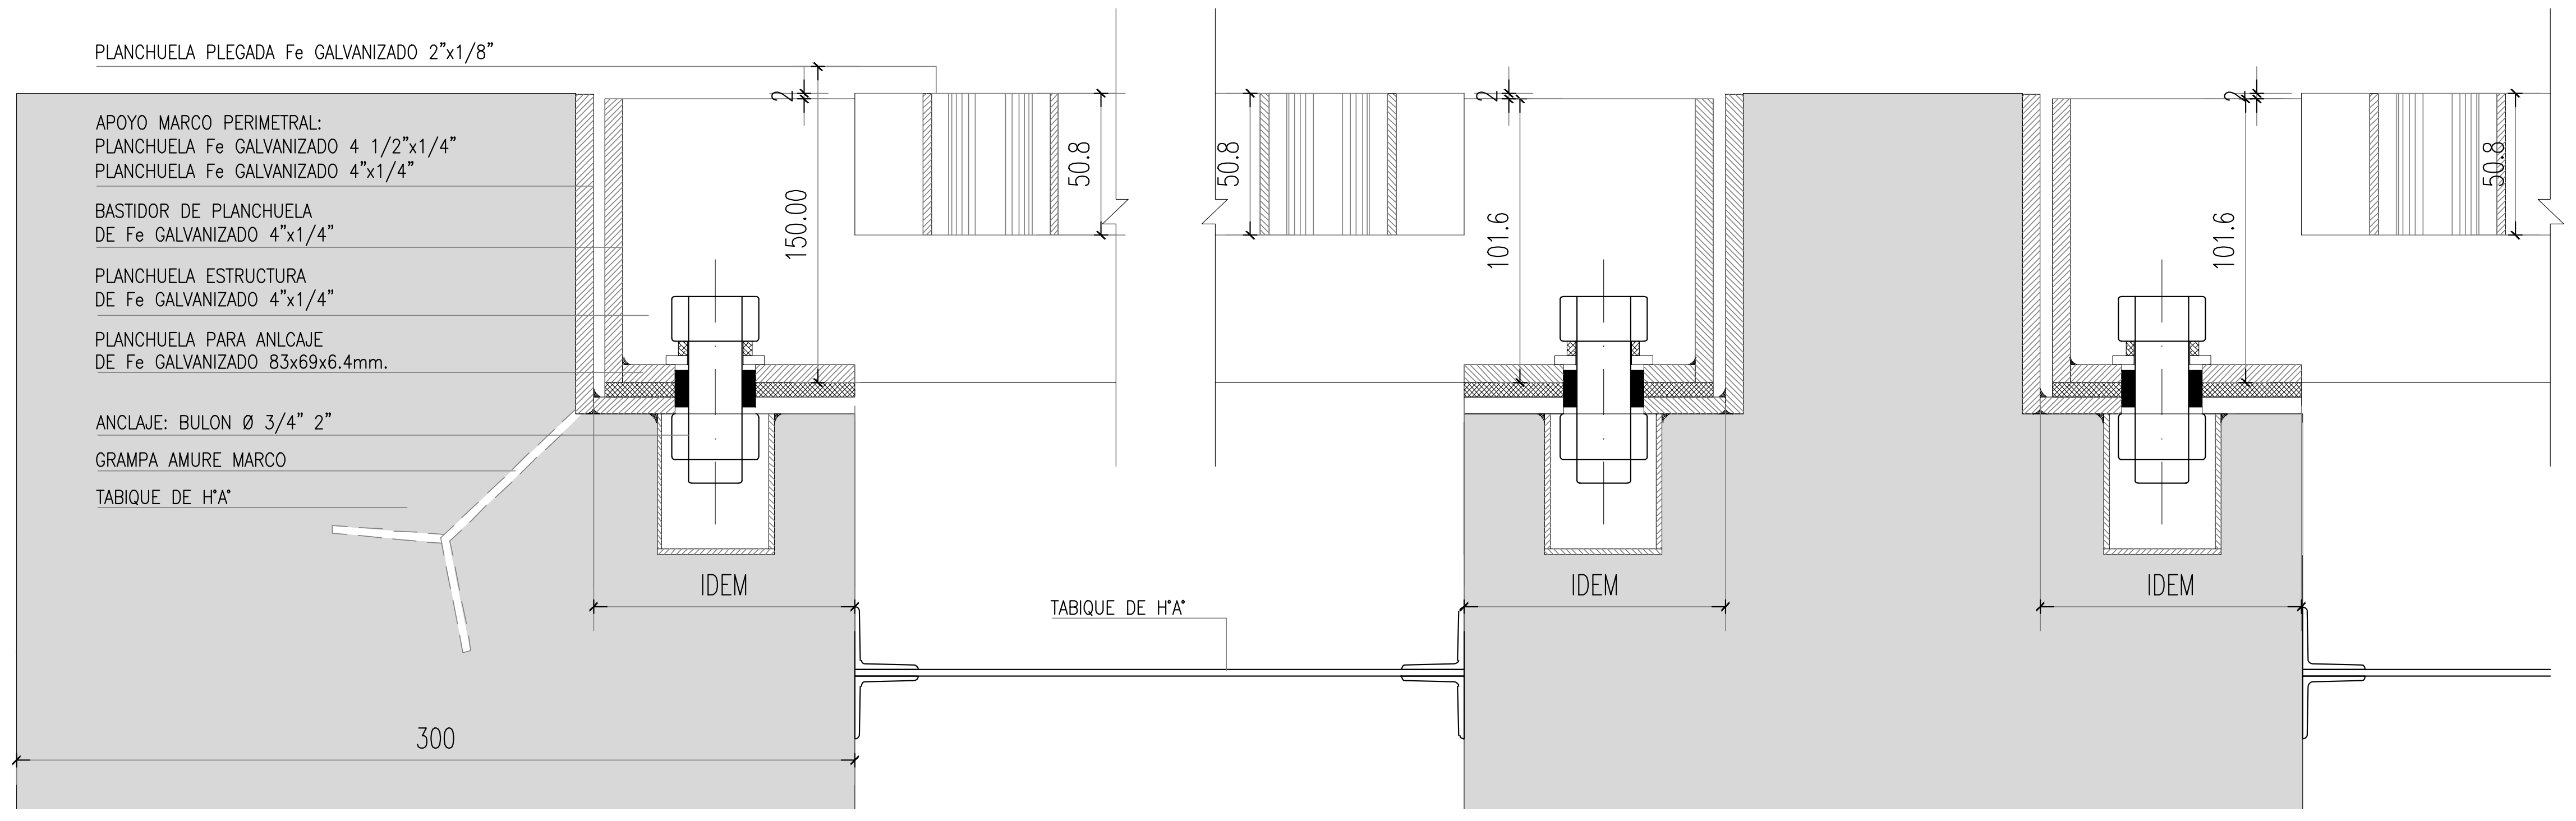

CORTE B-B 1:2.5
APOYO PERFIL

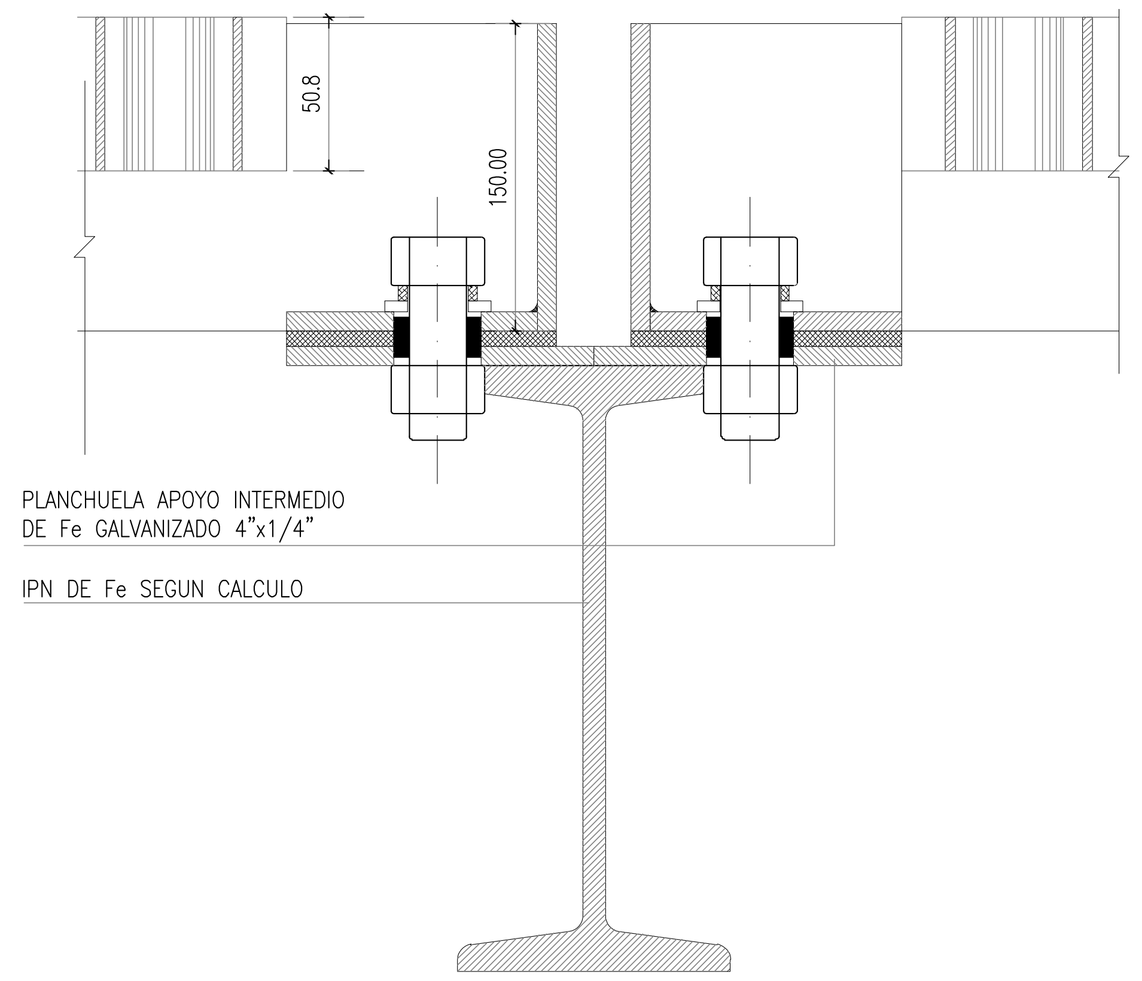

CORTE 1:25

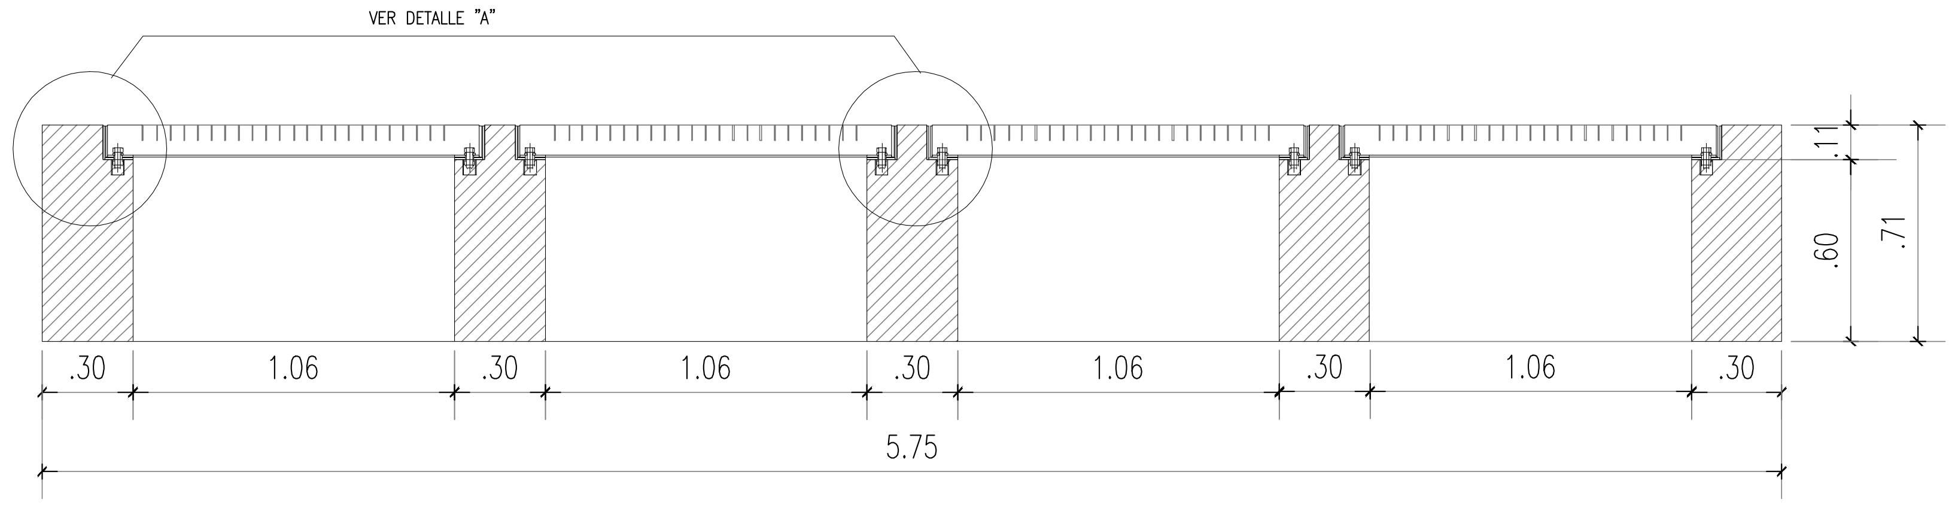

NOTAS: EL PRESENTE PLANO ES INDICATIVO. LA CONTRATISTA CONFECCIONARÁ LOS PLANOS DE DETALLE DEFINITIVO, QUE DEBERÁN SER APROBADOS POR LA D.G.O.INF.U Y LA INSPECCIÓN DE OBRA. EL PLANO PRESENTADO POR LA CONTRATISTA ESTARA EN UN TODO DE ACUERDO CON LA NORMATIVA VIGENTE.
TODAS LAS MEDIDAS Y NIVELES SE VERIFICARÁN EN OBRA POR EL CONTRATISTA.
TODOS LOS DETALLES CONSTRUCTIVOS SERAN COORDINADOS Y COMPATIBILIZADOS EN OBRA.

PLANO NO APTO PARA CONSTRUCCIÓN

MODIFICACIONES:

REVISION	FECHA	DESCRIPCION
00	30-01-2026	EMISIÓN PARA LICITACIÓN
01	10-04-2026	EMISIÓN PARA LICITACIÓN

Gobierno de la Ciudad de Buenos Aires

MINISTERIO DE INFRAESTRUCTURA
SUBSECRETARIA DE PROYECTOS Y OBRAS
DIRECCION GENERAL DE PROYECTOS

DGPRO

Obra: LÍNEA F
Plano Estación Corrientes - Detalle Reja de Extracción
Fecha : 10/04/2026
Eq. de Proyecto: UPU - ATEC - IATASA
Dibujó: JS
PLANO-2026-18240009-GCABA-SSPO
LF-ES-CRR-ARQ-PL-020-R01
Revisó: GV
Escala: 1:25/ 1:10
Plano N°: A020

GOBIERNO DE LA CIUDAD DE BUENOS AIRES
"2026 - Año del 30° Aniversario de la sanción de la Constitución de la Ciudad Autónoma de Buenos Aires"

Hoja Adicional de Firmas
Plano

Número: PLANO-2026-18240009-GCABA-SSPO

Buenos Aires, Viernes 17 de Abril de 2026

Referencia: LF-ES-CRR-ARQ-PL-020_1

El documento fue importado por el sistema GEDO con un total de 1 pagina/s.

Digitally signed by Comunicaciones Oficiales
Date: 2026.04.17 13:11:54 -03:00

Facundo Lombardo
Subsecretario
SUBSECRETARIA PROYECTOS Y OBRAS
MINISTERIO DE MOVILIDAD E INFRAESTRUCTURA

Digitally signed by Comunicaciones Oficiales
Date: 2026.04.17 13:11:55 -03:00