

CORTE LONGITUDINAL B03 - 01 de 03


1 : 100

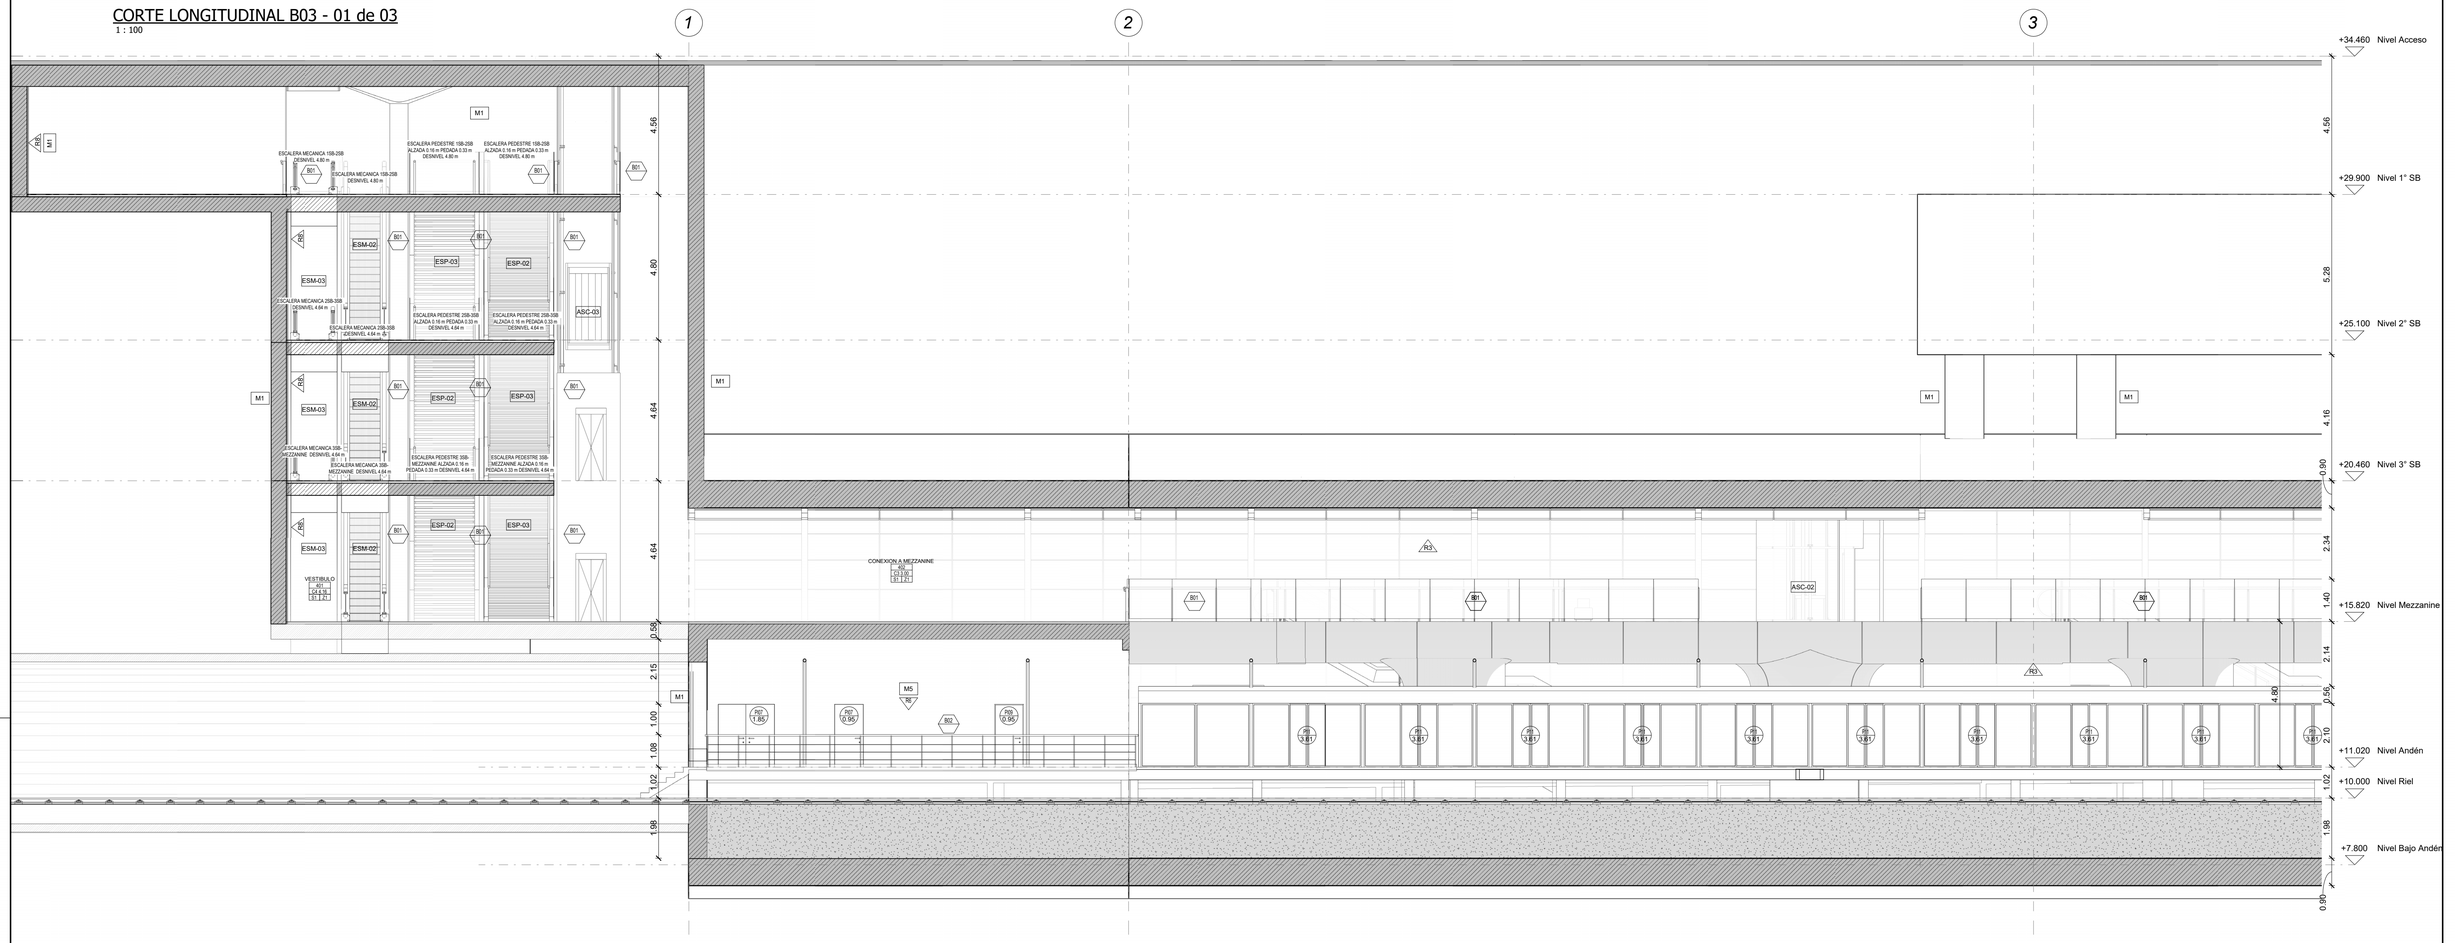


PODOTÁCTIL

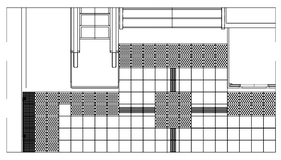

DETALLE ESQUEMA 01

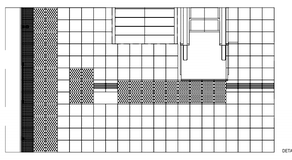

DETALLE ESQUEMA 02

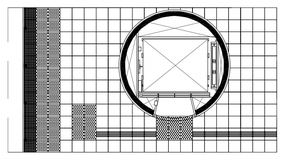

DETALLE ESQUEMA 03

SOLADO TIPO S3
LOS SOLADOS DE PREVENCIÓN SON SEÑALIZACIONES EN PISOS QUE SE UTILIZAN PARA:
-INDICAR COMIENZO Y FINALIZACIÓN DE UNA FRANJA GUÍA.
-SEÑALAR BIFURCACIONES EN UNA FRANJA GUÍA.
-ALERTAR SOBRE SITUACIONES DE RIESGO DE CAÍDAS.
-INFORMAR SOBRE LA EXISTENCIA DE OBSTÁCULOS Y ELEMENTOS DE INFORMACIÓN.
EL SOLADO DE PREVENCIÓN SE COLOCARÁ, SOBRE TODO EL ANCHO, FRENTE DE ESCALERAS Y RAMPAS, EN UNA FRANJA DE 600mm DE LARGO COMO MÍNIMO.
TAMBIÉN E COLOCARÁ EN EL PERÍMETRO DE TODOS LOS BAJO ESCALERAS PERO EN UNA FRANJA DE 300mm.

SOLADO TIPO S4
LAS FRANJAS DE GUÍA PARA DISCAPACITADO VISUALES SON SEÑALIZACIONES EN SOLADOS QUE INDICAN LA DIRECCIÓN DE RECORRIDO, CUYAS ACANALADURAS SIEMPRE DEBEN ESTAR ORIENTADAS EN LA DIRECCIÓN DE LA MARCHA.
4.2.3 SE DEBEN COLOCAR DENTRO DEL VOLUMEN LIBRE DE RIESGO, SEGÚN IRAM 1170:92. A UNA DISTANCIA MÍNIMA DE 600mm DE LOS ELEMENTOS FIJOS, EN GRANDES ESPACIOS SIN PAUTAS DE REFERENCIA PRÓXIMAS.

SOLADO TIPO S5
LOS SOLADOS DE PELIGRO SON SEÑALIZACIONES EN PISOS QUE SE UTILIZAN PARA:
-ALERTAR SOBRE SITUACIONES DE RIESGO DE CAÍDAS POR LA PRESENCIA DE DESNIVELES INFRANQUEABLES, BORDES DE ANDENES, ESCALERAS MECÁNICAS EN EL LÍMITE DE ÁREAS RESTRINGIDAS POR SEGURIDAD.
EL SOLADO DEBERÁ TENER UNA SUPERFICIE DE PELIGRO EN LOS BORDES DE ANDENES.
EN EL BORDE DE ANDÉN EL SOLADO DE PELIGRO SE COMBINARÁ CON DOS FRANJAS DEL SOLADO DE PREVENCIÓN COMO LO INDICA LA FIGURA

NOTACIÓN

LOCAL — INDICA NOMBRE DE LOCAL
N XX — NUMERO DE LOCAL
NIVEL DE PLANTA
CIELORRASO Y ALTURA DEL LOCAL
SOLADO Y ZÓCALO
INDICA NUMERO DE CARPINTERIA
INDICA ANCHO DE VANO
INDICA DETALLE DE SECTOR O LOCAL
DETALLE 01 VER PLANO #.001
INDICA TIPO DE MURO SEGUN PLANILLA
INDICA TERMINACION MURO SEGUN PLANILLA

MUROS

M1 TABIQUE DE HORMIGÓN ARMADO S/ CÁLCULO.

M2 TABIQUE DE HORMIGÓN BLANCO A LA VISTA UNA SOLA CARA, ENCOFRADO FENÓLICO TIPO "GRANDIS" SELECCION DE PRIMERA CALIDAD CON SEPARADORES A 30 MM, PASADORES MODULADOS S/ PLANO DE ENCOFRADO.

M3 TABIQUE COMPUESTO: TABIQUE DE HORMIGÓN ARMADO SEGÚN CÁLCULO + CAMARA DE AIRE 5CM + TABIQUE DE LADRILLO COMÚN DE 12X25X5 APAREJO DE 15 CM.

M4 TABIQUE DE LADRILLO CERÁMICO HUECO DE 12X18X33.

M5 TABIQUE DE LADRILLO CERÁMICO HUECO DE 18X18X33.

M6 TABIQUE DE LADRILLO COMÚN 12X25X5 CM. REVOCADO. • ESTRUCTURA METÁLICA DE CHAPA GALVANIZADA DE 70MM +FIBRA DE VIDRIO (70 MM 35 KG/M3) +SEPARACIÓN DE 3 CM + FIBRA DE VIDRIO (50 MM 35 KG/M3) + 2 PLACAS CEMENTICIAS DE 15 MM. • ESTRUCTURA GALVANIZADA DE 54 MM + FIBRA DE VIDRIO (50 MM 50KG/M3) + CHAPA PERFORADA SEGÚN CÁLCULO SOBRE BASTIDOR DE ALUMINIO.

M7 TABIQUE COMPUESTO: TABIQUE DE HORMIGÓN ARMADO SEGÚN CÁLCULO ESPESOR VARIABLE + CAMARA DE AIRE 5CM + TABIQUE DE LADRILLO CERÁMICO HUECO DE 8X18X33.

M8 TABIQUE COMPUESTO: TABIQUE DE HORMIGÓN ARMADO SEGÚN CÁLCULO ESPESOR VARIABLE + TABIQUE DE LADRILLO CERÁMICO HUECO DE 8X18X33.

M9 TABIQUE DE LADRILLO COMÚN DE 12X25X5, APAREJO DE 15CM

M10 TABIQUE DE HORMIGÓN ARMADO SEG. CÁLCULO + ESTRUCTURA METÁLICA DE CHAPA GALVANIZADA DE 70MM +FIBRA DE VIDRIO (70 MM 35 KG/M3) + 2 PLACAS CEMENTICIAS DE 15 MM + ESTRUCTURA GALVANIZADA DE 54 MM + FIBRA DE VIDRIO (50 MM 50KG/M3) + CHAPA PERFORADA SEGÚN CÁLCULO SOBRE BASTIDOR DE ALUMINIO.

TERMINACIONES Y REVESTIMIENTOS

R1 PLACA GRANÍTICA TIPO TERRAZZO VIBRADA, PRENSADA Y PULIDA PARA TERMINACIÓN E IMPERMEABILIZACIÓN EN OBRA. TERMINACIÓN SATINADA. MEDIDA NOMINAL 397MM/397MM/18MM (TOLERANCIA +/-1MM). CANTO RECTIFICADO. ABSORCIÓN DE AGUA 3.7 IRAM 4176. COLOR DE MASA. COLOR: GRANULOMETRIA Y PORCENTAJE DE PIEDRA A DEFINIR SOBRE MUESTRAS.

R2 PINTURA SILICONADA HIDROFUGA INCOLORA EN BASE ACUOSA "SILEQUIM A" O SIMILAR EQUIVALENTE.

R3 G.R.C. (GLASS FIBER REINFORCED CONCRETE) COMPUESTO DE UNA MATRIZ DE MORTERO ARMADO CON FIBRA DE VIDRIO RESISTENTE A LOS ÁLCALIS. SISTEMA TIPO STUD-FRAME FORMADO POR UNA CÁSCARA DE G.R.C. DE 10 MM A LA QUE SE LE INCORPORA UN BASTIDOR TUBULAR METÁLICO ZINCADO FIJADO MEDIANTE CONECTORES METÁLICOS A DICHA CÁSCARA TIPO PICAST O SIMILAR EQUIVALENTE.

R4 G.R.C. CON AISLACIÓN ACÚSTICA. (GLASS FIBER REINFORCED CONCRETE) COMPUESTO DE UNA MATRIZ DE MORTERO ARMADO CON FIBRA DE VIDRIO RESISTENTE A LOS ÁLCALIS. SISTEMA TIPO STUD-FRAME FORMADO POR UNA CÁSCARA PERFORADA DE G.R.C. DE 10 MM A LA QUE SE LE INCORPORA UN BASTIDOR TUBULAR METÁLICO ZINCADO FIJADO MEDIANTE CONECTORES METÁLICOS A DICHA CÁSCARA CON AISLACIÓN DE LANA DE ROCA 50MM 74 KG/M3 + VELO DE VIDRIO NEGRO. TIPO PICAST O SIMILAR EQUIVALENTE.

R5 PINTURA AL LÁTEX ACRÍLICO. COLOR A DEFINIR.

R6 ESMALTE SINTÉTICO AL AGUA. COLOR A DEFINIR.

R7 BANDEJAS DE ACERO INNOXIDABLE AISI 300 D=2.5MM CON RESPALDO DE LAMINADO FENÓLICO E 15MM COLOCADO CON SISTEMA DE PERCHAS DE ALUMINIO. TERMINACION PULIDO SATINADO.

R8 REVESTIMIENTO CON LIGANTE ACRÍLICO PIEDRA PLAST. DE MOLINOS TARQUINI O SIMILAR EQUIVALENTE. COLOR: PANTERRE BALVANERA.

R9 REVESTIMIENTO ACRÍLICO Y MINERAL GRANALLADO TEXTURA DE BAJA DENSIDAD. DE MOLINOS TARQUINI O SIMILAR EQUIVALENTE. COLOR A DEFINIR.

CIELORRASOS

C1 CIELORRASO SUSPENDIDO DE PLACAS DE ROCA DE YESO RESISTENTE A LA HUMEDAD JUNTA TOMADA COMPUESTO POR PLACA DE ROCA DE YESO DE 12.5MM + ESTRUCTURA METÁLICA DE CHAPA GALVANIZADA N° 24 COMPUESTA POR SOLERAS DE 70 MM Y MONTANTES DE 69 MM SEPARADOS CADA 40 CM C/ REFUERZO PARA ARTEF. DE ILUMINACIÓN.

C2 CIELORRASO SUSPENDIDO DE PLACAS DE ROCA DE YESO JUNTA TOMADA COMPUESTO POR PLACA DE ROCA DE YESO RESISTENTE RF/60 DE 12.5MM + ESTRUCTURA METÁLICA DE CHAPA GALVANIZADA N° 24 COMPUESTA POR SOLERAS DE 70 MM Y MONTANTES DE 69 MM SEPARADOS CADA 40 CM C/ REFUERZO PARA ARTEF. DE ILUMINACIÓN.

C3 GRC (GLASS FIBER REINFORCED CONCRETE) COMPUESTO DE MORTERO Y VIDRIO. ESPESOR 10MM SOBRE BASTIDOR METÁLICO ZINCADO SEGÚN CÁLCULO. TIPO PICAST O SIMILAR EQUIVALENTE.

C4 PINTURA SILICONADA HIDROFUGA INCOLORA EN BASE ACUOSA "SILEQUIM A" O SIMILAR EQUIVALENTE, SOBRE HORMIGÓN A LA VISTA TAPONADO PARA PINTAR.

C5 PINTURA AL LÁTEX ACRÍLICO SOBRE HORMIGÓN A LA VISTA TAPONADO PARA PINTAR. COLOR A DEFINIR.

C6 CIELORRASO MODULAR METÁLICO PERFORADO ACÚSTICO SUSPENDIDO. COLOR A DEFINIR.

C7 LAMAS DE GRC (GLASS FIBER REINFORCED CONCRETE) COMPUESTO DE MORTERO Y VIDRIO. ESPESOR 15CM. ALTURA 100CM. SOBRE BASTIDOR METÁLICO ZINCADO SEGÚN CÁLCULO. TIPO PICAST O SIMILAR EQUIVALENTE.

ZÓCALOS Y SOLIAS


Z1 ZÓCALO SANITARIO H:100MM. RADIO DE CURVATURA 25MM. LARGO 397MM. ANCHO: 50MM. ESPESOR 18MM. EDEN 51.

Z2 ZÓCALO DE ALISADO DE CEMENTO CON COLOR INCORPORADO H:125MM ESPESOR 15MM.


SO1 SOLIA VARILLA ACERO INOXIDABLE "316 MARCA ATRIM O SIMILAR EQUIVALENTE.

SOLADOS


S1 PLACA GRANÍTICA TIPO TERRAZZO VIBRADA, PRENSADA Y PULIDA PARA TERMINACIÓN E IMPERMEABILIZACIÓN EN OBRA. TERMINACIÓN SATINADA. MEDIDA NOMINAL 397MM/397MM/18MM (TOLERANCIA +/-1MM). CANTO RECTIFICADO. ABSORCIÓN DE AGUA 3.7% (IRAM 4176). RESISTENCIA AL DESGASTE 133(IRAM 4159M2). PRUEBA DE IMPACTO: 180 (IRAM/IRCH) ALTURA. RESISTENCIA A LA FLEXIÓN 59KG/CM2(IRAM/IRCH/CIRC). COLOR DE MASA. COLOR: GRANULOMETRIA Y PORCENTAJE DE PIEDRA A DEFINIR SOBRE MUESTRAS.

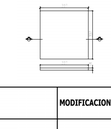

S2 ESCALÓN GRANÍTICO CONTINUO EJECUTADO IN SITU CON AGREGADO DE FIBRAS DE NYLON SOBRE CARPETA DE CONCRETO PARA TERMINACIÓN E IMPERMEABILIZACIÓN EN OBRA. TERMINACIÓN SATINADA. COLOR DE MASA. COLOR: GRANULOMETRIA Y PORCENTAJE DE PIEDRA A DEFINIR SOBRE MUESTRAS. ESPESOR COLADO 10MM CON MALLA DE 150X150MM X150GR/S.

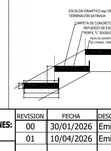


S3 SOLADO DE PREVENCIÓN. PLACA GRANÍTICA TIPO TERRAZZO VIBRADA, PRENSADA Y PULIDA PARA TERMINACIÓN E IMPERMEABILIZACIÓN EN OBRA. EDEN 51. SUPERFICIE TEXTURADA EN FORMA DE BOTONES EN RELIEVE DE 6MM +/- 1MM DE ALTURA, CON DIÁMETRO DE BASE 25MM +/- 5MM. COLOCADOS EN TRESBOLILLO CON UNA DISTANCIA AL CENTRO DE LOS RELIEVES DE 60MM +/- 5MM. COLOR DE MASA. COLOR: GRANULOMETRIA Y PORCENTAJE DE PIEDRA A DEFINIR SOBRE MUESTRAS.

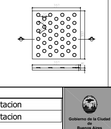

S4 SOLADO GUÍA PARA DISCAPACITADOS VISUALES. PLACA GRANÍTICA TIPO TERRAZZO VIBRADA, PRENSADA Y PULIDA PARA TERMINACIÓN E IMPERMEABILIZACIÓN EN OBRA. EDEN 51. SUPERFICIE TEXTURADA EN FORMA DE TRES BARRAS EN RELIEVE DE SECCIÓN PIRAMIDAL TRUNCA SIN ARISTAS VIVAS DE 4MM DE ALTURA POR 30MM MÁS 4MM DE BASE SEPARADAS 37MM +/-1MM. LA LONGITUD DE LAS BARRAS SERÁ DE 38MM. COLOR DE MASA. COLOR: GRANULOMETRIA Y PORCENTAJE DE PIEDRA A DEFINIR SOBRE MUESTRAS.



S5 PLACA GRANÍTICA TIPO TERRAZZO VIBRADA, PRENSADA Y PULIDA PARA TERMINACIÓN E IMPERMEABILIZACIÓN EN OBRA. EDEN 51. SUPERFICIE ANTIDESLIZANTE CONSTITUIDA POR UNA RELIEVE DE CUADRADOS DE 2MM. COLOR DE MASA. COLOR: GRANULOMETRIA Y PORCENTAJE DE PIEDRA A DEFINIR SOBRE MUESTRAS.

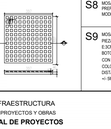

S6 SOLADO DE CEMENTO CON COLOR INCORPORADO Y CON DINCURECEDOR CLIARCITCO. TERMINACIÓN ACEITADO. COLOR A DEFINIR CON TRATAMIENTO ANTI-POLVO, CURADOR Y SELLADOR TRANSPARENTE DMVFLOOR CURE HARD 24.

S7 VIDRIO LAMINADO TRIPLE CAPA 10+10 +10 CON PVB TRANSPARENTE DE 0.76MM. TRATAMIENTO SUPERFICIAL ANTIDESLIZANTE EN BANDAS EJECUTADO MECÁNICAMENTE POR DESGASTADO EN LA TOTALIDAD DE LA SUPERFICIE DE LA PIEZA.

S8 MOSAICO RANURADO. LOSETA GRANÍTICA REFORZADA Y PRENSADA ANTIMOHO E 30M. MODELO 04 PARES. COLOR A DEFINIR.

S9 MOSAICO PODOTÁCTIL. BALDOSA DE PREVENCIÓN. PIEZA PREFABRICADA CEMENTICIA DE ADOHERACH E.30M. SUPERFICIE DE TEXTURADA EN FORMA DE BOTONES EN RELIEVE DE 5MM +/- 1MM DE ALTURA, CON DIÁMETRO DE BASE 35MM +/- 5MM, COLOCADOS EN TRESBOLILLO CON UNA DISTANCIA AL CENTRO DE LOS RELIEVES DE 60MM +/- 5MM. COLOR AMARILLO.

S10 MOSAICO PODOTACTIL. BALDOSA GUÍA. PIEZA PREFABRICADA CEMENTICIA DE ADOHERACH E.30M. SUPERFICIE TEXTURADA EN FORMA DE CINCO BARRAS EN RELIEVE DE SECCIÓN PIRAMIDAL TRUNCA SIN ARISTAS VIVAS DE 4MM DE ALTURA POR 30MM MÁS 4MM DE BASE SEPARADAS 37MM +/- 1MM. LA LONGITUD DE LAS BARRAS SERÁ DE 38MM. COLOR A DEFINIR.

S11 PAVIMENTO CONTINUO ASFALTICO EN CALIENTE EXISTENTE

S12 PAVIMENTO PEATONAL DE HORMIGÓN ESTRIADO (PEINADO).

S13 SOLADO EXISTENTE. (NIC).

S14 PORFIDO PATAGONICO COLOR GRIS 100MX50CM E: 4 A 6CM

S15 BALDOSA DE PÓRFIDO CORTE A DISCO GRIS, ANCHO 40CM X LARGO VARIABLE E: 2 A 3CM.

NOTAS:

EL PRESENTE PLANO ES INDICATIVO. LA CONTRATISTA CONFECCIONARÁ LOS PLANOS DE DETALLE ESTRICTOS, QUE DEBERÁN SER APROBADOS POR LA D.G.O.SM U Y LA INSPECCIÓN DE OBRA. EL PLANO PRESENTADO POR LA CONTRATISTA ESTARÁ EN UN TODO DE ACUERDO CON LA NORMATIVA VIGENTE, TENDRÁ LAS MEDIDAS Y DEMÁS DE VERIFICARSE EN OBRA POR LA CONTRATISTA.
TODOS LOS DETALLES CONSTRUCTIVOS DEBERÁN COORDINARSE Y CONFRONTARSE EN OBRA.

PLANO NO APTO PARA CONSTRUCCIÓN

MODIFICACIONES:	REVISION	FECHA	DESCRIPCION
	00	30/01/2026	Emision para Licitacion
	01	10/04/2026	Emision para Licitacion

Gobierno de la Ciudad Buenos Aires

MINISTERIO DE INFRAESTRUCTURA
SUBSECRETARIA DE PROYECTOS Y OBRAS
DIRECCION GENERAL DE PROYECTOS

DGPRO

Obra: LÍNEA F			Plano
Plano ESTACION CORRIENTES - CORTE LONGITUDINAL B03 - 01 de 03			PLANO-2026-18241704-GCABA-SSPO LF-ES-CRR-ARQ-PL-014-01-R01
Fecha :10/04/2026	Eq. de Proyecto: UPU - ATEC - IATASA	Dibujó: J.S.	Revisó: G.V.	Escala: 1 : 100	A014-01

G O B I E R N O DE LA C I U D A D DE B U E N O S A I R E S

"2026 - Año del 30° Aniversario de la sanción de la Constitución de la Ciudad Autónoma de Buenos Aires"

Hoja Adicional de Firmas
Plano

Número: PLANO-2026-18241704-GCABA-SSPO

Buenos Aires, Viernes 17 de Abril de 2026

Referencia: LF-ES-CRR-ARQ-PL-014-01_1

El documento fue importado por el sistema GEDO con un total de 1 pagina/s.

Digitally signed by Comunicaciones Oficiales
Date: 2026.04.17 13:16:00 -03:00

Facundo Lombardo
Subsecretario
SUBSECRETARIA PROYECTOS Y OBRAS
MINISTERIO DE MOVILIDAD E INFRAESTRUCTURA

Digitally signed by Comunicaciones Oficiales
Date: 2026.04.17 13:16:01 -03:00