
PLANTA NIVEL MEZZANINE - PARTE 3

ESCALA 1:100

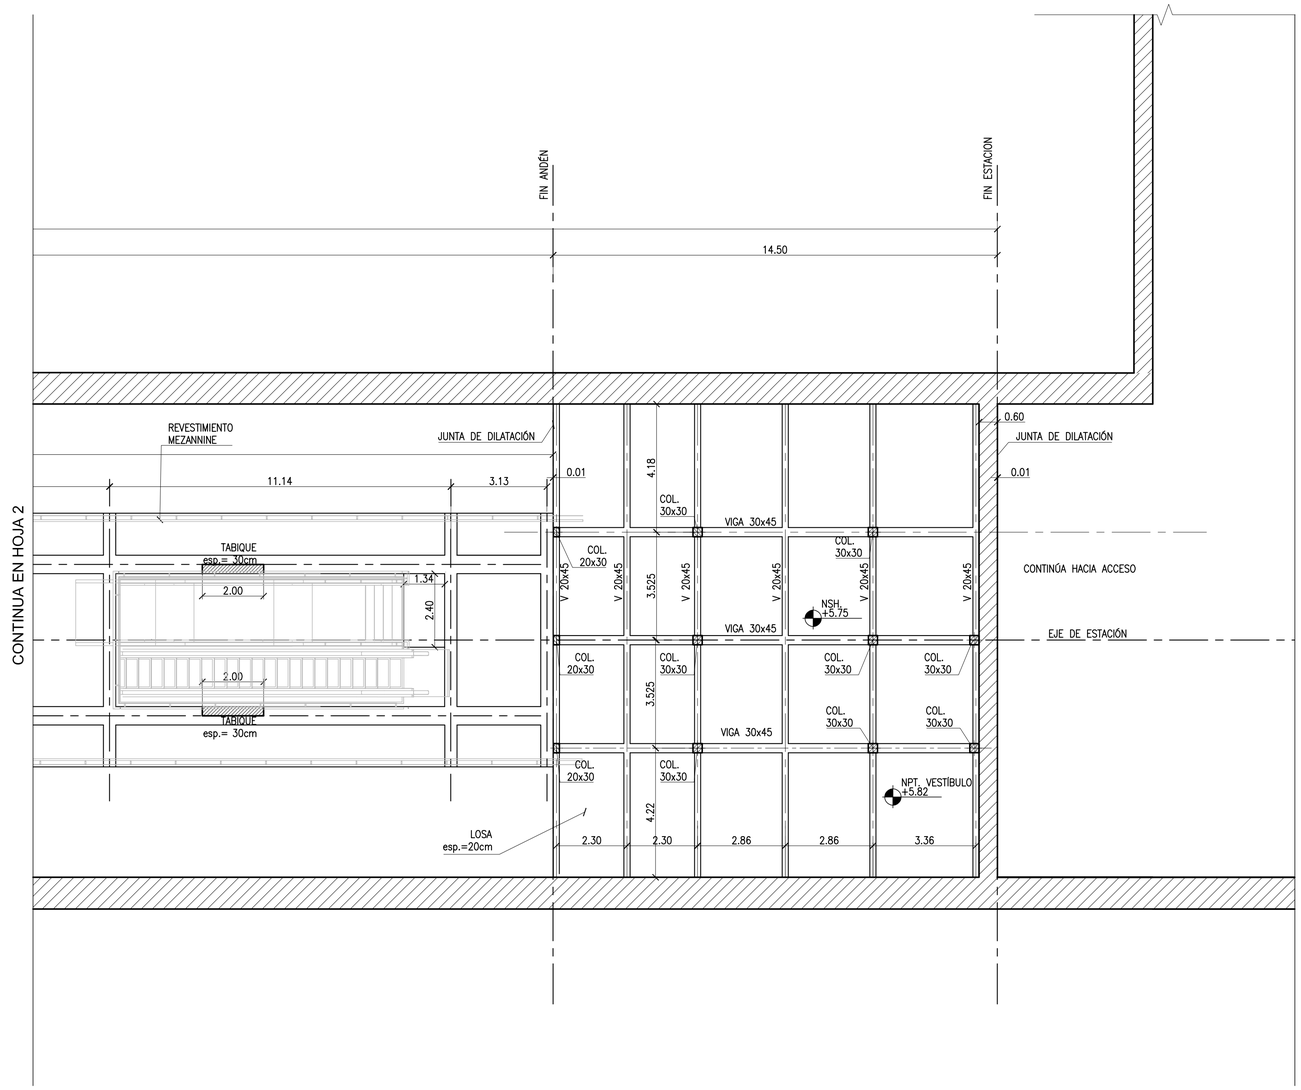

NOTAS:

COTAS SEGUN SISTEMA DE COORDENADAS DE LA CIUDAD DE BUENOS AIRES
NIVELES Y MEDIDAS EN METROS SALVO INDICACION CONTRARIA
DIMENSIONES EN CENTIMETROS

MATERIALES:

HORMIGON CAVERNA ESTACION: H-35
HORMIGON ESTRUCTURAS: H-30
HORMIGON RELLENO: H-25

ACERO PARA HORMIGON ARMADO: ADN420

REFERENCIAS:
NPT: NIVEL PISO TERMINADO

NOTAS:

EL PRESENTE PLANO ES INDICATIVO. LA CONTRATISTA CONFECCIONARÁ LOS PLANOS DE DETALLE DEFINITIVO, QUE DEBERÁN SER APROBADOS POR LA D.G.DIR.U Y LA INSPECCIÓN DE OBRA. EL PLANO PRESENTADO POR LA CONTRATISTA ESTARÁ EN UN TODO DE ACUERDO CON LA NORMATIVA VIGENTE.
TODAS LAS MEDIDAS Y NIVELES SE VERIFICARAN EN OBRA POR EL CONTRATISTA.
TODOS LOS DETALLES CONSTRUCTIVOS SERAN COORDINADOS Y CONFIRMADOS EN OBRA

PLANO NO APTO PARA CONSTRUCCION.

NOTA

MODIFICACIONES:

REVISION	FECHA	DESCRIPCION
0	20/02/26	EMISION INICIAL

MINISTERIO DE INFRAESTRUCTURA
SUBSECRETARIA DE PROYECTOS Y OBRAS
DIRECCION GENERAL DE PROYECTOS

DGPRO

Obra: LINEA F				PLANO-2026-18246865-GCABA-SSPRO N°	3/3
Plano: Estación Pacífico - Encofrado Planta de Mezzanine - Parte 03 de 03				LF-ES-PAC-EST-PL-003-03	
Fecha: 20/02/2026	Eq. de Proyecto: UPU-ATEC-IATASA	Dibujó: L.G.	Revisó: F.O.	Escala: 1:100	

G O B I E R N O DE LA C I U D A D DE B U E N O S A I R E S

"2026 - Año del 30° Aniversario de la sanción de la Constitución de la Ciudad Autónoma de Buenos Aires"

Hoja Adicional de Firmas
Plano

Número: PLANO-2026-18246865-GCABA-SSPO

Buenos Aires, Viernes 17 de Abril de 2026

Referencia: LF-ES-PAC-EST-PL-003-03_0

El documento fue importado por el sistema GEDO con un total de 1 pagina/s.

Digitally signed by Comunicaciones Oficiales
Date: 2026.04.17 13:29:41 -03:00

Facundo Lombardo
Subsecretario
SUBSECRETARIA PROYECTOS Y OBRAS
MINISTERIO DE MOVILIDAD E INFRAESTRUCTURA

Digitally signed by Comunicaciones Oficiales
Date: 2026.04.17 13:29:41 -03:00