

CORTE TRANSVERSAL 1

ESCALA 1:100

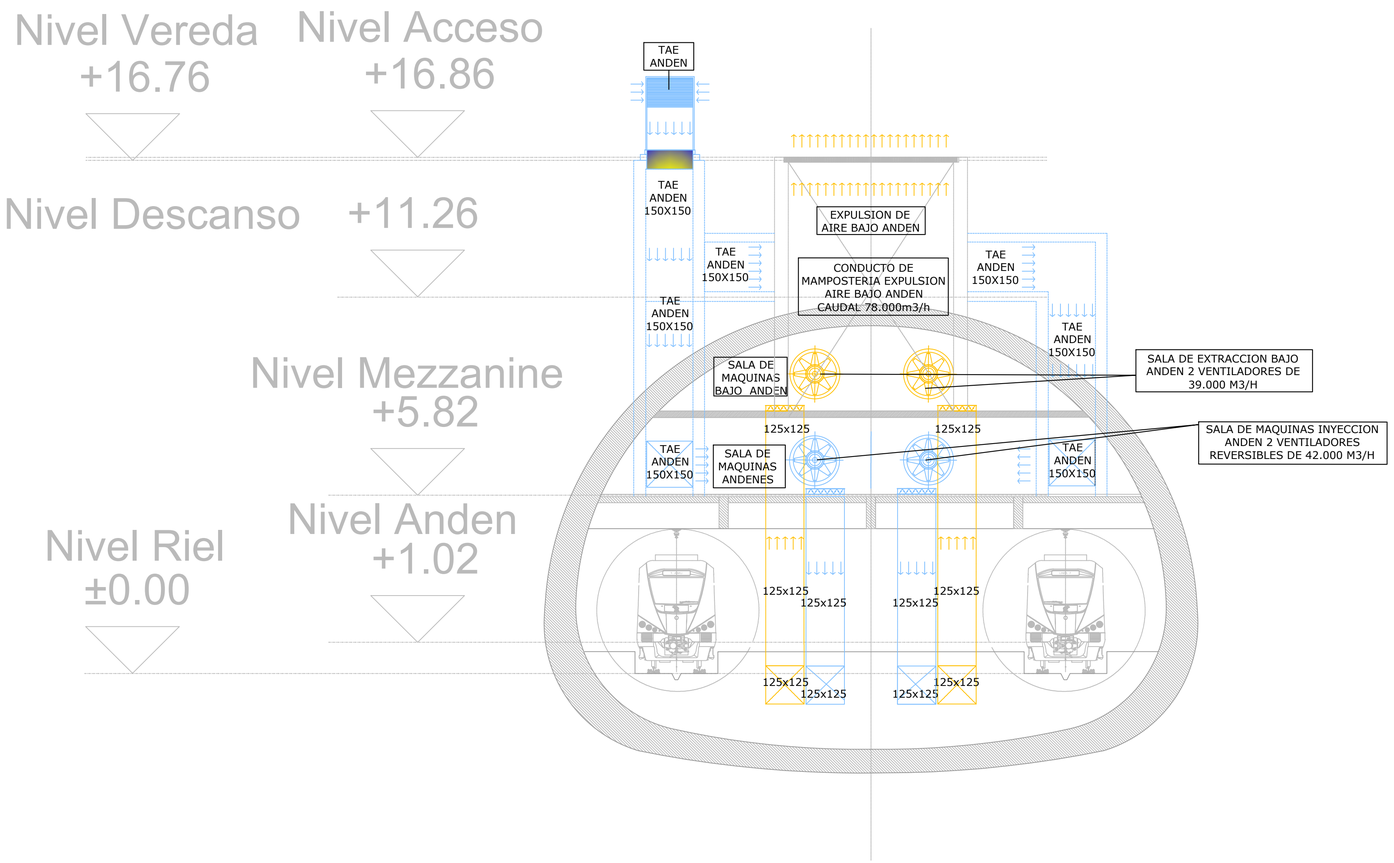

CROQUIS UBICACION

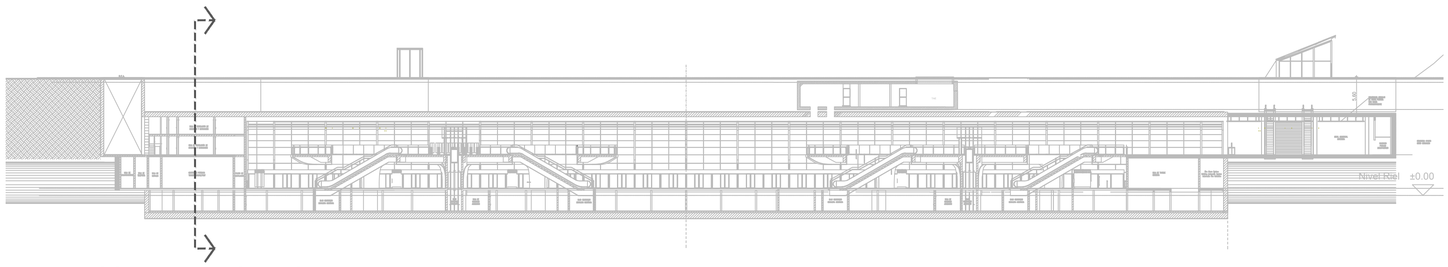

CORTE TRANSVERSAL 1

NOTAS:
1- PREVIO A INICIO DE OBRA EL CONTRATISTA CONFECCIONARA Y PRESENTARA LOS DETALLES EJECUTIVOS QUE SERAN APROBADOS POR LA D.G.DP.U.Y LA INSPECCION DE OBRA. EL PLANO PRESENTADO POR LA CONTRATISTA ESTARA EN UN TODO DE ACUERDO CON LA NORMATIVA VIGENTE.
TODAS LAS MEDIDAS Y NIVELES SE VERIFICARAN EN OBRA POR EL CONTRATISTA.
TODOS LOS DETALLES CONSTRUCTIVOS SERAN COORDINADOS Y COMPATIBILIZADOS EN OBRA

PLANO NO APTO PARA CONSTRUCCION.

MODIFICACIONES:

REVISION	FECHA	DESCRIPCION
0	20/02/2026	EMISIÓN PARA LICITACIÓN

Gobierno de la Ciudad de Buenos Aires

MINISTERIO DE INFRAESTRUCTURA
SUBSECRETARIA DE PROYECTOS Y OBRAS
DIRECCION GENERAL DE PROYECTOS

DGPRO

Obra: LÍNEA F					PLANO-2026-18268381-GCABA-SSPO	Hoja N°
Plano: INSTALACIÓN TERMOMECÁNICA - CORTES TRANSVERSALES					LF-ES-PAC-VEN-PL-007-01	1/2
Fecha: 20/02/2026	Eq. de Proyecto: UPU-ATEC-IATASA	Dibujó: M.S.	Revisó: J.C.	Escala: 1:100		

25/3/2026 16:56 p. m.
LF-ES-PAC-VEN-PL_007-01.dwg

G O B I E R N O DE LA C I U D A D DE B U E N O S A I R E S

"2026 - Año del 30° Aniversario de la sanción de la Constitución de la Ciudad Autónoma de Buenos Aires"

Hoja Adicional de Firmas
Plano

Número: PLANO-2026-18268381-GCABA-SSPO

Buenos Aires, Viernes 17 de Abril de 2026

Referencia: LF-ES-PAC-VEN-PL-007-01_0

El documento fue importado por el sistema GEDO con un total de 1 pagina/s.

Digitally signed by Comunicaciones Oficiales
Date: 2026.04.17 14:30:34 -03:00

Facundo Lombardo
Subsecretario
SUBSECRETARIA PROYECTOS Y OBRAS
MINISTERIO DE MOVILIDAD E INFRAESTRUCTURA

Digitally signed by Comunicaciones Oficiales
Date: 2026.04.17 14:30:34 -03:00