CORTE LONGITUDINAL

ESCALA 1:100

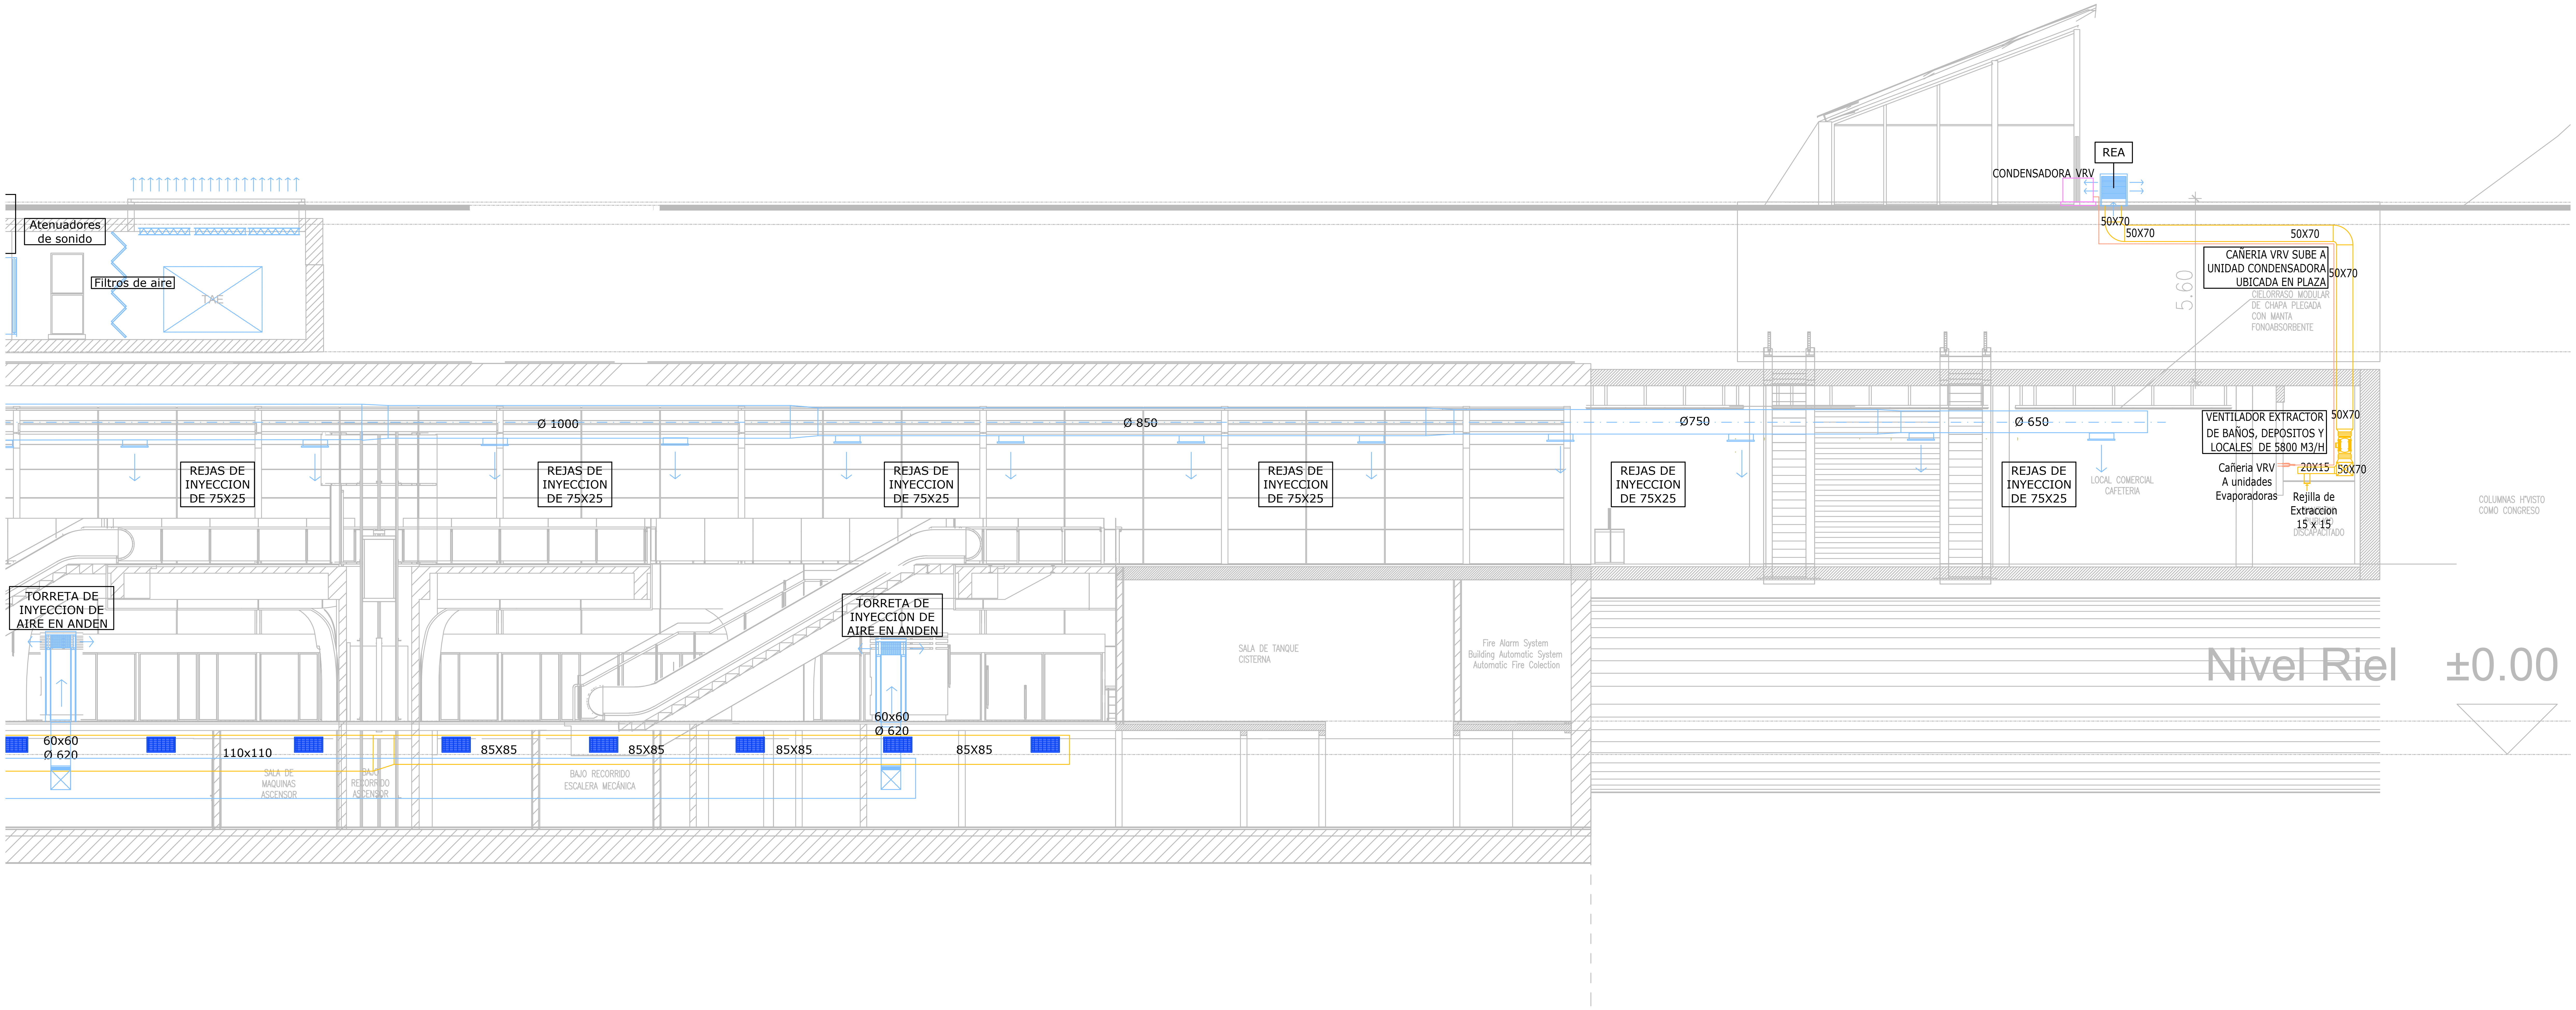
Atenuadores de sonido
Filtros de aire
TAE
Ø 1000
Ø 850
Ø750
Ø 650
REJAS DE INYECCION DE 75X25
REJAS DE INYECCION DE 75X25
REJAS DE INYECCION DE 75X25
REJAS DE INYECCION DE 75X25
REJAS DE INYECCION DE 75X25
REJAS DE INYECCION DE 75X25
TORRETA DE INYECCION DE AIRE EN ANDEN
TORRETA DE INYECCION DE AIRE EN ANDEN
60x60
Ø 620
60x60
Ø 620
110x110
85X85
85X85
85X85
85X85
SALA DE MAQUINAS ASCENSOR
BAJO RECORRIDO ASCENSOR
BAJO RECORRIDO ESCALERA MECÁNICA
SALA DE TANQUE CISTERNA
Fire Alarm System
Building Automatic System
Automatic Fire Colection
REA
CONDENSADORA VRV
50X70
50X70
50X70
50X70
50X70
50X70
CAÑERIA VRV SUBE A UNIDAD CONDENSADORA UBICADA EN PLAZA
CIELORRASO MODULAR DE CHAPA PLEGADA CON MANTA FONOABSORBENTE
5.60
VENTILADOR EXTRACTOR DE BAÑOS, DEPOSITOS Y LOCALES DE 5800 M3/H
Cañeria VRV A unidades Evaporadoras
20X15
Rejilla de Extraccion 15 x 15
SANITARIO PUBLICO DISCAPACITADO
LOCAL COMERCIAL CAFETERIA
COLUMNAS H°VISTO COMO CONGRESO
Nivel Riel ±0.00

CROQUIS UBICACION

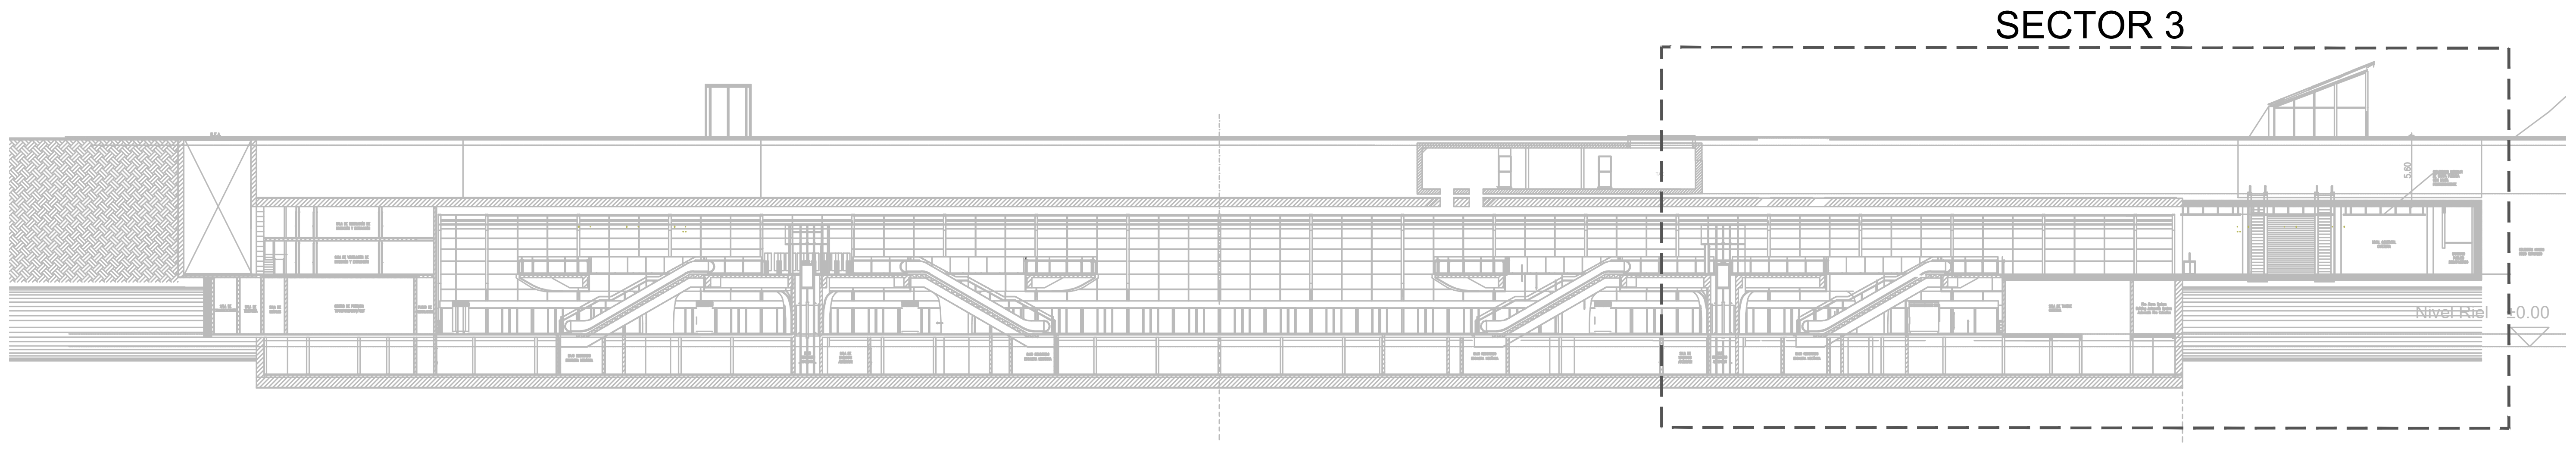

NOTAS:

EL PRESENTE PLANO ES INDICATIVO. LA CONTRATISTA CONFECCIONARA LOS PLANOS DE DETALLE DEFINITIVO, QUE DEBERAN SER APROBADOS POR LA D.G.O.INF.U Y LA INSPECCION DE OBRA. EL PLANO PRESENTADO POR LA CONTRATISTA ESTARA EN UN TODO DE ACUERDO CON LA NORMATIVA VIGENTE.
TODAS LAS MEDIDAS Y NIVELES SE VERIFICARAN EN OBRA POR EL CONTRATISTA.
TODOS LOS DETALLES CONSTRUCTIVOS SERAN COORDINADOS Y COMPATIBILIZADOS EN OBRA

PLANO NO APTO PARA CONSTRUCCION.

MODIFICACIONES:

REVISION	FECHA	DESCRIPCION
0	20/02/2026	EMISIÓN PARA LICITACIÓN

Gobierno de la Ciudad de Buenos Aires

MINISTERIO DE INFRAESTRUCTURA
SUBSECRETARIA DE PROYECTOS Y OBRAS
DIRECCION GENERAL DE PROYECTOS

DGPRO

Obra: LÍNEA F
Plano: INSTALACIÓN TERMOMECÁNICA - CORTE LONGITUDINAL
Fecha: 20/02/2026
Eq. de Proyecto: UPU-ATEC-IATASA
Dibujó: M.S.
PLANO-2026-18268496-GCABA-SSPO
Plano N°
LF-ES-PAC-VEN-PL-006-03
3/3
Revisó: J.C.
Escala: 1:100

25/3/2026 15:47 p. m.
LF-ES-PAC-VEN-PL-006-03.dwg

GOBIERNO DE LA CIUDAD DE BUENOS AIRES
"2026 - Año del 30° Aniversario de la sanción de la Constitución de la Ciudad Autónoma de Buenos Aires"

Hoja Adicional de Firmas
Plano

Número: PLANO-2026-18268496-GCABA-SSPO

Buenos Aires, Viernes 17 de Abril de 2026

Referencia: LF-ES-PAC-VEN-PL-006-03_0

El documento fue importado por el sistema GEDO con un total de 1 pagina/s.

Digitally signed by Comunicaciones Oficiales
Date: 2026.04.17 14:30:55 -03:00

Facundo Lombardo
Subsecretario
SUBSECRETARIA PROYECTOS Y OBRAS
MINISTERIO DE MOVILIDAD E INFRAESTRUCTURA

Digitally signed by Comunicaciones Oficiales
Date: 2026.04.17 14:30:55 -03:00