

PLANTA NIVEL BAJO ANDÉN

ESCALA 1:100

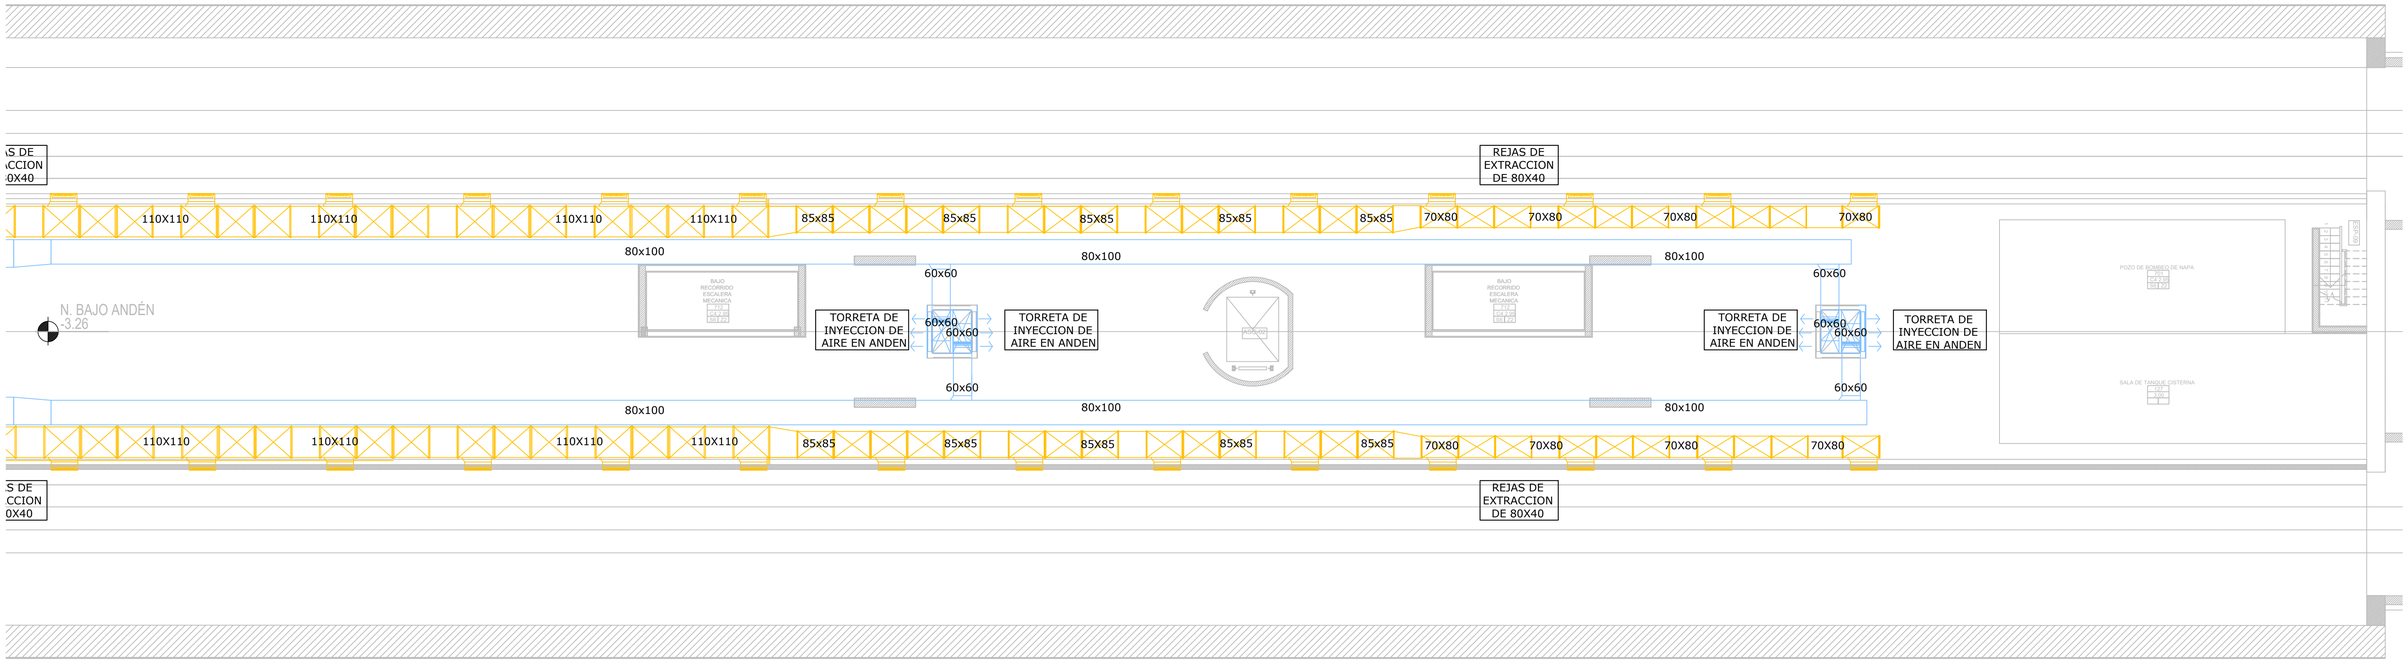

CROQUIS UBICACION

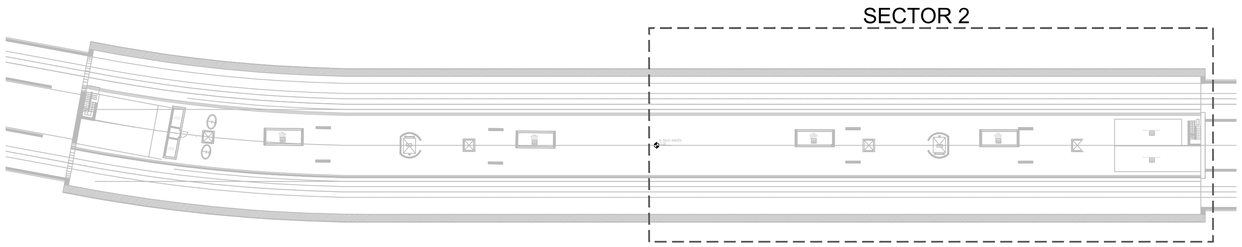

NOTAS:
1- PREVIO A CUALQUIER TIPO DE CONSTRUCCIÓN, DEBERÁN SER APROBADOS POR LA D.G.M.U.Y LA INSPECCION DE OBRA. EL PLANO PRESENTADO POR LA CONTRATISTA ESTARA EN UN TODO DE ACUERDO CON LA NORMATIVA VIGENTE.
TODAS LAS MEDIDAS Y NIVELES SE VERIFICARAN EN OBRA POR EL CONTRATISTA.
TODOS LOS DETALLES CONSTRUCTIVOS SERAN COORDINADOS Y COMPATIBILIZADOS EN OBRA

PLANO NO APTO PARA CONSTRUCCION.

MODIFICACIONES:

REVISION	FECHA	DESCRIPCION
0	20/02/2026	EMISIÓN PARA LICITACIÓN

MINISTERIO DE INFRAESTRUCTURA
SUBSECRETARIA DE PROYECTOS Y OBRAS
DIRECCION GENERAL DE PROYECTOS

DGPRO

Obra: LÍNEA F
Plano: INSTALACIÓN TERMOMECÁNICA - PLANTA NIVEL BAJO ANDÉN
Fecha: 20/02/2026 | Eq. de Proyecto: UPU-ATEC-IATASA | Dibujó: M.S. | Revisó: J.C. | Escala: 1:100

PLANO-2026-18269441-GCABA-SSTRA
LF-ES-PAC-VEN-PL-005-02
HOJA N° 2/2

25/3/2026 15:26 p. m.
LF-ES-PAC-VEN-PL-005-02.dwg

G O B I E R N O DE LA C I U D A D DE B U E N O S A I R E S

"2026 - Año del 30° Aniversario de la sanción de la Constitución de la Ciudad Autónoma de Buenos Aires"

Hoja Adicional de Firmas
Plano

Número: PLANO-2026-18269441-GCABA-SSPO

Buenos Aires, Viernes 17 de Abril de 2026

Referencia: LF-ES-PAC-VEN-PL-005-02_0

El documento fue importado por el sistema GEDO con un total de 1 pagina/s.

Digitally signed by Comunicaciones Oficiales
Date: 2026.04.17 14:33:15 -03:00

Facundo Lombardo
Subsecretario
SUBSECRETARIA PROYECTOS Y OBRAS
MINISTERIO DE MOVILIDAD E INFRAESTRUCTURA

Digitally signed by Comunicaciones Oficiales
Date: 2026.04.17 14:33:16 -03:00