

PLANTA NIVEL 1°VESTÍBULO/MEZZANINE

ESCALA 1:100

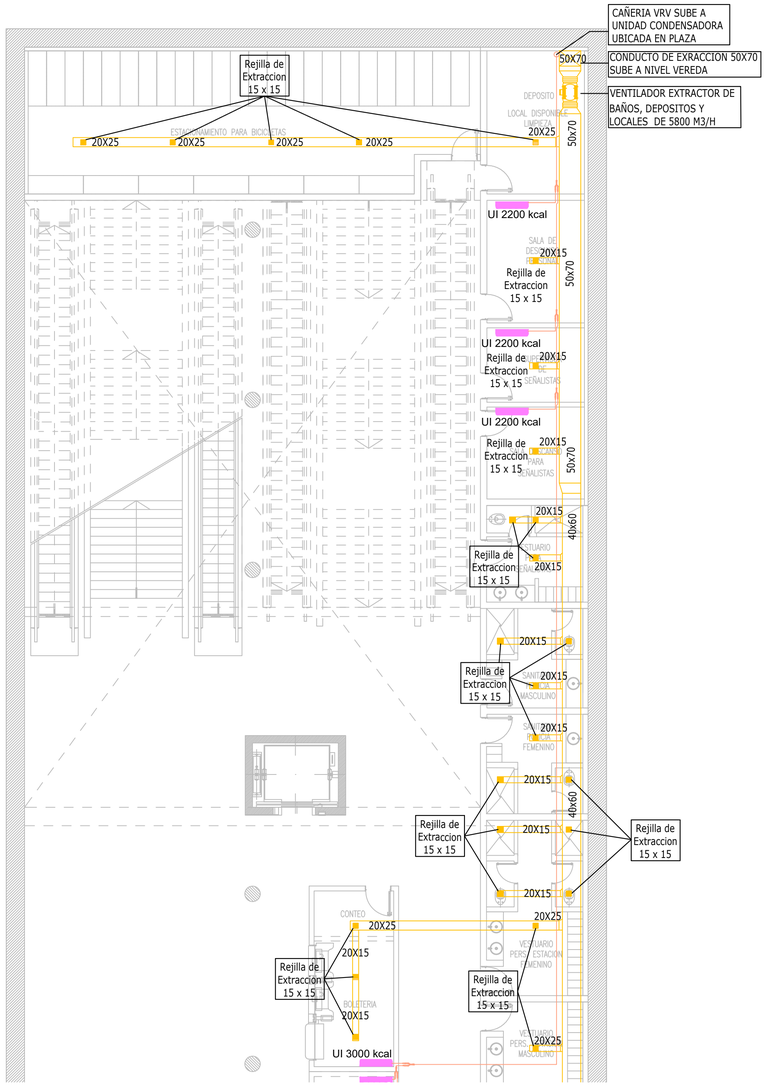

CROQUIS UBICACION

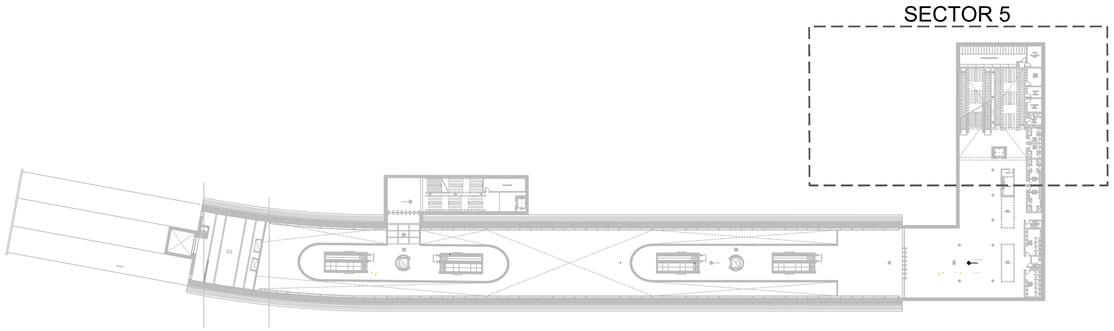

NOTAS:

EL PRESENTE PLANO ES INDICATIVO. EL CONTRATISTA CONFECCIONARÁ LOS PLANOS DE DETALLE DEFINITIVO QUE DEBERÁN SER APROBADOS POR LA D.G.O.INF.U. Y LA INSPECCION DE OBRA. EL PLANO PRESENTADO POR LA CONTRATISTA ESTARA EN UN TODO DE ACUERDO CON LA NORMATIVA VIGENTE.
TODAS LAS MEDIDAS Y NIVELES SE VERIFICARAN EN OBRA POR EL CONTRATISTA.
TODOS LOS DETALLES CONSTRUCTIVOS SERAN COORDINADOS Y COMPATIBILIZADOS EN OBRA.

PLANO NO APTO PARA CONSTRUCCION.

MODIFICACIONES:

REVISION	FECHA	DESCRIPCION
0	20/02/2026	EMISIÓN PARA LICITACIÓN

Gobierno de la Ciudad de Buenos Aires

MINISTERIO DE INFRAESTRUCTURA
SUBSECRETARIA DE PROYECTOS Y OBRAS
DIRECCION GENERAL DE PROYECTOS

DGPRO

Obra: LÍNEA F				PLANO-2026-18270398-GCABA-SSPO	
Plano: INSTALACIÓN TERMOMECÁNICA - PLANTA NIVEL 1°VESTÍBULO				LF-ES-PAC-VEN-PL-003-05	HOJA N° 5/5
Fecha: 20/02/2026	Eq. de Proyecto: UPU-ATEC-IATASA	Dibujó: M.S.	Revisó: J.C.	Escala: 1:100	

25/3/2026 15:15 p. m.
LF-ES-PAC-VEN-PL-003-05.dwg

G O B I E R N O DE LA C I U D A D DE B U E N O S A I R E S

"2026 - Año del 30° Aniversario de la sanción de la Constitución de la Ciudad Autónoma de Buenos Aires"

Hoja Adicional de Firmas
Plano

Número: PLANO-2026-18270398-GCABA-SSPO

Buenos Aires, Viernes 17 de Abril de 2026

Referencia: LF-ES-PAC-VEN-PL-003-05_0

El documento fue importado por el sistema GEDO con un total de 1 pagina/s.

Digitally signed by Comunicaciones Oficiales
Date: 2026.04.17 14:35:35 -03:00

Facundo Lombardo
Subsecretario
SUBSECRETARIA PROYECTOS Y OBRAS
MINISTERIO DE MOVILIDAD E INFRAESTRUCTURA

Digitally signed by Comunicaciones Oficiales
Date: 2026.04.17 14:35:35 -03:00