

PLANTA NIVEL 1°VESTÍBULO/MEZZANINE

ESCALA 1:100

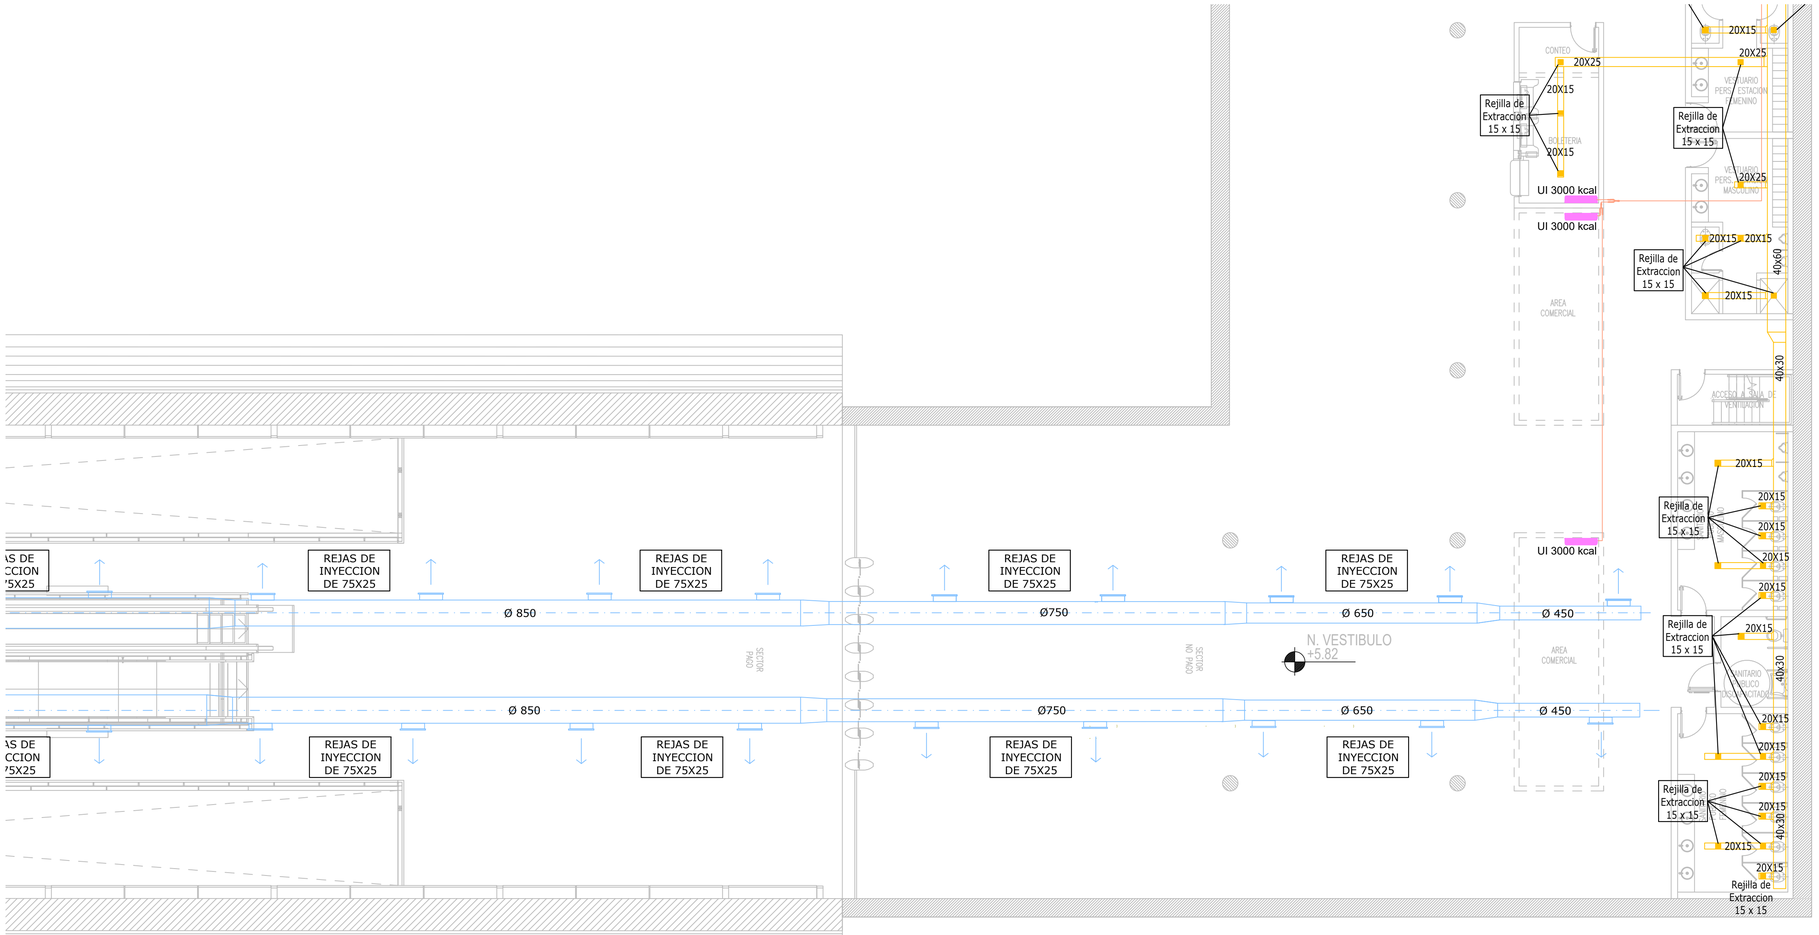

CROQUIS UBICACION

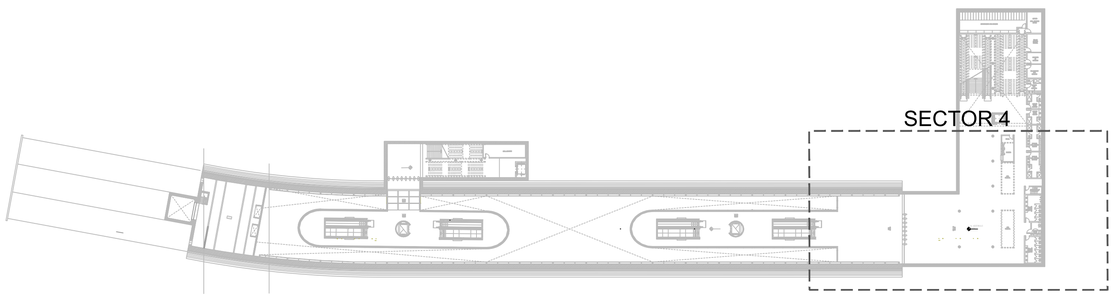

NOTAS:
EL PRESENTE PLANO ES INDICATIVO, LA CONSTRUCCION DEBERA SER REALIZADA DE ACUERDO AL DETALLE DEFINITIVO, QUE DEBERAN SER APROBADOS POR LA D.G.O.INF.U Y LA INSPECCION DE OBRA. EL PLANO PRESENTADO POR LA CONTRATISTA ESTARA EN UN TODO DE ACUERDO CON LA NORMATIVA VIGENTE.
TODAS LAS MEDIDAS Y NIVELES SE VERIFICARAN EN OBRA POR EL CONTRATISTA.
TODOS LOS DETALLES CONSTRUCTIVOS SERAN COORDINADOS Y COMPATIBILIZADOS EN OBRA

PLANO NO APTO PARA CONSTRUCCION.

MODIFICACIONES:

REVISION	FECHA	DESCRIPCION
0	20/02/2026	EMISIÓN PARA LICITACIÓN

MINISTERIO DE INFRAESTRUCTURA
SUBSECRETARIA DE PROYECTOS Y OBRAS
DIRECCION GENERAL DE PROYECTOS

DGPRO

Obra: LÍNEA F					PLANO-2026-18270477-GCABA-SSPO	
Plano: INSTALACIÓN TERMOMECÁNICA - PLANTA NIVEL 1°VESTÍBULO					LF-ES-PAC-VEN-PL-003-04	
Fecha: 20/02/2026	Eq. de Proyecto: UPU-ATEC-IATASA	Dibujó: M.S.	Revisó: J.C.	Escala: 1:100		4/5

25/3/2026, 15:14 p. m.
LF-ES-PAC-VEN-PL-003-04.dwg

G O B I E R N O DE LA C I U D A D DE B U E N O S A I R E S

"2026 - Año del 30° Aniversario de la sanción de la Constitución de la Ciudad Autónoma de Buenos Aires"

Hoja Adicional de Firmas
Plano

Número: PLANO-2026-18270477-GCABA-SSPO

Buenos Aires, Viernes 17 de Abril de 2026

Referencia: LF-ES-PAC-VEN-PL-003-04_0

El documento fue importado por el sistema GEDO con un total de 1 pagina/s.

Digitally signed by Comunicaciones Oficiales
Date: 2026.04.17 14:35:46 -03:00

Facundo Lombardo
Subsecretario
SUBSECRETARIA PROYECTOS Y OBRAS
MINISTERIO DE MOVILIDAD E INFRAESTRUCTURA

Digitally signed by Comunicaciones Oficiales
Date: 2026.04.17 14:35:47 -03:00