PLANTA NIVEL 1°VESTÍBULO/MEZZANINE

ESCALA 1:100

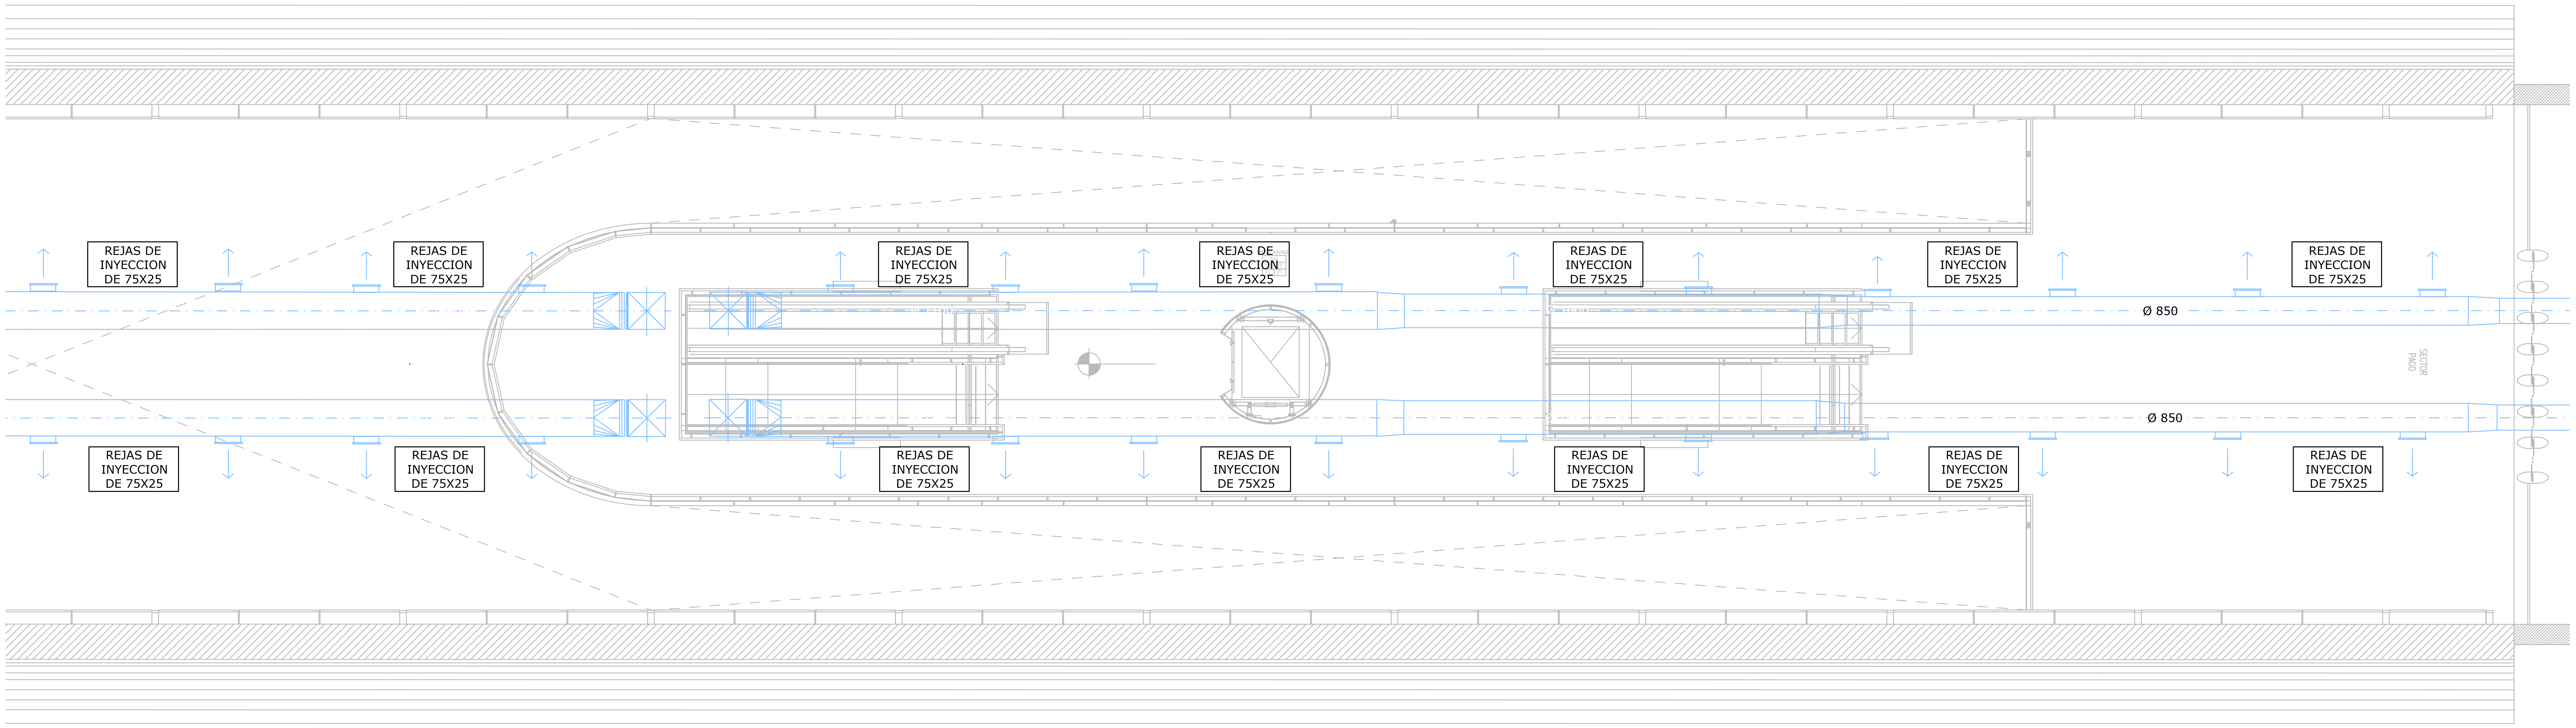
REJAS DE INYECCION DE 75X25
REJAS DE INYECCION DE 75X25
REJAS DE INYECCION DE 75X25
REJAS DE INYECCION DE 75X25
REJAS DE INYECCION DE 75X25
REJAS DE INYECCION DE 75X25
REJAS DE INYECCION DE 75X25
Ø 850
Ø 850
REJAS DE INYECCION DE 75X25
REJAS DE INYECCION DE 75X25
REJAS DE INYECCION DE 75X25
REJAS DE INYECCION DE 75X25
REJAS DE INYECCION DE 75X25
REJAS DE INYECCION DE 75X25
REJAS DE INYECCION DE 75X25

CROQUIS UBICACION

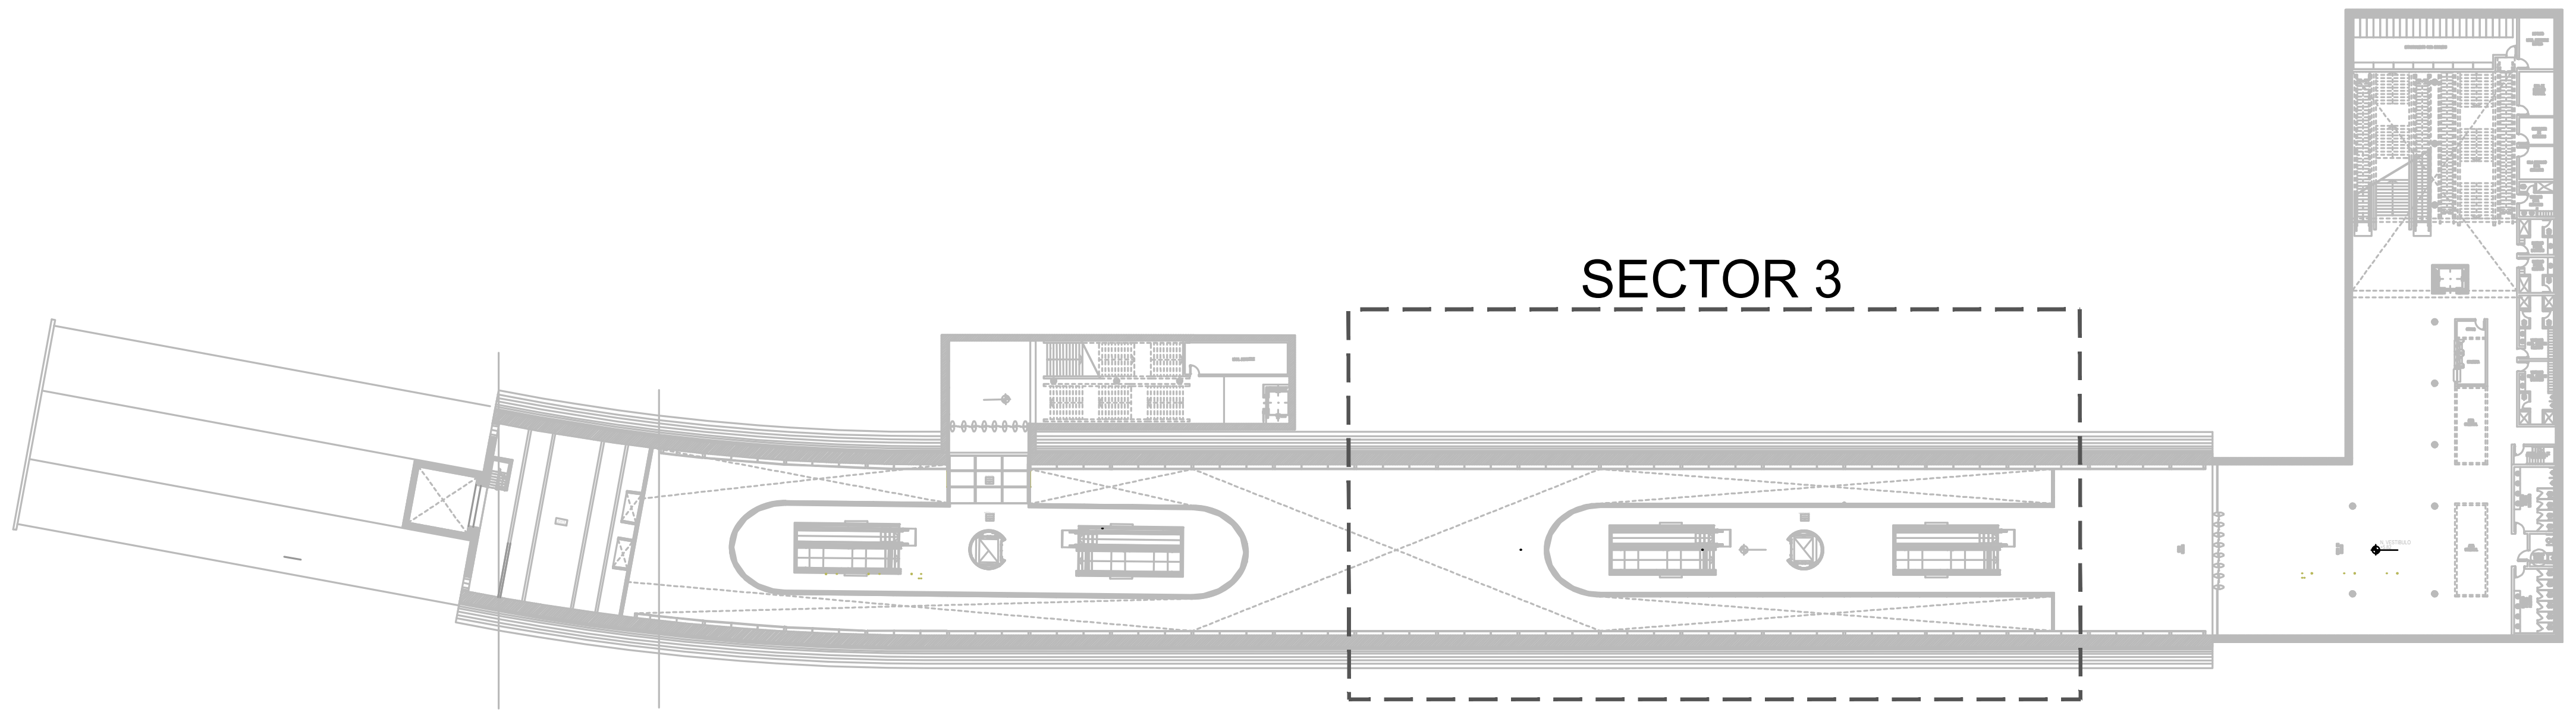

25/3/2026 15:08 p. m.
LF-ES-PAC-VEN-PL-003-03.dwg

NOTAS:
EL PRESENTE PLANO ES INDICATIVO. LA CONTRATISTA CONFECCIONARA LOS PLANOS DE DETALLE DEFINITIVO, QUE DEBERAN SER APROBADOS POR LA D.G.O.INF.U Y LA INSPECCION DE OBRA. EL PLANO PRESENTADO POR LA CONTRATISTA ESTARA EN UN TODO DE ACUERDO CON LA NORMATIVA VIGENTE.
TODAS LAS MEDIDAS Y NIVELES SE VERIFICARAN EN OBRA POR EL CONTRATISTA.
TODOS LOS DETALLES CONSTRUCTIVOS SERAN COORDINADOS Y COMPATIBILIZADOS EN OBRA.

PLANO NO APTO PARA CONSTRUCCION.

MODIFICACIONES:

REVISION	FECHA	DESCRIPCION
0	20/02/2026	EMISIÓN PARA LICITACIÓN

Gobierno de la Ciudad de Buenos Aires

MINISTERIO DE INFRAESTRUCTURA
SUBSECRETARIA DE PROYECTOS Y OBRAS
DIRECCION GENERAL DE PROYECTOS

DGPRO

Obra: LÍNEA F
Plano: INSTALACIÓN TERMOMECÁNICA - PLANTA NIVEL 1°VESTÍBULO
Fecha: 20/02/2026
Eq. de Proyecto: UPU-ATEC-IATASA
Dibujó: M.S.
PLANO-2026-18270582-GCABA-SSPO
LF-ES-PAC-VEN-PL-003-03
Revisó: J.C.
Escala: 1:100
Plano N°
3/5

GOBIERNO DE LA CIUDAD DE BUENOS AIRES
"2026 - Año del 30° Aniversario de la sanción de la Constitución de la Ciudad Autónoma de Buenos Aires"

Hoja Adicional de Firmas
Plano

Número: PLANO-2026-18270582-GCABA-SSPO

Buenos Aires, Viernes 17 de Abril de 2026

Referencia: LF-ES-PAC-VEN-PL-003-03_0

El documento fue importado por el sistema GEDO con un total de 1 pagina/s.

Digitally signed by Comunicaciones Oficiales
Date: 2026.04.17 14:36:00 -03:00

Facundo Lombardo
Subsecretario
SUBSECRETARIA PROYECTOS Y OBRAS
MINISTERIO DE MOVILIDAD E INFRAESTRUCTURA

Digitally signed by Comunicaciones Oficiales
Date: 2026.04.17 14:36:01 -03:00