PLANTA NIVEL 1°VESTÍBULO/MEZZANINE
NIVEL 1

ESCALA 1:100

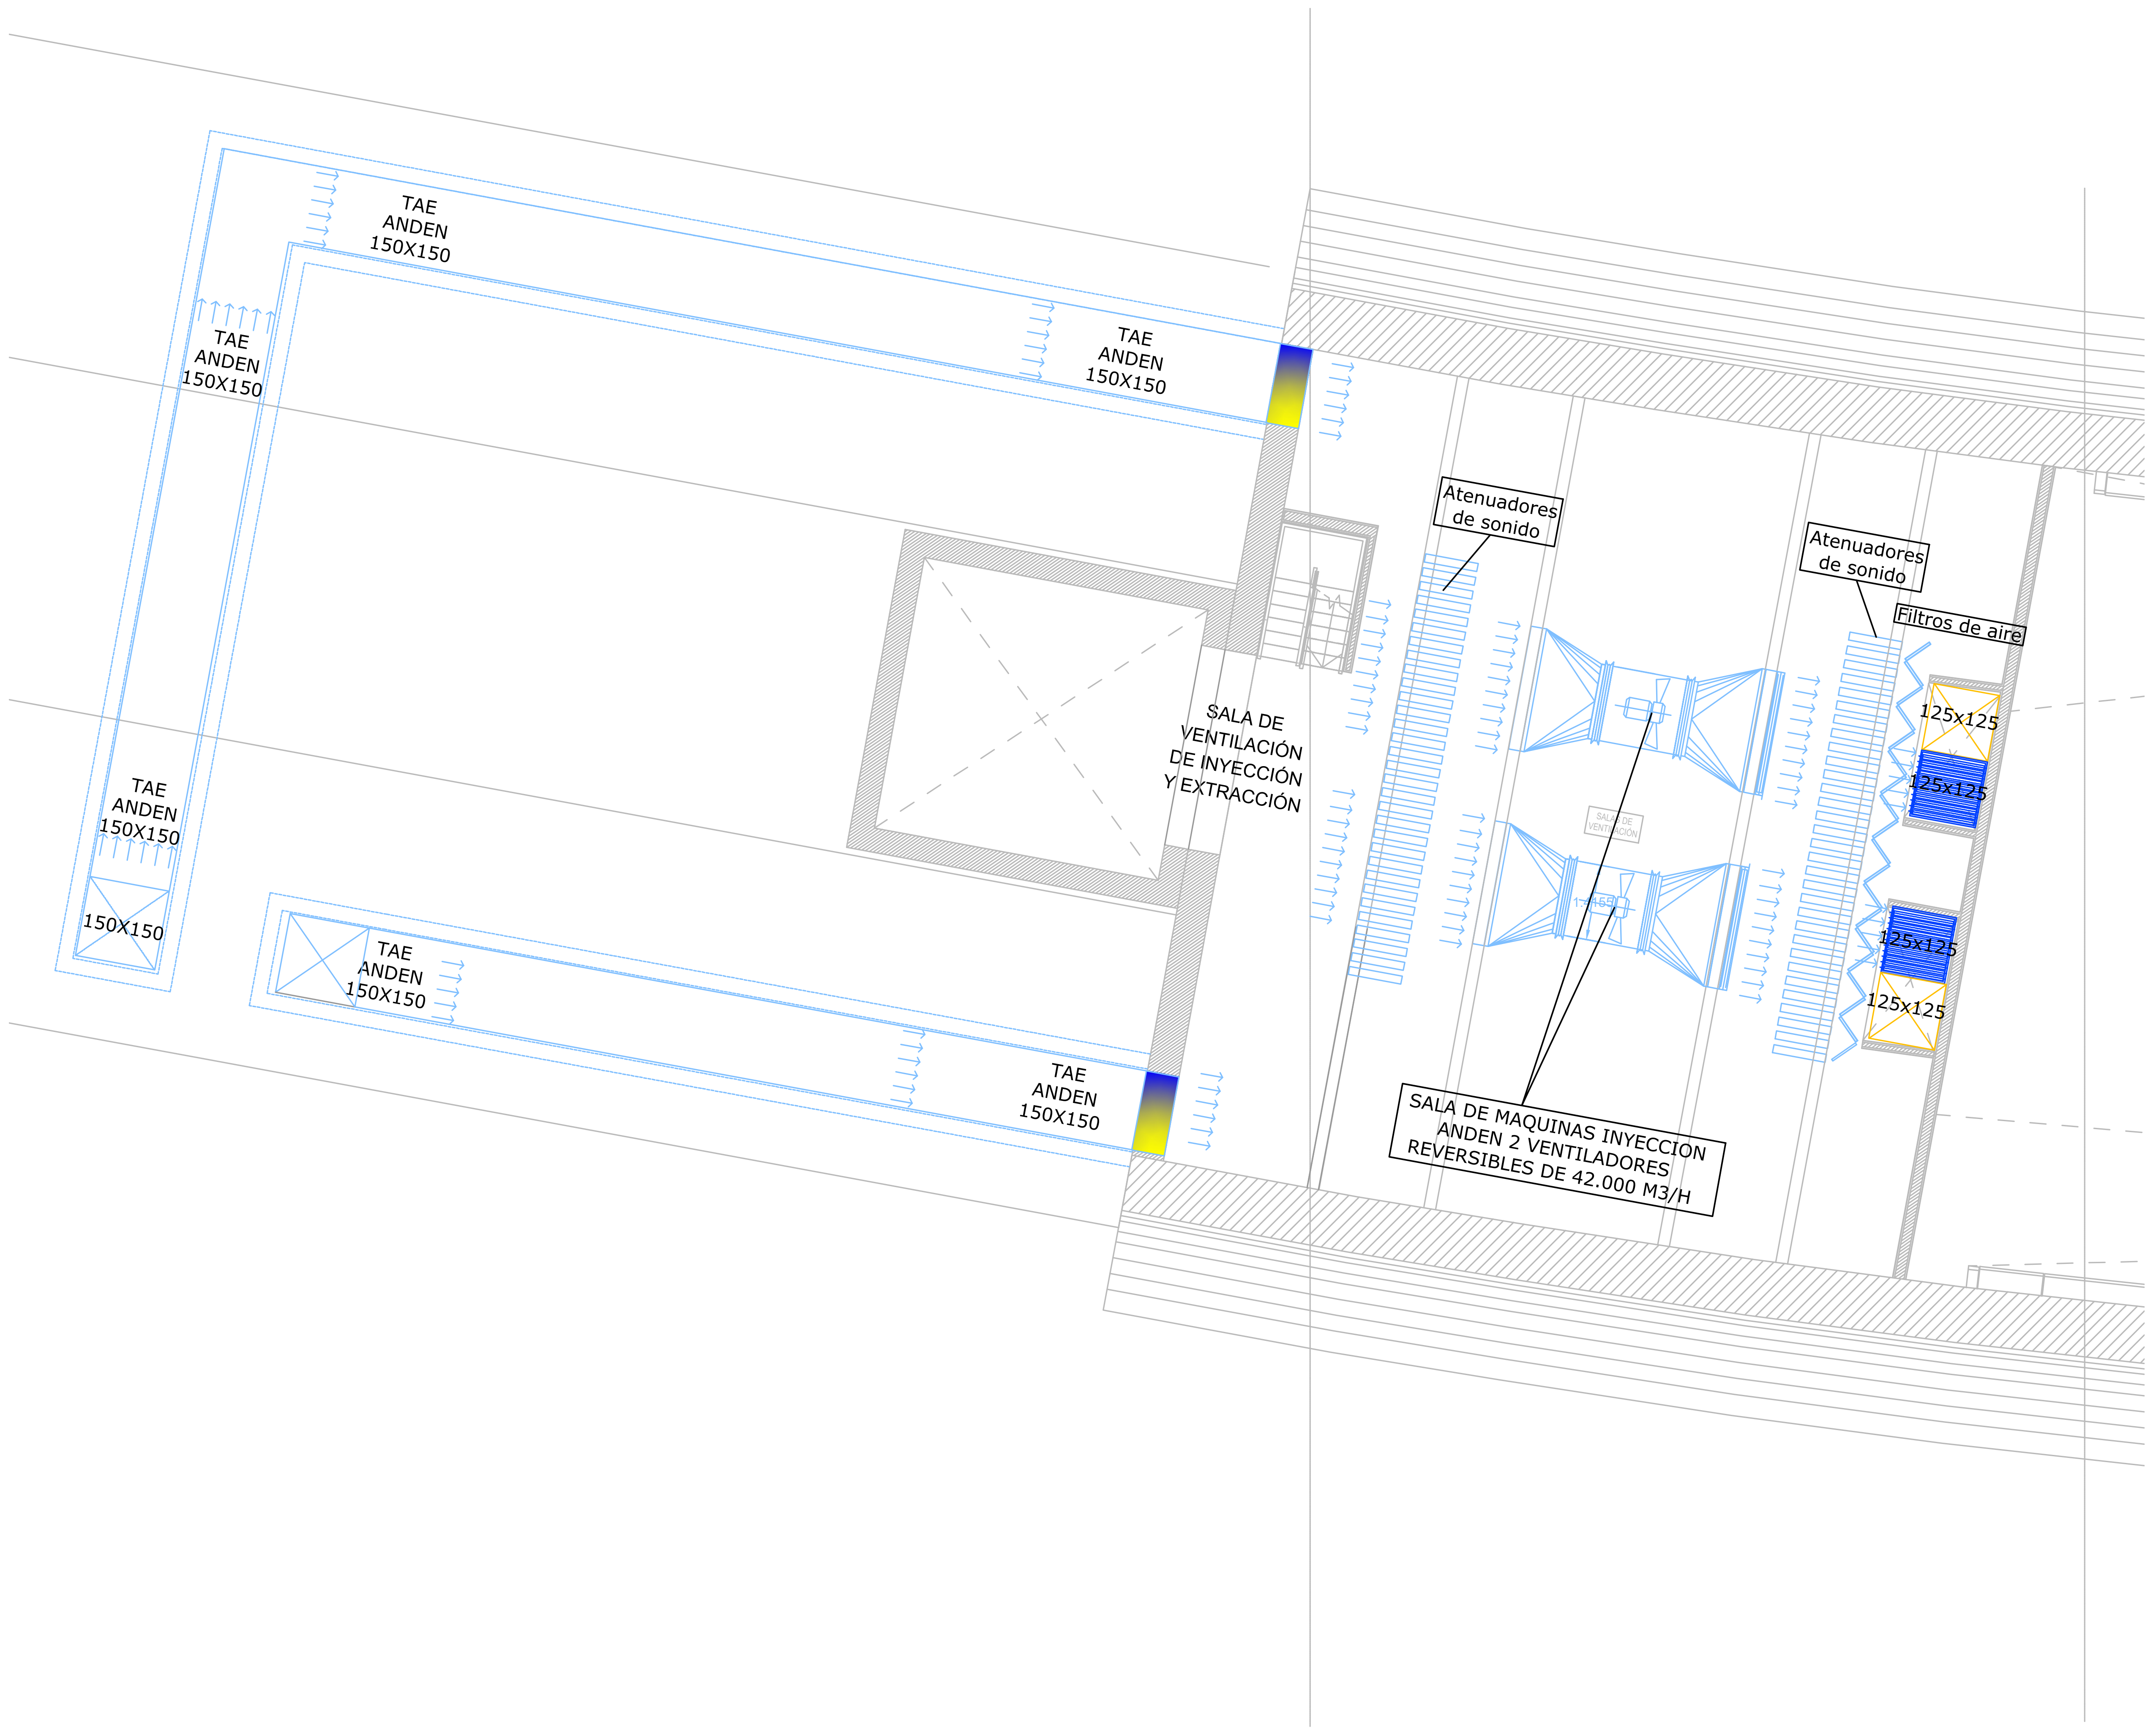
TAE
ANDEN
150X150
TAE
ANDEN
150X150
TAE
ANDEN
150X150
TAE
ANDEN
150X150
150X150
TAE
ANDEN
150X150
TAE
ANDEN
150X150
SALA DE
VENTILACIÓN
DE INYECCIÓN
Y EXTRACCIÓN
Atenuadores
de sonido
Atenuadores
de sonido
Filtros de aire
125x125
125x125
125x125
125x125
SALA DE MAQUINAS INYECCION
ANDEN 2 VENTILADORES
REVERSIBLES DE 42.000 M3/H

PLANTA NIVEL 1°VESTÍBULO/MEZZANINE
NIVEL 2

ESCALA 1:100

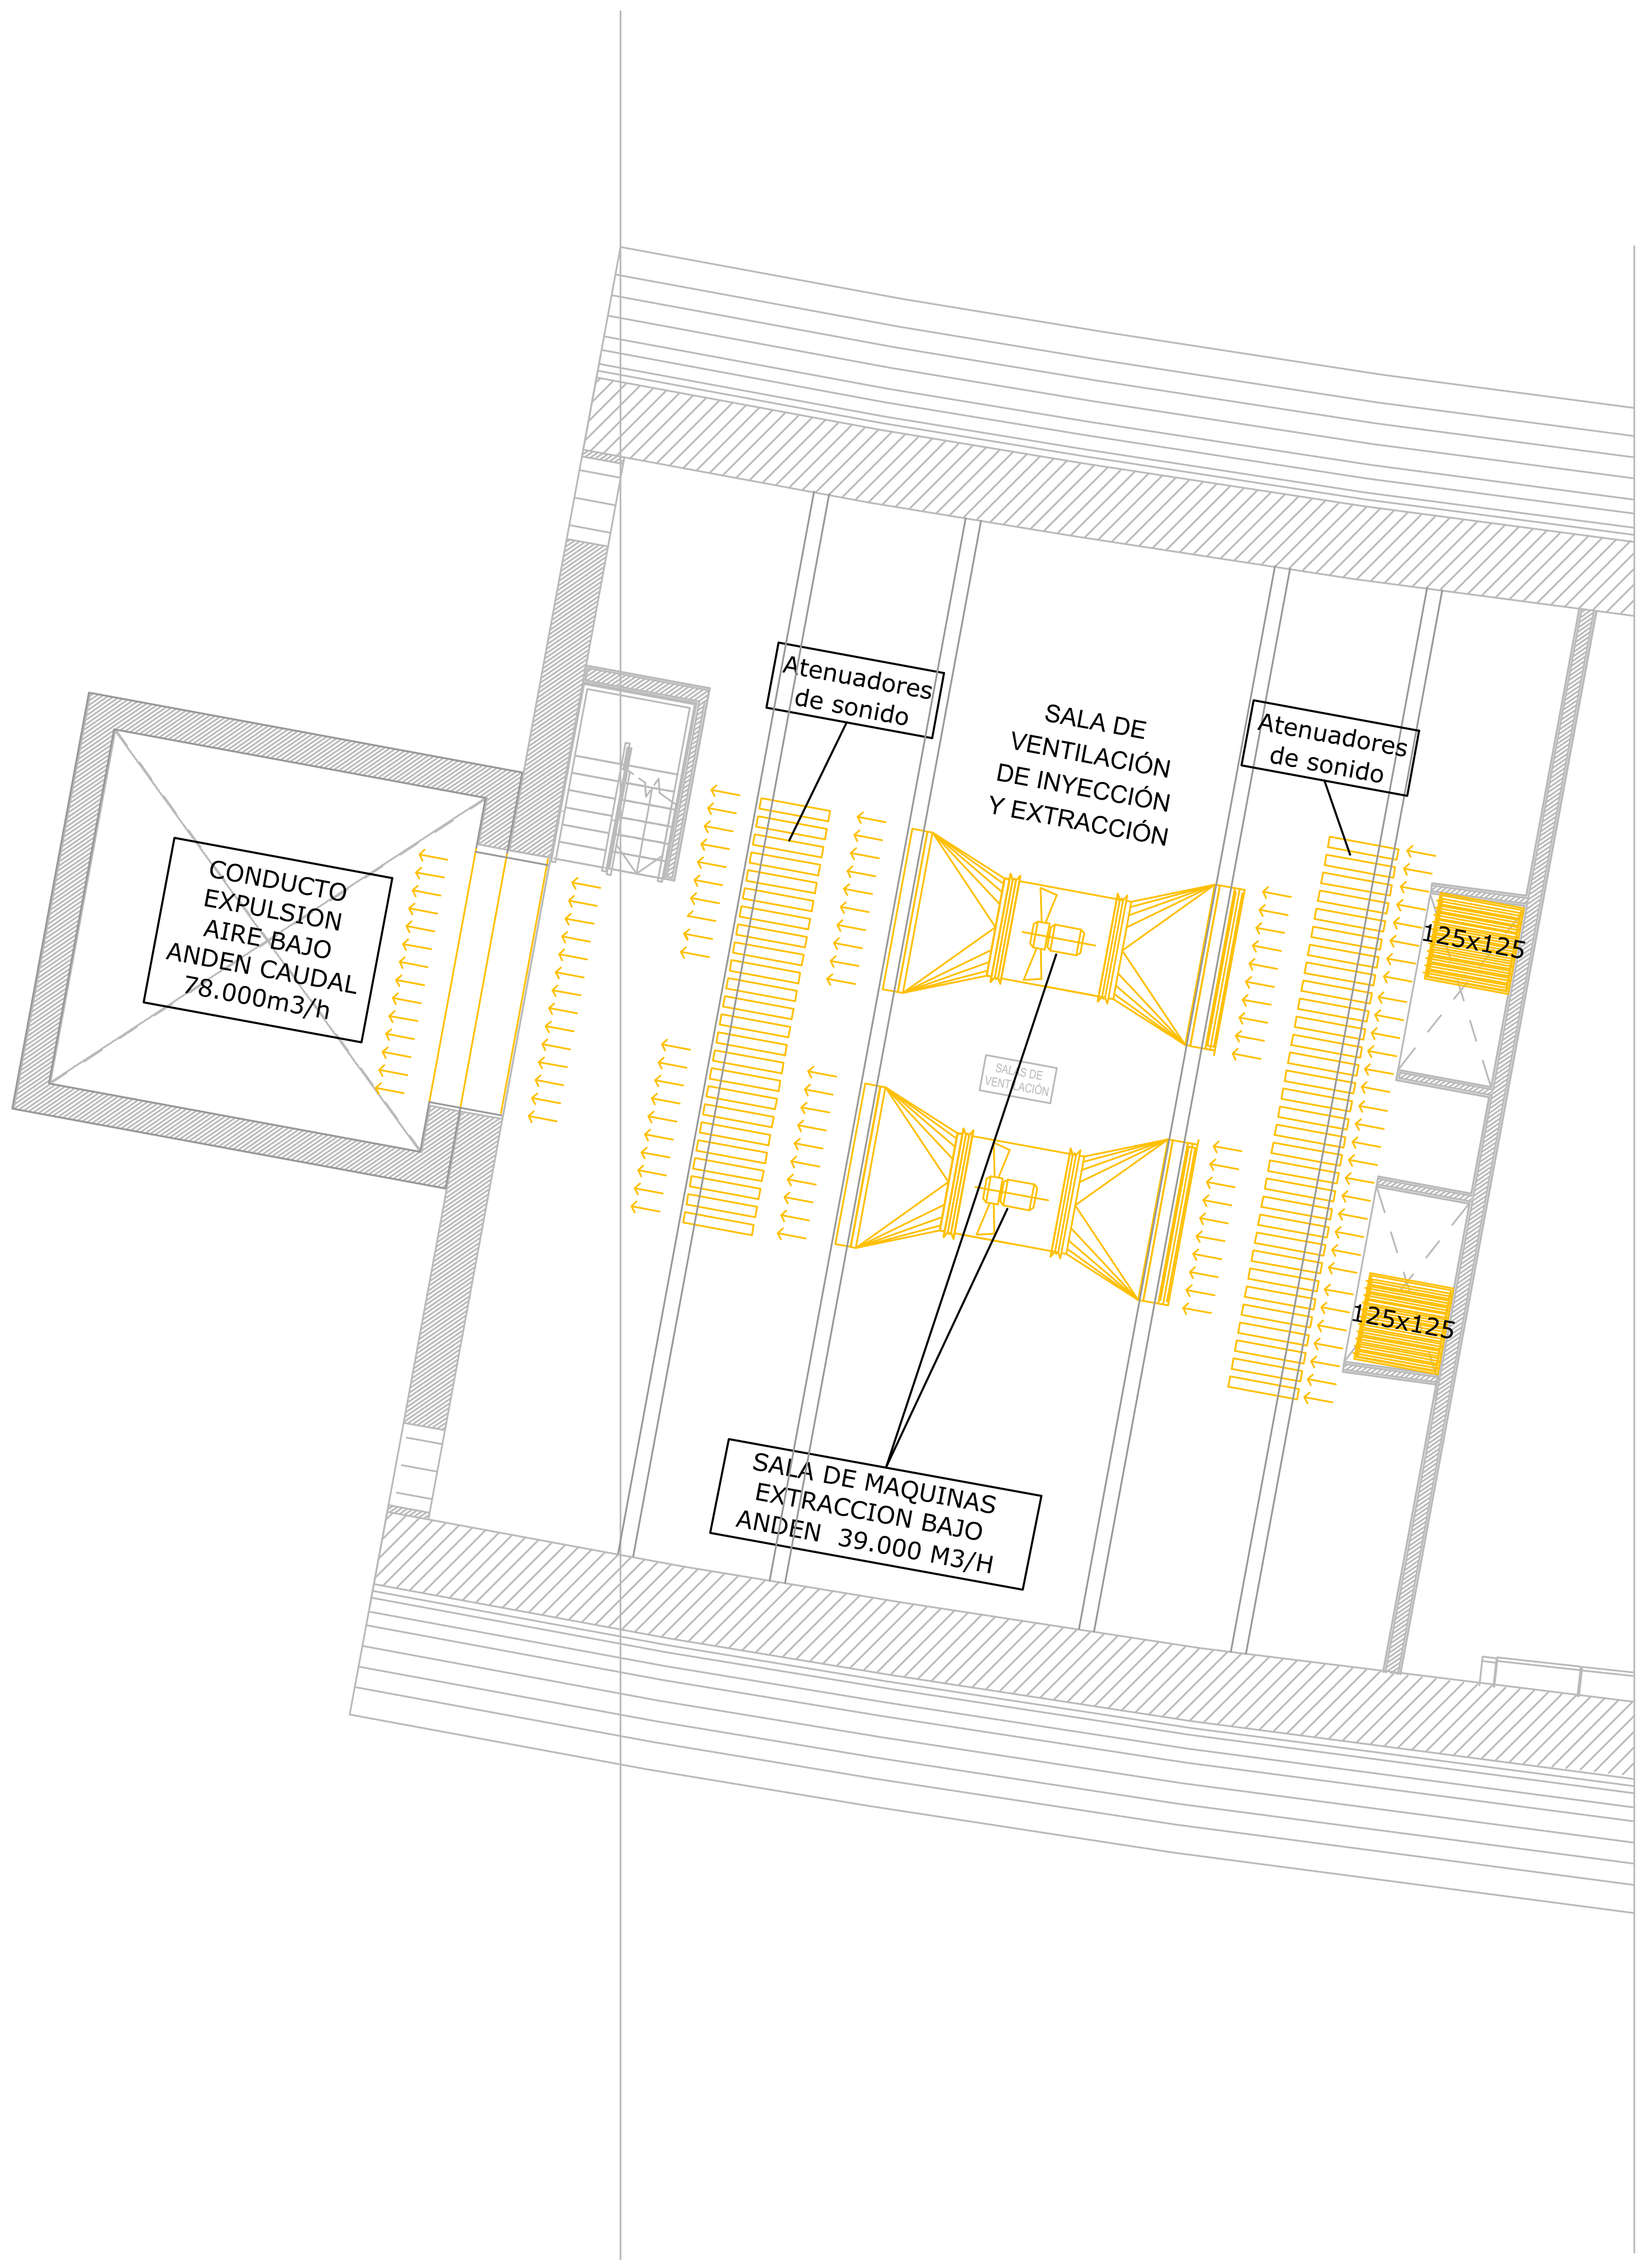
CONDUCTO
EXPULSION
AIRE BAJO
ANDEN CAUDAL
78.000m3/h
Atenuadores
de sonido
SALA DE
VENTILACIÓN
DE INYECCIÓN
Y EXTRACCIÓN
Atenuadores
de sonido
125x125
125x125
SALA DE MAQUINAS
EXTRACCION BAJO
ANDEN 39.000 M3/H

CROQUIS UBICACION

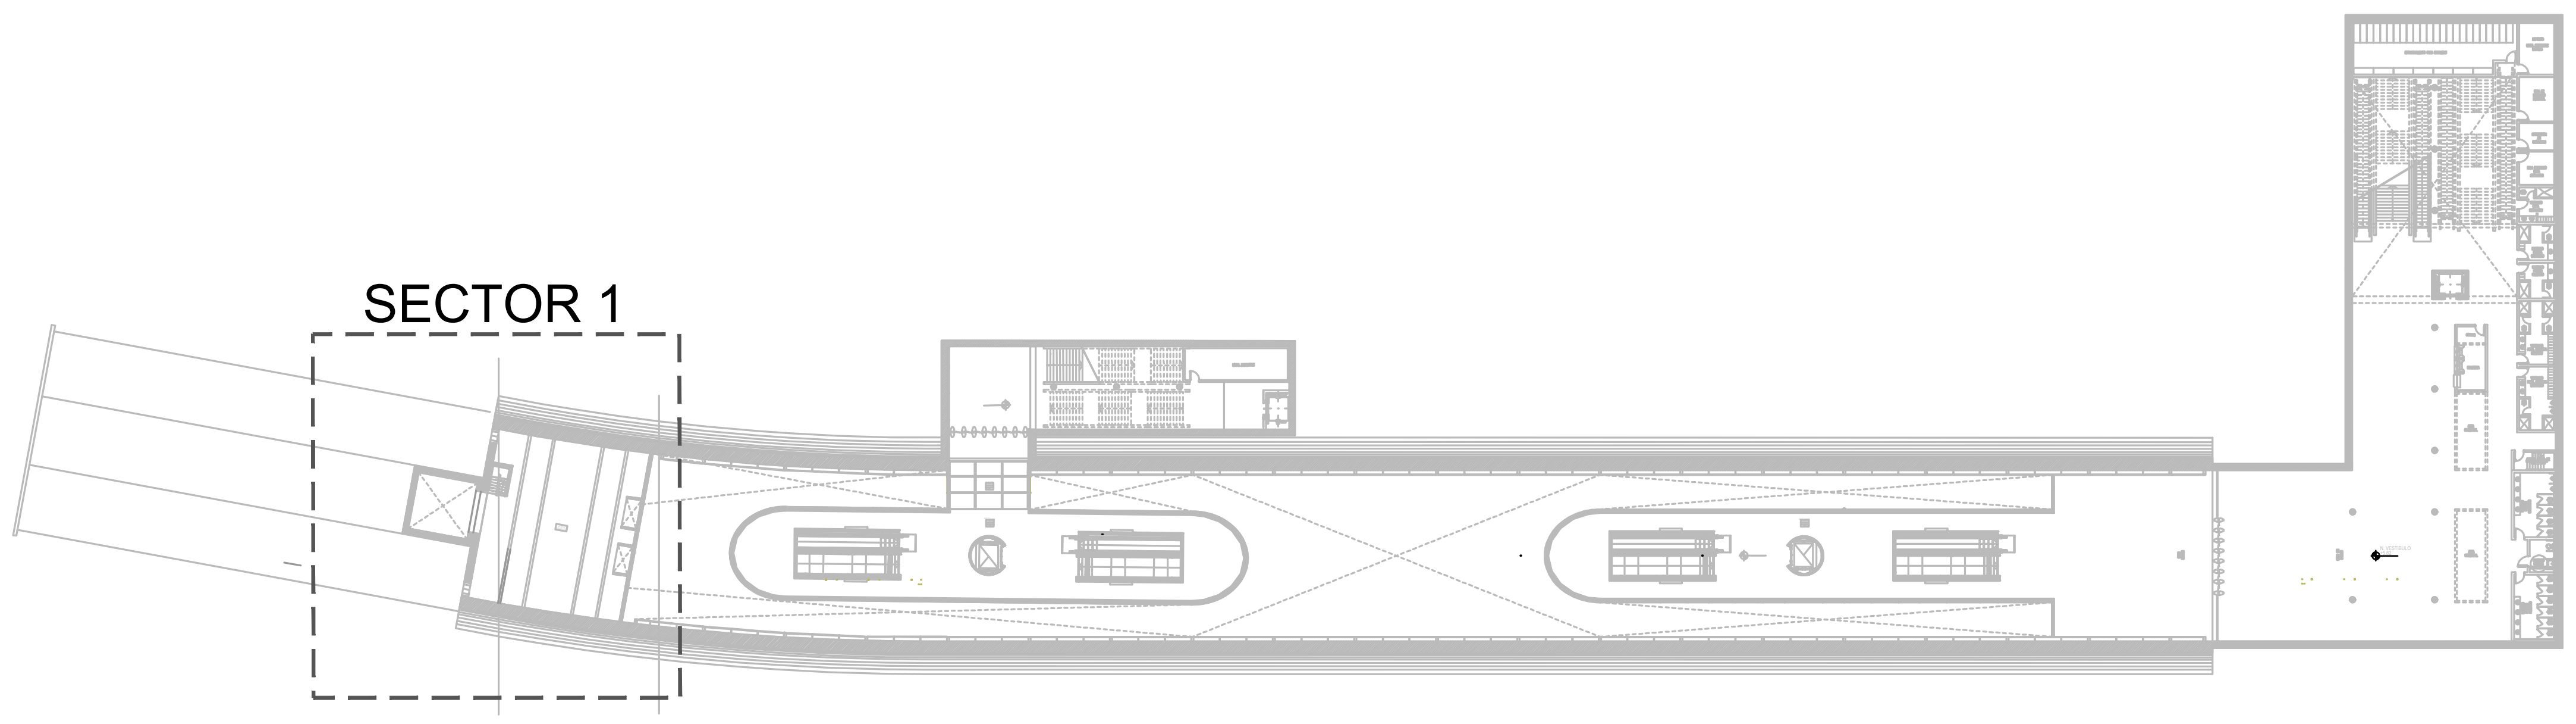

NOTAS:
EL PRESENTE PLANO ES INDICATIVO. LA CONTRATISTA CONFECCIONARA LOS PLANOS DE DETALLE DEFINITIVO, QUE DEBERAN SER APROBADOS POR LA D.G.O.INF.U Y LA INSPECCION DE OBRA. EL PLANO PRESENTADO POR LA CONTRATISTA ESTARA EN UN TODO DE ACUERDO CON LA NORMATIVA VIGENTE.
TODAS LAS MEDIDAS Y NIVELES SE VERIFICARAN EN OBRA POR EL CONTRATISTA.
TODOS LOS DETALLES CONSTRUCTIVOS SERAN COORDINADOS Y COMPATIBILIZADOS EN OBRA.

PLANO NO APTO PARA CONSTRUCCION.

MODIFICACIONES:

REVISION	FECHA	DESCRIPCION
0	20/02/2026	EMISIÓN PARA LICITACIÓN

Gobierno de la Ciudad de Buenos Aires

MINISTERIO DE INFRAESTRUCTURA
SUBSECRETARIA DE PROYECTOS Y OBRAS
DIRECCION GENERAL DE PROYECTOS

DGPRO

Obra: LÍNEA F
Plano: INSTALACIÓN TERMOMECÁNICA - PLANTA NIVEL 1°VESTÍBULO
Fecha: 20/02/2026
Eq. de Proyecto: UPU-ATEC-IATASA
Dibujó: M.S.
PLANO-2026-18270755-GCABA-SSPO
Plano N°
LF-ES-PAC-VEN-PL-003-01
Revisó: J.C.
Escala: 1:100
1/5

GOBIERNO DE LA CIUDAD DE BUENOS AIRES
"2026 - Año del 30° Aniversario de la sanción de la Constitución de la Ciudad Autónoma de Buenos Aires"

Hoja Adicional de Firmas
Plano

Número: PLANO-2026-18270755-GCABA-SSPO

Buenos Aires, Viernes 17 de Abril de 2026

Referencia: LF-ES-PAC-VEN-PL-003-01_0

El documento fue importado por el sistema GEDO con un total de 1 pagina/s.

Digitally signed by Comunicaciones Oficiales
Date: 2026.04.17 14:36:25 -03:00

Facundo Lombardo
Subsecretario
SUBSECRETARIA PROYECTOS Y OBRAS
MINISTERIO DE MOVILIDAD E INFRAESTRUCTURA

Digitally signed by Comunicaciones Oficiales
Date: 2026.04.17 14:36:24 -03:00