

PLANTA NIVEL ANDÉN

ESCALA 1:100

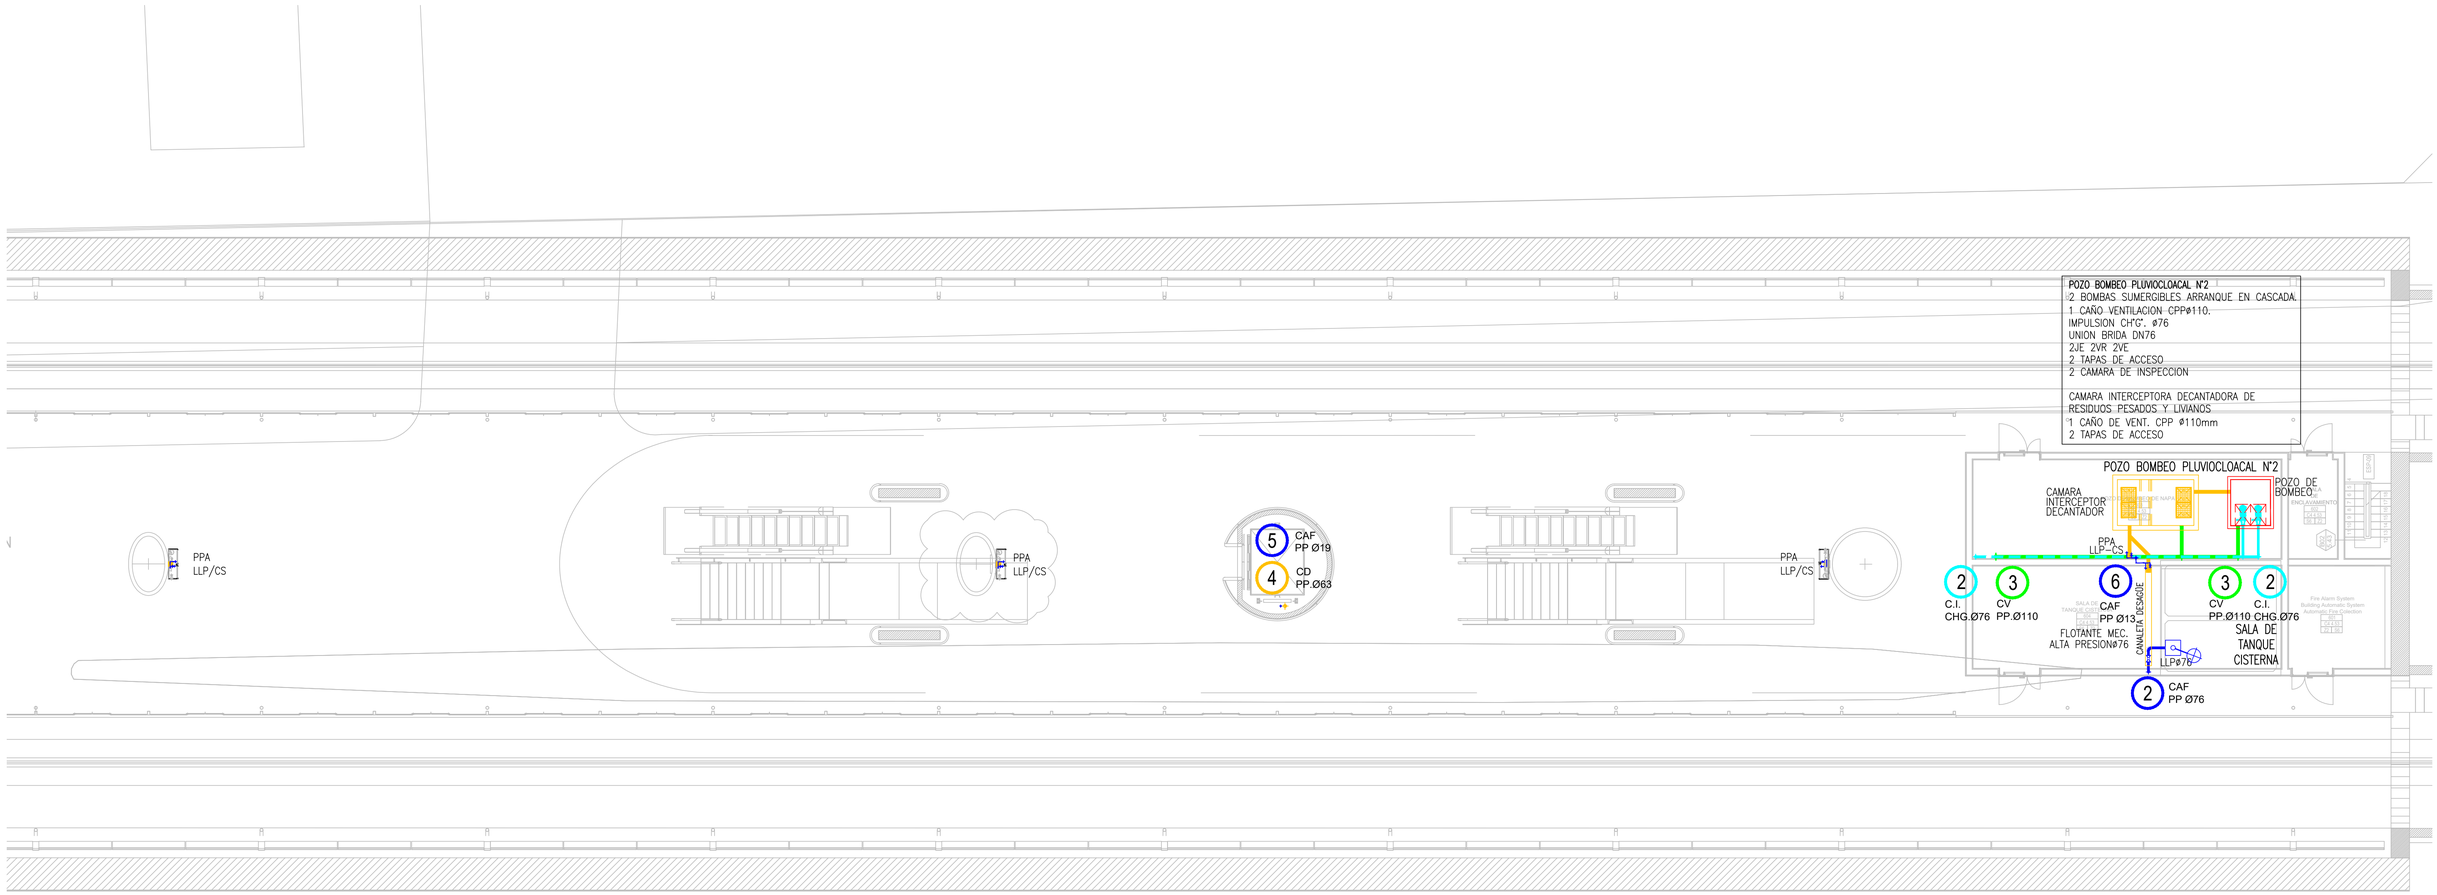

CROQUIS UBICACION

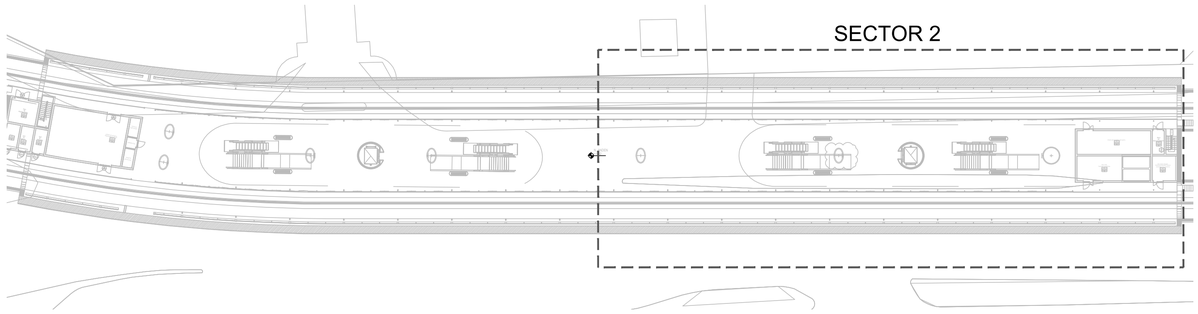

REFERENCIAS

- INSTALACION CLOACAL – PRIMARIA
- INSTALACION CLOACAL – SECUNDARIA
- INSTALACION CLOACAL IMPULSION – PRIMARIA
- INSTALACION CLOACAL – VENTILACION
- INSTALACION AGUA FRIA
- INSTALACION AGUA FRIA POR CIELORRASO
- INSTALACION AGUA CALIENTE
- INSTALACION AGUA CALIENTE POR CIELORRASO

LLP	LLAVE DE PASO
CS	CANILLA DE SERVICIO
BDA	BOCA DE DESAGUE ABIERTA
BDT	BOCA DE DESAGUE CERRADA
CDV	CAÑO DE DESCARGA VENTILACION
CV	CAÑO DE VENTILACION
PPA	PILETA DE PISO ABIERTA
CI	CAMARA DE INSPECCION
BR	BOCA DE REGISTRO
CA	CAMARA AQUIETAMIENTO

NOTAS

CAÑERIAS DESCARGA SANITARIAS
- MATERIAL: POLIPROPILENO APTO PARA USO SANITARIO
- UNIONES: CON ORING DE DOBLE LABIO APTO PARA USO SANITARIO
- SISTEMA: TIPO AWADUCT O SIMILAR

CAÑERIAS DE AGUA FRIA Y CALIENTE
- MATERIAL: POLIPROPILENO APTO PARA AGUA POTABLE FRIA Y CALIENTE
- UNIONES: POR TERMOFUSION
- SISTEMA: TIPO AQUA SYSTEM, SALADILLO O SIMILAR

CAÑERIAS DE IMPULSION CLOACAL
- MATERIAL: ACERO GALVANIZADO (HG)
- UNIONES EN GENERAL: ROSCADAS
- UNIONES PARA DESARME: BRIDADAS

NOTAS: LA PRESENTE PLANTA ES INDICATIVA. LA CONTRATISTA CONFECCIONARA LOS PLANOS DE DETALLE CONSTRUCTIVO, QUE DEBERAN SER APROBADOS POR LA D.G.O.INF.U Y LA INSPECCION DE OBRA. EL PLANO PRESENTADO POR LA CONTRATISTA ESTARA EN UN TODO DE ACUERDO CON LA NORMATIVA VIGENTE.
TODAS LAS MEDIDAS Y NIVELES SE VERIFICARAN EN OBRA POR EL CONTRATISTA.
TODOS LOS DETALLES CONSTRUCTIVOS SERAN COORDINADOS Y COMPATIBILIZADOS EN OBRA

PLANO NO APTO PARA CONSTRUCCION.

MODIFICACIONES:

REVISION	FECHA	DESCRIPCION
0	20/02/2026	EMISIÓN PARA LICITACIÓN

MINISTERIO DE INFRAESTRUCTURA
SUBSECRETARIA DE PROYECTOS Y OBRAS
DIRECCION GENERAL DE PROYECTOS

DGPRO

Obra: LÍNEA F				PLANO-2026-18271871-GCABA-SSPOP	Hoja N°
Plano: INSTALACIÓN SANITARIA - PLANTA NIVEL ANDÉN				LF-ES-PAC-SAN-PL-004-02	2/2
Fecha: 20/02/2026	Eq. de Proyecto: UPU-ATEC-IATASA	Dibujó: M.S.	Revisó: J.C.	Escala: 1:100	

18/3/2026 17:38 p. m.
LF-ES-PAC-SAN-PL-004-02.dwg

G O B I E R N O DE LA C I U D A D DE B U E N O S A I R E S

"2026 - Año del 30° Aniversario de la sanción de la Constitución de la Ciudad Autónoma de Buenos Aires"

Hoja Adicional de Firmas
Plano

Número: PLANO-2026-18271871-GCABA-SSPO

Buenos Aires, Viernes 17 de Abril de 2026

Referencia: LF-ES-PAC-SAN-PL-004-02_0

El documento fue importado por el sistema GEDO con un total de 1 pagina/s.

Digitally signed by Comunicaciones Oficiales
Date: 2026.04.17 14:39:12 -03:00

Facundo Lombardo
Subsecretario
SUBSECRETARIA PROYECTOS Y OBRAS
MINISTERIO DE MOVILIDAD E INFRAESTRUCTURA

Digitally signed by Comunicaciones Oficiales
Date: 2026.04.17 14:39:13 -03:00