PLANTA NIVEL 1°VESTÍBULO/MEZZANINE

ESCALA 1:100

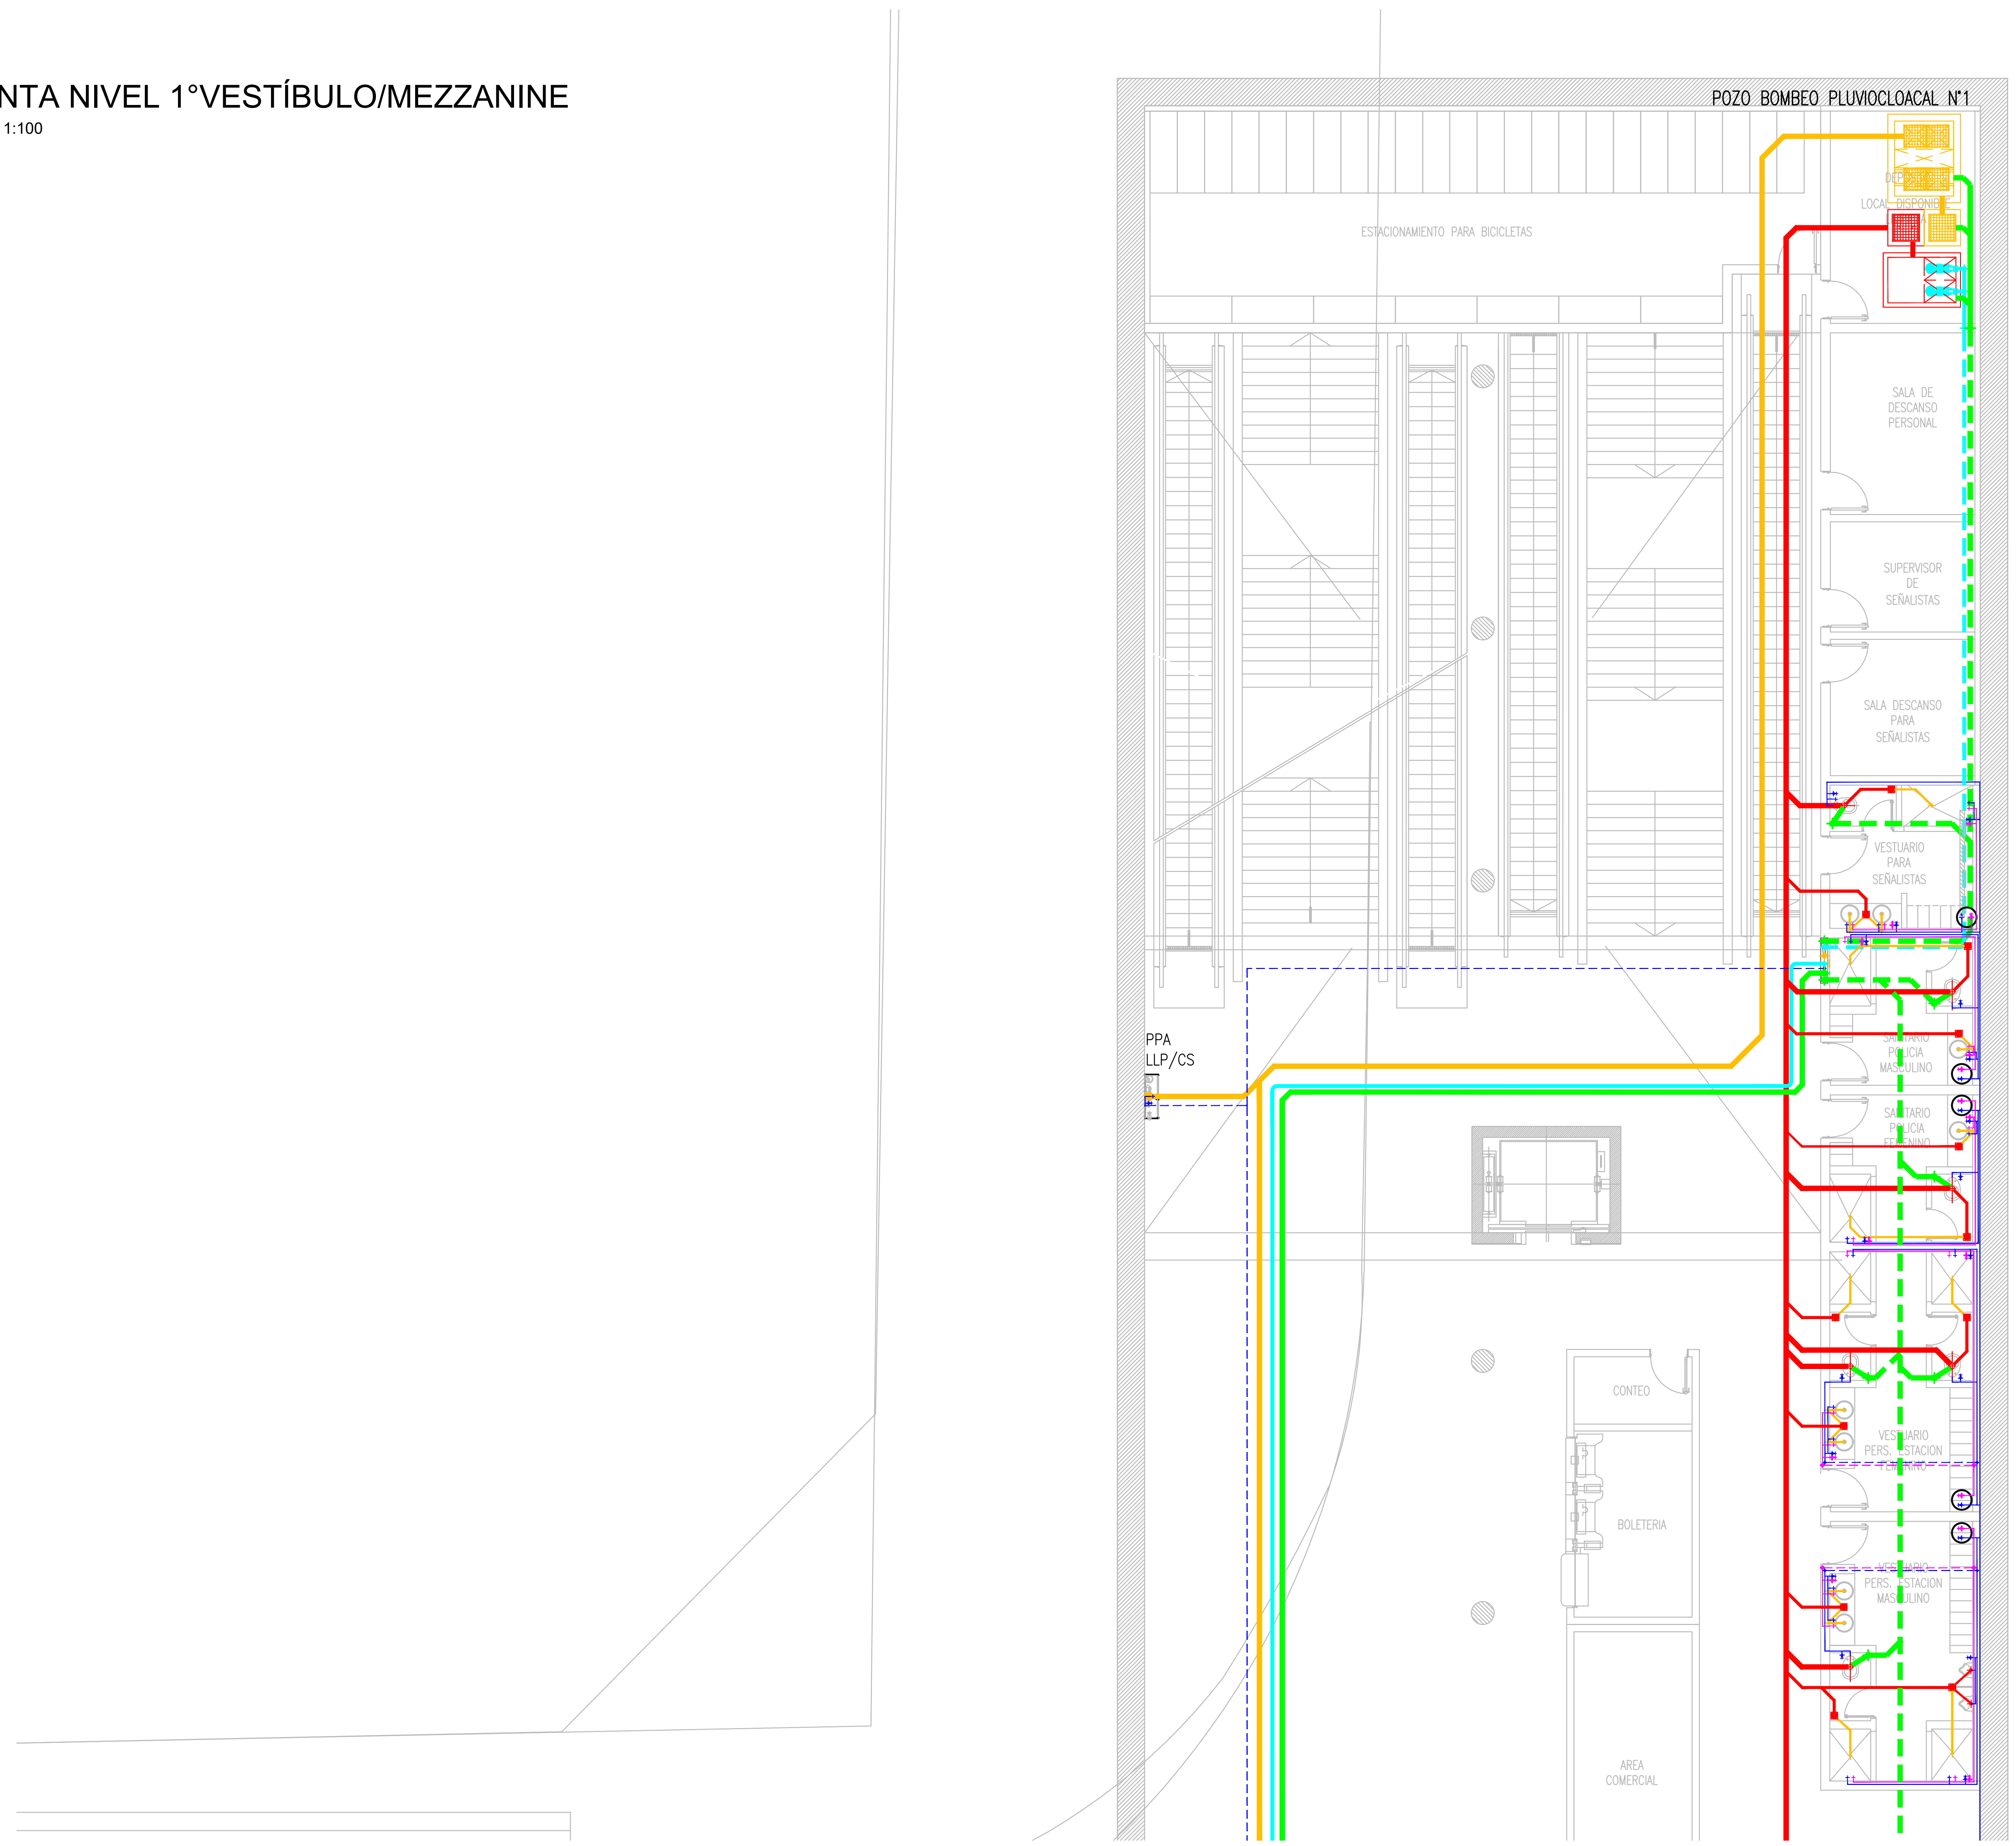
POZO BOMBEO PLUVIOCLOACAL N°1
ESTACIONAMIENTO PARA BICICLETAS
DEPOSITO
LOCAL DISPONIBLE
SALA DE DESCANSO PERSONAL
SUPERVISOR DE SEÑALISTAS
SALA DESCANSO PARA SEÑALISTAS
VESTUARIO PARA SEÑALISTAS
SANITARIO POLICIA MASCULINO
SANITARIO POLICIA FEMENINO
VESTUARIO PERS. ESTACION FEMENINO
VESTUARIO PERS. ESTACION MASCULINO
PPA
LLP/CS
CONTEO
BOLETERIA
AREA COMERCIAL

POZO BOMBEO PLUVIOCLOACAL N°1
2 BOMBAS SUMERGIBLES ARRANQUE EN CASCADA.
1 CAÑO VENTILACION CPPø110.
IMPULSION CH°G°. ø76
UNION BRIDA DN76
2JE 2VR 2VE
2 TAPAS DE ACCESO
2 CAMARA DE INSPECCION

CAMARA INTERCEPTORA DECANTADORA DE RESIDUOS PESADOS Y LIVIANOS
1 CAÑO DE VENT. CPP ø110mm
2 TAPAS DE ACCESO

VESTUARIO PARA SEÑALISTA

DISTRIB. INT. AF ø13
2 L° c/MEZCLADOR–DESC. CPPØ38 A PPA ø63
1 I°P° DAI DESC CPPØ110
1 DU c/MEZCLADOR–DESC. CPPØ38 A PPA ø63
4 LLP AF Ø13
3 LLP AC Ø13
2 PPA Ø63
1 TERMOTANQUE ELECTRICO 54 lts.

③	CAF PP Ø38	①	Cv PP.Ø110
①	C.I. CHG.Ø76	②	Cv PP.Ø110
②	C.I. CHG.Ø76	③	Cv PP.Ø110
②	CD PP.Ø110		

SANITARIO POLICIA MASCULINO

DISTRIB. INT. AF ø13
1 L° c/MEZCLADOR–DESC. CPPØ38 A PPA ø63
1 I°P° DAI DESC CPPØ110
1 DU c/MEZCLADOR–DESC. CPPØ38 A PPA ø63
4 LLP AF Ø13
3 LLP AC Ø13
2 PPA Ø63
1 TERMOTANQUE ELECTRICO 54 lts.

SANITARIO POLICIA FEMENINO

DISTRIB. INT. AF ø13
1 L° c/MEZCLADOR–DESC. CPPØ38 A PPA ø63
1 I°P° DAI DESC CPPØ110
1 DU c/MEZCLADOR–DESC. CPPØ38 A PPA ø63
4 LLP AF Ø13
3 LLP AC Ø13
2 PPA Ø63
1 TERMOTANQUE ELECTRICO 54 lts.

VESTUARIO PERS. ESTACION FEMENINO

DISTRIB. INT. AF ø13
2 L° c/MEZCLADOR–DESC. CPPØ38 A PPA ø63
2 I°P° DAI DESC CPPØ110
2 DU c/MEZCLADOR–DESC. CPPØ38 A PPA ø63
5 LLP AF Ø13
3 LLP AC Ø13
3 PPA Ø63
1 TERMOTANQUE ELECTRICO 54 lts.

VESTUARIO PERS. ESTACION MASCULINO

DISTRIB. INT. AF ø13
2 L° c/MEZCLADOR–DESC. CPPØ38 A PPA ø63
1 I°P° DAI DESC CPPØ110
2 M° c/VALV. AUT.–DESC. CPPø38 A PPA ø63
2 DU c/MEZCLADOR–DESC. CPPØ38 A PPA ø63
5 LLP AF Ø13
3 LLP AC Ø13

CROQUIS UBICACION

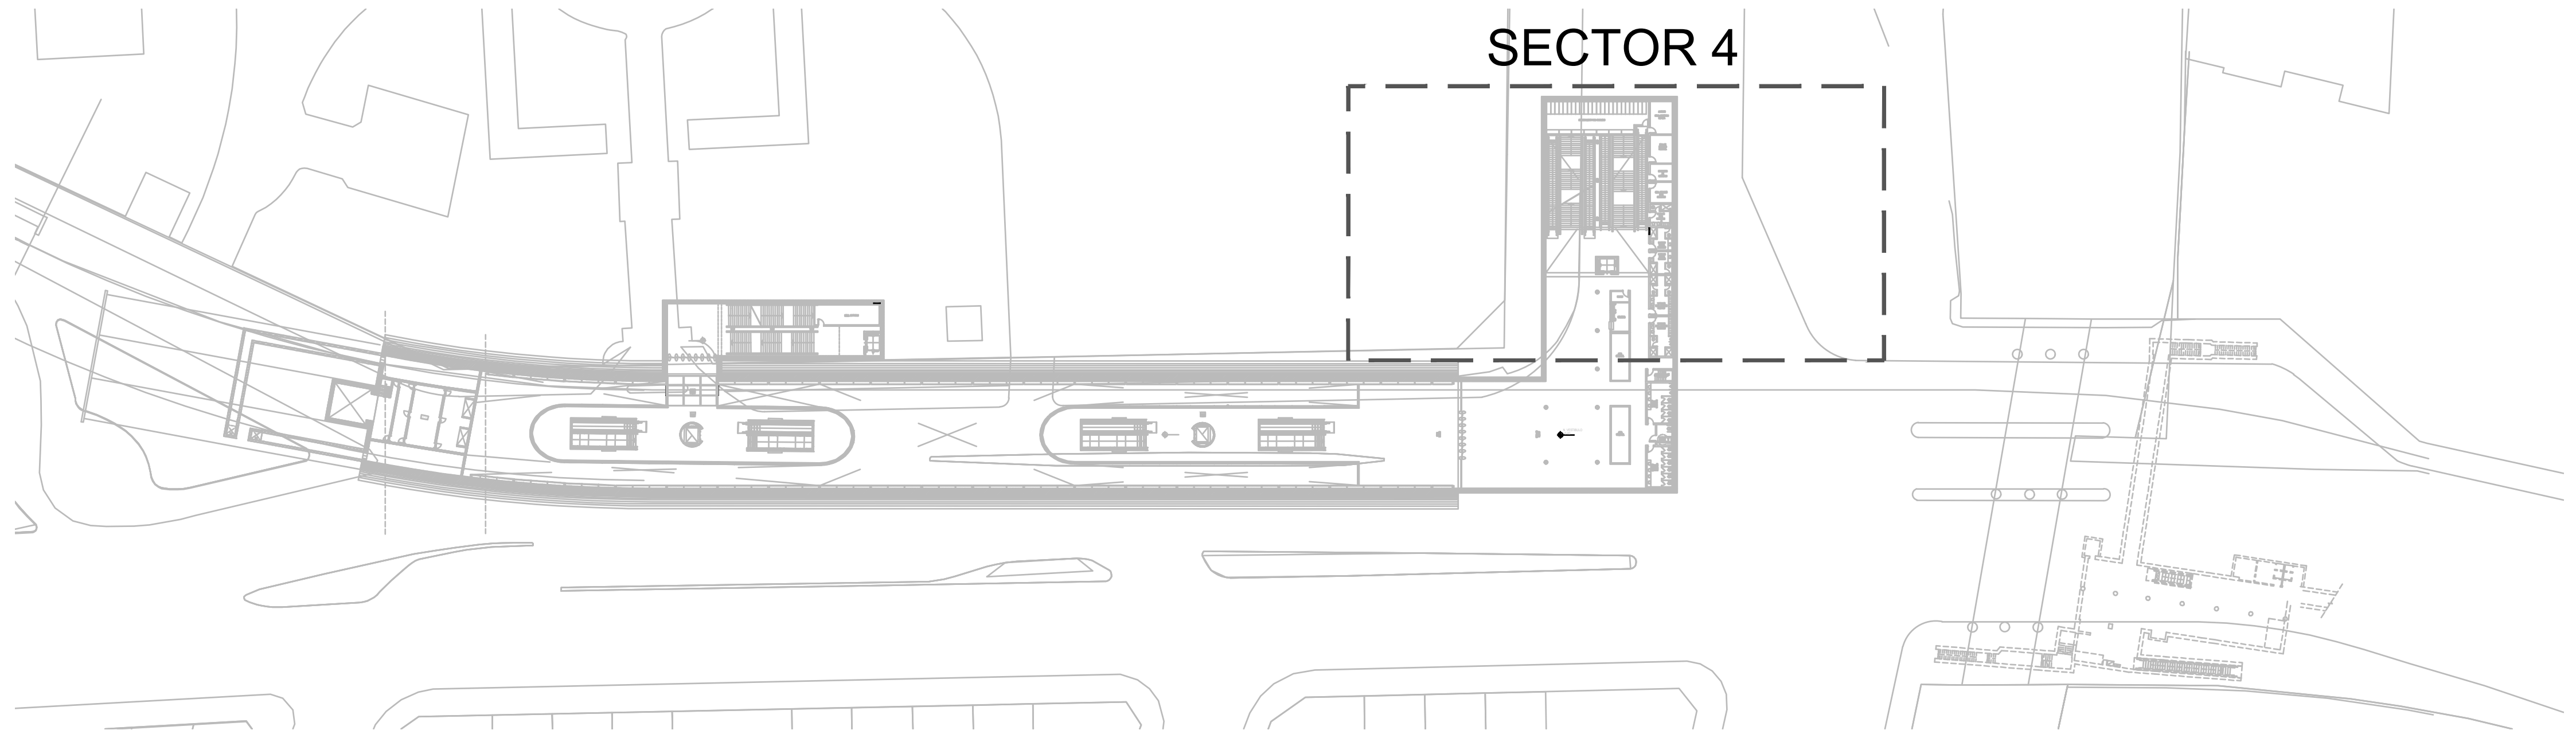

REFERENCIAS

🟥	INSTALACION CLOACAL – PRIMARIA
🟧	INSTALACION CLOACAL – SECUNDARIA
━	INSTALACION CLOACAL IMPULSION – PRIMARIA
– – –	INSTALACION CLOACAL – VENTILACION
━	INSTALACION AGUA FRIA
– – –	INSTALACION AGUA FRIA POR CIELORRASO
━	INSTALACION AGUA CALIENTE
– – –	INSTALACION AGUA CALIENTE POR CIELORRASO

LLP	LLAVE DE PASO
CS	CANILLA DE SERVICIO
BDA	BOCA DE DESAGUE ABIERTA
BDT	BOCA DE DESAGUE CERRADA
CDV	CAÑO DE DESCARGA VENTILACION
CV	CAÑO DE VENTILACION
PPA	PILETA DE PISO ABIERTA
CI	CAMARA DE INSPECCION
BR	BOCA DE REGISTRO
CA	CAMARA AQUIETAMIENTO

NOTAS

CAÑERIAS DESCARGA SANITARIAS
  MATERIAL: POLIPROPILENO APTO PARA USO SANITARIO
  UNIONES: CON ORING DE DOBLE LABIO APTO PARA USO SANITARIO
  SISTEMA: TIPO AWADUCT O SIMILAR

CAÑERIAS DE AGUA FRIA Y CALIENTE
  MATERIAL: POLIPROPILENO APTO PARA AGUA POTABLE FRIA Y CALIENTE
  UNIONES: POR TERMOFUSION
  SISTEMA: TIPO AQUA SYSTEM, SALADILLO O SIMILAR

CAÑERIAS DE IMPULSION CLOACAL
  MATERIAL: ACERO GALVANIZADO (HG)
  UNIONES EN GENERAL: ROSCADAS
  UNIONES PARA DESARME: BRIDADAS

NOTAS: EL PRESENTE PLANO ES INDICATIVO. LA CONTRATISTA CONFECCIONARA LOS PLANOS DE DETALLE DEFINITIVO, QUE DEBERAN SER APROBADOS POR LA D.G.O.INF.U Y LA INSPECCION DE OBRA. EL PLANO PRESENTADO POR LA CONTRATISTA ESTARA EN UN TODO DE ACUERDO CON LA NORMATIVA VIGENTE.
TODAS LAS MEDIDAS Y NIVELES SE VERIFICARAN EN OBRA POR EL CONTRATISTA.
TODOS LOS DETALLES CONSTRUCTIVOS SERAN COORDINADOS Y COMPATIBILIZADOS EN OBRA.

PLANO NO APTO PARA CONSTRUCCION.

MODIFICACIONES:

REVISION	FECHA	DESCRIPCION
0	20/02/2026	EMISIÓN PARA LICITACIÓN

Gobierno de la Ciudad de Buenos Aires
MINISTERIO DE INFRAESTRUCTURA
SUBSECRETARIA DE PROYECTOS Y OBRAS
DIRECCION GENERAL DE PROYECTOS

DGPRO

Obra: LÍNEA F			PLANO-2026-18272033-GCABA-SSPO	Plano N°
Plano: INSTALACIÓN SANITARIA - PLANTA NIVEL 1°VESTÍBULO/MEZZANINE			LF-ES-PAC-SAN-PL-003-04	4/4
Fecha: 20/02/2026	Eq. de Proyecto: UPU-ATEC-IATASA	Dibujó: M.S.	Revisó: J.C. Escala: 1:100	

Página 1 de 1

18/3/2026 17:35 p. m.
LF-ES-PAC-SAN-PL-003-04.dwg

GOBIERNO DE LA CIUDAD DE BUENOS AIRES

"2026 - Año del 30° Aniversario de la sanción de la Constitución de la Ciudad Autónoma de Buenos Aires"

Hoja Adicional de Firmas
Plano

Número: PLANO-2026-18272033-GCABA-SSPO

Buenos Aires, Viernes 17 de Abril de 2026

Referencia: LF-ES-PAC-SAN-PL-003-04_0

El documento fue importado por el sistema GEDO con un total de 1 pagina/s.

Digitally signed by Comunicaciones Oficiales
Date: 2026.04.17 14:39:36 -03:00

Facundo Lombardo
Subsecretario
SUBSECRETARIA PROYECTOS Y OBRAS
MINISTERIO DE MOVILIDAD E INFRAESTRUCTURA

Digitally signed by Comunicaciones Oficiales
Date: 2026.04.17 14:39:37 -03:00