

# PLANTA NIVEL 1°VESTÍBULO/MEZZANINE

ESCALA 1:100

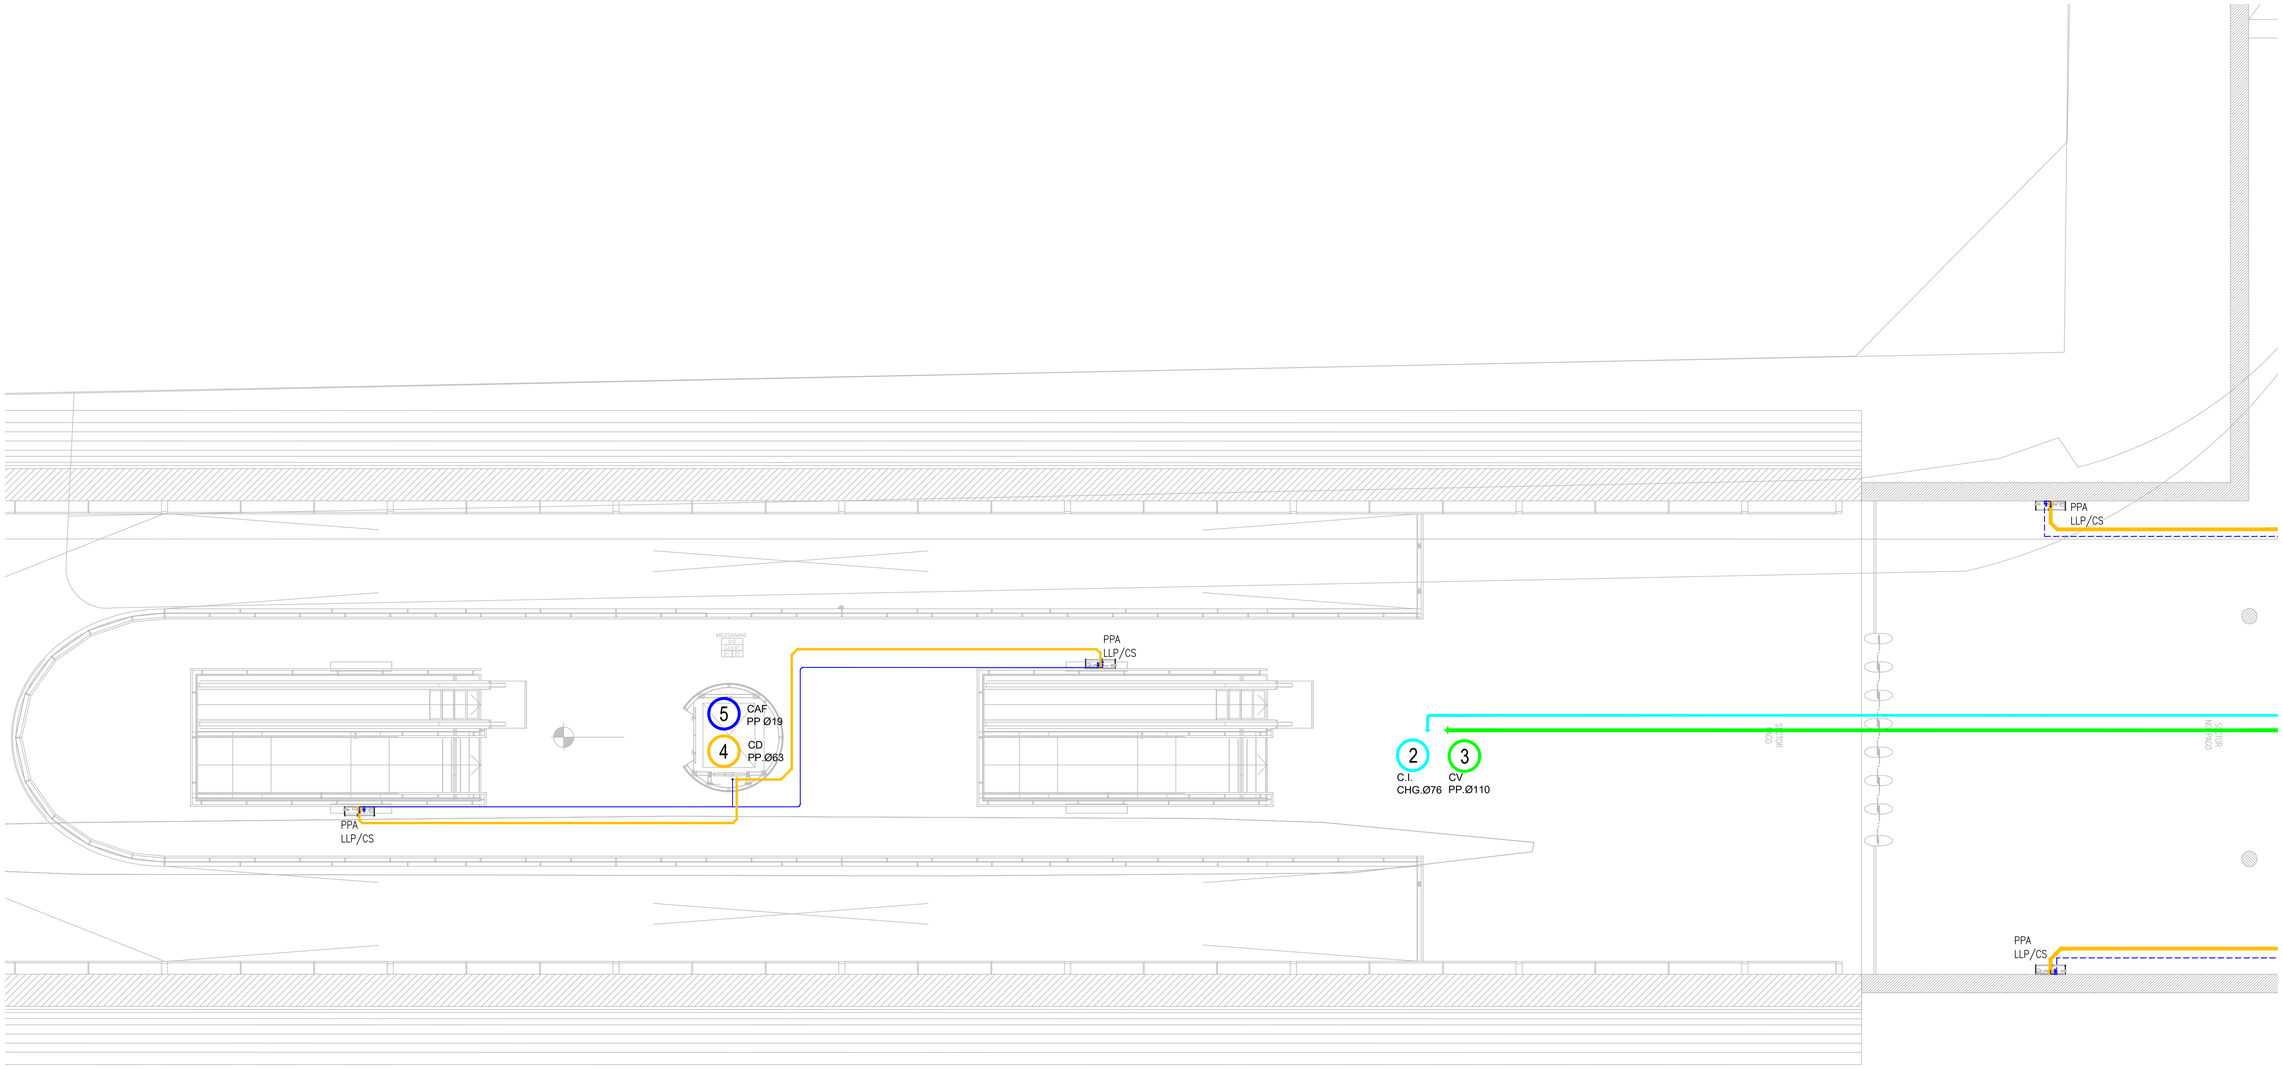


## CROQUIS UBICACION

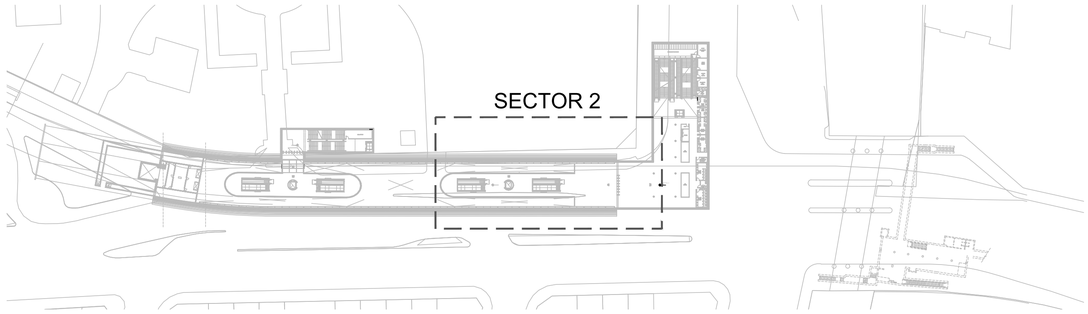


## REFERENCIAS

- INSTALACION CLOACAL – PRIMARIA
- INSTALACION CLOACAL – SECUNDARIA
- INSTALACION CLOACAL IMPULSION – PRIMARIA
- INSTALACION CLOACAL – VENTILACION
- INSTALACION AGUA FRIA
- INSTALACION AGUA FRIA POR CIELORRASO
- INSTALACION AGUA CALIENTE
- INSTALACION AGUA CALIENTE POR CIELORRASO

| | |
|---|---|
| LLP | LLAVE DE PASO |
| CS | CANILLA DE SERVICIO |
| BDA | BOCA DE DESAGUE ABIERTA |
| BDT | BOCA DE DESAGUE CERRADA |
| CDV | CAÑO DE DESCARGA VENTILACION |
| CV | CAÑO DE VENTILACION |
| PPA | PILETA DE PISO ABIERTA |
| CI | CAMARA DE INSPECCION |
| BR | BOCA DE REGISTRO |
| CA | CAMARA AQUIETAMIENTO |

## NOTAS

CAÑERIAS DESCARGA SANITARIAS
MATERIAL: POLIPROPILENO APTO PARA USO SANITARIO
UNIONES: CON ORING DE DOBLE LABIO APTO PARA USO SANITARIO
SISTEMA: TIPO AWADUCT O SIMILAR

CAÑERIAS DE AGUA FRIA Y CALIENTE
MATERIAL: POLIPROPILENO APTO PARA AGUA POTABLE FRIA Y CALIENTE
UNIONES: POR TERMOFUSION
SISTEMA: TIPO AQUA SYSTEM, SALADILLO O SIMILAR

CAÑERIAS DE IMPULSION CLOACAL
MATERIAL: ACERO GALVANIZADO (HG)
UNIONES EN GENERAL: ROSCADAS
UNIONES PARA DESARME: BRIDADAS

NOTAS: LA EJECUCIÓN Y PUESTA EN SERVICIO DE LA INSTALACIÓN DEBERÁ SER REALIZADA POR EMPRESA MATRICULADA, QUE ASUMIRÁ LOS TRABAJOS APROBADOS POR LA D.G.OUM.U Y LA INSPECCIÓN DE OBRA. EL PLANO PRESENTADO POR LA CONTRATISTA ESTARÁ EN UN TODO DE ACUERDO CON LA NORMATIVA VIGENTE.
TODAS LAS MEDIDAS Y NIVELES SE VERIFICARAN EN OBRA POR EL CONTRATISTA.
TODOS LOS DETALLES CONSTRUCTIVOS SERÁN COORDINADOS Y COMPATIBILIZADOS EN OBRA

PLANO NO APTO PARA CONSTRUCCION.

MODIFICACIONES:

| REVISION | FECHA | DESCRIPCION |
|---|---|---|
| 0 | 20/02/2026 | EMISIÓN PARA LICITACIÓN |

Gobierno de la Ciudad de Buenos Aires

MINISTERIO DE INFRAESTRUCTURA
SUBSECRETARIA DE PROYECTOS Y OBRAS
**DIRECCION GENERAL DE PROYECTOS**

**DGPRO**

Obra: LÍNEA F
PLANO-2026-18272157-GCABA-SSPO
Plano: INSTALACIÓN SANITARIA - PLANTA NIVEL 1°VESTÍBULO/MEZZANINE
LF-ES-PAC-SAN-PL-003-02
Fecha: 20/02/2026 | Eq. de Proyecto: UPU-ATEC-IATASA | Dibujó: M.S. | Revisó: J.C. | Escala: 1:100
Lámina N° 2/4

18/3/2026 17:33 p. m.
LF-ES-PAC-SAN-PL-003-02.dwg

G O B I E R N O DE LA C I U D A D DE B U E N O S A I R E S

"2026 - Año del 30° Aniversario de la sanción de la Constitución de la Ciudad Autónoma de Buenos Aires"

**Hoja Adicional de Firmas**
**Plano**

**Número:** PLANO-2026-18272157-GCABA-SSPO

Buenos Aires, Viernes 17 de Abril de 2026

**Referencia:** LF-ES-PAC-SAN-PL-003-02_0

---

El documento fue importado por el sistema GEDO con un total de 1 pagina/s.

Digitally signed by Comunicaciones Oficiales
Date: 2026.04.17 14:40:01 -03:00

Facundo Lombardo
Subsecretario
SUBSECRETARIA PROYECTOS Y OBRAS
MINISTERIO DE MOVILIDAD E INFRAESTRUCTURA

Digitally signed by Comunicaciones Oficiales
Date: 2026.04.17 14:40:02 -03:00