18/3/2026 17:26 p. m.
LF-ES-PAC-SAN-PL-001-01.dwg

PLANTA NIVEL ACCESO

ESCALA 1:100

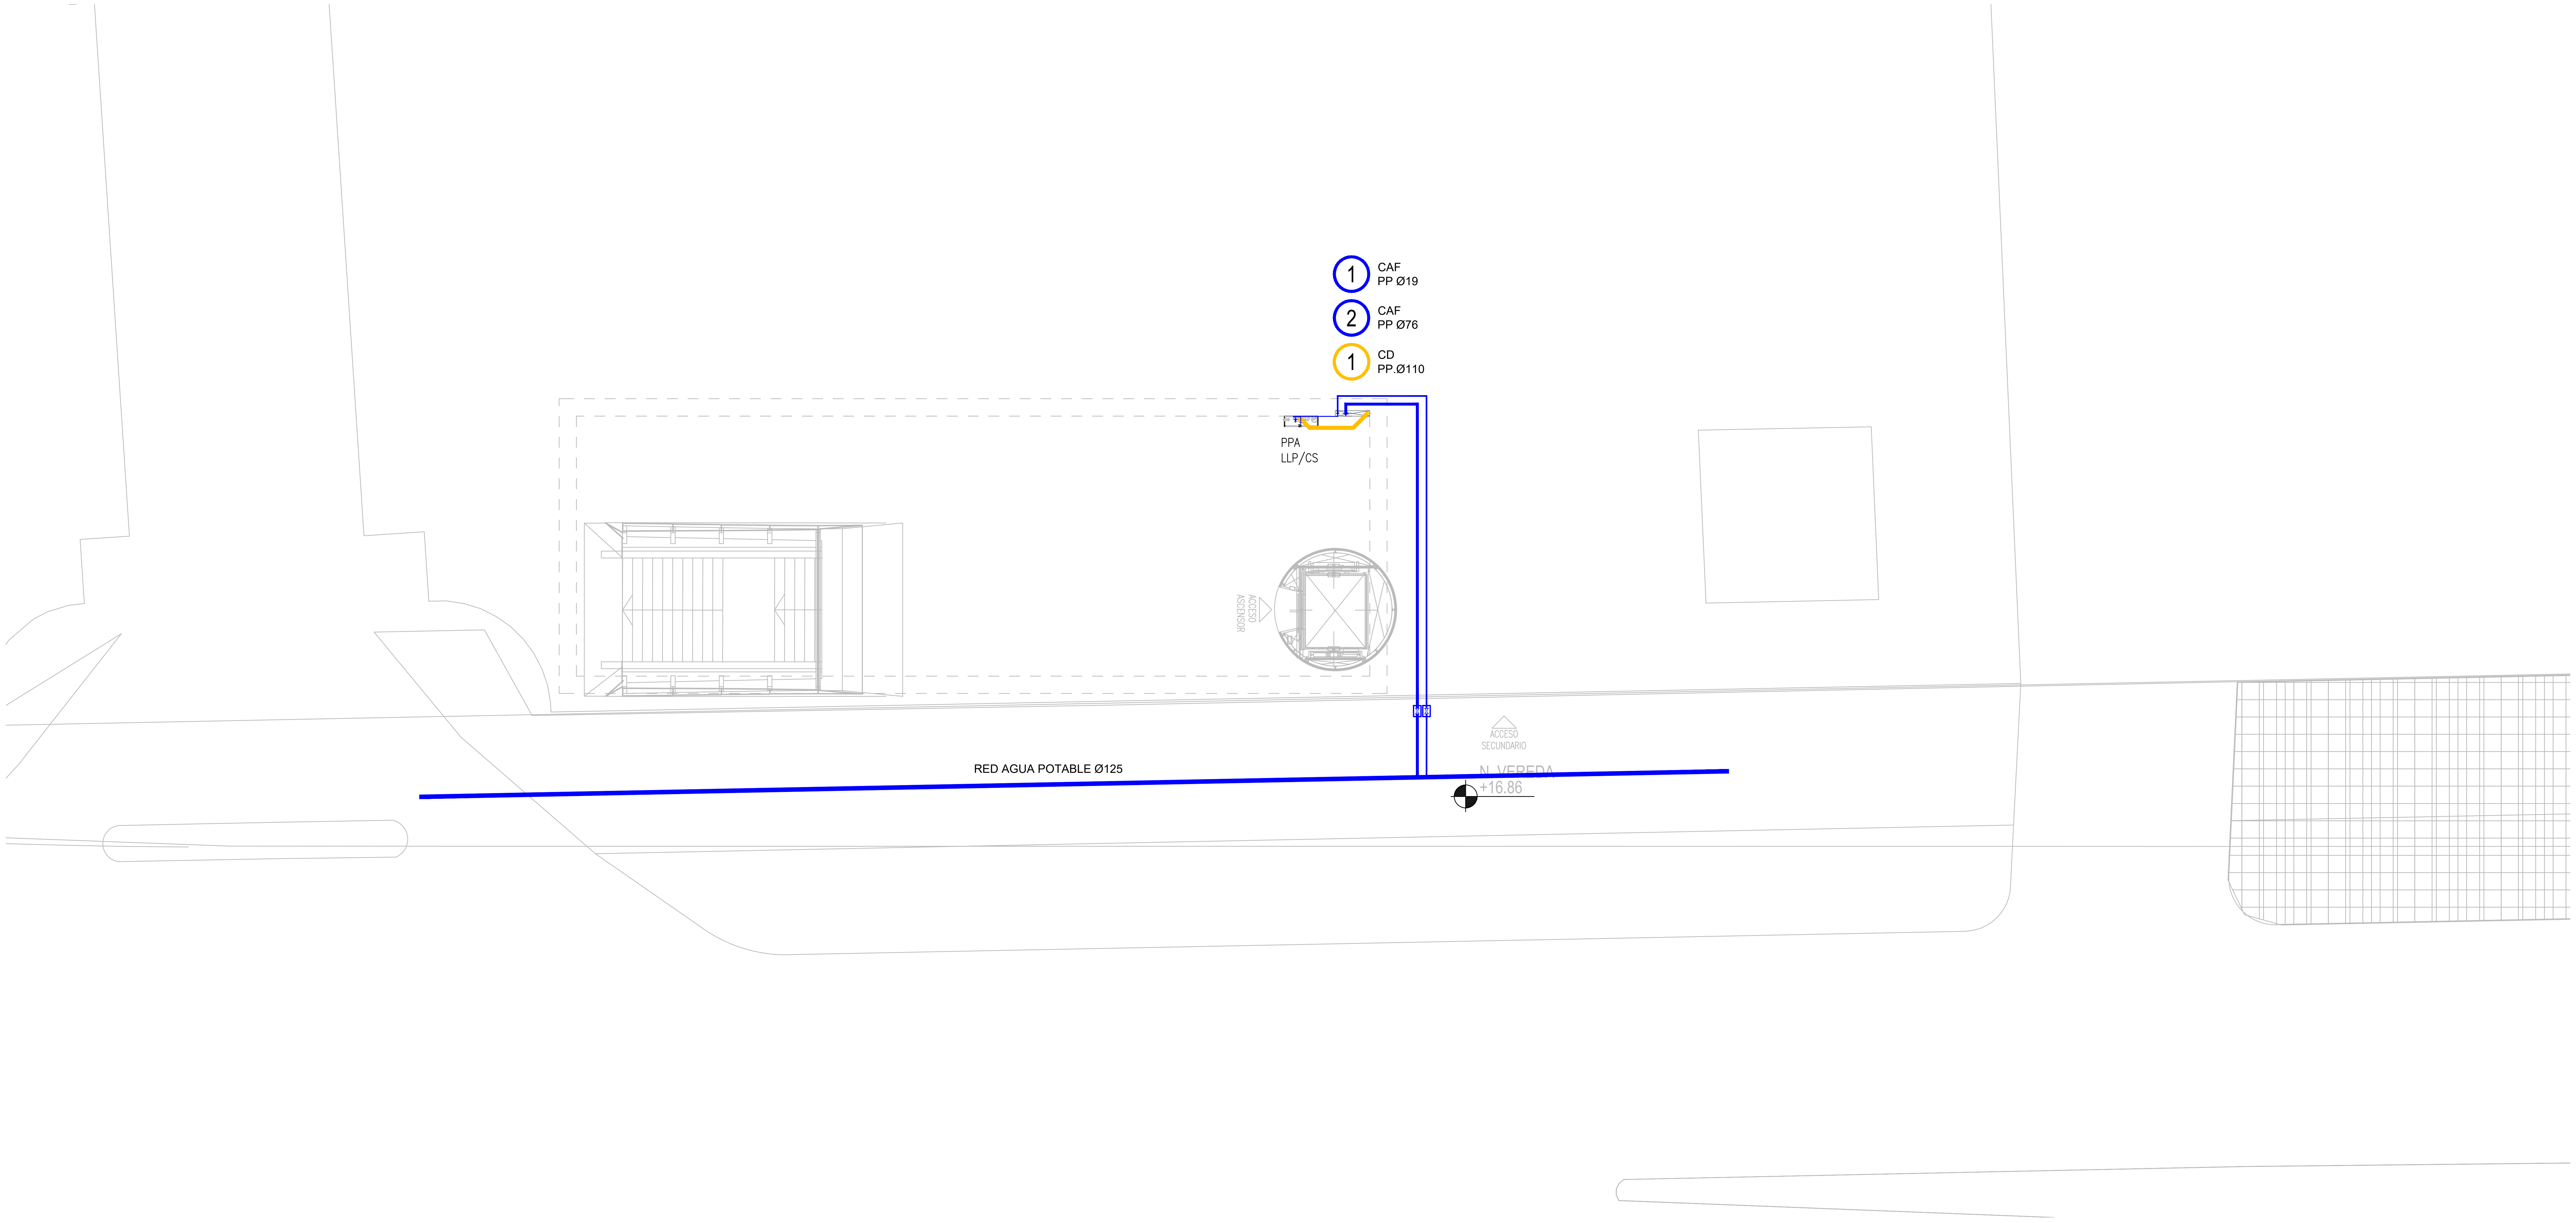

CROQUIS UBICACION

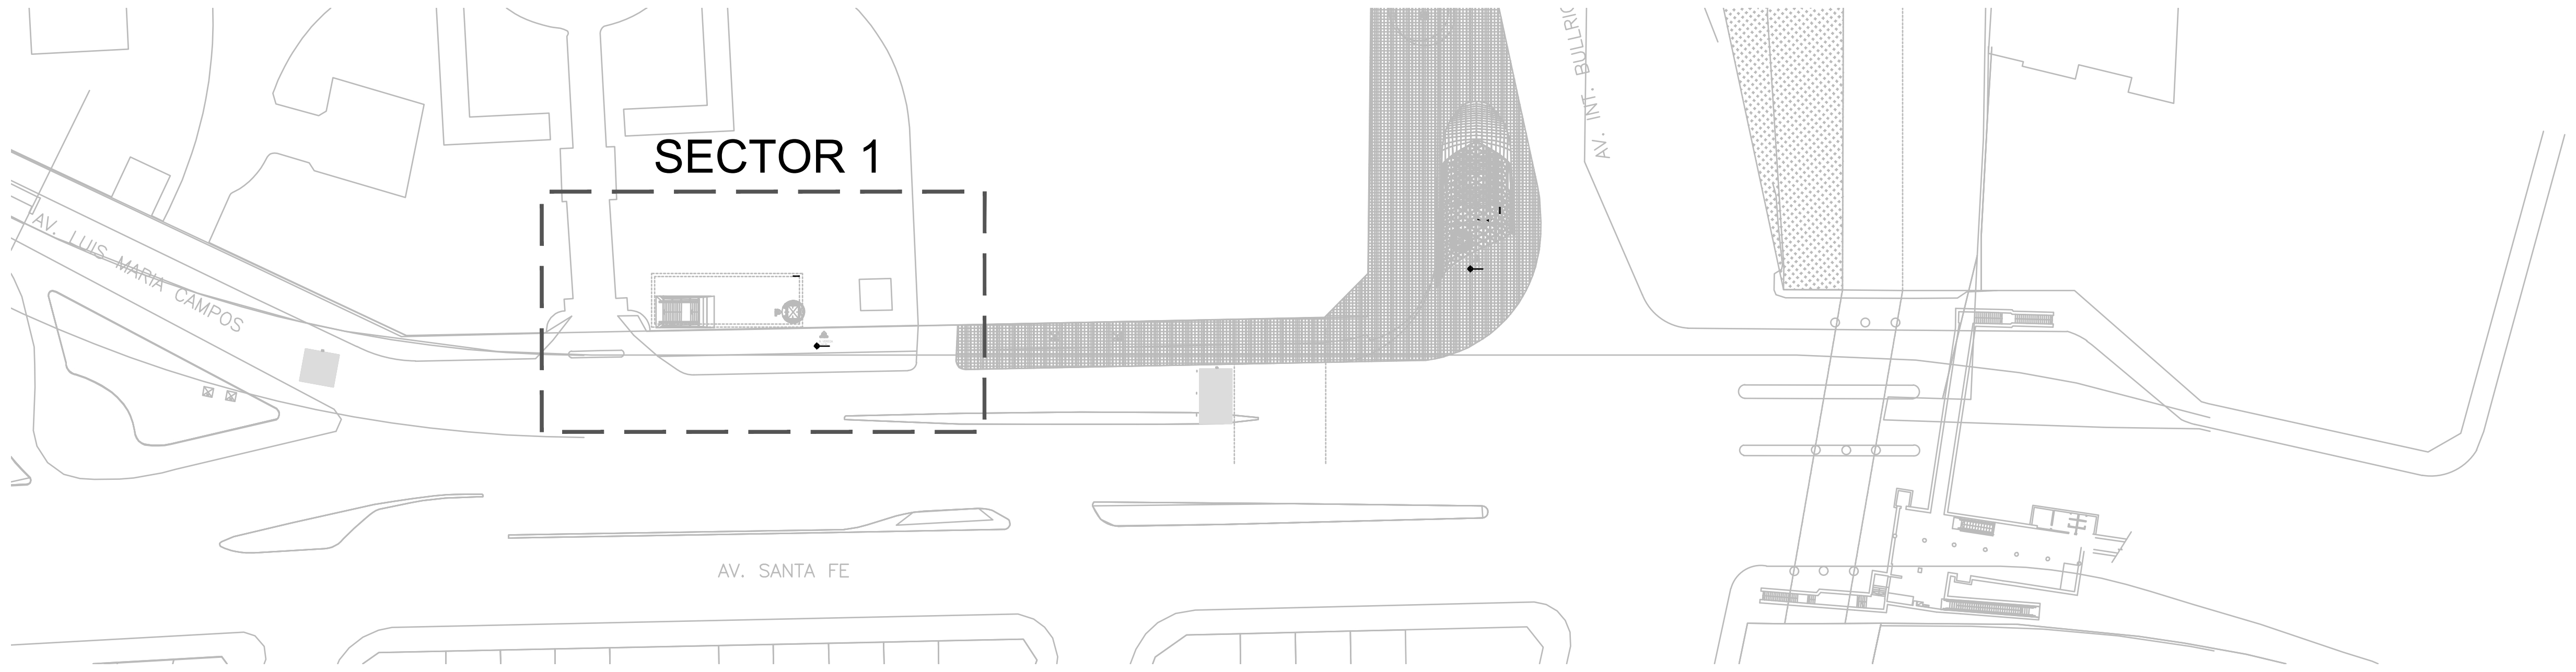

REFERENCIAS

- INSTALACION CLOACAL – PRIMARIA
- INSTALACION CLOACAL – SECUNDARIA
- INSTALACION CLOACAL IMPULSION – PRIMARIA
- INSTALACION CLOACAL – VENTILACION
- INSTALACION AGUA FRIA
- INSTALACION AGUA FRIA POR CIELORRASO
- INSTALACION AGUA CALIENTE
- INSTALACION AGUA CALIENTE POR CIELORRASO

LLP	LLAVE DE PASO
CS	CANILLA DE SERVICIO
BDA	BOCA DE DESAGUE ABIERTA
BDT	BOCA DE DESAGUE CERRADA
CDV	CAÑO DE DESCARGA VENTILACION
CV	CAÑO DE VENTILACION
PPA	PILETA DE PISO ABIERTA
CI	CAMARA DE INSPECCION
BR	BOCA DE REGISTRO
CA	CAMARA AQUIETAMIENTO

NOTAS

CAÑERIAS DESCARGA SANITARIAS
MATERIAL: POLIPROPILENO APTO PARA USO SANITARIO
UNIONES: CON ORING DE DOBLE LABIO APTO PARA USO SANITARIO
SISTEMA: TIPO AWADUCT O SIMILAR

CAÑERIAS DE AGUA FRIA Y CALIENTE
MATERIAL: POLIPROPILENO APTO PARA AGUA POTABLE FRIA Y CALIENTE
UNIONES: POR TERMOFUSION
SISTEMA: TIPO AQUA SYSTEM, SALADILLO O SIMILAR

CAÑERIAS DE IMPULSION CLOACAL
MATERIAL: ACERO GALVANIZADO (HG)
UNIONES EN GENERAL: ROSCADAS
UNIONES PARA DESARME: BRIDADAS

NOTAS: EL PRESENTE PLANO ES INDICATIVO. LA CONTRATISTA CONFECCIONARA LOS PLANOS DE DETALLE DEFINITIVO, QUE DEBERAN SER APROBADOS POR LA D.G.O.INF.U Y LA INSPECCION DE OBRA. EL PLANO PRESENTADO POR LA CONTRATISTA ESTARA EN UN TODO DE ACUERDO CON LA NORMATIVA VIGENTE.
TODAS LAS MEDIDAS Y NIVELES SE VERIFICARAN EN OBRA POR EL CONTRATISTA.
TODOS LOS DETALLES CONSTRUCTIVOS SERAN COORDINADOS Y COMPATIBILIZADOS EN OBRA.

PLANO NO APTO PARA CONSTRUCCION.

MODIFICACIONES:

REVISION	FECHA	DESCRIPCION
0	20/02/2026	EMISIÓN PARA LICITACIÓN

Gobierno de la Ciudad de Buenos Aires

MINISTERIO DE INFRAESTRUCTURA
SUBSECRETARIA DE PROYECTOS Y OBRAS
DIRECCION GENERAL DE PROYECTOS

DGPRO

Obra: LÍNEA F
PLANO-2026-18272914-GCABA-SSPO
Plano N°
Plano: INSTALACIÓN SANITARIA - PLANTA NIVEL ACCESO
LF-ES-PAC-SAN-PL-001-01
1/2
Fecha: 20/02/2026
Eq. de Proyecto: UPU-ATEC-IATASA
Dibujó: M.S.
Revisó: J.C.
Escala: 1:100

Hoja Adicional de Firmas
Plano

Número: PLANO-2026-18272914-GCABA-SSPO

Buenos Aires, Viernes 17 de Abril de 2026

Referencia: LF-ES-PAC-SAN-PL-001-01_0

El documento fue importado por el sistema GEDO con un total de 1 pagina/s.

Digitally signed by Comunicaciones Oficiales
Date: 2026.04.17 14:41:57 -03:00

Facundo Lombardo
Subsecretario
SUBSECRETARIA PROYECTOS Y OBRAS
MINISTERIO DE MOVILIDAD E INFRAESTRUCTURA

Digitally signed by Comunicaciones Oficiales
Date: 2026.04.17 14:41:59 -03:00