

PLANTA NIVEL SALA DE VENTILACIÓN

ESCALA 1:100

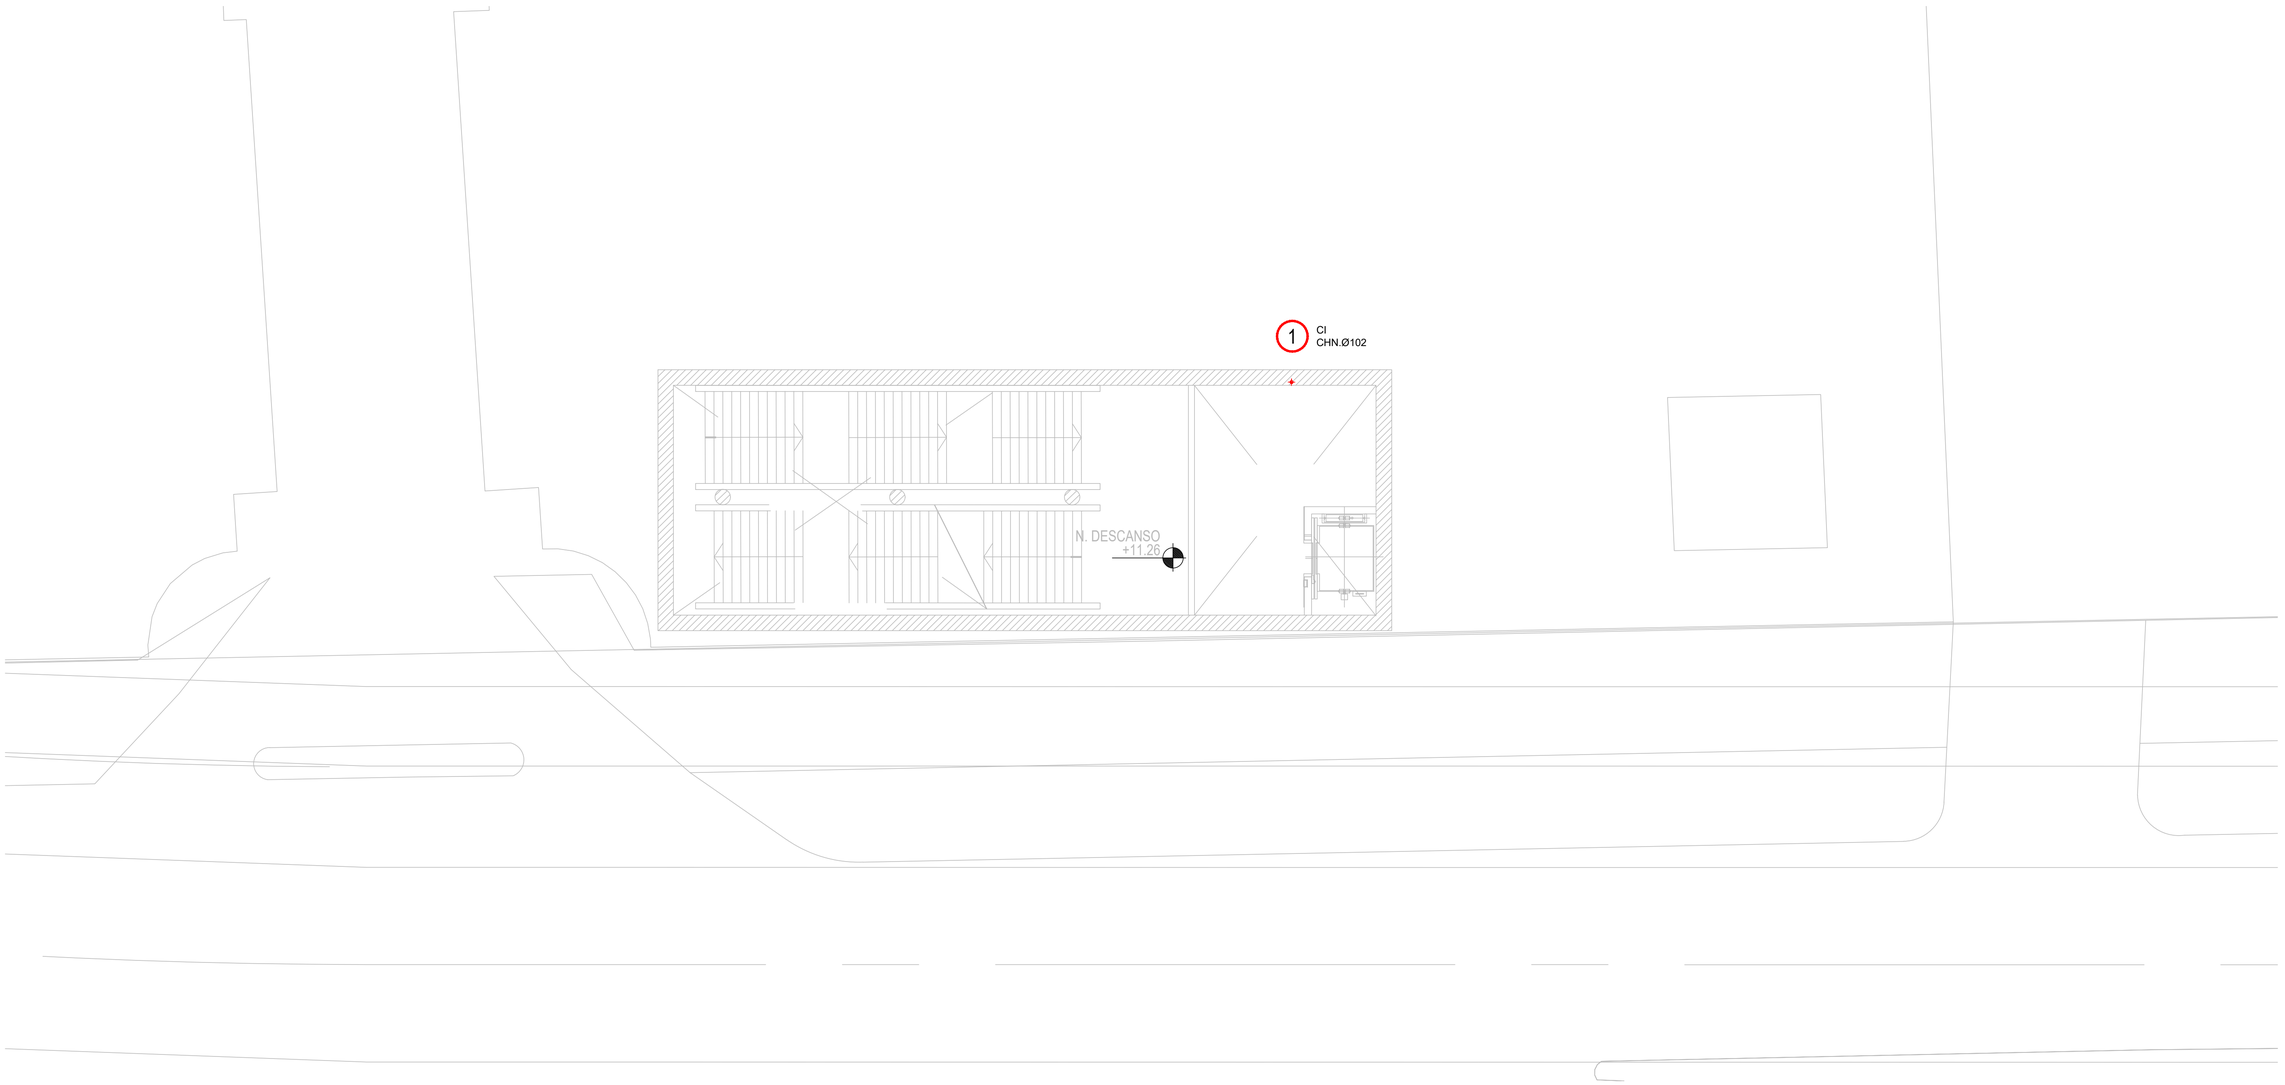

CROQUIS UBICACION

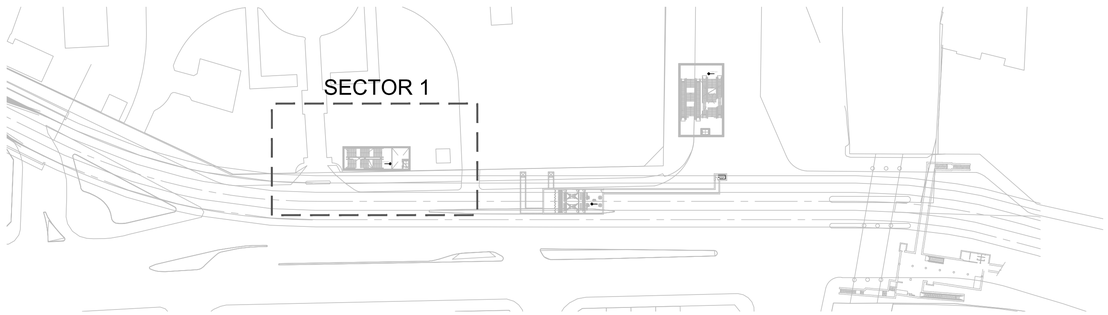

REFERENCIAS

HIDRANTE INTERIOR COMPUESTO POR VALVULA TEATRO ø1-3/4"c/MANGUERA ø 45mm. x 20mts. LANZA C/BOQUILLA A CHORRO / NIEBLA LLAVE P/AJUSTAR UNIONES

MATAFUEGO DE POLVO QUIMICO CLASE ABC x 5 Kg.

MATAFUEGO DE CO2 x 3.5 Kg.

COLUMNA ALIMENTACIÓN DE HIDRANTES.

NOTAS

-LA UBICACION DEFINITIVA DE LAS TOMAS, CONEXIONES CON LAS REDES PUBLICAS, VENTILACIONES Y TODO ELEMENTO QUE EMERJA O SE UBIQUE A NIVEL CALZADA O VEREDA SERÁ COORDINADA CON LA DIRECCION DE OBRA.

-EL PROYECTO EJECUTIVO DE LAS INSTALACIONES SE DEBERÁ ADAPTAR A LA ARQUITECTURA DEFINITIVA.

-LA DISTANCIA MÁXIMA ENTRE SOPORTES NO DEBE EXCEDER LOS 4,6 M (15 FT) PARA CAÑERÍAS DE DIAMETROS MAYORES A ø1¼" Y NO MAS DE 3,65m (12 FT) PARA CAÑERÍAS DE ø 1¼" O MENORES.

-LAS CAÑERIAS ENTERRADAS LLEVARAN PROTECCION ANTICORROSIVA POR MEDIO DE REVESTIMIENTO EN POLIETILENO TRICAPA EXTRUIDO Y/O POLIGUARD.

NOTAS: EL PRESENTE PROYECTO EJECUTIVO, EN CONFORMIDAD CON PLANOS DE ANTEPROYECTO APROBADOS POR LA D.G.D.M.U.I Y LA INSPECCION DE OBRA. EL PLANO PRESENTADO POR LA CONTRATISTA ESTARA EN UN TODO DE ACUERDO CON LA NORMATIVA VIGENTE.
TODAS LAS MEDIDAS Y NIVELES SE VERIFICARAN EN OBRA POR EL CONTRATISTA.
TODOS LOS DETALLES CONSTRUCTIVOS SERAN COORDINADOS Y COMPATIBILIZADOS EN OBRA

PLANO NO APTO PARA CONSTRUCCION.

MODIFICACIONES:

REVISION	FECHA	DESCRIPCION
0	20/02/2026	EMISIÓN PARA LICITACIÓN

MINISTERIO DE INFRAESTRUCTURA
SUBSECRETARIA DE PROYECTOS Y OBRAS
DIRECCION GENERAL DE PROYECTOS

DGPRO

Obra: LÍNEA F				PLANO-2026-18273984-GCABA-SSPO
Plano: INSTALACIÓN CONTRA INCENDIO - PLANTA NIVEL SALA DE VENTILACIÓN				LF-ES-PAC-INC-PL-002-01
Fecha: 20/02/2026	Eq. de Proyecto: UPU-ATEC-IATASA	Dibujó: M.S.	Revisó: J.C.	Escala: 1:100

HOJA N° 1/2

25/3/2026 17:37 p. m.
LF-ES-PAC-INC-PL-002-01.dwg

G O B I E R N O DE LA C I U D A D DE B U E N O S A I R E S

"2026 - Año del 30° Aniversario de la sanción de la Constitución de la Ciudad Autónoma de Buenos Aires"

Hoja Adicional de Firmas
Plano

Número: PLANO-2026-18273984-GCABA-SSPO

Buenos Aires, Viernes 17 de Abril de 2026

Referencia: LF-ES-PAC-INC-PL-002-01_0

El documento fue importado por el sistema GEDO con un total de 1 pagina/s.

Digitally signed by Comunicaciones Oficiales
Date: 2026.04.17 14:44:53 -03:00

Facundo Lombardo
Subsecretario
SUBSECRETARIA PROYECTOS Y OBRAS
MINISTERIO DE MOVILIDAD E INFRAESTRUCTURA

Digitally signed by Comunicaciones Oficiales
Date: 2026.04.17 14:44:53 -03:00